



Эскизный дизайн-проект интерьера квартиры в г.
Москва ЖК "Остров", ул. Нижние Мневники д. 7

МСК 392.12.25-ЭП ПРЕМИУМ

Визуализация и чертежи

 www.bdsn.ru
 [@designer_batenkov](https://www.instagram.com/designer_batenkov)
 +7(499)577-04-35
 info@1dsn.ru

ГАП
Гл. дизайнер
Гл. проектиров.

Батеньков А.С.
Власова В.А.
Лунькова В.Н.

Ведомость рабочих чертежей альбома			
	Лист	Наименование	Примечание
Интерьер			
	01	Ведомость рабочих чертежей	
	02	Ведомость рабочих чертежей	
	03	План обмера помещений.	
	04	План обмера помещений	
	05	План демонтажа стен и элементов	
	06	Схема монтажа стен из газобетонных блоков.	
	07	План монтажа стен и элементов с учетом отделки.	
	08	Монтаж. Сечения 02, 03, 08, 09, 10. Вид 1, вид 2. Узел 7, узел 8, 9.	
	09	Монтаж. Сечения 01, 04, 05. Узел 2, 3.	
	10	Монтаж. Сечения 06, 07. Узел 1, 4, 5, 6.	
	11	Общие указания по выполнению строительно-ремонтных работ.	
	12	План помещений после перепланировки.	
	13	План расстановки мебели и сан.тех.оборудования.	
	14	План заполнения дверных проемов и отделка подоконников.	
	15	Ведомость дверных проемов.	
	16	Схема размещения сан.тех.оборудования, канализации, ХВС, ГВС.	
	17	План размещения оборудования против протечек воды.	
	18	План размещения электрооборудования с мебелью.	
	19	План размещения электрооборудования.	
	20	План размещения групп включения освещения с мебелью.	
	21	План размещения освещения и выключателей.	
	22	Ведомость розеток и выключателей.	
	23	Ведомость осветительных приборов.	
	24	Схема размещения трансформаторов, контроллеров и блоков управления освещением.	
	25	Ведомость трансформаторов и светодиодных лент.	
	26	План размещения теплого пола, терморегуляторов и приборов отопления.	
	27	План размещения блоков управления.	
	28	Общий план полов с размещением мебели.	
	29	Общий план покрытий полов.	
	30	План плинтусов.	
	31	Общий план конструкций и отделки потолка.	
	32	Потолки. Сечения 1-1, 2-2, 3-3, 4-4, 5-5, 6-6, 7-7, 8-8, 9-9, 10-10, 11-11.	
	33	Общий план потока с вентиляцией.	
	34	План обозначения разверток стен.	
Прихожая Кухня Гостиная.			
	35	Видовые точки.	
	36	Видовые точки.	
	37	Видовые точки.	
	38	Видовые точки.	
	39	Видовые точки.	
	40	Видовые точки.	
	41	Видовые точки.	
	42	План отделки пола.	

Ведомость рабочих чертежей альбома			
	Лист	Наименование	Примечание
Интерьер			
	43	План отделки потолка.	
	44	План размещения электрооборудования.	
	45	План размещения освещения и выключателей.	
	46	Развертки стен А-01, А-02, А-03, А-04.	
	47	Развертки стен А-05, А-06, А-07, А-08.	
	48	Развертки стен А-09.	
	49	Развертки стен А-10.	
	50	Развертки стен А-11, А-12, А-13.	
	51	Ведомость отделочных материалов	
Кладовая.			
	52	План отделки пола. План отделки потолка.	
	53	План размещения электрооборудования. План размещения освещения и выключателей.	
	54	Развертки стен Б-01, Б-02.	
	55	Развертки стен Б-03, Б-04. Ведомость отделочных материалов.	
Гардеробная №1.			
	56	План отделки пола. План отделки потолка. План размещения электрооборудования. План размещения освещения и выключателей.	
	57	Развертки стен В-01, В-02, В-03, В-04.	
Душевая.			
	58	Видовые точки.	
	59	Видовые точки.	
	60	План отделки пола. План отделки потолка.	
	61	План размещения электрооборудования. План размещения освещения и выключателей.	
	62	Развертки стен Г-01, Г-02, Г-03.	
	63	Развертки стен Г-04, Г-05.	

МСК 392.12.25-ЭП ПРЕМИУМ			
Эскизный дизайн-проект интерьера квартиры в г. Москва ЖК "Остров", ул. Нижние Мневники д. 7			
Ведомость рабочих чертежей			
Дизайнер интерьера  №1 Александр Батеньков	Стадия	Лист	Листов
	ЭП	01	120
		Подп.	Дата
ГАП	Батеньков А.С.		
Гл. дизайнер	Власова В.А.		
Гл. проектиров.	Лунькова В.Н.		


Ведомость рабочих чертежей альбома			
	Лист	Наименование	Примечание
Спальня №1.			
	64	Видовые точки.	
	65	Видовые точки.	
	66	План отделки пола.	
	67	План отделки потолка.	
	68	План размещения электрооборудования.	
	69	План размещения освещения и выключателей.	
	70	Развертки стен Д-01, Д-02.	
	71	Развертки стен Д-03, Д-04, Д-05, Д-06, Д-07, Д-08.	
	72	Ведомость отделочных материалов.	
Спальня №2.			
	73	Видовые точки.	
	74	Видовые точки.	
	75	План отделки пола.	
	76	План отделки потолка.	
	77	План размещения электрооборудования.	
	78	План размещения освещения и выключателей.	
	79	Развертки стен Е-01, Е-02.	
	80	Развертки стен Е-03, Е-04, Е-05, Е-06.	
	81	Ведомость отделочных материалов.	
Мастер спальня.			
	82	Видовые точки.	
	83	Видовые точки.	
	84	Видовые точки.	
	85	Видовые точки.	
	86	Видовые точки.	
	87	План отделки пола.	
	88	План отделки потолка.	
	89	План размещения электрооборудования.	
	90	План размещения освещения и выключателей.	
	91	Развертки стен И-01, И-02.	
	92	Развертки стен И-03, И-04.	
	93	Развертки стен И-05.	
	94	Развертки стен И-06, И-07, И-08, И-09, И-10.	
	95	Ведомость отделочных материалов.	
Мастер ванная			
	96	Видовые точки.	
	97	Видовые точки.	
	98	План отделки пола.	
	99	План отделки потолка.	
	100	План размещения электрооборудования.	
	101	План размещения освещения и выключателей.	
	102	Развертки стен К-01, К-02.	
	103	Развертки стен К-03, К-04, К-05.	
	104	Ведомость отделочных материалов.	
	105	Примечания.	

МСК 392.12.25-ЭП ПРЕМИУМ			
Эскизный дизайн-проект интерьера квартиры в г. Москва ЖК "Остров", ул. Нижние Мневники д. 7			
Ведомость рабочих чертежей			
Дизайнер интерьера  №1 Александр Батеньков	Стадия	Лист	Листов
	ЭП	02	120
		Подп.	Дата
Г.АП	Батеньков А.С.		
Гл. дизайнер	Власова В.А.		
Гл. проектиров.	Луныкова В.Н.		

Согласования:

Взам инв. №
Подпись и дата
Инв. № подл.

ПЛАН КВАРТИРЫ

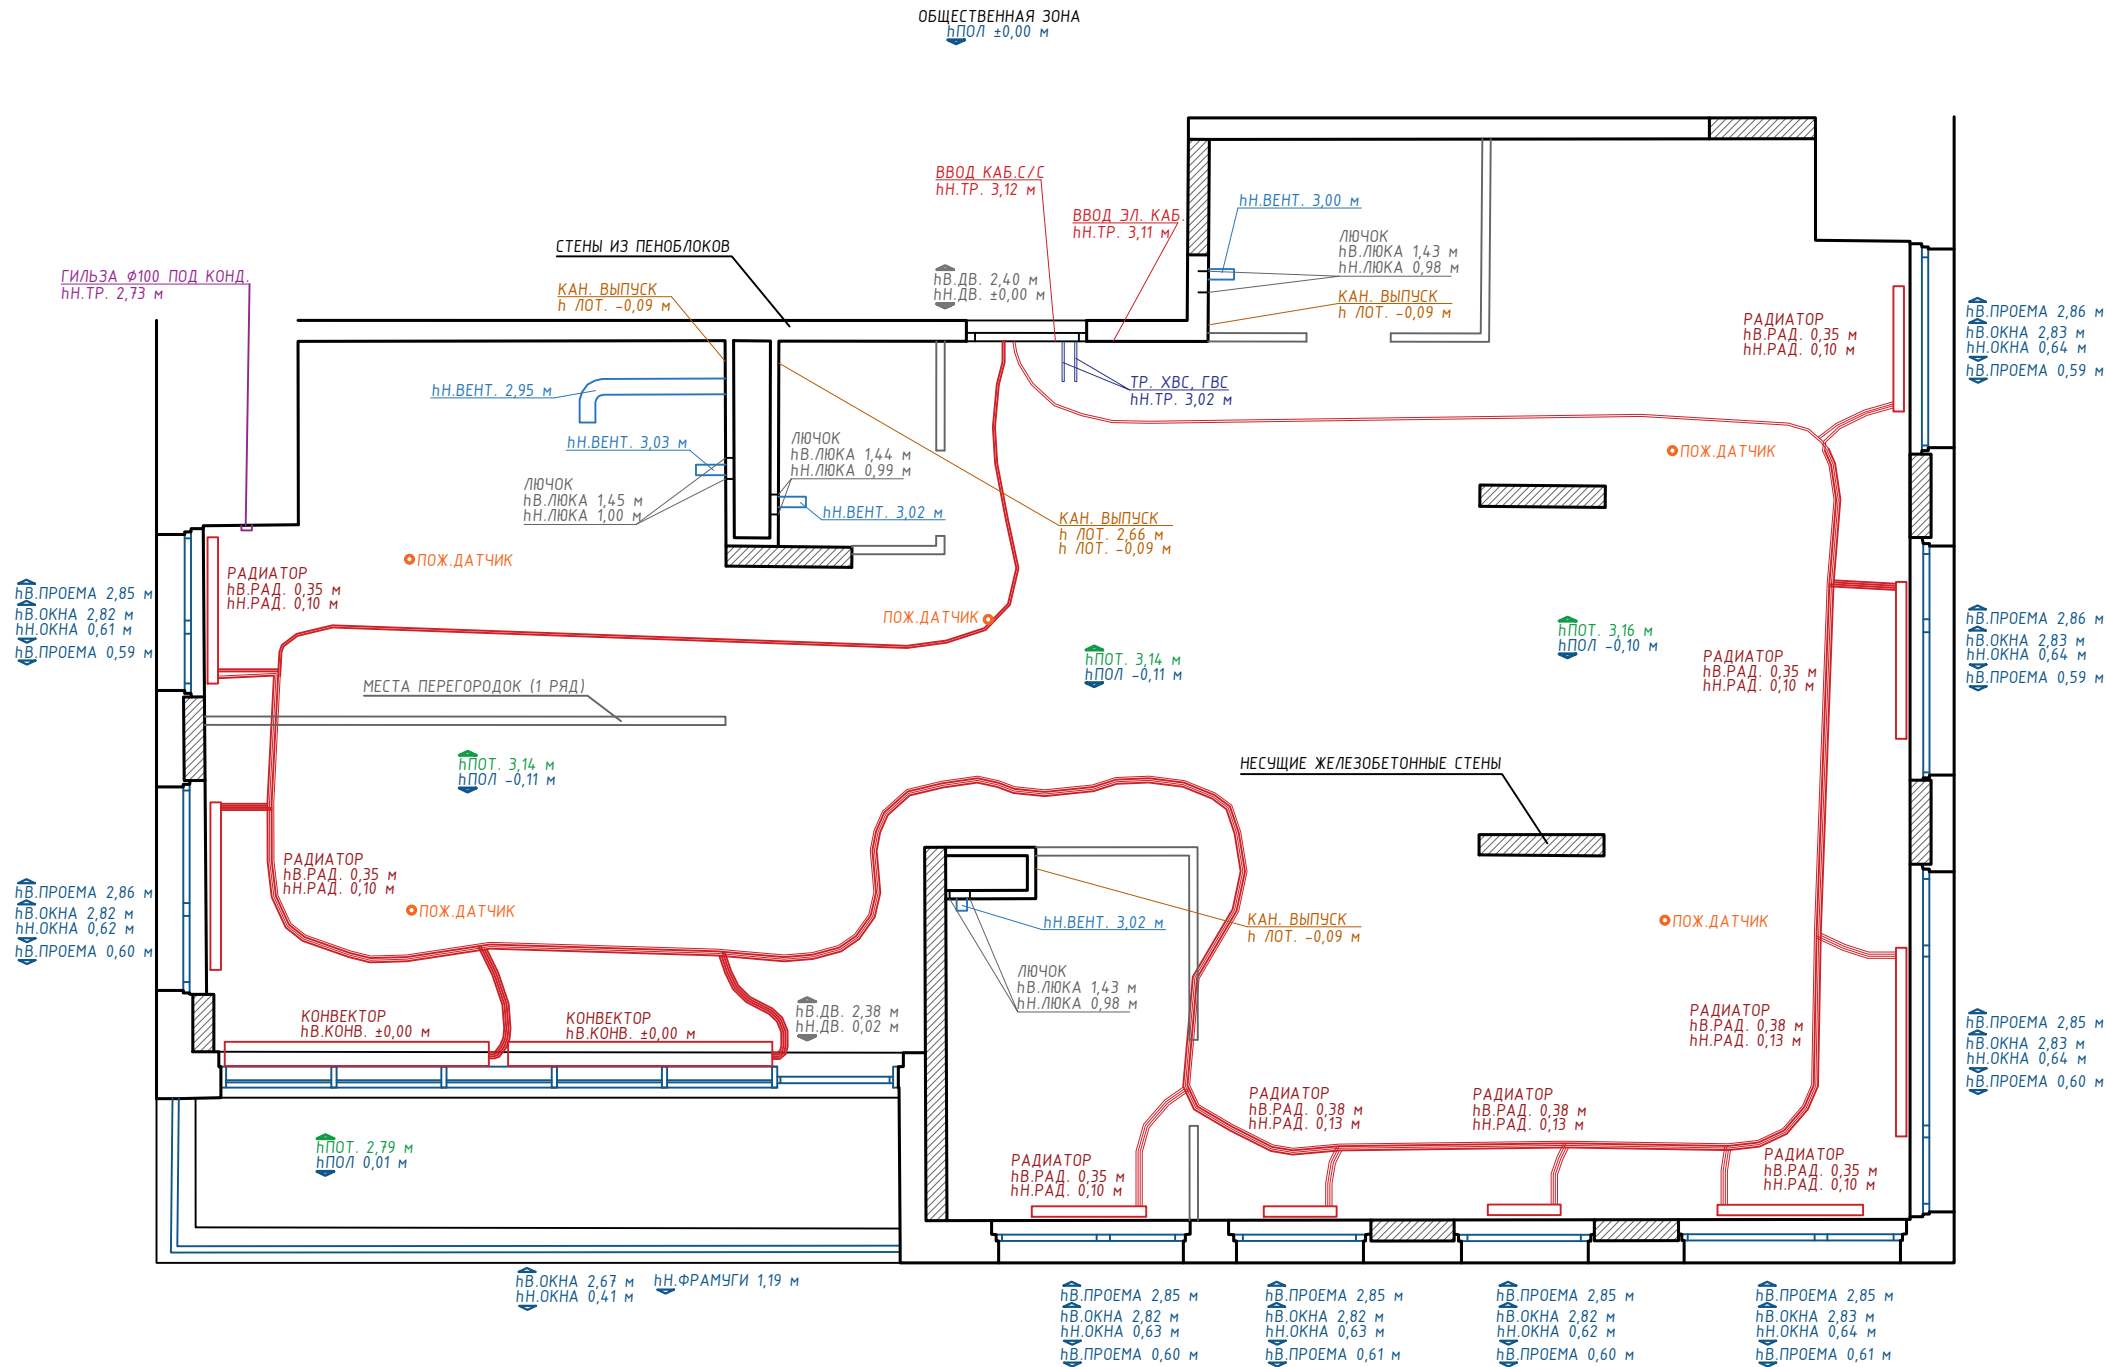

ПЛОЩАДЬ КВАРТИРЫ:

Площадь квартиры, м²: 133,6
Площадь лоджии, м²: 9,0
Общая площадь квартиры, м²: 142,6

УСЛОВНЫЕ ОБОЗНАЧЕНИЯ:

- Высотные отметки характерных конструктивных и технологических элементов здания
- Стены и колонны железобетонные несущие
- Стены из пеноблоков и кирпича
- Места установки перегородок (1 ряд)
- Трубы отопления
- Трубы ГВС, ХВС
- Вентиляция
- Окна и витражи

ПРИМЕЧАНИЯ:

Данный чертеж получен в результате инженерно-геодезической исполнительной съемки помещений. Плано-высотное положение несущих и ограждающих конструкций, а также архитектурных и технологических элементов определялось посредством тахеометрической инженерно-геодезической съемки электронным тахеометром;
Съемка произведена электронным тахеометром Sokkia Topcon 550 RX-L (производство Японии);
Все высотные отметки указаны в метрах. За относительную отметку со значением ±0,00 м принята отметка чистого пола лестничной клетки возле входной двери;
Все размеры указаны в миллиметрах;
Инженерно-геодезическая съемка здания производилась 3 февраля 2026 года;
Все строительные конструкции показаны по состоянию на дату съемки;
В электронном виде масштаб чертежа 1000:1 (одна условная единица в пространстве модели чертежа AutoDesk AutoCAD соответствует одному миллиметру на местности);

МЕТРОЛОГИЧЕСКАЯ ПОВЕРКА
ЭЛЕКТРОННОГО ТАХЕОМЕТРА



ИНЖЕНЕРНО-ГЕОДЕЗИЧЕСКАЯ ДОКУМЕНТАЦИЯ

Москва, ул. Нижние Мневники, д. 7

Изм.	Лист	Фамилия	Подпись	Дата				
					Обмеры частных апартаментов			
					Стадия	Лист	Листов	
						1	1	
Инж.-геод.		Валтонен Д. А.		03.02.26	План квартиры			



ИП Валтонен Д. А.
+7 (915) 401-74-38
valtonen.d@gmail.com


Согласования:

Взам инв. №

Подпись и дата

Инв. № подл.

ОБМЕРНЫЙ ЧЕРТЕЖ

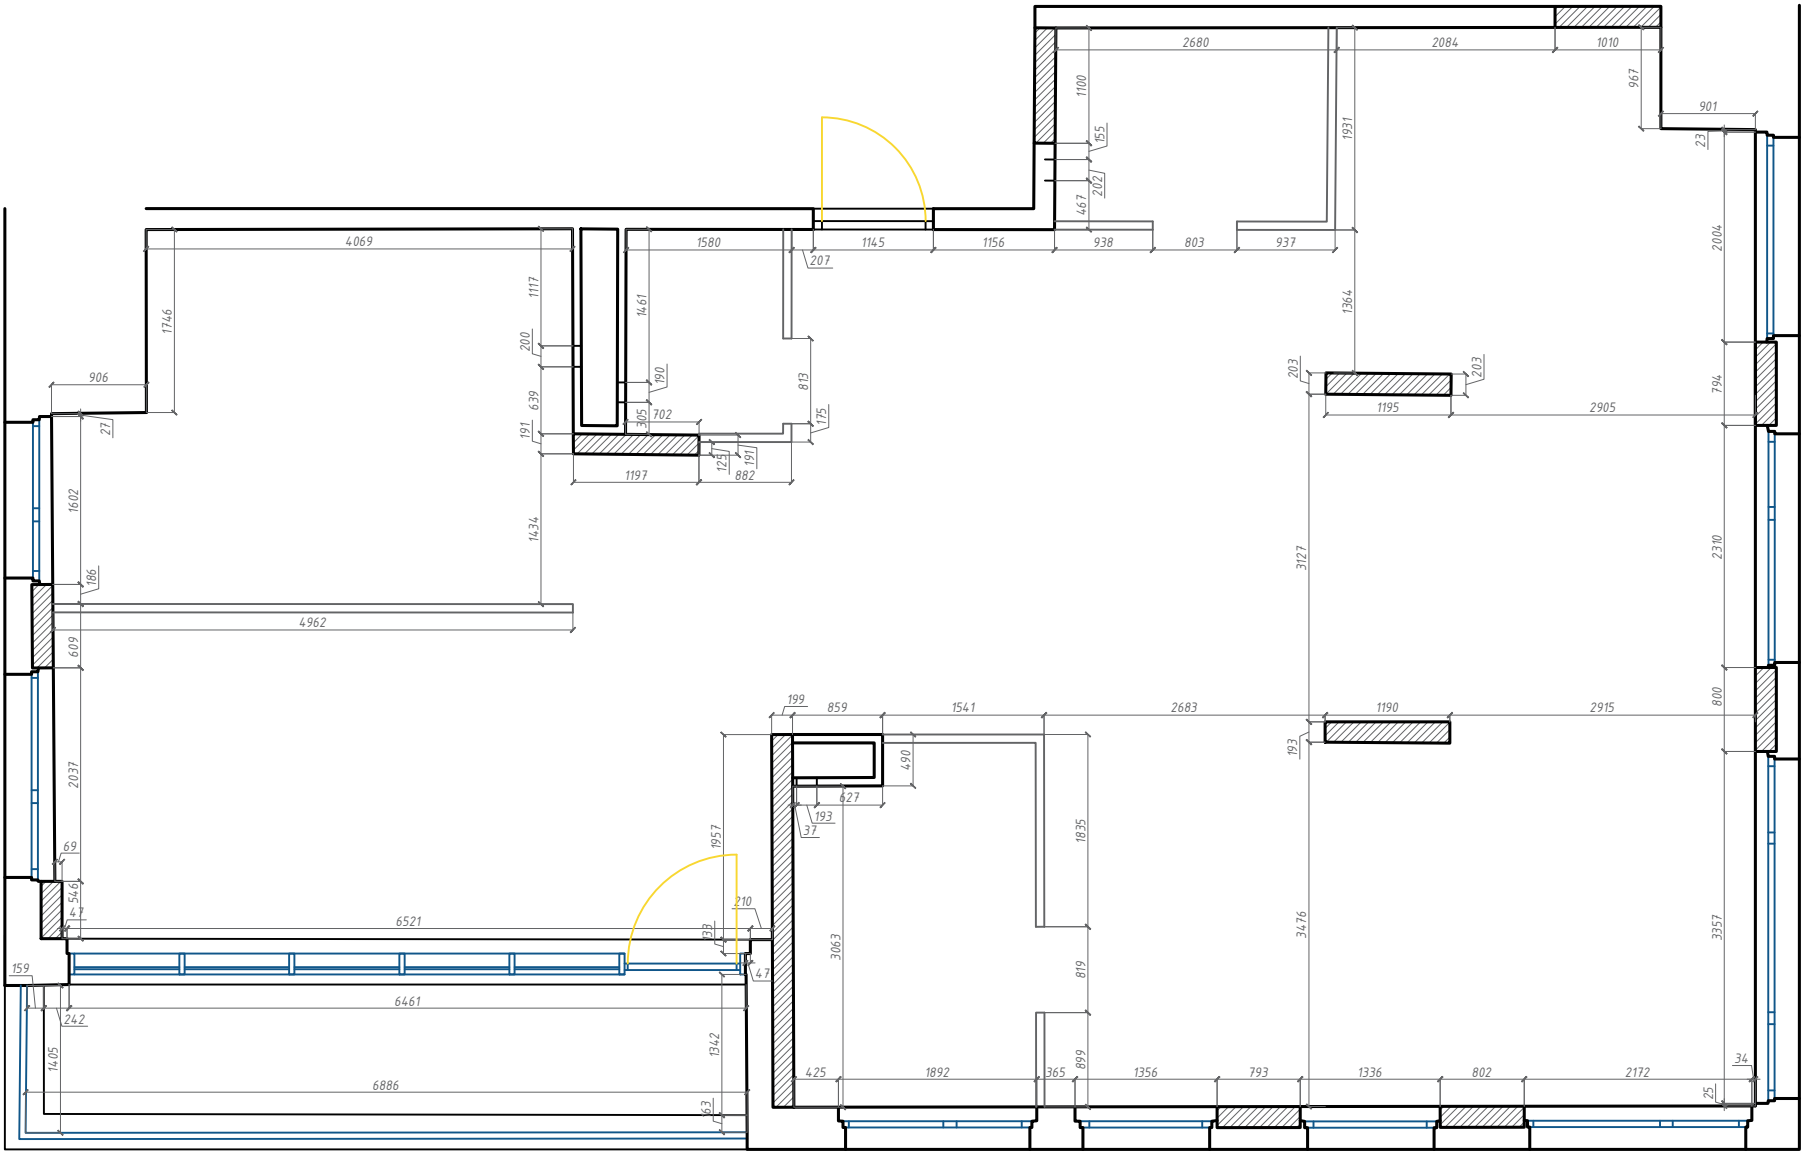

ПЛОЩАДЬ КВАРТИРЫ:

Площадь квартиры, м²: 133,6
Площадь лоджии, м²: 9,0
Общая площадь квартиры, м²: 142,6

УСЛОВНЫЕ ОБОЗНАЧЕНИЯ:

- ПВ ОКНА +3,02 м

ВН ОКНА +1,29 м

Высотные отметки характерных конструктивных и технологических элементов здания

Стены и колонны железобетонные несущие

Стены из пеноблоков и кирпича

Места установки перегородок (1 ряд)

Трубы отопления

Трубы ГВС, ХВС

Вентиляция

Окна и витражи


ПРИМЕЧАНИЯ:

Данный чертеж получен в результате инженерно-геодезической исполнительной съемки помещений. Плано-высотное положение несущих и ограждающих конструкций, а также архитектурных и технологических элементов определялось посредством тахеометрической инженерно-геодезической съемки электронным тахеометром;
Съемка произведена электронным тахеометром Sokkia Topcon 550 RX-L (производство Японии);
Все высотные отметки указаны в метрах. За относительную отметку со значением ±0,00 м принята отметка чистого пола лестничной клетки возле входной двери;
Все размеры указаны в миллиметрах;
Инженерно-геодезическая съемка здания производилась 3 февраля 2026 года;
Все строительные конструкции показаны по состоянию на дату съемки;
В электронном виде масштаб чертежа 1000:1 (одна условная единица в пространстве модели чертежа AutoDesk AutoCAD соответствует одному миллиметру на местности);

МЕТРОЛОГИЧЕСКАЯ ПОВЕРКА
ЭЛЕКТРОННОГО ТАХЕОМЕТРА



ИНЖЕНЕРНО-ГЕОДЕЗИЧЕСКАЯ ДОКУМЕНТАЦИЯ				
Москва, ул. Нижние Мневники, д. 7				
Изм.	Лист	Фамилия	Подпись	Дата
Обмеры частных апартаментов			Стадия	Лист
				1
Обмерный чертеж			Листов	
			1	
Инж.-геод.	Валтонен Д. А.		03.02.26	
			ИП Валтонен Д. А. +7 (915) 401-74-38 valtonen.d@gmail.com	

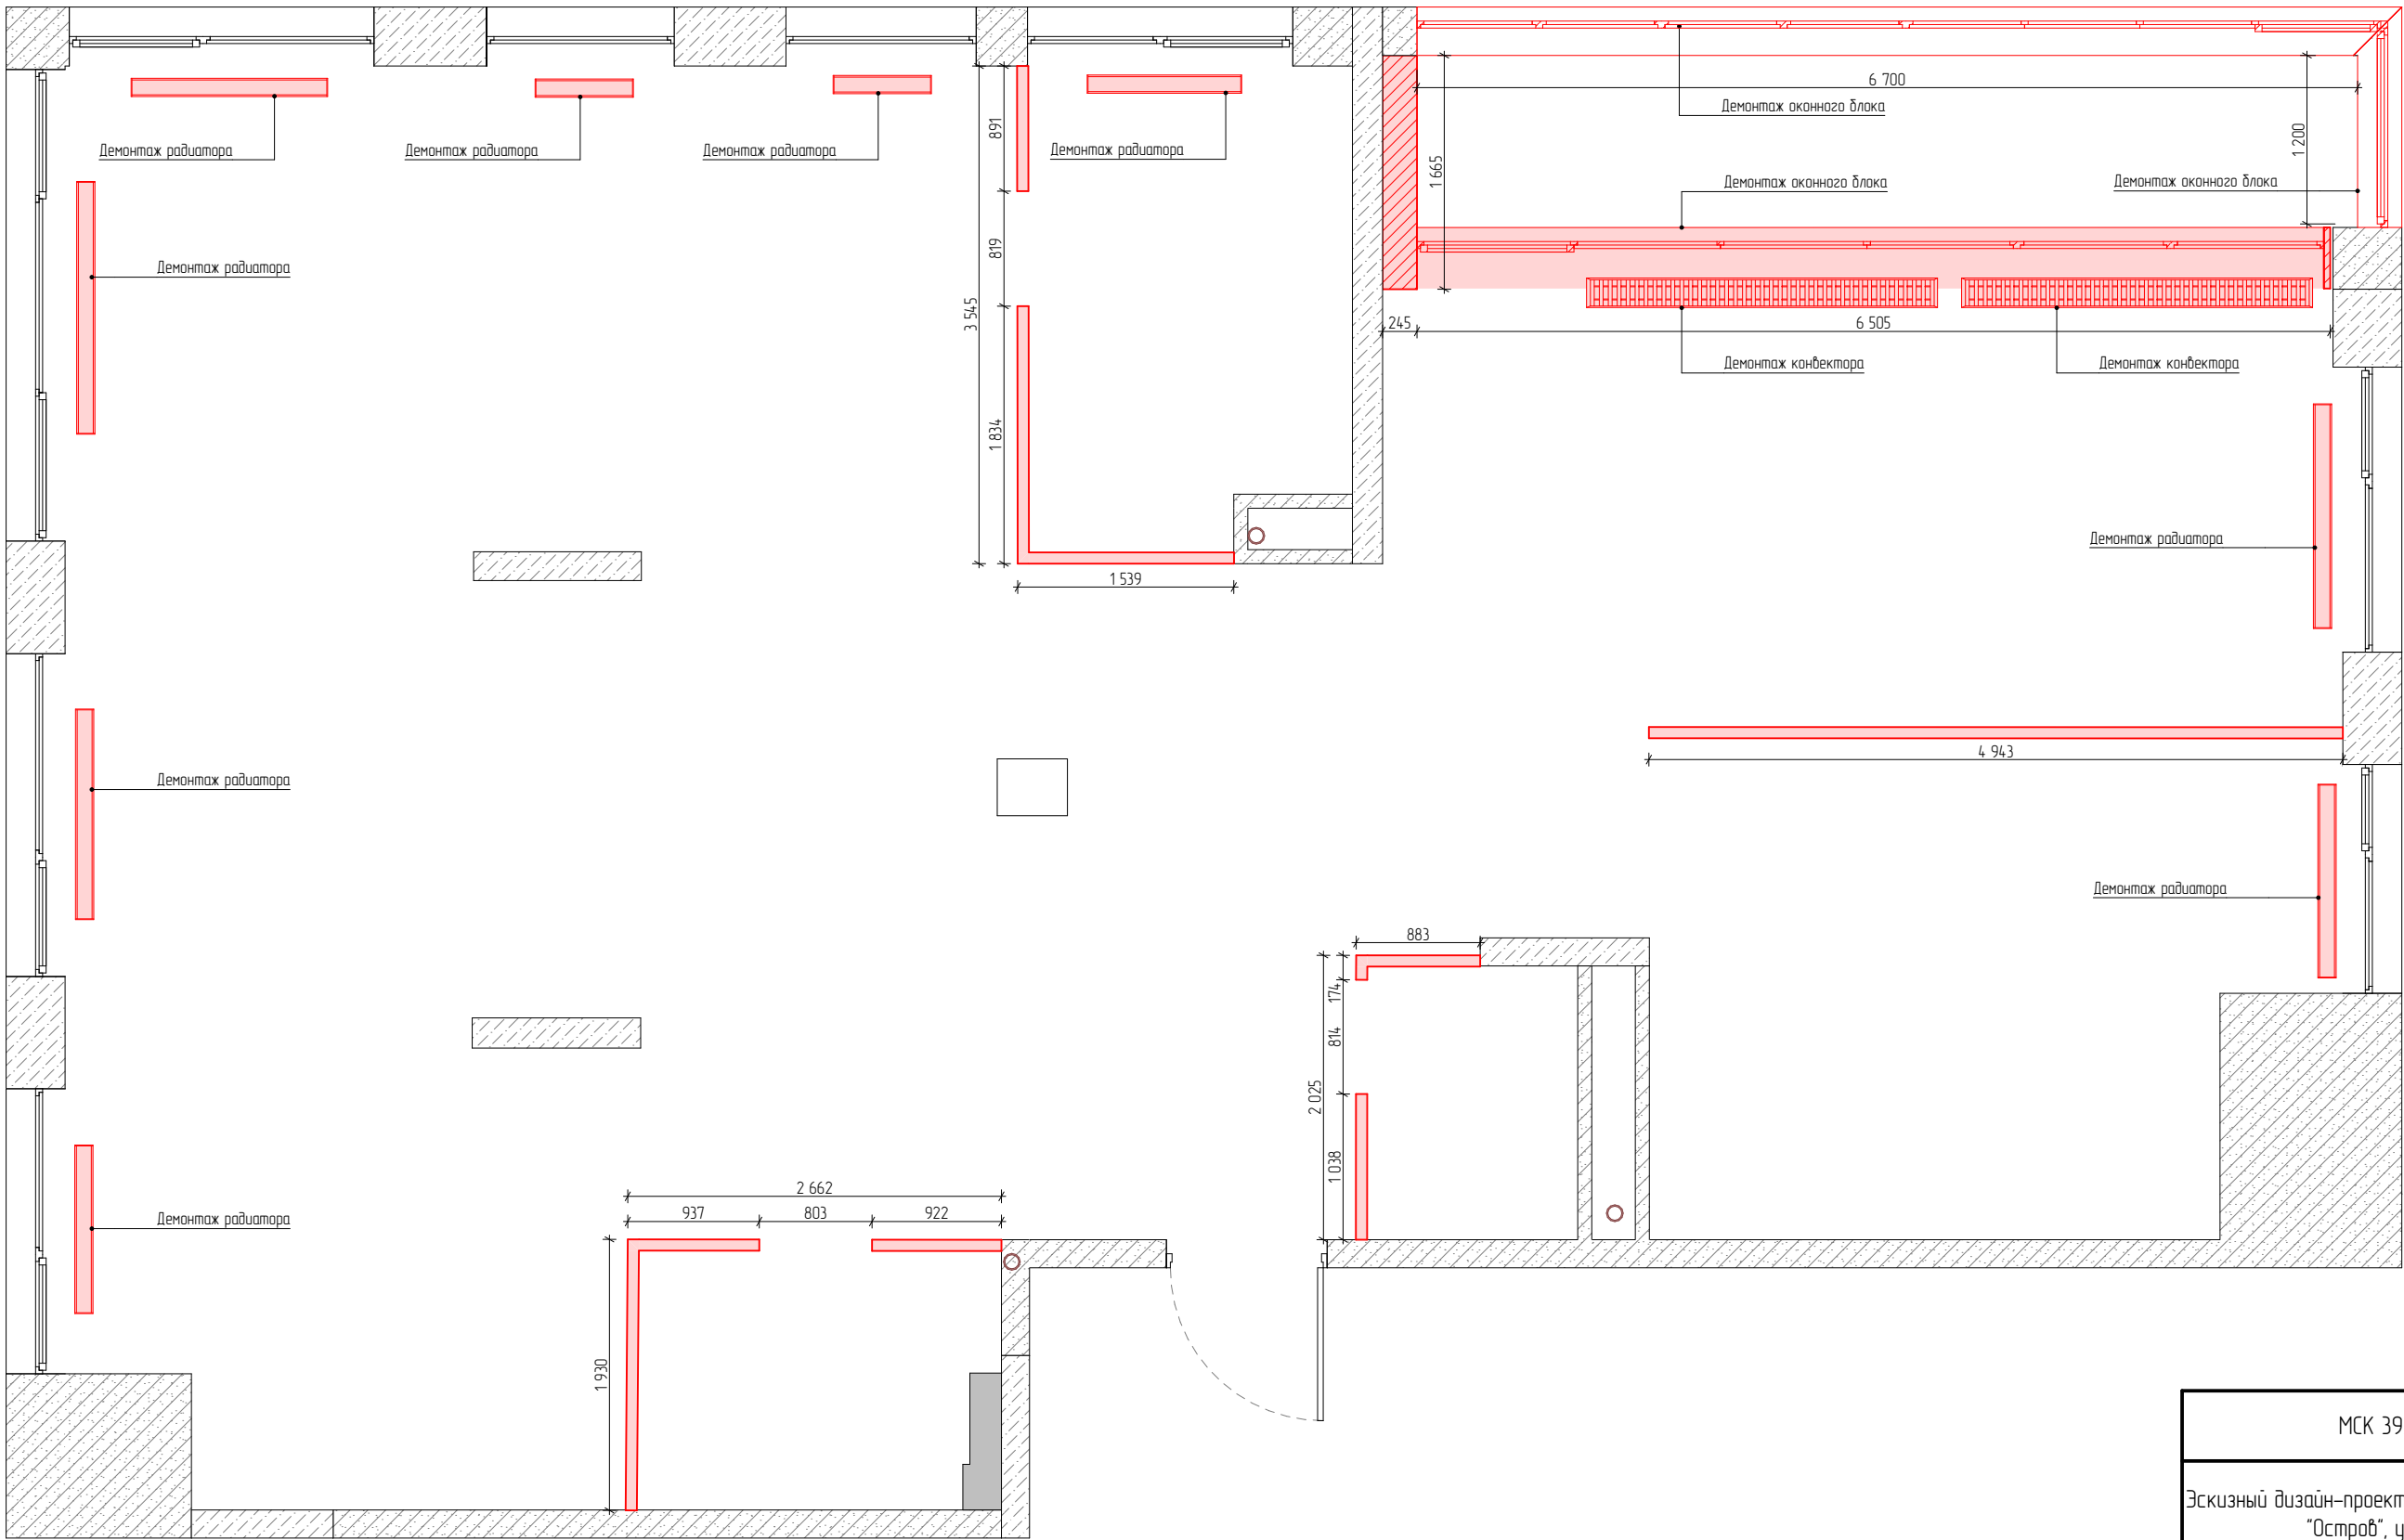


Условные обозначения:

- Демонтаж конструкций намеченных стен
- Конструкции стен из газобетонных блоков
- Сущ. коньектор отопления
- Сущ. радиатор отопления

Примечания:

- Демонтаж стен и элементов производить после согласования с конструктором.
- Демонтаж балконного блока с окном выполнить только при условии установки теплой рамы.
- Замену окон уточнить по месту со специалистами по необходимости и требованию заказчика.

МСК 392.12.25-ЭП ПРЕМИУМ			
Эскизный дизайн-проект интерьера квартиры в г. Москва ЖК "Остров", ул. Нижние Мневники д. 7			
План демонтажа стен и элементов			
Дизайнер интерьера №1 Александр Батеньков	Стадия	Лист	Листов
	ЭП	05	120
		Подп.	Дата
ГАП	Батеньков А.С.		
Гл. дизайнер	Власова В.А.		
Гл. проектиров.	Луныкова В.Н.		

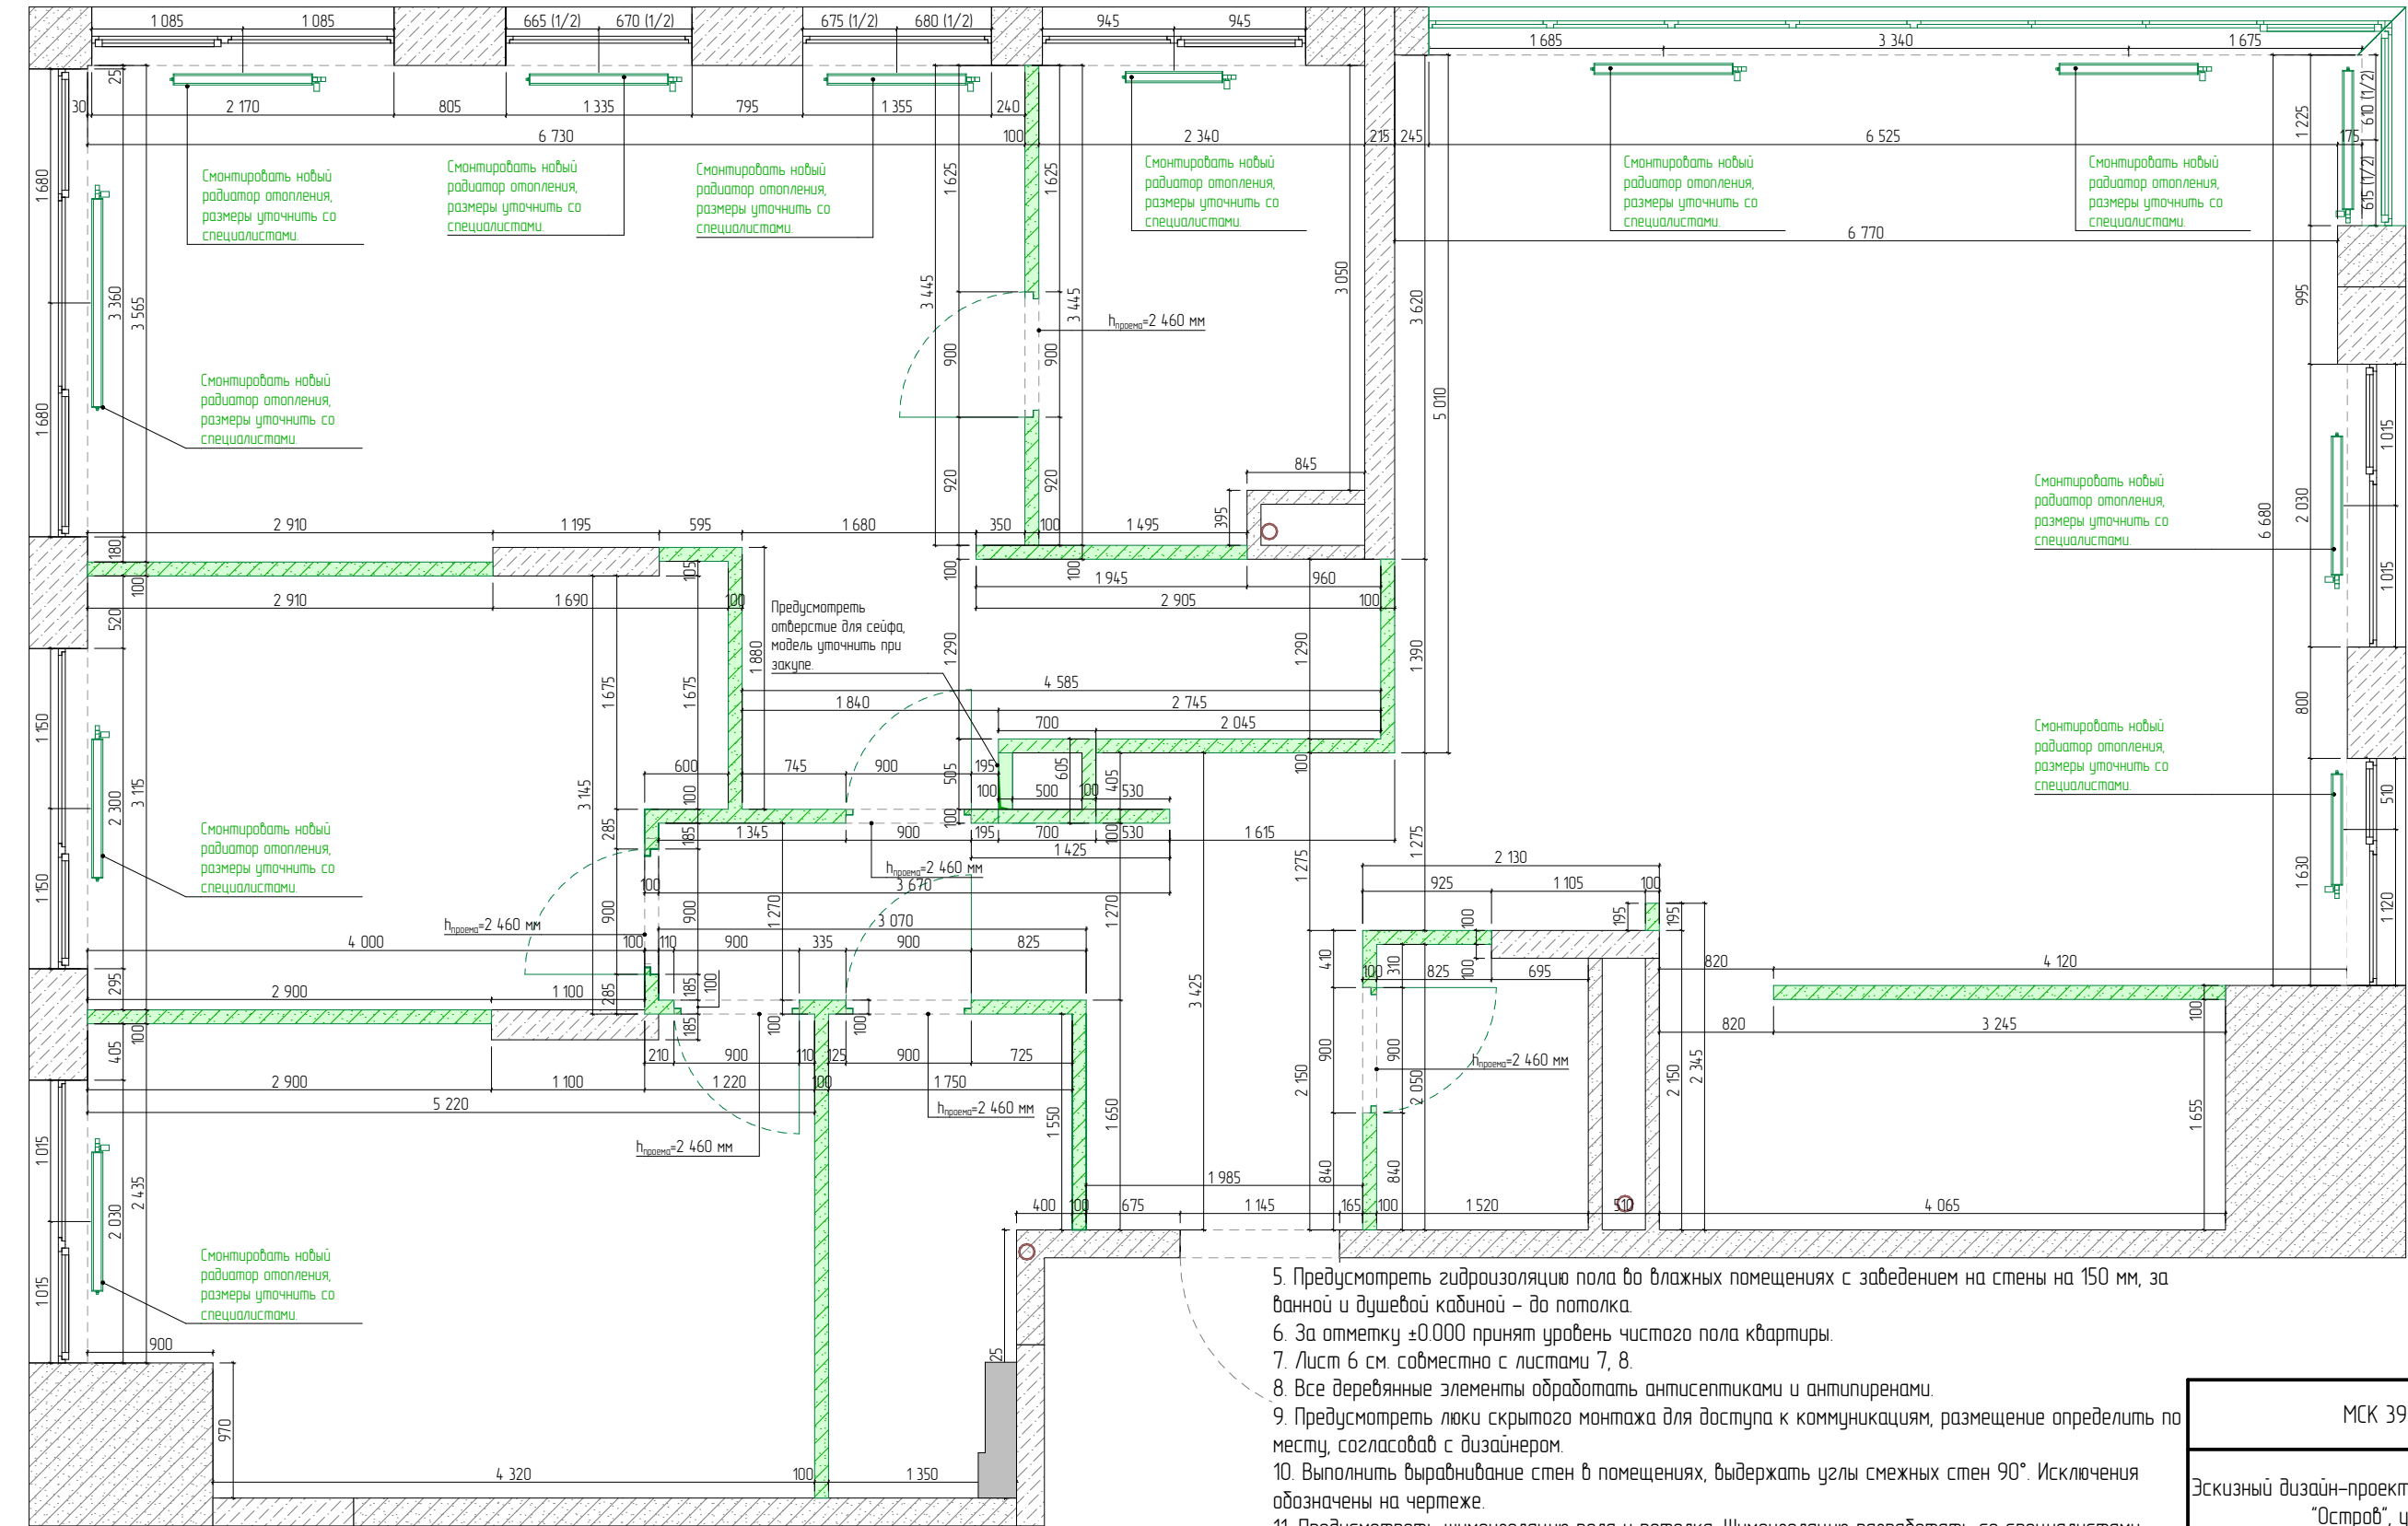

Примечания:

Условные обозначения:

- Конструкции стен из газобетонных блоков
- Конструкция стен из ж/бетона
- Монтаж конструкций из газобетонных блоков (100 мм)
- Монтаж монолитной стены (100 мм)
- Существующие коммуникации (стояки)
- Монтаж радиатора отопления

- Высоту помещений до плиты перекрытия принимаем 3140 мм. Уточнить после выравнивания и определения уровня чистого пола во всех помещениях объекта (на выравнивание и устройство чистого пола закладываем 110* мм).
- Во влажных помещениях перегородки и конструкции выполнить из акдапанелей.
- Размеры и характеристики радиаторов отопления согласовать со специалистами, предусмотреть терморегуляторы.
- Высоту проемов выполнить 2460 мм от уровня чистого пола. Уточнить после подбора и согласования модели дверей. Исключения указаны на чертеже выносной надписью.


- Предусмотреть гидроизоляцию пола во влажных помещениях с заведением на стены на 150 мм, за ванной и душевой кабиной – до потолка.
- За отметку ±0.000 принят уровень чистого пола квартиры.
- Лист 6 см. совместно с листами 7, 8.
- Все деревянные элементы обработать антисептиками и антипиренами.
- Предусмотреть люки скрытого монтажа для доступа к коммуникациям, размещение определить по месту, согласовав с дизайнером.
- Выполнить выравнивание стен в помещениях, выдержать углы смежных стен 90°. Исключения обозначены на чертеже.
- Предусмотреть шумоизоляцию пола и потолка. Шумоизоляцию разработать со специалистами, уточнить состав и толщину слоев шумоизоляционных материалов. Уточнить необходимость устройства с заказчиком. (при необходимости по ТЗ.)
- Конструкцию стены за унитазом с бачком скрытого монтажа зашить после установки инсталляции (бачка).
- Выполнить армирование конструкций стен стеклотканевой армирующей сеткой с ячейкой 5х5 мм для предотвращения растрескивания оштукатуренных поверхностей (места где нет отделки обоями и керамической плиткой).
- За отметку чистого пола квартиры принять отметку чистого пола межквартирной площадки этажа.
- Толщину выравнивания стен штукатуркой уточнить по месту.
- Выполнить шумоизоляцию канализационных и других стояков, согласовать со специалистами по месту.
- Подвод коммуникаций к радиаторам отопления согласовать по месту с дизайнером, при возможности выполнить из стены с нижним подключением.

МСК 392.12.25-ЭП ПРЕМИУМ

Эскизный дизайн-проект интерьера квартиры в г. Москва ЖК "Остров", ул. Нижние Мневники д. 7

Схема монтажа стен из газобетонных блоков

Дизайнер интерьера  Александр Батеньков	Стадия	Лист	Листов
	ЭП	06	120
		Подп.	Дата
ГАП	Батеньков А.С.		
Гл. дизайнер	Власова В.А.		
Гл. проектиров.	Лунькова В.Н.		

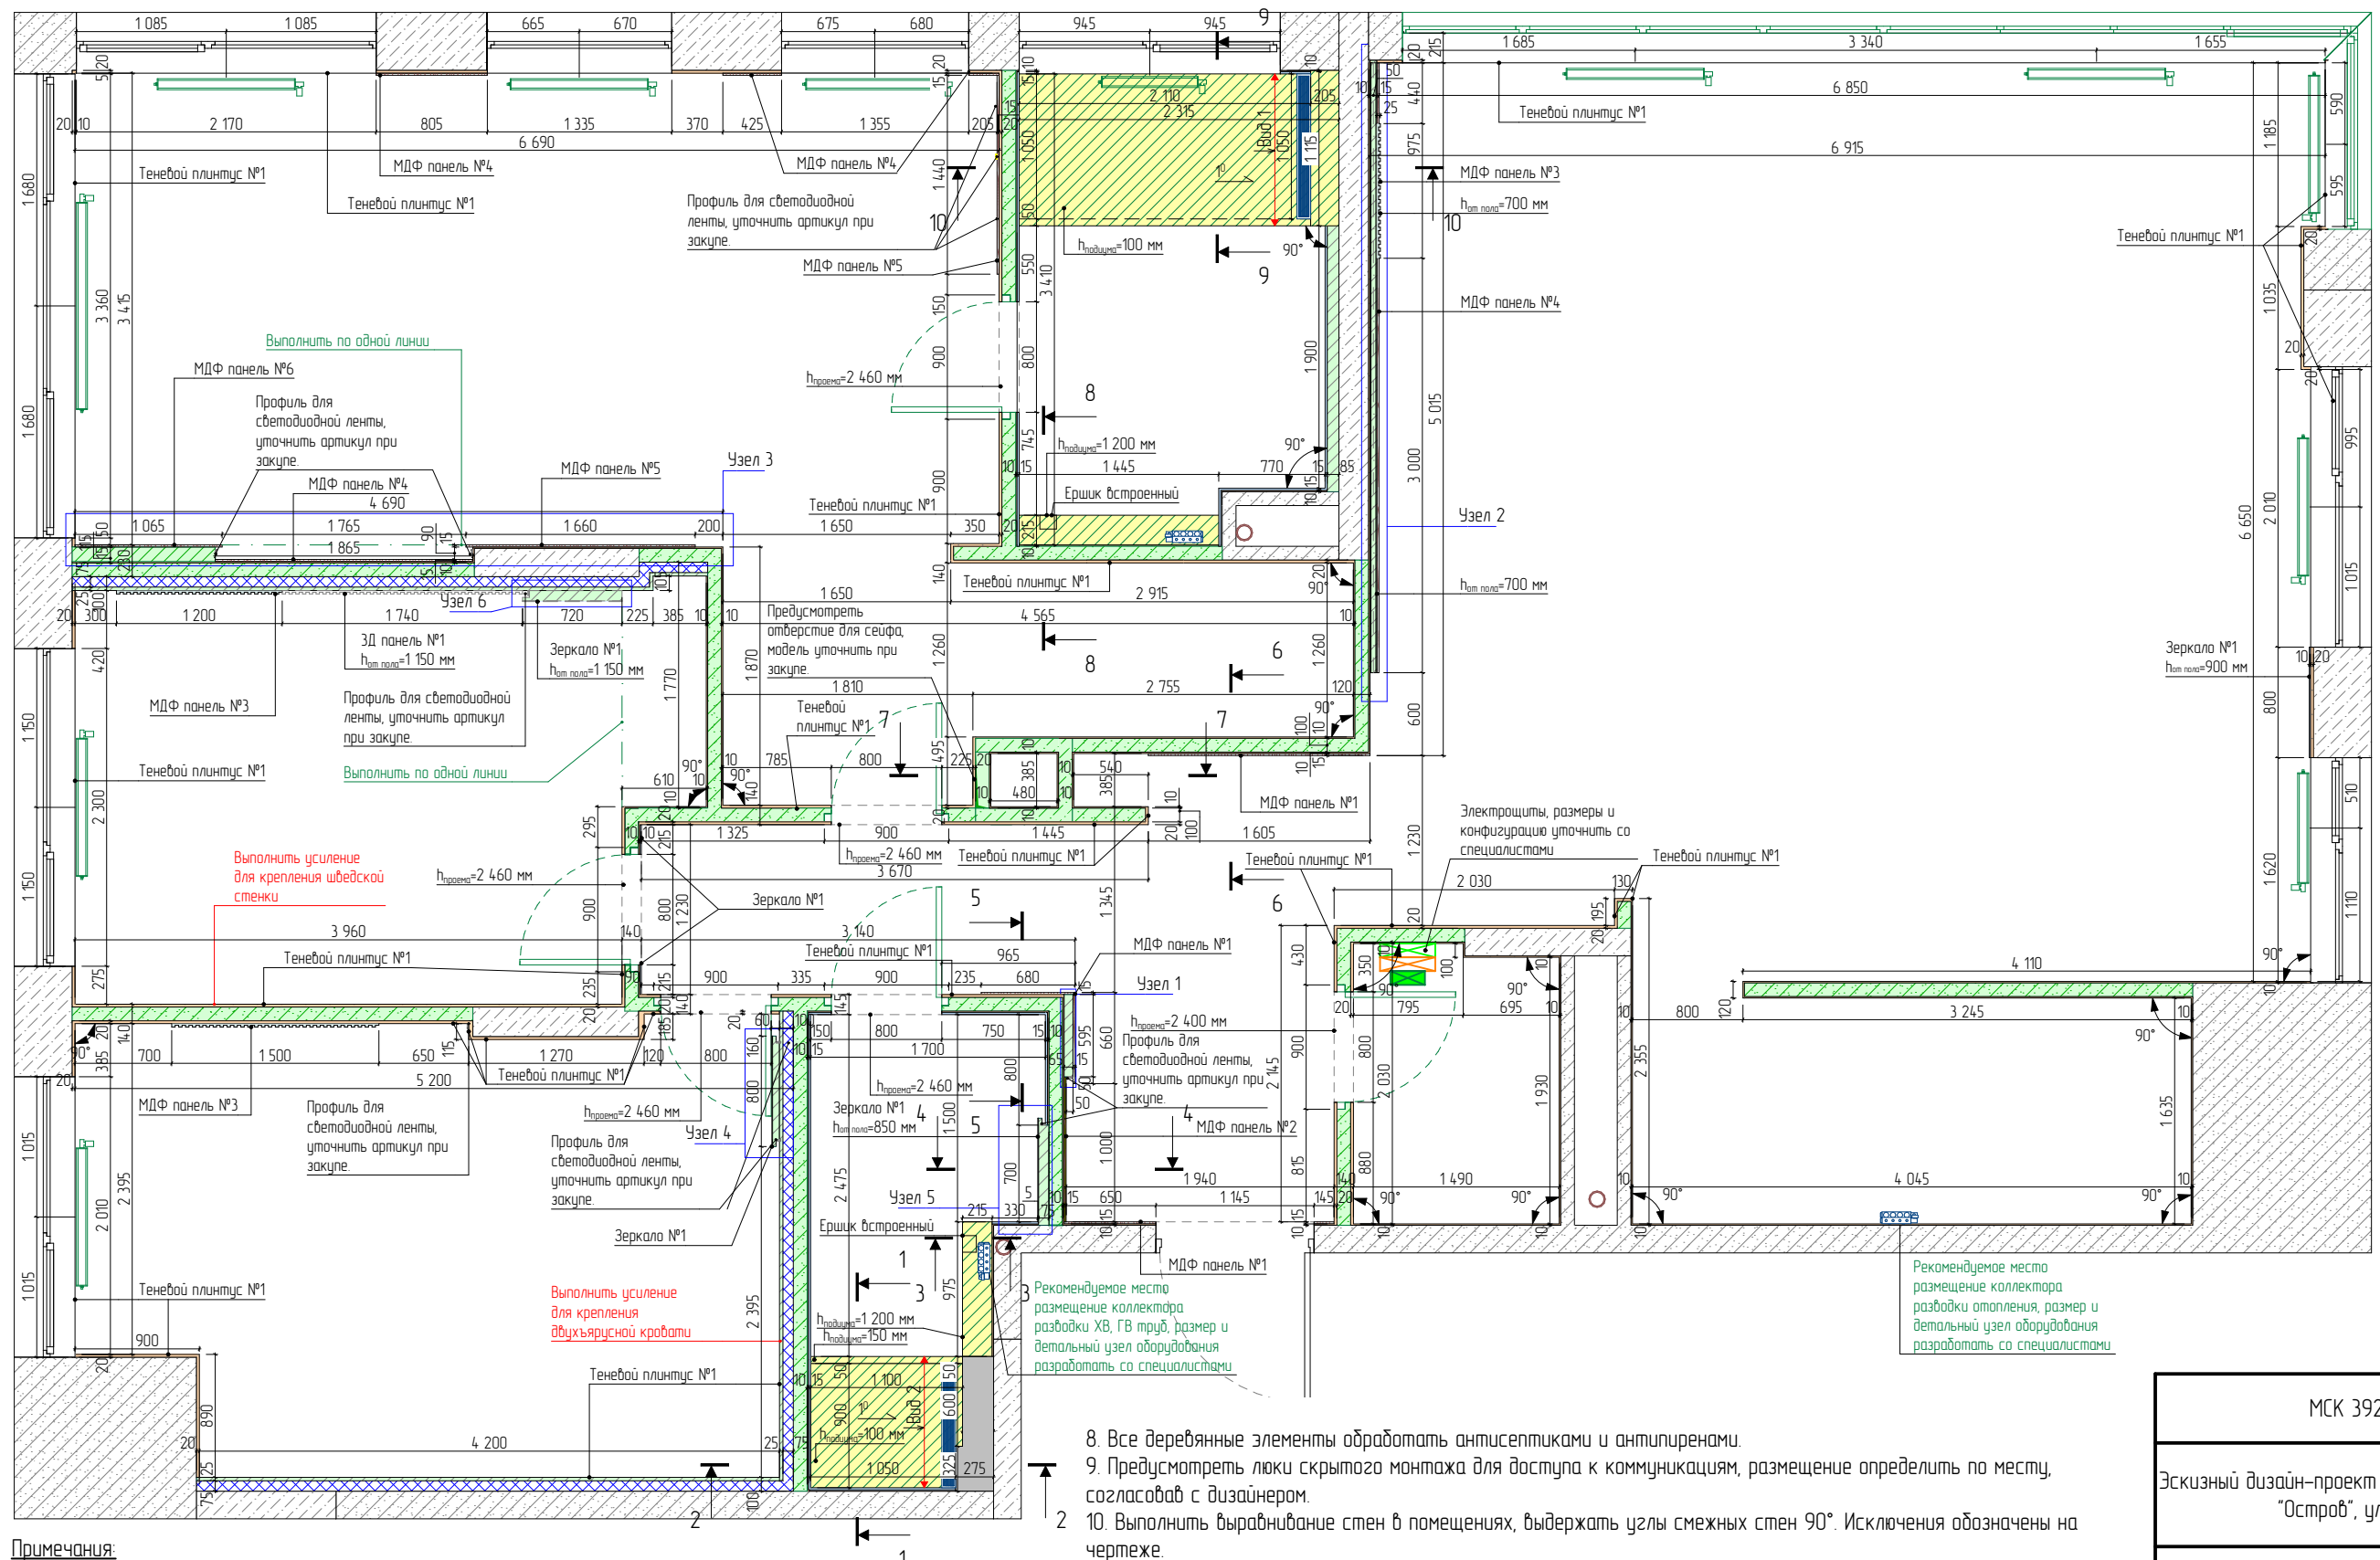

- Условные обозначения:
- Монтаж конструкция из ж/б бетона (100 мм)
 - Монтаж радиатора отопления
 - Конструкции стен из газобетонных блоков
 - Коллектор ГВС, ХВС
 - Слаботочный щит
 - Электро щит
 - wi-fi оборудование
 - Монтаж подиума (подиума дана с учетом чистовой отделки)
 - Монтаж МДФ панелей
 - Монтаж выравнивающей штукатурки под чистовую отделку (закладываем 10-20* мм)
 - Монтаж конструкций из ГКВЛ
 - Монтаж керамической плитки (керамогранита) с клеем (15-20* мм)
 - Монтаж зеркала с клеем (6-10* мм)
 - Шумоизоляция (75 мм)

Примечания:

- Высоту помещений до плиты перекрытия принимаем 3140 мм. Уточнить после выравнивания и определения уровня чистого пола во всех помещениях объекта (на выравнивание и устройство чистого пола закладываем 110* мм).
- * – размеры уточнить по месту после выполнения черновых отделочных работ.
- Во влажных помещениях перегородки и конструкции выполнять из аквипанелей.
- Размеры и характеристики радиаторов отопления согласовать со специалистами, предусмотреть терморегуляторы.
- Высоту проемов выполнять 2460 мм от уровня чистого пола. Уточнить после подбора и согласования модели дверей. Исключения указаны на чертеже выносной надписью.
- Предусмотреть гидроизоляцию пола во влажных помещениях с заведением на стены на 150 мм, за ванной и душевой кабиной – до потолка.
- За отметку ±0.000 принят уровень чистого пола квартиры.
- Лист 7 см. совместно с листами 6, 8, 9.


- Все деревянные элементы обработать антисептиками и антипиренами.
- Предусмотреть люки скрытого монтажа для доступа к коммуникациям, размещение определить по месту, согласовав с дизайнером.
- Выполнить выравнивание стен в помещениях, выдержать углы смежных стен 90°. Исключения обозначены на чертеже.
- Предусмотреть шумоизоляцию пола и потолка. Шумоизоляцию разработать со специалистами, уточнить состав и толщину слоев шумоизоляционных материалов. Уточнить необходимость устройства с заказчиком. (при необходимости по ТЗ.)
- Конструкция стены за унитазом с бачком скрытого монтажа зашить после установки инсталляции (бачка).
- Выполнить армирование конструкций стен стеклотканевой армирующей сеткой с ячейкой 5x5 мм для предотвращения растрескивания оштукатуренных поверхностей (места где нет отделки обоями и керамической плиткой).
- За отметку чистого пола квартиры принять отметку чистого пола межквартирной площадки этажа.
- Толщину выравнивания стен штукатуркой уточнить по месту.
- Выполнить шумоизоляцию канализационных и других стояков, согласовать со специалистами по месту.
- Подвод коммуникаций к радиаторам отопления согласовать по месту с дизайнером, при возможности выполнить из стены с нижним подключением.
- Расположение плинтуса скрытого монтажа см. лист 29.







МСК 392.12.25–ЭП ПРЕМИУМ

Эскизный дизайн–проект интерьера квартиры в г. Москва ЖК "Остров", ул. Нижние Мневники д. 7

План монтажа стен и элементов с учетом отделки.

Дизайнер интерьера №1 Александр Батеньков	Стадия	Лист	Листов
	ЭП	07	120
		Подп.	Дата
Г.АП	Батеньков А.С.		
Гл. дизайнер	Власова В.А.		
Гл. проектиров.	Луцькова В.Н.		

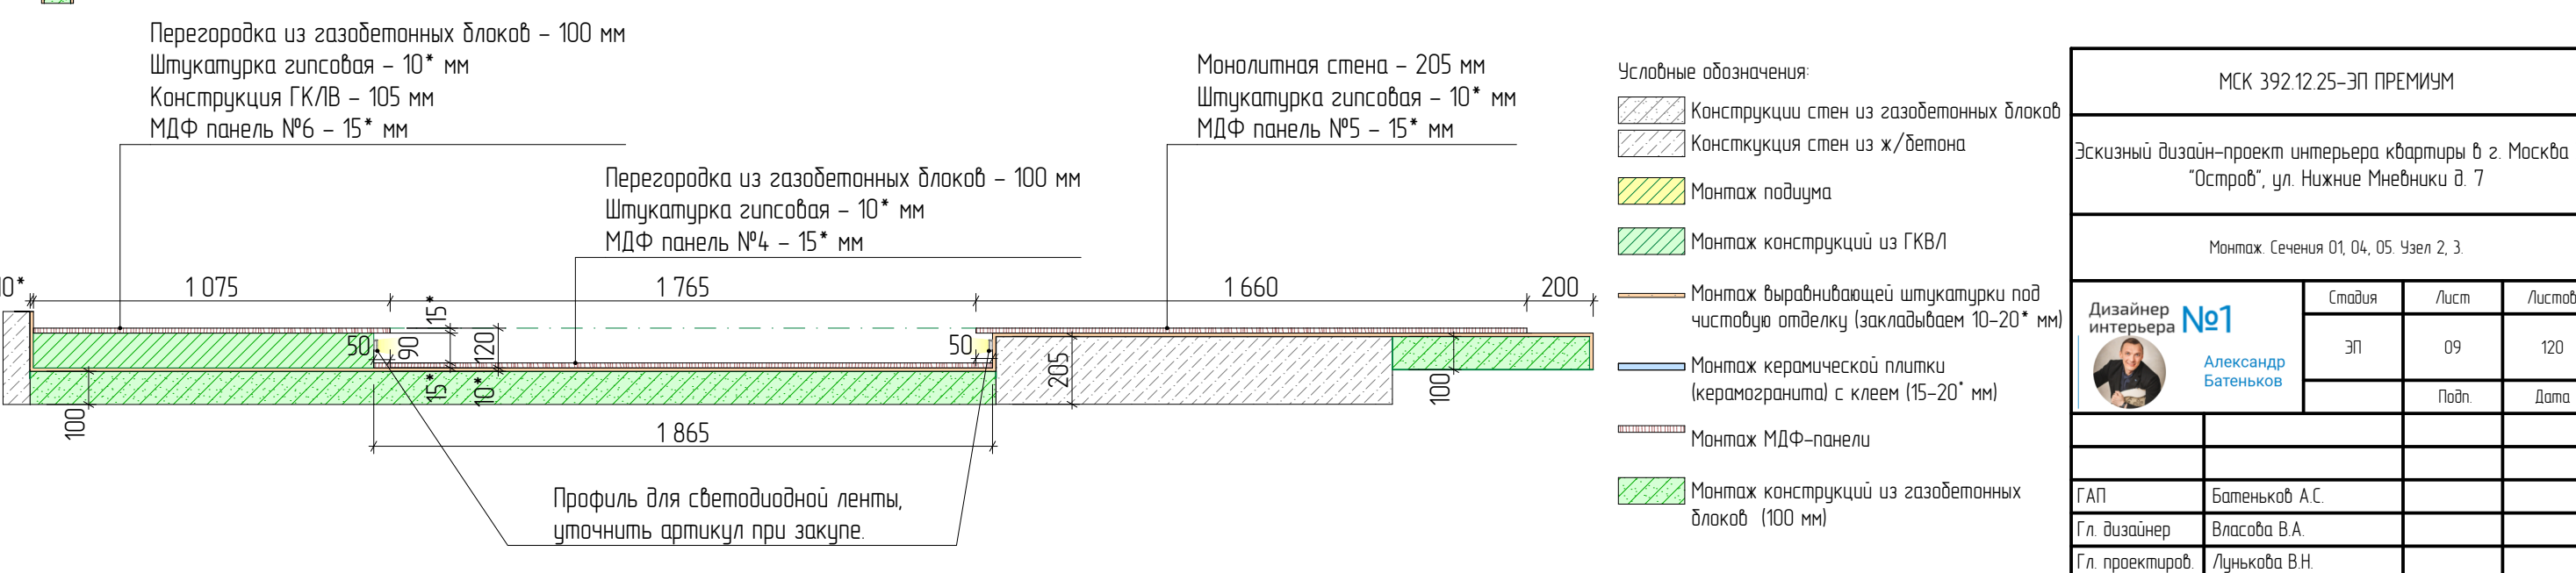


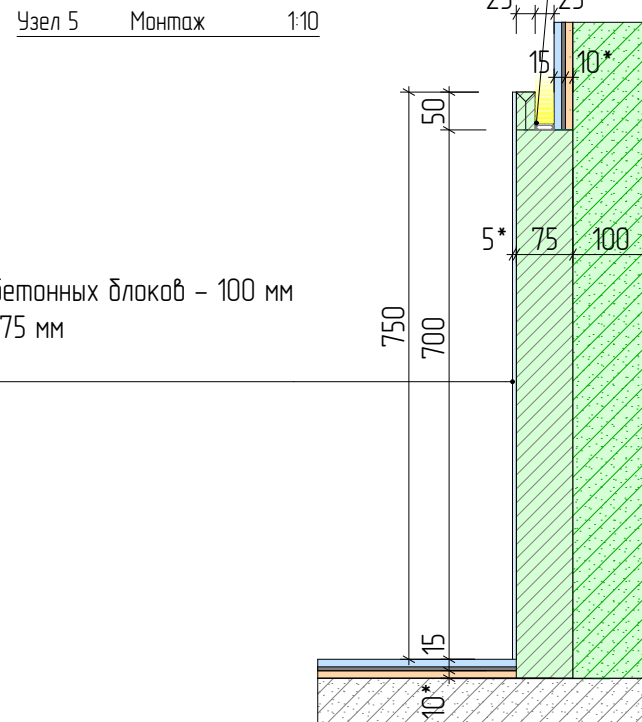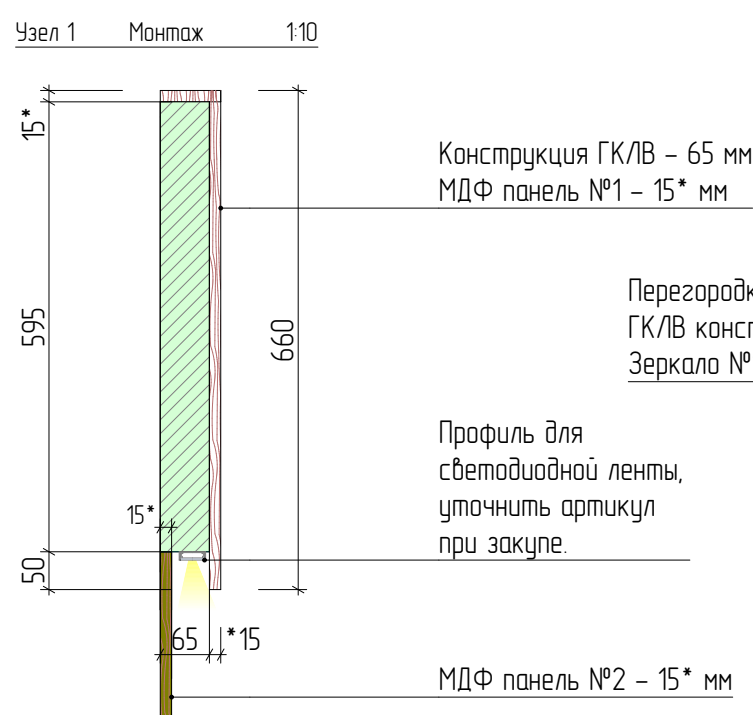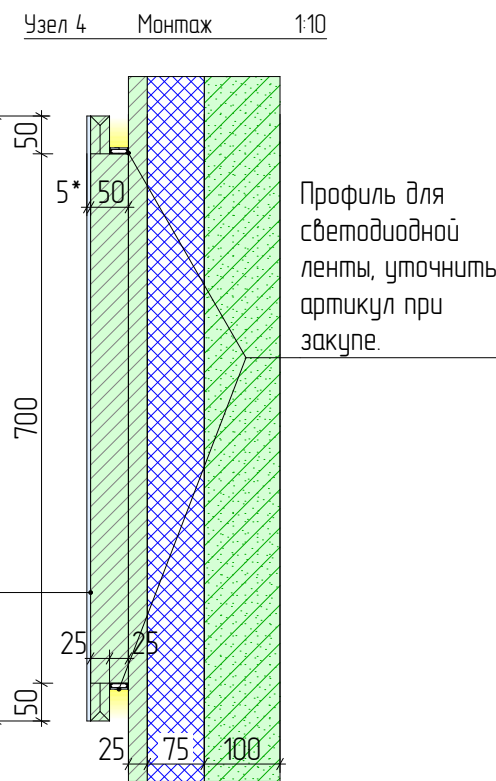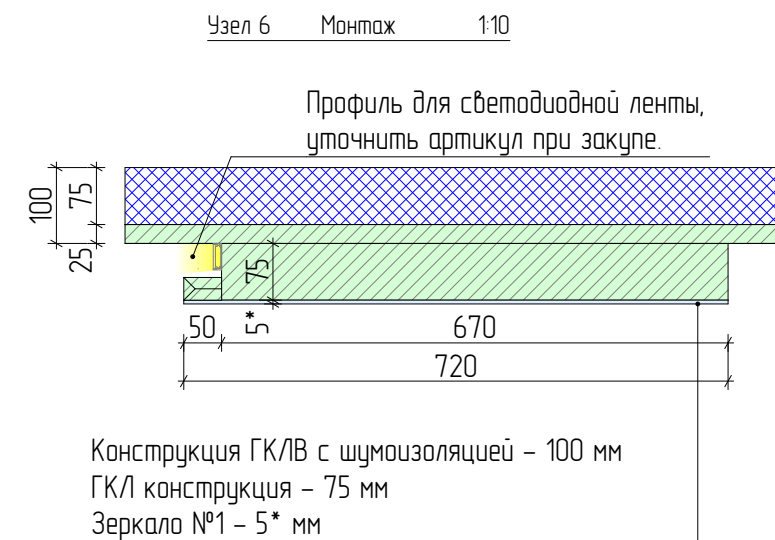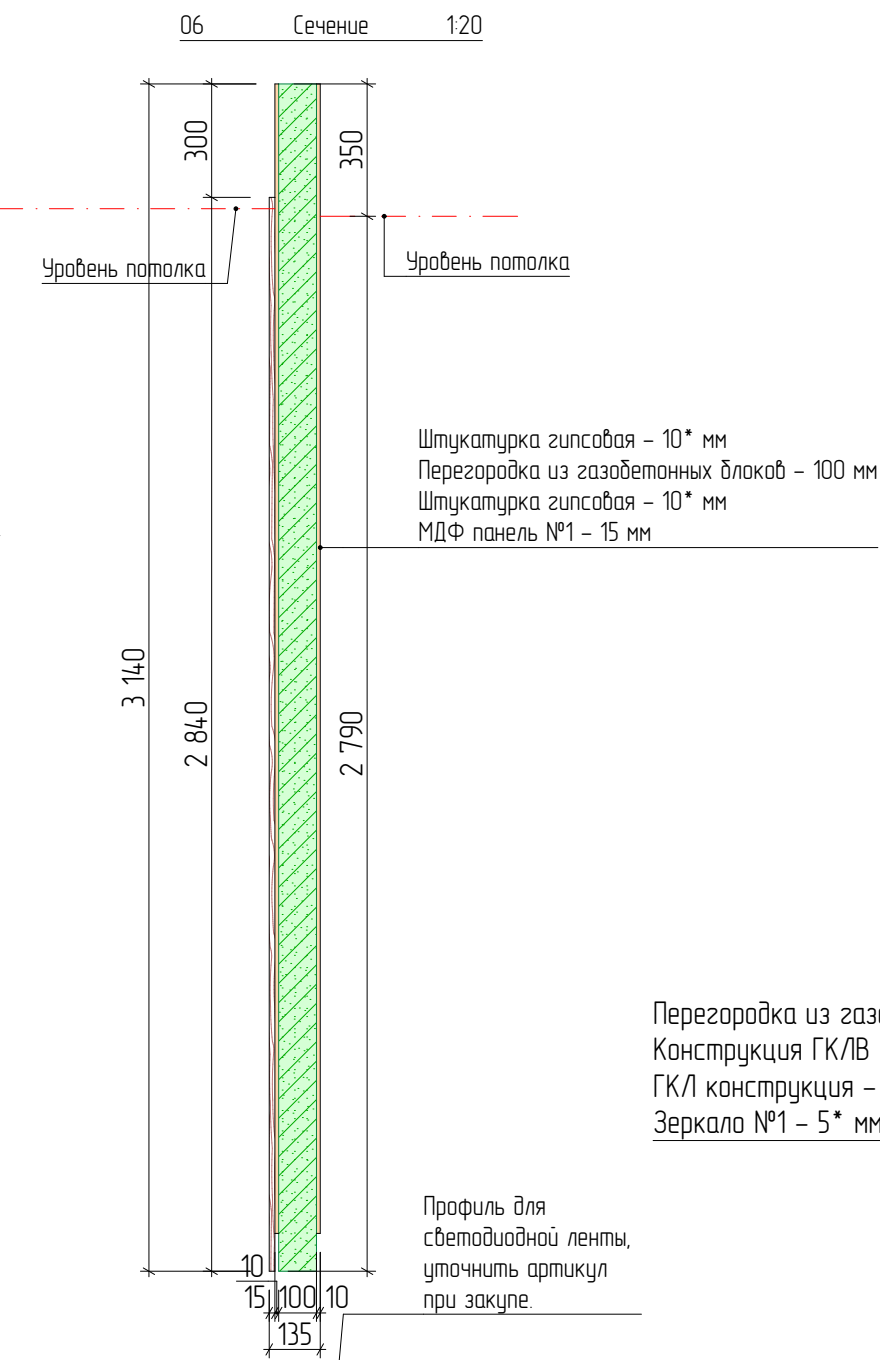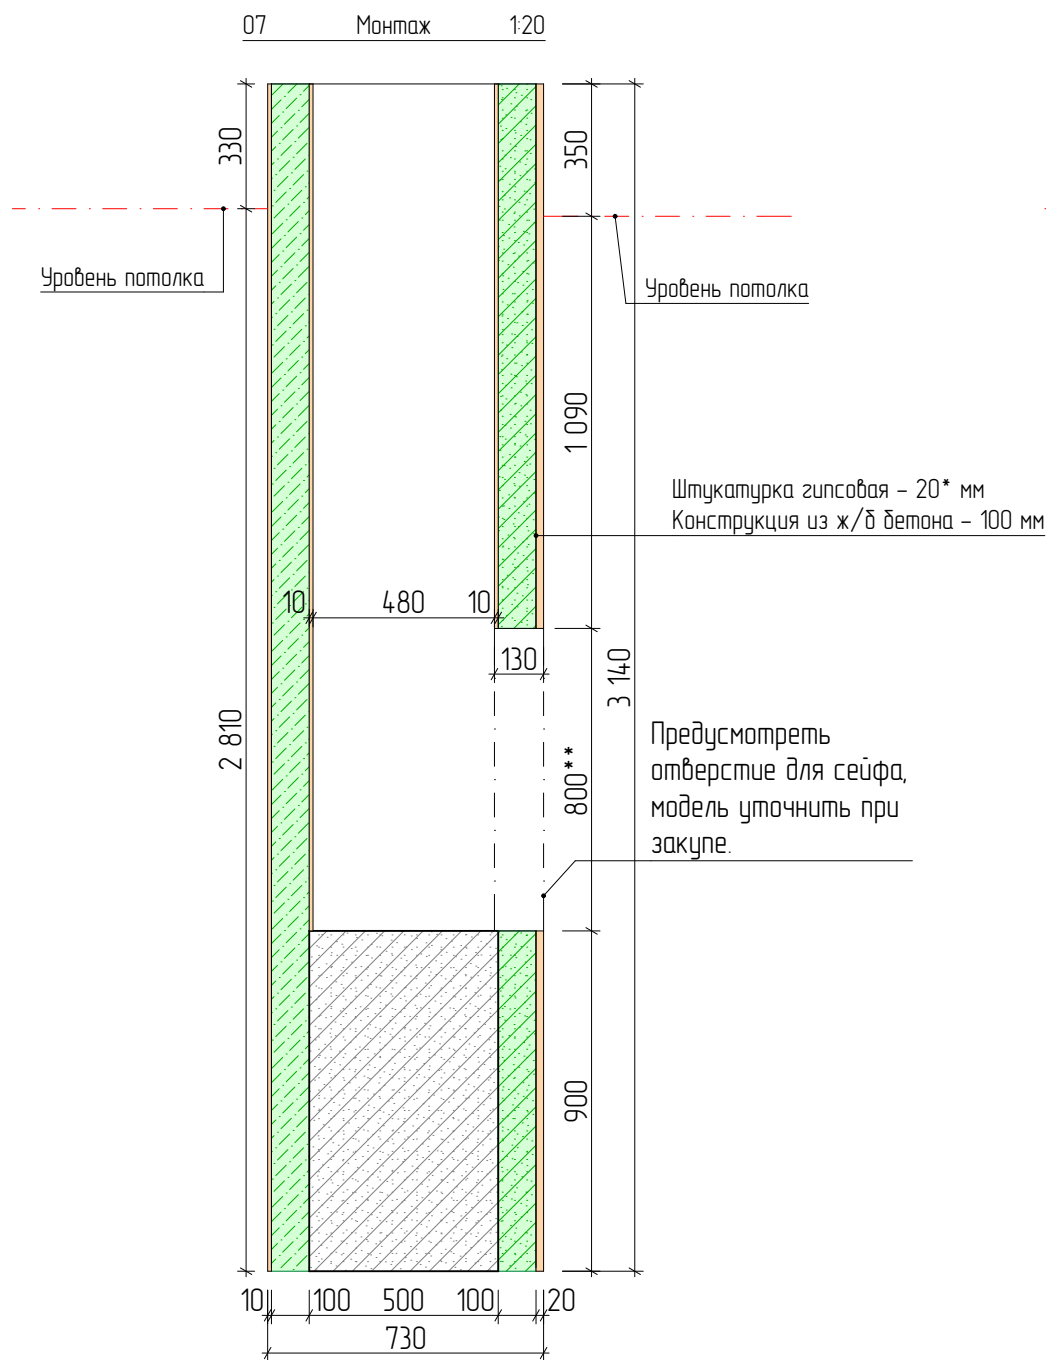

Условные обозначения:

- Конструкции стен из газобетонных блоков
- Конструкция стен из ж/бетона
- Монтаж подиума
- Монтаж конструкций из ГКВЛ
- Монтаж выравнивающей штукатурки под чистовую отделку (закладываем 10-20* мм)
- Монтаж керамической плитки (керамогранита) с клеем (15-20* мм)
- Монтаж МДФ-панели
- Монтаж конструкций из газобетонных блоков (100 мм)
- Шумоизоляция (75 мм)

МСК 392.12.25-ЭП ПРЕМИУМ			
Эскизный дизайн-проект интерьера квартиры в г. Москва ЖК "Остров", ул. Нижние Мневники д. 7			
Монтаж. Сечения 06, 07. Узел 1, 4, 5, 6.			
Дизайнер интерьера  Александр Батеньков	Стадия	Лист	Листов
	ЭП	10	120
		Подп.	Дата
ГАП	Батеньков А.С.		
Гл. дизайнер	Власова В.А.		
Гл. проектиров.	Луныкова В.Н.		

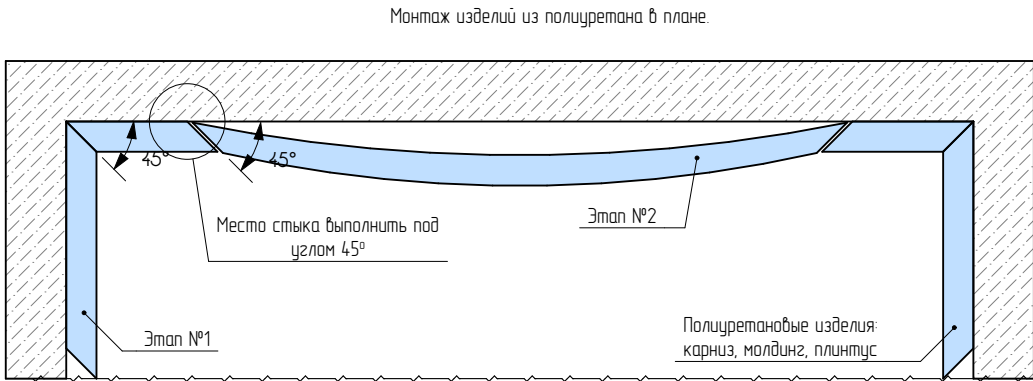


Этапы и указания монтажа полиуретана:






1. Первоначально монтировать угловые элементы изделия.
2. Смонтировать среднюю часть: полиуретан отрезать на 2–3 мм больше чем фактически, заводить как распорку с усилением.
3. Все запилы, в т.ч. и на прямых участках, выполнять под углом 45°.
4. Карнизы крепить к стене гвоздями (тяжелые элементы – саморезами).
5. В узлах стыков полиуретана промазывать специальным “стыковочным клеем”.
6. При монтаже полиуретановых изделий не допустимы щели.
7. *–толщину клеевого раствора и декоративного кирпича (керамической плитки, камня, керамогранита) уточнить по факту закупа.
8. **– набрать толщину отделки под изделие из полиуретана слоями ГКЛ.

Общие указания к выполнению ремонтно-строительных работ к проекту.

1. По факту обмера и факту выполнения работ по проекту допускаются расхождения до 20 мм.
2. Демонтаж стен и элементов конструкции выполнять после согласования с конструктором. Демонтировать существующую отделку помещений.
3. Уточнить высоту помещений после определения уровня чистого пола во всех помещениях.
4. * – размеры уточнить по месту.
5. Перегородки выполнить из гипсокартонных листов на металлическом каркасе толщиной 100, 125 мм.
6. Все высоты указаны от уровня чистого пола: ±0,000.
7. Размеры и характеристики радиаторов отопления согласовать со специалистами, предусмотреть терморегуляторы. Выводы коммуникаций для радиаторов отопления согласовать со специалистами.
8. Предусмотреть гидроизоляцию пола с заведением на всю высоту стены до потолка в помещениях с повышенной влажностью.
9. Все деревянные элементы и детали конструкций обработать антисептиками и антипиренами.
10. Выполнить выравнивание стен в помещениях, выдержать углы смежных стен 90°. Исключения обозначены на чертеже.
11. Предусмотреть люки скрытого монтажа для доступа к коммуникациям, размещение определить по месту.
12. Выполнить армирование конструкций стен стеклотканевой армирующей сеткой с ячейкой 5x5 мм для предотвращения растрескивания оштукатуренных поверхностей (места где нет отделки обоями и керамической плиткой).
13. Прокладку коммуникаций водоснабжения (ГВС, ХВС, канализация) производить специалистами.
14. Согласовать схему канализации со специалистами. Уклон канализационных труб выполнить не менее допустимой величины (1 см на 1 метр трубы). Согласовать со специалистами.
15. Привязку вывода коммуникаций уточнить после подбора сантехнического оборудования. Выполнить по инструкции монтажа.
16. Предусмотреть люки скрытого монтажа для доступа к коммуникациям, размещение определить по месту, согласовать с сантехниками.
17. Размещение выводов электропитания для внутренних и наружных блоков кондиционирования уточнить при согласовании моделей кондиционеров со специалистами.
18. Размещение и габаритные размеры электрощита согласовать со специалистами.
19. Размещение распаечных коробок определить по месту специалистами, выполнить исполнительную схему.
20. Датчики пожарной и охранной сигнализации и электровыводы для них разместить совместно со специалистами, предварительно вызвав их на объект.
21. Узлы носят рекомендательный характер, при необходимости доработать с изменениями по месту со специалистами.

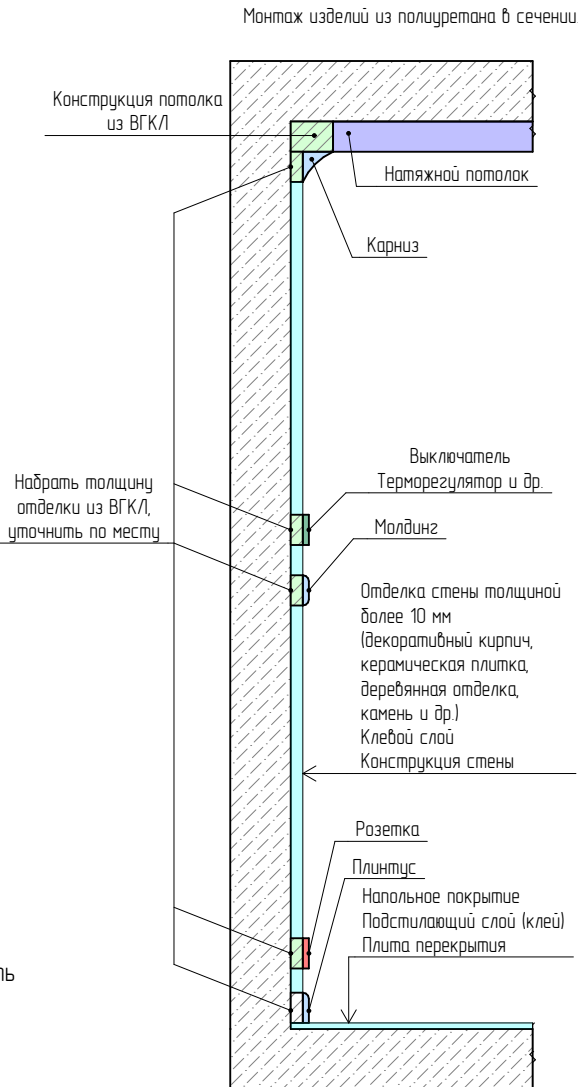

Узел монтажа натяжного потолка к стене с отделкой керамической плиткой.

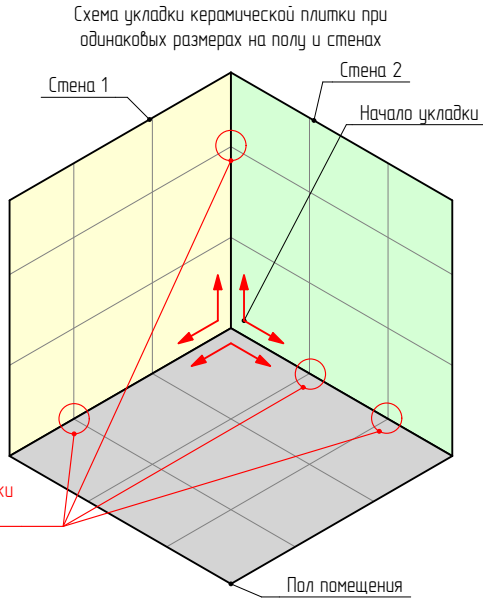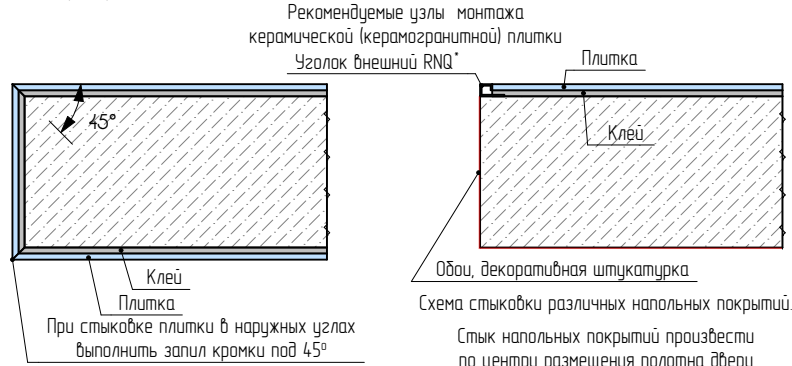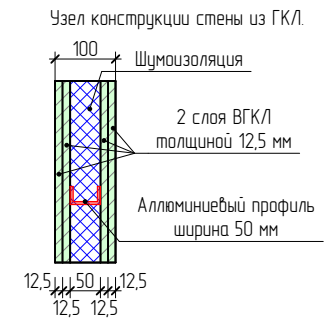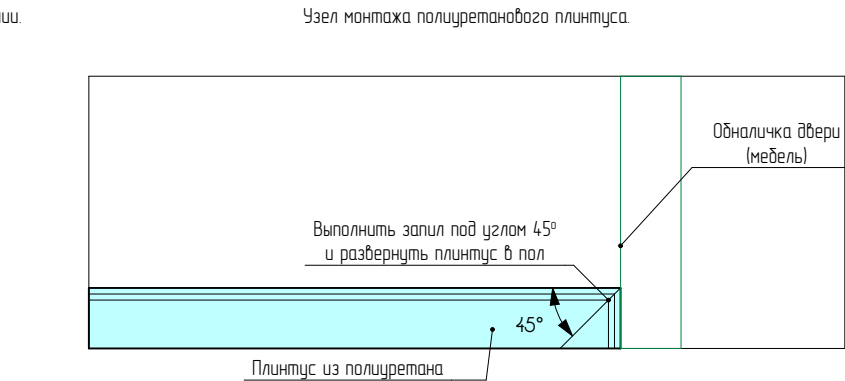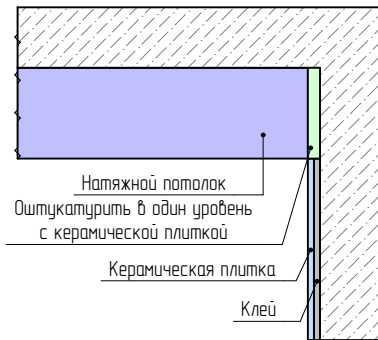

Совместить швы плитки на стенах и полу




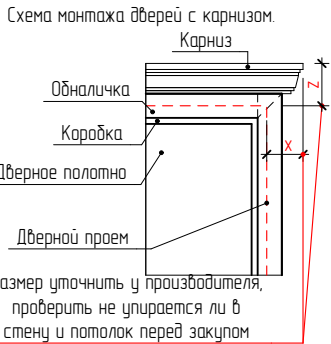


Схема монтажа подоконника

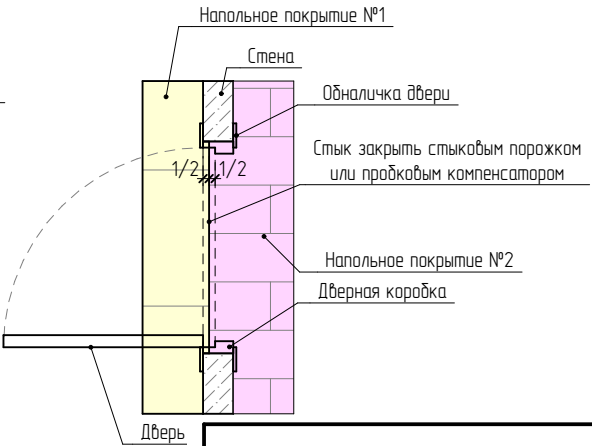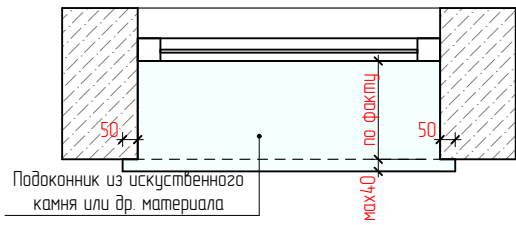


МСК 392.12.25–ЭП ПРЕМИУМ			
Эскизный дизайн–проект интерьера квартиры в г. Москва ЖК “Остров”, ул. Нижние Мневники д. 7			
Общие указания по выполнению строительно-ремонтных работ.			
Дизайнер интерьера №1 Александр Батеньков	Стадия	Лист	Листов
	ЭП	11	120
		Подп.	Дата
Г.АП	Батеньков А.С.		
Гл. дизайнер	Власова В.А.		
Гл. проектиров.	Лунькова В.Н.		

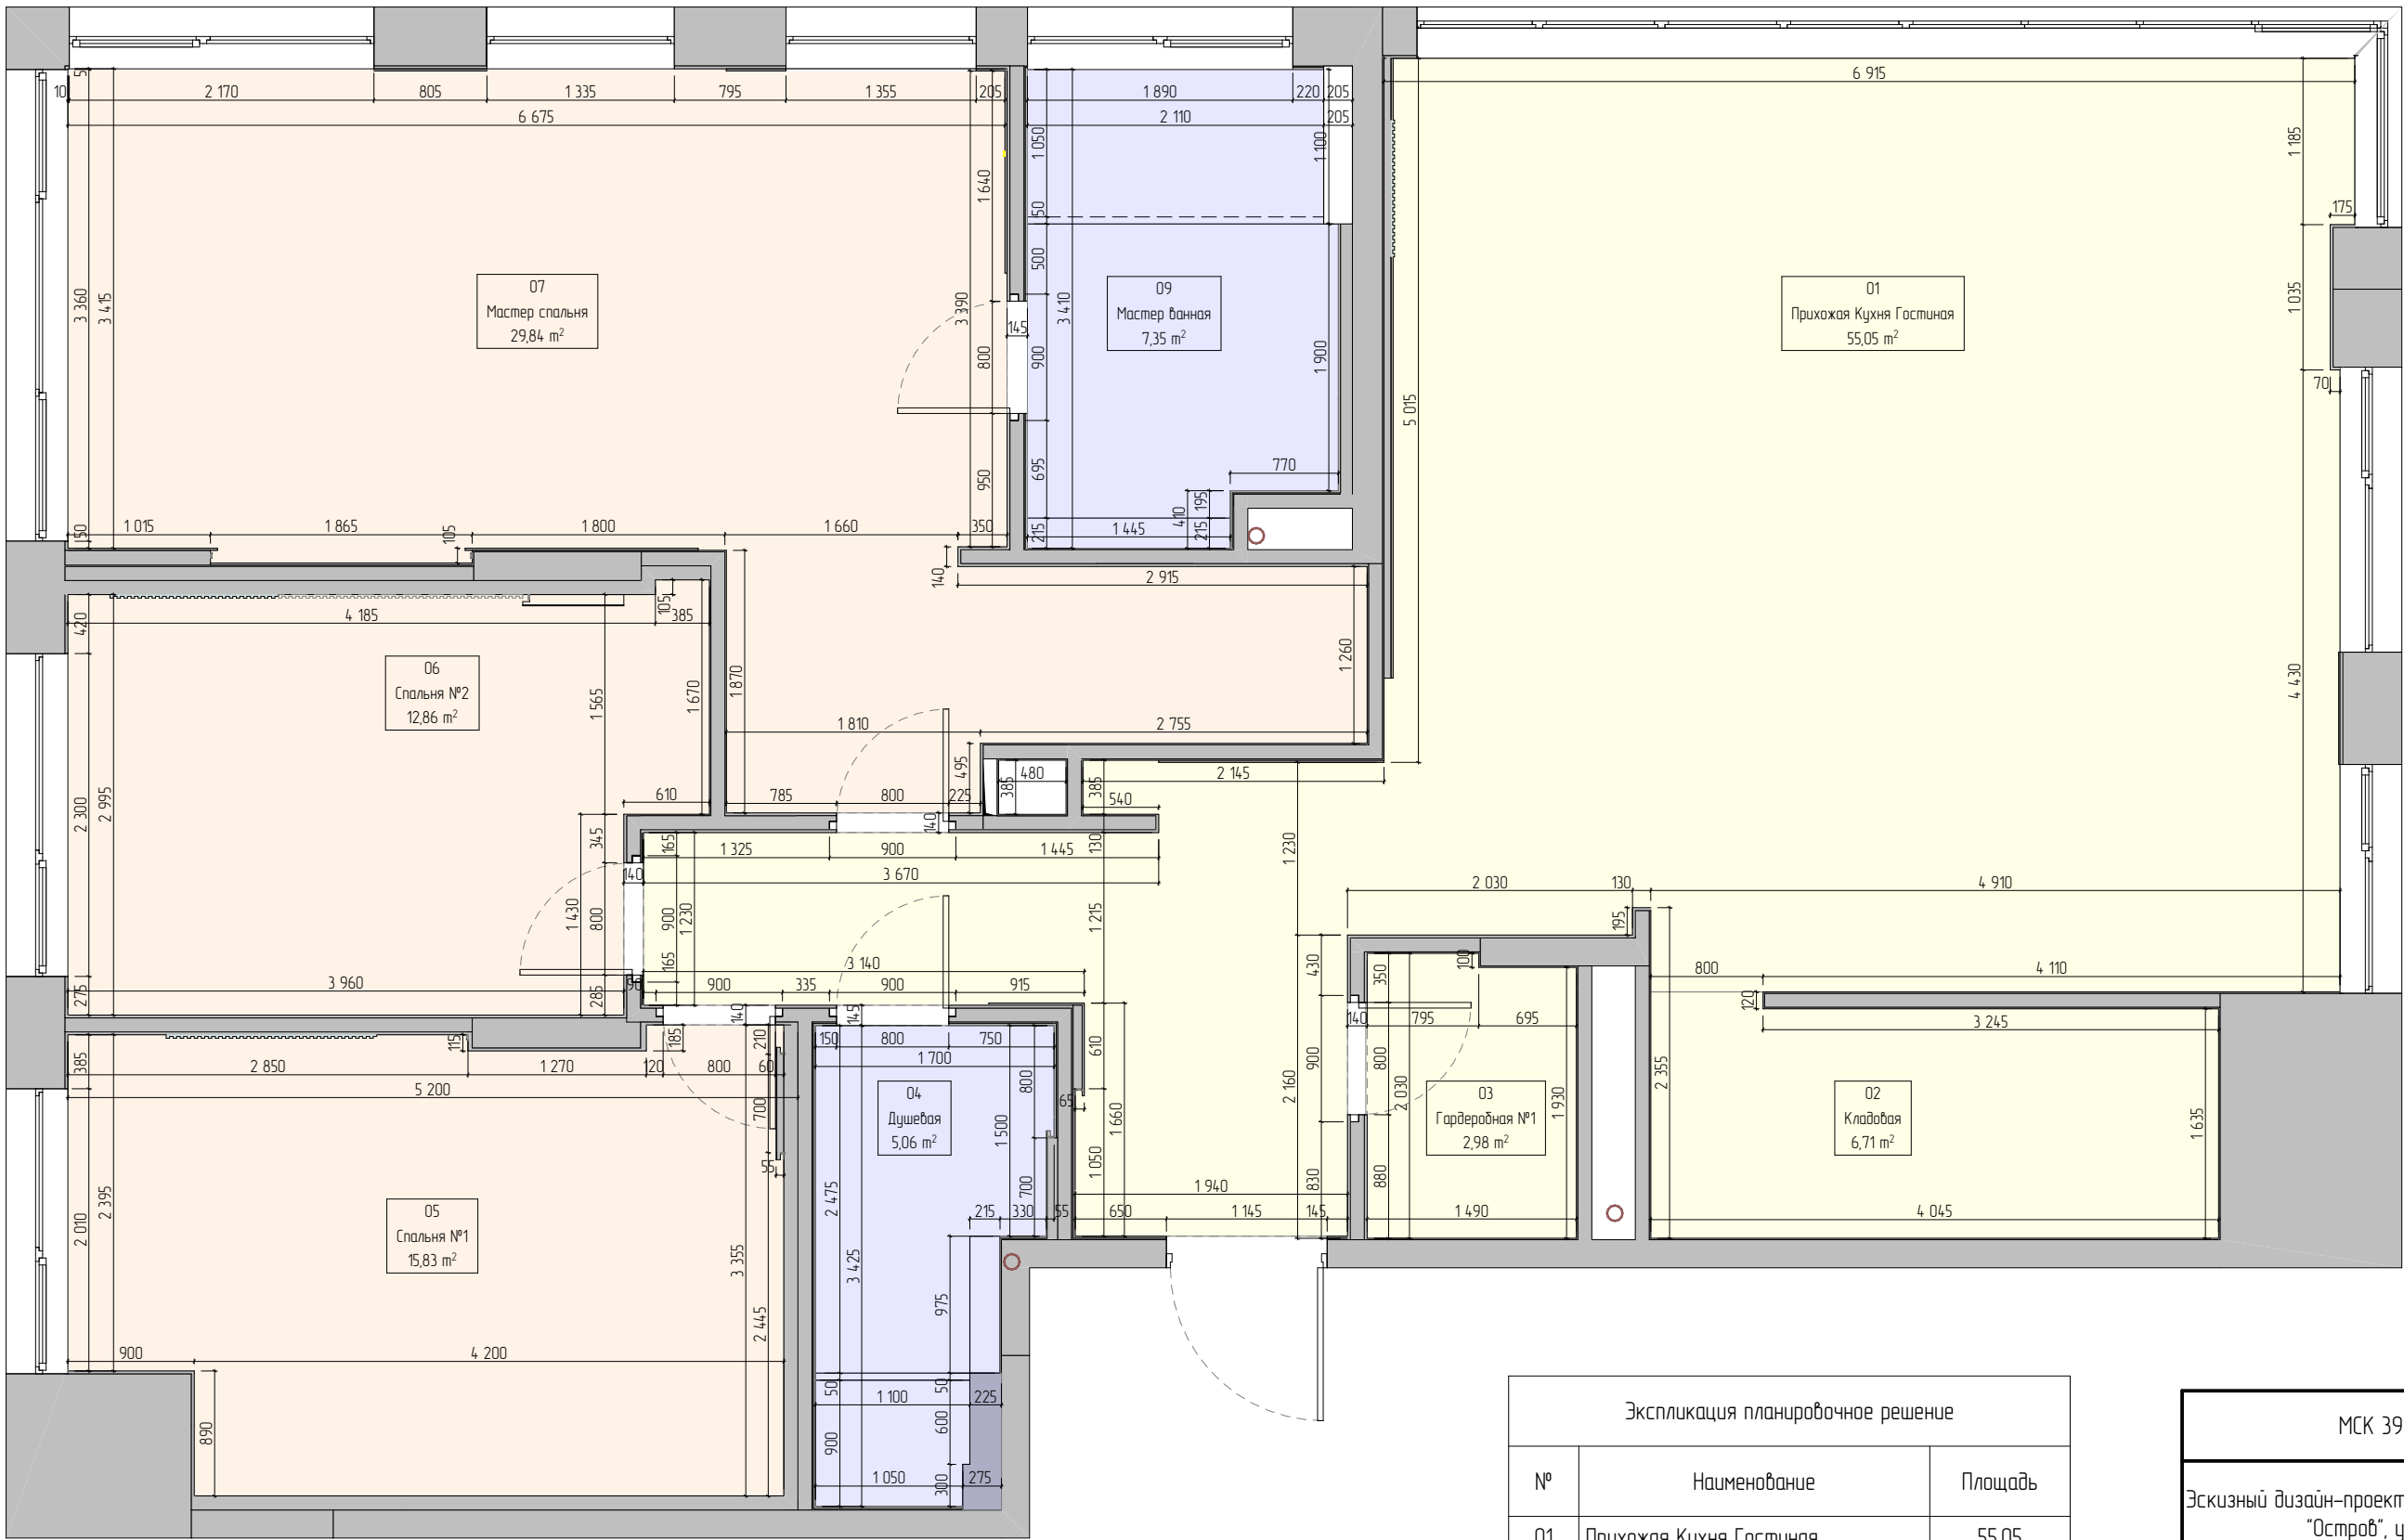

Экспликация планировочное решение		
№	Наименование	Площадь
01	Прихожая Кухня Гостиная	55,05
02	Кладовая	6,71
03	Гардеробная №1	2,98
04	Душевая	5,06
05	Спальня №1	15,83
06	Спальня №2	12,86
07	Мастер спальня	29,84
09	Мастер ванная	7,35
		135,68 м²

МСК 392.12.25-ЭП ПРЕМИУМ			
Эскизный дизайн-проект интерьера квартиры в г. Москва ЖК "Остров", ул. Нижние Мневники д. 7			
План помещений после перепланировки.			
Дизайнер интерьера №1 Александр Батеньков	Стадия	Лист	Листов
	ЭП	12	120
		Подп.	Дата
ГАП	Батеньков А.С.		
Гл. дизайнер	Власова В.А.		
Гл. проектиров.	Луцькова В.Н.		

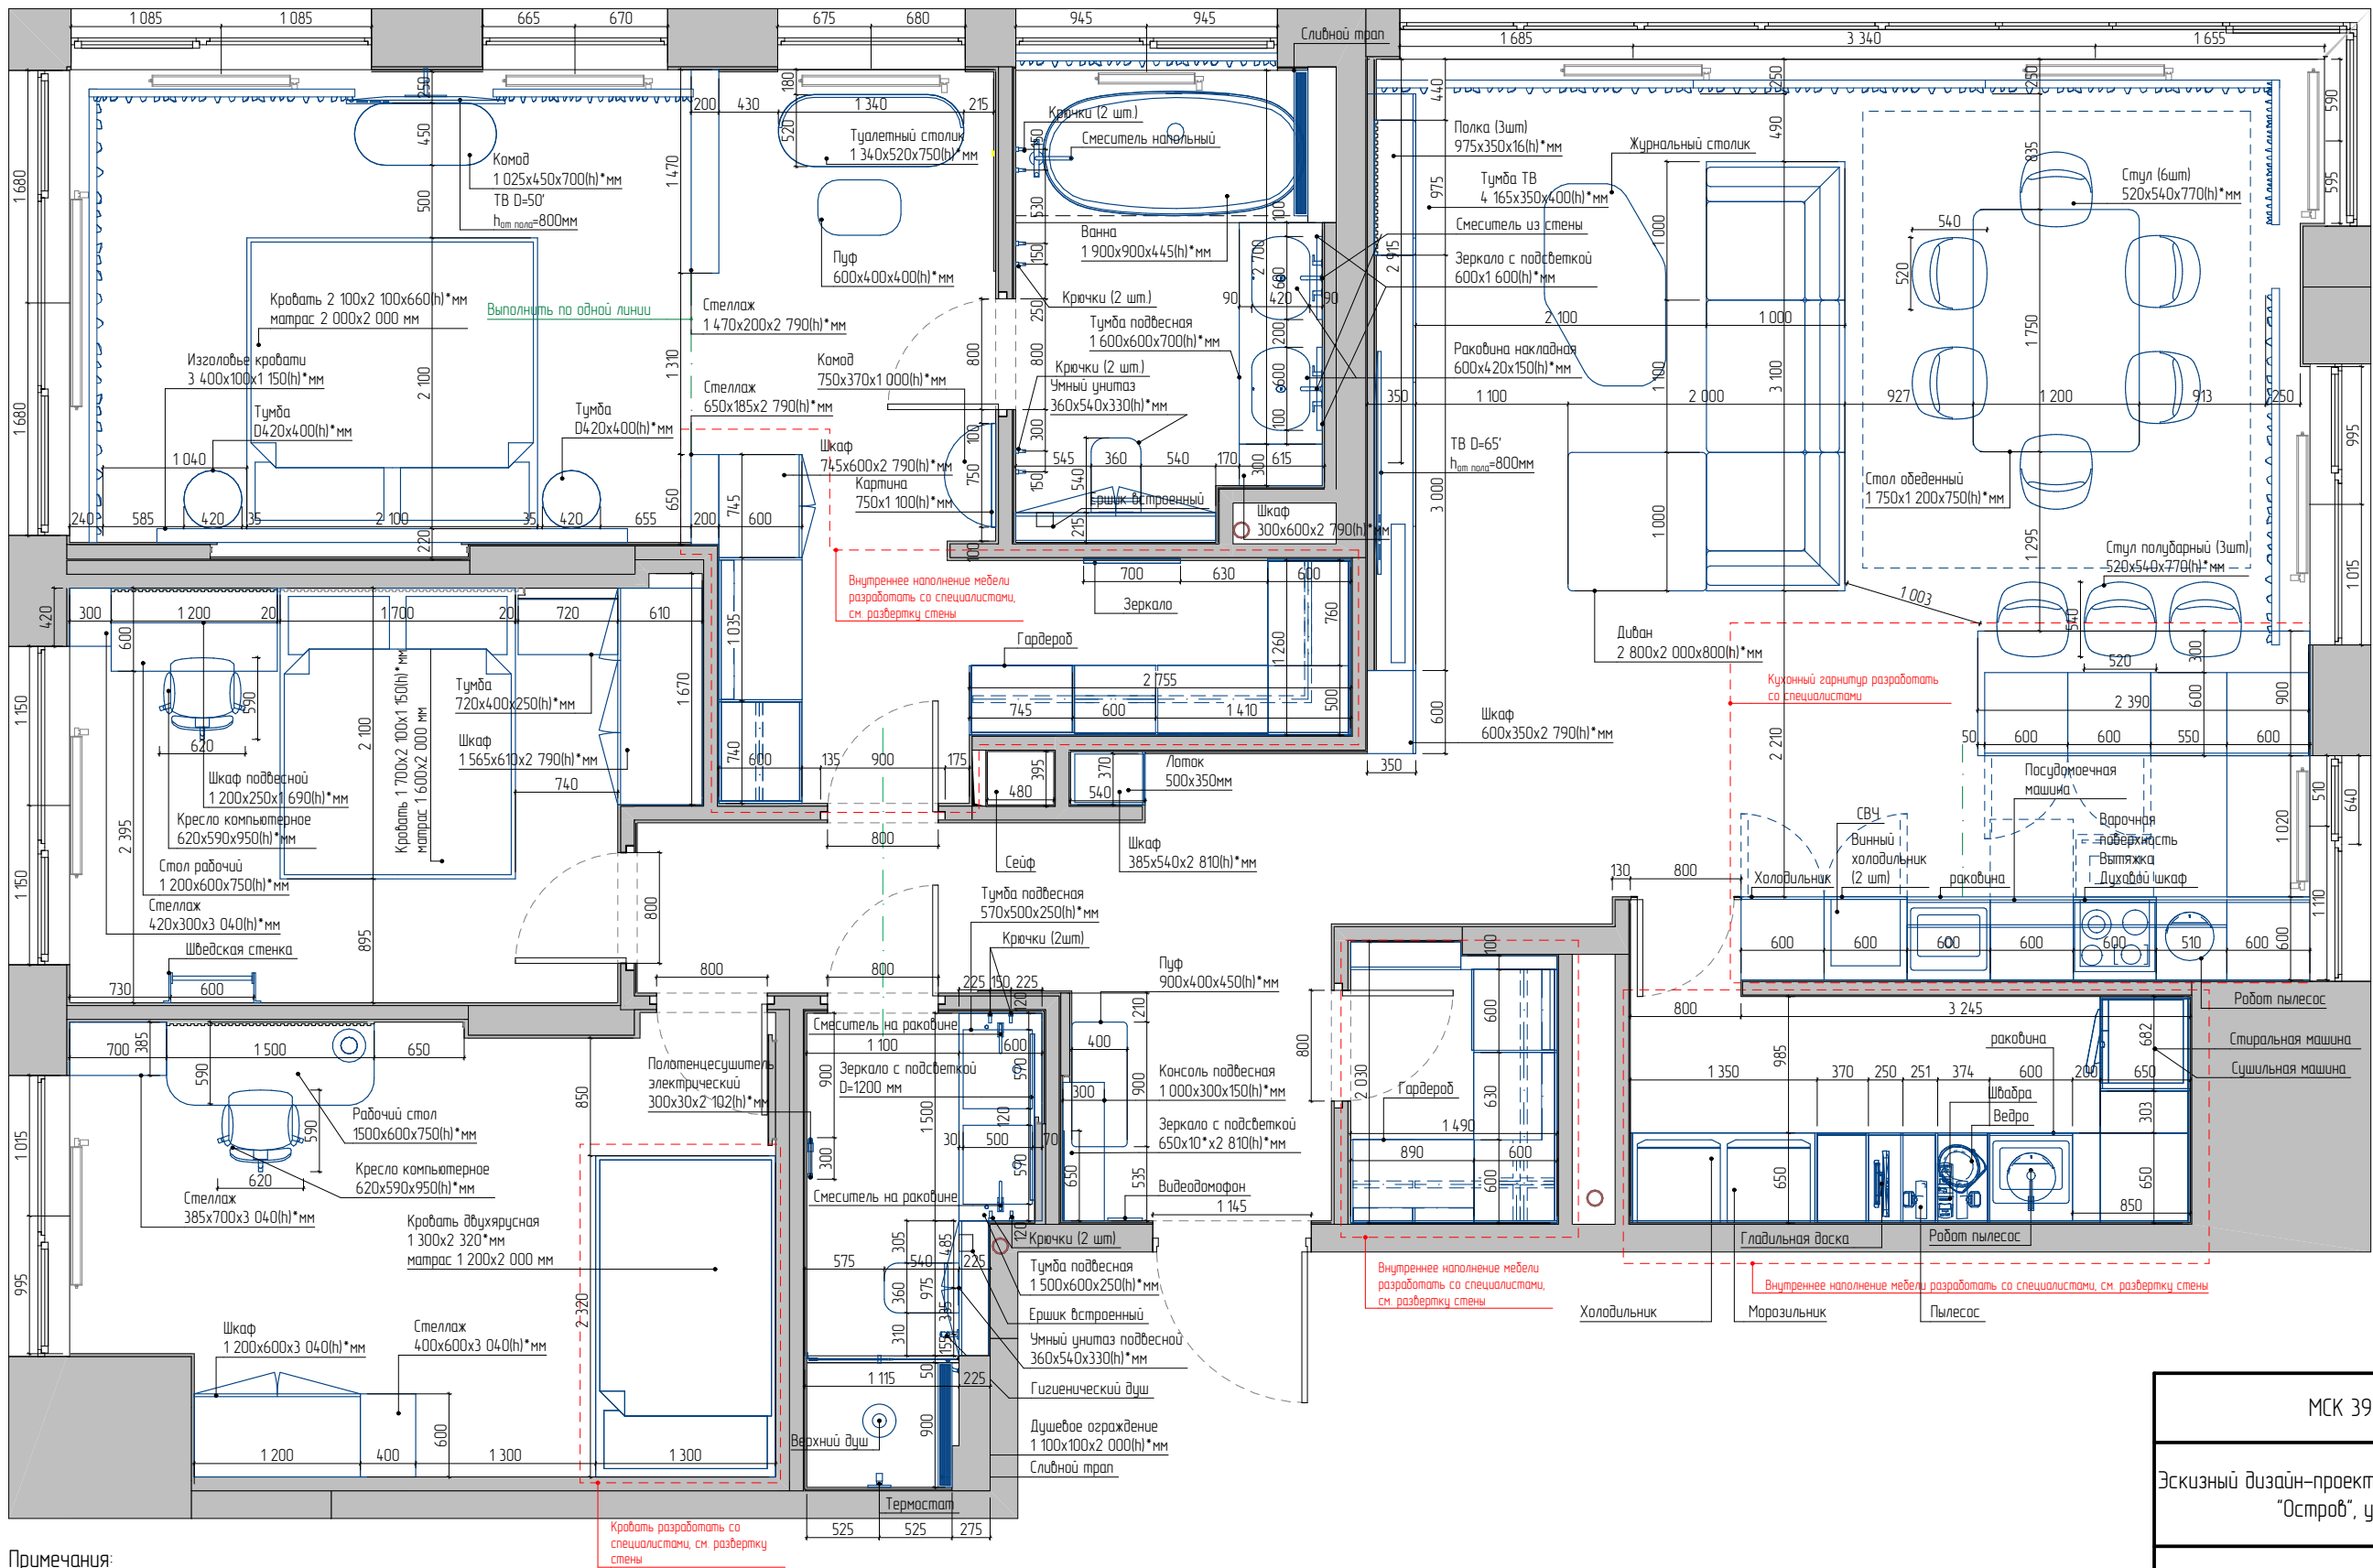

Примечания:


- * – размеры уточнить по месту после выполнения черновых отделочных работ.
- Размеры, привязки и характеристики кухонного гарнитура согласовать со специалистами после выбора модели.
- Размеры и характеристики радиаторов отопления согласовать со специалистами, предусмотреть терморегуляторы.
- Привязку вывода коммуникаций уточнить после подбора сан.тех. оборудования. Выполнить по инструкции монтажа.
- Вывод коммуникаций для посудомоечной машины провести гибкими шлангами в цоколе кухонного гарнитура, разработать со специалистами.
- Предусмотреть фильтры для очистки водопроводной воды на магистрали водопровода.
- ** – размеры уточнить у изготовителей мебели.
- Предусмотреть люки скрытого монтажа для доступа к коммуникациям, размещение уточнить по месту.
- Привязки выводов коммуникаций даны чистовые, с учетом толщины финишной отделки стен.
- Габаритные размеры сан.тех. оборудования уточнить при выборе модели и покупке. Выводы коммуникаций выполнить по инструкции монтажа.

МСК 392.12.25-ЭП ПРЕМИУМ

Эскизный дизайн-проект интерьера квартиры в г. Москва ЖК "Остров", ул. Нижние Мневники д. 7

План расстановки мебели и сан.тех.оборудования.

Дизайнер интерьера  Александр Батеньков	Стадия	Лист	Листов
	ЭП	13	120
		Подп.	Дата
Г.АП	Батеньков А.С.		
Гл. дизайнер	Власова В.А.		
Гл. проектиров.	Луцькова В.Н.		

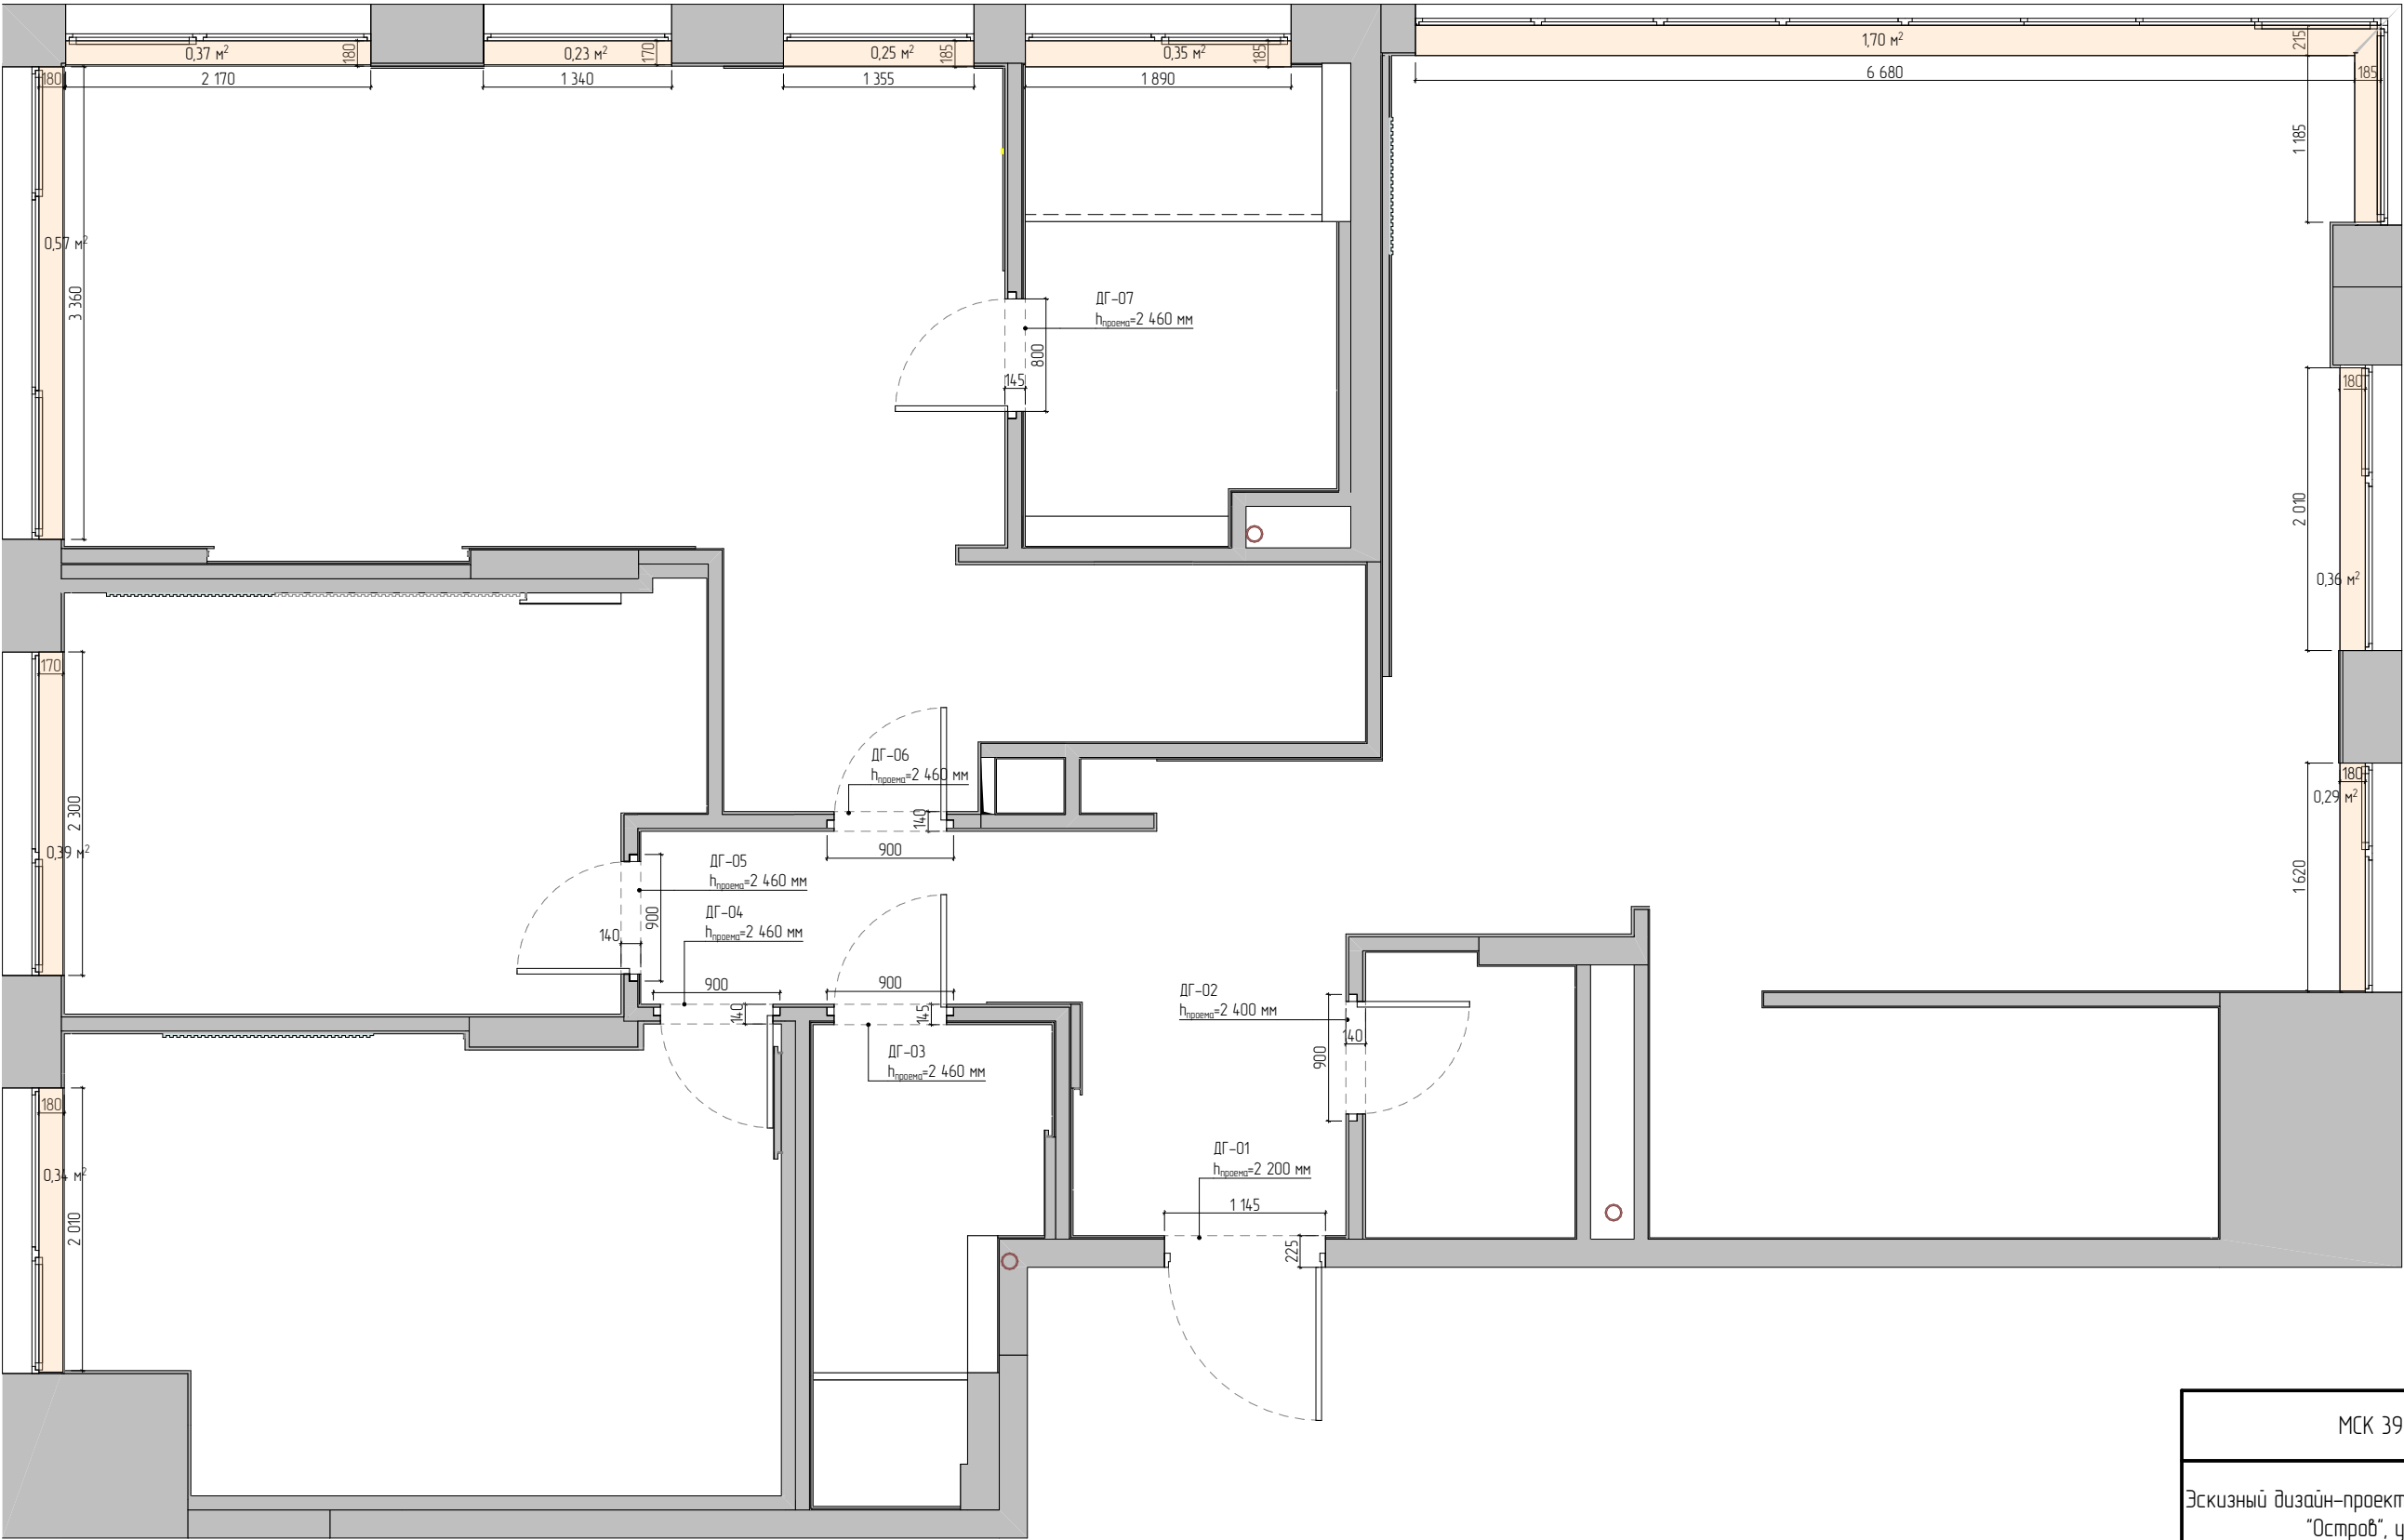

Условное обозначение:

Подоконник №1. Искусственный камень. Цвет при выборе образца.

Примечания:

- * – размеры уточнить по месту после выполнения черновых отделочных работ.
- Размеры дверных проемов выполнить по инструкции монтажа дверей.
- Подоконники выполнить из искусственного камня.

МСК 392.12.25-ЭП ПРЕМИУМ			
Эскизный дизайн-проект интерьера квартиры в г. Москва ЖК "Остров", ул. Нижние Мневники д. 7			
План заполнения дверных проемов и отделка подоконников.			
Дизайнер интерьера  Александр Батеньков	Стадия	Лист	Листов
	ЭП	14	120
		Подп.	Дата
ГАП	Батеньков А.С.		
Гл. дизайнер	Власова В.А.		
Гл. проектиров.	Луныкова В.Н.		


Ведомость дверей				
Номер	Размеры проема Ш x В	Символ на плане	Вид со стороны Открывания	Примечания
ДГ-01	1 145×2 300			Сейф-дверь входная, необходимость замены уточнить по месту внутренняя накладка МДФ панель (в цвет МДФ панелей стен), размер уточнить по факту со специалистами
ДГ-02	900×2 460			Дверь глухая со скрытым коробом Invisible с открыванием от себя, отделка – покраска в цвет стен. Размер полотна 800х2 400 мм.
ДГ-03	900×2 460			Дверь глухая со скрытым коробом Invisible с открыванием на себя, отделка – покраска в цвет стен коридора. Размер полотна 800х2 400 мм.
ДГ-04	900×2 460			Дверь глухая со скрытым коробом Invisible с открыванием от себя, отделка – покраска в цвет стен. Размер полотна 800х2 400 мм.
ДГ-05	900×2 460			Дверь глухая со скрытым коробом Invisible с открыванием от себя, отделка со стороны коридора – тонированное стекло, со стороны спальни – в цвет стен. Размер полотна 800х2 400 мм.
ДГ-06	900×2 460			Дверь глухая со скрытым коробом Invisible с открыванием от себя, отделка – покраска в цвет стен. Размер полотна 800х2 400 мм.
ДГ-07	900×2 460			Дверь глухая со скрытым коробом Invisible с открыванием на себя, отделка со стороны санузла – МДФ, со стороны master спальни – покраска в цвет стен.. Размер полотна 800х2 400 мм.

МСК 392.12.25–ЭП ПРЕМИУМ

Эскизный дизайн–проект интерьера квартиры в г. Москва ЖК “Остров”, ул. Нижние Мневники д. 7

Ведомость дверных проемов.

Дизайнер интерьера Александр Батеньков	Стадия	Лист	Листов
	ЭП	15	120
		Подп.	Дата
Г.АП	Батеньков А.С.		
Гл. дизайнер	Власова В.А.		
Гл. проектиров.	Луныкова В.Н.		

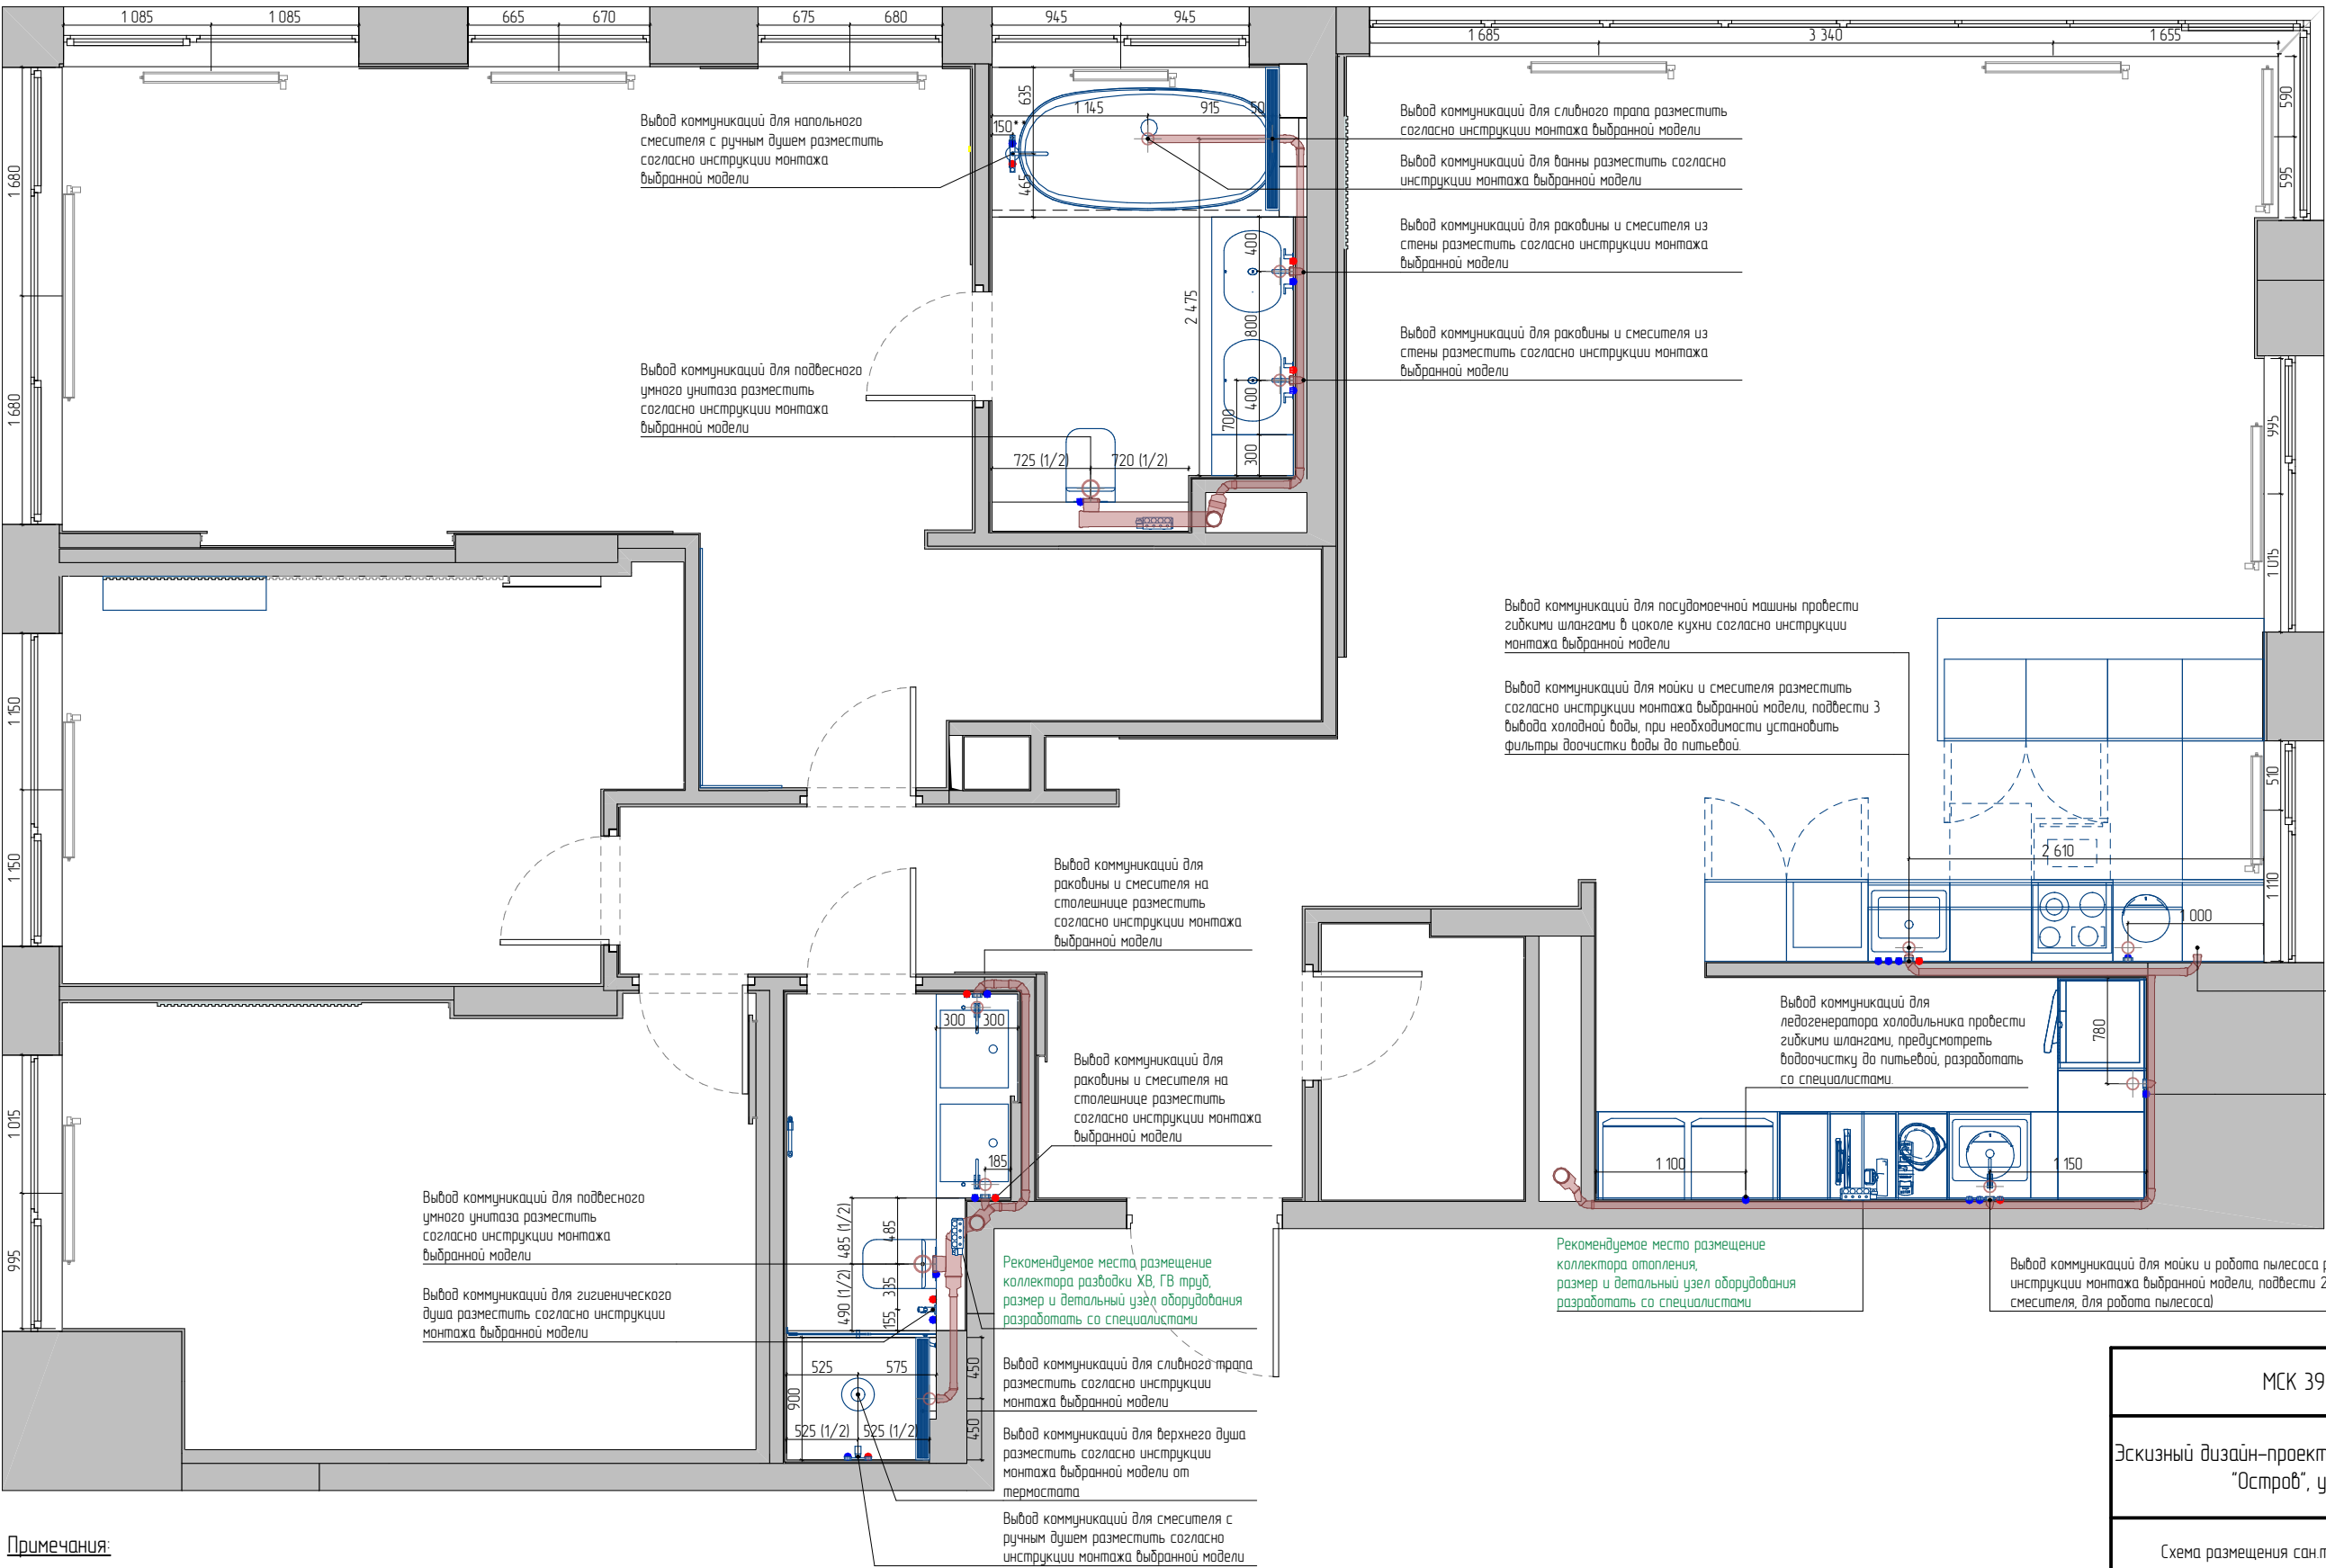


- Условные обозначения:
- Конструкции наружных стен
 - Трубы канализации
 - Радиатор отопления
 - Выход коммуникаций (ХВС, ГВС, канал-ция)

Примечания:

- Привязку вывода коммуникаций уточнить после подбора сан.тех. оборудования. Выполнить по инструкции монтажа.
- Вывод коммуникаций для посудомоечной машины провести гибкими шлангами в цоколе кухонного гарнитура, разработать со специалистами.
- Предусмотреть фильтры для очистки водопроводной воды на магистрали водопровода.
- Предусмотреть люки скрытого монтажа для доступа к коммуникациям, размещение определить по месту, согласовать с сантехниками.
- Уклон канализационных труб выполнить минимально допустимой величины (1 см на 1 метр трубы).
- Согласовать схему канализации со специалистами.
- Выводы коммуникаций для радиаторов отопления согласовать со специалистами.
- * – размеры уточнить по месту.
- Размеры и характеристики радиаторов отопления согласовать со специалистами, предусмотреть терморегуляторы.
- Данный лист требует доработки в соответствии с техническими схемами и схемами размещения сантехнических выпусков под конкретное сантехническое оборудование, которое будет выдано поставщиками сантехнического оборудования после закупки данного оборудования.

МСК 392.12.25–ЭП ПРЕМИУМ			
Эскизный дизайн–проект интерьера квартиры в г. Москва ЖК "Остров", ул. Нижние Мневники д. 7			
Схема размещения сан.тех.оборудования, канализации, ХВС, ГВС.			
Дизайнер интерьера №1 Александр Батеньков	Стадия	Лист	Листов
	ЭП	16	120
		Подп.	Дата
ГАП	Батеньков А.С.		
Гл. дизайнер	Власова В.А.		
Гл. проектиров.	Луныкова В.Н.		

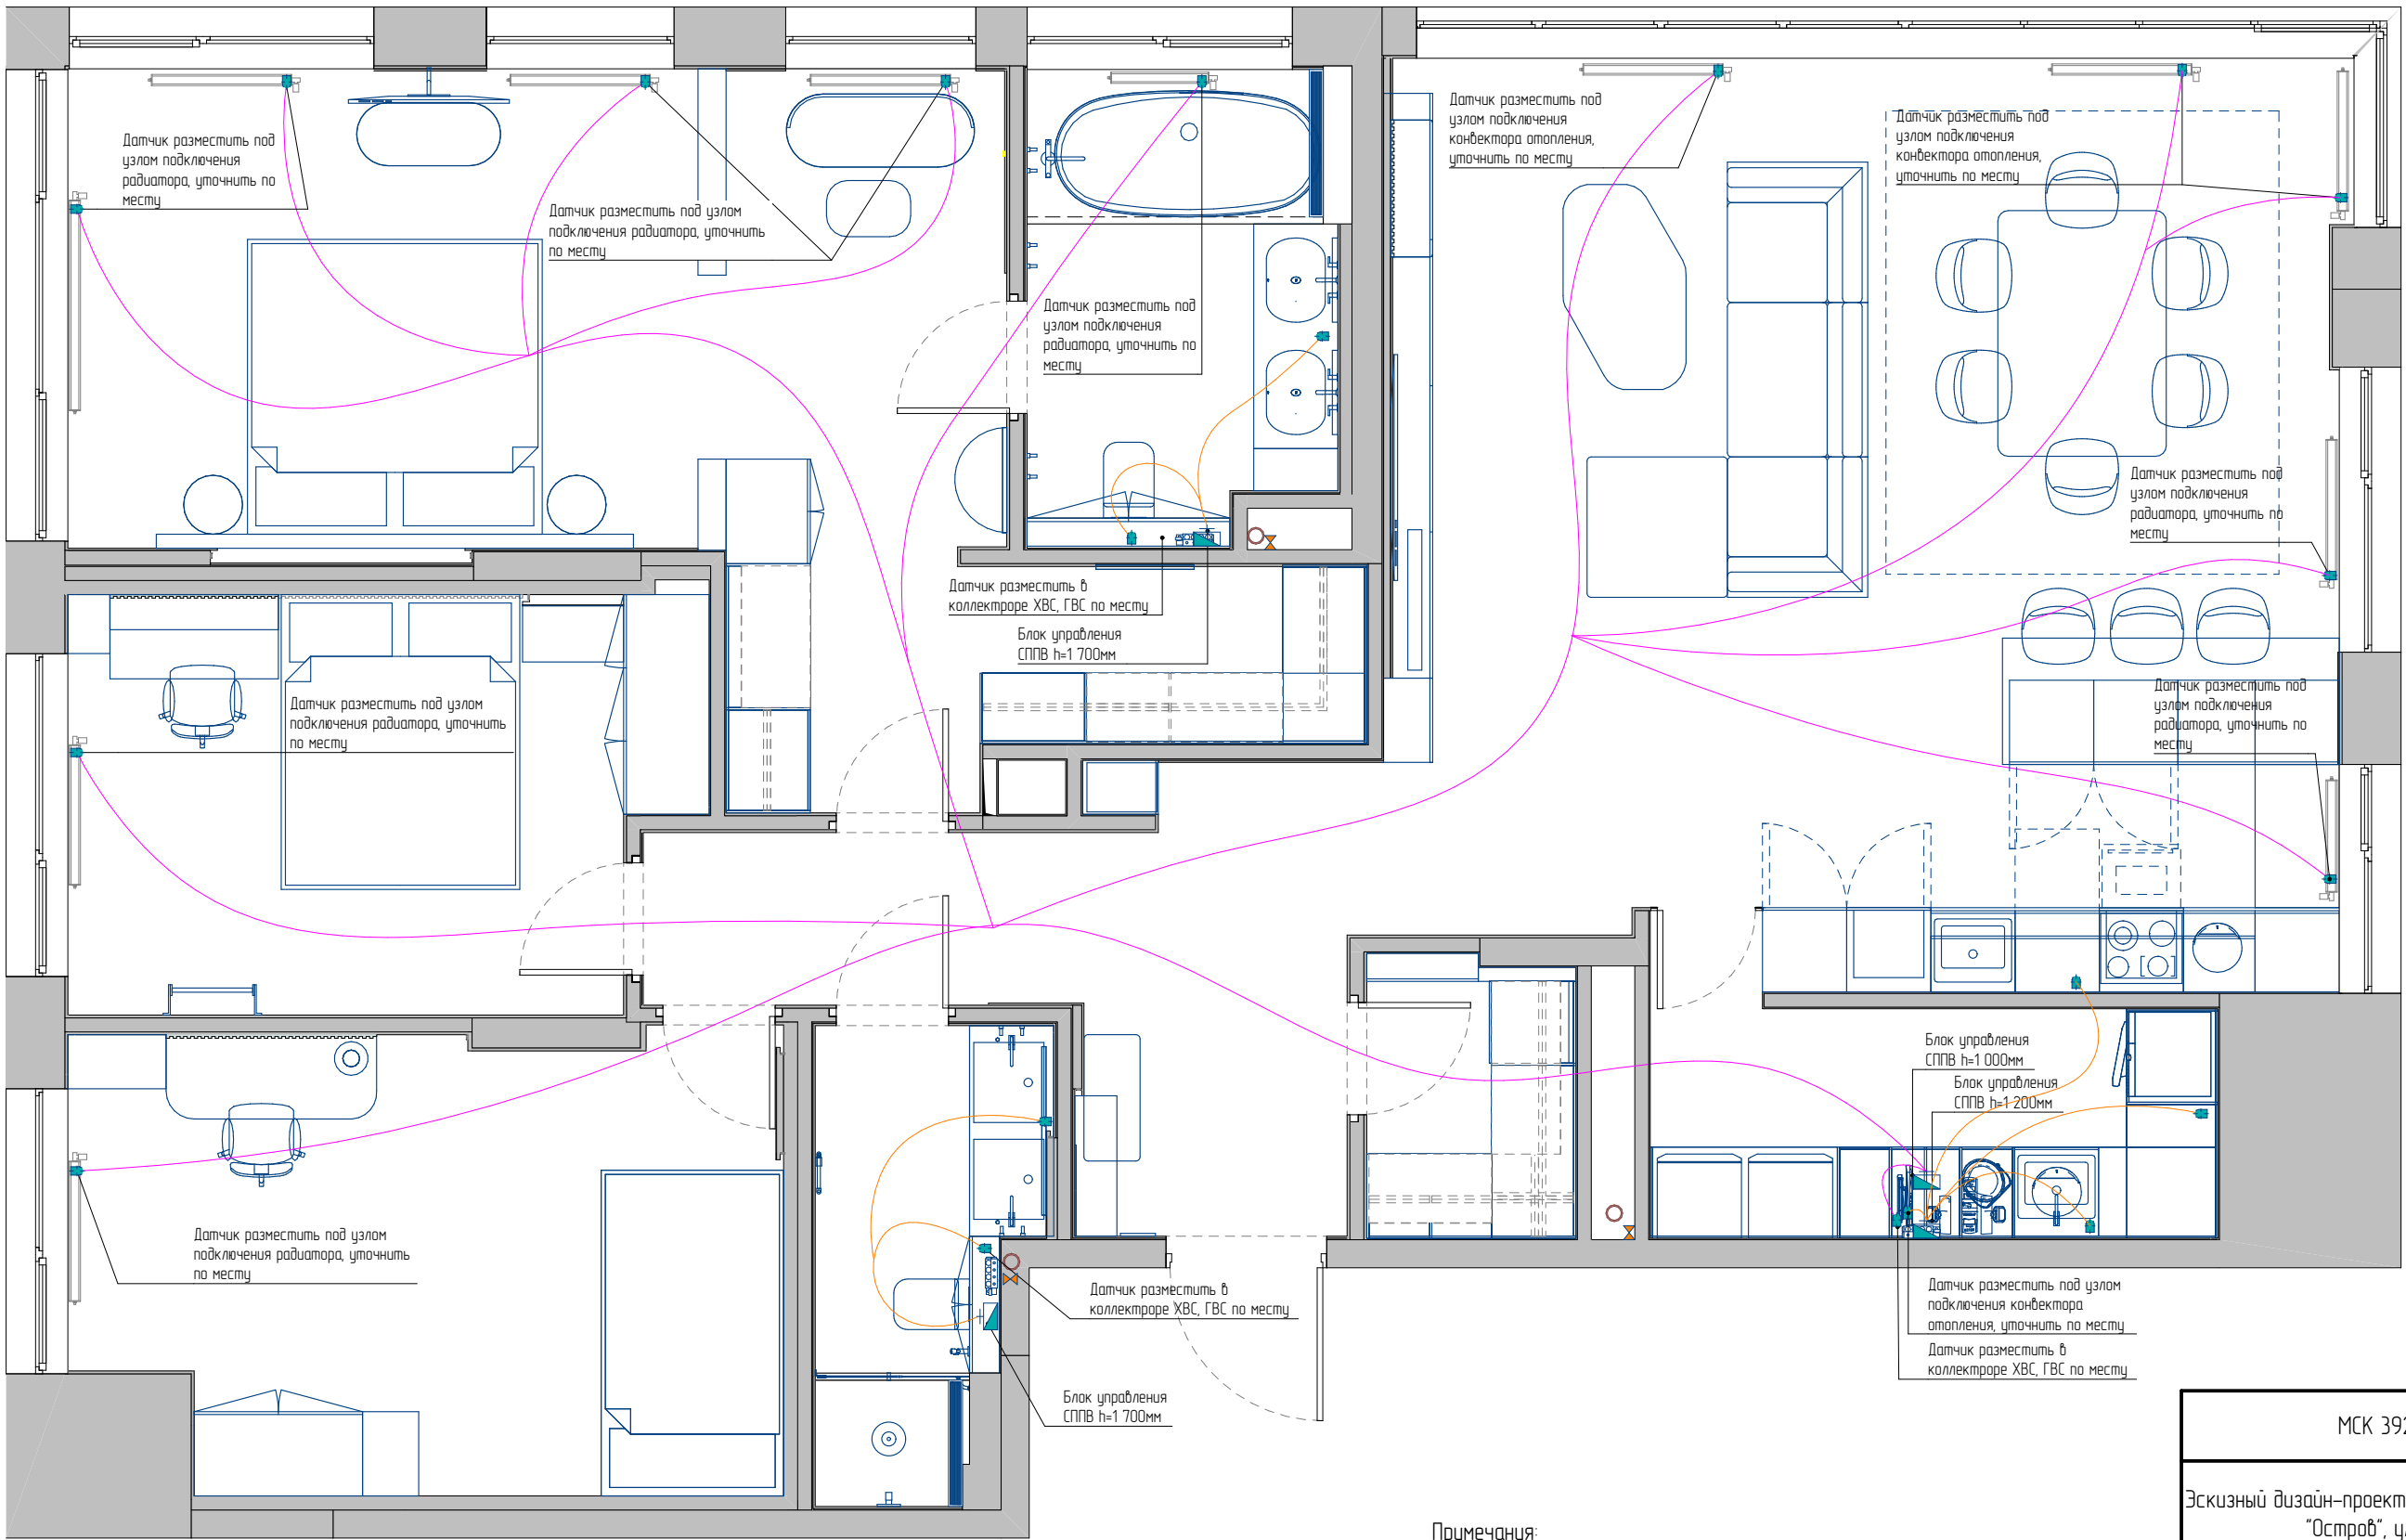

- Условные обозначения:
- Конструкции наружных стен
 - Радиатор отопления
 - Модуль управления системой защиты от протечек воды
 - Датчик протечки


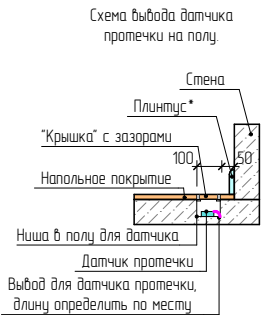


Схема подключения системы датчиков протечки воды.

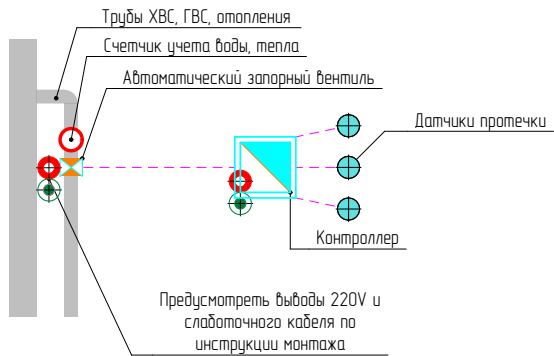

Ведомость оборудования системы против протечки воды.			
Обозначение	Наименование	Кол-во	Примечание
✂	автоматический запорный вентиль	3	
⚡	Блок управления СППВ	4	
■	Датчик протечки	21	

- Примечания:
- * – размеры уточнить по месту.
 - Размеры и характеристики радиаторов отопления согласовать со специалистами, предусмотреть терморегуляторы.
 - Размещение датчиков протечки согласовать со специалистами.
 - Количество автоматических запорных вентилей определить по месту.
 - Предусмотреть электровыводы для оборудования против протечки воды.
 - Автоматические запорные вентили разместить на трубах ХВС, ГВС перед счетчиками расхода воды и на трубах отопления, размещение определить по месту.
 - К блокам управления канальными кондиционерами и вентиляцией подвести электрокабель по техническому заданию от специалистов, работы проводить совместно.

МСК 392.12.25-ЭП ПРЕМИУМ


Эскизный дизайн-проект интерьера квартиры в г. Москва ЖК "Остров", ул. Нижние Мневники д. 7

План размещения оборудования против протечек воды.

Дизайнер интерьера №1
Александр Батеньков

Стадия	Лист	Листов
ЭП	17	120
	Подп.	Дата

ГАП	Батеньков А.С.		
Гл. дизайнер	Власова В.А.		
Гл. проектиров.	Лунькова В.Н.		

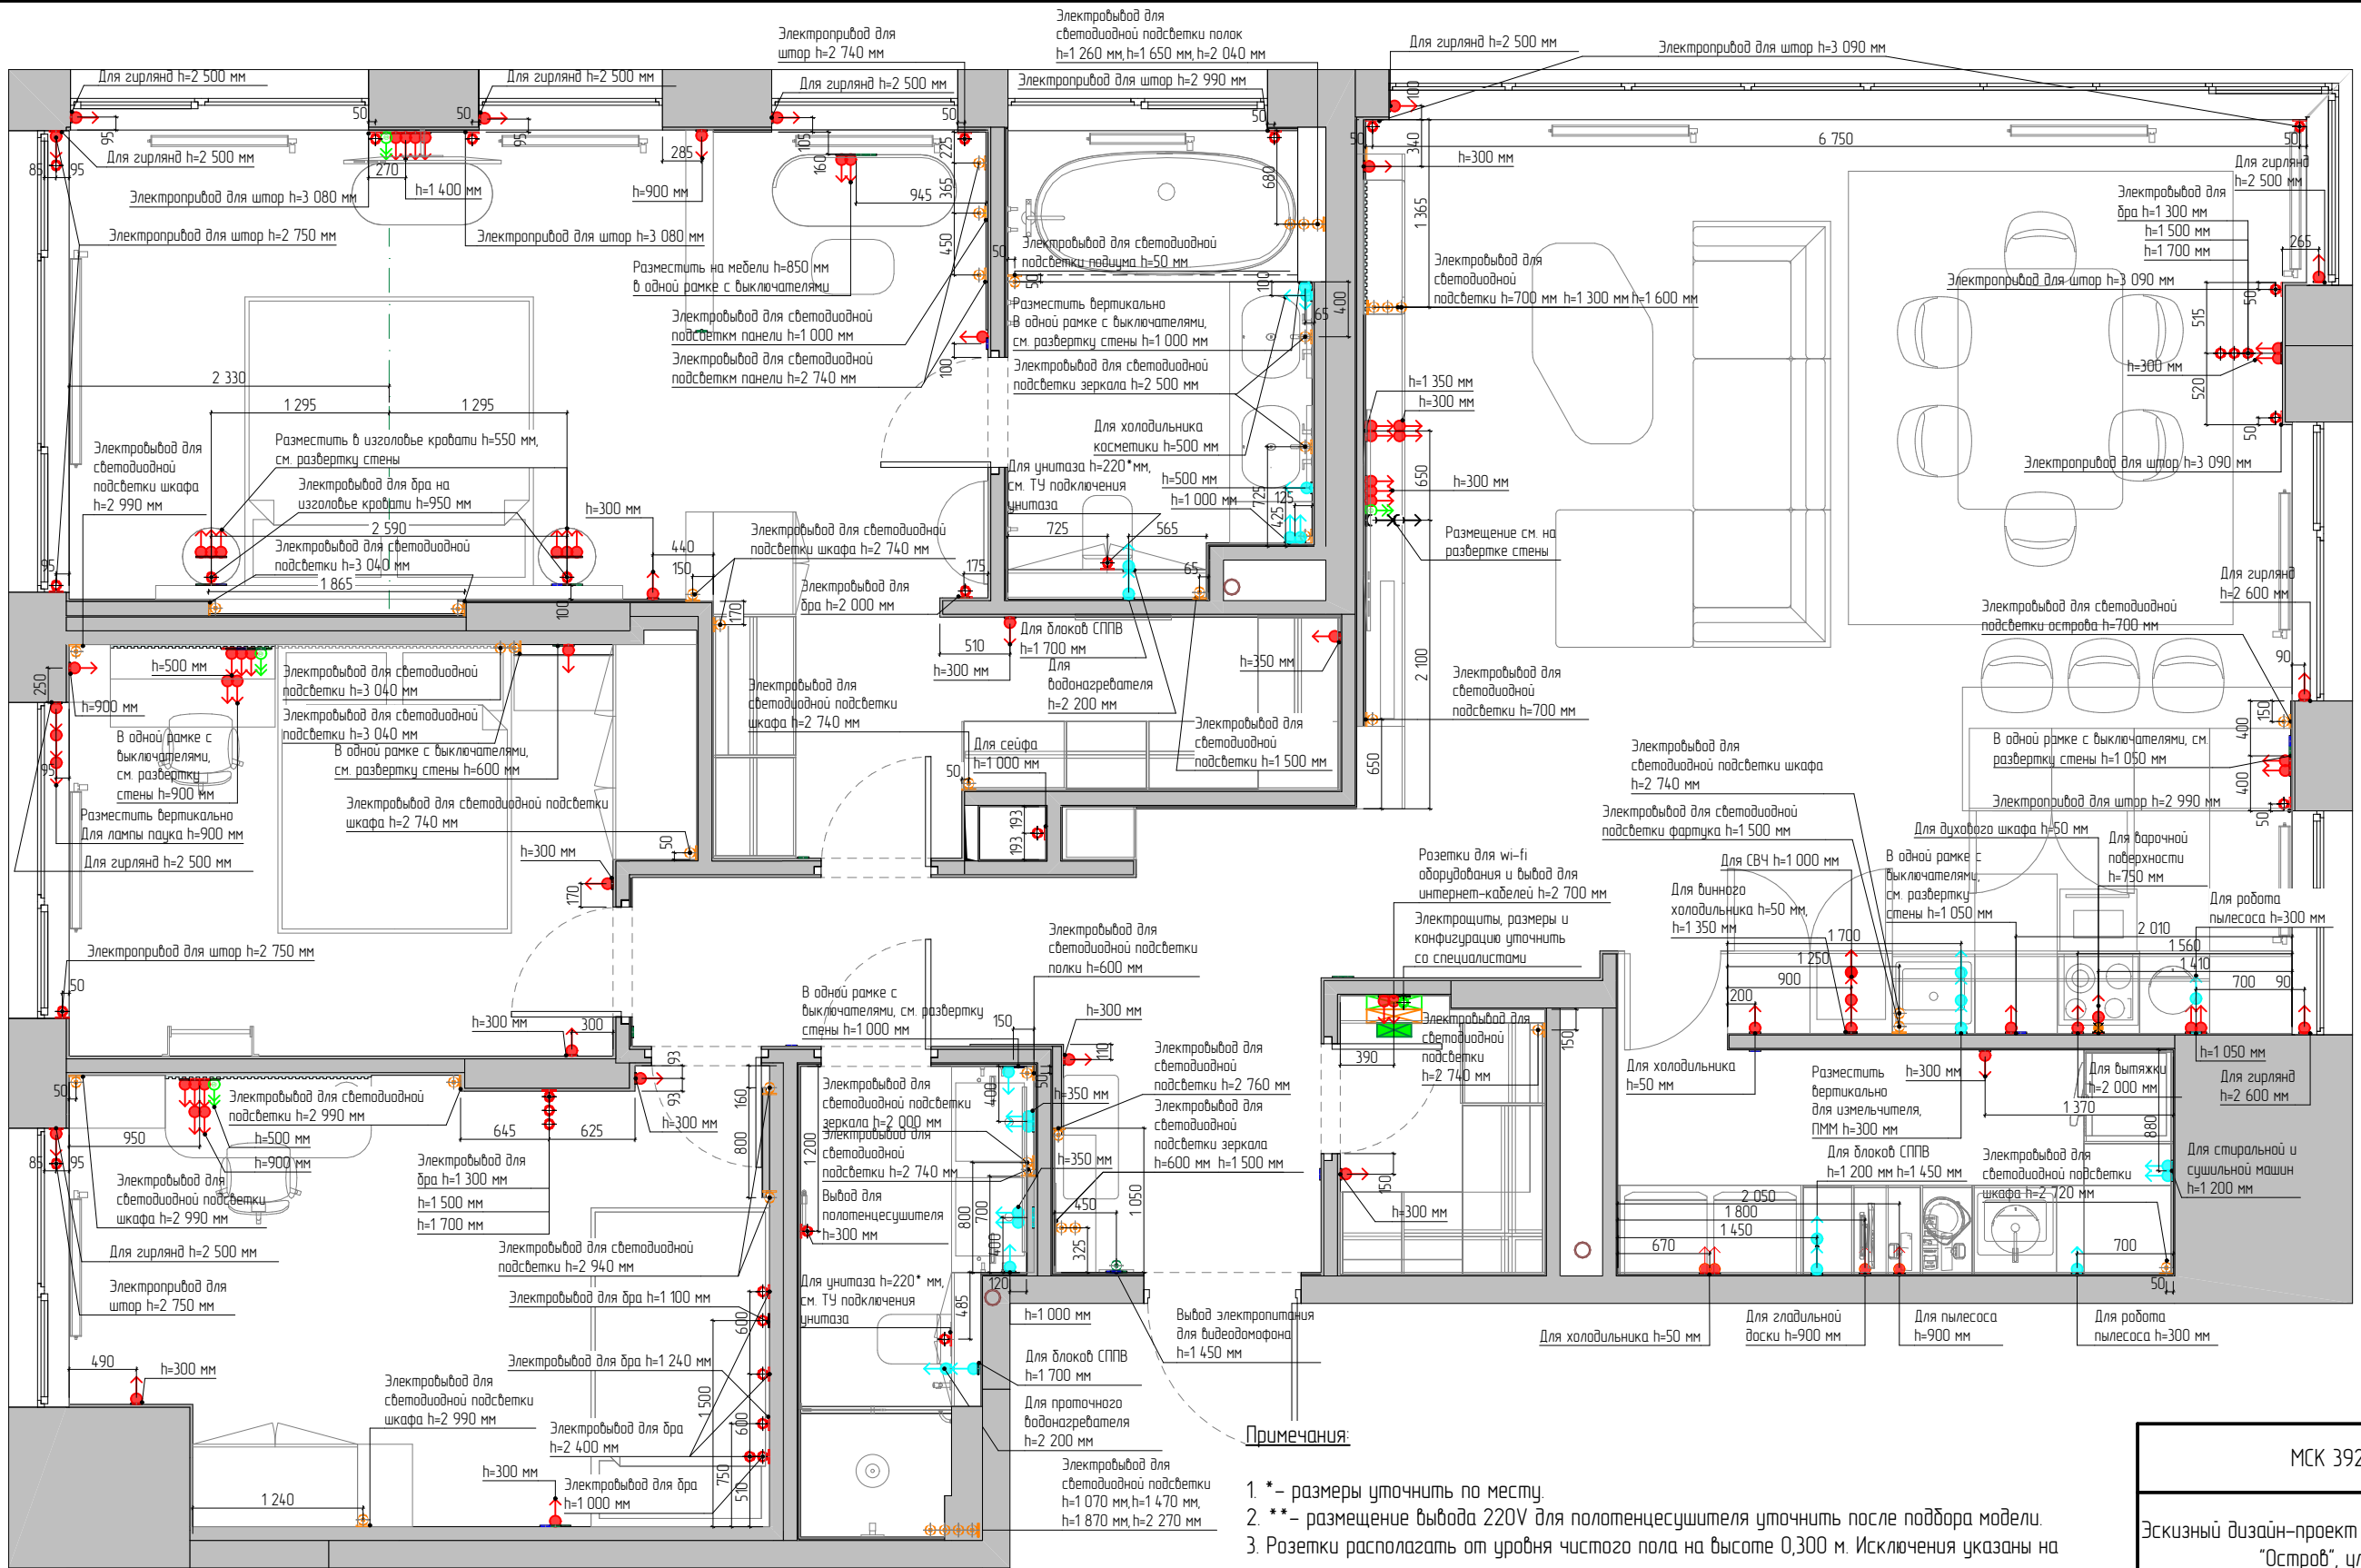

Условные обозначения:



Электрощит



Слаботочный щит



Розетка 220V влагозащищенная



Розетка 220V



Выход электрокабеля для светодиодной ленты



Выход электрокабеля для варочной поверхности



Выход спец. кабеля



Выход интернет кабеля



Выход 220V



wi-fi оборудование


Примечания:

- * – размеры уточнить по месту.
- ** – размещение вывода 220V для полотенцесушителя уточнить после подбора модели.
- Розетки располагать от уровня чистого пола на высоте 0,300 м. Исключения указаны на чертеже.
- Приязку и размещение розеток и выводов кухонного гарнитура согласовать с изготовителями после подбора мебели заказчиком.
- Размещение и габаритные размеры электрощита согласовать со специалистами.
- Предусмотреть совместимость видеодомофона квартиры с общедомовой системой.
- К WI-FI оборудованию подвести 5 выводов интернет-кабеля из расчета: общее количество интернет выводов и розеток + один (вывод в квартиру из подъезда). Размещение wi-fi оборудования и усилителей для него определить по месту, вызов предварительно на объект специалистов.
- Размещение всех выводов и розеток согласовать со специалистами «Умный дом».
- Размеры и характеристики радиаторов отопления согласовать со специалистами, предусмотреть терморегуляторы.
- Датчики пожарной и охранной сигнализации и электровыводы для них разместить совместно со специалистами, предварительно вызвав их на объект.
- Размещение и монтаж стабилизатора напряжения согласовать со специалистами.
- Размещение розеток и электровыводов по высоте см. на развертках стен.

МСК 392.12.25-ЭП ПРЕМИУМ

Эскизный дизайн-проект интерьера квартиры в г. Москва ЖК "Остров", ул. Нижние Мневники д. 7

План размещения электрооборудования с мебелью.

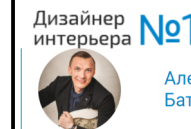

Стадия

Лист

Листов

ЭП

18

120


Подп.

Дата

ГАП Батеньков А.С.

Гл. дизайнер Власова В.А.

Гл. проектиров. Луныкова В.Н.

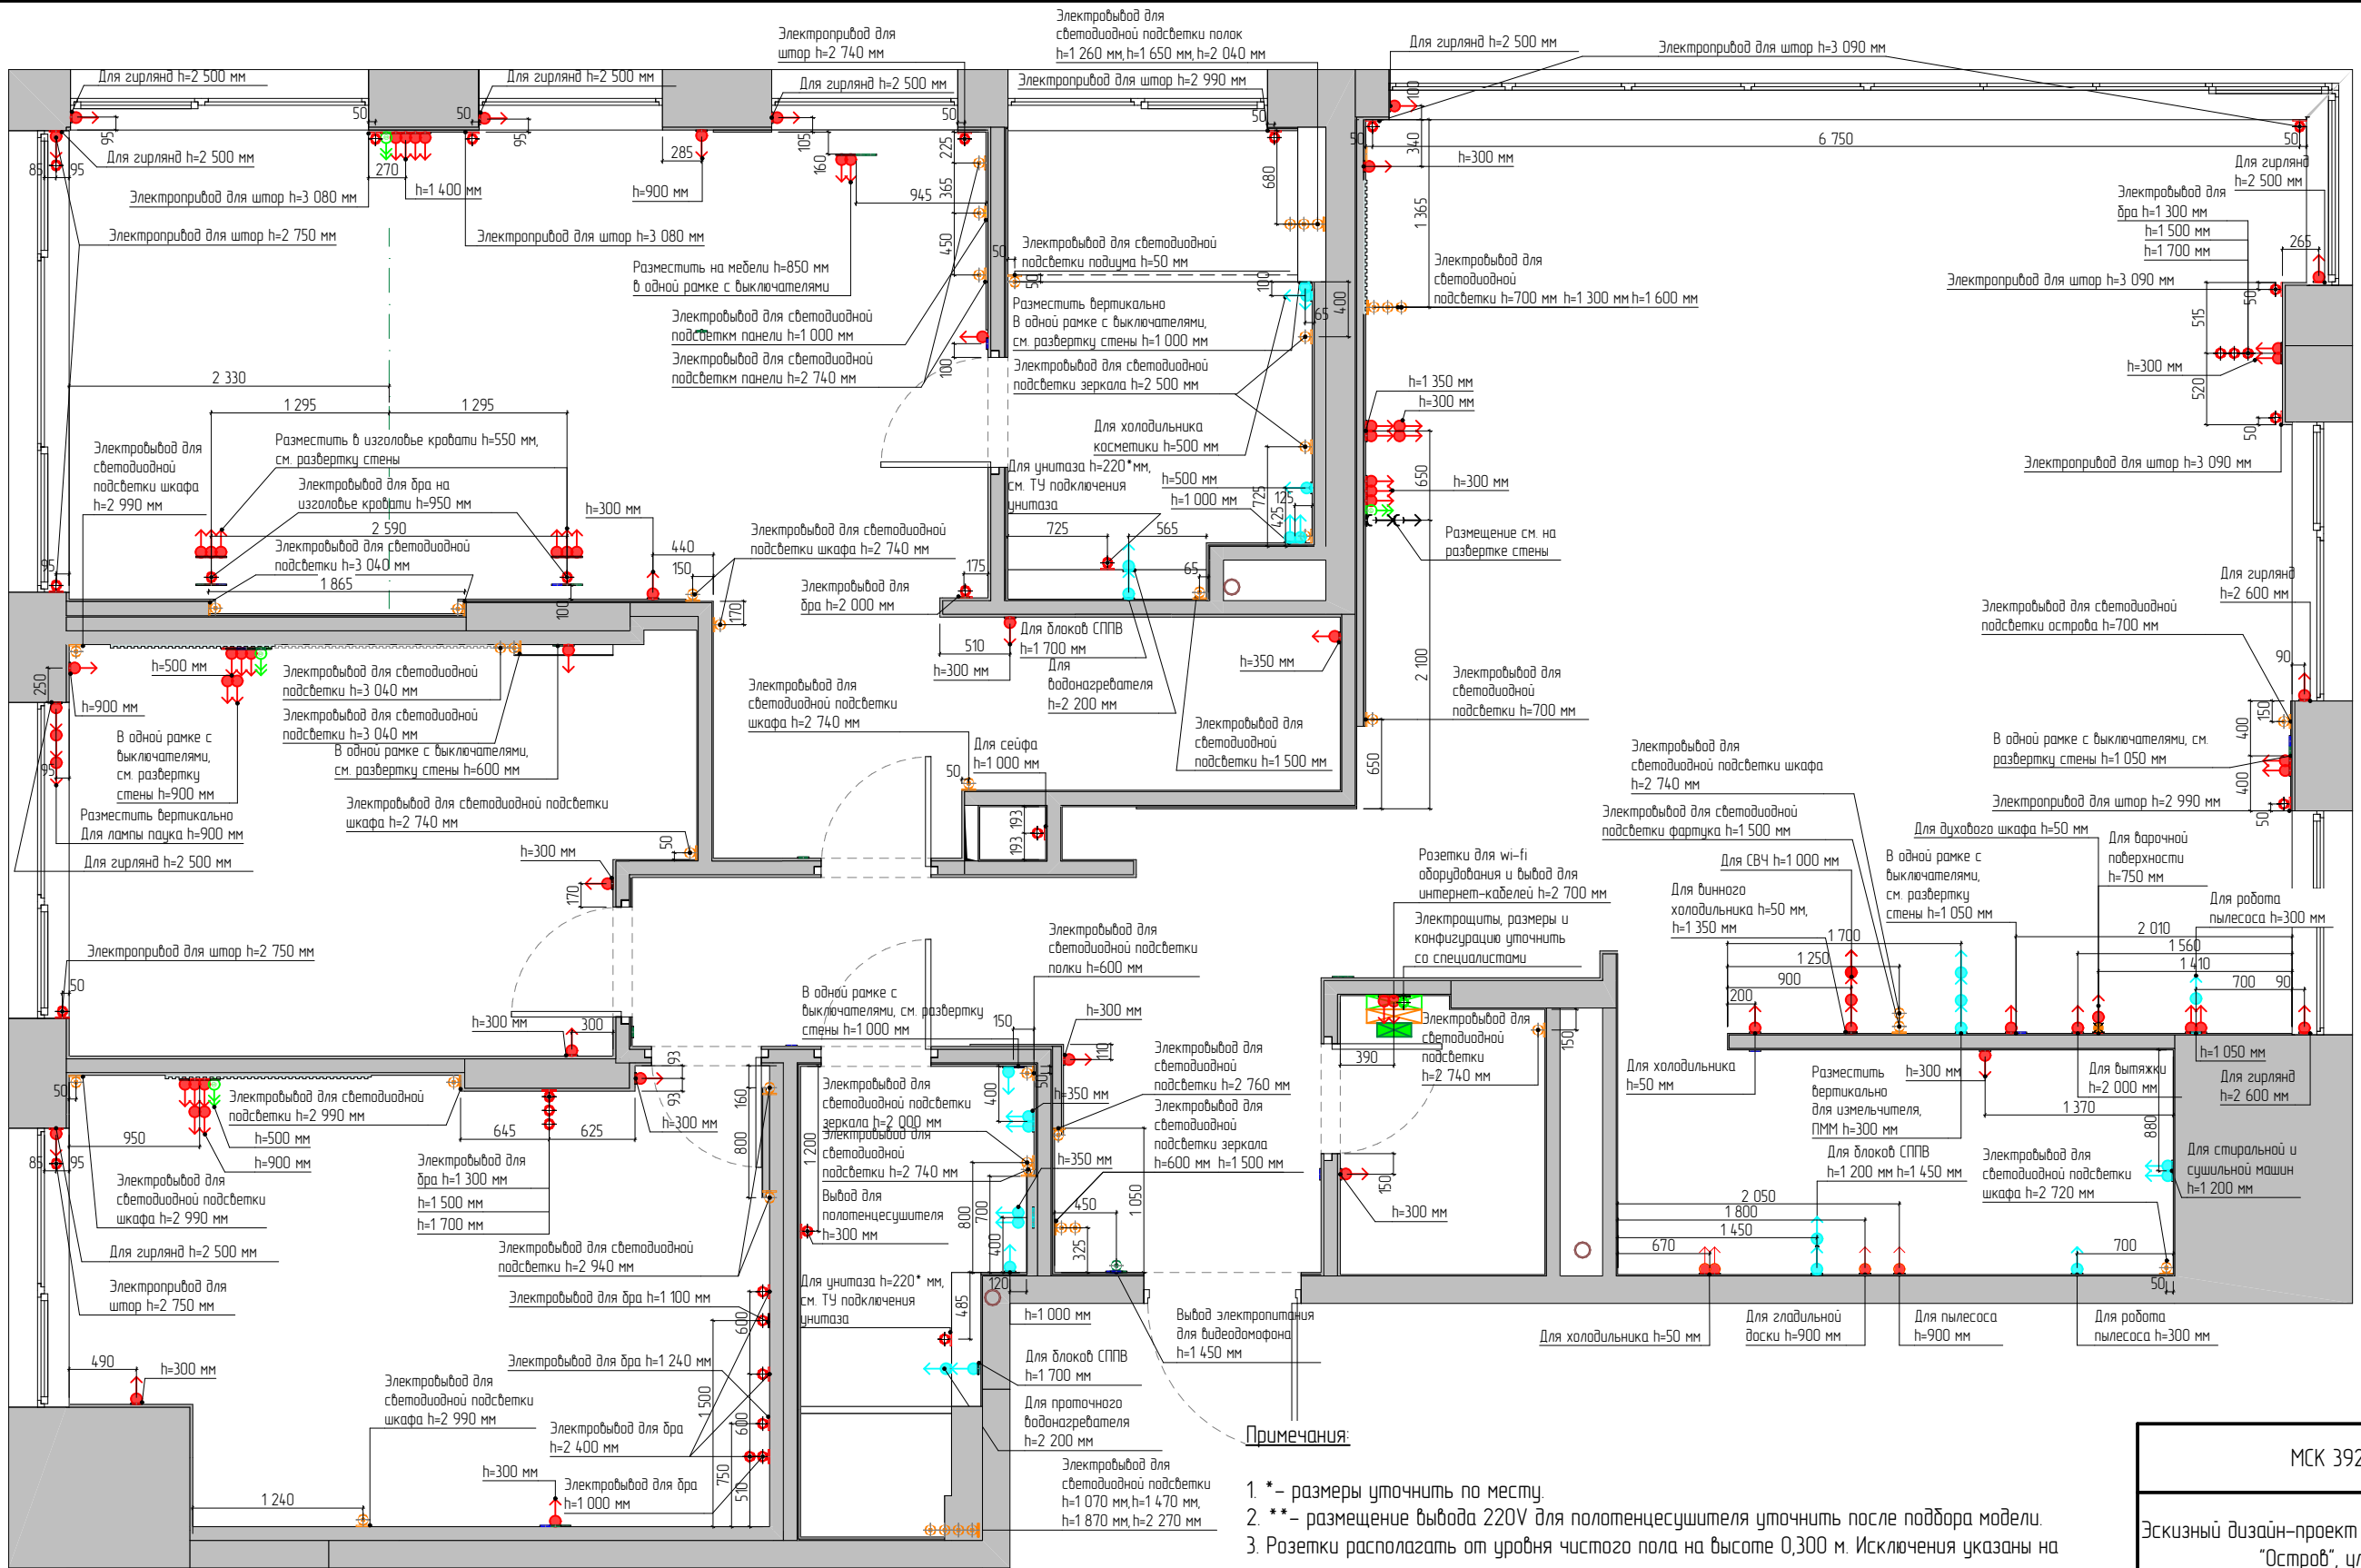

Условные обозначения:



Электрощит



Слаботочный щит



Розетка 220V влагозащищенная



Розетка 220V



Выход электрокабеля для светодиодной ленты



Выход электрокабеля для варочной поверхности



Выход спец. кабеля



Выход интернет кабеля



Выход 220V



wi-fi оборудование


Примечания:

- * – размеры уточнить по месту.
- ** – размещение вывода 220V для полотенцесушителя уточнить после подбора модели.
- Розетки располагать от уровня чистого пола на высоте 0,300 м. Исключения указаны на чертеже.
- Приязку и размещение розеток и выводов кухонного гарнитура согласовать с изготовителями после подбора мебели заказчиком.
- Размещение и габаритные размеры электрощита согласовать со специалистами.
- Предусмотреть совместимость видеодомофона квартиры с общедомовой системой.
- К WI-FI оборудованию подвести _ выводов интернет-кабеля из расчета: общее количество интернет выводов и розеток + один (вывод в квартиру из подъезда). Размещение wi-fi оборудования и усилителей для него определить по месту, вызов предварительно на объект специалистов.
- Размещение всех выводов и розеток согласовать со специалистами «Умный дом».
- Размеры и характеристики радиаторов отопления согласовать со специалистами, предусмотреть терморегуляторы.
- Датчики пожарной и охранной сигнализации и электровыбоы для них разместить совместно со специалистами, предварительно вызвав их на объект.
- Размещение и монтаж стабилизатора напряжения согласовать со специалистами.
- Размещение розеток и электровыводов по высоте см. на развертках стен.

МСК 392.12.25-ЭП ПРЕМИУМ

Эскизный дизайн-проект интерьера квартиры в г. Москва ЖК "Остров", ул. Нижние Мневники д. 7

План размещения электрооборудования.

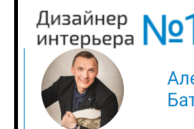

Александр Батеньков

Стадия

Лист

Листов

ЭП

19

120

Подп.

Дата

Г.АП


Батеньков А.С.

Гл. дизайнер

Власова В.А.

Гл. проектиров.

Лунькова В.Н.

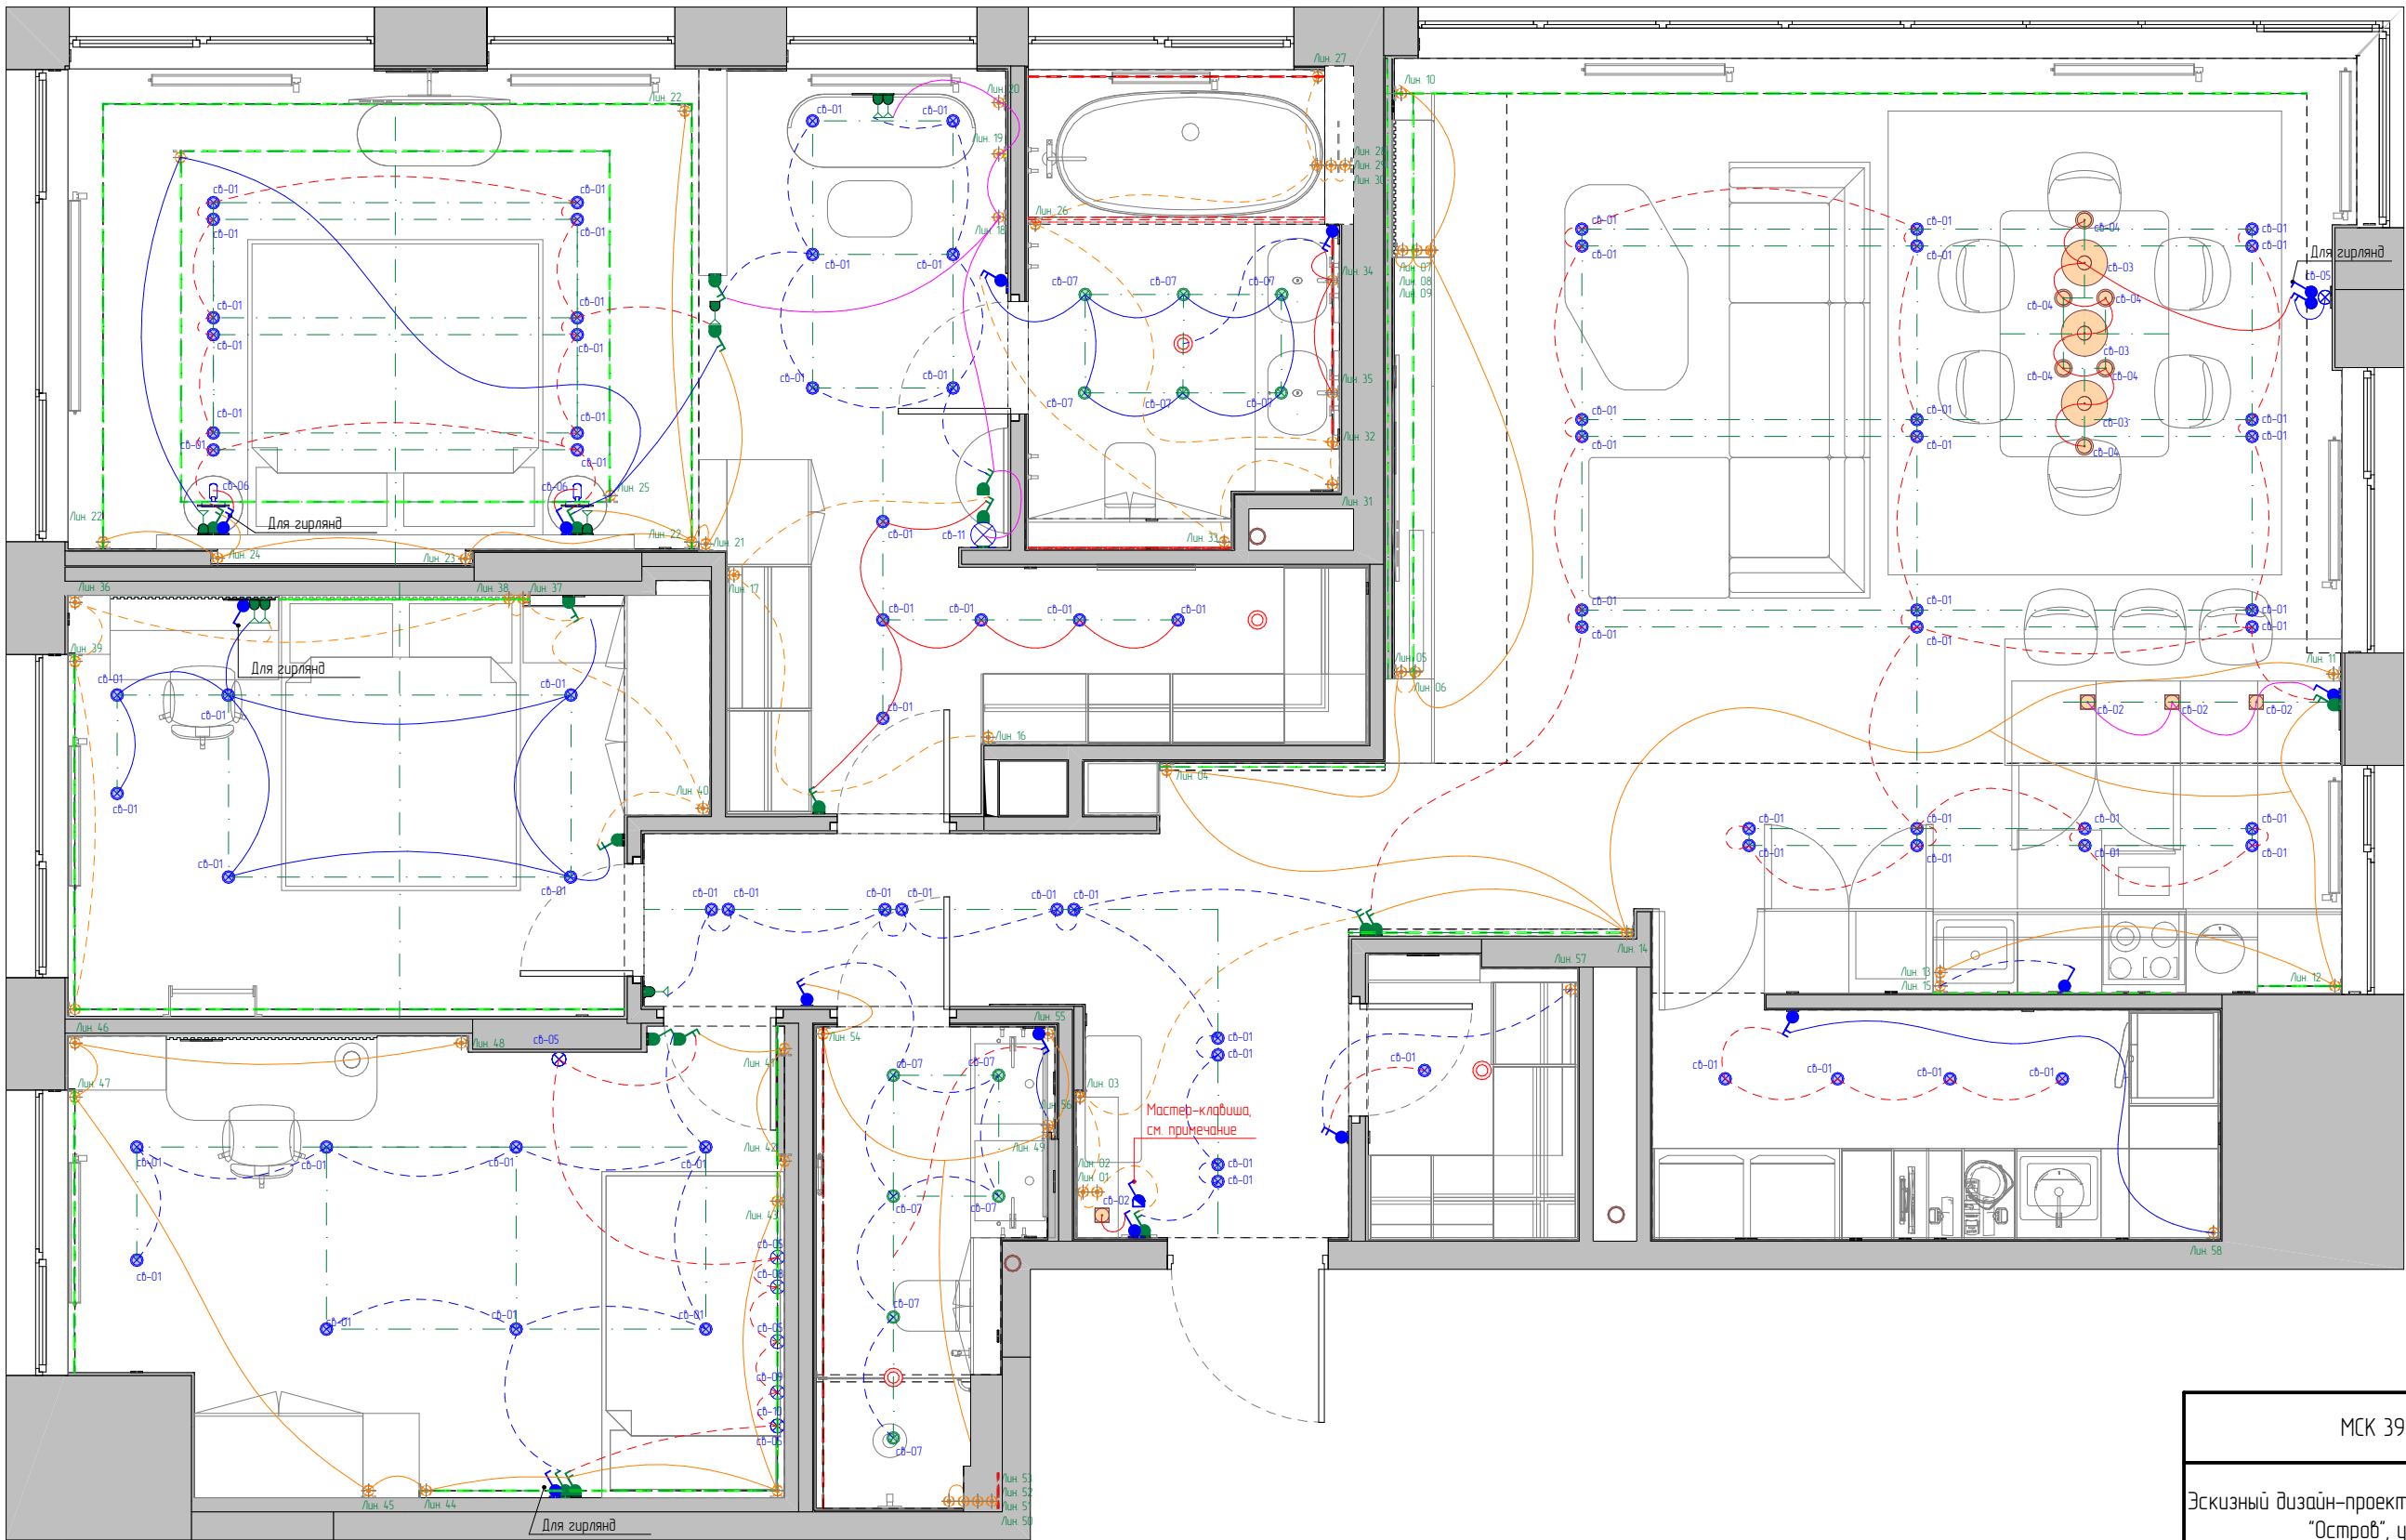

Условные обозначения:

- | | | | |
|--|--|--|--|
| | Выход 220V | | Мастер-клавиша |
| | Выход электрокабеля для светодиодной ленты | | Выключатель двухклавишный |
| | Выключатель одноклавишный | | Переключатель одноклавишный переходной |
| | Диффузор, вытяжка | | Светильник точечный встраиваемый |
| | Люстра подвесная потолочная | | Светильник точечный встраиваемый влагозащищенный |
| | Переключатель двухклавишный | | Светодиодная лента |
| | | | Светодиодная лента, влагозащищенная |

Примечания:

- * – размеры уточнить по месту.
- Выключатели располагать от уровня чистого пола на высоте 0,900 м. Исключения указаны на чертеже.
- Светильники, встроенные в мебель, согласовать с изготовителями мебели.
- Мастер клавиши:
№1 – выключение всего освещения квартиры, размещение согласовать с заказчиком при начале строительных работ;
№2 – выключение электропитания (розетки) кроме холодильника, морозильных камер, охранной сигнализации, датчиков протечки и др. по согласованию с заказчиком непосредственно на объекте.



МСК 392.12.25-ЭП ПРЕМИУМ



Эскизный дизайн-проект интерьера квартиры в г. Москва ЖК "Остров", ул. Нижние Мневники д. 7

План размещения групп включения освещения с мебелью.


Дизайнер интерьера №1 Александр Батеньков	Стадия	Лист	Листов
	ЭП	20	120
		Подп.	Дата
ГАП	Батеньков А.С.		
Гл. дизайнер	Власова В.А.		
Гл. проектиров.	Луныкова В.Н.		

Ведомость розеток и выключателей			
Условный вид	Наименование	Кол-во	Примечание
Гардероб №1			
	Рамка на 1 пост	1	
	Рамка на 3 поста	1	
	Розетка 220V	3	
Гардероб №2			
	Переключатель двухклавишный	1	
	Рамка на 1 пост	3	
	Розетка 220V	2	
Душевая			
	Выключатель двухклавишный	1	
	Рамка на 1 пост	3	
	Рамка на 2 поста	3	
	Розетка 220V, влагозащищенная IP44 и выше	8	
Кладовая			
	Выключатель двухклавишный	1	
	Рамка на 1 пост	7	
	Рамка на 2 поста	2	
	Розетка 220V	5	
	Розетка 220V, влагозащищенная IP44 и выше	5	
Коридор			
	Выключатель двухклавишный	2	
	Выключатель одноклавишный	1	
	Мастер-клавиша	1	
	Переключатель двухклавишный	3	
	Переключатель одноклавишный переходной	1	
	Рамка на 1 пост	5	
	Рамка на 2 поста	2	
	Розетка 220V	1	

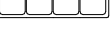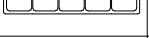Ведомость розеток и выключателей			
Условный вид	Наименование	Кол-во	Примечание
Кухня-гостиная			
	Выключатель одноклавишный	2	
	Интернет-розетка двойная	1	
	Кабель-канал (2 медельные заглушки)	2	
	Переключатель двухклавишный	1	
	Рамка на 1 пост	13	
	Рамка на 2 поста	6	
	Рамка на 3 поста	1	
	Рамка на 4 поста	1	
	Рамка на 5 постов	1	
	Розетка 220V	25	
	Розетка 220V, влагозащищенная IP44 и выше	4	
Мастер-ванная			
	Выключатель двухклавишный	1	
	Рамка на 1 пост	4	
	Рамка на 2 поста	2	
	Розетка 220V, влагозащищенная IP44 и выше	7	
Мастер-спальня			
	Выключатель двухклавишный	2	
	Выключатель одноклавишный	1	
	Интернет-розетка двойная	1	
	Переключатель двухклавишный	6	
	Переключатель одноклавишный переходной	5	
	Рамка на 1 пост	8	
	Рамка на 2 поста	1	
	Рамка на 3 поста	5	
	Рамка на 4 поста	1	

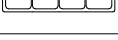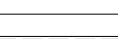
Ведомость розеток и выключателей			
Условный вид	Наименование	Кол-во	Примечание
	Рамка на 5 постов	1	
	Розетка 220V	19	
Спальня №1			
	Выключатель одноклавишный	1	
	Интернет-розетка двойная	1	
	Переключатель двухклавишный	2	
	Переключатель одноклавишный	2	
	Рамка на 1 пост	4	
	Рамка на 2 поста	2	
	Рамка на 3 поста	1	
	Рамка на 4 поста	1	
	Розетка 220V	9	
Спальня №2			
	Выключатель одноклавишный	1	
	Интернет-розетка двойная	1	
	Переключатель двухклавишный	2	
	Переключатель одноклавишный переходной	2	
	Рамка на 1 пост	5	
	Рамка на 2 поста	2	
	Рамка на 4 поста	1	
	Рамка на 5 постов	1	
	Розетка 220V	12	

МСК 392.12.25-ЭП ПРЕМИУМ			
Эскизный дизайн-проект интерьера квартиры в г. Москва ЖК "Остров", ул. Нижние Мневники д. 7			
Ведомость розеток и выключателей.			
Дизайнер интерьера  №1 Александр Батеньков	Стадия	Лист	Листов
	ЭП	22	120
		Подп.	Дата
Г.АП	Батеньков А.С.		
Гл. дизайнер	Власова В.А.		
Гл. проектиров.	Луцькова В.Н.		

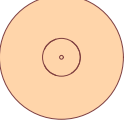Ведомость осветительных приборов				
№	Обозначение	Наименование	Кол-во	Примечание
Гардероб №1				
сб-01		Светильник точечный встраиваемый	1	шт.
Гардероб №2				
сб-01		Светильник точечный встраиваемый	5	шт.
Душевая				
сб-07		Светильник точечный встраиваемый влагозащищенный	6	шт.
Кладовая				
сб-01		Светильник точечный встраиваемый	4	шт.
Коридор				
сб-01		Светильник точечный встраиваемый	10	шт.
сб-02		Светильник подвесной потолочный	1	шт.
Кухня-гостиная				
сб-01		Светильник точечный встраиваемый	26	шт.
сб-02		Светильник подвесной потолочный	3	шт.
сб-03		Светильник подвесной потолочный	3	шт.
сб-04		Светильник подвесной потолочный	6	шт.
сб-05		Светильник настенный (бра)	3	шт.
Мастер-ванная				
сб-07		Светильник точечный встраиваемый влагозащищенный	6	шт.
Мастер-спальня				
сб-01		Светильник точечный встраиваемый	19	шт.
сб-06		Светильник настенный (бра)	2	шт.
сб-11		Светильник настенный (бра)	1	шт.

Ведомость осветительных приборов				
№	Обозначение	Наименование	Кол-во	Примечание
Спальня №1				
сб-01		Светильник точечный встраиваемый	8	шт.
сб-05		Светильник настенный (бра)	6	шт.
сб-08		Светильник настенный (бра)	1	шт.
сб-09		Светильник настенный (бра)	1	шт.
сб-10		Светильник настенный (бра)	1	шт.
Спальня №2				
сб-01		Светильник точечный встраиваемый	6	шт.

МСК 392.12.25-ЭП ПРЕМИУМ			
Эскизный дизайн-проект интерьера квартиры в г. Москва ЖК "Остров", ул. Нижние Мневники д. 7			
ИнтерьерВедомость осветительных приборов.			
Дизайнер интерьера  №1 Александр Батеньков	Стадия	Лист	Листов
	ЭП	23	120
		Подп.	Дата
ГАП	Батеньков А.С.		
Гл. дизайнер	Власова В.А.		
Гл. проектиров.	Луныкова В.Н.		
Разработал	Ильина Е.Е.		

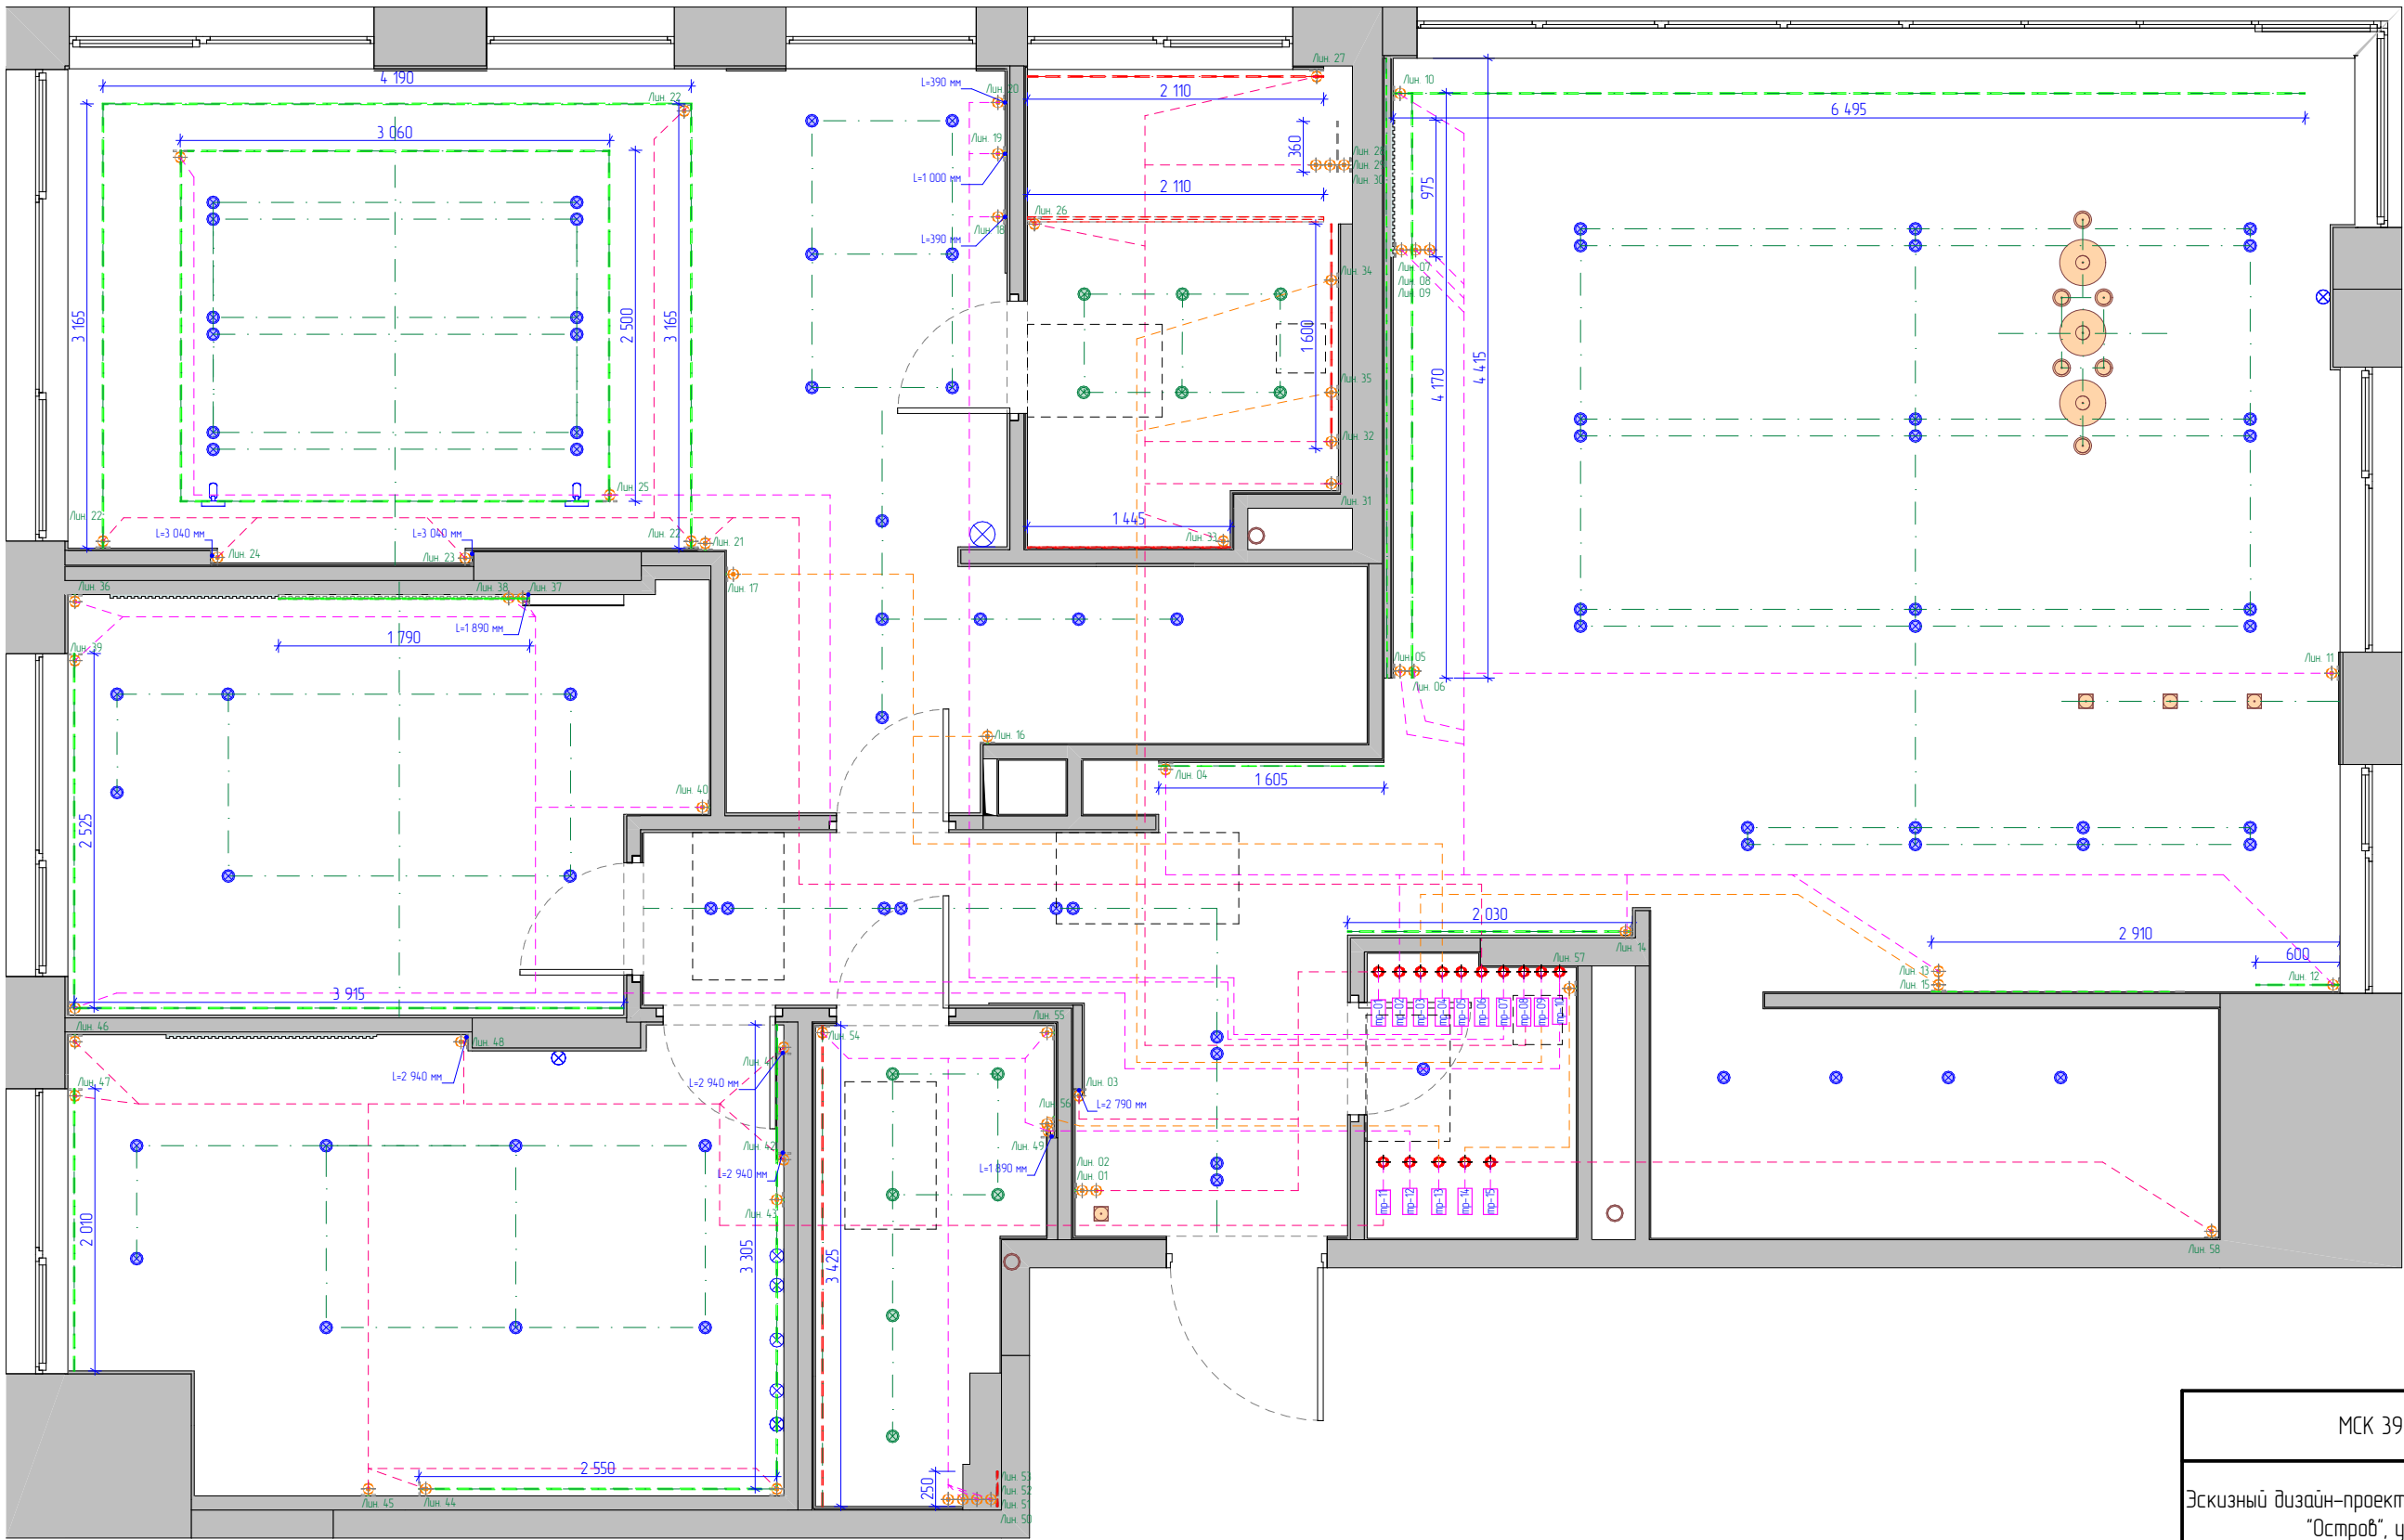

Условные обозначения:

- 

Выход 220V
- 

Выход электрокабеля для светодиодной ленты
- 

Диффузор, вытяжка
- 

Люстра подвесная потолочная
- 

Светильник точечный встраиваемый
- 

Светильник точечный встраиваемый влагозащищенный
- 

Светодиодная лента
- 

Светодиодная лента, влагозащищенная
- 

Трансформатор для светодиодной ленты

Примечания:

- * – размеры уточнить по месту после выполнения черновых отделочных работ.
- Предусмотреть люки скрытого монтажа для доступа к трансформаторам.
- Количество контроллеров уточнить со специалистами из расчета один контроллер на одну группу включения.
- Предусмотрены встраиваемые точечные светильники со светодиодными лампами (220 V), уточнить при выборе светильников и ламп.
- Для расчета мощности трансформаторов (блоков питания) для светодиодных лент расчетная потребляемая мощность на 1 м.п. ленты взята: лин. 1 (сверхяркая) –19,2 Вт/м, лин. 2–30 – 9,6 Вт/м. При покупке ленты и трансформаторов проверить со специалистами.

МСК 392.12.25–ЭП ПРЕМИУМ

Эскизный дизайн-проект интерьера квартиры в г. Москва ЖК "Остров", ул. Нижние Мневники д. 7


Схема размещения трансформаторов, контроллеров и блока управления освещением

Дизайнер интерьера  Александр Батеньков	Стадия	Лист	Листов
	ЭП	24	120
		Подп.	Дата
Г.АП	Батеньков А.С.		
Гл. дизайнер	Власова В.А.		
Гл. проектиров.	Луцькова В.Н.		

Ведомость трансформаторов и светодиодных лент						
Обозначение	Тр-р	Длина, м.п	Кол-во тр-р, шт	Цвет ленты t	Имя профиля	Помещение
Лин. 01	Тр-01	-	1	2700-3000 К**	Профиль уточнить с изготовителями зеркала	Коридор
Лин. 02	Тр-01	-		2700-3000 К**	Профиль уточнить с изготовителями зеркала	Коридор
Лин. 03	Тр-01	2,790		2700-3000 К**	Профиль уточнить при закупе, подсветка ниши	Коридор
Лин. 04	Тр-02	1,605	1	2700-3000 К**	Профиль уточнить при закупе, закарнизная подсветка	Коридор
Лин. 05	Тр-02	4,170		2700-3000 К**	Профиль уточнить при закупе, подсветка ниши	Кухня-гостиная
Лин. 06	Тр-02	4,415		2700-3000 К**	Профиль уточнить при закупе, закарнизная подсветка	Кухня-гостиная
Лин. 07	Тр-02	0,975		2700-3000 К**	Профиль уточнить при закупе,подсветка плинтуса	Кухня-гостиная
Лин. 08	Тр-02	0,975		2700-3000 К**	Профиль уточнить при закупе,подсветка плинтуса	Кухня-гостиная
Лин. 09	Тр-02	0,975		2700-3000 К**	Профиль уточнить при закупе,подсветка плинтуса	Кухня-гостиная
Лин. 10	Тр-02	6,495		2700-3000 К**	Профиль уточнить при закупе,подсветка плинтуса	Кухня-гостиная
Лин. 11	Тр-02			2700-3000 К**	Профиль уточнить с изготовителями кухни	Кухня-гостиная
Лин. 12	Тр-02	0,600		2700-3000 К**	Профиль уточнить при закупе, закарнизная подсветка	Кухня-гостиная
Лин. 13	Тр-02	-		2700-3000 К**	Профиль уточнить с изготовителями кухни	Кухня-гостиная
Лин. 14	Тр-02	2,030		2700-3000 К**	Профиль уточнить при закупе, закарнизная подсветка	Коридор
Лин. 15	Тр-03	-	1	2700-3000 К**	Профиль уточнить с изготовителями кухни	Кухня-гостиная
Лин. 16	Тр-04	-	1	2700-3000 К**	Профиль уточнить с изготовителями мебели	Гардероб №2
Лин. 17	Тр-04	-		2700-3000 К**	Профиль уточнить с изготовителями мебели	Гардероб №2
Лин. 18	Тр-05	0,390	1	2700-3000 К**	Профиль уточнить при закупе, подсветка ниши	Мастер-спальня
Лин. 19	Тр-05	1,000		2700-3000 К**	Профиль уточнить при закупе, подсветка ниши	Мастер-спальня
Лин. 20	Тр-05	0,390		2700-3000 К**	Профиль уточнить при закупе, подсветка ниши	Мастер-спальня
Лин. 21	Тр-06	-	1	2700-3000 К**	Профиль уточнить с изготовителями мебели	Мастер-спальня
Лин. 22	Тр-06	6,33		2700-3000 К**	Профиль уточнить при закупе, закарнизная подсветка	Мастер-спальня
Лин. 22	Тр-06	4,190		2700-3000 К**	Профиль уточнить при закупе, закарнизная подсветка	Мастер-спальня
Лин. 23	Тр-06	3,040		2700-3000 К**	Профиль уточнить при закупе, подсветка ниши	Мастер-спальня
Лин. 24	Тр-06	3,040		2700-3000 К**	Профиль уточнить при закупе, подсветка ниши	Мастер-спальня
Лин. 25	Тр-07	5,000	1	2700-3000 К**	Профиль уточнить при закупе, закарнизная подсветка	Мастер-ванная
Лин. 25	Тр-07	6,120		2700-3000 К**	Профиль уточнить при закупе, закарнизная подсветка	Мастер-ванная
Лин. 26	Тр-08	2,110	1	2700-3000 К**	Профиль уточнить при закупе, закарнизная подсветка	Мастер-ванная
Лин. 27	Тр-08	2,110		2700-3000 К**	Профиль уточнить при закупе, закарнизная подсветка	Мастер-ванная
Лин. 28	Тр-08	0,360		2700-3000 К**	Профиль уточнить при закупе, подсветка ниши	Мастер-ванная
Лин. 29	Тр-08	0,360		2700-3000 К**	Профиль уточнить при закупе, подсветка ниши	Мастер-ванная
Лин. 30	Тр-08	0,360		2700-3000 К**	Профиль уточнить при закупе, подсветка ниши	Мастер-ванная
Лин. 31	Тр-08	-		2700-3000 К**	Профиль уточнить с изготовителями мебели	Мастер-ванная
Лин. 32	Тр-08	1,600		2700-3000 К**	Профиль уточнить при закупе, закарнизная подсветка	Мастер-ванная
Лин. 33	Тр-08	1,445		2700-3000 К**	Профиль уточнить с изготовителями мебели	Мастер-ванная
Лин. 34	Тр-09	-	1	2700-3000 К**	Профиль уточнить с изготовителями зеркала	Мастер-ванная
Лин. 35	Тр-09	-		2700-3000 К**	Профиль уточнить с изготовителями зеркала	Мастер-ванная
Лин. 36	Тр-10	-	1	2700-3000 К**	Профиль уточнить с изготовителями мебели	Спальня №2
Лин. 37	Тр-10	1,890		2700-3000 К**	Профиль уточнить при закупе, подсветка ниши	Спальня №1
Лин. 38	Тр-10	1,790		2700-3000 К**	Профиль уточнить при закупе, подсветка ниши	Спальня №2
Лин. 39	Тр-10	3,915		2700-3000 К**	Профиль уточнить при закупе, закарнизная подсветка	Спальня №2
Лин. 39	Тр-10	2,525		2700-3000 К**	Профиль уточнить при закупе, закарнизная подсветка	Спальня №2
Лин. 40	Тр-10	-		2700-3000 К**	Профиль уточнить с изготовителями мебели	Спальня №2
Лин. 41	Тр-11	2,940	1	2700-3000 К**	Профиль уточнить при закупе, подсветка ниши	Спальня №1
Лин. 42	Тр-11	2,940		2700-3000 К**	Профиль уточнить при закупе, подсветка ниши	Спальня №1
Лин. 43	Тр-11	-		2700-3000 К**	Профиль уточнить с изготовителями мебели	Спальня №1

Ведомость трансформаторов и светодиодных лент						
Обозначение	Тр-р	Длина, м.п	Кол-во тр-р, шт	Цвет ленты t	Имя профиля	Помещение
Лин. 44	Тр-11	3,305		2700-3000 К**	Профиль уточнить при закупе, закарнизная подсветка	Спальня №1
Лин. 44	Тр-11	2,550		2700-3000 К**	Профиль уточнить при закупе, закарнизная подсветка	Спальня №1
Лин. 45	Тр-11	-		2700-3000 К**	Профиль уточнить с изготовителями мебели	Спальня №1
Лин. 46	Тр-11	-		2700-3000 К**	Профиль уточнить с изготовителями мебели	Спальня №1
Лин. 47	Тр-11	2,010		2700-3000 К**	Профиль уточнить при закупе, закарнизная подсветка	Спальня №1
Лин. 48	Тр-11	2,890		2700-3000 К**	Профиль уточнить при закупе, подсветка ниши	Спальня №1
Лин. 49	Тр-12	1,890		2700-3000 К**	Профиль уточнить при закупе, подсветка ниши	Душевая
Лин. 50	Тр-12	0,25		2700-3000 К**	Профиль уточнить при закупе, подсветка ниши	Душевая
Лин. 51	Тр-12	0,25		2700-3000 К**	Профиль уточнить при закупе, подсветка ниши	Душевая
Лин. 52	Тр-12	0,25		2700-3000 К**	Профиль уточнить при закупе, подсветка ниши	Душевая
Лин. 53	Тр-12	0,25		2700-3000 К**	Профиль уточнить при закупе, подсветка ниши	Душевая
Лин. 54	Тр-12	3,425	1	2700-3000 К**	Профиль уточнить при закупе, закарнизная подсветка	Душевая
Лин. 55	Тр-12	-		2700-3000 К**	Профиль уточнить с изготовителями мебели	Душевая
Лин. 56	Тр-13	-	1	2700-3000 К**	Профиль уточнить с изготовителями зеркала	Душевая
Лин. 57	Тр-14	-	1	2700-3000 К**	Профиль уточнить с изготовителями мебели	Гардероб №1
Лин. 58	Тр-15	-	1	2700-3000 К**	Профиль уточнить с изготовителями мебели	Кладовая

МСК 392.12.25-ЭП ПРЕМИУМ			
Эскизный дизайн-проект интерьера квартиры в г. Москва ЖК "Остров", ул. Нижние Мневники д. 7			
Ведомость трансформаторов и светодиодных лент.			
Дизайнер интерьера  №1 Александр Батеньков	Стадия	Лист	Листов
	ЭП	25	120
		Подп.	Дата
Г.АП	Батеньков А.С.		
Гл. дизайнер	Власова В.А		
Гл. проектиров.	Луцькова В.Н.		

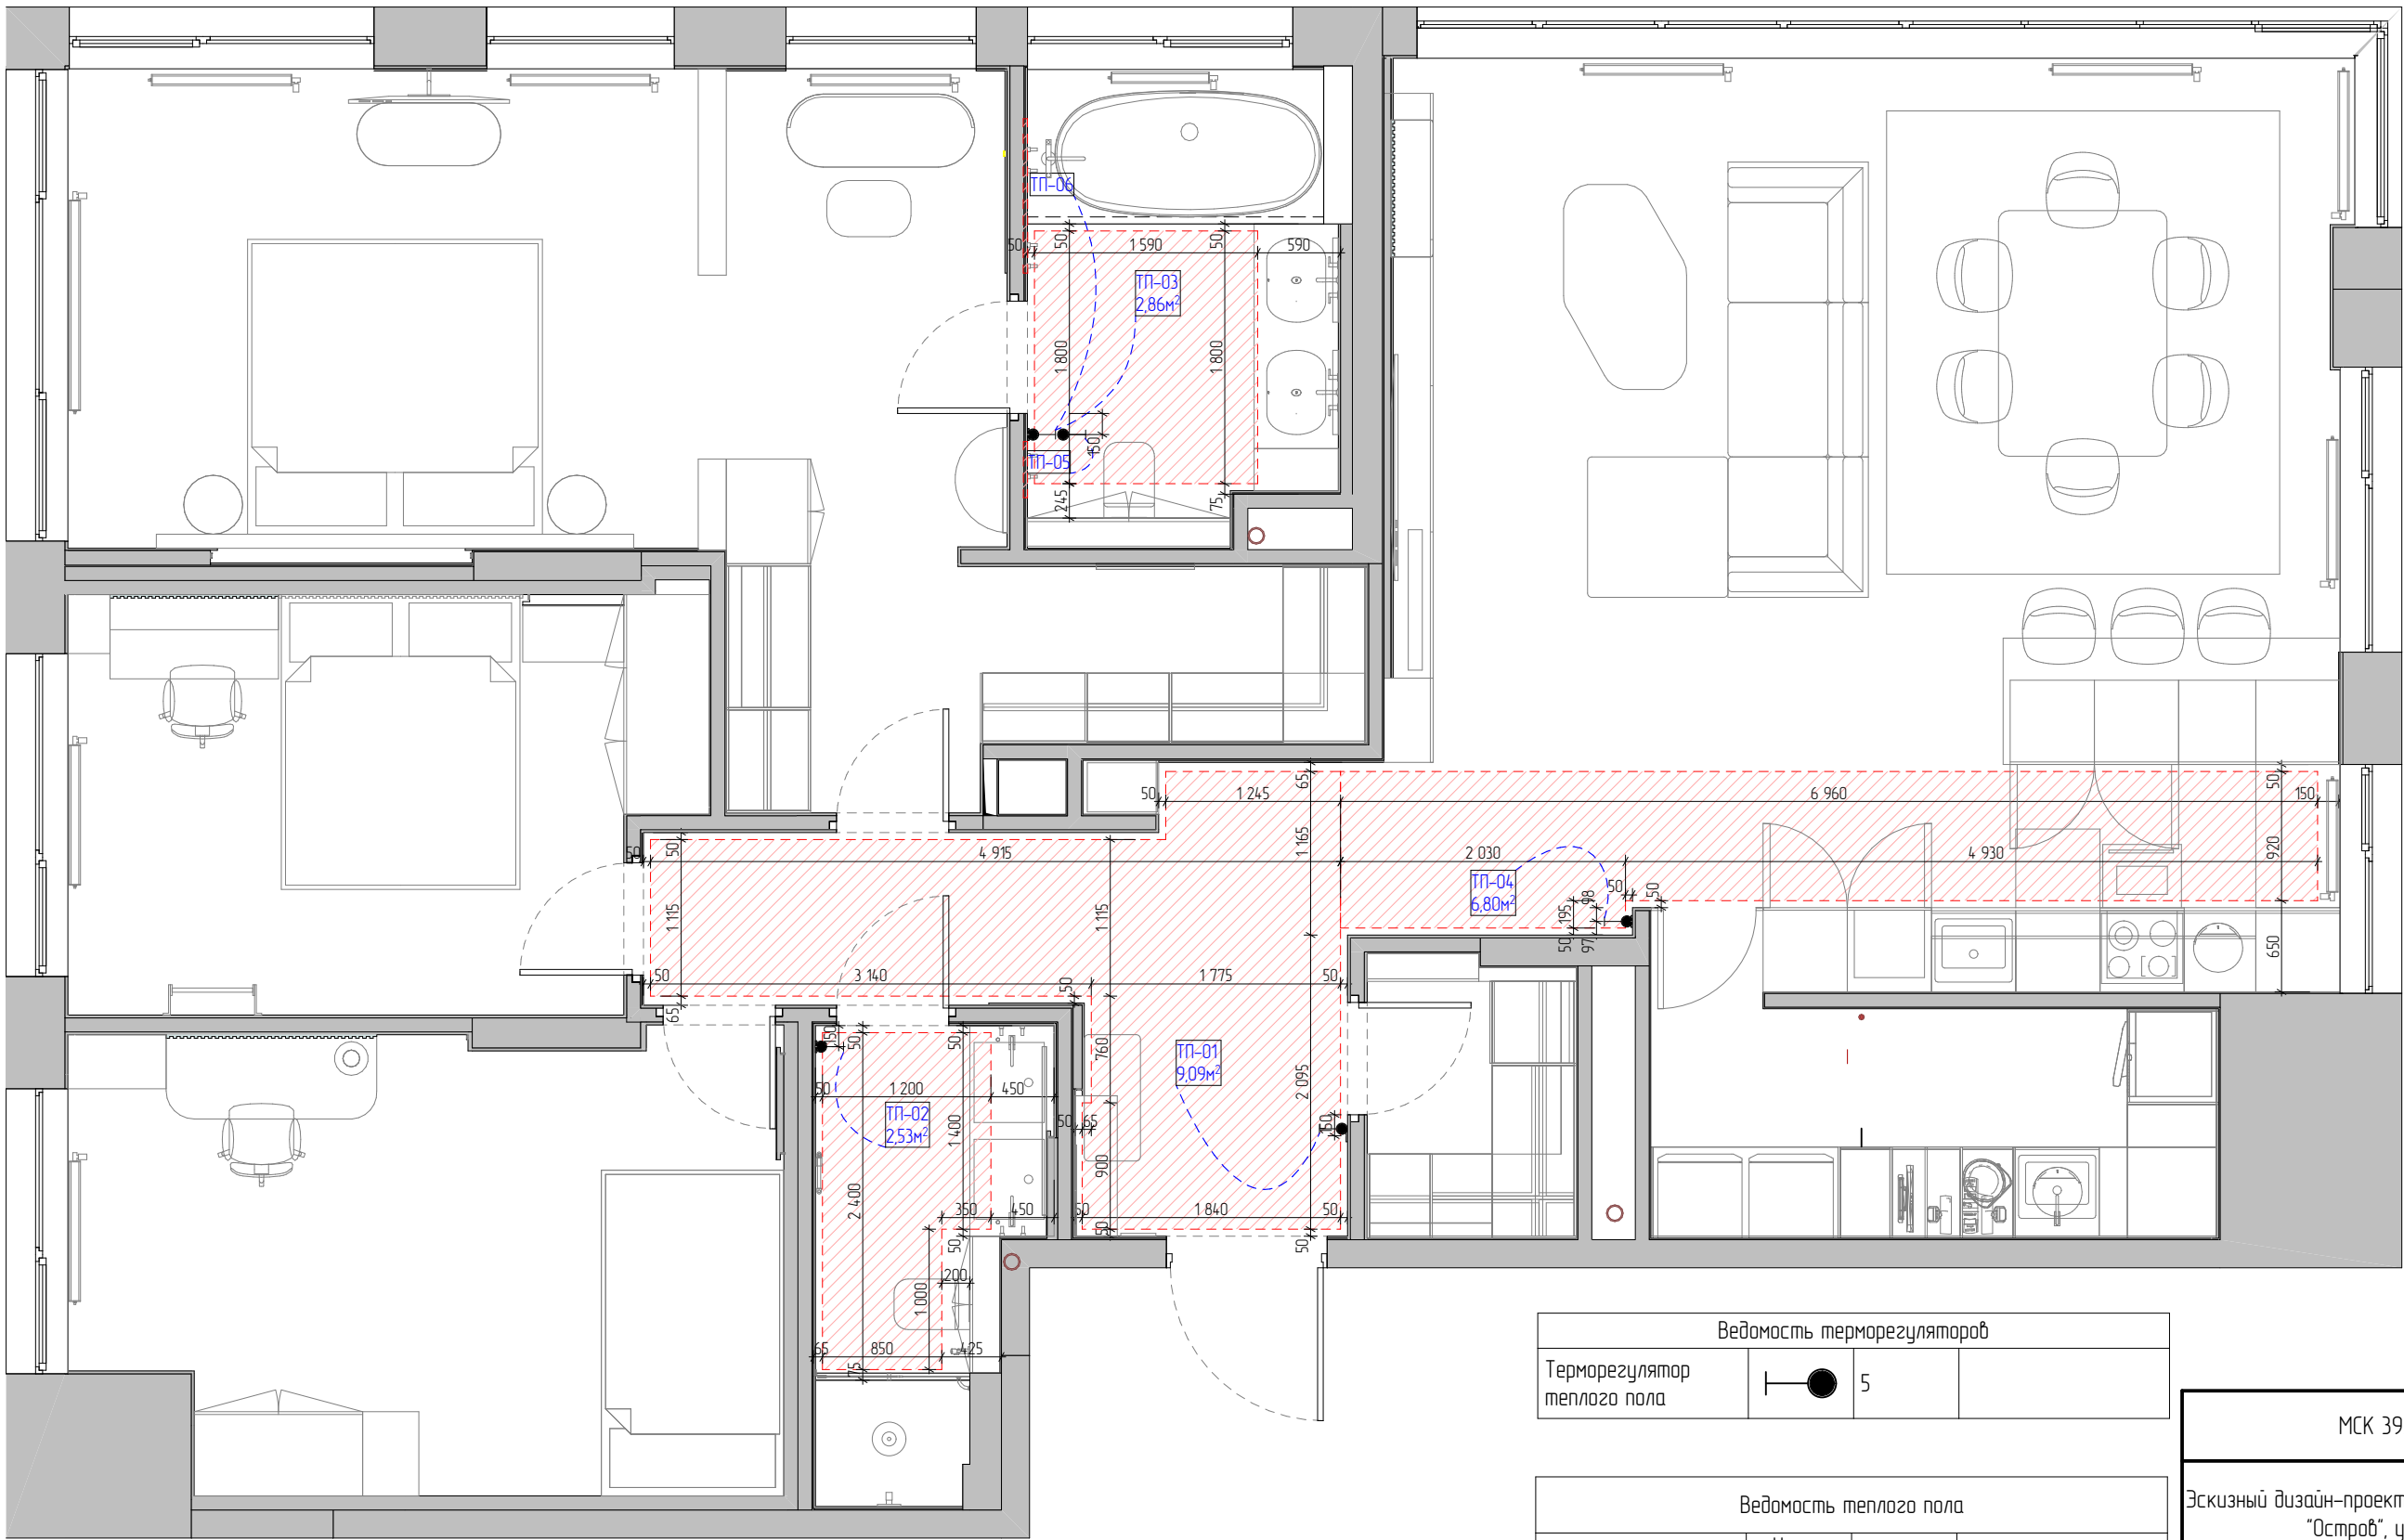


- Условные обозначения:
- Конструкции наружных стен
 - Существующие коммуникации (стояки)
 - Рadiator отопления
 - Теплый пол, электрические маты
 - Регулятор теплого пола

- Примечания:
- Регуляторы теплого пола располагать от уровня чистого пола на высоте 750 мм. Исключения указаны на чертеже.
 - Размеры и характеристики радиаторов отопления согласовать со специалистами, предусмотреть терморегуляторы.
 - Отступ теплого пола от стен и мебели выполнить 50 мм.
 - * – размеры уточнить по месту после выполнения черновых отделочных работ.

Ведомость терморегуляторов			
Терморегулятор теплого пола		5	

Ведомость теплого пола			
Помещение	Номер зоны	Площадь	Примечание
Коридор	ТП-01	9,09	
Душевая	ТП-02	2,53	
Мастер-ванная	ТП-03	2,86	
Кухня-гостиная	ТП-04	6,80	
Мастер-ванная	ТП-05	0,48	на стене, см. развертку
Мастер-ванная	ТП-06	1,32	на стене, см. развертку


МСК 392.12.25-ЭП ПРЕМИУМ			
Эскизный дизайн-проект интерьера квартиры в г. Москва ЖК "Остров", ул. Нижние Мневники д. 7			
План размещения теплого пола, терморегуляторов и приборов отопления.			
Дизайнер интерьера №1 Александр Батеньков	Стадия	Лист	Листов
	ЭП	26	120
		Подп.	Дата
Г.АП	Батеньков А.С.		
Гл. дизайнер	Власова В.А.		
Гл. проектиров.	Лунькова В.Н.		

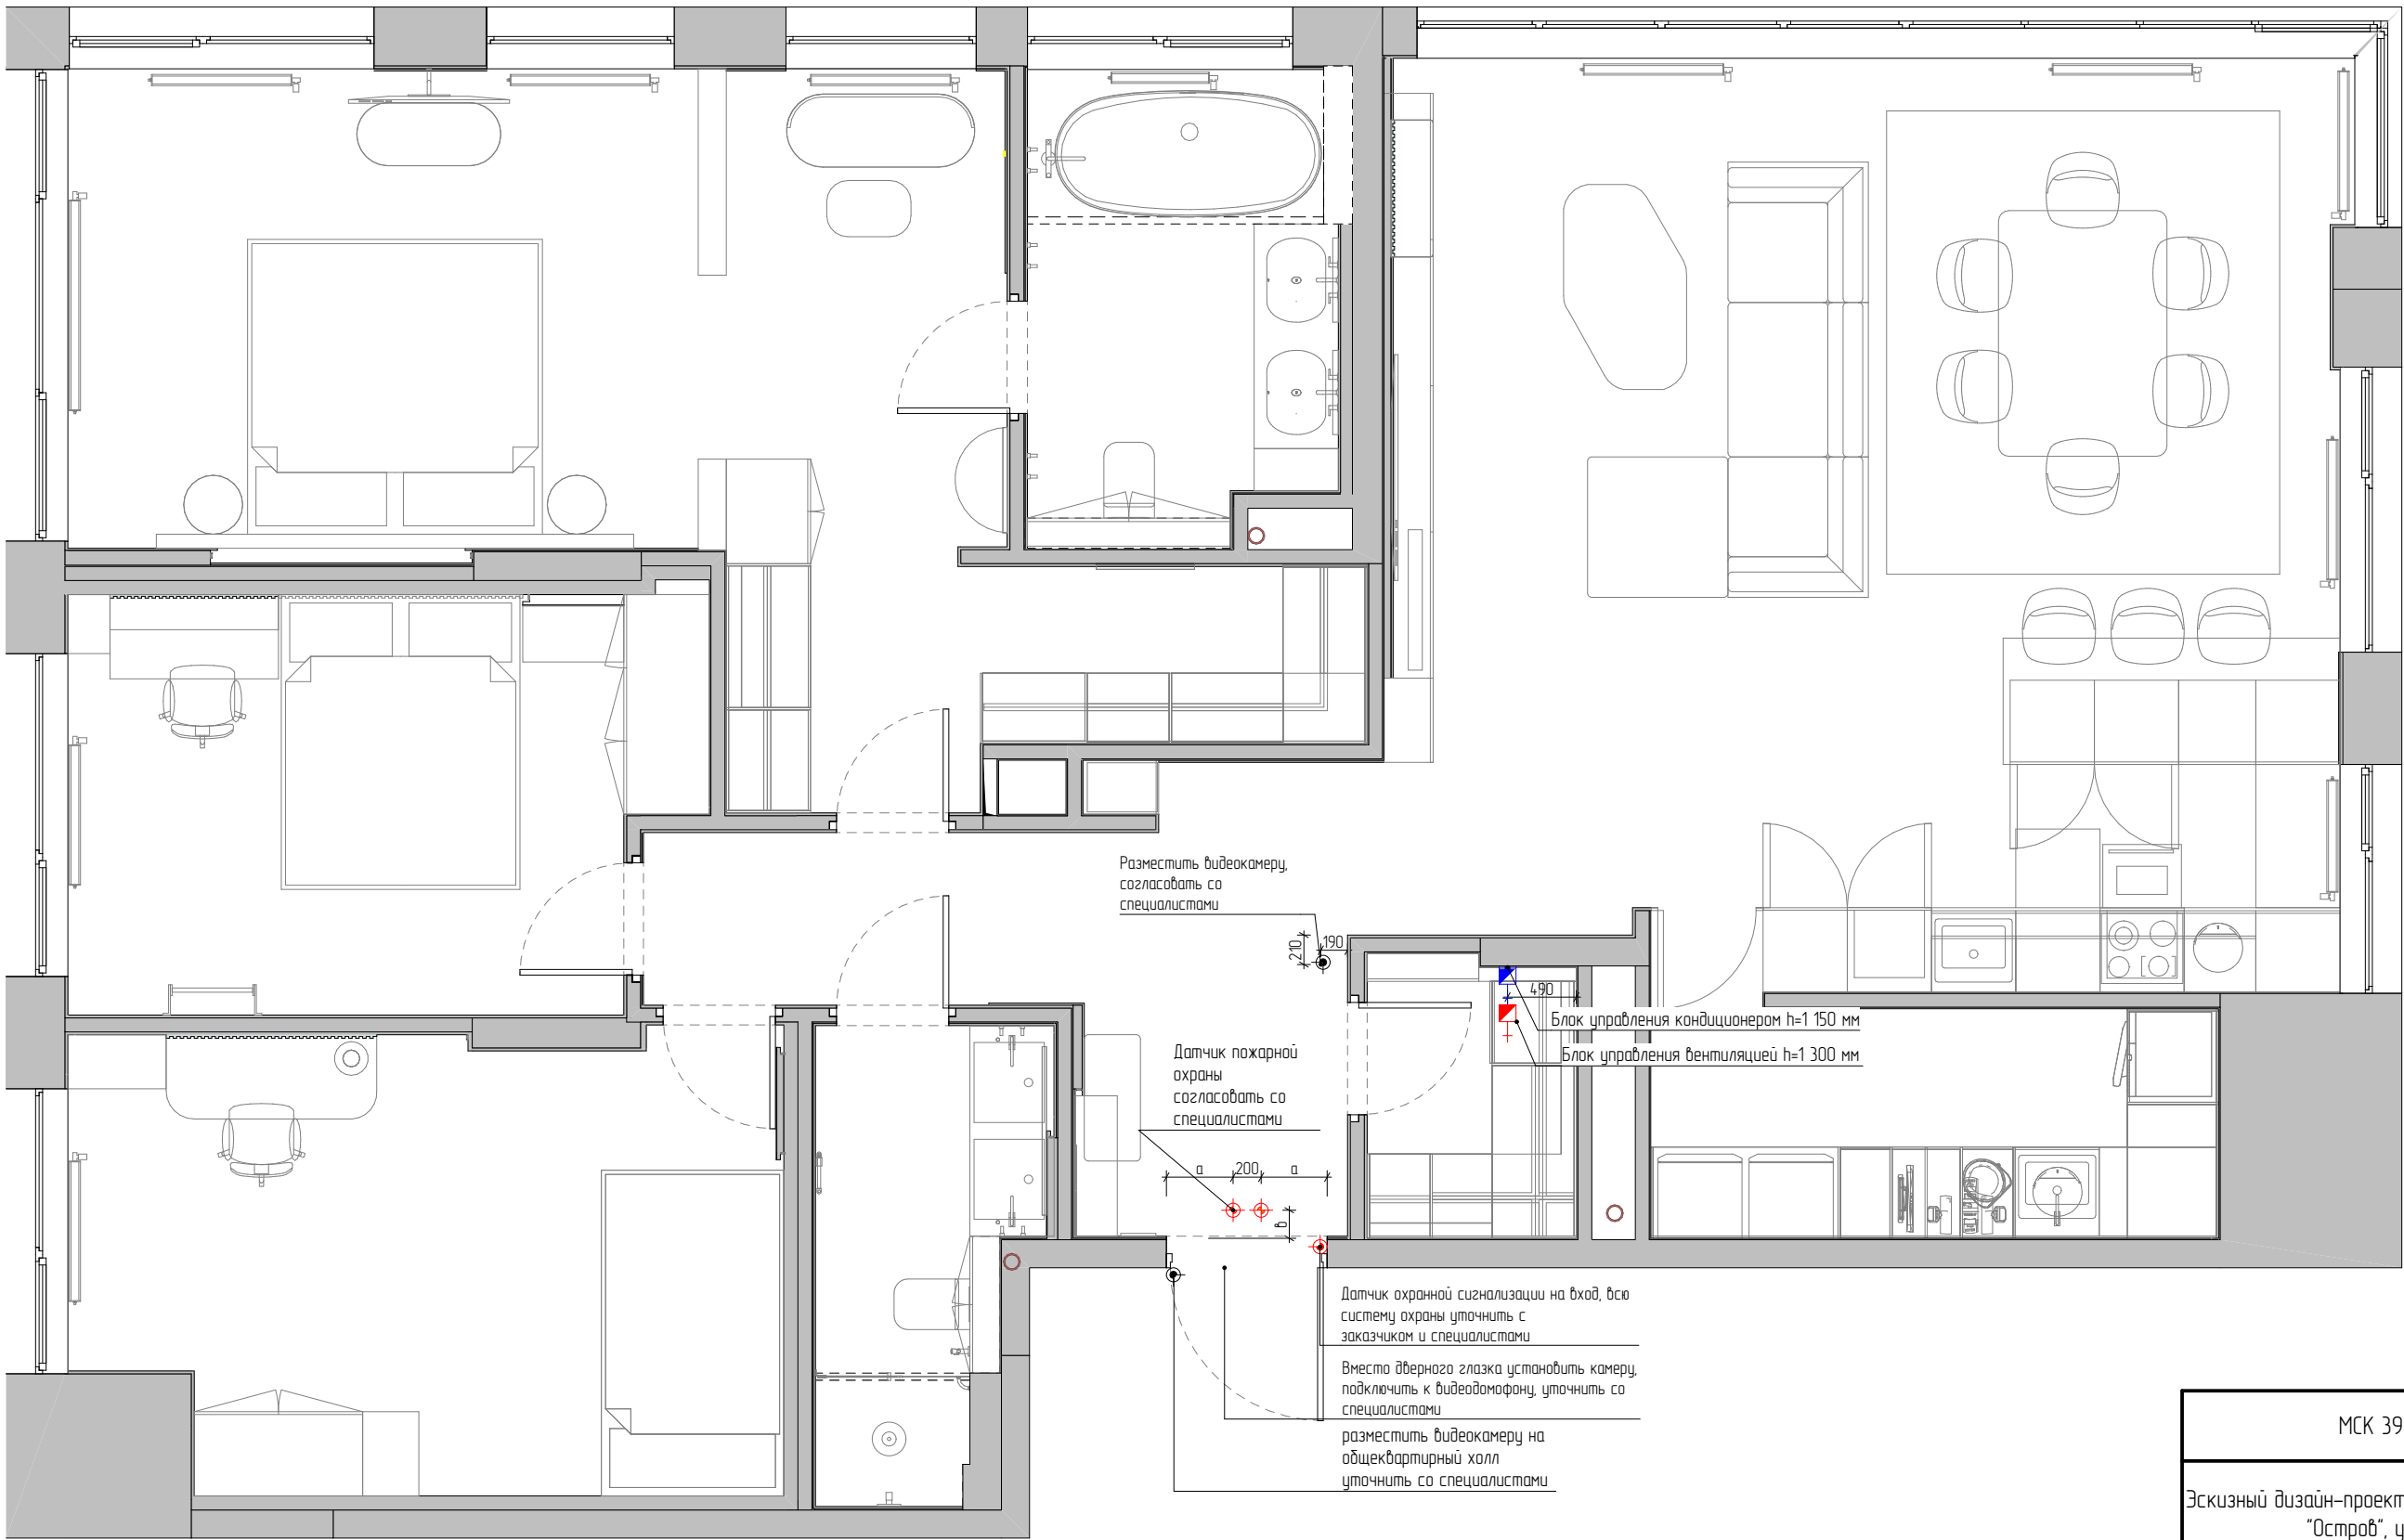

- Условные обозначения:
- Конструкции наружных стен
 - • Существующие коммуникации (стояки)
 - + Блок управления канальным кондиционером
 - + Блок управления вентиляционной системой
 - Камера видеонаблюдения
 - Датчик охранной сигнализации
 - Датчик пожарной сигнализации

Ведомость блоков управления			
Обозначение	Наименование	Количество	Примечание
+	Блок управления вентиляционной системой	1	
+	Блок управления канальным кондиционером	1	

МСК 392.12.25-ЭП ПРЕМИУМ			
Эскизный дизайн-проект интерьера квартиры в г. Москва ЖК "Остров", ул. Нижние Мневники д. 7			
План размещения блоков управления.			
Дизайнер интерьера №1 Александр Батеньков	Стадия	Лист	Листов
	ЭП	27	120
		Подп.	Дата
ГАП	Батеньков А.С.		
Гл. дизайнер	Власова В.А.		
Гл. проектиров.	Луныкова В.Н.		

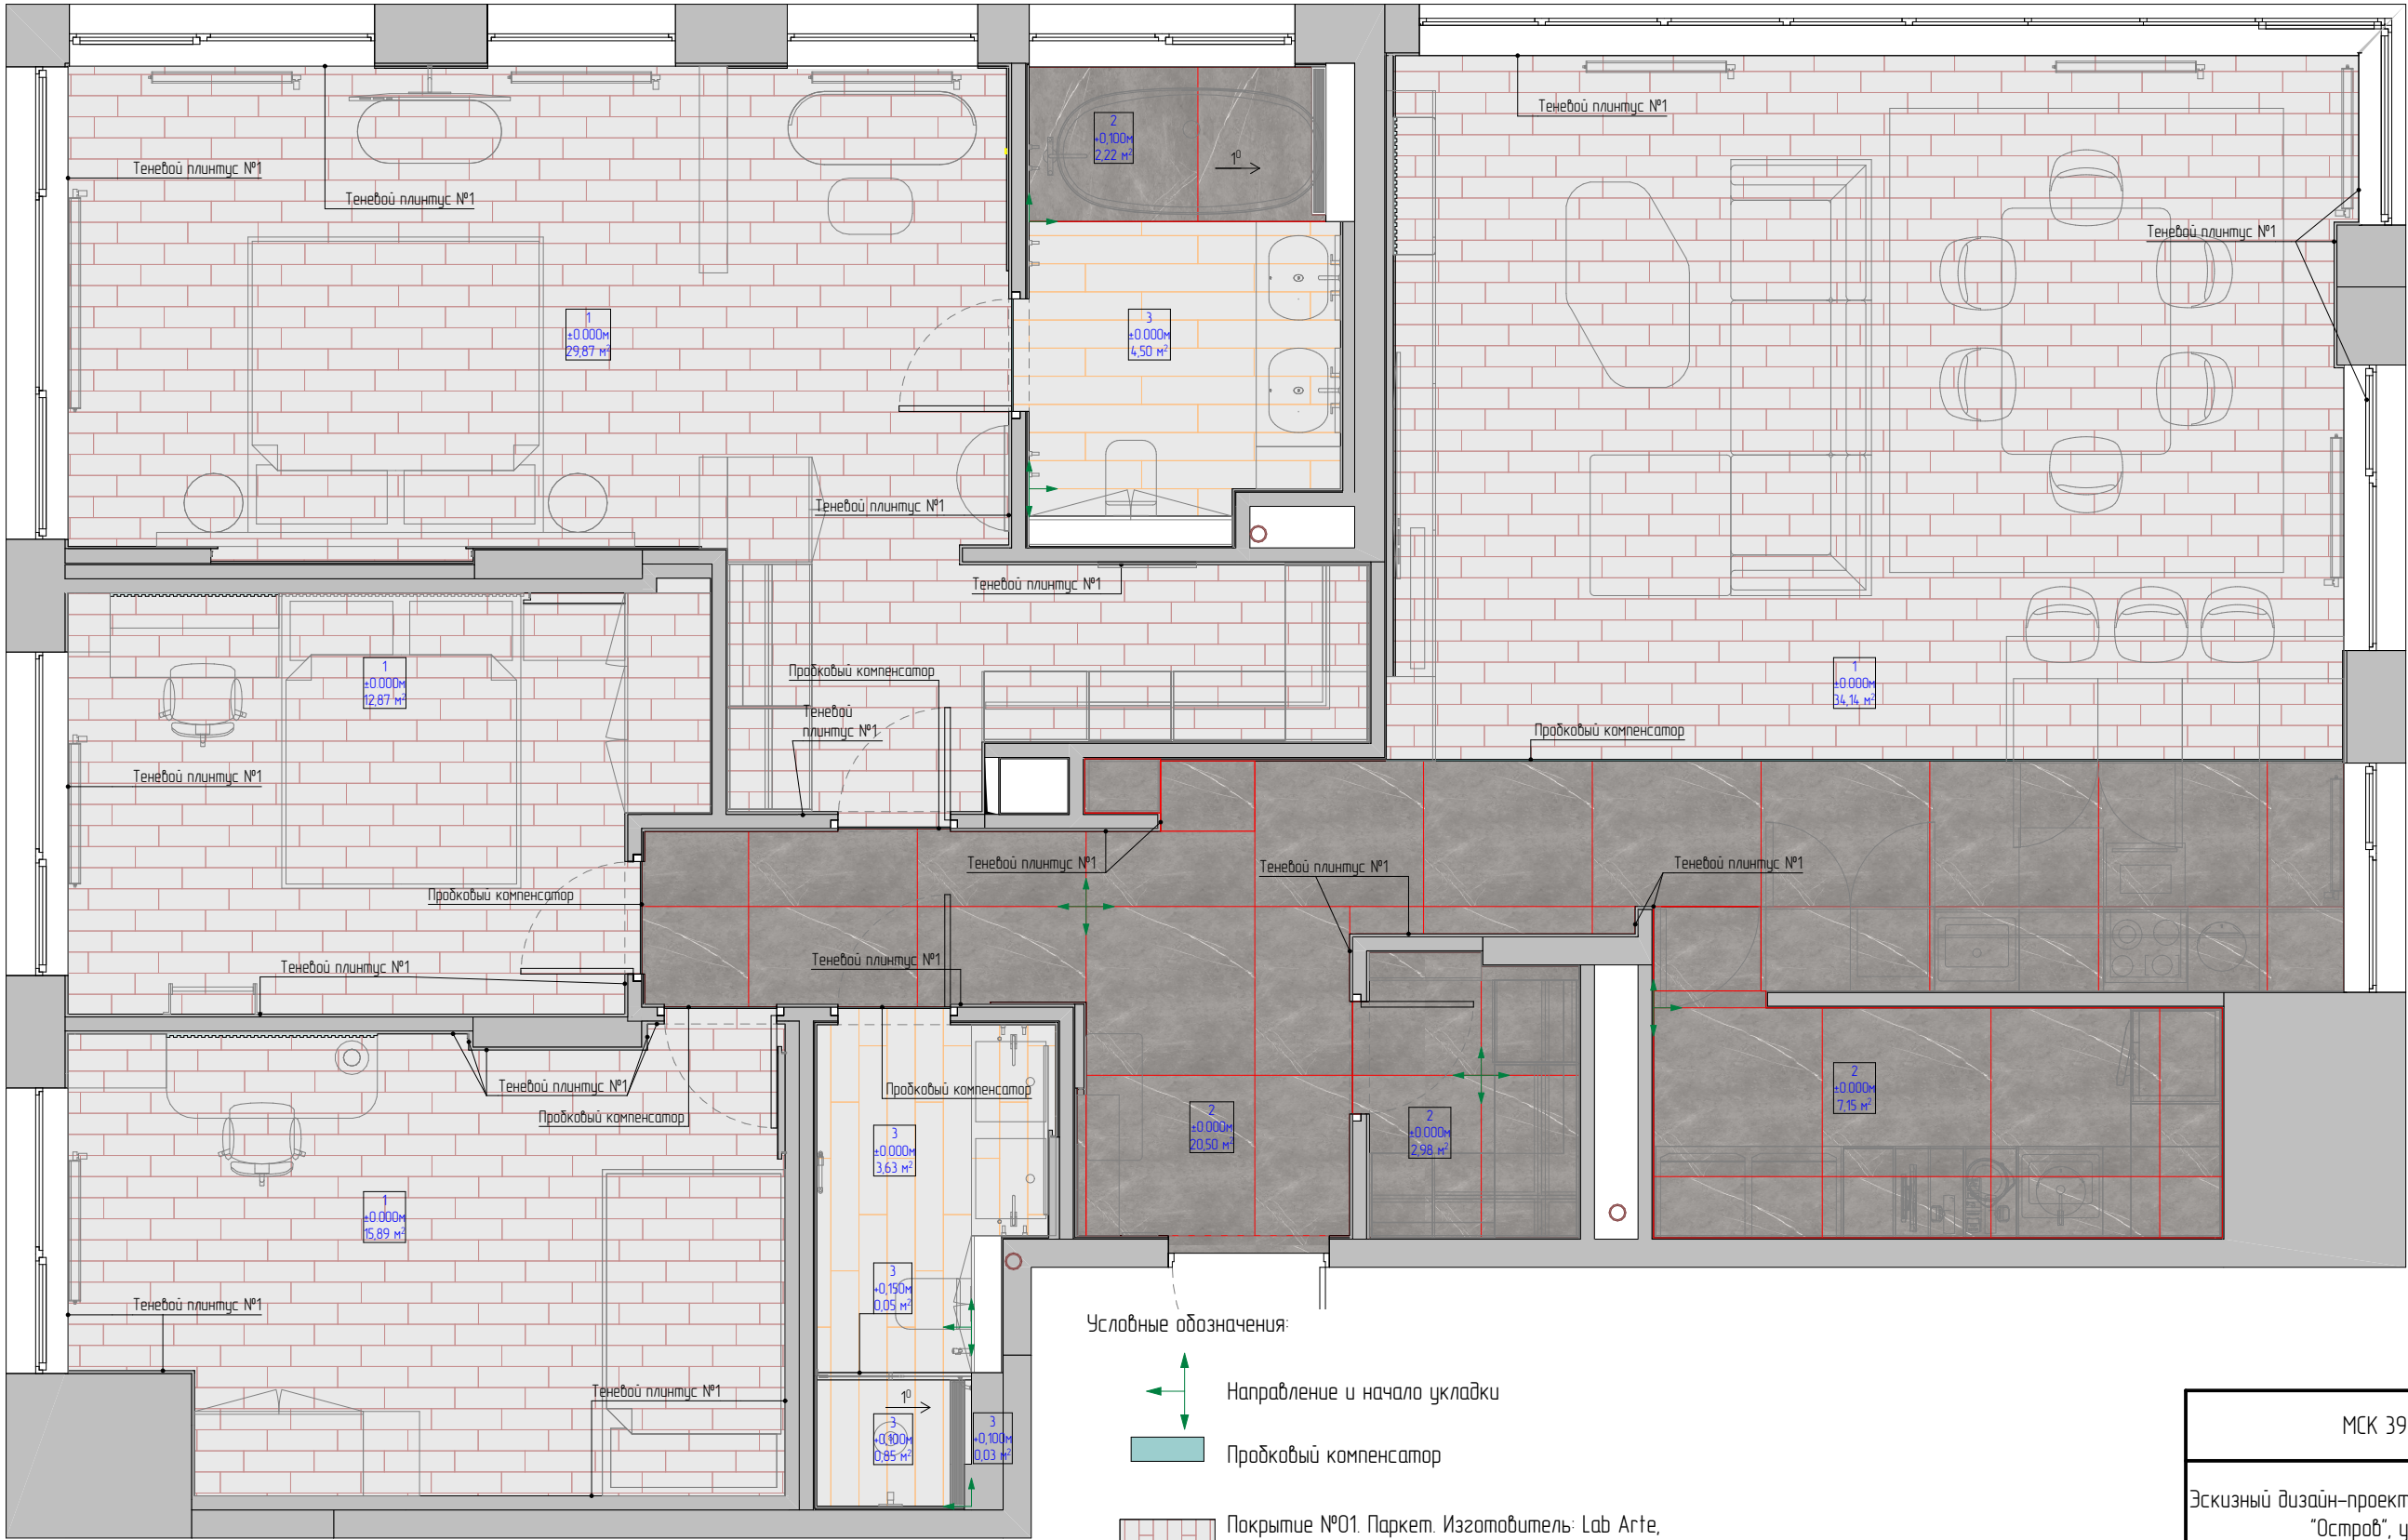


Примечания:

- * – размеры уточнить по месту после выполнения черновых отделочных работ.
- За отметку ±0,000 принят уровень чистого пола.
- Во влажных помещениях предусмотреть гидроизоляцию пола с заведением на стены до потолка.
- Совместить швы плитки на подиумах и основном полу.
- При монтаже напольных покрытий уточнить необходимость устройства дверных проемов с порогом.
- * – размеры уточнить по месту после выполнения черновых отделочных работ и установки дверей со скрытой коробкой.
- ** – размер уточнить по месту в зависимости от точного расположения полотна двери, стыковка двух разных напольных покрытий должна проходить точно по центру вдоль дверного полотна.

Условные обозначения:

- Направление и начало укладки
- Пробковый компенсатор
- Покрытие №01. Паркет. Изготовитель: Lab Arte, кол-я: Angle Дуб Натур, размер: 500x150 мм, точный артикул и производителя уточнить при выборе образца, толщину уточнить при закупке.
- Покрытие №02. Керамогранит. Изготовитель: Elegant Grey, кол-я: Forte Dei Marmi, размер: 1200x1200 мм, толщину уточнить при закупке.
- Покрытие №03. Керамогранит. Изготовитель: Nutmeg, кол-я: Woodslate Life, размер: 1200x200 мм, толщину уточнить при закупке.

МСК 392.12.25–ЭП ПРЕМИУМ			
Эскизный дизайн–проект интерьера квартиры в г. Москва ЖК "Остров", ул. Нижние Мневники д. 7			
Общий план полов с размещением мебели.			
Дизайнер интерьера №1 Александр Батеньков	Стадия	Лист	Листов
	ЭП	28	120
		Подп.	Дата
ГАП	Батеньков А.С.		
Гл. дизайнер	Власова В.А.		
Гл. проектиров.	Луцькова В.Н.		

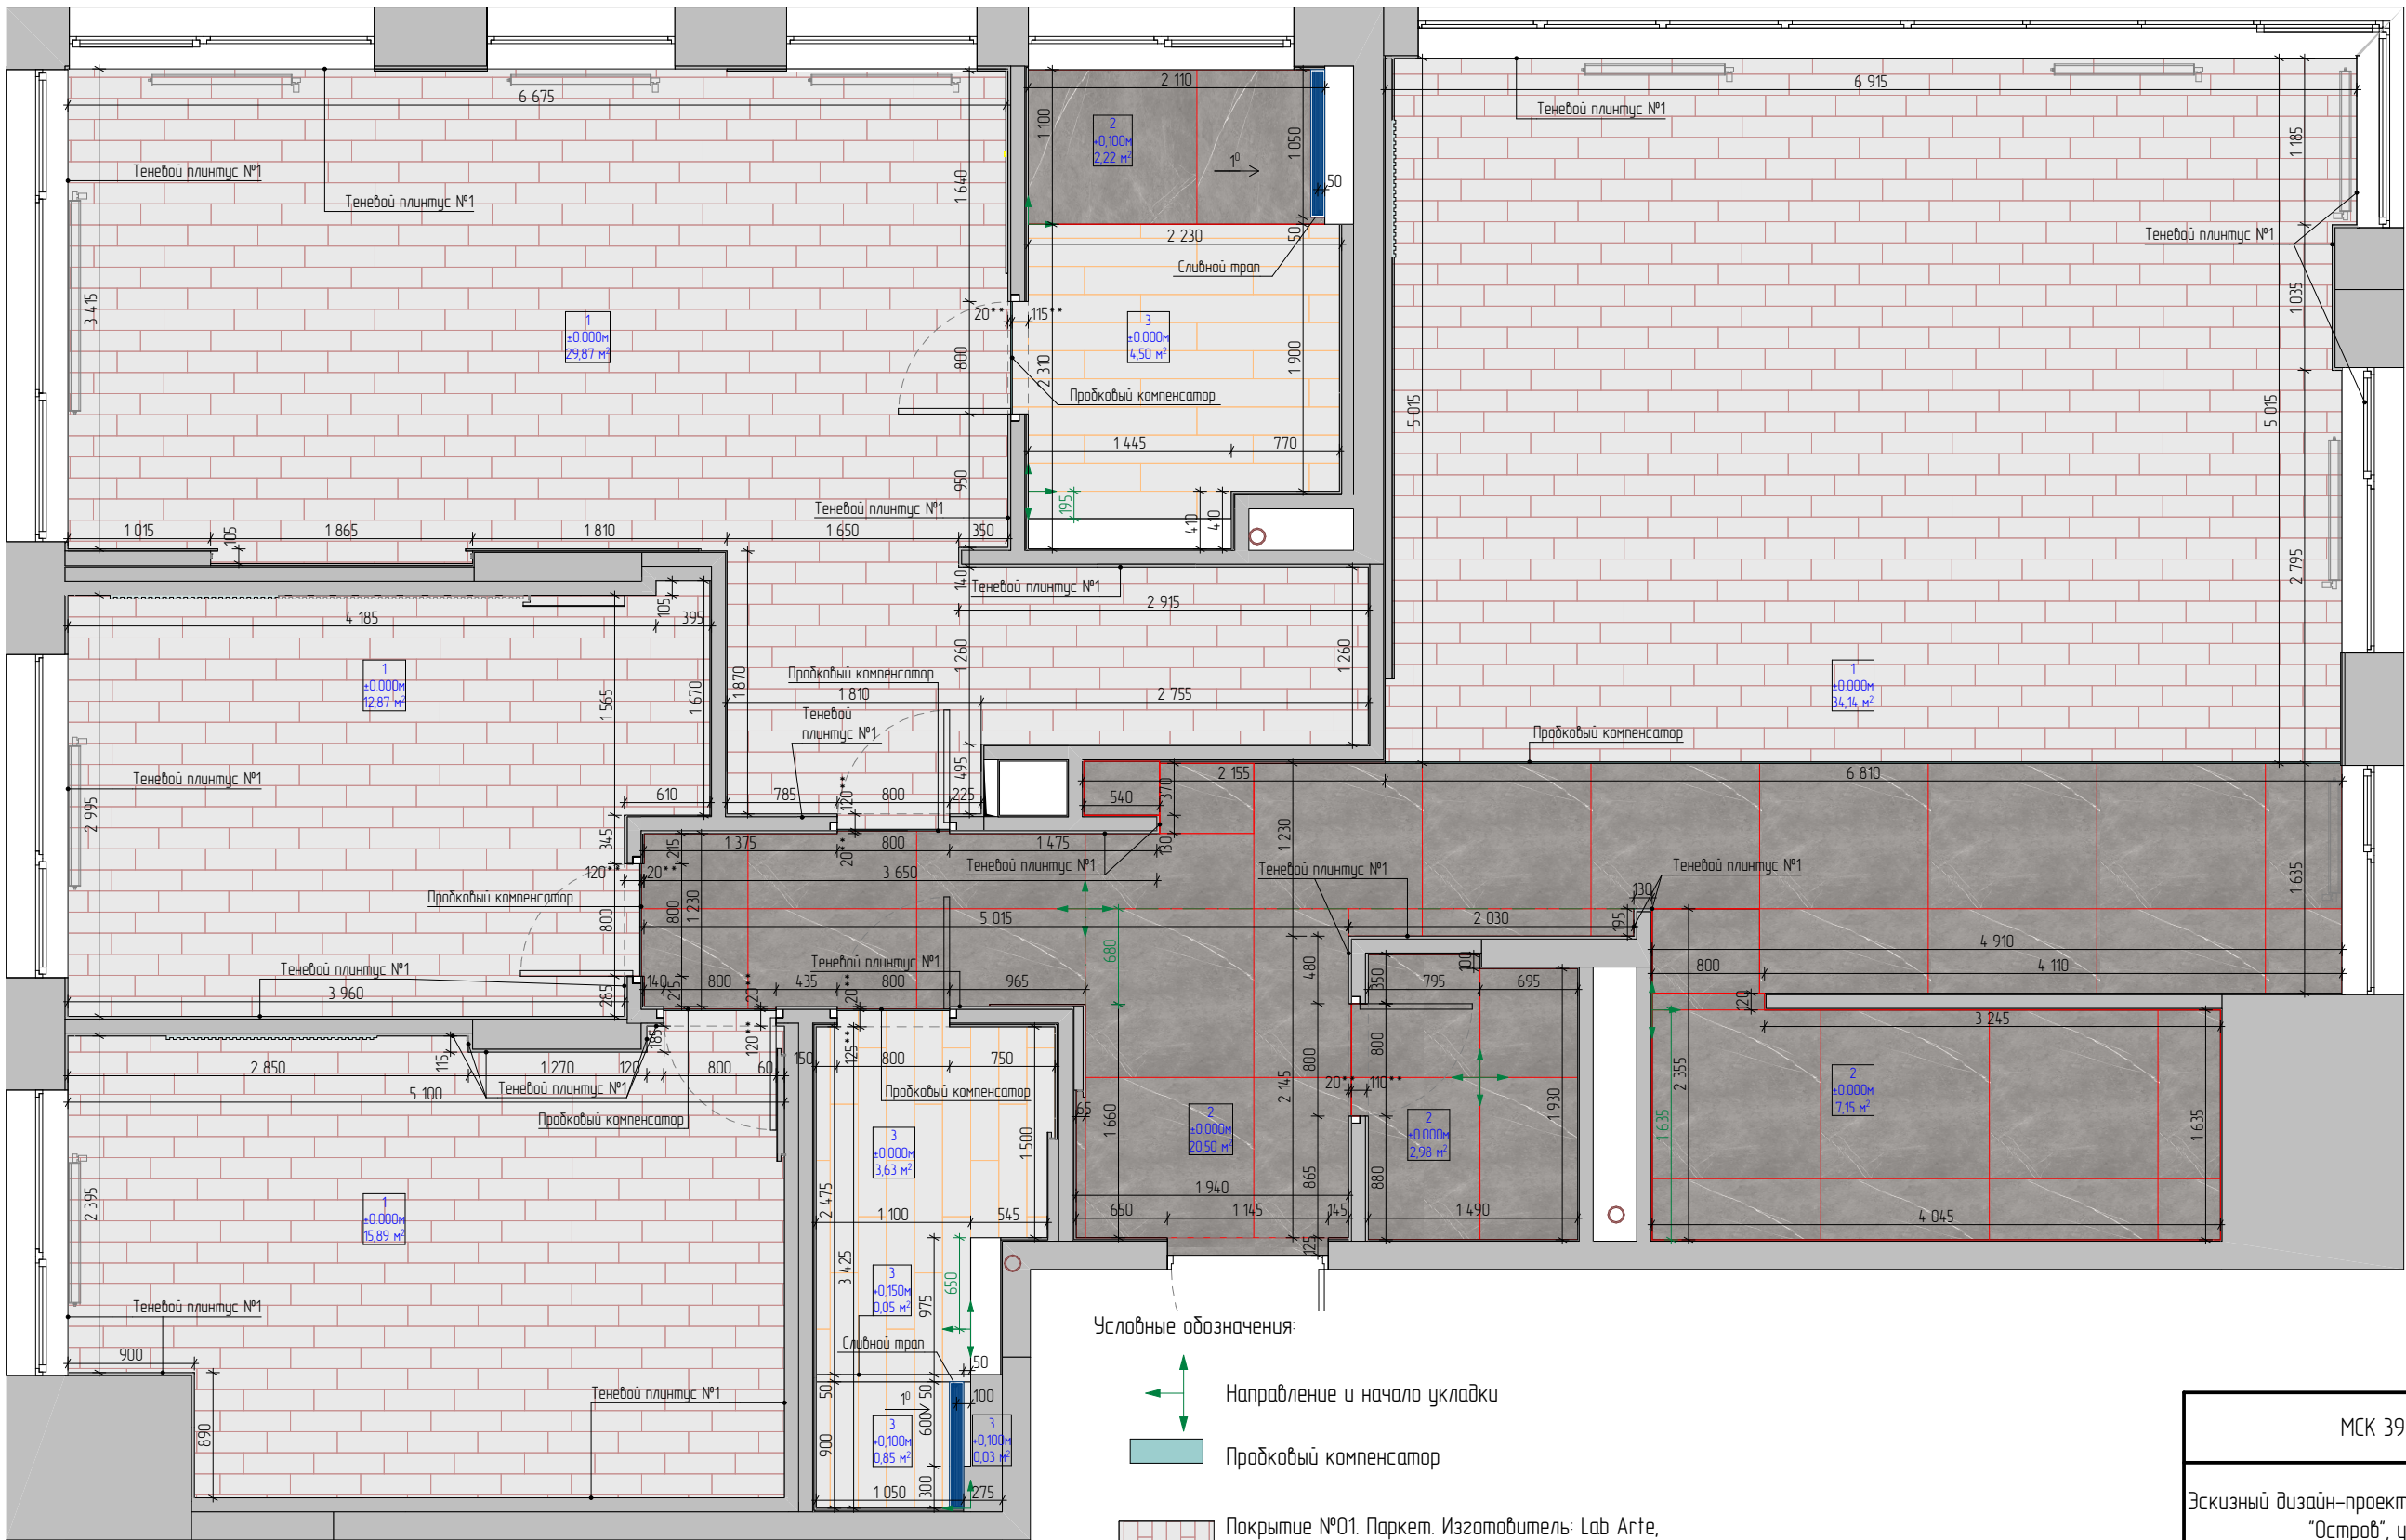


Примечания:

- * - размеры уточнить по месту после выполнения черновых отделочных работ.
- За отметку $\pm 0,000$ принят уровень чистого пола.
- Во влажных помещениях предусмотреть гидроизоляцию пола с заведением на стены до потолка.
- Совместить швы плитки на подиумах и основном полу.
- При монтаже напольных покрытий уточнить необходимость устройства дверных проемов с порогами.
- * - размеры уточнить по месту после выполнения черновых отделочных работ и установки дверей со скрытой коробкой.
- ** - размер уточнить по месту в зависимости от точного расположения полотна двери, стыковка двух разных напольных покрытий должна проходить точно по центру вдоль дверного полотна.

Условные обозначения:

- Направление и начало укладки
- Пробковый компенсатор
- Покрывтие №01. Паркет. Изготовитель: Lab Arte, кол-я: Angle Дуб Натур, размер: 500x150 мм, точный артикул и производителя уточнить при выборе образца, толщину уточнить при закупке.
- Покрывтие №02. Керамогранит. Изготовитель: Elegant Grey, кол-я: Forte Dei Marmi, размер: 1200x1200 мм, толщину уточнить при закупке.
- Покрывтие №03. Керамогранит. Изготовитель: Nutmeg, кол-я: Woodslate Life, размер: 1200x200 мм, толщину уточнить при закупке.

МСК 392.12.25-ЭП ПРЕМИУМ			
Эскизный дизайн-проект интерьера квартиры в г. Москва ЖК "Остров", ул. Нижние Мневники д. 7			
Общий план покрытий полов.			
Дизайнер интерьера №1 Александр Батеньков	Стадия	Лист	Листов
	ЭП	29	120
		Подп.	Дата
ГАП	Батеньков А.С.		
Гл. дизайнер	Власова В.А.		
Гл. проектиров.	Луныкова В.Н.		

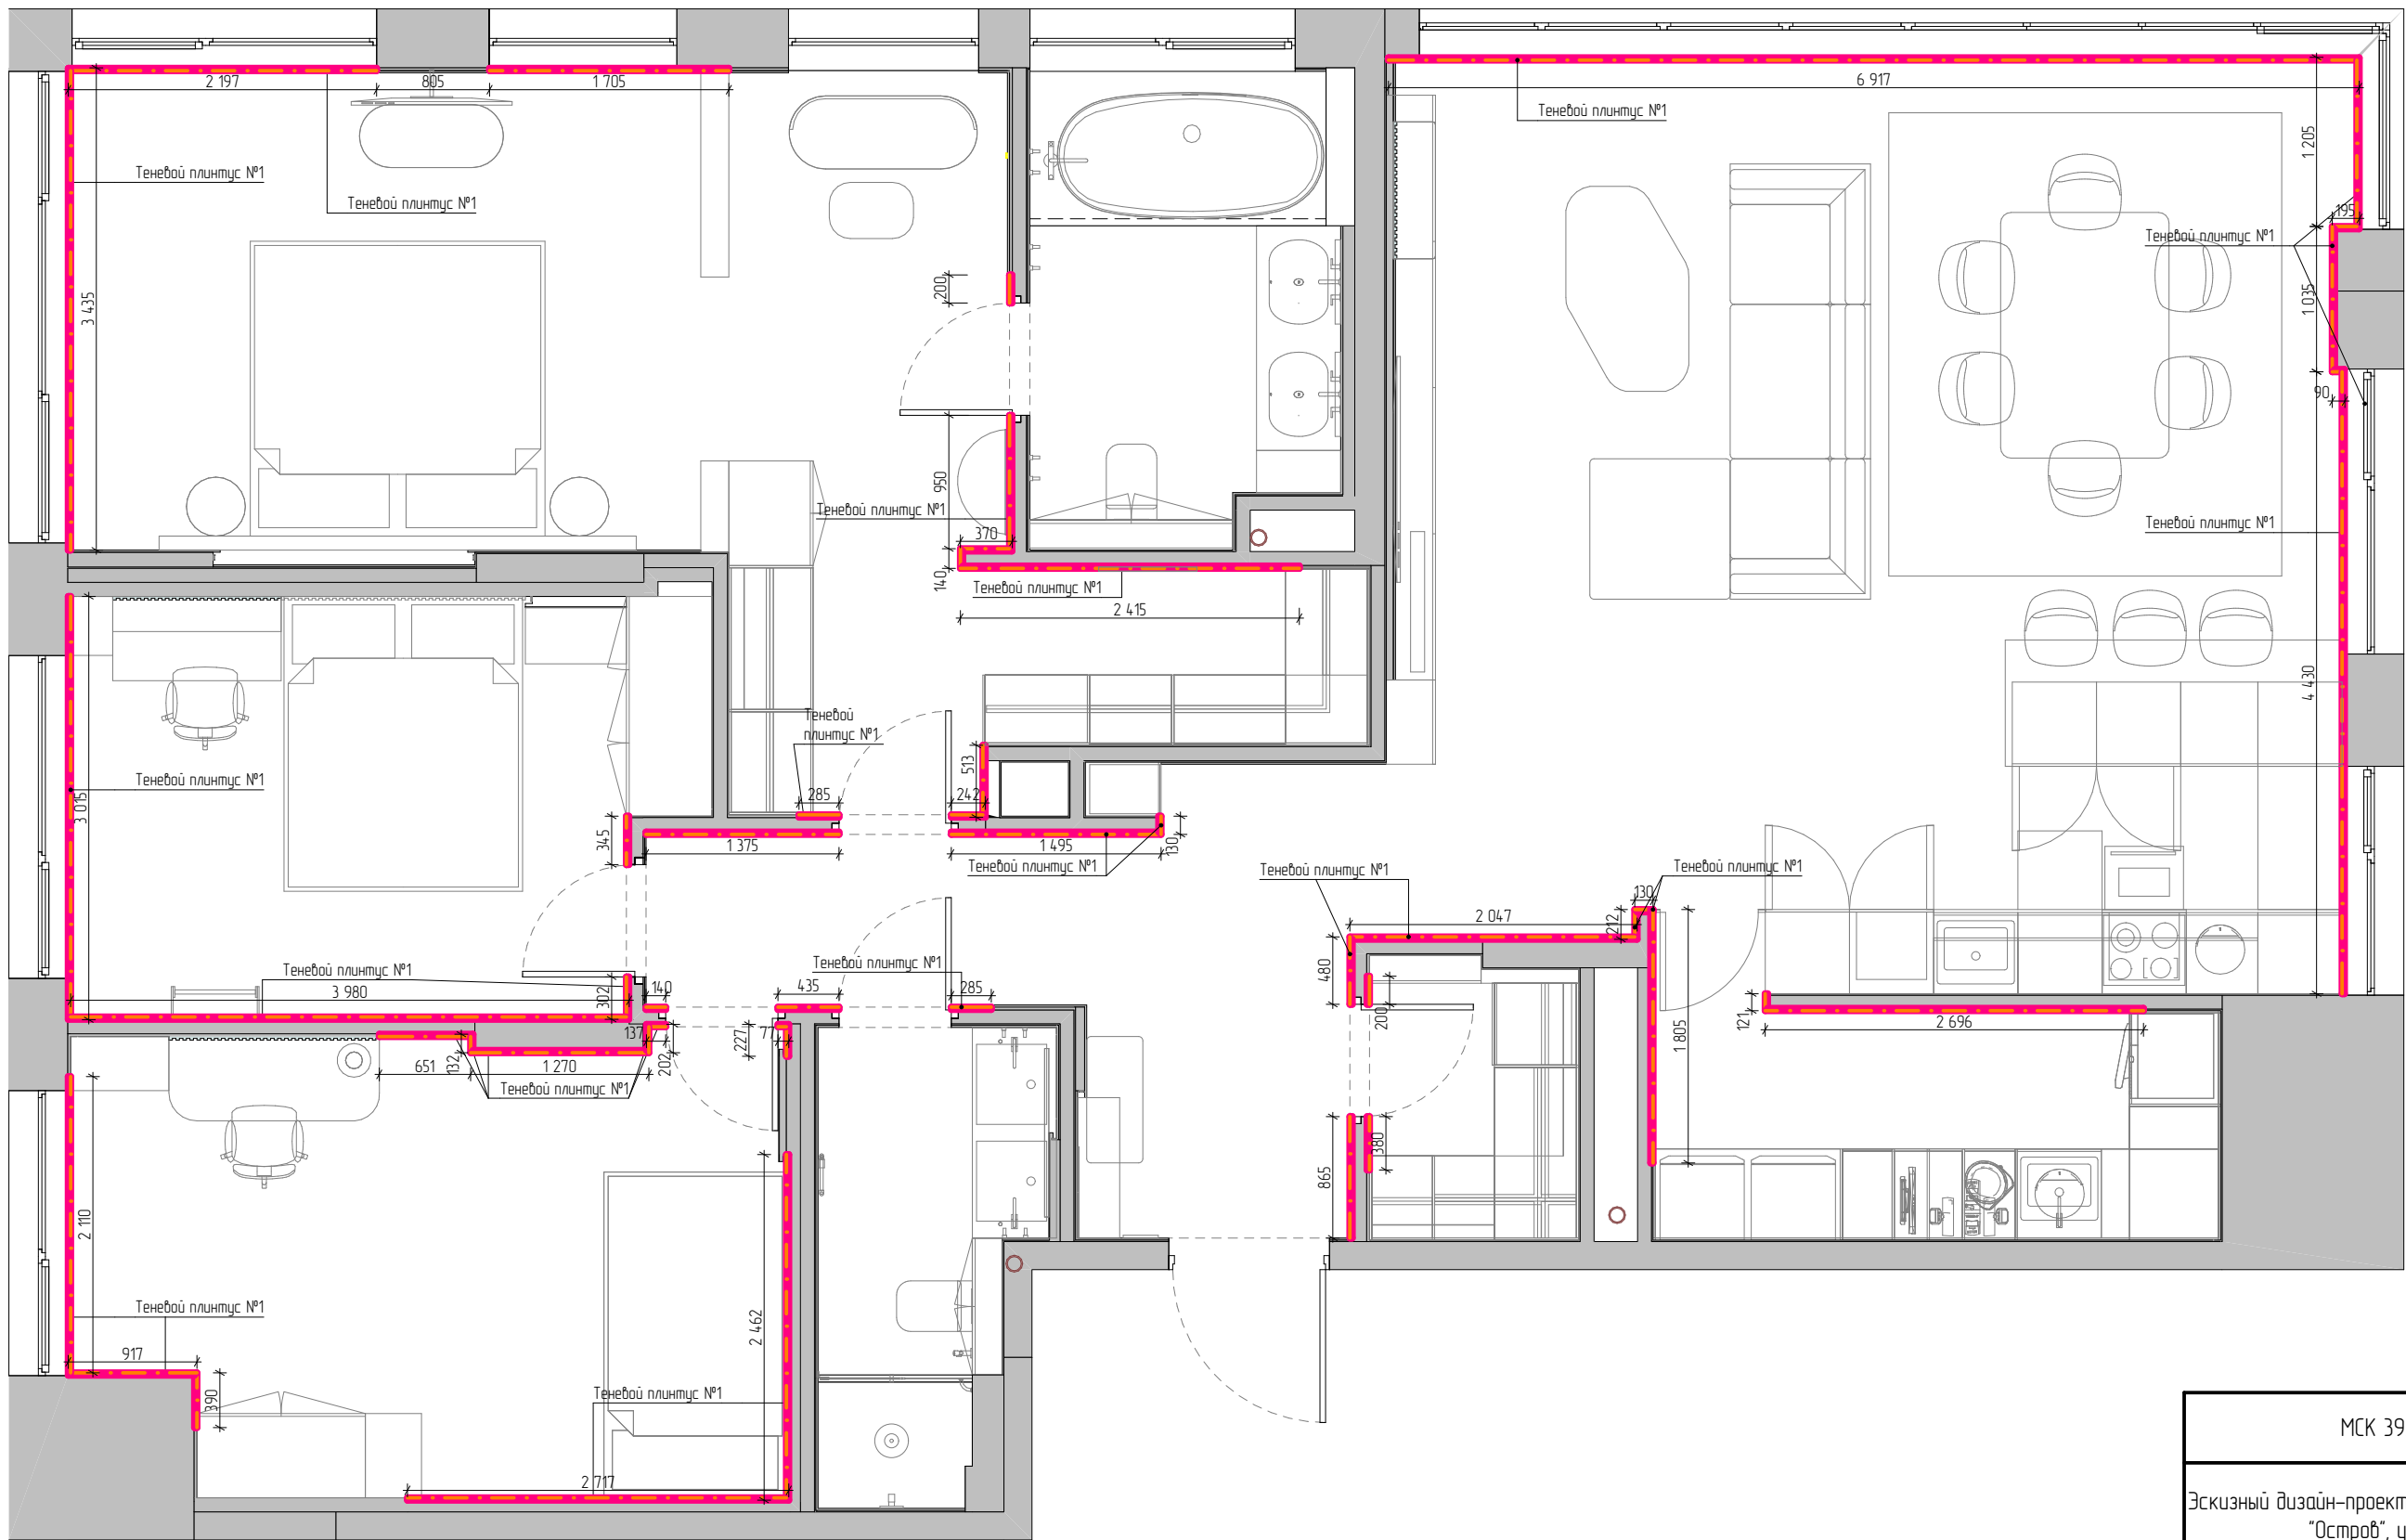


Условные обозначения:

- Конструкции наружных стен
- Существующие коммуникации (стояки)
- Плинтус №1. Теневой плинтус скрытого монтажа с МДФ вставкой. Теневой зазор от пола 100 мм. Цвет при выборе образца (в цвет стен)

Примечания:

- * – размеры уточнить по месту после выполнения черновых отделочных работ.
- Цвет окрашивания плинтуса уточнить по месту авторским сопровождением


МСК 392.12.25–ЭП ПРЕМИУМ			
Эскизный дизайн–проект интерьера квартиры в г. Москва ЖК "Остров", ул. Нижние Мневники д. 7			
План плинтусов.			
Дизайнер интерьера №1 Александр Батеньков	Стадия	Лист	Листов
	ЭП	30	120
		Подп.	Дата
ГАП	Батеньков А.С.		
Гл. дизайнер	Власова В.А.		
Гл. проектиров.	Луныкова В.Н.		

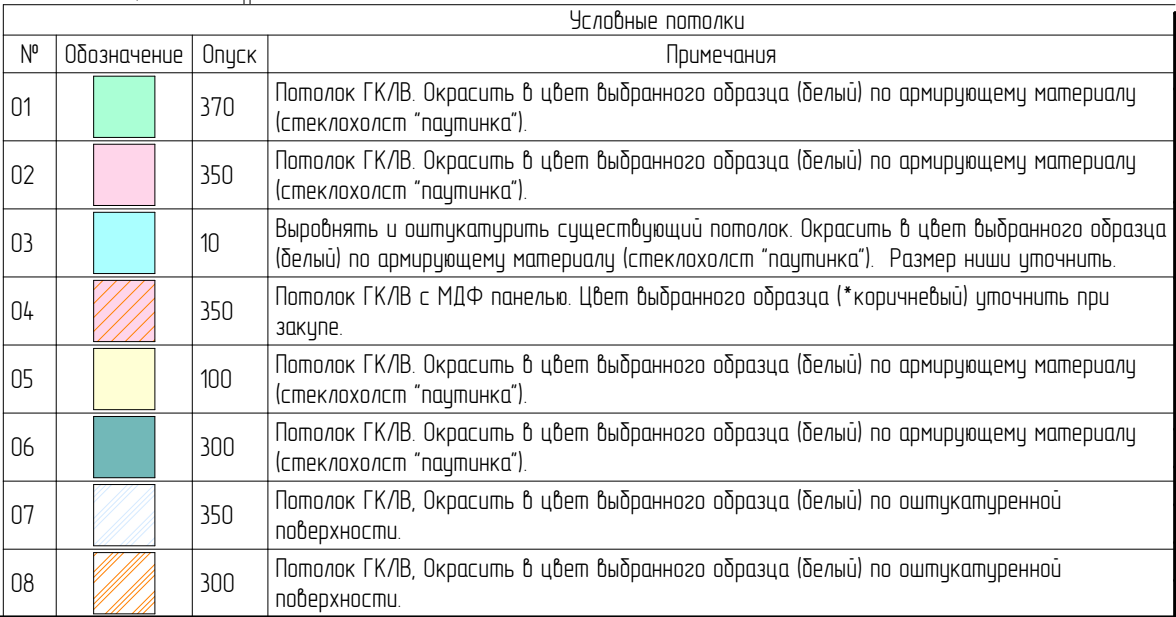

1. * – размеры уточнить по месту после выполнения черновых работ.
2. Выполнить уровни потолка из влагостойкого ГКЛ для предотвращения деформации потолка при затоплении.
3. Высоту уровней потолка отсчитывать от существующей ж/б плиты перекрытия помещения.
4. Предусмотреть усиление потолка фанерой в местах крепления потолочных карнизов для штор.
5. Во влажных помещениях обои под покраску на потолок не клеить, заменить на оштукатуривание по армирующей сетке, согласовать со специалистами.
6. От вытяжки провести вентиляционный короб до общедомового канала в конструкции потолка, уточнить по месту со специалистами и заказчиком.
7. Шумоизоляцию разработать со специалистами, уточнить состав и толщину слоев шумоизоляционных материалов. Уточнить необходимость устройства с заказчиком.

	Вывод 220V		Светильник точечный встраиваемый
	Вывод электрокабеля для светодиодной ленты		Светильник точечный встраиваемый влагозащищенный
	Диффузор, вытяжка		Светодиодная лента
	Люстра подвесная потолочная		Светодиодная лента, влагозащищенная
			Люк доступа

Лунькова В.Н.		
---------------	--	--

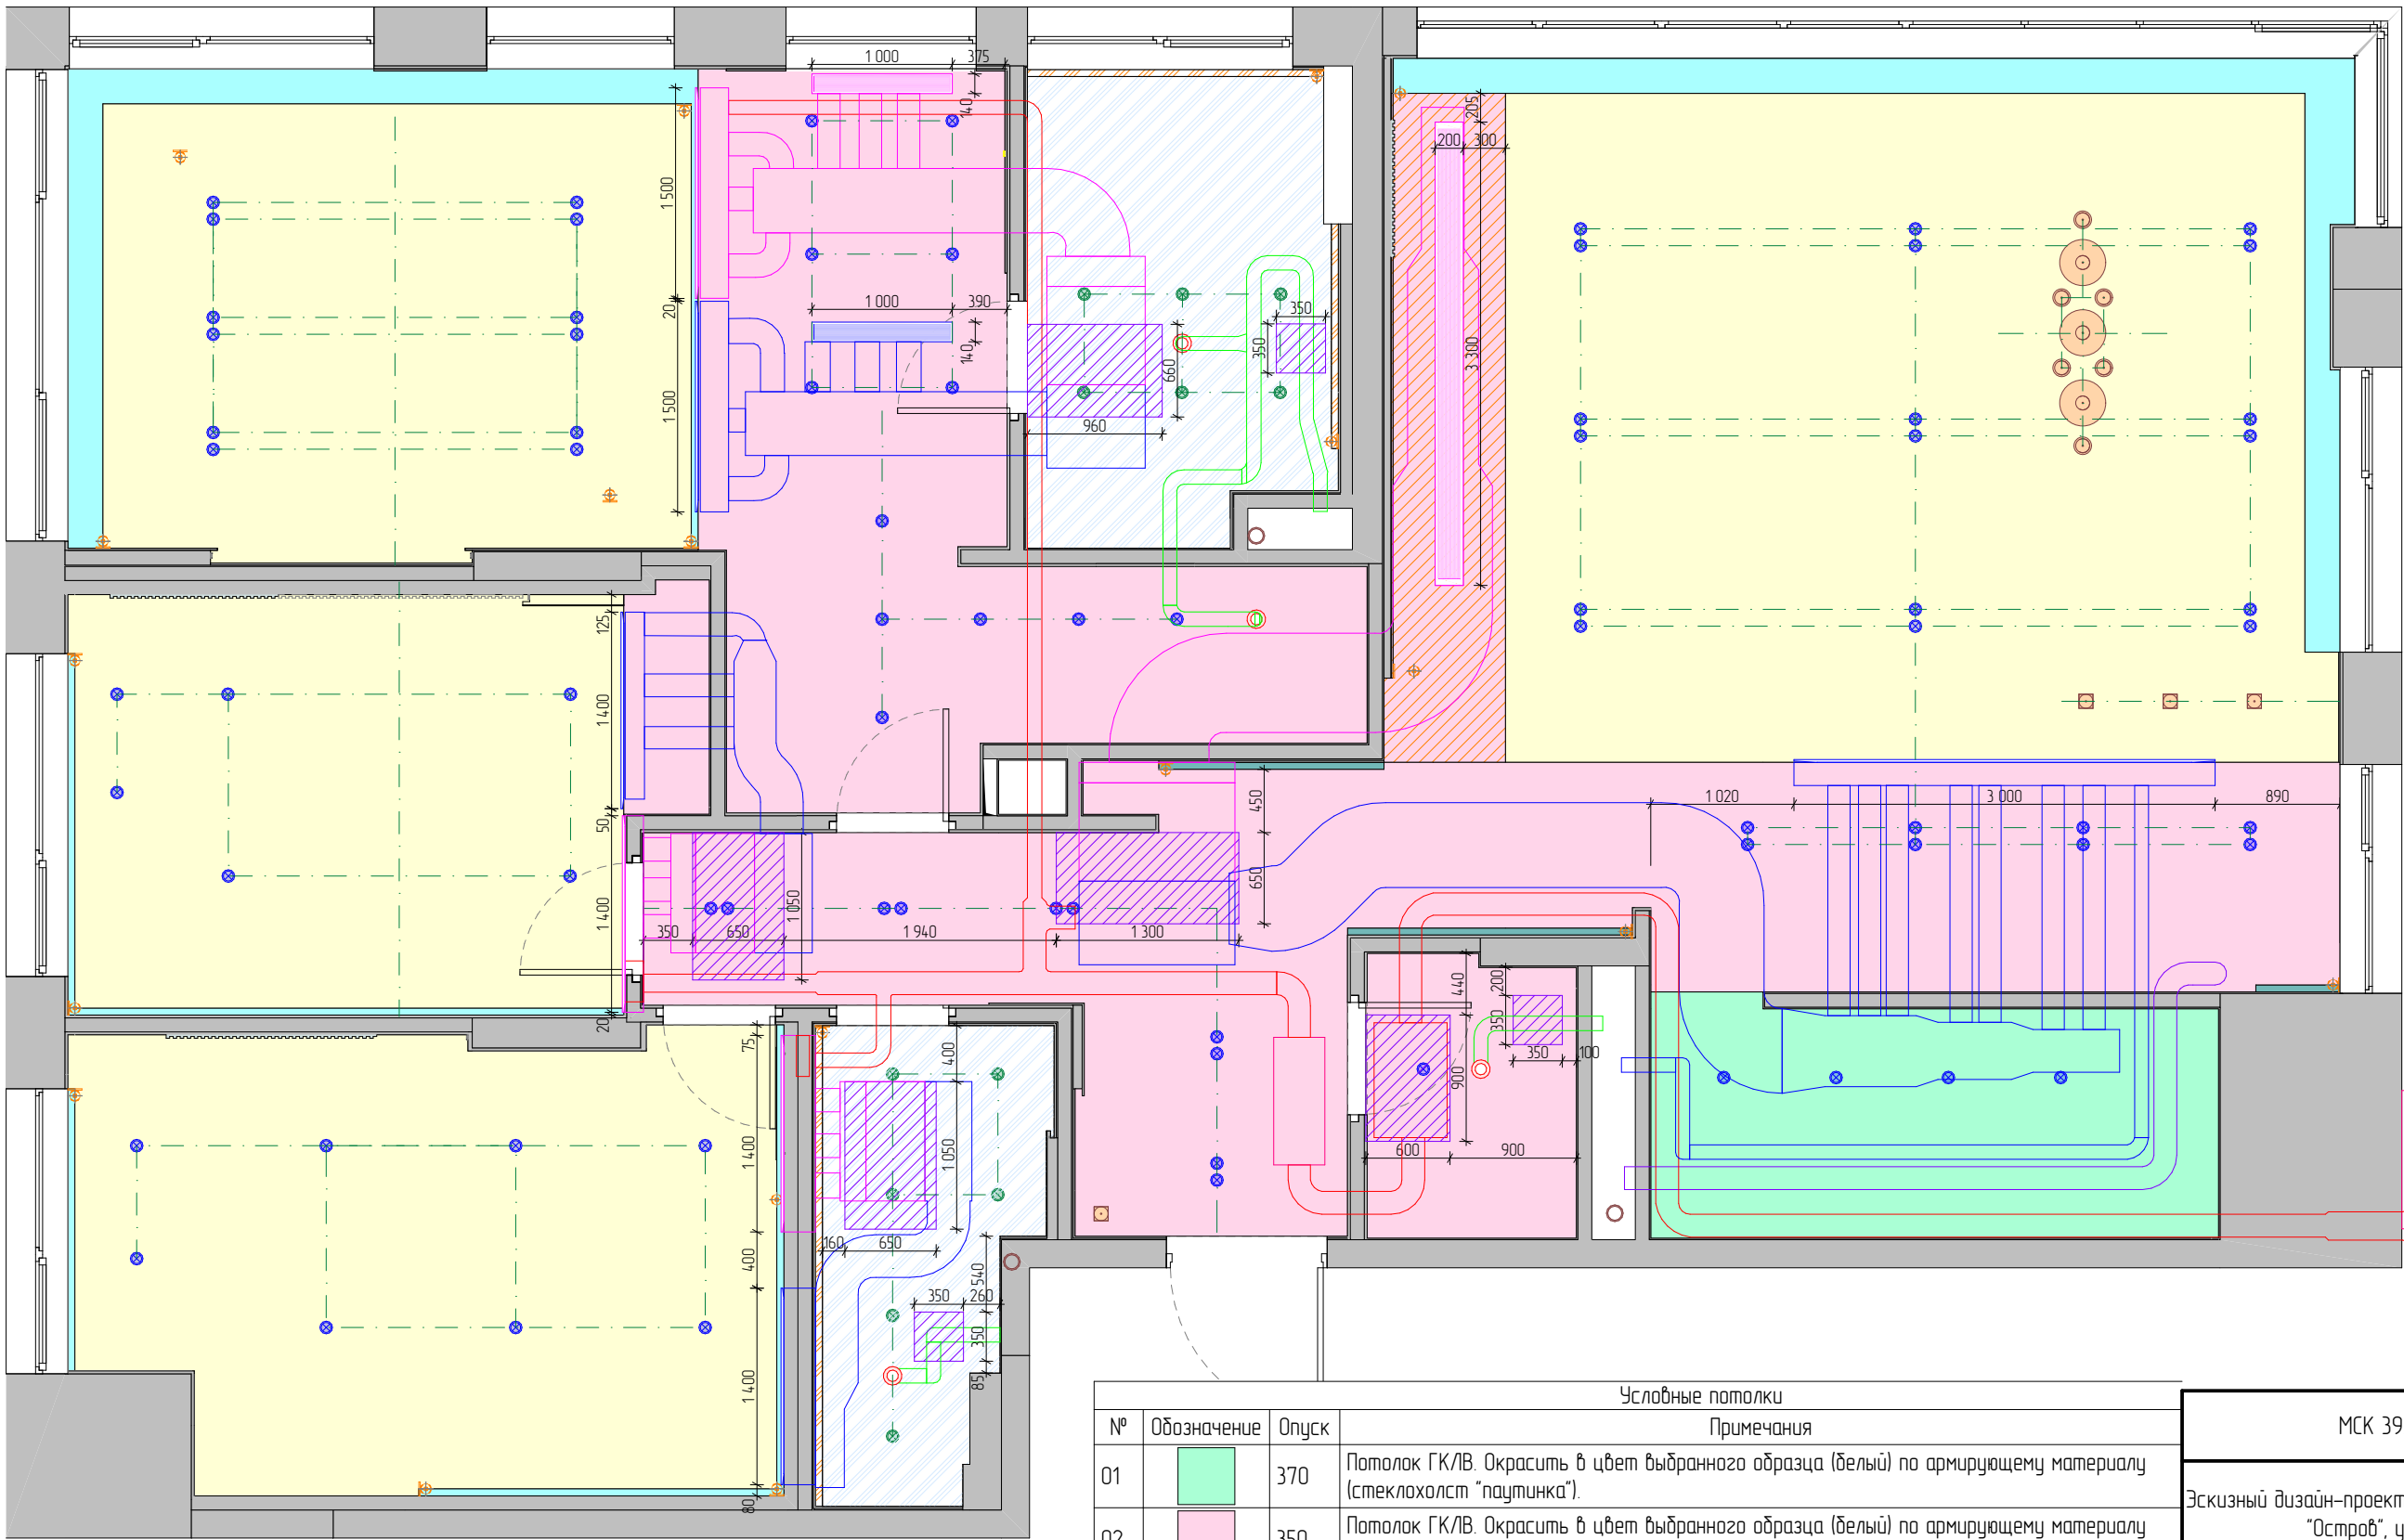

- Примечания:
- 1. * – размеры уточнить по месту.
 - 2. Выполнить уровни потолка из влагостойкого ГКЛ для предотвращения деформации потолка при затоплении.
 - 3. Высоту уровней потолка отсчитывать от существующей ж/б плиты перекрытия помещения.
 - 4. Размещение вентиляционного оборудования разработать совместно со специалистами.
 - 5. Вентиляционные короба максимально прижать к существующему уровню потолка (плите перекрытия).

Условные обозначения:

Вывод 220V

Вывод электрокабеля для светодиодной ленты

Диффузор, вытяжка

Люстра подвесная потолочная

Светильник точечный встраиваемый

Светильник точечный встраиваемый влагозащищенный

Светодиодная лента

Светодиодная лента, влагозащищенная


Люк доступа

Воздуховод

Внутренний блок кондиционера (канальный тип)

Условные потолки			
№	Обозначение	Опуск	Примечания
01		370	Потолок ГК/В. Окрасить в цвет выбранного образца (белый) по армирующему материалу (стеклохолст "паутинка").
02		350	Потолок ГК/В. Окрасить в цвет выбранного образца (белый) по армирующему материалу (стеклохолст "паутинка").
03		10	Выровнять и оштукатурить существующий потолок. Окрасить в цвет выбранного образца (белый) по армирующему материалу (стеклохолст "паутинка"). Размер ниши уточнить.
04		350	Потолок ГК/В с МДФ панелью. Цвет выбранного образца (*коричневый) уточнить при закупе.
05		100	Потолок ГК/В. Окрасить в цвет выбранного образца (белый) по армирующему материалу (стеклохолст "паутинка").
06		300	Потолок ГК/В. Окрасить в цвет выбранного образца (белый) по армирующему материалу (стеклохолст "паутинка").
07		350	Потолок ГК/В, Окрасить в цвет выбранного образца (белый) по оштукатуренной поверхности.
08		300	Потолок ГК/В, Окрасить в цвет выбранного образца (белый) по оштукатуренной поверхности.

МСК 392.12.25–ЭП ПРЕМИУМ			
Эскизный дизайн–проект интерьера квартиры в г. Москва ЖК "Остров", ул. Нижние Мневники д. 7			
Общий план потока с вентиляцией.			
Дизайнер интерьера №1 Александр Батеньков	Стадия	Лист	Листов
	ЭП	33	120
		Подп.	Дата
ГАП	Батеньков А.С.		
Гл. дизайнер	Власова В.А.		
Гл. проектиров.	Луныкова В.Н.		

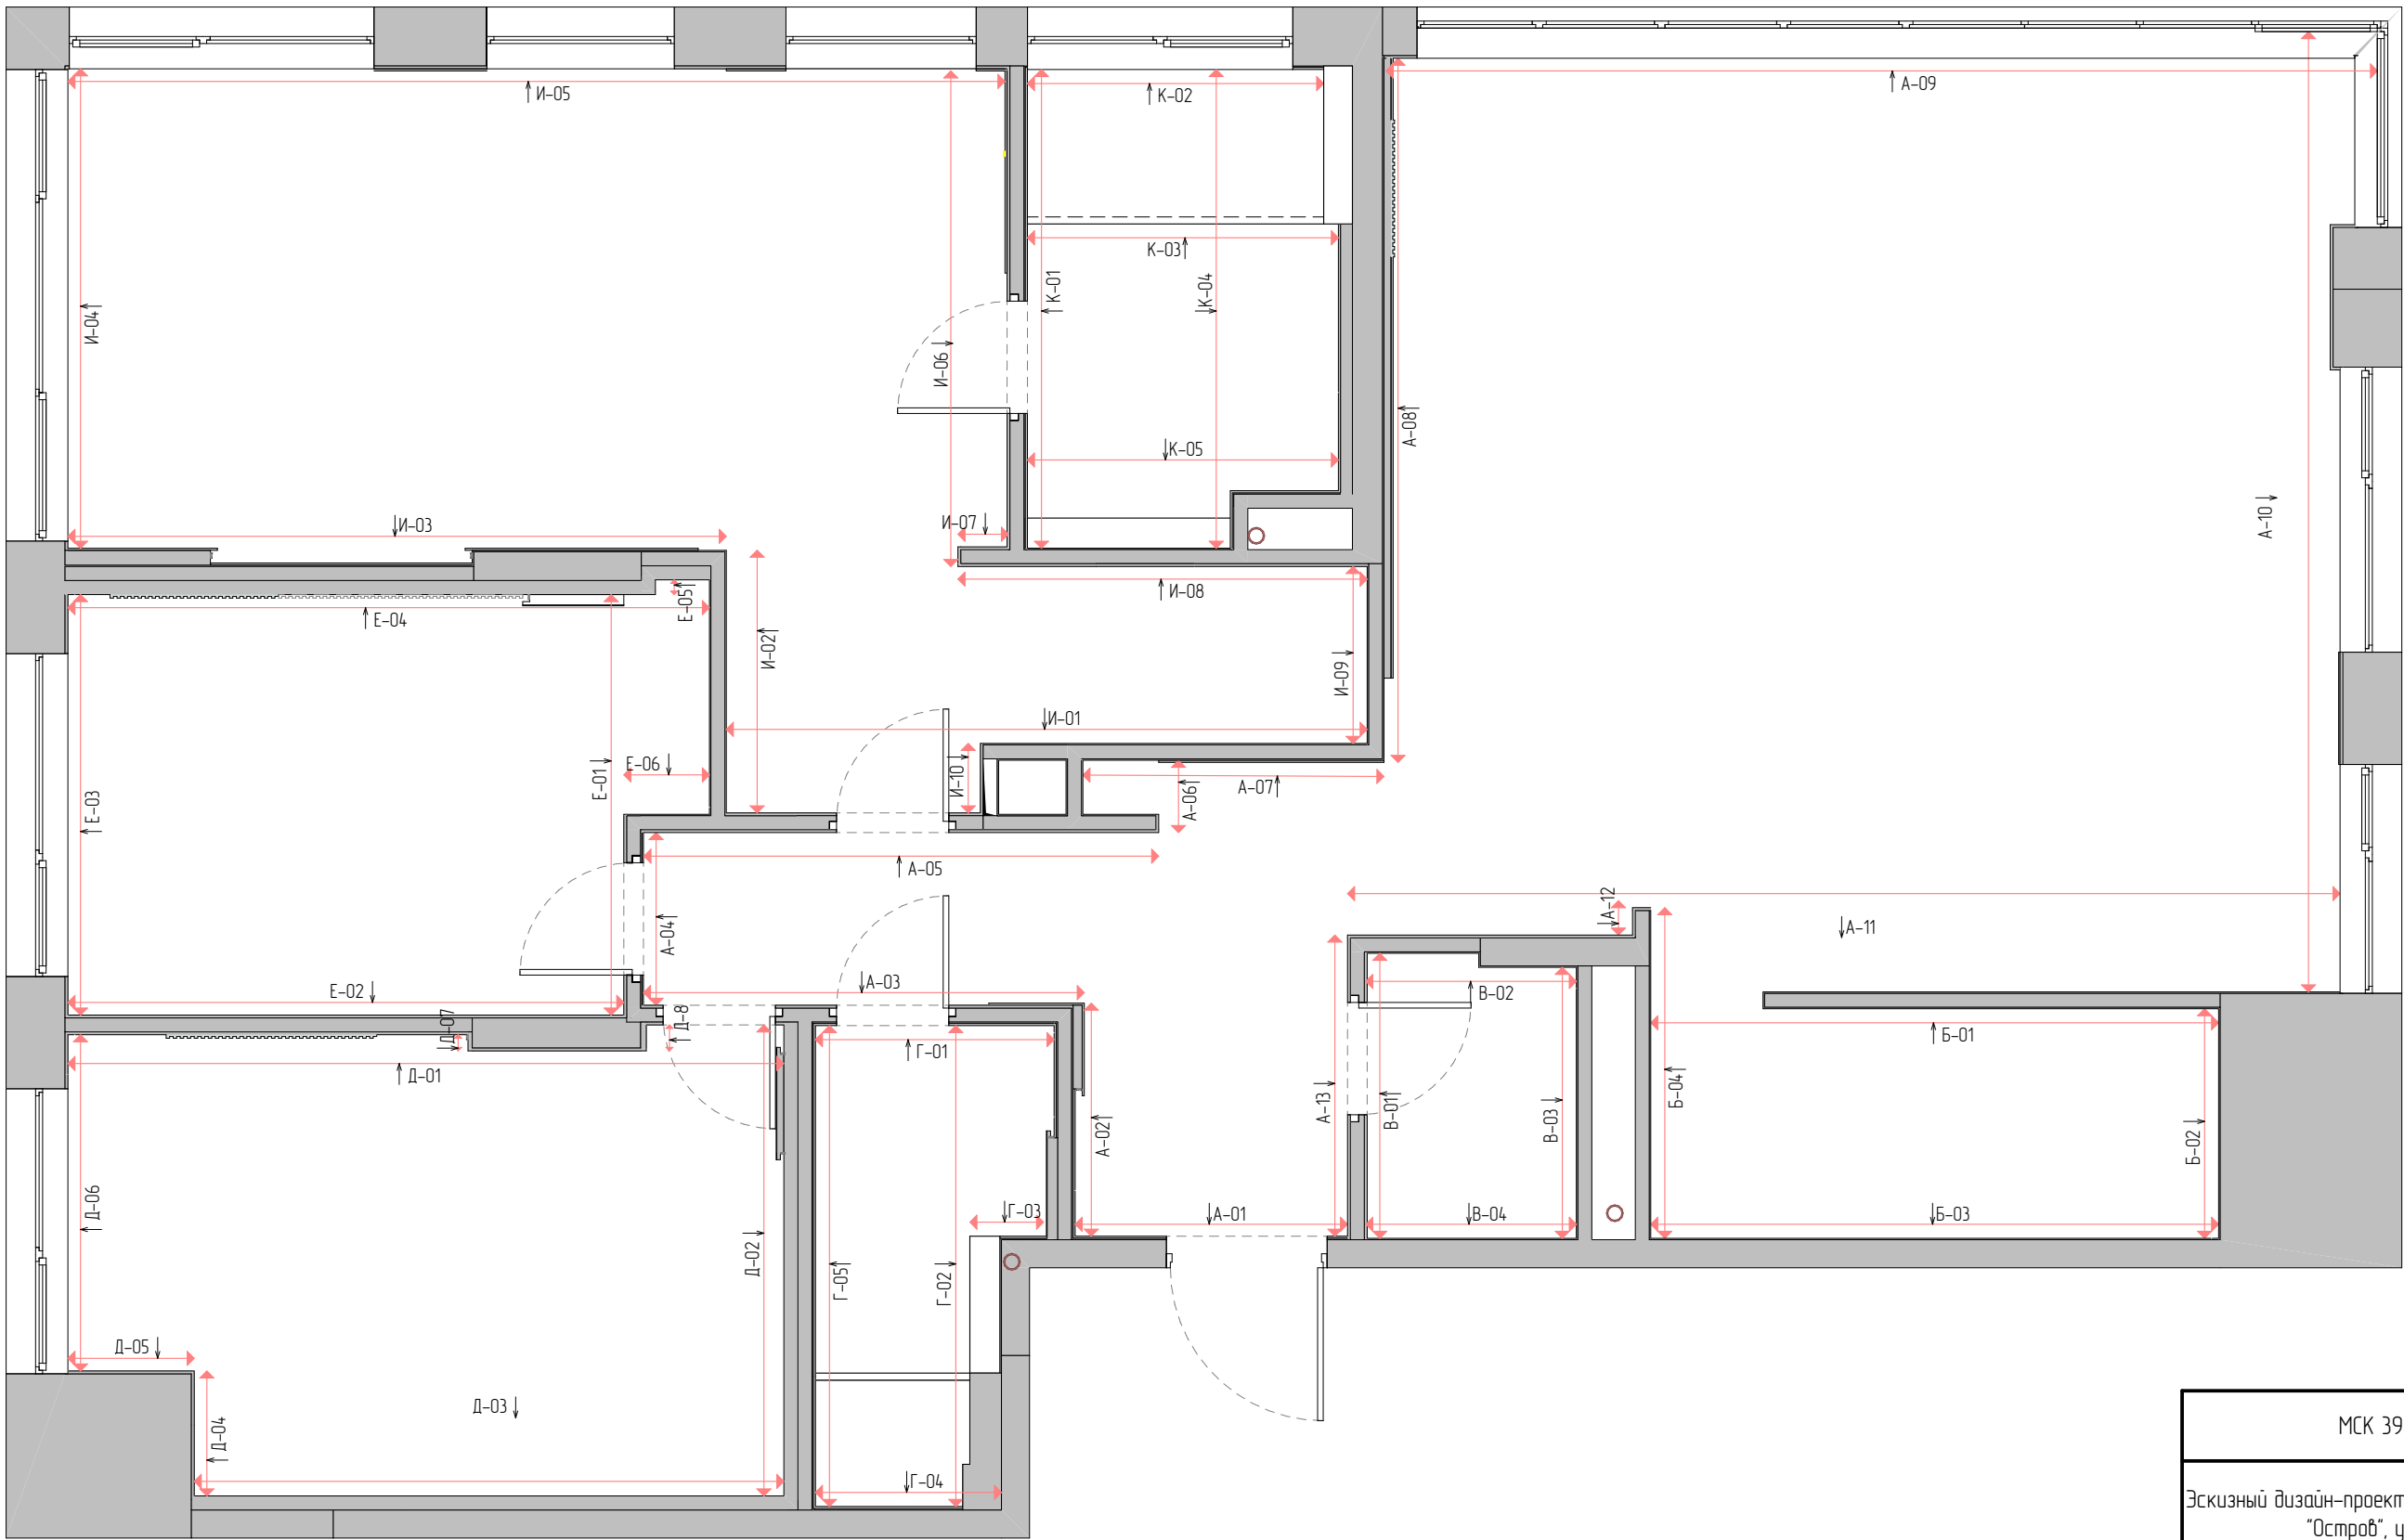


МСК 392.12.25-ЭП ПРЕМИУМ			
Эскизный дизайн-проект интерьера квартиры в г. Москва ЖК "Остров", ул. Нижние Мневники д. 7			
План обозначения разверток стен.			
Дизайнер интерьера  №1 Александр Батеньков	Стадия	Лист	Листов
	ЭП	34	120
		Подп.	Дата
ГАП	Батеньков А.С.		
Гл. дизайнер	Власова В.А.		
Гл. проектиров.	Луцькова В.Н.		




МСК 392.12.25-ЭП ПРЕМИУМ			
Эскизный дизайн-проект интерьера квартиры в г. Москва ЖК "Остров", ул. Нижние Мневники д. 7			
Прихожая Кухня Гостиная.Видовые точки.			
Дизайнер интерьера  Александр Батеньков	Стадия	Лист	Листов
	ЭП	35	120
		Подп.	Дата
ГАП	Батеньков А.С.		
Гл. дизайнер	Власова В.А.		
Гл. проектиров.	Луныкова В.Н.		
Разработал	Ильина Е.Е.		



МСК 392.12.25-ЭП ПРЕМИУМ			
Эскизный дизайн-проект интерьера квартиры в г. Москва ЖК "Остров", ул. Нижние Мневники д. 7			
Прихожая Кухня Гостиная. Видовые точки.			
Дизайнер интерьера  Александр Батеньков	Стадия	Лист	Листов
	ЭП	36	120
		Подп.	Дата
ГАП	Батеньков А.С.		
Гл. дизайнер	Власова В.А.		
Гл. проектиров.	Луныкова В.Н.		
Разработал	Ильина Е.Е.		

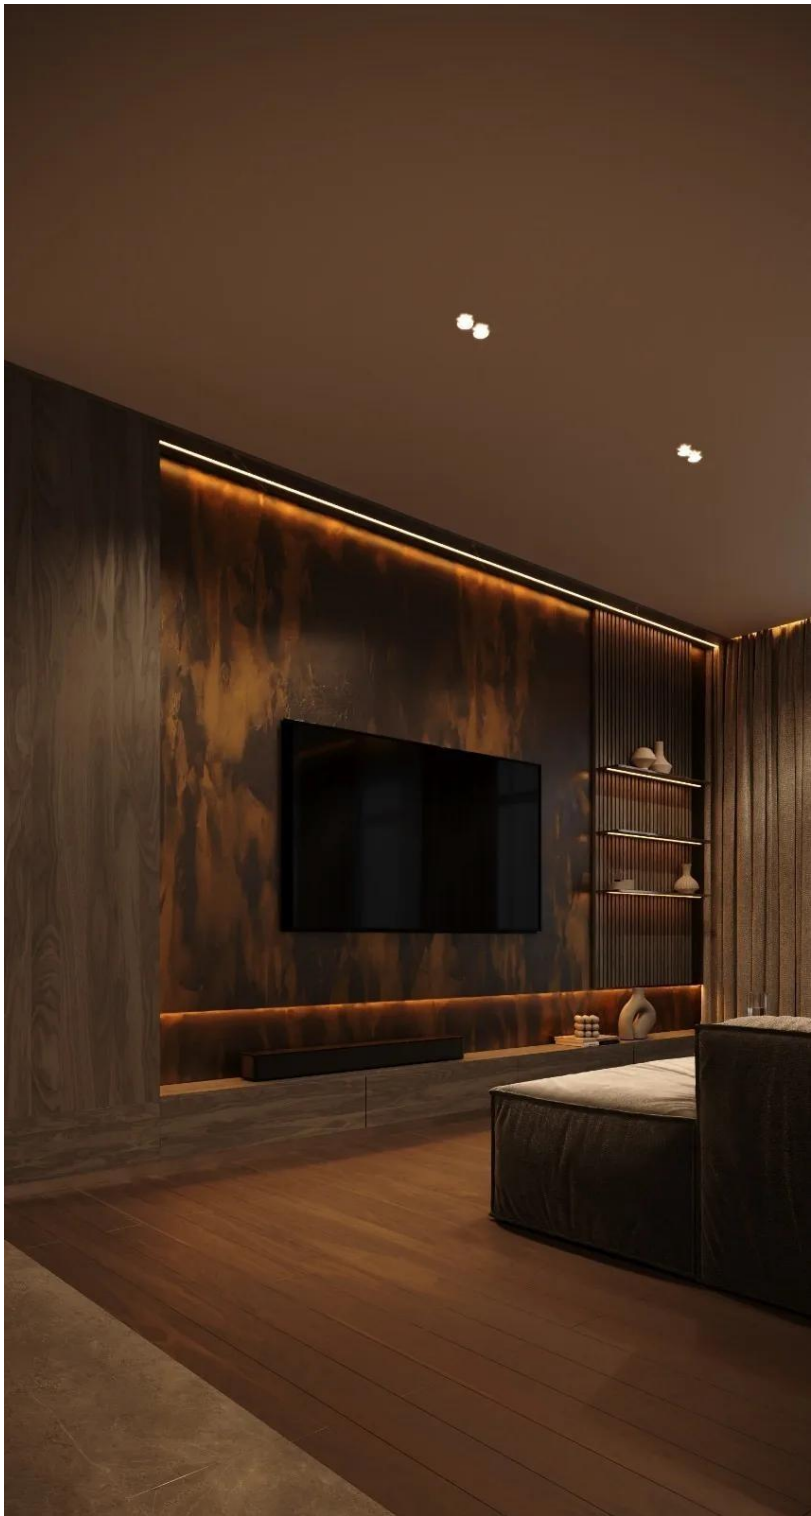

МСК 392.12.25-ЭП ПРЕМИУМ			
Эскизный дизайн-проект интерьера квартиры в г. Москва ЖК "Остров", ул. Нижние Мневники д. 7			
Прихожая Кухня ГостинаяВидовые точки.			
Дизайнер интерьера  Александр Батеньков	Стадия	Лист	Листов
	ЭП	37	120
		Подп.	Дата
ГАП	Батеньков А.С.		
Гл. дизайнер	Власова В.А.		
Гл. проектиров.	Луныкова В.Н.		
Разработал	Ильина Е.Е.		

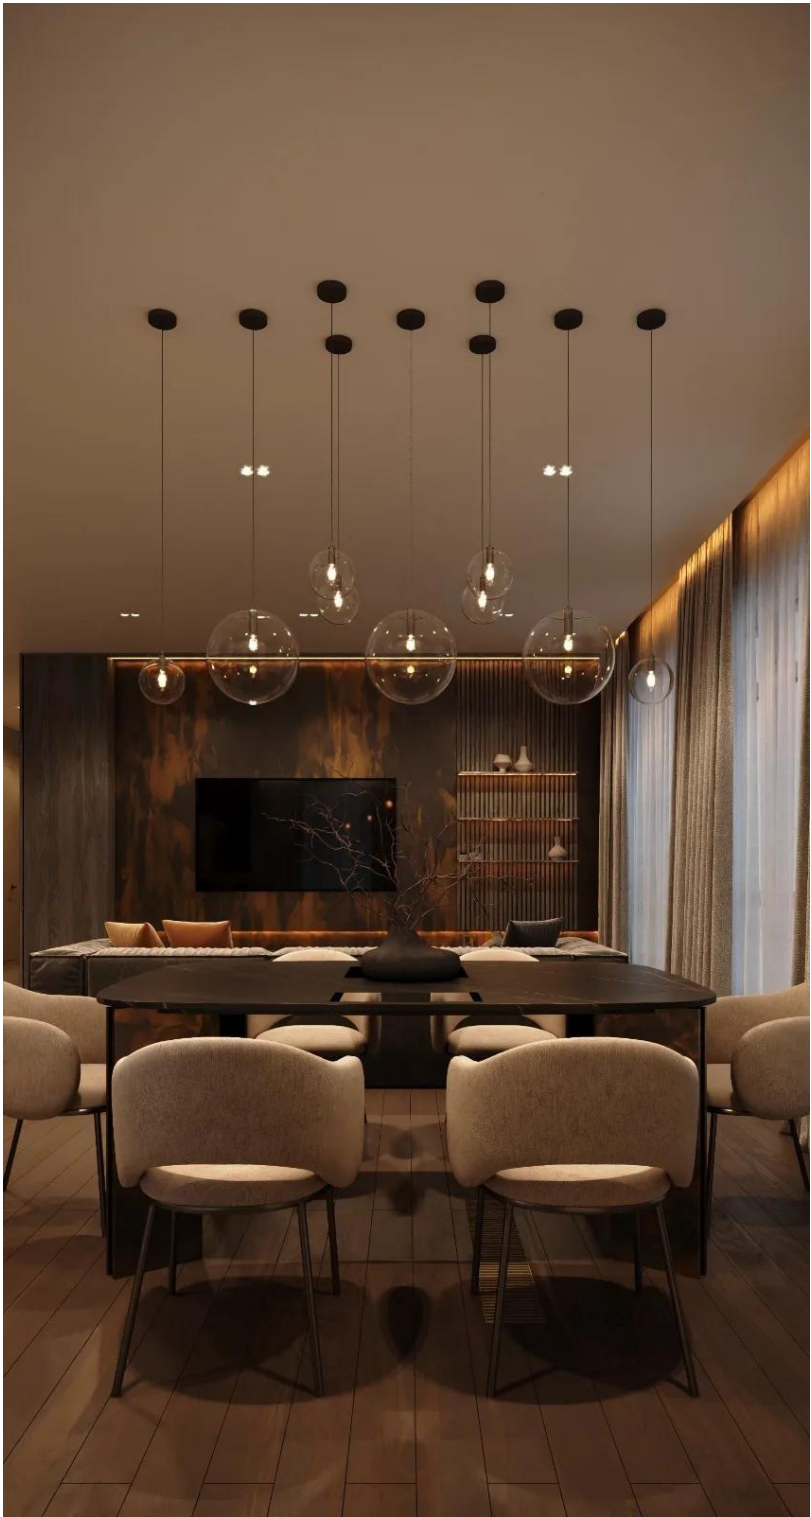

МСК 392.12.25-ЭП ПРЕМИУМ			
Эскизный дизайн-проект интерьера квартиры в г. Москва ЖК "Остров", ул. Нижние Мневники д. 7			
Прихожая Кухня Гостиная.Видовые точки.			
Дизайнер интерьера  Александр Батеньков	Стадия	Лист	Листов
	ЭП	38	120
		Подп.	Дата
ГАП	Батеньков А.С.		
Гл. дизайнер	Власова В.А.		
Гл. проектиров.	Луныкова В.Н.		
Разработал	Ильина Е.Е.		




МСК 392.12.25-ЭП ПРЕМИУМ			
Эскизный дизайн-проект интерьера квартиры в г. Москва ЖК "Остров", ул. Нижние Мневники д. 7			
Прихожая Кухня Гостиная. Видовые точки.			
Дизайнер интерьера  Александр Батеньков	Стадия	Лист	Листов
	ЭП	39	120
		Подп.	Дата
ГАП	Батеньков А.С.		
Гл. дизайнер	Власова В.А.		
Гл. проектиров.	Луныкова В.Н.		
Разработал	Ильина Е.Е.		



МСК 392.12.25-ЭП ПРЕМИУМ			
Эскизный дизайн-проект интерьера квартиры в г. Москва ЖК "Остров", ул. Нижние Мневники д. 7			
Прихожая Кухня Гостиная. Видовые точки.			
Дизайнер интерьера  №1 Александр Батеньков	Стадия	Лист	Листов
	ЭП	40	120
		Подп.	Дата
ГАП	Батеньков А.С.		
Гл. дизайнер	Власова В.А.		
Гл. проектиров.	Луныкова В.Н.		
Разработал	Ильина Е.Е.		



МСК 392.12.25-ЭП ПРЕМИУМ			
Эскизный дизайн-проект интерьера квартиры в г. Москва ЖК "Остров", ул. Нижние Мневники д. 7			
Прихожая Кухня Гостиная.Видовые точки.			
Дизайнер интерьера  №1 Александр Батеньков	Стадия	Лист	Листов
	ЭП	41	120
		Подп.	Дата
ГАП	Батеньков А.С.		
Гл. дизайнер	Власова В.А.		
Гл. проектиров.	Луныкова В.Н.		
Разработал	Ильина Е.Е.		

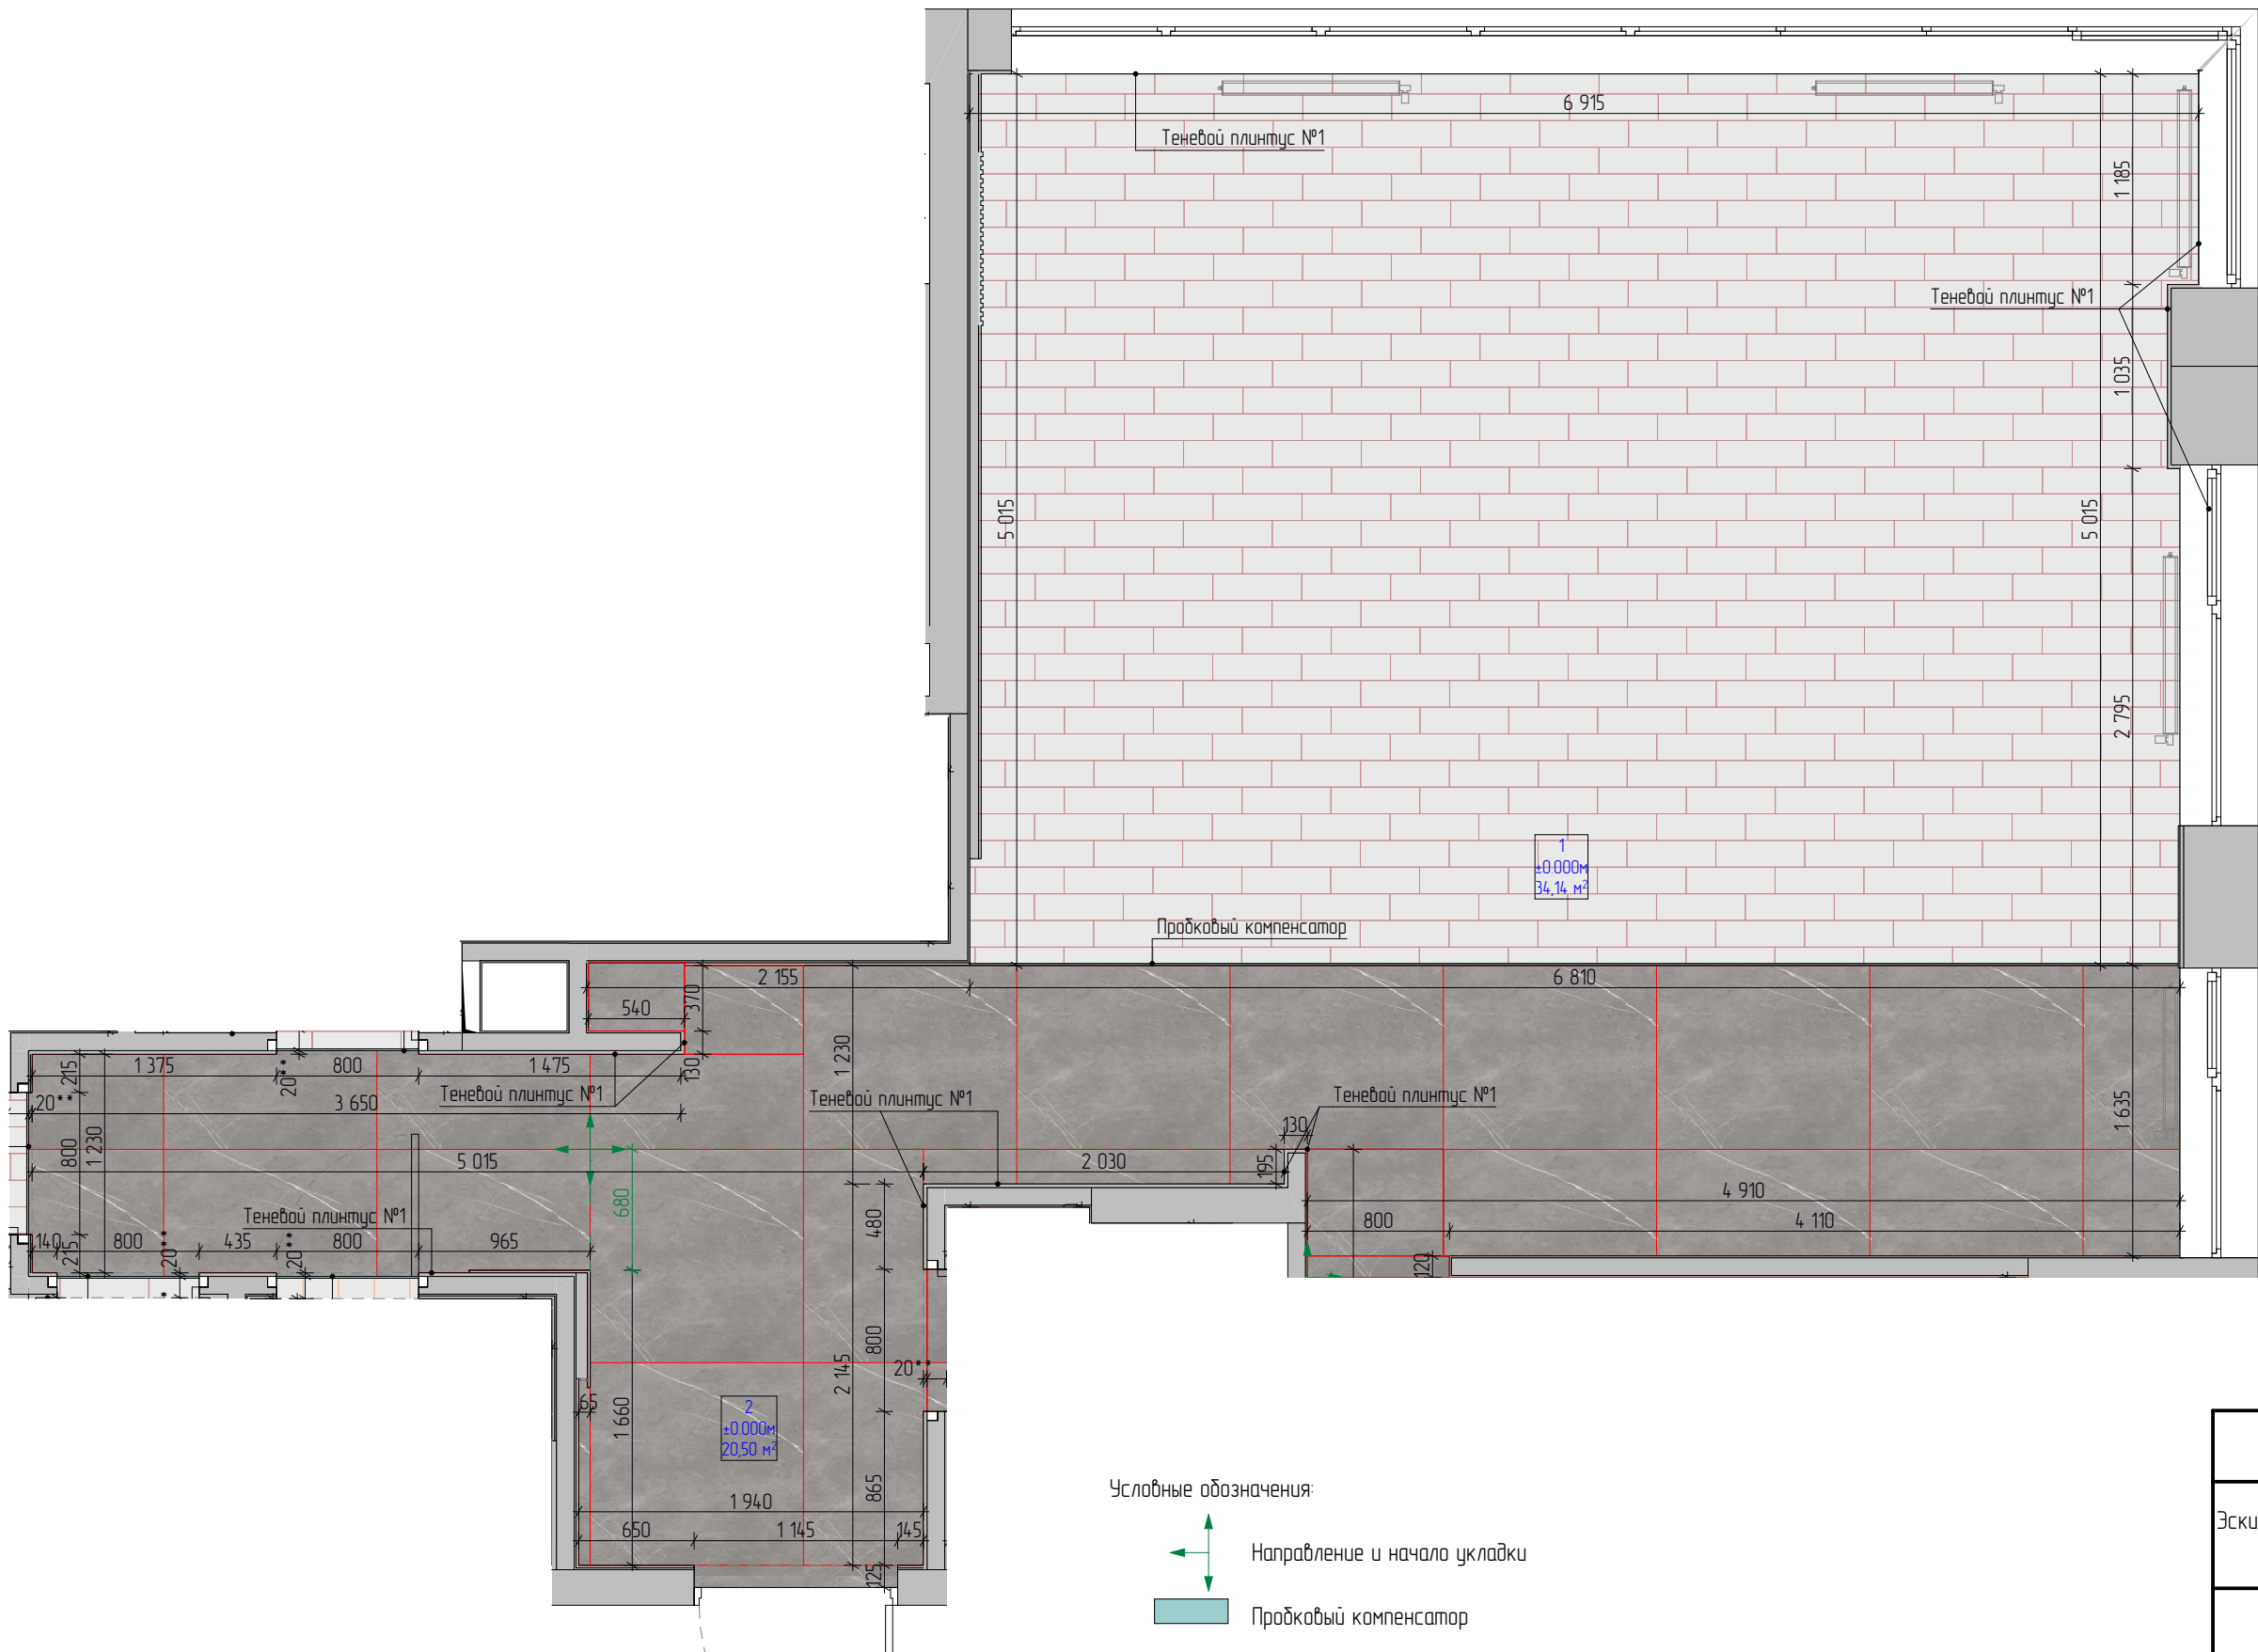

Примечания:

- *- размеры уточнить по месту после выполнения черновых отделочных работ.
- За отметку $\pm 0,000$ принят уровень чистого пола.
- При монтаже напольных покрытий уточнить необходимость устройства дверных проемов с порогом.
- *- размеры уточнить по месту после выполнения черновых отделочных работ и установки дверей со скрытой коробкой.
- **-размер уточнить по месту в зависимости от точного расположения полотна двери, стыковка двух разных напольных покрытий должна проходить точно по центру вдоль дверного полотна.


Условные обозначения:

Направление и начало укладки

Пороговый компенсатор

- Покрытие №01. Паркет. Изготовитель: Lab Arte, кол-я: Angle Дуб Натур, размер: 500x150 мм, точный артикул и производителя уточнить при выборе образца, толщину уточнить при покупке..
- Покрытие №02. Керамогранит. Изготовитель: Elegant Grey, кол-я: Forte Dei Marmi, размер: 1200x1200 мм, толщину уточнить при покупке.

МСК 392.12.25-ЭП ПРЕМИУМ			
Эскизный дизайн-проект интерьера квартиры в г. Москва ЖК "Остров", ул. Нижние Мневники д. 7			
Прихожая Кухня ГостинаяПлан отделки пола			
Дизайнер интерьера  №1 Александр Батеньков	Стадия	Лист	Листов
	ЭП	42	120
		Подп.	Дата
ГАП	Батеньков А.С.		
Гл. дизайнер	Власова В.А.		
Гл. проектиров.	Луныкова В.Н.		
Разработал	Ильина Е.Е.		

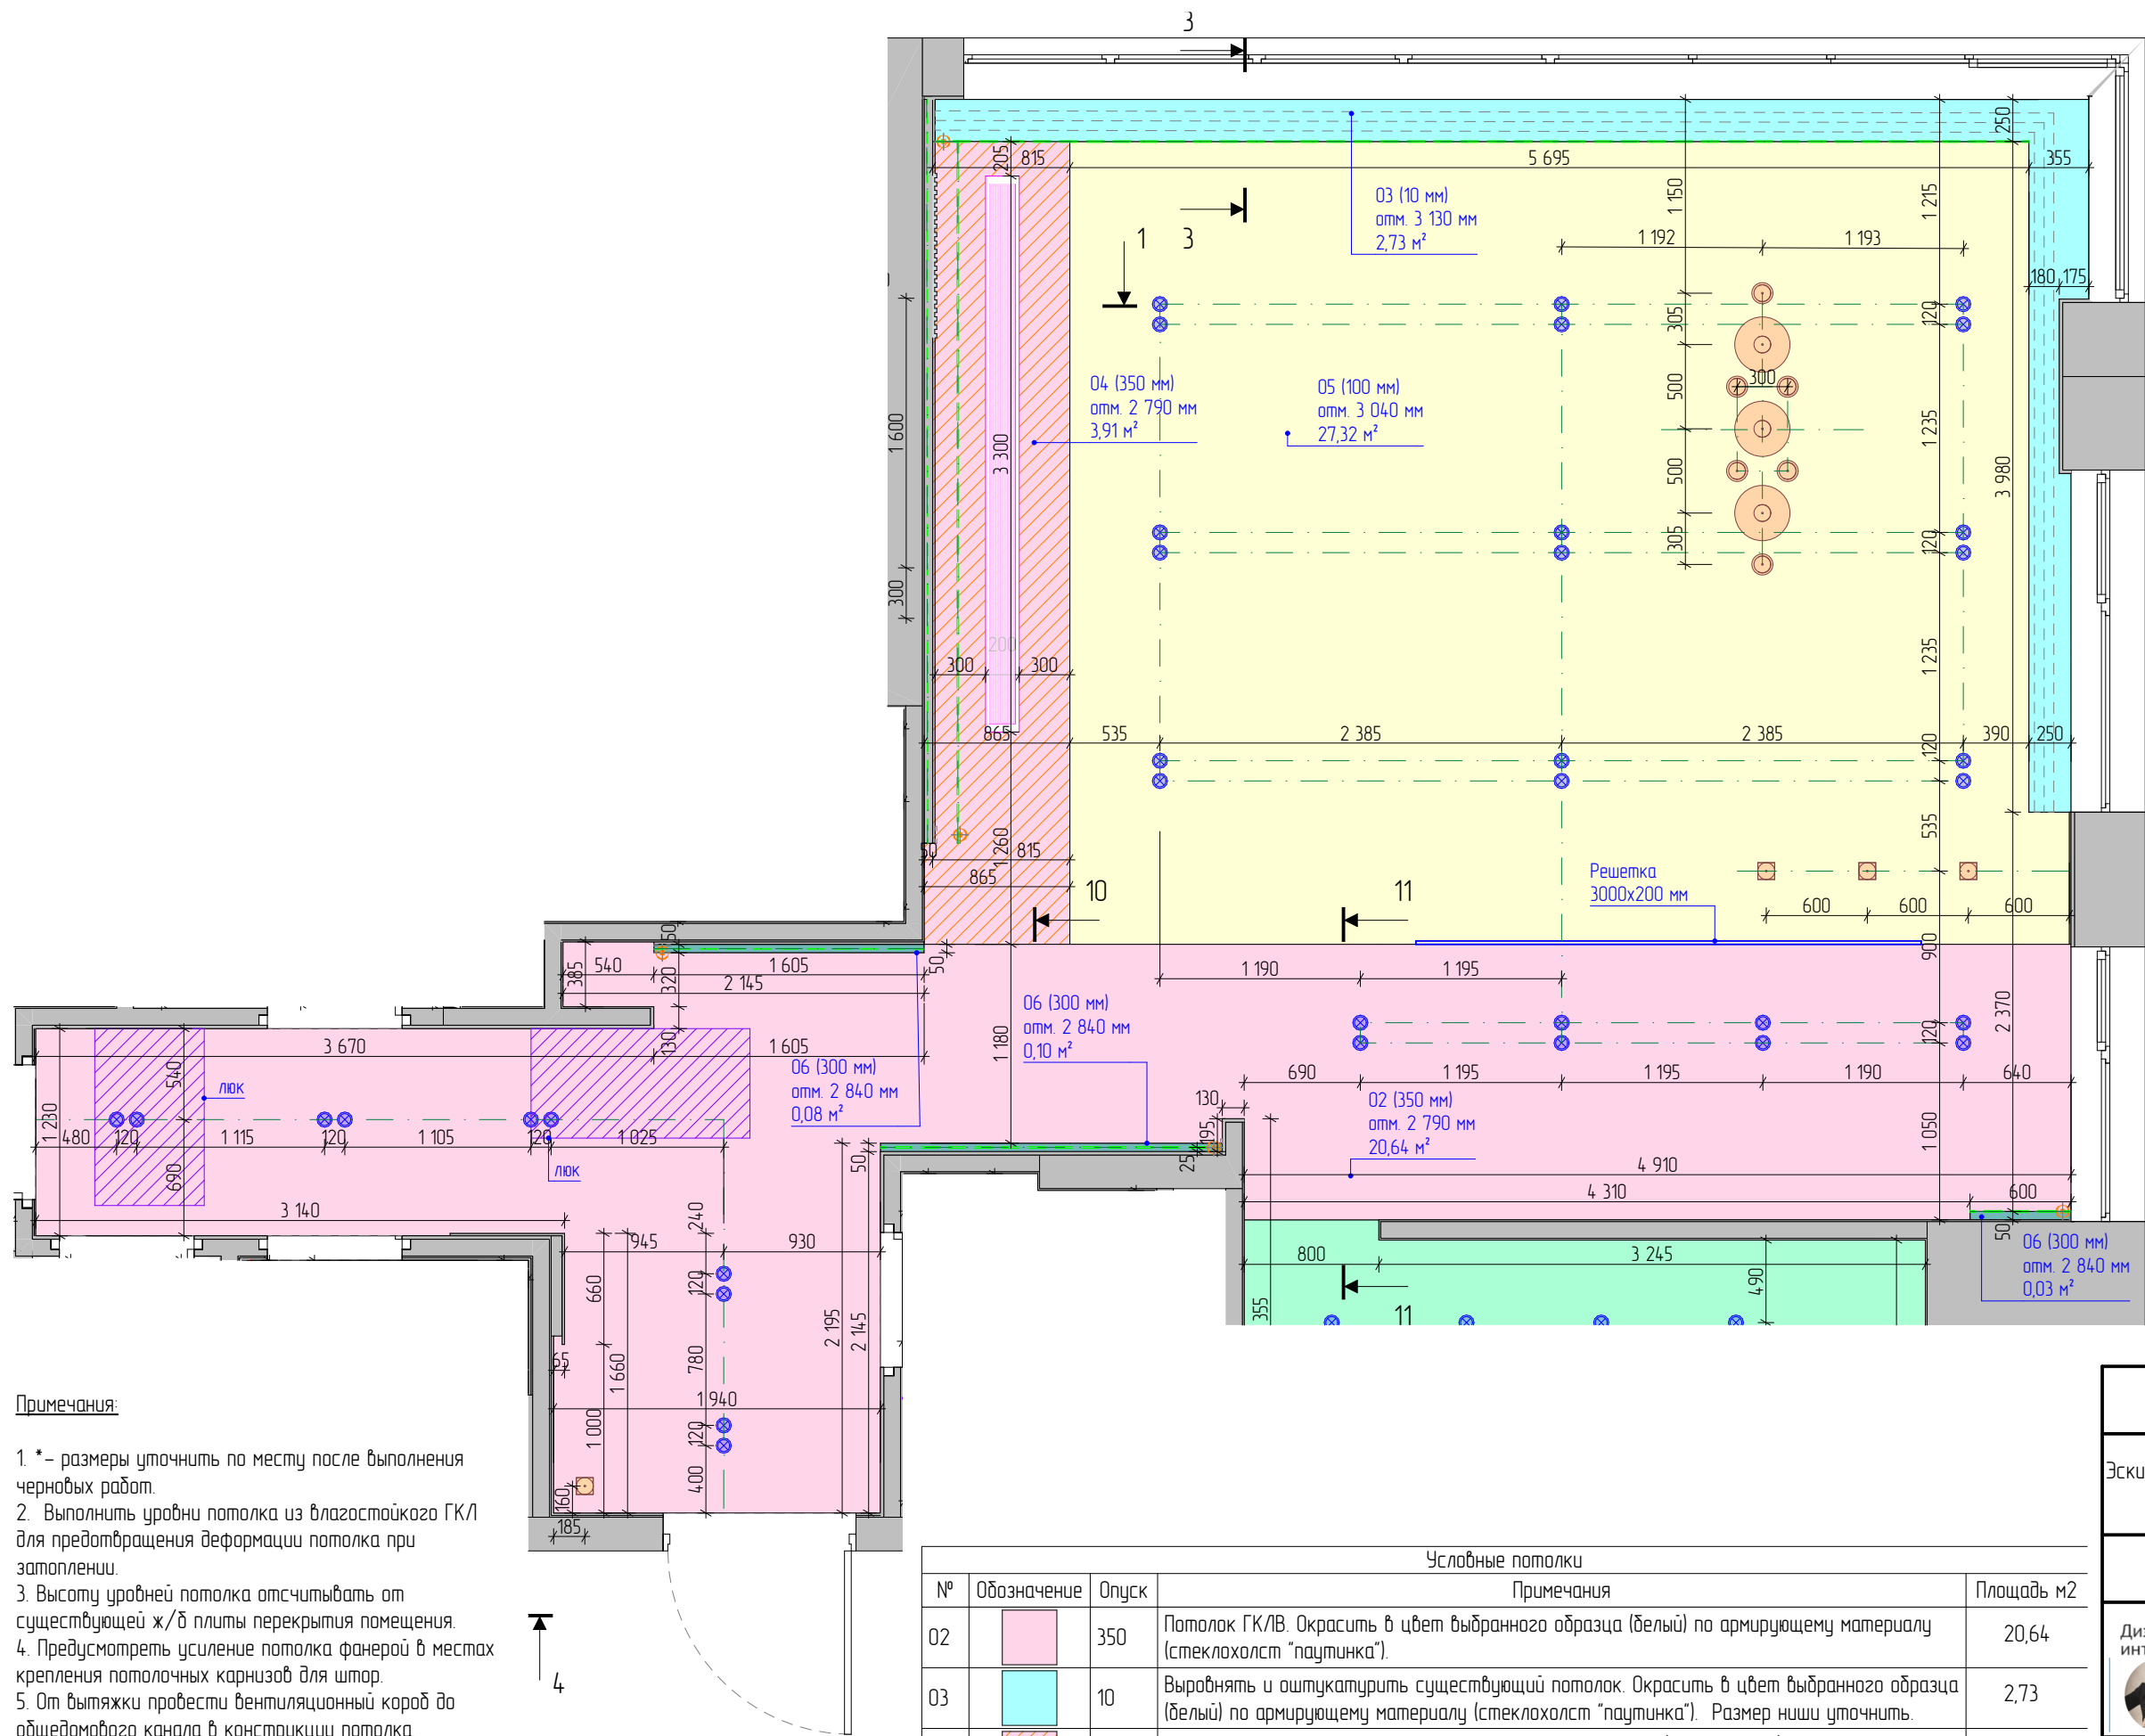


- Условные обозначения:
- Выход электрокабеля для светодиодной ленты
 - Люстра подвесная потолочная
 - Светильник точечный встраиваемый
 - Светодиодная лента
 - Люк доступа

- Примечания:
- * – размеры уточнить по месту после выполнения черновых работ.
 - Выполнить уровни потолка из влагостойкого ГКЛ для предотвращения деформации потолка при затоплении.
 - Высоту уровней потолка отсчитывать от существующей ж/б плиты перекрытия помещения.
 - Предусмотреть усиление потолка фанерой в местах крепления потолочных карнизов для штор.
 - От вытяжки провести вентиляционный короб до общедомового канала в конструкции потолка, уточнить по месту со специалистами и заказчиком.
 - Шумоизоляцию разработать со специалистами, уточнить состав и толщину слоев шумоизоляционных материалов. Уточнить необходимость устройства с заказчиком.

Условные потолки				
№	Обозначение	Опуск	Примечания	Площадь м2
02		350	Потолок ГК/ЛВ. Окрасить в цвет выбранного образца (белый) по армирующему материалу (стеклохолст "паутинка").	20,64
03		10	Выровнять и оштукатурить существующий потолок. Окрасить в цвет выбранного образца (белый) по армирующему материалу (стеклохолст "паутинка"). Размер ниши уточнить.	2,73
04		350	Потолок ГК/ЛВ с МДФ панелью. Цвет выбранного образца (*коричневый) уточнить при закупе.	3,91
05		100	Потолок ГК/ЛВ. Окрасить в цвет выбранного образца (белый) по армирующему материалу (стеклохолст "паутинка").	27,32
06		300	Потолок ГК/ЛВ. Окрасить в цвет выбранного образца (белый) по армирующему материалу (стеклохолст "паутинка").	0,21


МСК 392.12.25-ЭП ПРЕМИУМ				
Эскизный дизайн-проект интерьера квартиры в г. Москва ЖК "Остров", ул. Нижние Мневники д. 7				
Прихожая Кухня Гостиная.План отделки потолка.				
Дизайнер интерьера №1 Александр Батеньков	Стадия	Лист	Листов	
	ЭП	43	120	
		Подп.	Дата	
ГАП	Батеньков А.С.			
Гл. дизайнер	Власова В.А.			
Гл. проектиров.	Луныкова В.Н.			
Разработал	Ильина Е.Е.			

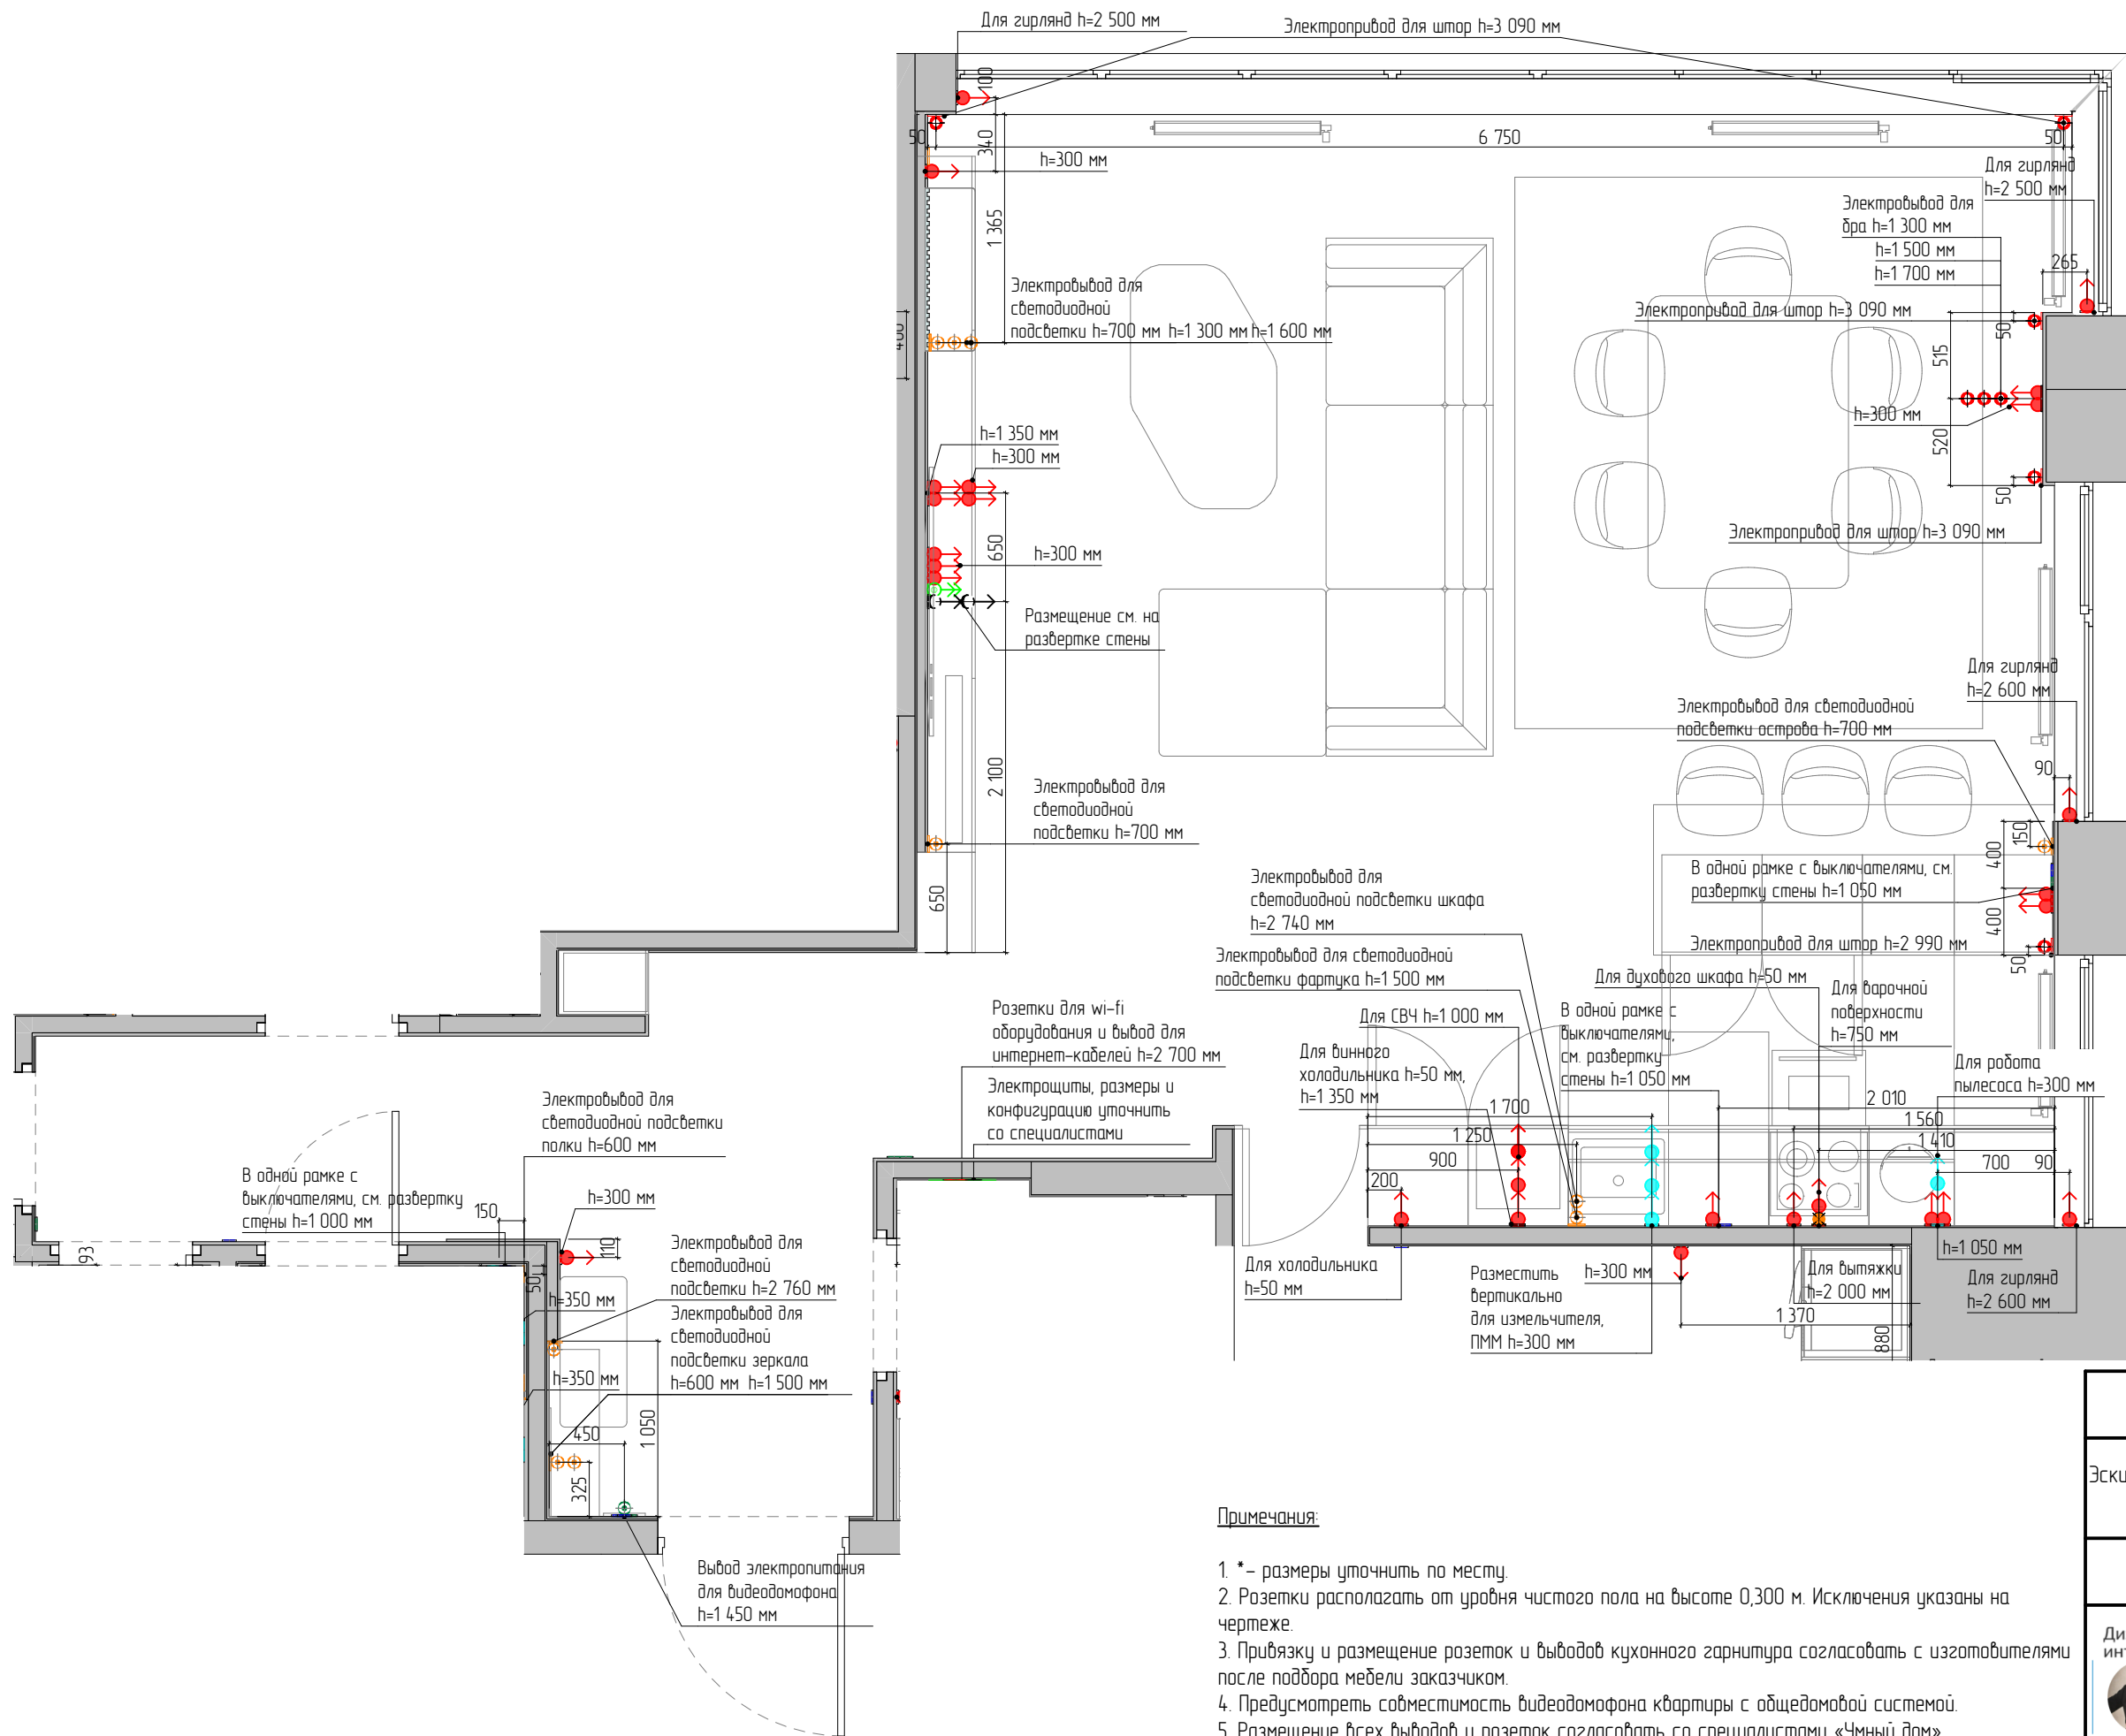

- Условные обозначения:
- Розетка 220V влагозащищенная
 - Розетка 220V
 - Вывод электрокабеля для светодиодной ленты
 - Вывод электрокабеля для варочной поверхности
 - Вывод спец. кабеля
 - Вывод интернет кабеля
 - wi-fi оборудование

- Примечания:
- * – размеры уточнить по месту.
 - Розетки располагать от уровня чистого пола на высоте 0,300 м. Исключения указаны на чертеже.
 - Приязку и размещение розеток и выводов кухонного гарнитура согласовать с изготовителями после подбора мебели заказчиком.
 - Предусмотреть совместимость видеодомофона квартиры с общедомовой системой.
 - Размещение всех выводов и розеток согласовать со специалистами «Умный дом».
 - Размеры и характеристики радиаторов отопления согласовать со специалистами, предусмотреть терморегуляторы.
 - Датчики пожарной и охранной сигнализации и электровыводы для них разместить совместно со специалистами, предварительно вызвав их на объект.
 - Размещение розеток и электровыводов по высоте см. на развертках стен.

МСК 392.12.25–ЭП ПРЕМИУМ			
Эскизный дизайн–проект интерьера квартиры в г. Москва ЖК "Остров", ул. Нижние Мневники д. 7			
Прихожая Кухня Гостиная.План размещения электрооборудования.			
Дизайнер интерьера №1 Александр Батеньков	Стадия	Лист	Листов
	ЭП	44	120
		Подп.	Дата
ГАП	Батеньков А.С.		
Гл. дизайнер	Власова В.А.		
Гл. проектиров.	Луныкова В.Н.		
Разработал	Ильина Е.Е.		






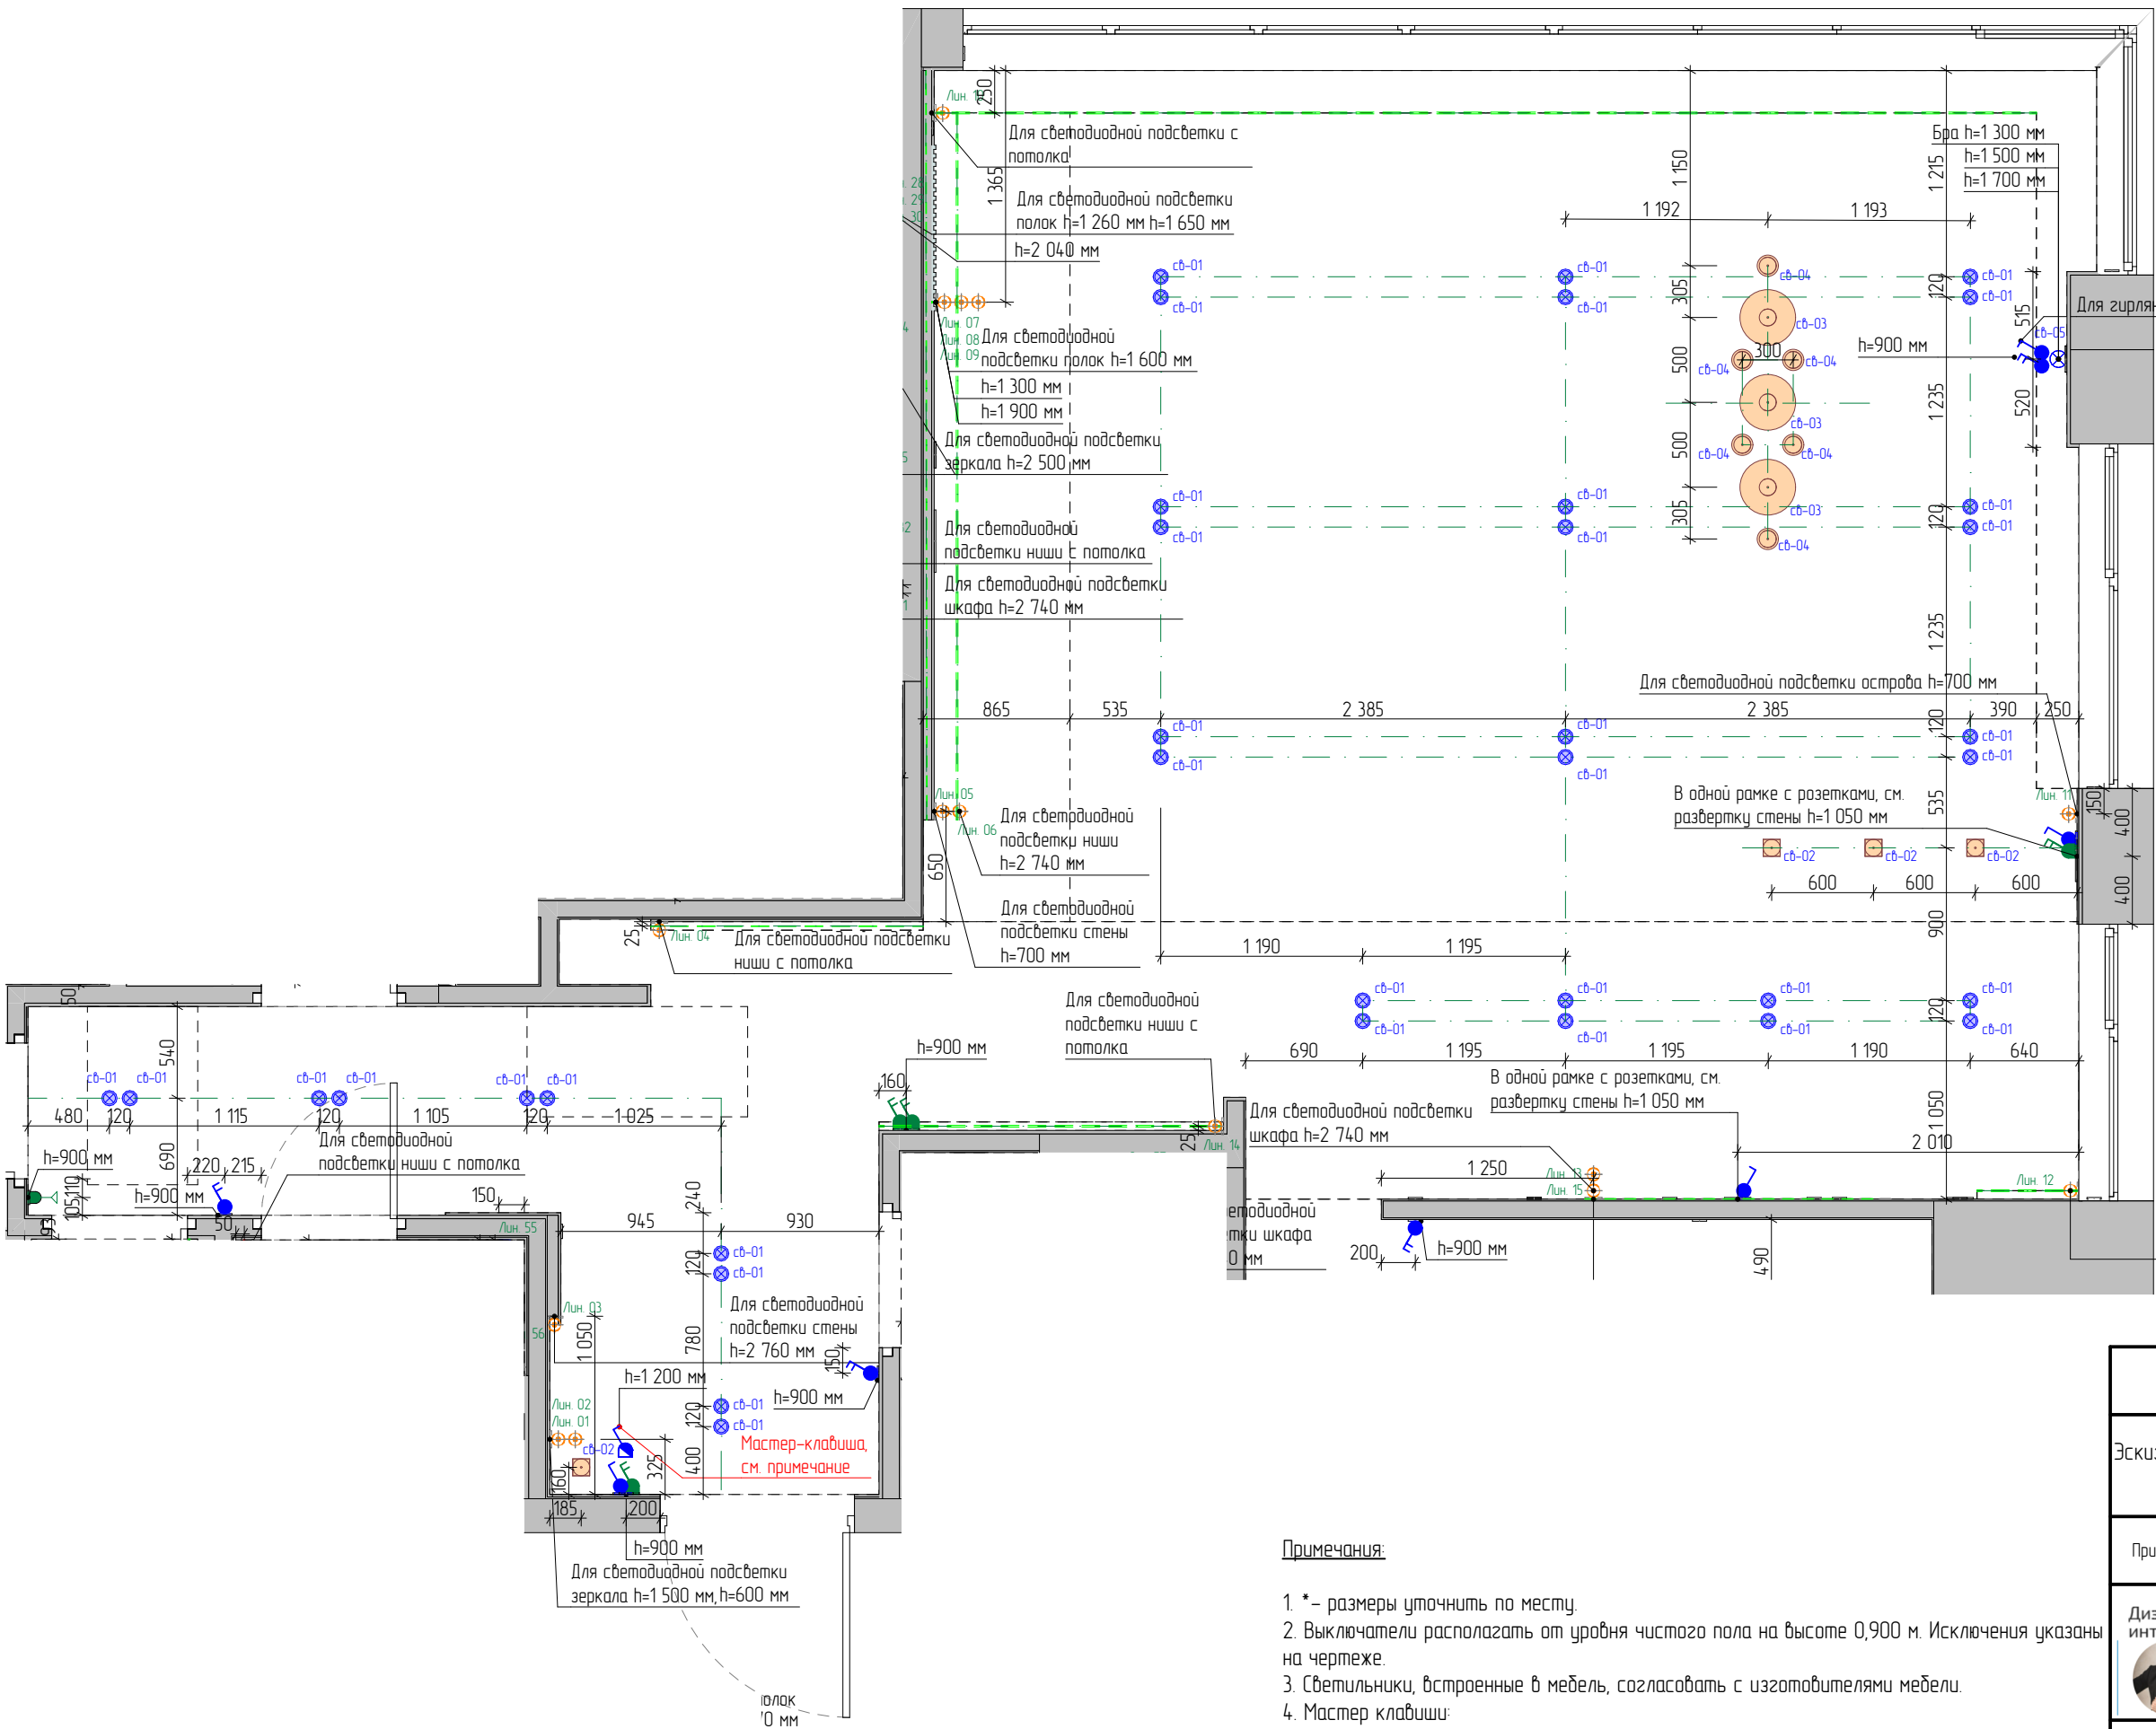


- Условные обозначения:
- Выход 220V
 - Выход электрокабеля для светодиодной ленты
 - Выключатель одноклавишный
 - Выключатель двухклавишный
 - Люстра подвесная потолочная
 - Переключатель двухклавишный
 - Переключатель одноклавишный переходной
 - Светильник точечный встраиваемый
 - Светодиодная лента

Примечания:

- * – размеры уточнить по месту.
- Выключатели располагать от уровня чистого пола на высоте 0,900 м. Исключения указаны на чертеже.
- Светильники, встроенные в мебель, согласовать с изготовителями мебели.
- Мастер клавиши:
№1 – выключение всего освещения квартиры, размещение согласовать с заказчиком при начале строительных работ;
№2 – выключение электропитания (розетки) кроме холодильника, морозильных камер, охранной сигнализации, датчиков протечки и др. по согласованию с заказчиком непосредственно на объекте.

МСК 392.12.25–ЭП ПРЕМИУМ			
Эскизный дизайн–проект интерьера квартиры в г. Москва ЖК "Остров", ул. Нижние Мневники д. 7			
Прихожая Кухня ГостинаяПлан размещения освещения и выключателей.			
Дизайнер интерьера №1 Александр Батеньков	Стадия	Лист	Листов
	ЭП	45	120
		Подп.	Дата
ГАП	Батеньков А.С.		
Гл. дизайнер	Власова В.А.		
Гл. проектиров.	Луныкова В.Н.		
Разработал	Ильина Е.Е.		

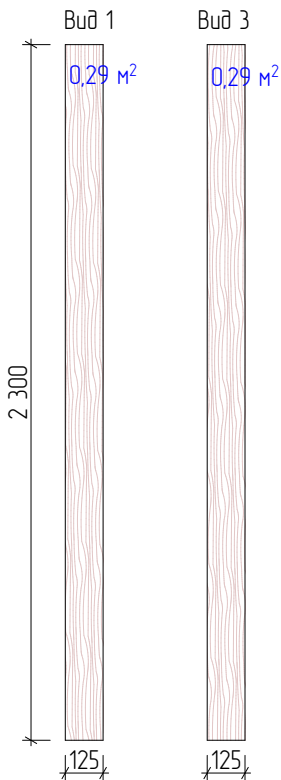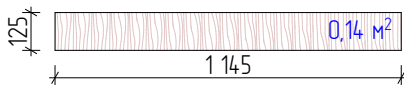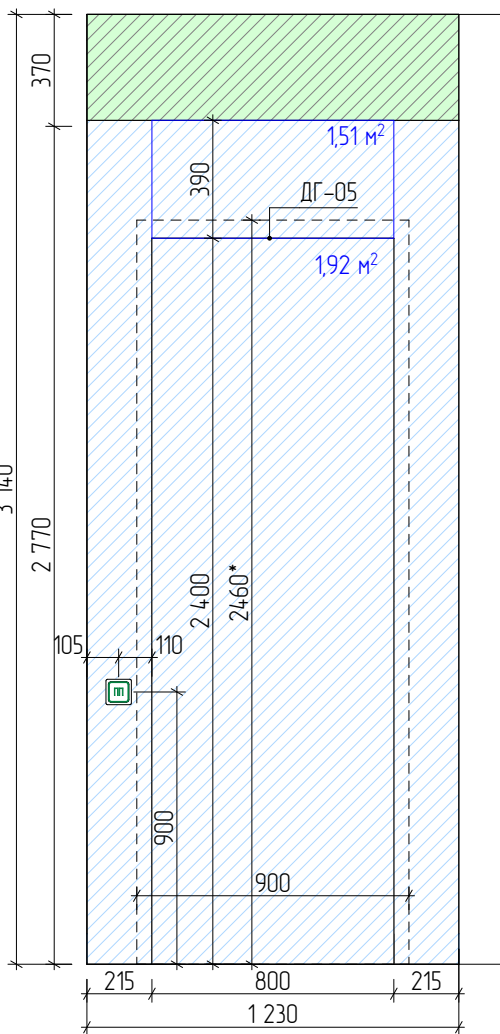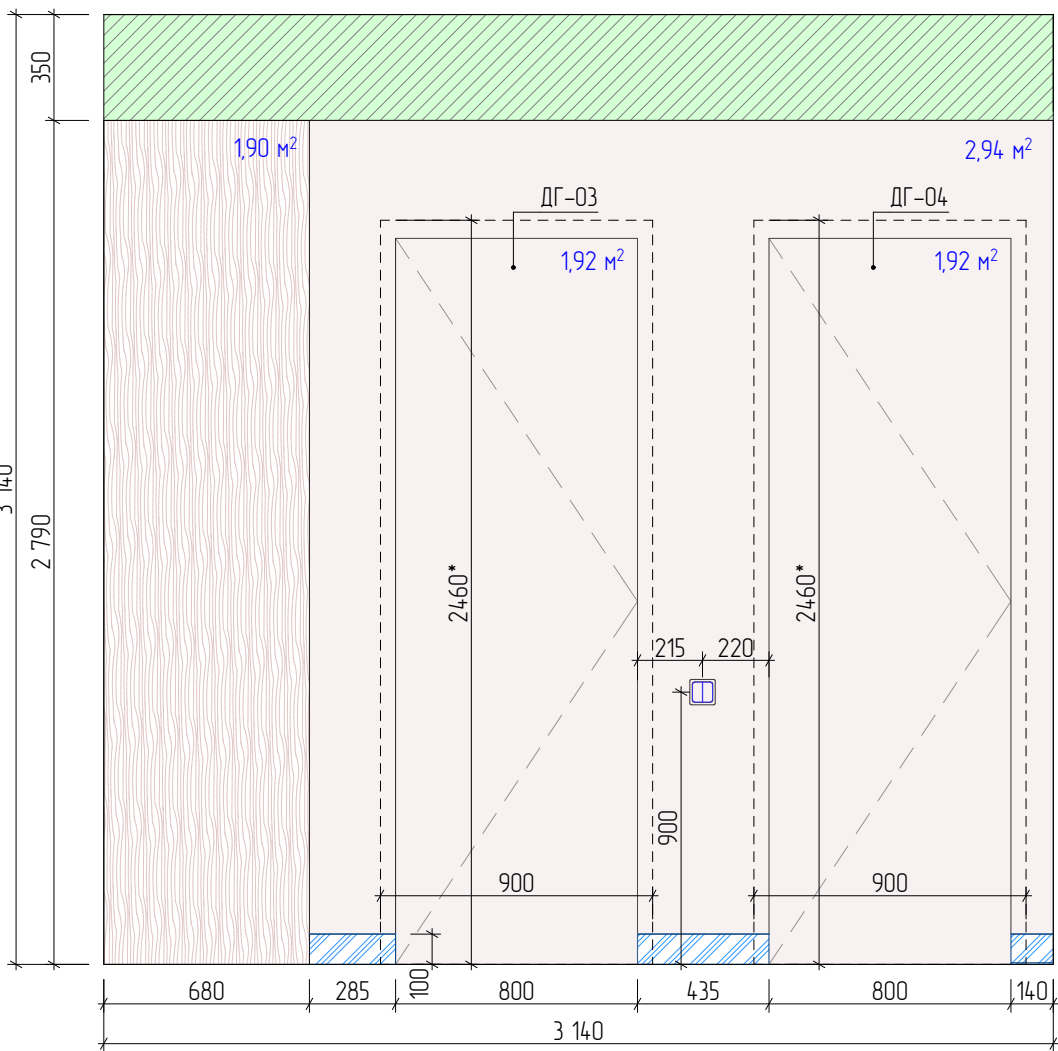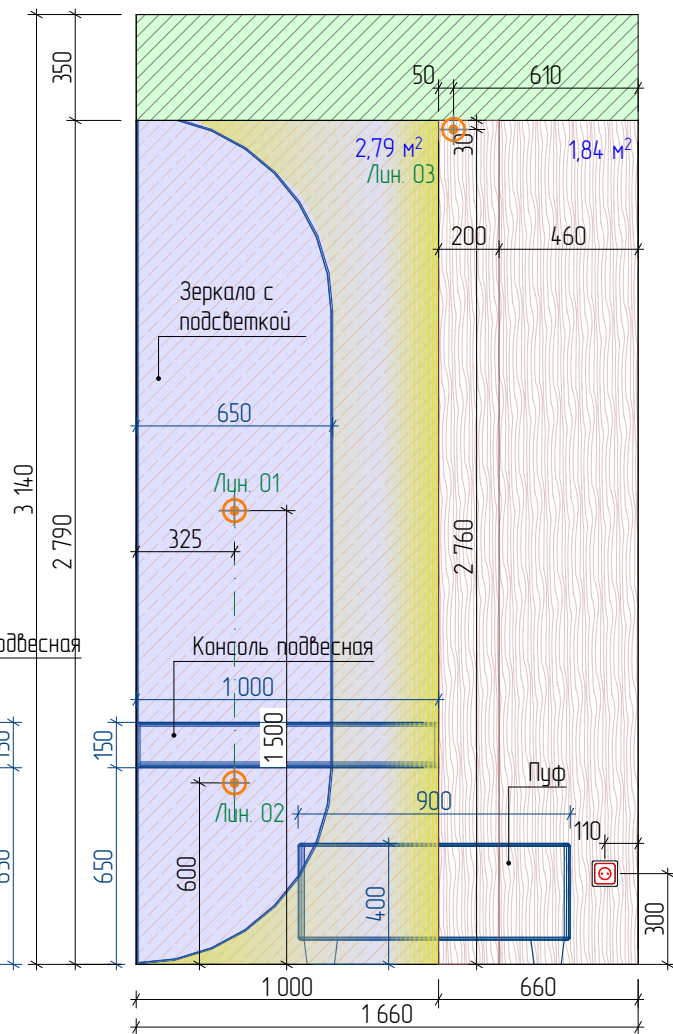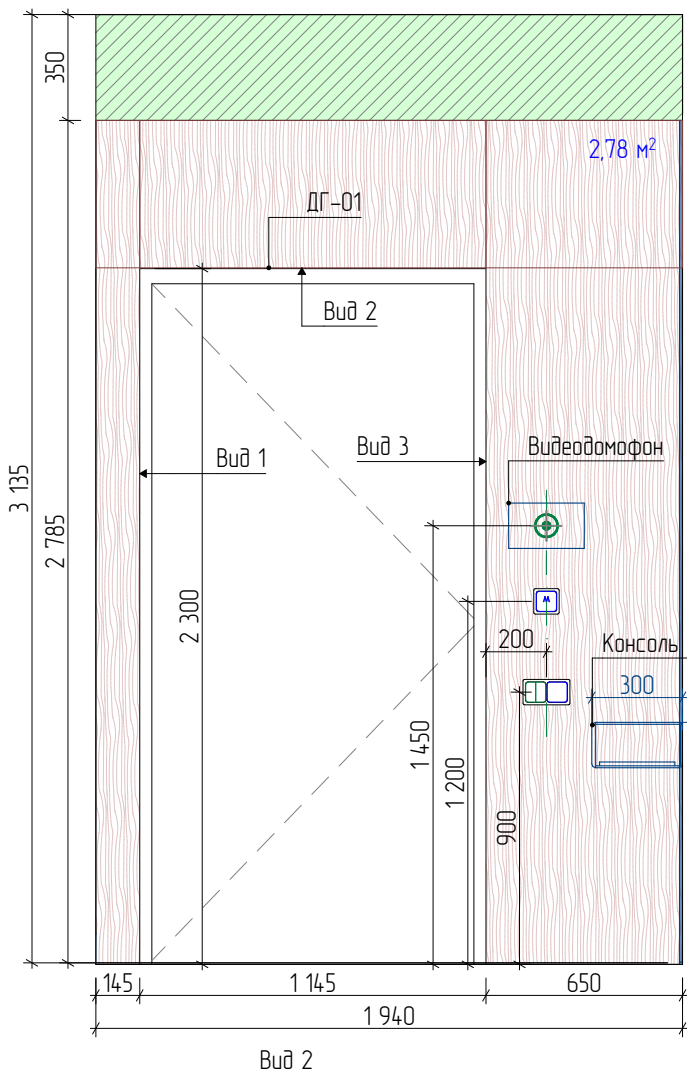





Условные обозначения:

- Плинтус №1. Теневой плинтус скрытого монтажа с МДФ вставкой. Теневой зазор от пола 100 мм. Цвет при выборе образца (в цвет стен).
- Монтаж конструкций из ГКВЛ
- Покраска №1. Выполнить по подготовленной поверхности (стеклохолст*). Цвет при выборе образца (бежевый*).
- МДФ панель №1. Шпонированная. Цвет и фактура при выборе образца (орех*).
- МДФ панель №2. Цвет и фактура при выборе образца (темный мрамор*).
- Зеркало №1. Разработать со специалистами (тонированное*) размеры и резка по чертежу.
- Выход электрокабеля для светодиодной ленты
- Выход спец кабелей
- Розетка 220 V
- Выключатель одноклавишный
- Выключатель двухклавишный
- Переключатель одноклавишный переходной
- Переключатель двухклавишный
- Мастер-клавиша

Примечания:

- * - размеры уточнить по месту после выполнения черновых отделочных работ.
- Выключатели располагать от уровня чистого пола на высоте 900 мм. Исключения указаны на чертеже.
- Розетки располагать от уровня чистого пола на высоте 300 мм. Исключения указаны на чертеже.
- Цвет окрашивания плинтуса уточнить после согласования образца.
- Высоту проемов выполнить 2460 мм от уровня чистого пола. Уточнить после подбора и согласования модели дверей.
- Резку зеркала решить по месту авторским надзором.
- Плинтус подрезать по месту в местах стыковки с дверями и мебелью.
- Внутреннее наполнение мебели разработать со специалистами.
- Серым/синим цветом показаны размеры мебели. Мебель разработать со специалистами, размеры уточнить после выполнения чистовой отделки.

МСК 392.12.25-ЭП ПРЕМИУМ			
Эскизный дизайн-проект интерьера квартиры в г. Москва ЖК "Остров", ул. Нижние Мневники д. 7			
Прихожая Кухня Гостиная.Развертки стен А-01, А-02, А-03, А-04.			
Дизайнер интерьера №1 Александр Батеньков	Стадия	Лист	Листов
	ЭП	46	120
		Подп.	Дата
ГАП	Батеньков А.С.		
Гл. дизайнер	Власова В.А.		
Гл. проектиров.	Луцькова В.Н.		
Разработал	Ильина Е.Е.		

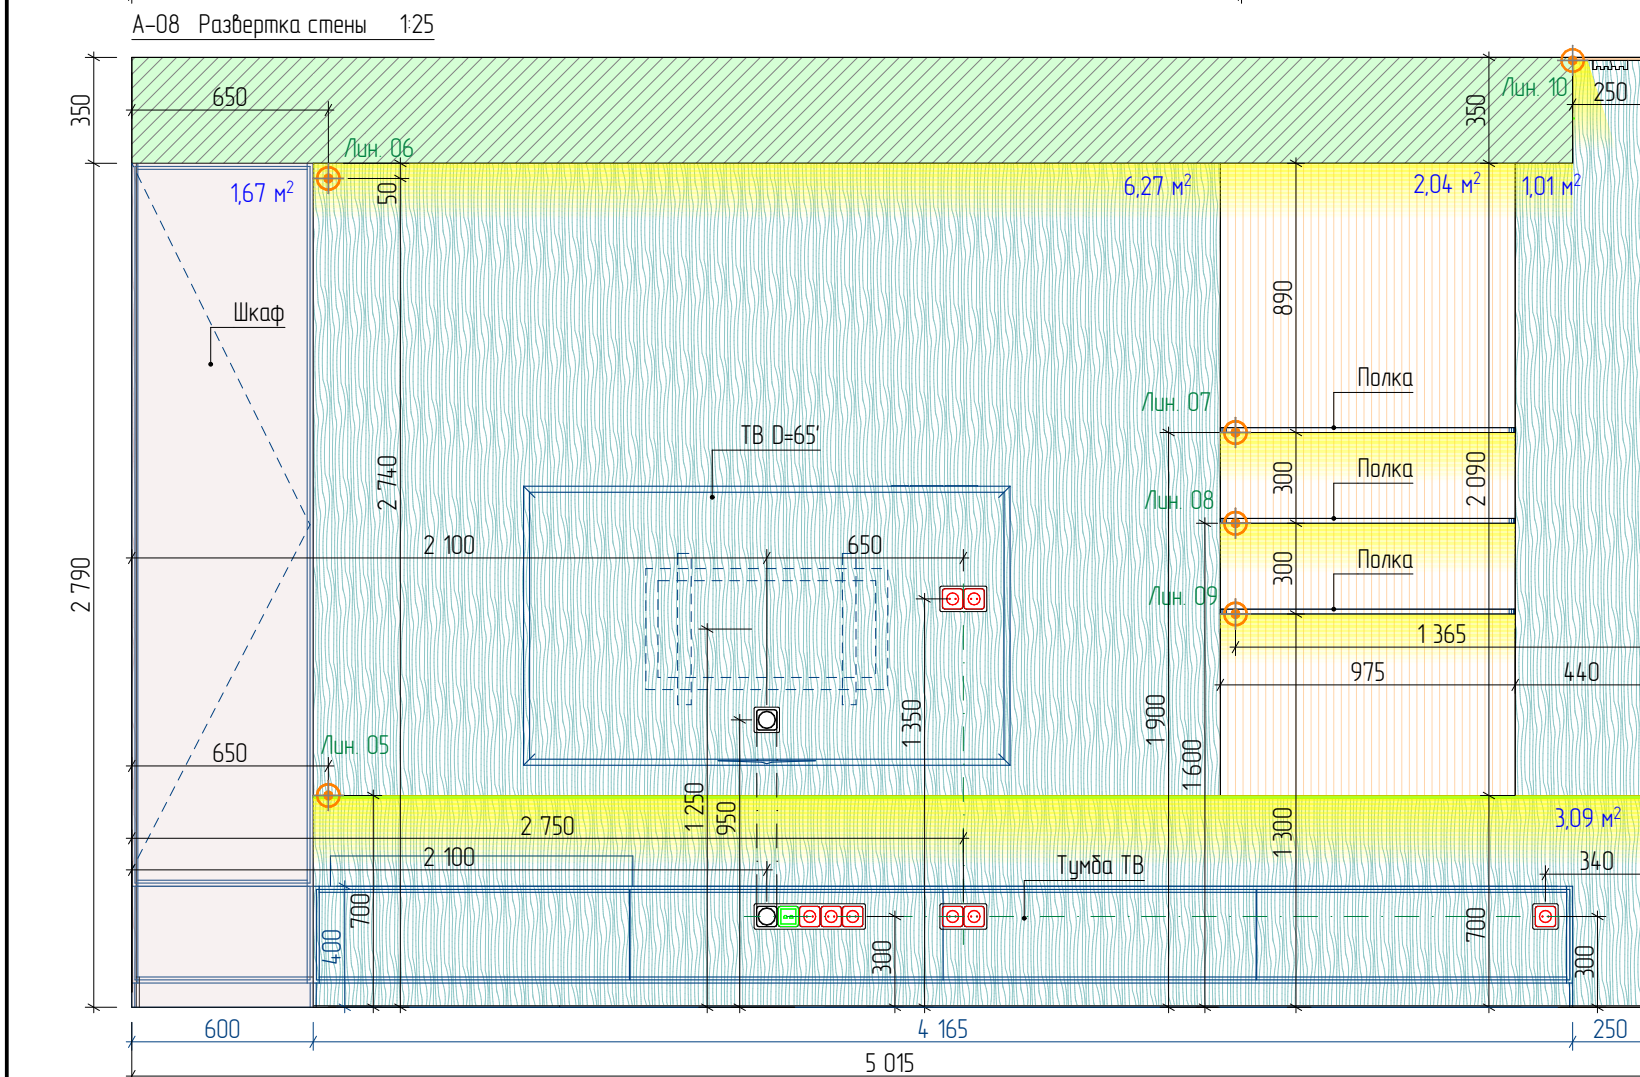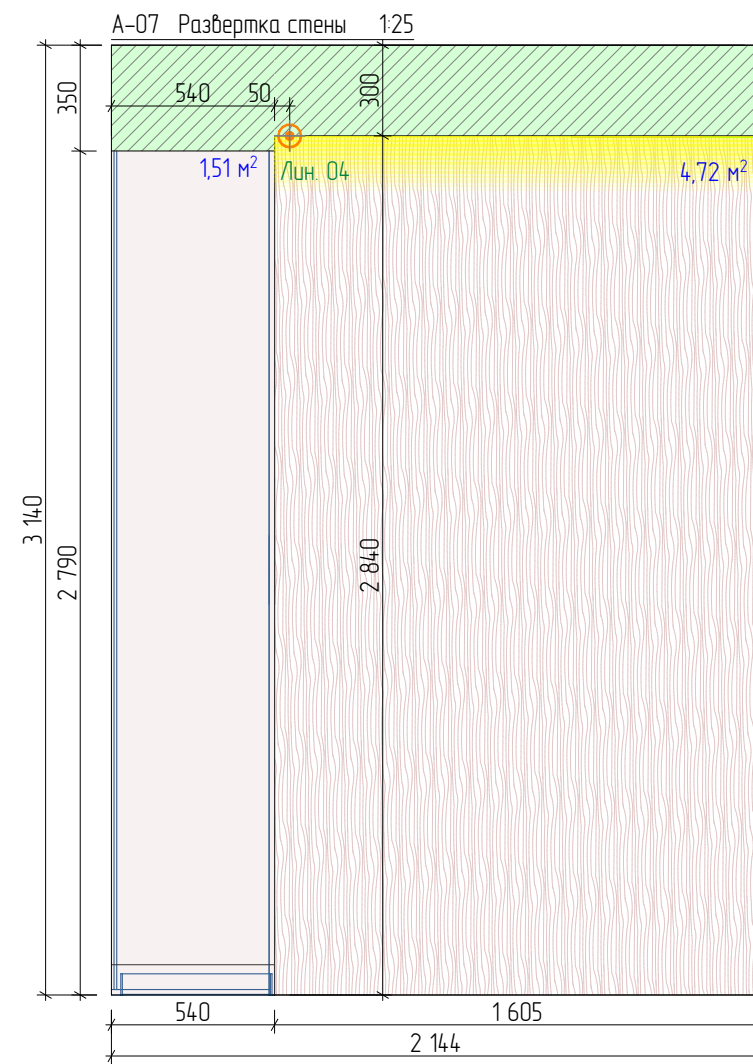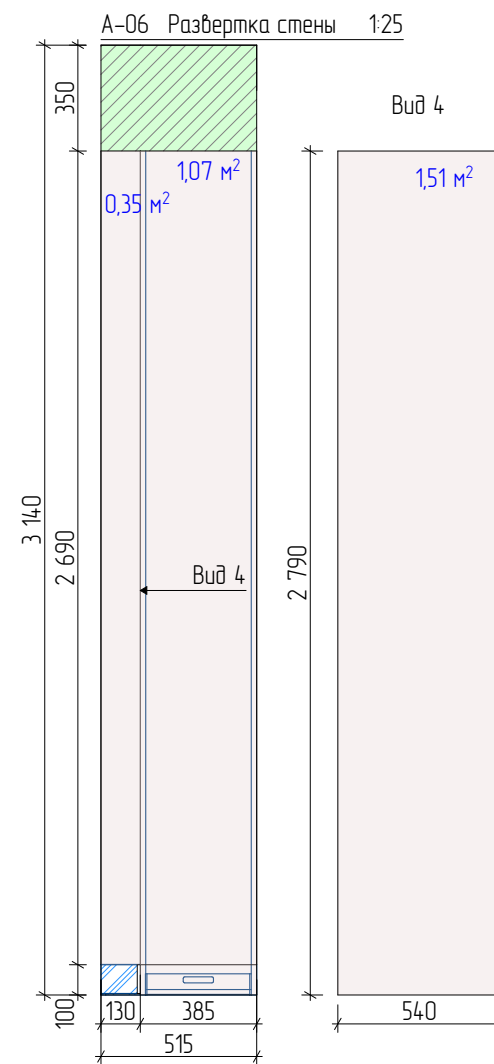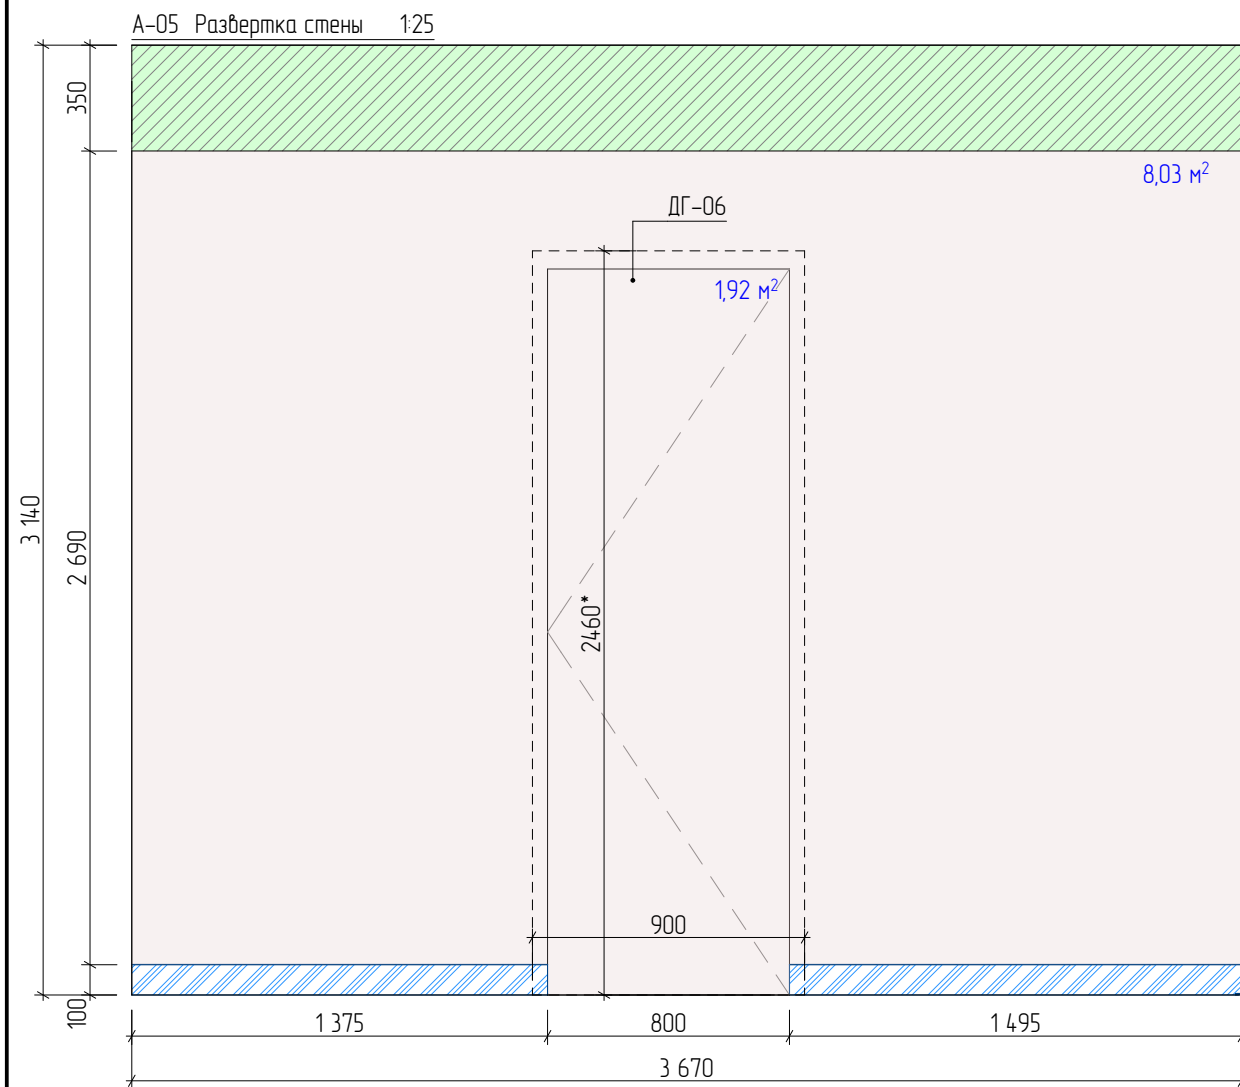

Условные обозначения:

- Плинтус №1. Теневой плинтус скрытого монтажа с МДФ вставкой. Теневой зазор от пола 100 мм. Цвет при выборе образца (в цвет стен).
- Монтаж конструкций из ГКВЛ
- Покраска №1. Выполнить по подготовленной поверхности (стеклохолст*). Цвет при выборе образца (бежевый*).
- МДФ панель №1. Шпонированная. Цвет и фактура при выборе образца (орех*).
- МДФ панель №3. ЗД панель. Цвет и фактура при выборе образца (в цвет мебели*).

- МДФ панель №4. Цвет и фактура при выборе образца (ржавый металл*).
- Розетка 220 V
- Интернет-розетка двойная
- Кабель-канал
- Вывод электрокабеля для светодиодной ленты


Примечания:

- * - размеры уточнить по месту после выполнения черновых отделочных работ.
- Выключатели располагать от уровня чистого пола на высоте 900 мм. Исключения указаны на чертеже.
- Розетки располагать от уровня чистого пола на высоте 300 мм. Исключения указаны на чертеже.
- Цвет окрашивания плинтуса уточнить после согласования образца.
- Высоту проемов выполнить 2460 мм от уровня чистого пола. Уточнить после подбора и согласования модели дверей.
- Плинтус подрезать по месту в местах стыковки с дверями и мебелью.
- Внутреннее наполнение мебели разработать со специалистами.
- Серым/синим цветом показаны размеры мебели. Мебель разработать со специалистами, размеры уточнить после выполнения чистой отделки.

МСК 392.12.25-ЭП ПРЕМИУМ



Эскизный дизайн-проект интерьера квартиры в г. Москва ЖК "Остров", ул. Нижние Мневники д. 7

Прихожая Кухня Гостиная Развертки стен А-05, А-06, А-07, А-08.

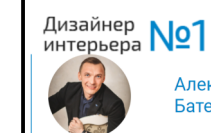

Александр Батеньков

Стадия	Лист	Листов
ЭП	47	120
	Подп.	Дата
ГАП	Батеньков А.С.	
Гл. дизайнер	Власова В.А.	
Гл. проектиров.	Луныкова В.Н.	
Разработал	Ильина Е.Е.	

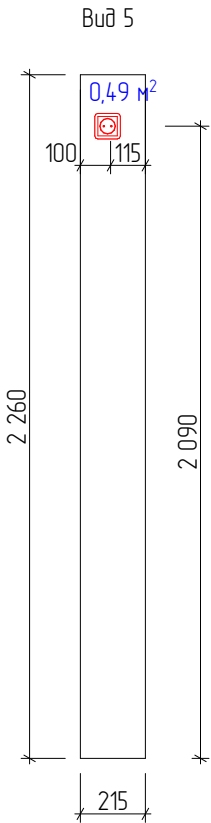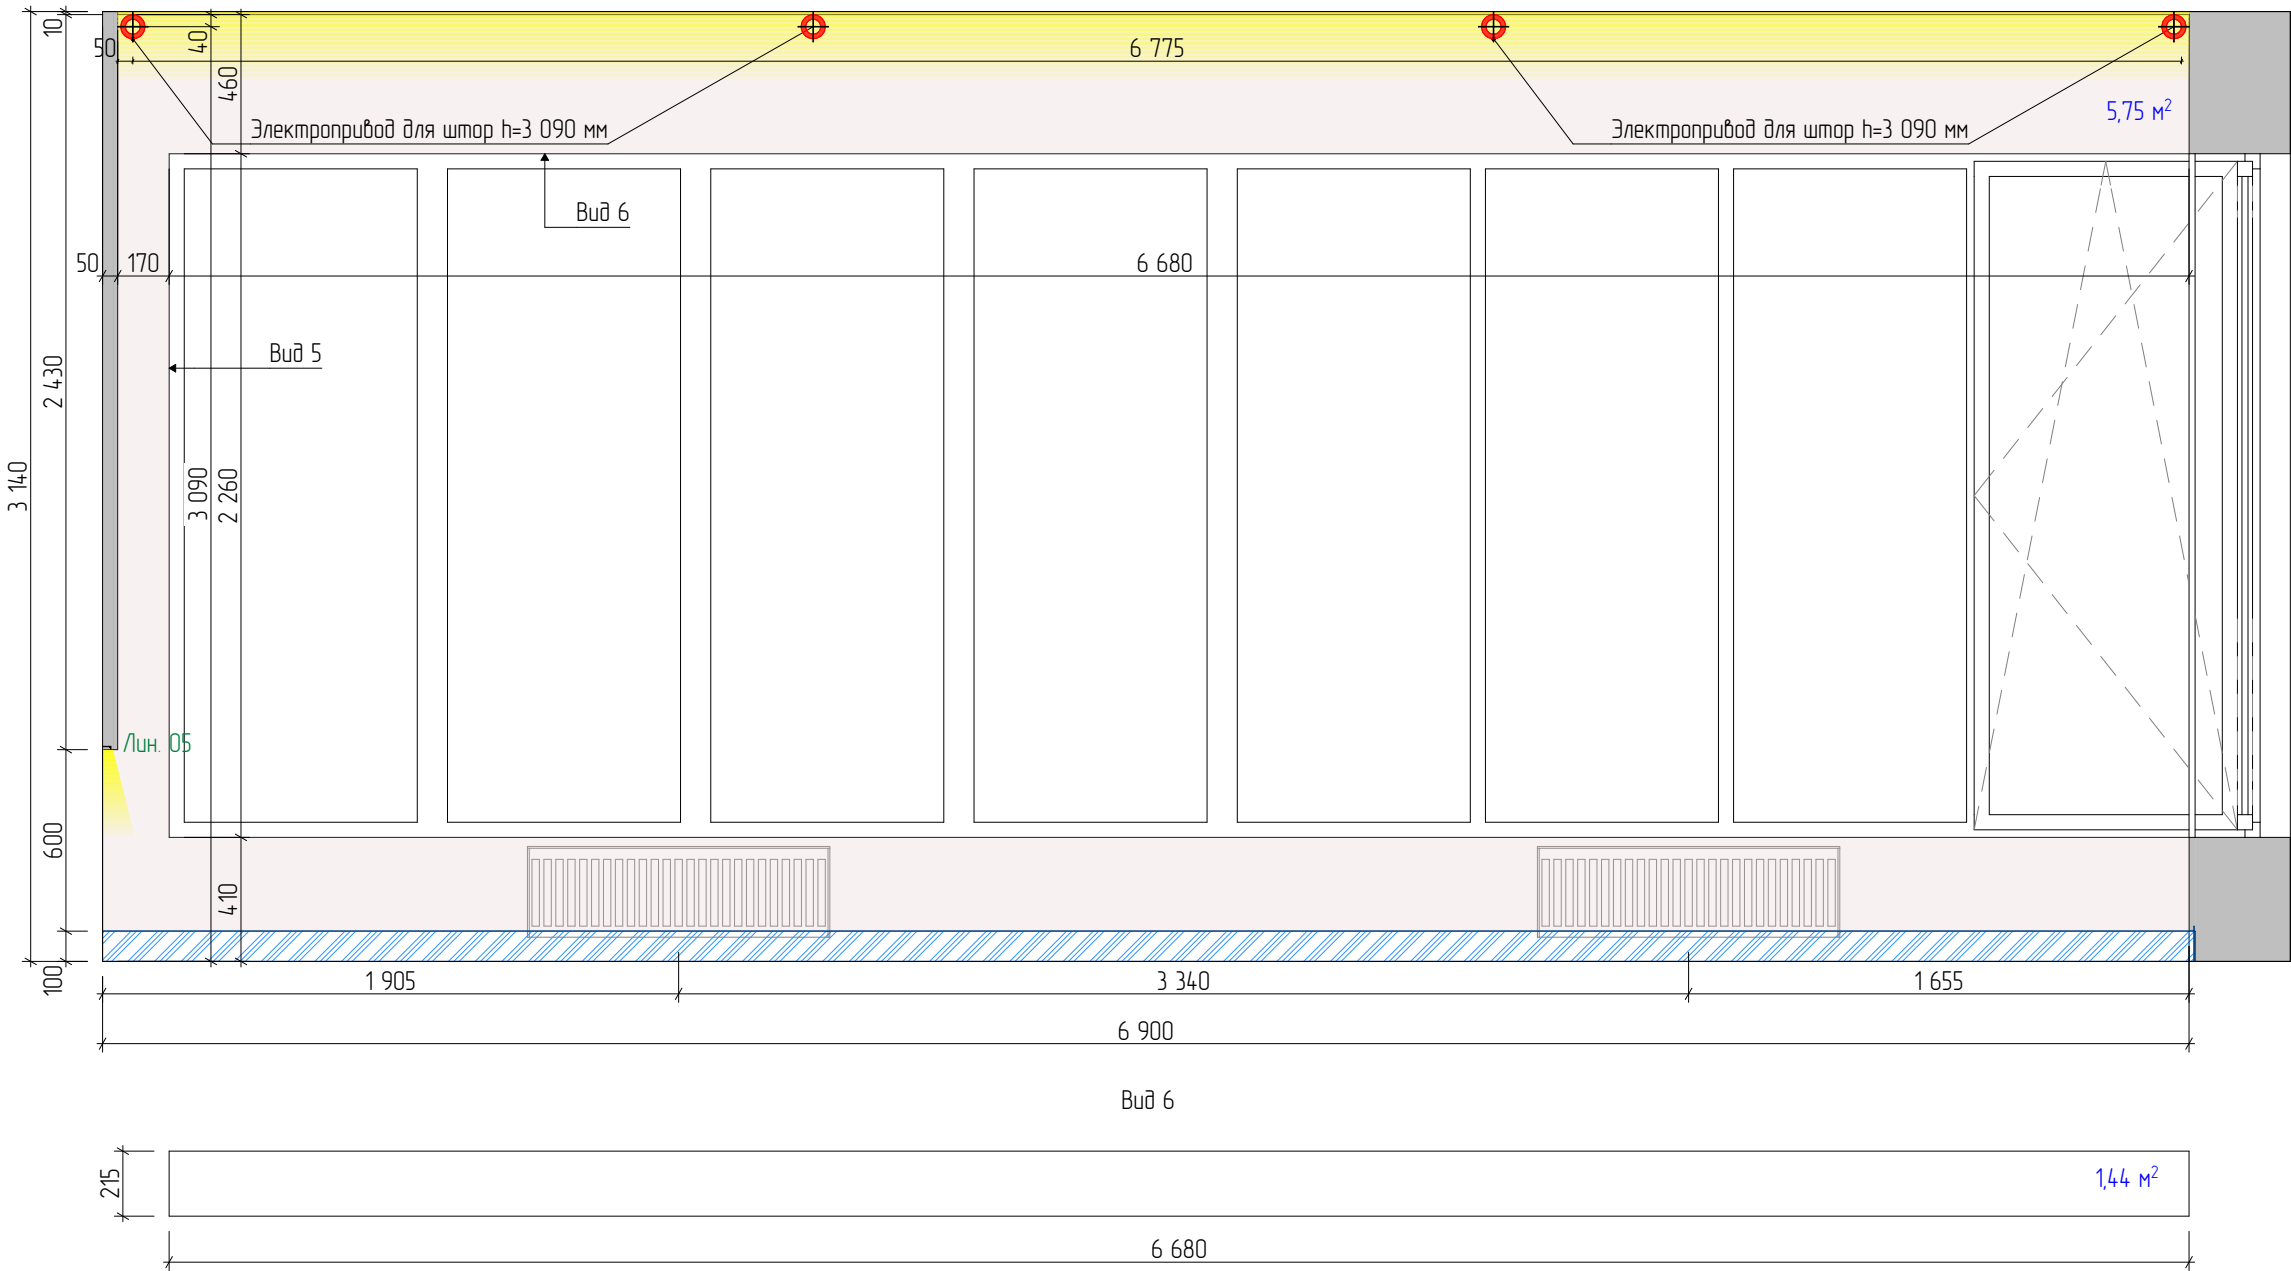


Условные обозначения:

- Плинтус №1. Теневой плинтус скрытого монтажа с МДФ вставкой. Теневой зазор от пола 100 мм. Цвет при выборе образца (в цвет стен).
- Монтаж конструкций из ГКВЛ
- Покраска №1. Выполнить по подготовленной поверхности (стеклохолст*). Цвет при выборе образца (бежевый*).
- Покраска №2. Выполнить по подготовленной поверхности (стеклохолст*). Цвет при выборе образца (белый*).
- Вывод 220 V
- Розетка 220 V


Примечания:

- * – размеры уточнить по месту после выполнения черновых отделочных работ.
- Выключатели располагать от уровня чистого пола на высоте 900 мм. Исключения указаны на чертеже.
- Розетки располагать от уровня чистого пола на высоте 300 мм. Исключения указаны на чертеже.
- Оконные откосы оклеить строительным флизелином и окрасить в белый цвет. Уточнить по месту.
- Размещение выводов для отопления согласовать со специалистами.
- Цвет окрашивания плинтуса уточнить после согласования образца.

МСК 392.12.25–ЭП ПРЕМИУМ			
Эскизный дизайн–проект интерьера квартиры в г. Москва ЖК "Остров", ул. Нижние Мневники д. 7			
Прихожая Кухня Гостиная.Развертки стен А-09.			
Дизайнер интерьера Александр Батеньков	Стадия	Лист	Листов
	ЭП	48	120
		Подп.	Дата
ГАП	Батеньков А.С.		
Гл. дизайнер	Власова В.А.		
Гл. проектиров.	Луныкова В.Н.		
Разработал	Ильина Е.Е.		

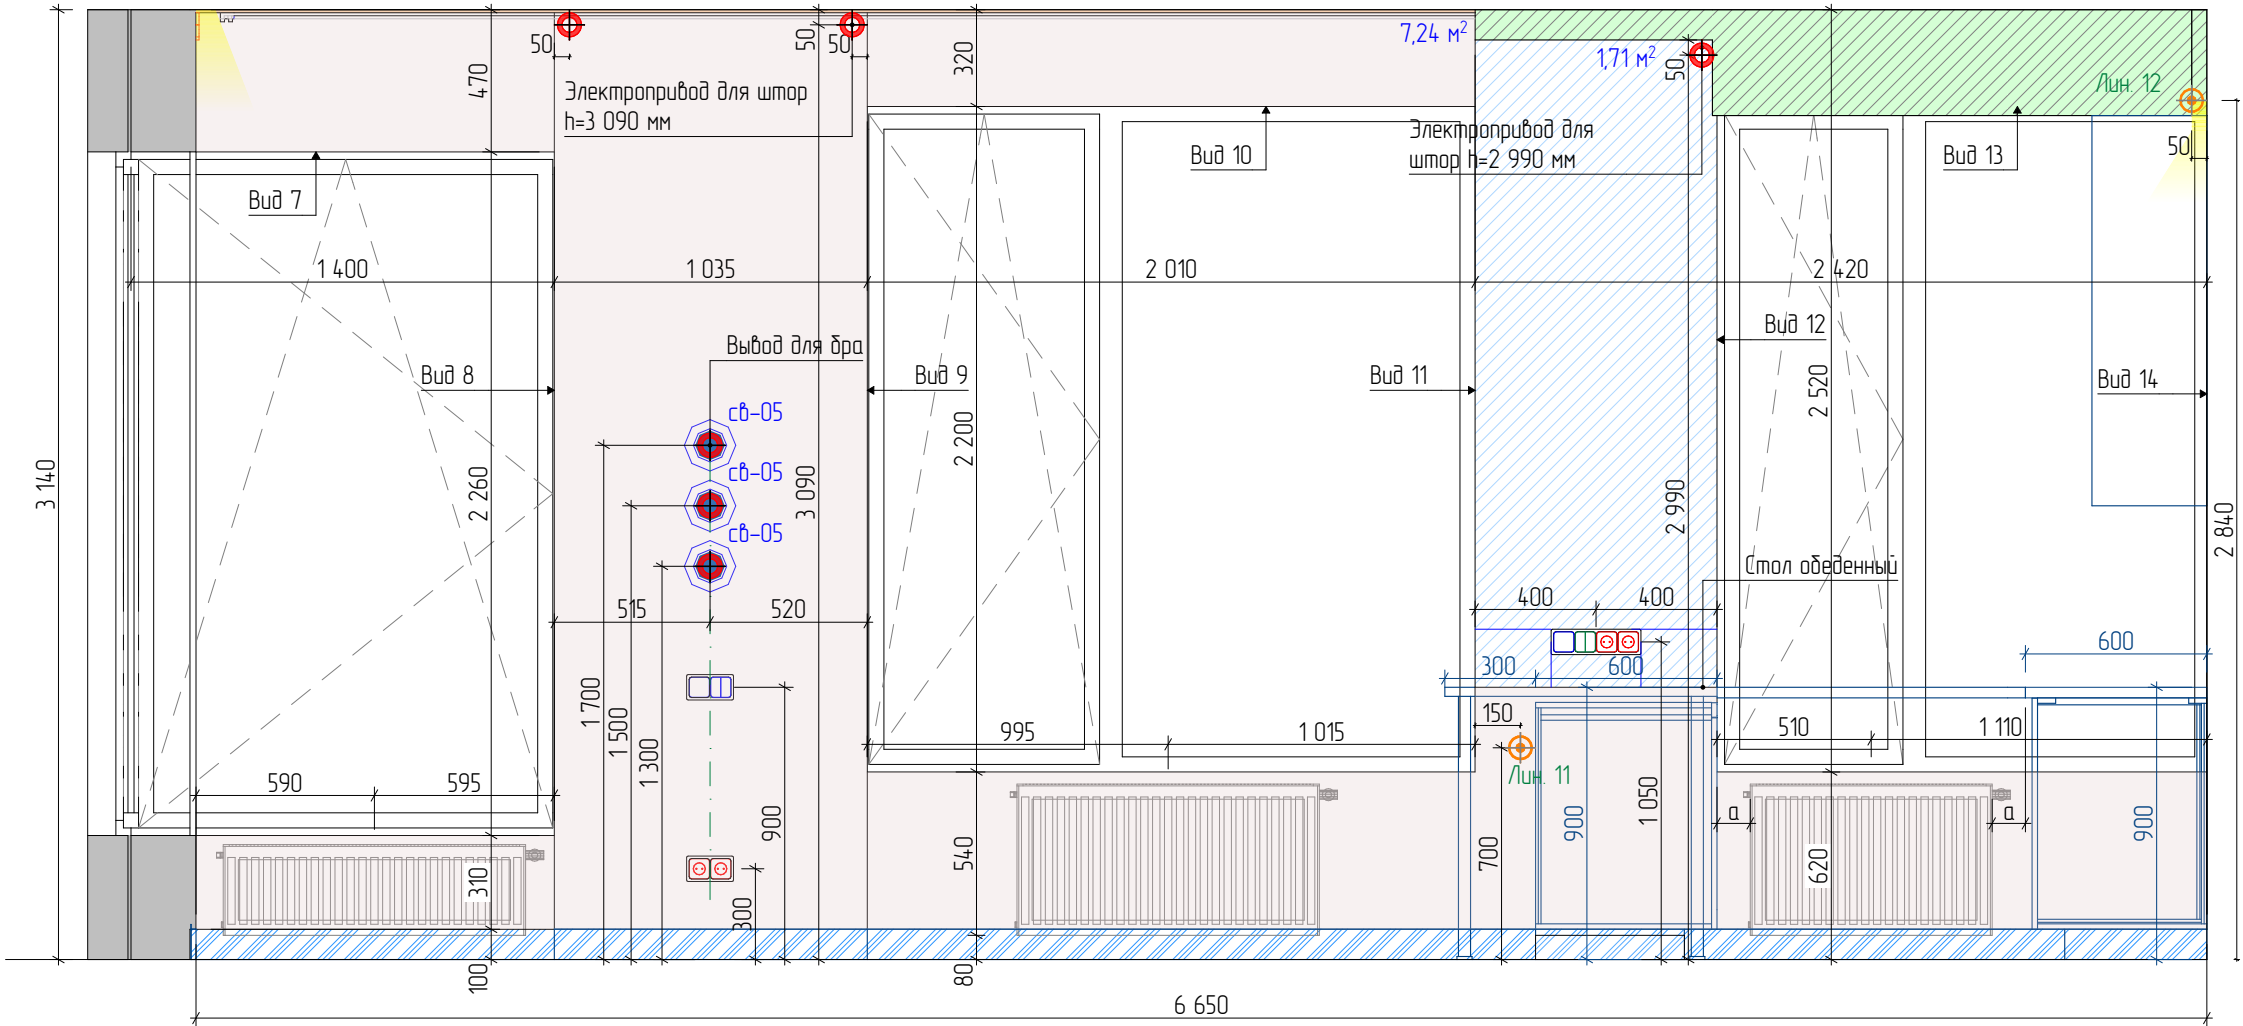


- Условные обозначения:
- Плинтус №1. Теневой плинтус скрытого монтажа с МДФ вставкой. Теневой зазор от пола 100 мм. Цвет при выборе образца (в цвет стен).
 - Монтаж конструкций из ГКВЛ
 - Покраска №1. Выполнить по подготовленной поверхности (стеклохолст*). Цвет при выборе образца (бежевый*).
 - Покраска №2. Выполнить по подготовленной поверхности (стеклохолст*). Цвет при выборе образца (белый*).
 - Зеркало №1. Разработать со специалистами (тонированное*) размеры и резка по чертежу.
 - Вывод 220 V
 - Вывод электрокабеля для светодиодной ленты
 - Розетка 220 V
 - Выключатель одноклавишный
 - Выключатель двухклавишный
 - Переключатель двухклавишный

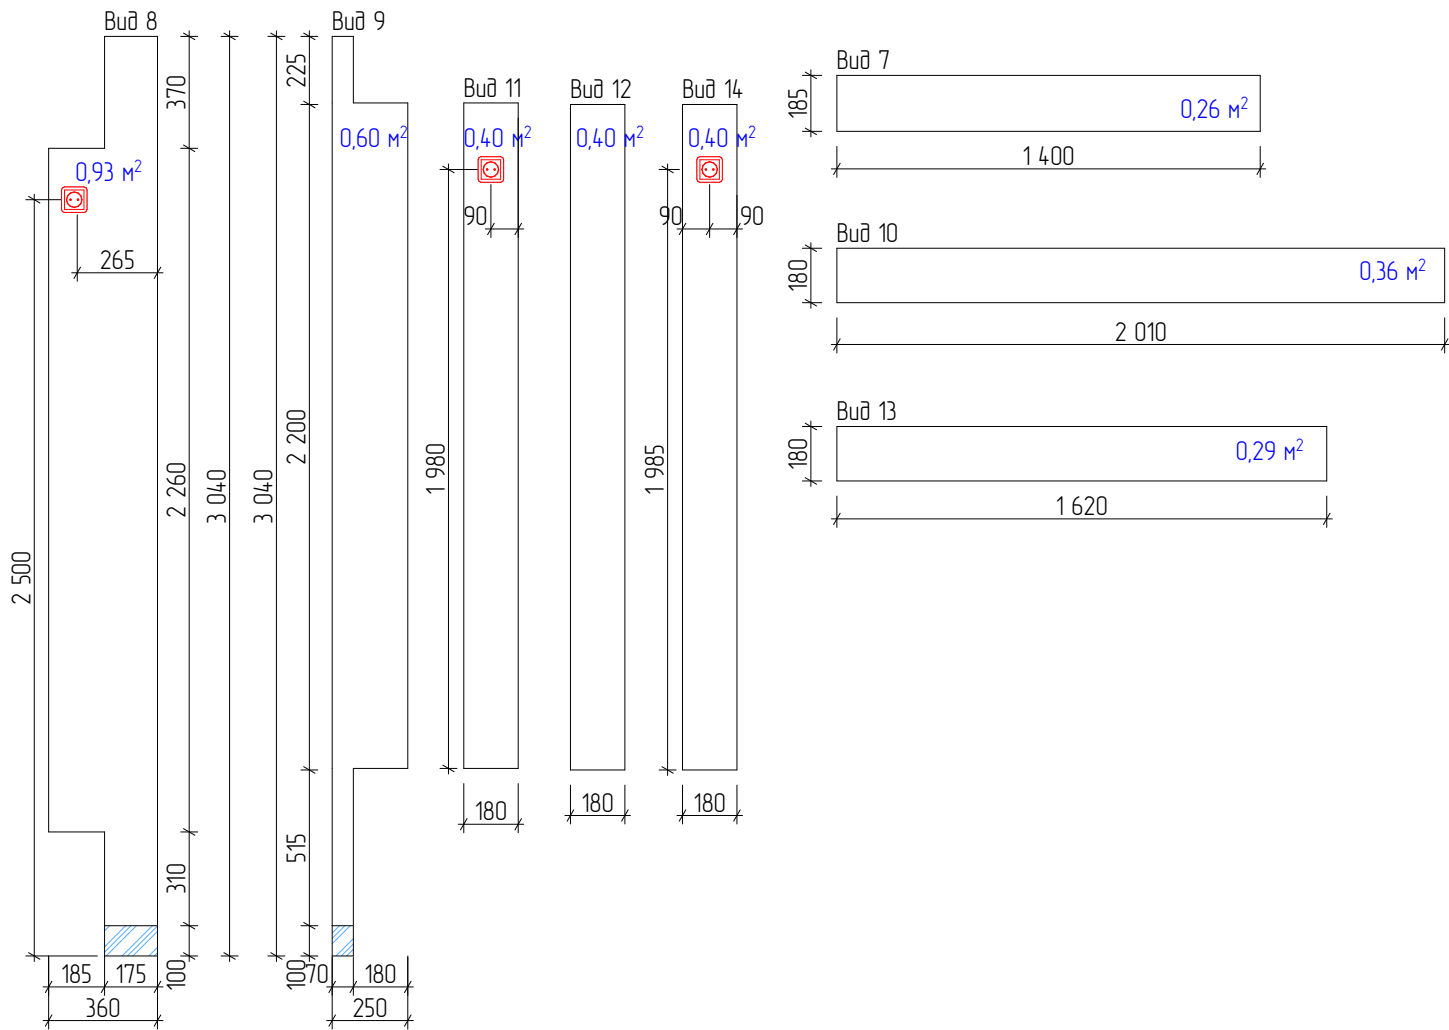

- Примечания:
- * – размеры уточнить по месту после выполнения черновых отделочных работ.
 - Выключатели располагать от уровня чистого пола на высоте 900 мм. Исключения указаны на чертеже.
 - Розетки располагать от уровня чистого пола на высоте 300 мм. Исключения указаны на чертеже.
 - Оконные откосы оклеить строительным флизелином и окрасить в белый цвет. Уточнить по месту.
 - Размещение выводов для отопления согласовать со специалистами.
 - Цвет окрашивания плинтуса уточнить после согласования образца.
 - Резку зеркала решить по месту авторским надзором.
 - Плинтус подрезать по месту в местах стыковки с дверями и мебелью.
 - Внутреннее наполнение мебели разработать со специалистами.
 - Серым/синим цветом показаны размеры мебели. Мебель разработать со специалистами, размеры уточнить после выполнения чистовой отделки.


МСК 392.12.25-ЭП ПРЕМИУМ			
Эскизный дизайн-проект интерьера квартиры в г. Москва ЖК "Остров", ул. Нижние Мневники д. 7			
Прихожая Кухня Гостиная.Развертки стен А-10.			
Дизайнер интерьера Александр Батеньков	Стадия	Лист	Листов
	ЭП	49	120
		Подп.	Дата
ГАП	Батеньков А.С.		
Гл. дизайнер	Власова В.А.		
Гл. проектиров.	Луныкова В.Н.		
Разработал	Ильина Е.Е.		

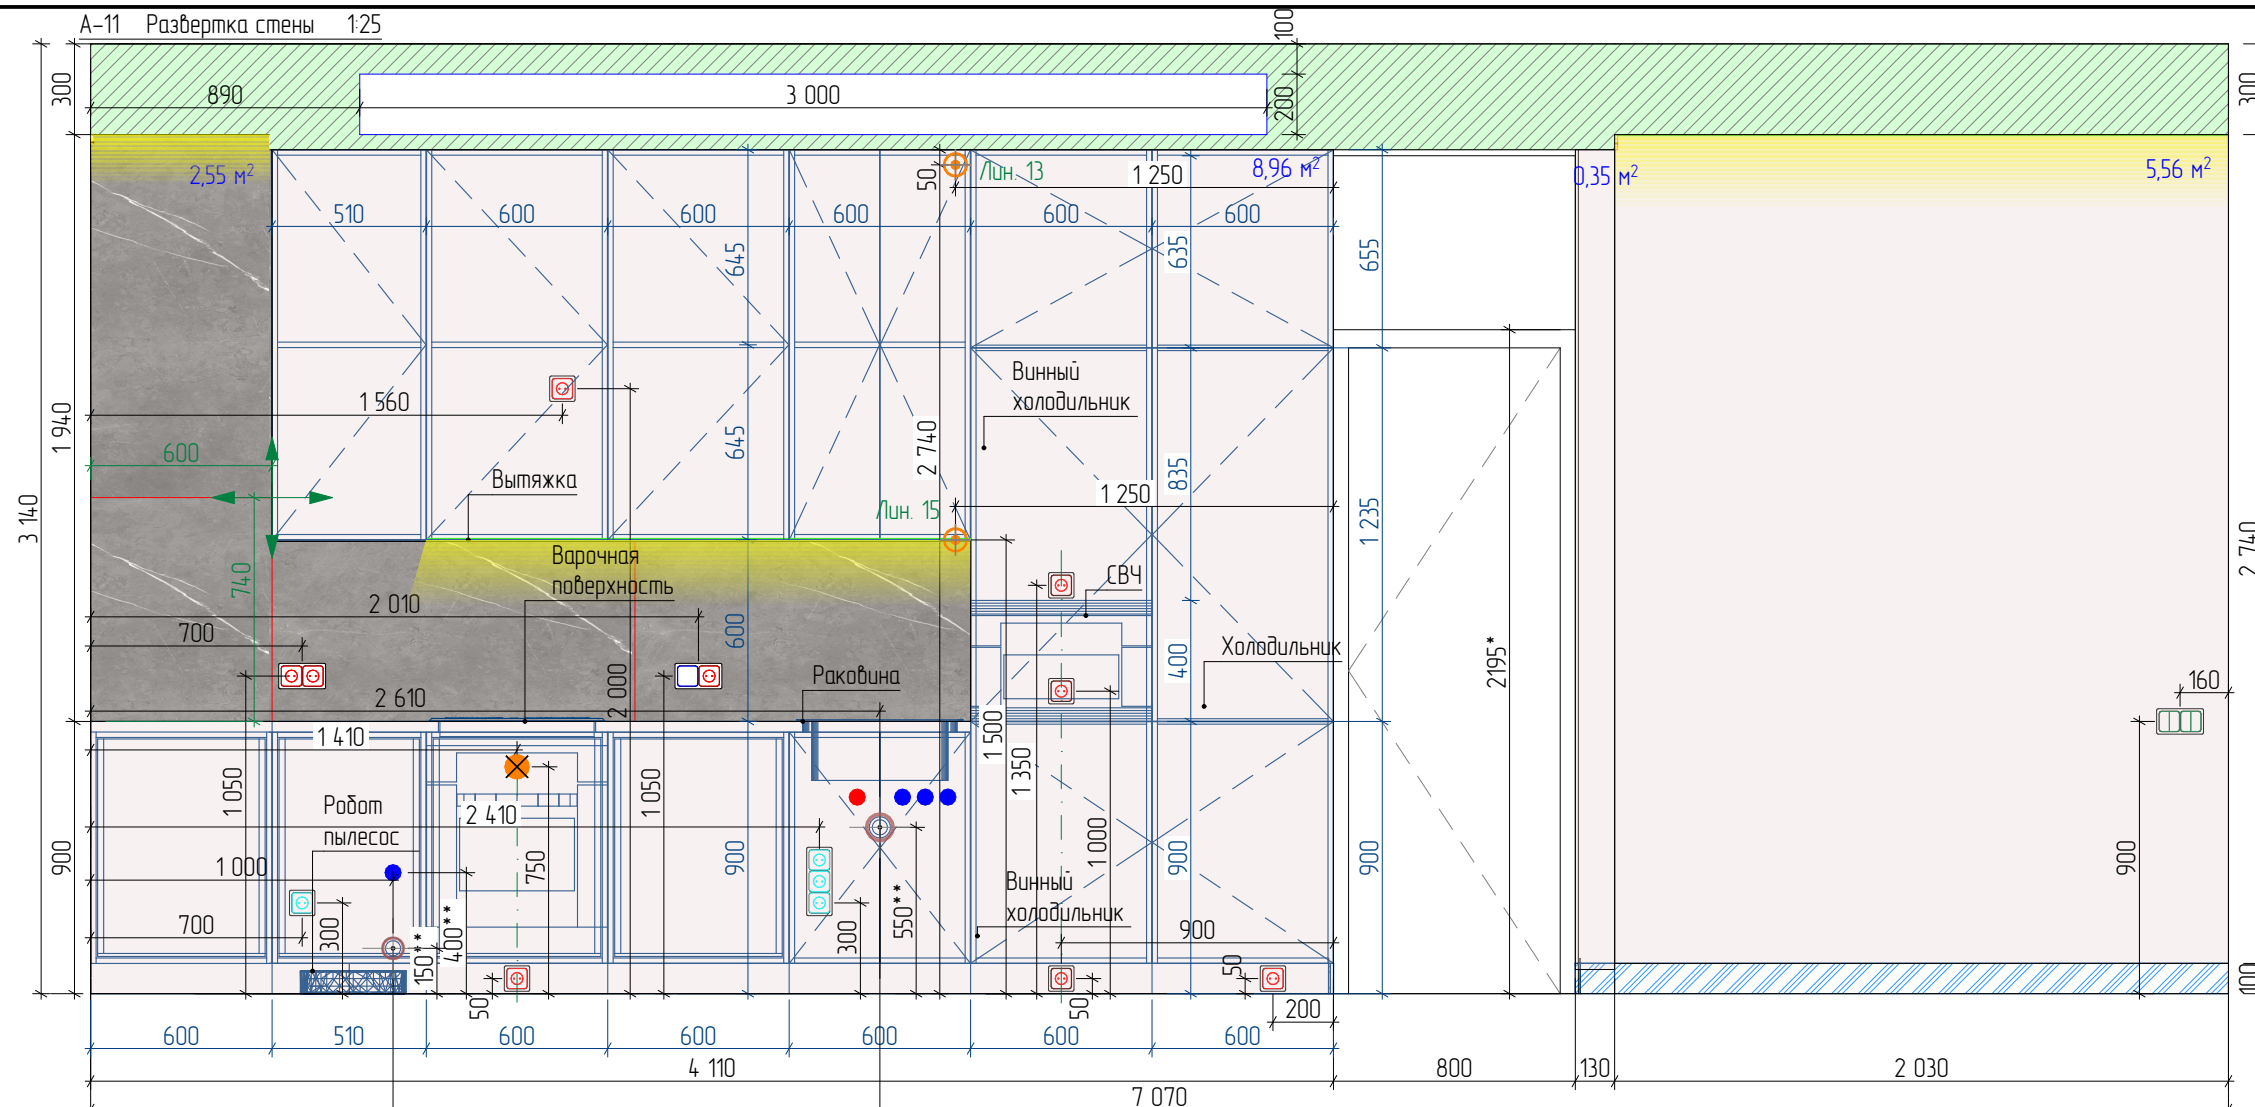

Вывод коммуникаций для робота пылесоса разместить согласно инструкции монтажа выбранной модели, подвести 1 вывод холодной воды и вывод канализации

Вывод коммуникаций для мойки и смесителя разместить согласно инструкции монтажа выбранной модели, подвести 3 вывода холодной воды, при необходимости установить фильтры доочистки воды до питьевого.

А-13 Развертка стены 1:25

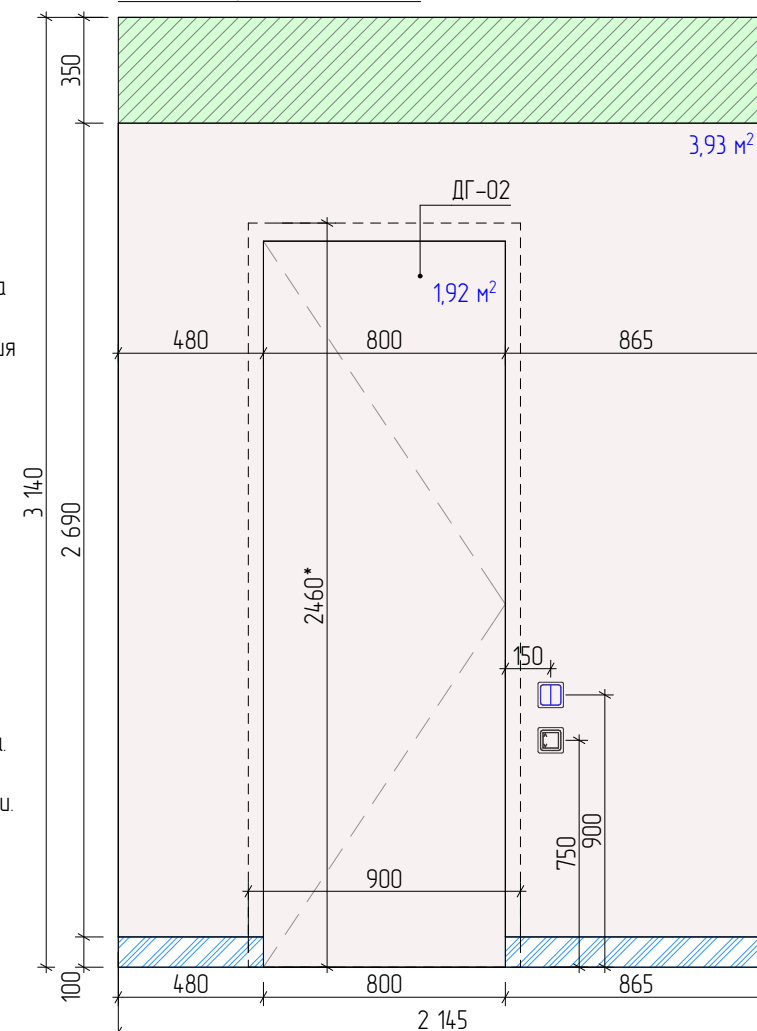


Условные обозначения:

- | | |
|---|--|
|  | Плинтус №1. Плинтус плинтус скрытого монтажа с МДФ вставкой. Теневой зазор от пола 100 мм. Цвет при выборе образца (в цвет стен). |
|  | Монтаж конструкций из ГКВЛ |
|  | Покраска №1. Выполнить по подготовленной поверхности (стеклохолст*). Цвет при выборе образца (бежевый*). |
|  | Керамогранит №01. Керамогранит. Изготовитель: Elegant Grey, кол-я: Forte Dei Marini, размер: 1200x1200 мм, толщину уточнить при закупке. |
|  | Вывод коммуникаций (ХВС, ГВС, канал-ция) |
|  | Вывод электрокабеля или розетка для варочной поверхности |
|  | Вывод электрокабеля для светодиодной ленты |
|  | Розетка 220 V, влагозащищенная IP44 и выше |
|  | Розетка 220 V |
|  | Регулятор теплого пола |
|  | Выключатель одноклавишный |

Примечания:

1. * – размеры уточнить по месту после выполнения черновых отделочных работ.
2. Выключатели располагать от уровня чистого пола на высоте 900 мм. Исключения указаны на чертеже.
3. Регуляторы теплого пола располагать от уровня чистого пола на высоте 750 мм. Исключения указаны на чертеже.
4. Розетки располагать от уровня чистого пола на высоте 300 мм. Исключения указаны на чертеже.
5. Размещение выводов для отопления согласовать со специалистами.
6. Размещение вывода 220 V для кондиционеров согласовать со специалистами.
7. Расположение розеток согласовать с изготовителями кухонного гарнитура. Внести изменения по технологической карте от специалистов.
8. Цвет окрашивания плитуса уточнить после согласования образца.
9. Размеры и конструкцию фартука для кухонного гарнитура уточнить после выбора и детальной проработке кухонного гарнитура, согласовать со специалистами.
10. Точную привязку выводов коммуникаций решить после выбора оборудования по инструкции монтажа.
11. Расположение розеток и выключателей согласовать с изготовителями кухонного гарнитура.
12. ** – размер уточнить по инструкции монтажа оборудования.
13. Розетки, выключатели, регуляторы теплого пола размещать по центру керамической плитки.
14. Высоту проемов выполнить 2460 мм от уровня чистого пола. Уточнить после подбора и согласования модели дверей.
15. Плитус подрезать по месту в местах стыковки с дверями и мебелью.
16. Внутреннее наполнение мебели разработать со специалистами.
17. Серым/синим цветом показаны размеры мебели. Мебель разработать со специалистами, размеры уточнить после выполнения чистовой отделки.

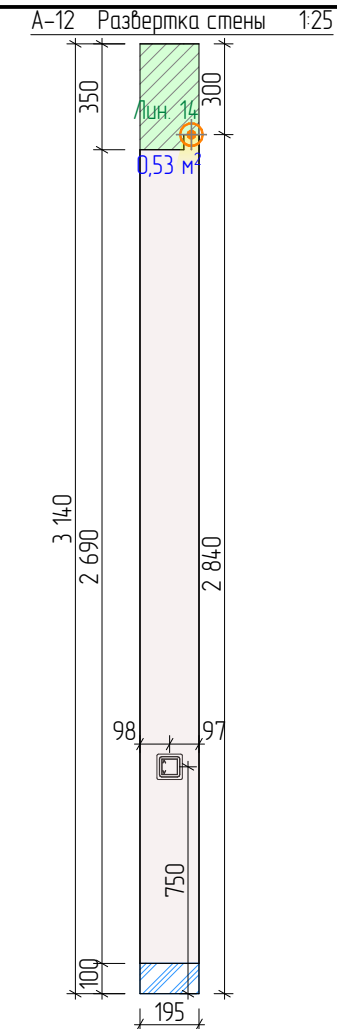

- Выключатель двухклавишный
- Переключатель двухклавишный
- Направление и начало укладки


МСК 392.12.25-ЭП ПРЕМИУМ			
Эскизный дизайн-проект интерьера квартиры в г. Москва ЖК "Остров", ул. Нижние Мневники д. 7			
Прихожая Кухня Гостиная Развертки стен А-11, А-12, А-13.			
Дизайнер интерьера №1  Александр Батеньков	Стадия	Лист	Листов
	ЭП	50	120
		Подп.	Дата
ГАП	Батеньков А.С.		
Гл. дизайнер	Власова В.А.		
Гл. проектиров.	Лунькова В.Н.		
Разработал	Ильина Е.Е.		

Ведомость отделочных материалов.

№	Обозначение	Наименование	Кол-во	Примечание
Пол:				
1		Пробковый компенсатор	10,01	м.п.
2		Покрытие №01. Паркет. Изготовитель: Lab Arte, кол-я: Angle Дуб Натур, размер: 500x150 мм, точный артикул и производителя уточнить при выборе образца, толщину уточнить при закупе.	34,14	м²
3		Покрытие №02. Керамогранит. Изготовитель: Elegant Grey, кол-я: Forte Dei Marini, размер: 1200x1200 мм, толщину уточнить при закупе.	20,50 19	м² укладки шт.
Стены:				
4		Плинтус №1. Теневой плинтус скрытого монтажа с МДФ вставкой. Теневой зазор от пола 100 мм. Цвет при выборе образца (в цвет стен).	21,36	м.п.
5		Покраска №1. Выполнить по подготовленной поверхности (стеклохолст*). Цвет при выборе образца (бежевый*).	57,08	м²
6		МДФ панель №1. Шпонированная. Цвет и фактура при выборе образца (орех*).	11,96	м²
7		МДФ панель №2. Цвет и фактура при выборе образца (темный мрамор*).	2,79	м²
8		МДФ панель №3. 3Д панель. Цвет и фактура при выборе образца (в цвет мебели*).	2,04	м²
9		МДФ панель №4. Цвет и фактура при выборе образца (ржавый металл*).	7,28	м²
10		Керамогранит №01. Керамогранит. Изготовитель: Elegant Grey, кол-я: Forte Dei Marini, размер: 1200x1200 мм, толщину уточнить при закупе.	2,55 2	м² укладки шт.
11		Зеркало №1. Разработать со специалистами (тонированное*) размеры и резка по чертежу.	4,14	м²
Откосы:				
12		Покраска №2. Выполнить по подготовленной поверхности. Цвет при выборе образца (белый*).	4,54	м²
Подоконник:				
13		Подоконник №1. Искусственный камень. Цвет при выборе образца.	2,35	м²

МСК 392.12.25–ЭП ПРЕМИУМ			
Эскизный дизайн–проект интерьера квартиры в г. Москва ЖК “Остров”, ул. Нижние Мневники д. 7			
Прихожая Кухня Гостиная.Ведомость отделочных материалов			
Дизайнер интерьера  №1 Александр Батеньков	Стадия	Лист	Листов
	ЭП	51	120
		Подп.	Дата
ГАП	Батеньков А.С.		
Гл. дизайнер	Власова В.А.		
Гл. проектиров.	Луцькова В.Н.		
Разработал	Ильина Е.Е.		

План отделки пола:

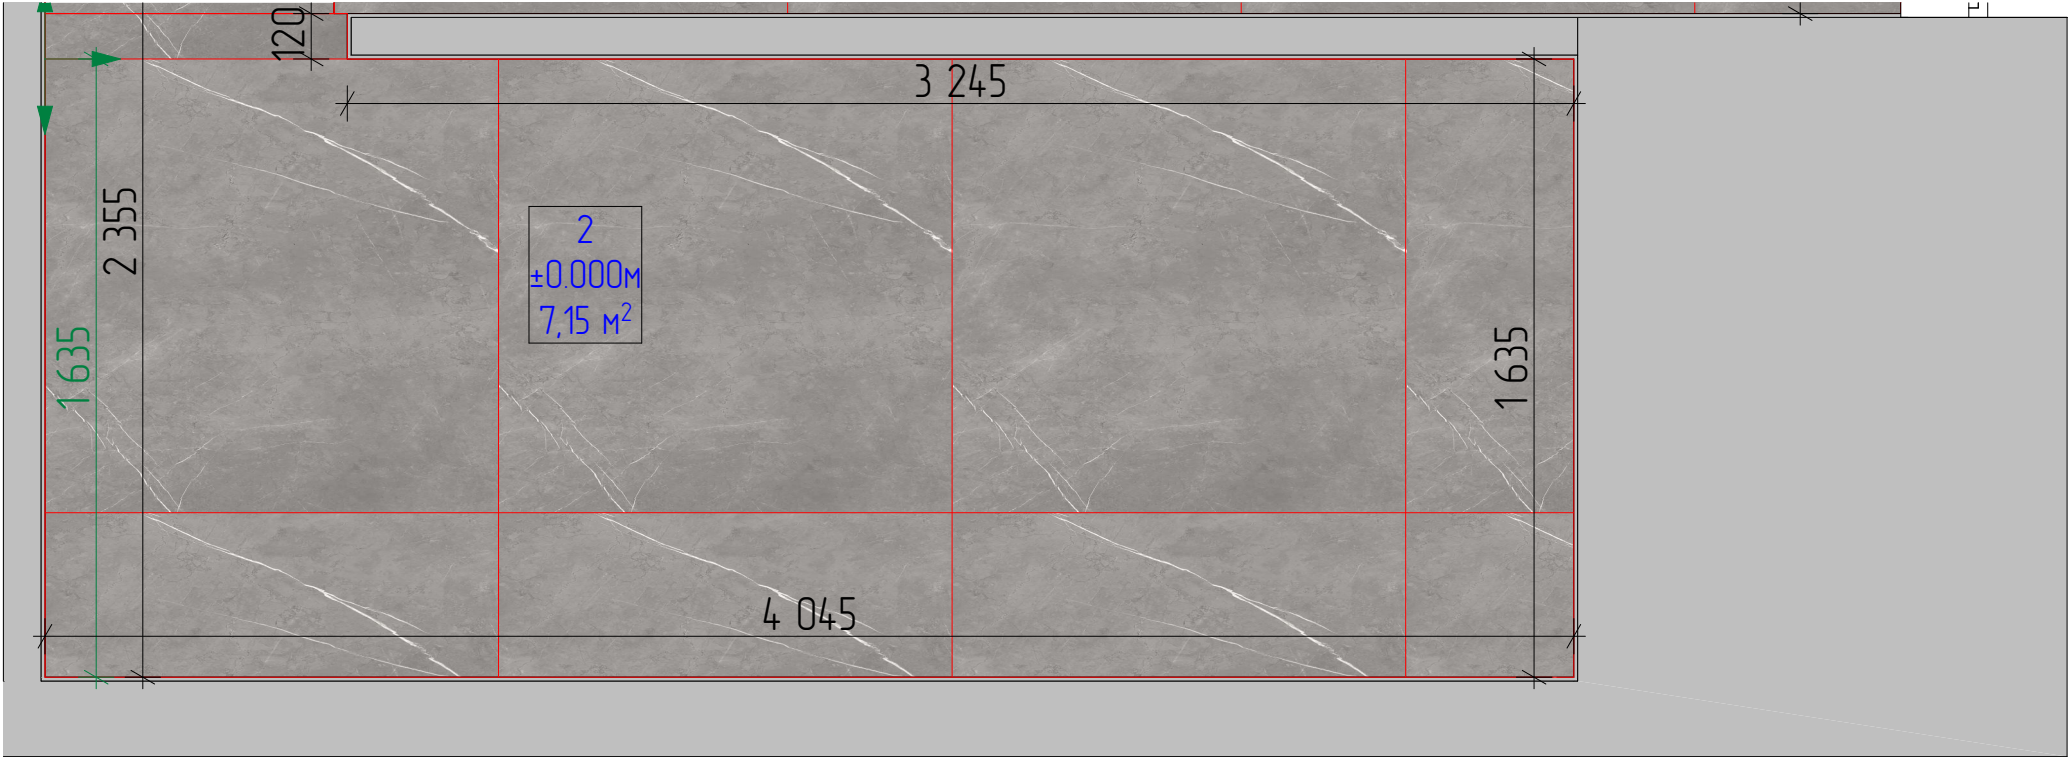


Условные обозначения:

- Направление и начало укладки
- Покрытие №02. Керамогранит. Изготовитель: Elegant Grey, кол-я: Forte Dei Mariti, размер: 1200x1200 мм, толщину уточнить при заказе.
- Светильник точечный встраиваемый
- Диффузор, вытяжка

Примечания:

- * – размеры уточнить по месту после выполнения черновых отделочных работ.
- За отметку ±0,000 принят уровень чистого пола.
- Во влажных помещениях предусмотреть гидроизоляцию пола с заведением на стены на 150 мм.
- При монтаже напольных покрытий уточнить необходимость устройства дверных проемов с порогом.
- * – размеры уточнить по месту после выполнения черновых отделочных работ и установки дверей со скрытой коробкой.
- ** – размер уточнить по месту в зависимости от точного расположения полотна двери, стыковка двух разных напольных покрытий должна проходить точно по центру вдоль дверного полотна.
- Выполнить уровень потолка из влагостойкого ГКЛ для предотвращения деформации потолка при затоплении.
- Высоту уровней потолка отсчитывать от существующей ж/д плиты перекрытия помещения.
- От вытяжки провести вентиляционный короб до общедомового канала в конструкции потолка, уточнить по месту со специалистами и заказчиком.
- Шумоизоляцию разработать со специалистами, уточнить состав и толщину слоев шумоизоляционных материалов. Уточнить необходимость устройства с заказчиком.


План отделки потолка:

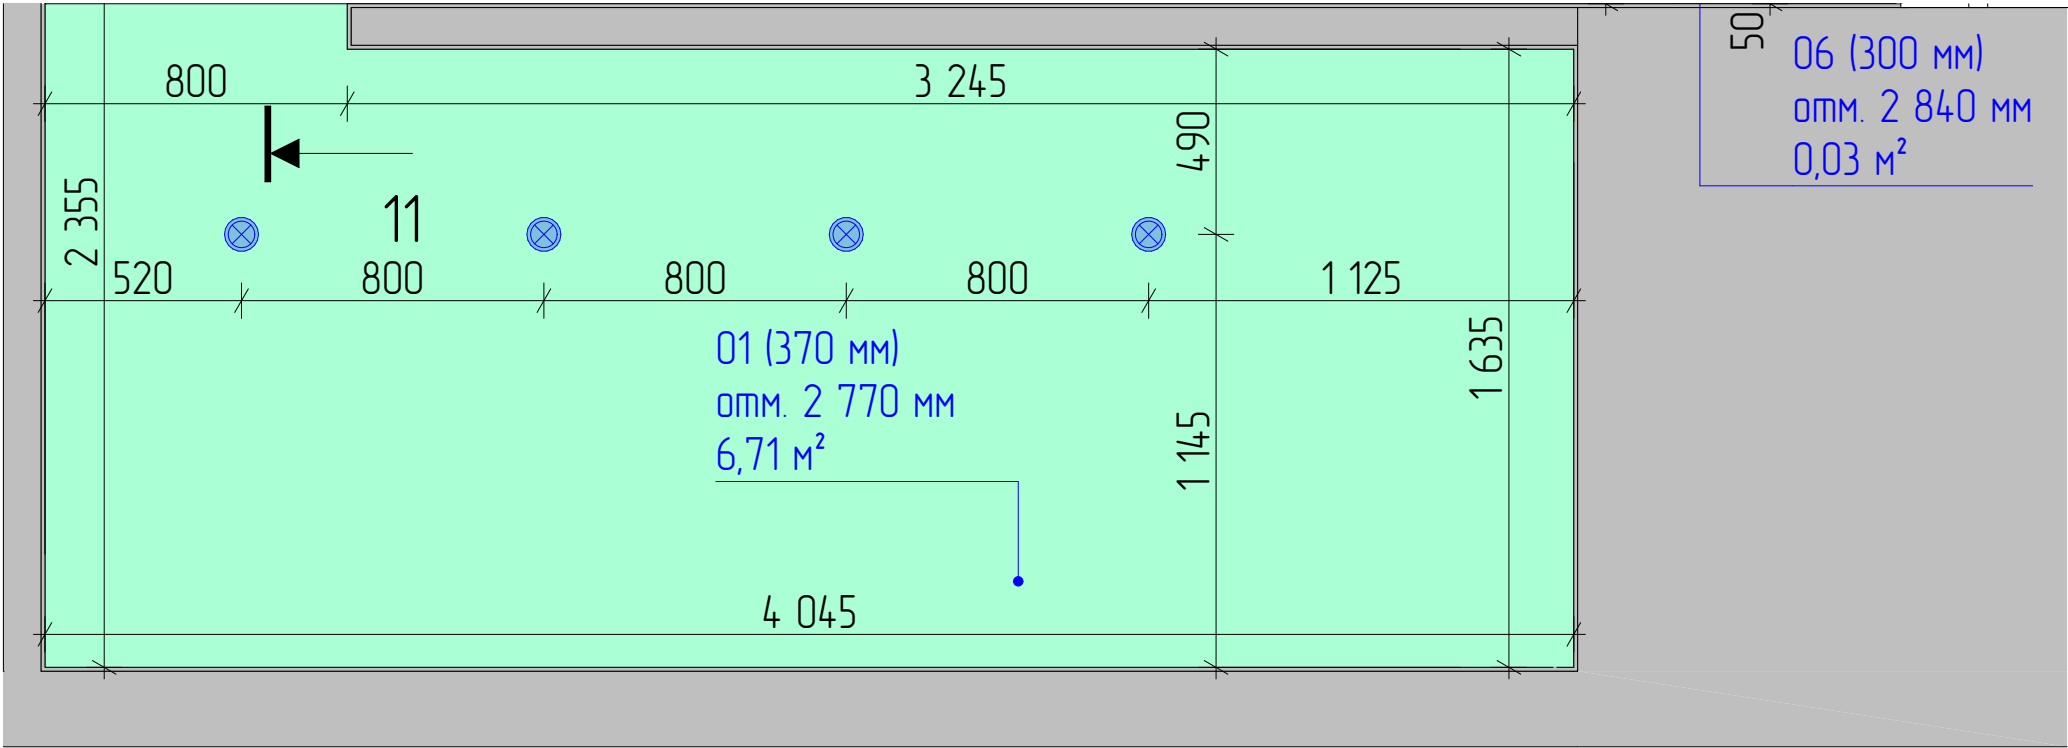


Условные потолки				
№	Обозначение	Опуск	Примечания	Площадь м2
01		370	Потолок ГКЛ/В. Окрасить в цвет выбранного образца (белый) по армирующему материалу (стеклохолст "паутинка").	6,71

МСК 392.12.25-ЭП ПРЕМИУМ			
Эскизный дизайн-проект интерьера квартиры в г. Москва ЖК "Остров", ул. Нижние Мневники д. 7			
Кладовая.План отделки пола. План отделки потолка.			
Дизайнер интерьера №1  Александр Батеньков	Стадия	Лист	Листов
	ЭП	52	120
		Подп.	Дата
ГАП	Батеньков А.С.		
Гл. дизайнер	Власова В.А.		
Гл. проектиров.	Луцькова В.Н.		
Разработал	Ильина Е.Е.		

План электрооборудования:

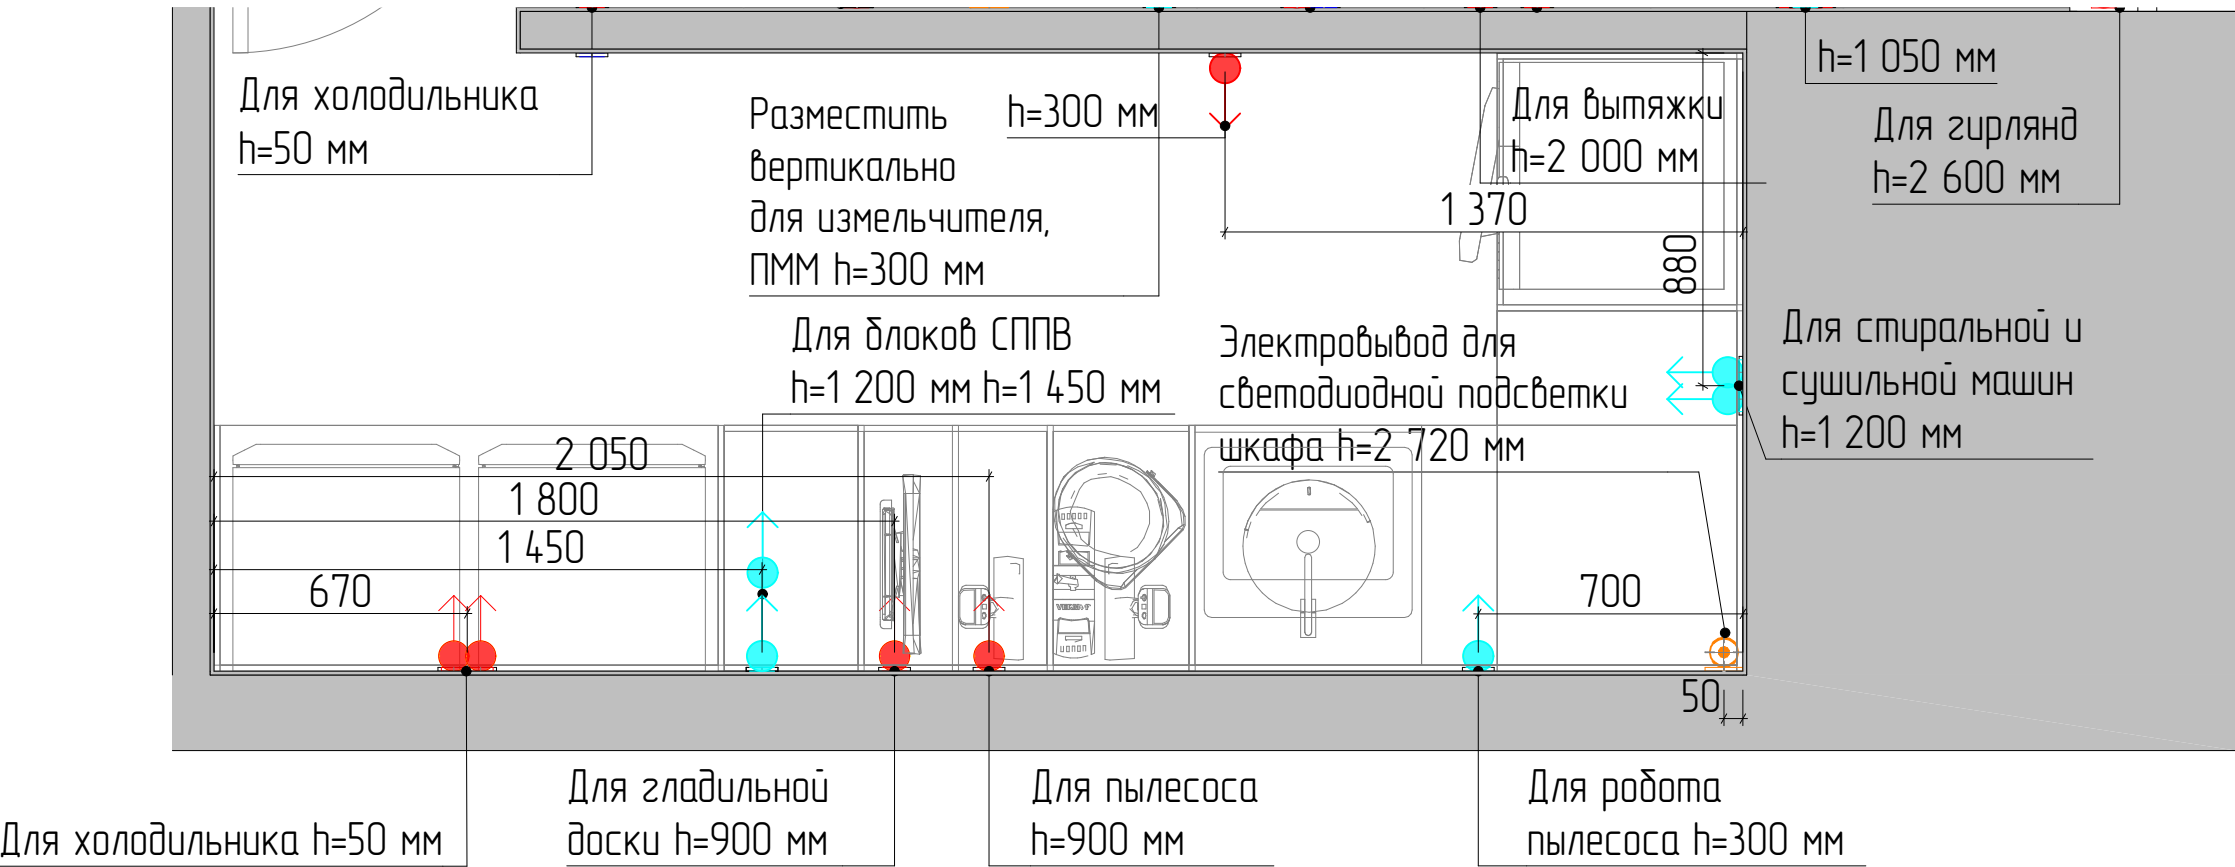

План размещения освещения и выключателей:

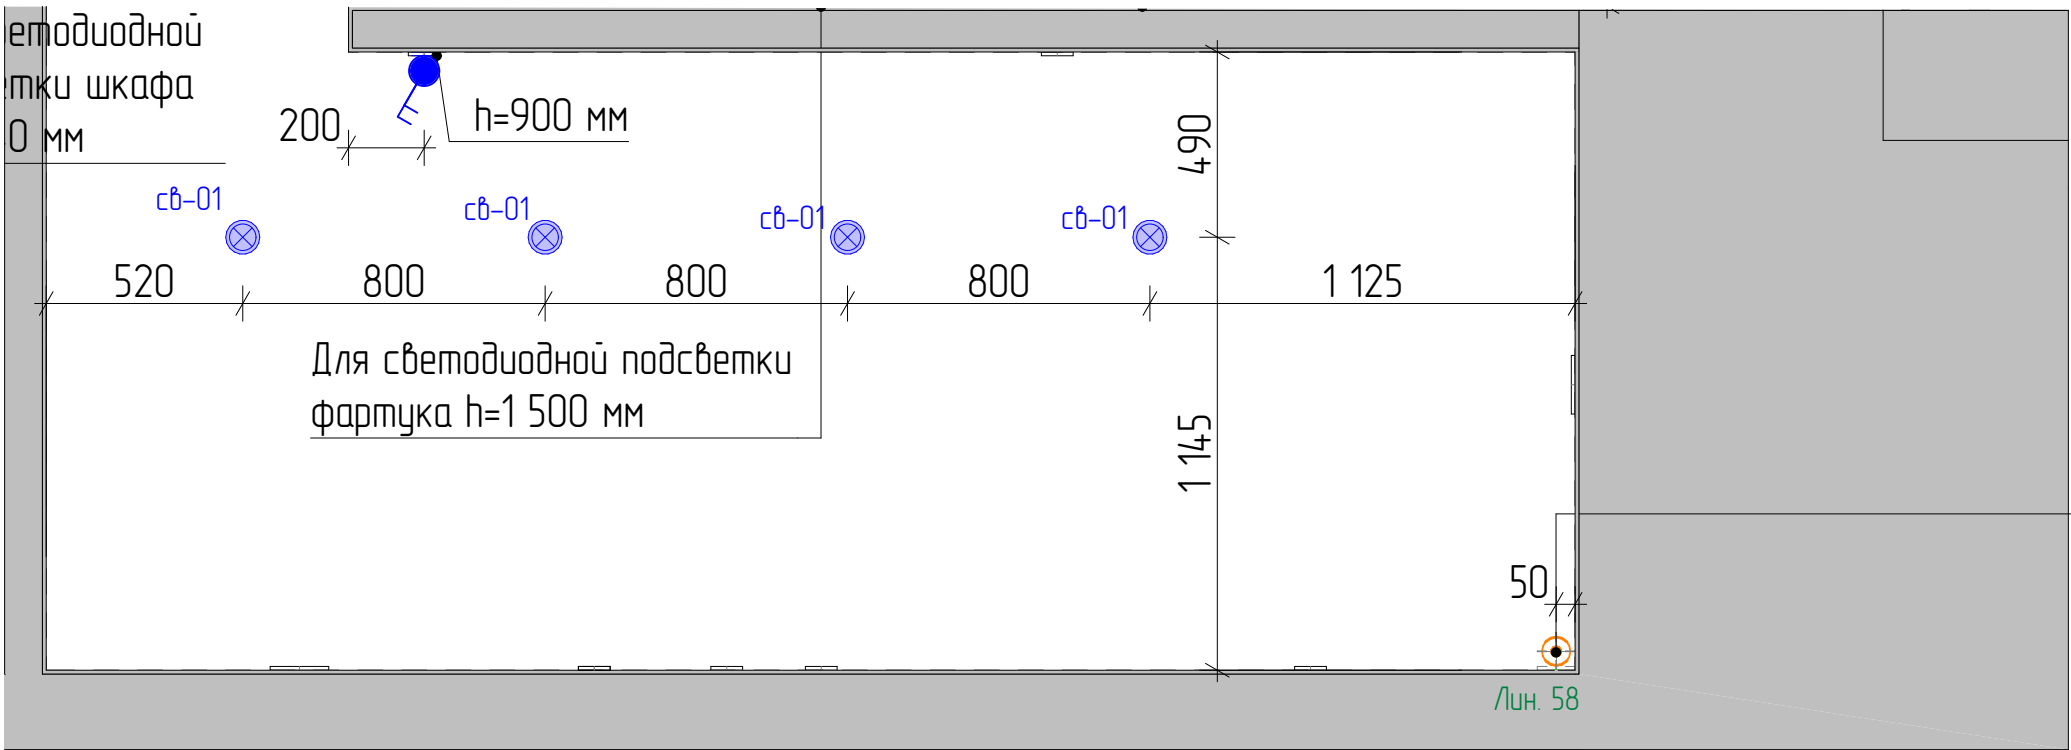

Примечания:

- * – размеры уточнить по месту.
- Розетки располагать от уровня чистого пола на высоте 0,300 м. Исключения указаны на чертеже.
- Размещение всех выводов и розеток согласовать со специалистами «Умный дом».
- Датчики пожарной и охранной сигнализации и электропроводы для них разместить совместно со специалистами, предварительно вызвав их на объект.
- Размещение розеток и электропроводов по высоте см. на развертках стен.


- Выключатели располагать от уровня чистого пола на высоте 0,900 м. Исключения указаны на чертеже.
- Светильники, встроенные в мебель, согласовать с изготовителями мебели.

- Условные обозначения:
- Розетка 220V влагозащищенная
 - Розетка 220V
 - Вывод электрокабеля для варочной поверхности
 - Диффузор, вытяжка
 - Светильник точечный встраиваемый
 - Выключатель двухклавишный

Для светодиодной подсветки шкафа h=2 720 мм

МСК 392.12.25-ЭП ПРЕМИУМ			
Эскизный дизайн-проект интерьера квартиры в г. Москва ЖК "Остров", ул. Нижние Мневники д. 7			
Кладовая.План размещения электрооборудования. План размещения освещения и выключателей.			
Дизайнер интерьера №1 Александр Батеньков	Стадия	Лист	Листов
	ЭП	53	120
		Подп.	Дата
ГАП	Батеньков А.С.		
Гл. дизайнер	Власова В.А.		
Гл. проектиров.	Луныкова В.Н.		
Разработал	Ильина Е.Е.		


Б-01 Развертка стены 1:25

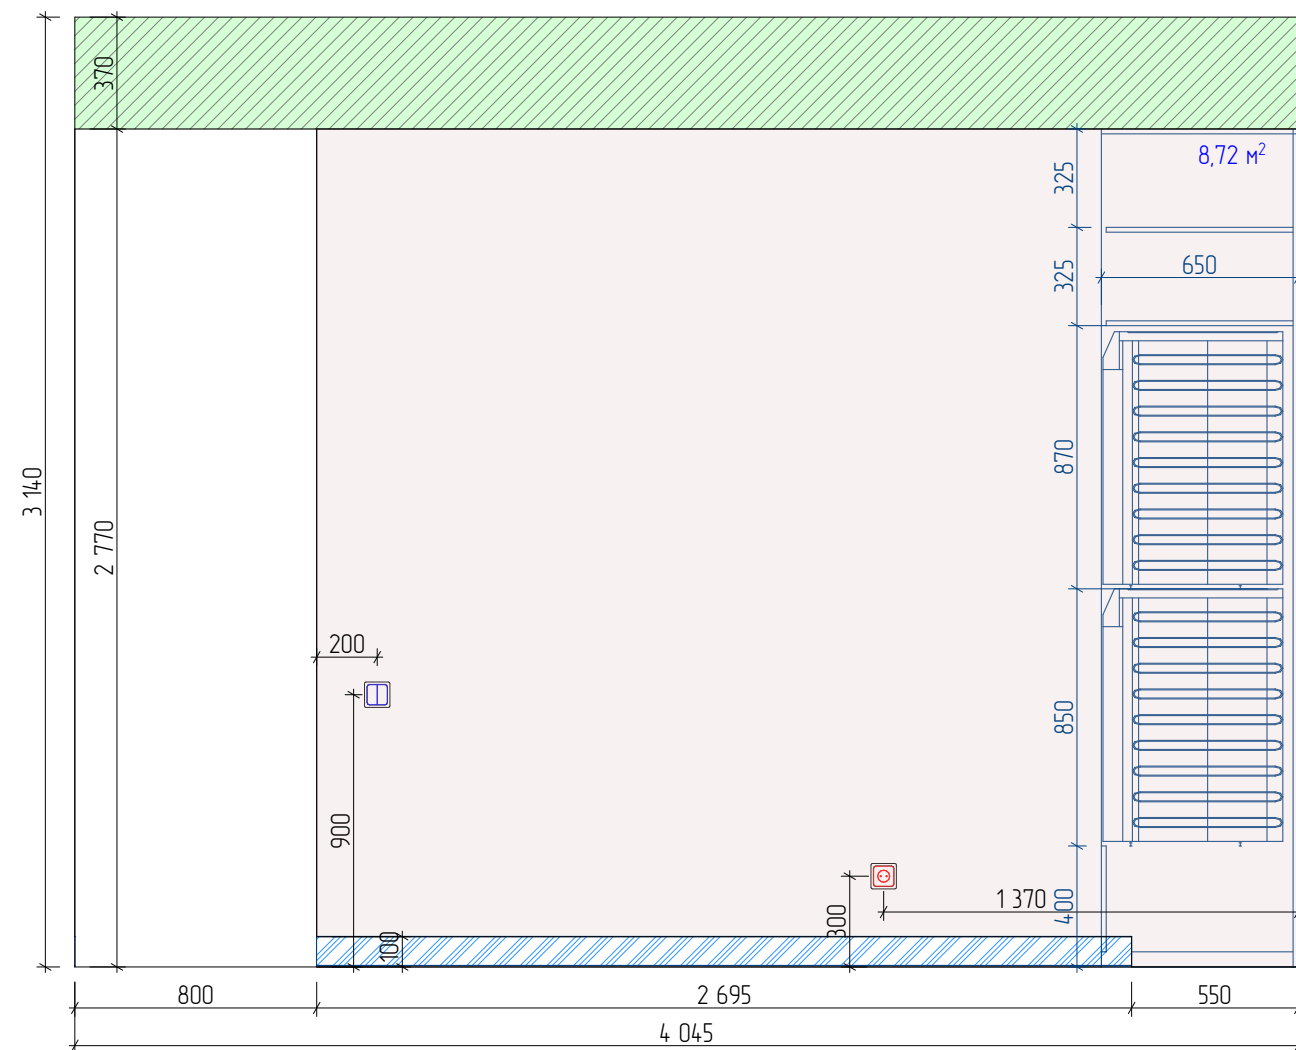

Условные обозначения:

-  Плинтус №1. Плинтус плинтус скрытого монтажа с МДФ вставкой. Теневой зазор от пола 100 мм. Цвет при выборе образца (в цвет стен).
-  Монтаж конструкций из ГКВЛ
-  Покраска №1. Выполнить по подготовленной поверхности (стеклохолст*). Цвет при выборе образца (бежевый*).
-  Розетка 220 V, влагозащитенная IP44 и выше
-  Розетка 220 V
-  Выключатель двухклавишный
-  Вывод коммуникаций (ХВС, ГВС, канал-ция)

Б-02 Развертка стены 1:25


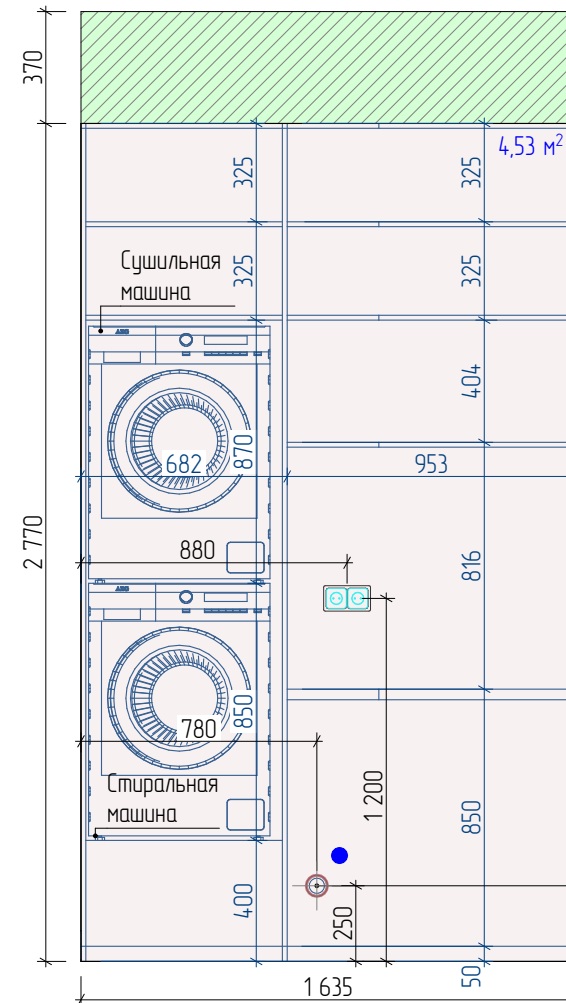


Вывод коммуникации для стиральной и сушильной машин разместить согласно инструкции монтажа выбранной модели

Примечания:

1. * – размеры уточнить по месту после выполнения черновых отделочных работ.
2. Выключатели располагать от уровня чистого пола на высоте 900 мм. Исключения указаны на чертеже.
3. Розетки располагать от уровня чистого пола на высоте 300 мм. Исключения указаны на чертеже.
4. Цвет окрашивания плитуса уточнить после согласования образца.
5. Точную привязку выводов коммуникаций решить после выбора оборудования по инструкции монтажа.
6. Предусмотреть гидроизоляцию пола с заведением на стену (150 мм).
7. ** – размер уточнить по инструкции монтажа оборудования.
8. Внутреннее наполнение мебели разработать со специалистами.
9. Серым/синим цветом показаны размеры мебели. Мебель разработать со специалистами, размеры уточнить после выполнения чистовой отделки.

МСК 392.12.25-ЭП ПРЕМИУМ			
Эскизный дизайн-проект интерьера кбартуры в г. Москва ЖК "Остроб", ул. Нижние Мневники д. 7			
Кладовая.Развертки стен Б-01, Б-02.			
Дизайнер интерьера  №1 Александр Батеньков	Стадия	Лист	Листов
	ЭП	54	120
		Подп.	Дата
ГАП	Батеньков А.С.		
Гл. дизайнер	Власова В.А.		
Гл. проектиров.	Луныкова В.Н.		
Разработал	Ильина Е.Е.		

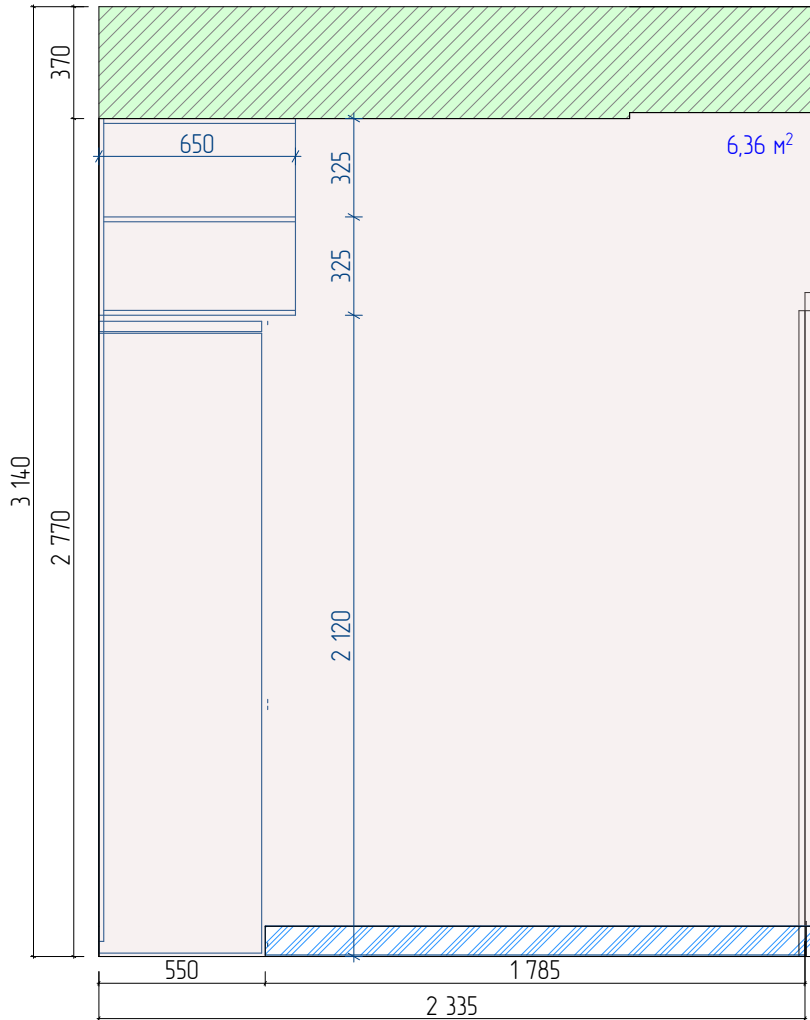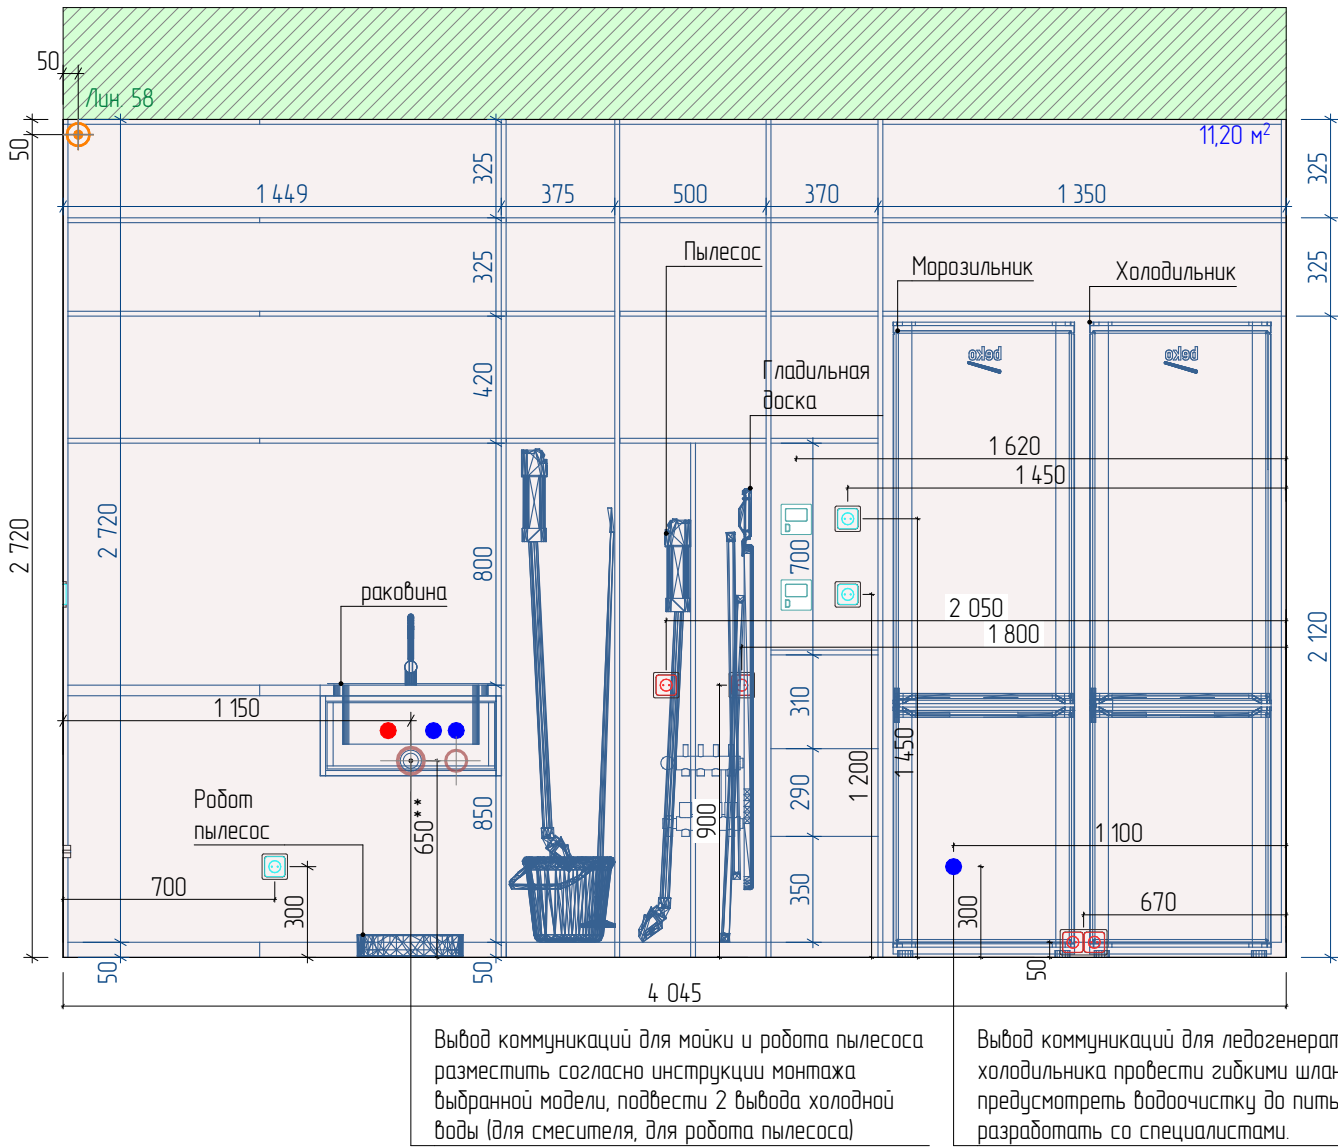

Ведомость отделочных материалов.

№	Обозначение	Наименование	Кол-во	Примечание
Пол:				
1		Покрывтие №02. Керамогранит. Изготовитель: Elegant Grey, кол-я: Forte Dei Mariti, размер: 1200x1200 мм, толщину уточнить при заказе.	7,15 6	м ² укладки шт.
Стены:				
2		Плинтус №1. Теневой плинтус скрытого монтажа с МДФ вставкой. Теневой зазор от пола 100 мм. Цвет при выборе образца (в цвет стен).	4,48	м.п.
3		Покраска №1. Выполнить по подготовленной поверхности (стеклохолст*). Цвет при выборе образца (бежевый*).	30,81	м ²

Условные обозначения:

- Плинтус №1. Теневой плинтус скрытого монтажа с МДФ вставкой. Теневой зазор от пола 100 мм. Цвет при выборе образца (в цвет стен).
- Монтаж конструкций из ГКВЛ
- Покраска №1. Выполнить по подготовленной поверхности (стеклохолст*). Цвет при выборе образца (бежевый*).
- Вывод электрокабеля для светодиодной ленты
- Розетка 220 V, влагозащищенная IP44 и выше
- Розетка 220 V
- Вывод коммуникаций (ХВС, ГВС, канал-ция)

Примечания:

- * – размеры уточнить по месту после выполнения черновых отделочных работ.
- Выключатели располагать от уровня чистого пола на высоте 900 мм. Исключения указаны на чертеже.
- Розетки располагать от уровня чистого пола на высоте 300 мм. Исключения указаны на чертеже.
- Цвет окрашивания плинтуса уточнить после согласования образца.
- Точную привязку выводов коммуникаций решить после выбора оборудования по инструкции монтажа.
- Предусмотреть гидроизоляцию пола с заведением на стену (150 мм).
- ** – размер уточнить по инструкции монтажа оборудования.
- Внутреннее наполнение мебели разработать со специалистами.
- Серым/синим цветом показаны размеры мебели. Мебель разработать со специалистами, размеры уточнить после выполнения чистовой отделки.


МСК 392.12.25–ЭП ПРЕМИУМ

Эскизный дизайн-проект интерьера квартиры в г. Москва ЖК "Остров", ул. Нижние Мневники д. 7


Кладовая.Развертки стен Б-03, Б-04. Ведомость отделочных материалов.

 Дизайнер интерьера №1 Александр Батеньков	Стадия	Лист	Листов
	ЭП	55	120
		Подп.	Дата
ГАП	Батеньков А.С.		
Гл. дизайнер	Власова В.А.		
Гл. проектиров.	Луныкова В.Н.		
Разработал	Ильина Е.Е.		


План отделки пола:

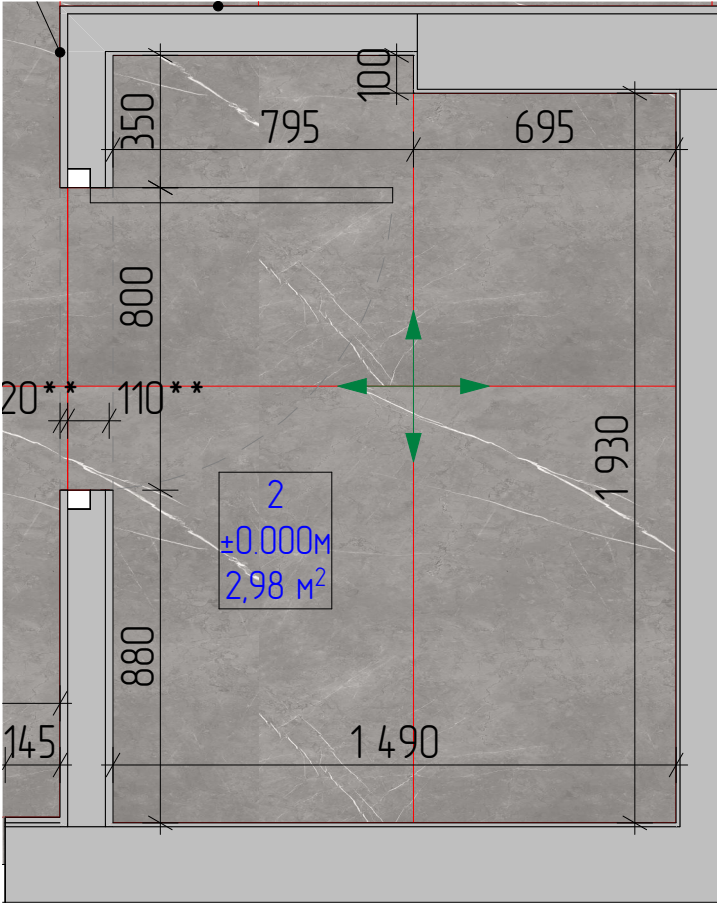

План отделки потолка:

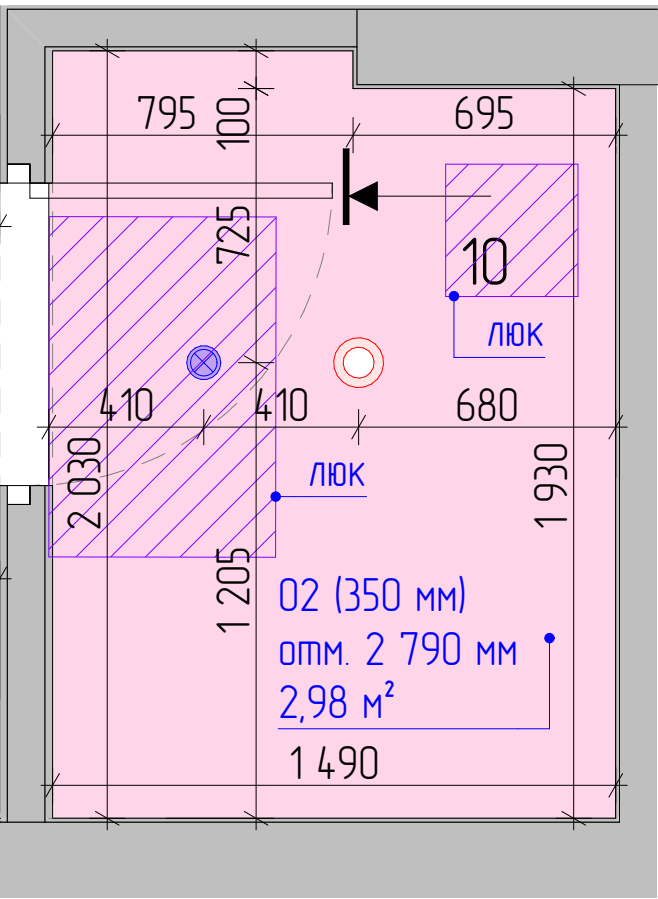


План электрооборудования:

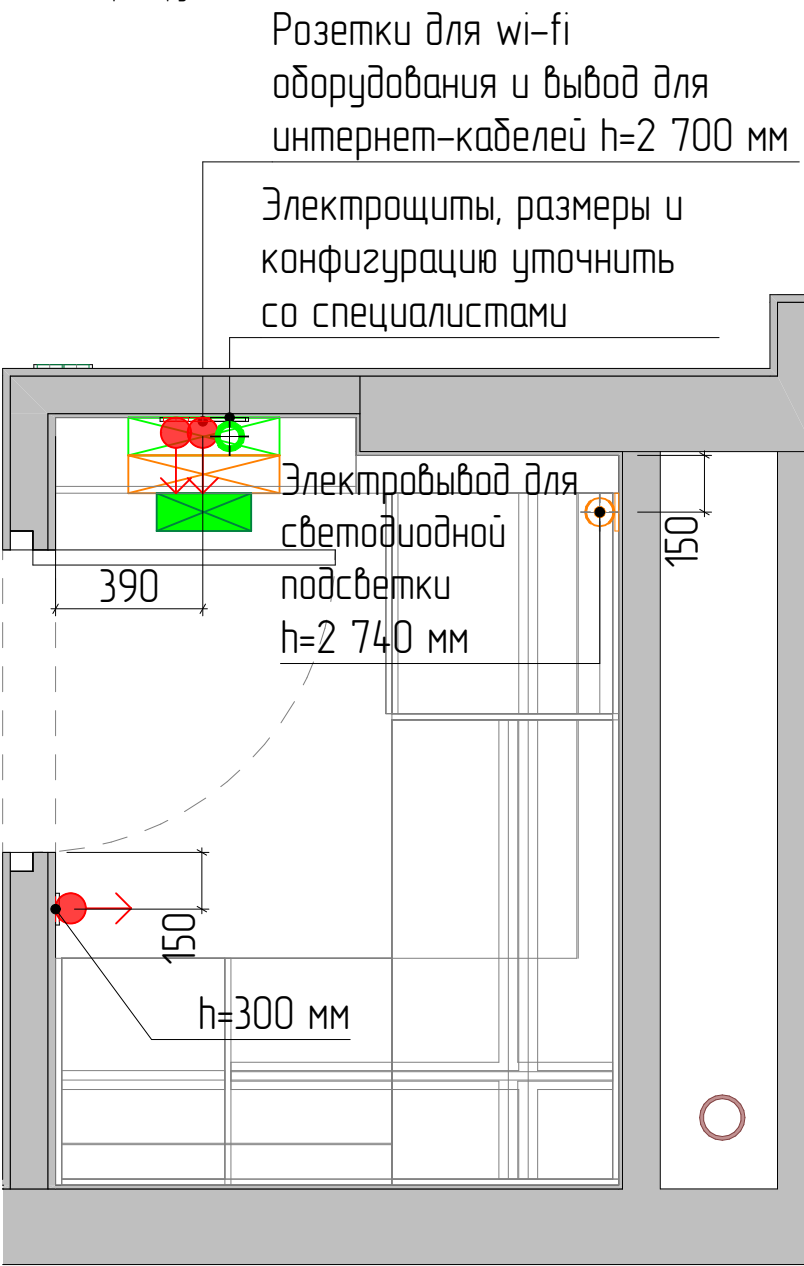

Примечания:

- *- размеры уточнить по месту после выполнения черновых отделочных работ.
- За отметку $\pm 0,000$ принят уровень чистого пола.
- При монтаже напольных покрытий уточнить необходимость устройства дверных проемов с порогом.
- *- размеры уточнить по месту после выполнения черновых отделочных работ и установки дверей со скрытой коробкой.
- **-размер уточнить по месту в зависимости от точного расположения полотна двери, стыковка двух разных напольных покрытий должна проходить точно по центру вдоль дверного полотна.
- Выполнить уровни потолка из влагостойкого ГКЛ для предотвращения деформации потолка при затоплении.
- Высоту уровней потолка отсчитывать от существующей ж/б плиты перекрытия помещения.
- От вытяжки провести вентиляционный короб до общедомового канала в конструкции потолка, уточнить по месту со специалистами и заказчиком.
- Шумоизоляцию разработать со специалистами, уточнить состав и толщину слоев шумоизоляционных материалов. Уточнить необходимость устройства с заказчиком.
- Розетки располагать от уровня чистого пола на высоте 0,300 м. Исключения указаны на чертеже.
- Размещение и габаритные размеры электрощита согласовать со специалистами.
- К WI-FI оборудованию подвести 5 выводов интернет-кабеля из расчета: общее количество интернет выводов + розеток + один (вывод в квартиру из подъезда). Размещение wi-fi оборудования и усилителей для него определить по месту, вызвав предварительно на объект специалистов.
- Размещение всех выводов и розеток согласовать со специалистами «Умный дом».
- Датчики пожарной и охранной сигнализации и электровыводы для них разместить совместно со специалистами, предварительно вызвав их на объект.
- Размещение розеток и электровыводов по высоте см. на развертках стен.
- Светильники, встроенные в мебель, согласовать с изготовителями мебели.

План размещения освещения и выключателей:

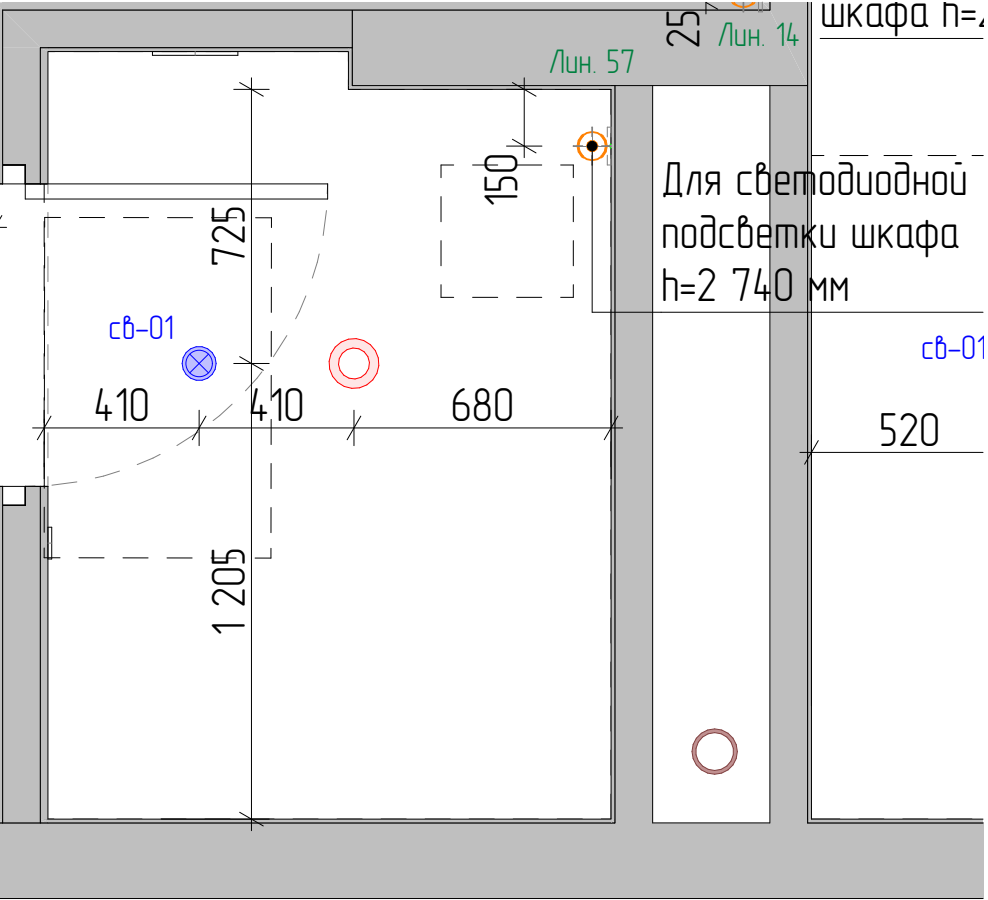

Условные обозначения:

- Условные обозначения:
- Направление и начало укладки
 - Покрывтие №02. Керамогранит. Изготовитель: Elegant Grey, кол-я: Forte Dei Marmi, размер: 1200x1200 мм, толщину уточнить при заказе.
 - Светильник точечный встраиваемый
 - Вывод электрокабеля для светодиодной ленты
 - Люк доступа
 - Розетка 220V
 - Вывод 220V
 - Wifi- оборудование
 - Электрощит
 - Слаботочный щит
 - Диффузор, вытяжка

Условные потолки				
№	Обозначение	Опуск	Примечания	Площадь м2
02		350	Потолок ГК/В. Окрасить в цвет выбранного образца (белый) по армирующему материалу (стеклохолст "паутинка").	2,98

МСК 392.12.25-ЭП ПРЕМИУМ





Эскизный дизайн-проект интерьера квартиры в г. Москва ЖК "Остров", ул. Нижние Мневники д. 7

Гардеробная №1. План отделки пола. План отделки потолка. План размещения электрооборудования. План размещения освещения и выключателей.

Дизайнер интерьера №1
Александр Батеньков

Стадия	Лист	Листов
ЭП	56	120
	Подп.	Дата

ГАП	Батеньков А.С.		
Гл. дизайнер	Власова В.А.		
Гл. проектиров.	Луныкова В.Н.		
Разработал	Ильина Е.Е.		

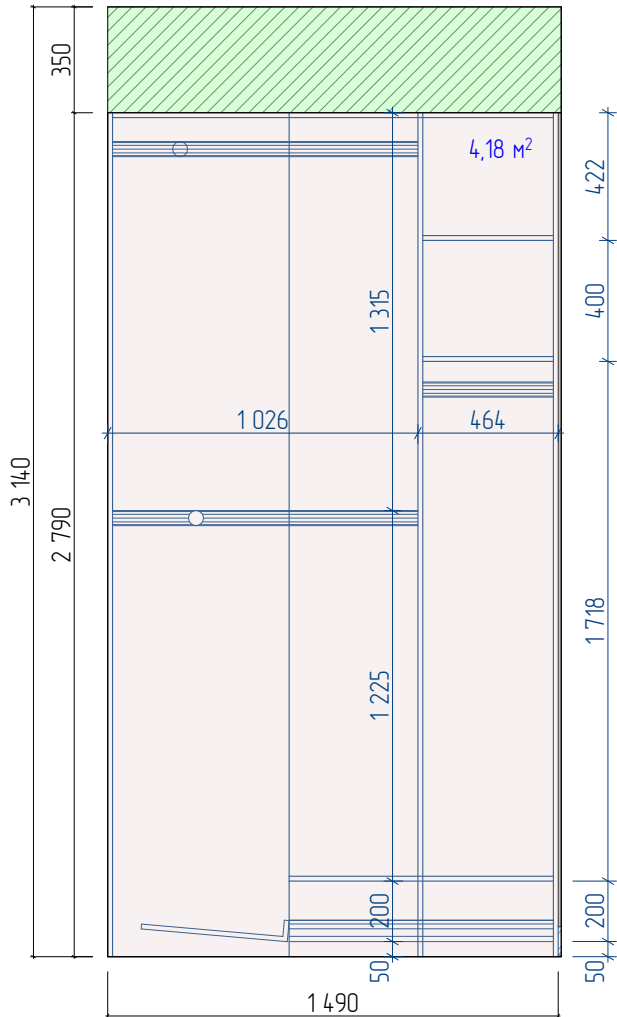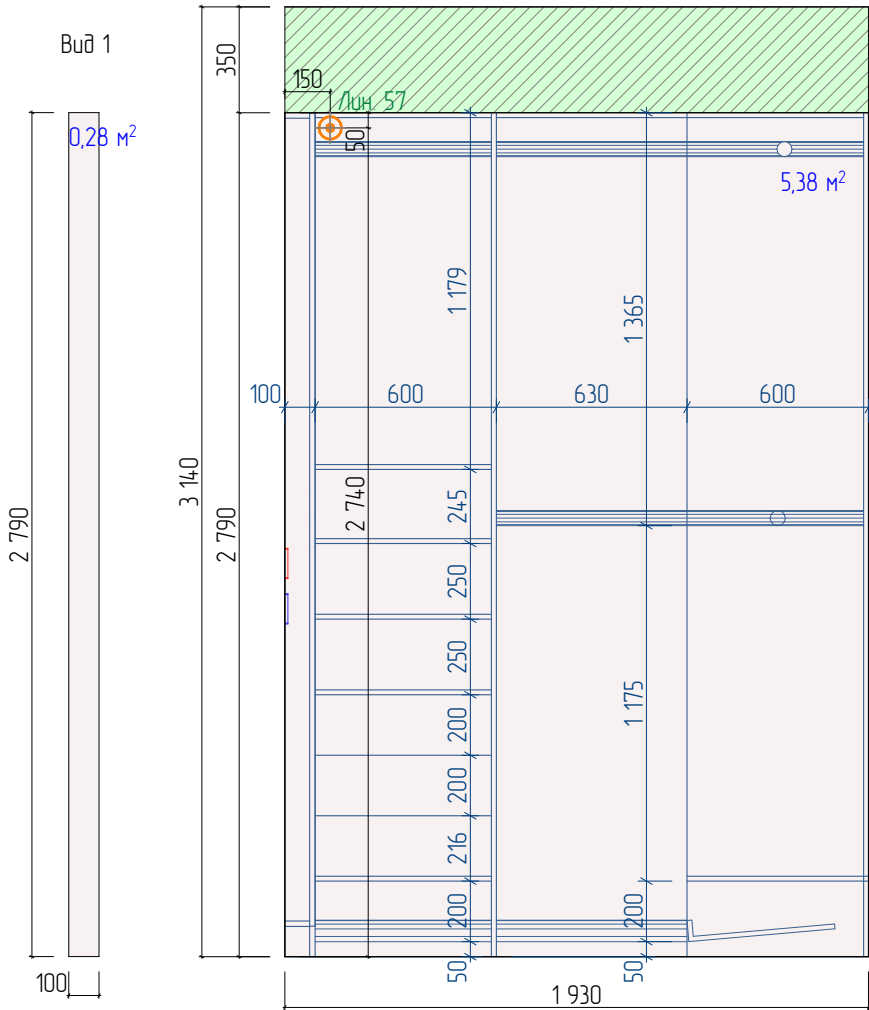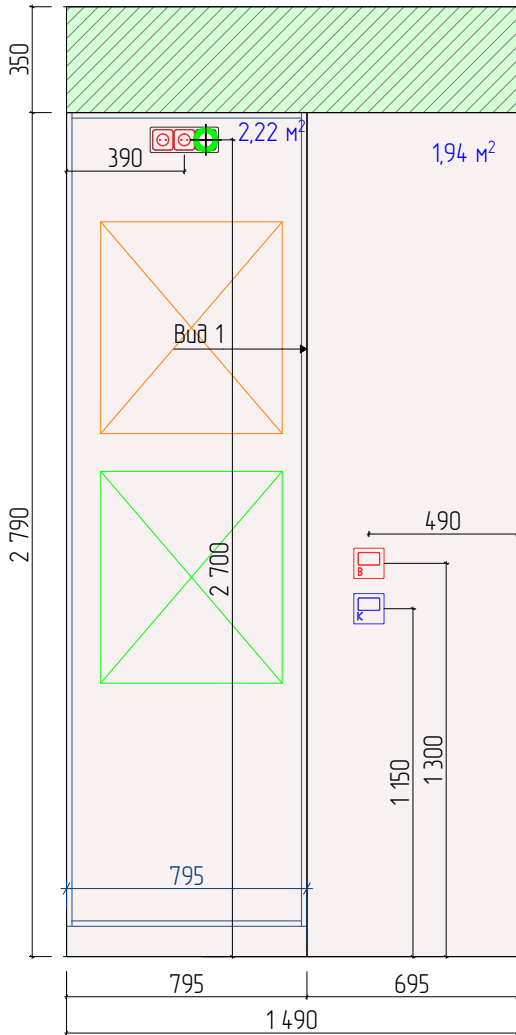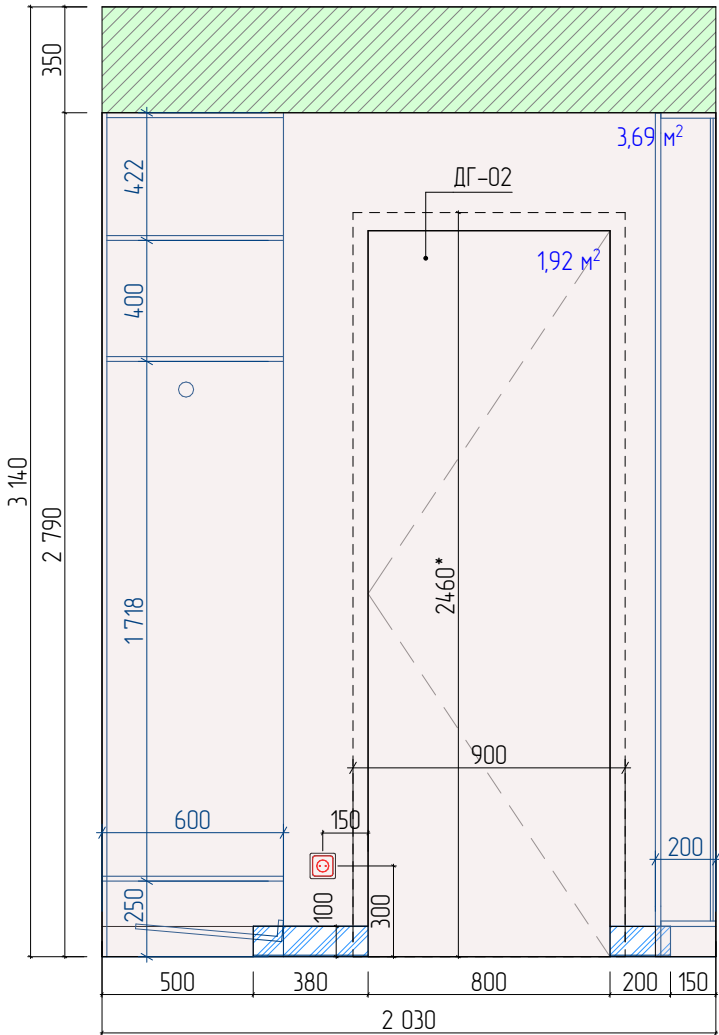

Условные обозначения:

- Монтаж конструкций из ГКВЛ
- Покраска №1. Выполнить по подготовленной поверхности (стеклохолст*). Цвет при выборе образца (бежевый*).
- Плинтус №1. Теневой плинтус скрытого монтажа с МДФ вставкой. Теневой зазор от пола 100 мм. Цвет при выборе образца (в цвет стен).
- Вывод internet-кабеля
- Вывод электрокабеля для светодиодной ленты
- Розетка 220 V
- Электрощит
- Слаботочный щит
- Блок управления каналным кондиционером
- Блок управления вентиляционной системой


Примечания:

- *- размеры уточнить по месту после выполнения черновых отделочных работ.
- Розетки располагать от уровня чистого пола на высоте 300 мм. Исключения указаны на чертеже.
- Цвет окрашивания плинтуса уточнить после согласования образца.
- Высоту проемов выполнить 2460 мм от уровня чистого пола. Уточнить после подбора и согласования модели дверей.
- Плинтус подрезать по месту в местах стыковки с дверями и мебелью.
- Внутреннее наполнение мебели разработать со специалистами.
- Серым/синим цветом показаны размеры мебели. Мебель разработать со специалистами, размеры уточнить после выполнения чистовой отделки.

Ведомость отделочных материалов.

№	Обозначение	Наименование	Кол-во	Примечание
Пол:				
1		Покрывтие №02. Керамогранит. Изготовитель: Elegant Grey, кол-я: Forte Dei Marini, размер: 1200x1200 мм, толщину уточнить при покупке.	2,98 3	м² укладки шт.
Стены:				
2		Плинтус №1. Теневой плинтус скрытого монтажа с МДФ вставкой. Теневой зазор от пола 100 мм. Цвет при выборе образца (в цвет стен).	0,50	м.п.
3		Покраска №1. Выполнить по подготовленной поверхности (стеклохолст*). Цвет при выборе образца (бежевый*).	19,61	м²

МСК 392.12.25-ЭП ПРЕМИУМ			
Эскизный дизайн-проект интерьера квартиры в г. Москва ЖК "Остров", ул. Нижние Мневники д. 7			
Гардеробная №1Развертки стен В-01, В-02, В-03, В-04.			
 Дизайнер интерьера №1 Александр Батеньков	Стадия	Лист	Листов
	ЭП	57	120
		Подп.	Дата
ГАП	Батеньков А.С.		
Гл. дизайнер	Власова В.А.		
Гл. проектиров.	Луныкова В.Н.		
Разработал	Ильина Е.Е.		

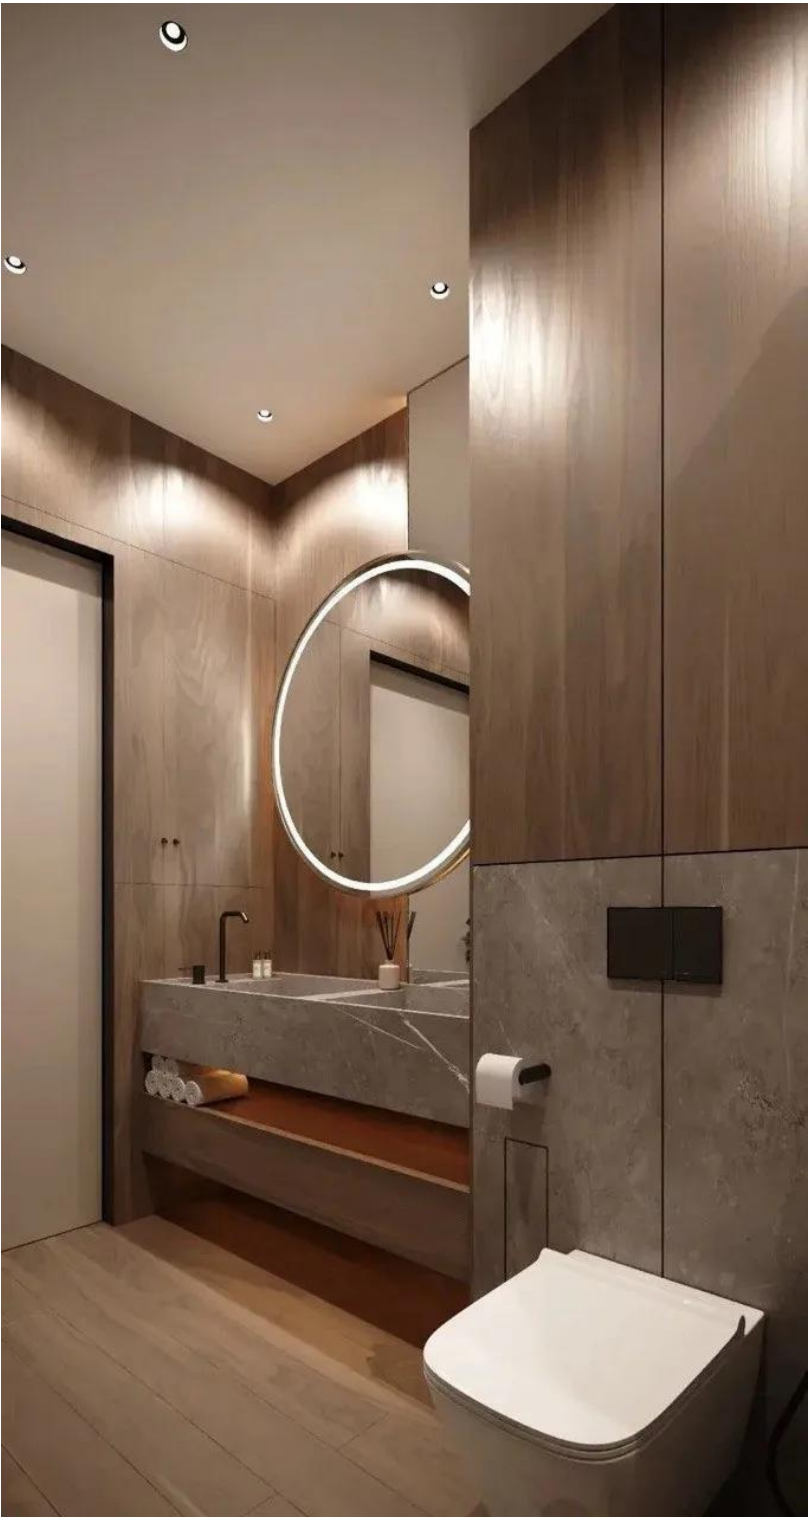


МСК 392.12.25-ЭП ПРЕМИУМ			
Эскизный дизайн-проект интерьера квартиры в г. Москва ЖК "Остров", ул. Нижние Мневники д. 7			
Душевая. Видовые точки.			
Дизайнер интерьера  №1 Александр Батеньков	Стадия	Лист	Листов
	ЭП	58	120
		Подп.	Дата
ГАП	Батеньков А.С.		
Гл. дизайнер	Власова В.А.		
Гл. проектиров.	Луныкова В.Н.		
Разработал	Ильина Е.Е.		




МСК 392.12.25-ЭП ПРЕМИУМ			
Эскизный дизайн-проект интерьера квартиры в г. Москва ЖК "Остров", ул. Нижние Мневники д. 7			
Душевая. Видовые точки.			
Дизайнер интерьера №1 Александр Батеньков	Стадия	Лист	Листов
	ЭП	59	120
		Подп.	Дата
ГАП	Батеньков А.С.		
Гл. дизайнер	Власова В.А.		
Гл. проектиров.	Луныкова В.Н.		
Разработал	Ильина Е.Е.		

План отделки пола:

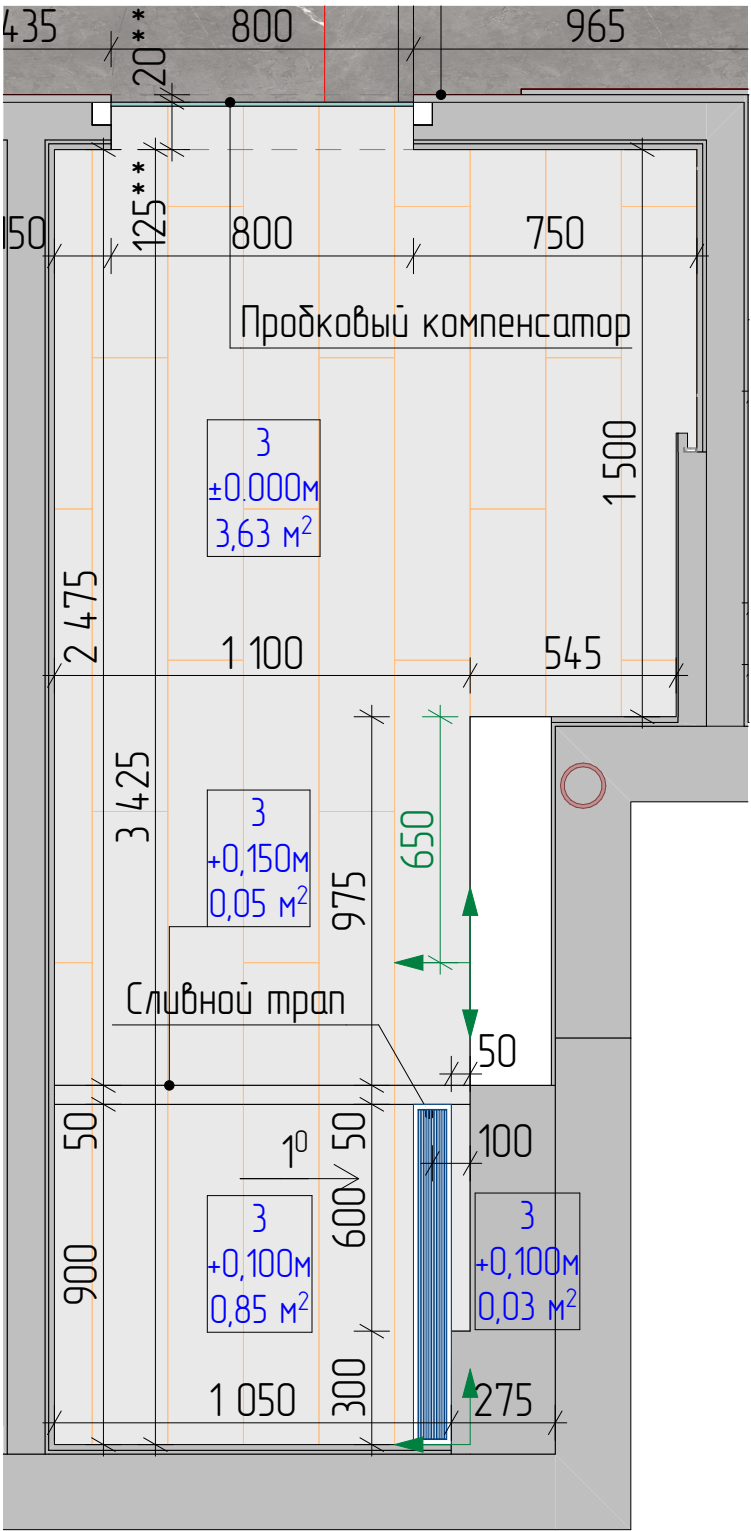

План отделки потолка:

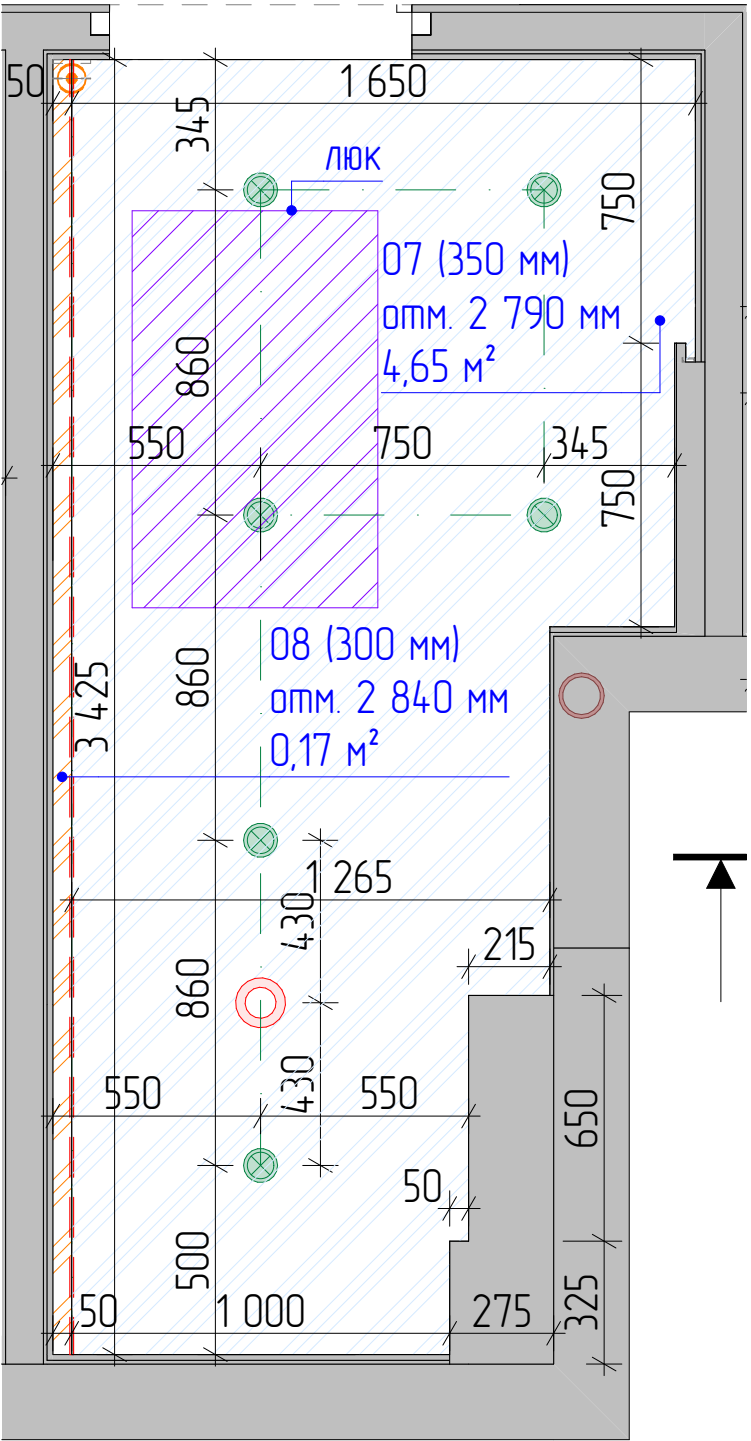

Условные обозначения:


- Направление и начало укладки
- Пробоковый компенсатор
- Покрывтие №03. Керамогранит. Изготовитель: Nutmeg, кол-я: Woodslate Life, размер: 1200x200 мм, толщину уточнить при закупке.
- Вывод 220V
- Вывод электрокабеля для светодиодной ленты
- Диффузор, вытяжка
- Светильник точечный встраиваемый влагозащищенный
- Светодиодная лента, влагозащищенная
- Люк доступа

- Примечания:
- *- размеры уточнить по месту после выполнения черновых отделочных работ.
 - За отметку ±0,000 принят уровень чистого пола.
 - Во влажных помещениях предусмотреть гидроизоляцию пола с заведением на стены на 150 мм, в зоне душевой до потолка.
 - Совместить швы плитки на подиумах и основном полу.
 - При монтаже напольных покрытий уточнить необходимость устройства дверных проемов с порогом.
 - *- размеры уточнить по месту после выполнения черновых отделочных работ и установки дверей со скрытой коробкой.
 - **-размер уточнить по месту в зависимости от точного расположения полотна двери, стыковка двух разных напольных покрытий должна проходить точно по центру вдоль дверного полотна.
 - Выполнить уровни потолка из влагостойкого ГКЛ для предотвращения деформации потолка при затоплении.
 - Высоту уровней потолка отсчитывать от существующей ж/б плиты перекрытия помещения.
 - Во влажных помещениях обои под покраску на потолок не клеить, заменить на оштукатуривание по армирующей сетке, согласовать со специалистами.
 - От вытяжки провести вентиляционный короб до общедомового канала в конструкции потолка, уточнить по месту со специалистами и заказчиком.
 - Шумоизоляцию разработать со специалистами, уточнить состав и толщину слоев шумоизоляционных материалов. Уточнить необходимость устройства с заказчиком.

Условные потолки				
№	Обозначение	Опуск	Примечания	Площадь м2
07		350	Потолок ГКЛ/В, Окрасить в цвет выбранного образца (белый) по оштукатуренной поверхности.	4,65
08		300	Потолок ГКЛ/В, Окрасить в цвет выбранного образца (белый) по оштукатуренной поверхности.	0,17

МСК 392.12.25-ЭП ПРЕМИУМ			
Эскизный дизайн-проект интерьера квартиры в г. Москва ЖК "Остров", ул. Нижние Мневники д. 7			
Душевая.План отделки пола. План отделки потолка.			
Дизайнер интерьера  Александр Батеньков	Стадия	Лист	Листов
	ЭП	60	120
		Подп.	Дата
ГАП	Батеньков А.С.		
Гл. дизайнер	Власова В.А.		
Гл. проектиров.	Лунькова В.Н.		
Разработал	Ильина Е.Е.		

План электрооборудования:

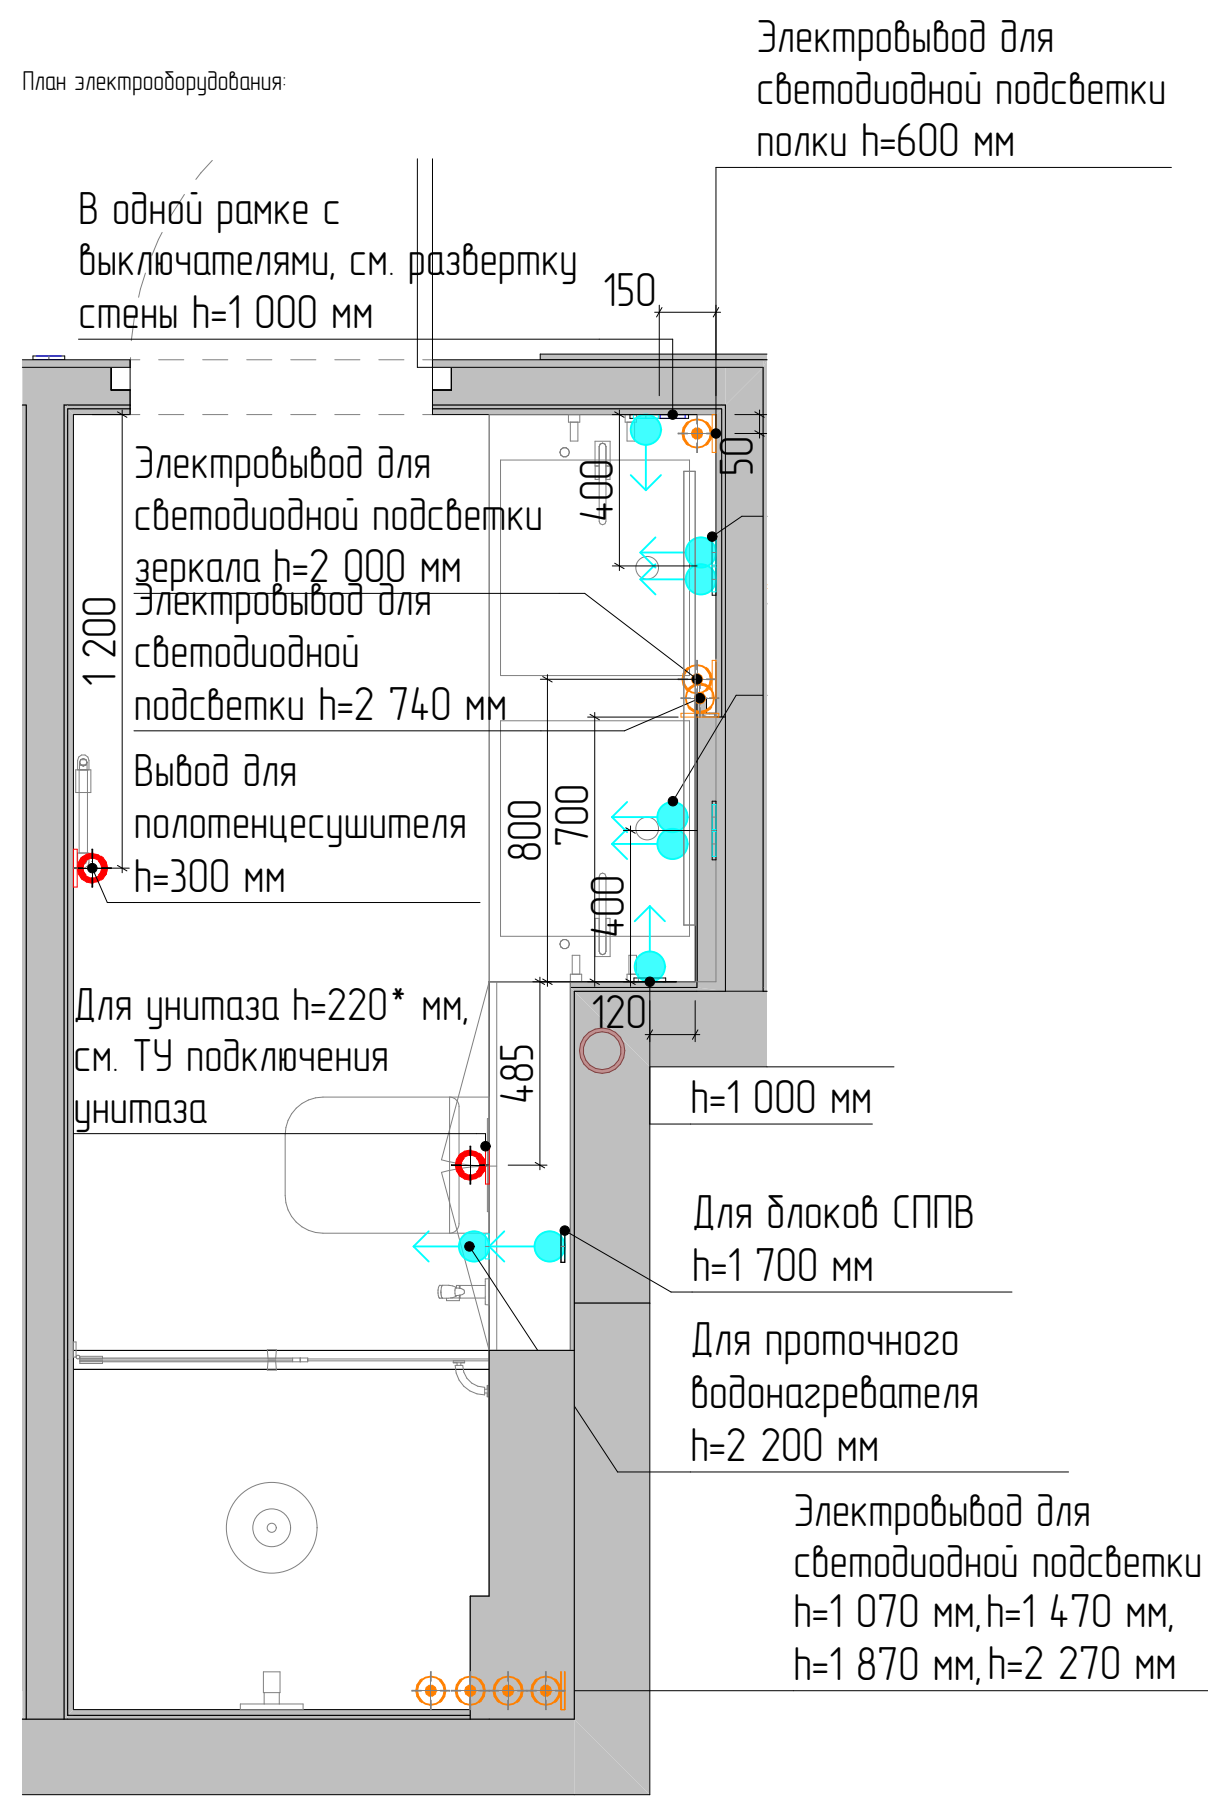


Примечания:

- 1. * – размеры уточнить по месту.
- 2. ** – размещение вывода 220V для полотенцесушителя уточнить после подбора модели.
- 3. Розетки располагать от уровня чистого пола на высоте 0,300 м. Исключения указаны на чертеже.
- 4. Размещение всех выводов и розеток согласовать со специалистами «Умный дом».
- 5. Размеры и характеристики радиаторов отопления согласовать со специалистами, предусмотреть терморегуляторы.
- 6. Размещение розеток и электровыводов по высоте см. на развертках стен.

- 7. Выключатели располагать от уровня чистого пола на высоте 0,900 м. Исключения указаны на чертеже.
- 8. Светильники, встроенные в мебель, согласовать с изготовителями мебели.


План размещения освещения и выключателей:

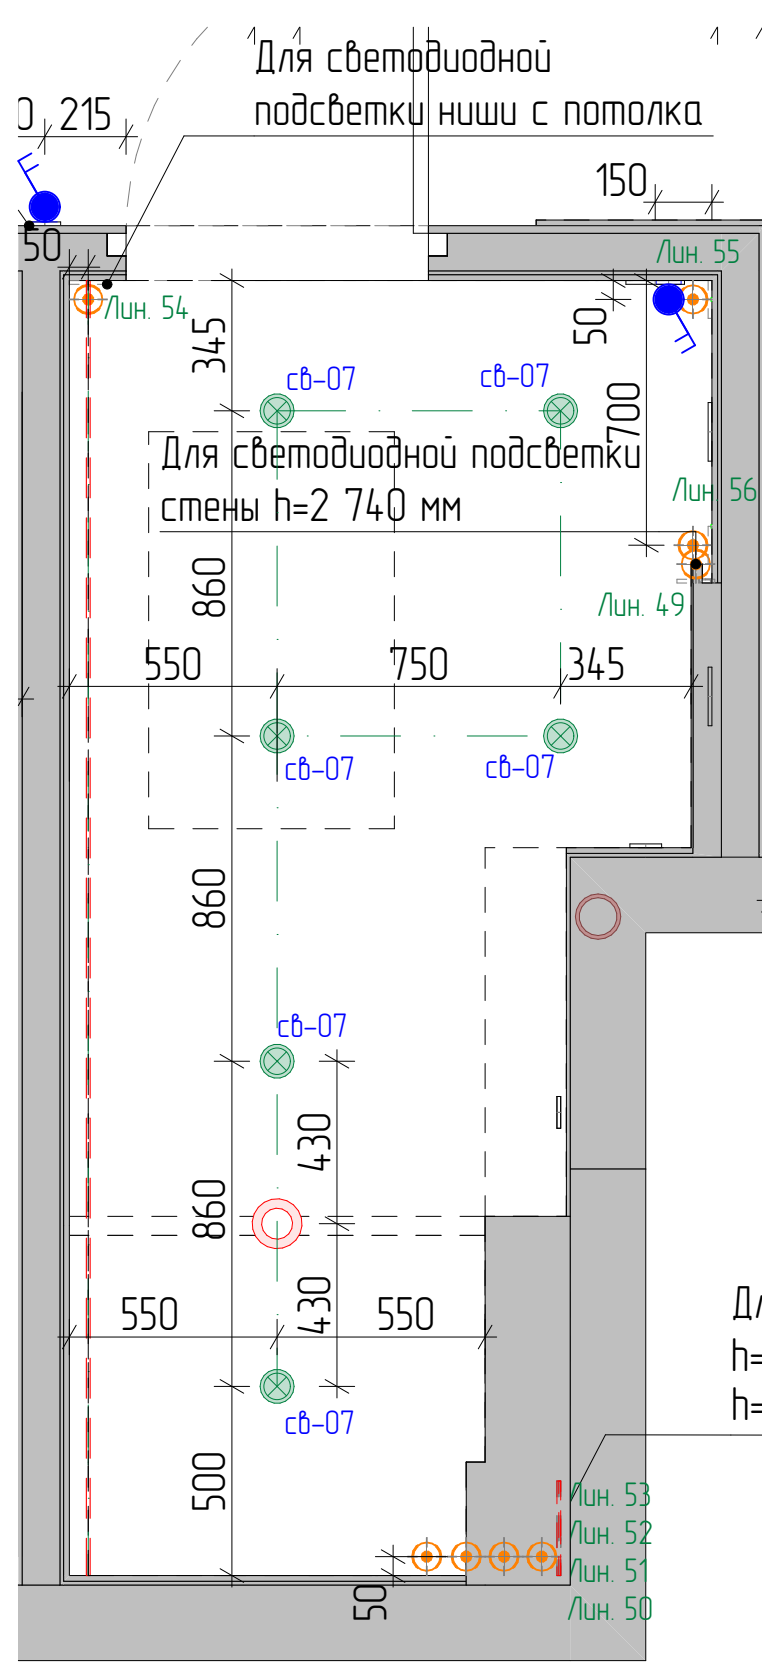






Условные обозначения:

- Розетка 220V влагозащищенная
- Вывод электрокабеля для варочной поверхности
- wi-fi оборудование
- Светильник точечный встраиваемый влагозащищенный
- Светодиодная лента, влагозащищенная
- Выключатель двухклавишный

МСК 392.12.25-ЭП ПРЕМИУМ			
Эскизный дизайн-проект интерьера квартиры в г. Москва ЖК "Остров", ул. Нижние Мневники д. 7			
Душевая. План размещения электрооборудования. План размещения освещения и выключателей.			
Дизайнер интерьера №1 Александр Батеньков	Стадия	Лист	Листов
	ЭП	61	120
		Подп.	Дата
ГАП	Батеньков А.С.		
Гл. дизайнер	Власова В.А.		
Гл. проектиров.	Луцькова В.Н.		
Разработал	Ильина Е.Е.		

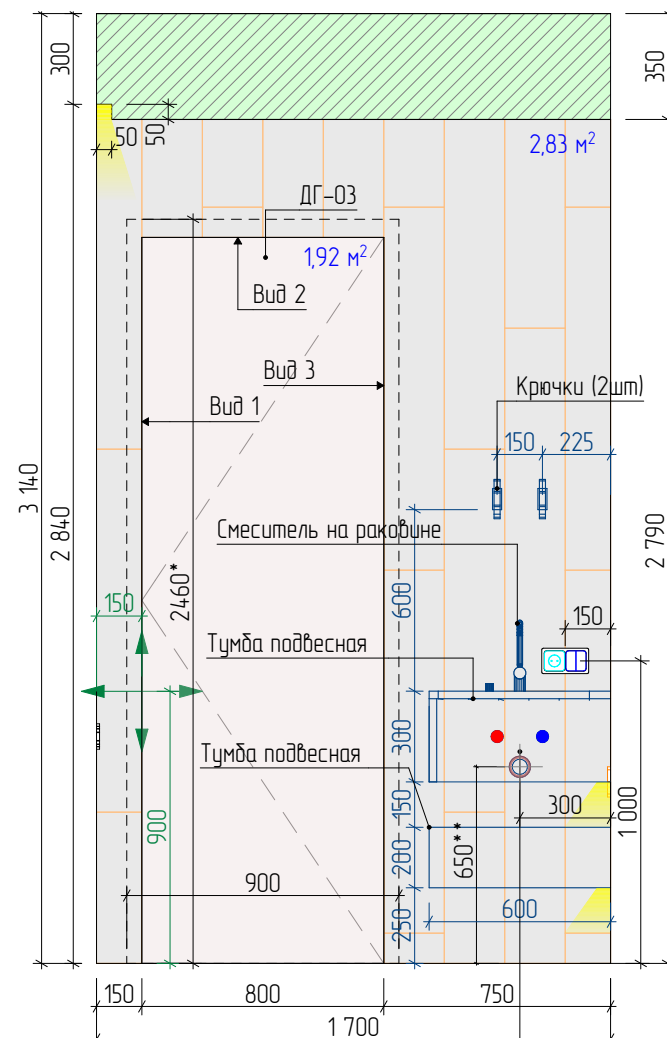

Вывод коммуникаций для раковины и смесителя на столешнице разместить согласно инструкции монтажа выбранной модели

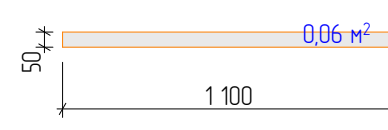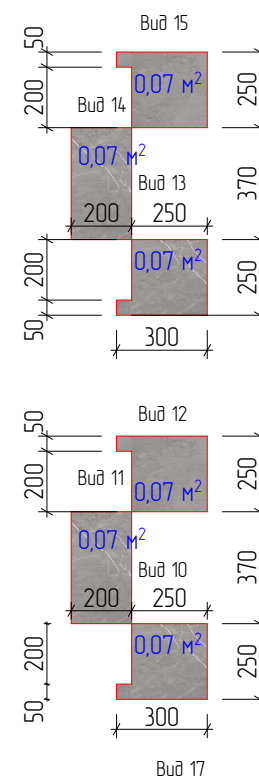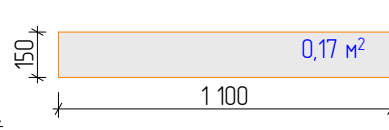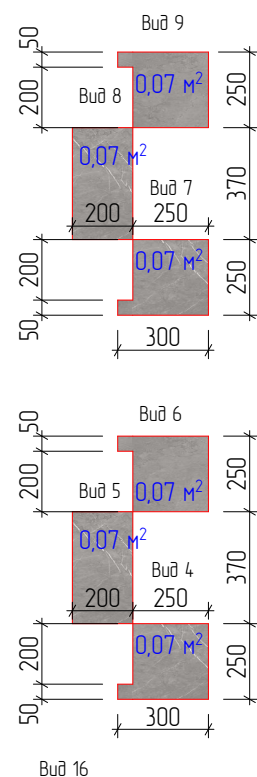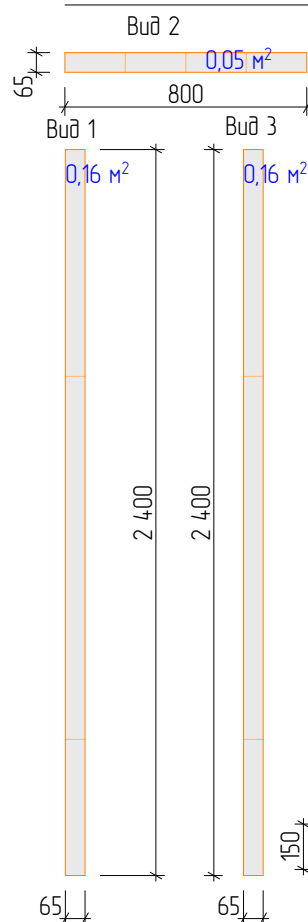


Условное обозначение:

- | | | | |
|---|---|---|--|
|  | Керамогранит №01. Керамогранит.
Изготовитель: Elegant Grey, кол-я: Forte Dei
Marmi, размер: 1200x1200 мм, толщину
уточнить при закупе. |  | Зеркало №2. Разработать со специалистами
(стандарт*) размеры и резка по чертежу. |
|  | |  | Покраска №3. Влагостойкая. Выполнить по
штукатуренной поверхности. Цвет при
выборе образца (белый*). |
|  | Керамогранит №02. Керамогранит.
Изготовитель: Nutmeg, кол-я: Woodslate Life,
размер: 1200x200 мм, толщину уточнить при
закупе. |  | Направление и начало укладки |


Примечания:

1. * – размеры уточнить по месту после выполнения черновых отделочных работ.
2. Выключатели располагать от уровня чистого пола на высоте 900 мм. Исключения указаны на чертеже.
3. Розетки располагать от уровня чистого пола на высоте 300 мм. Исключения указаны на чертеже.
4. Предусмотреть люк скрытого монтажа для доступа к коммуникациям, размещение уточнить по месту.
5. Совместить швы плитки на смежных стенах и полу.
6. Точную привязку выводов коммуникаций решить после выбора оборудования по инструкции монтажа.
7. Расположение розеток и выключателей согласовать с изготовителями кухонного гарнитура.
8. Предусмотреть гидроизоляцию пола с заведением на стену до потолка.
9. ** – размещение вывода 220V для электрического полотенцесушителя уточнить после подбора модели по технической документации.
10. ** – размер уточнить по инструкции монтажа оборудования.
11. Розетки, выключатели, регуляторы теплого пола размещать по центру керамической плитки.
12. Высоту проемов выполнить 2460 мм от уровня чистого пола. Уточнить после подбора и согласования модели дверей.
13. Резку зеркала решить по месту авторским надзором.
14. Внутреннее наполнение мебели разработать со специалистами.
15. Серым/синим цветом показаны размеры мебели. Мебель разработать со специалистами, размеры уточнить после выполнения чистовой отделки.

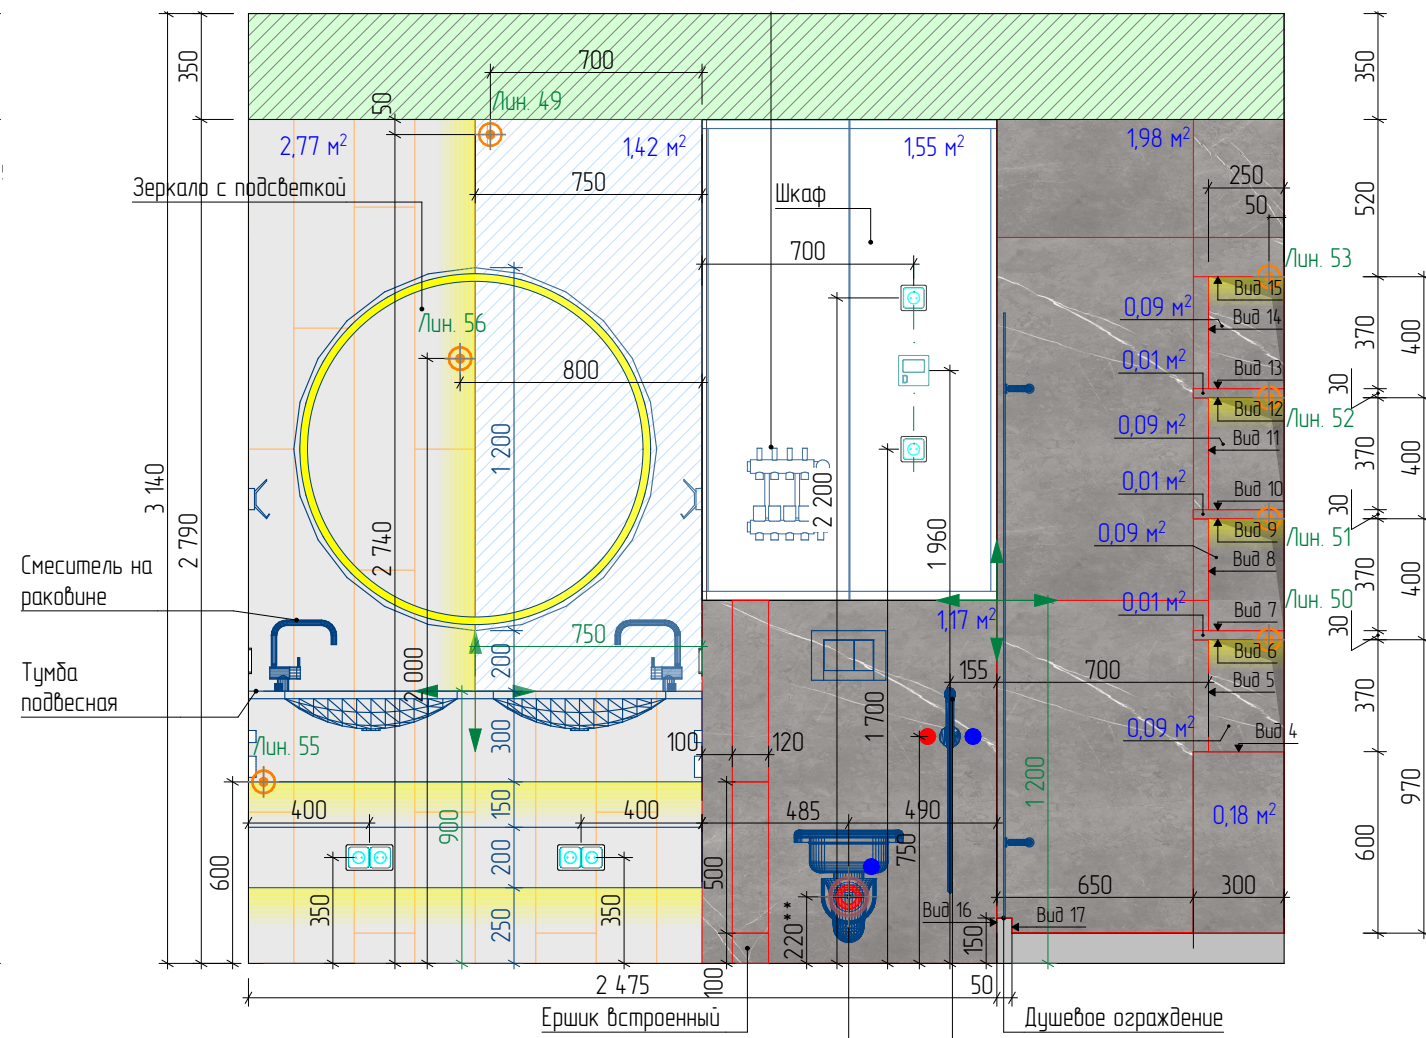

Умный унитаз подвесной
Вывод коммуникаций для подвесного умного унитаза разместить
согласно инструкции монтажа выбранной модели

Гигиенический душ
Вывод коммуникаций для гигиенического душа разместить
согласно инструкции монтажа выбранной модели

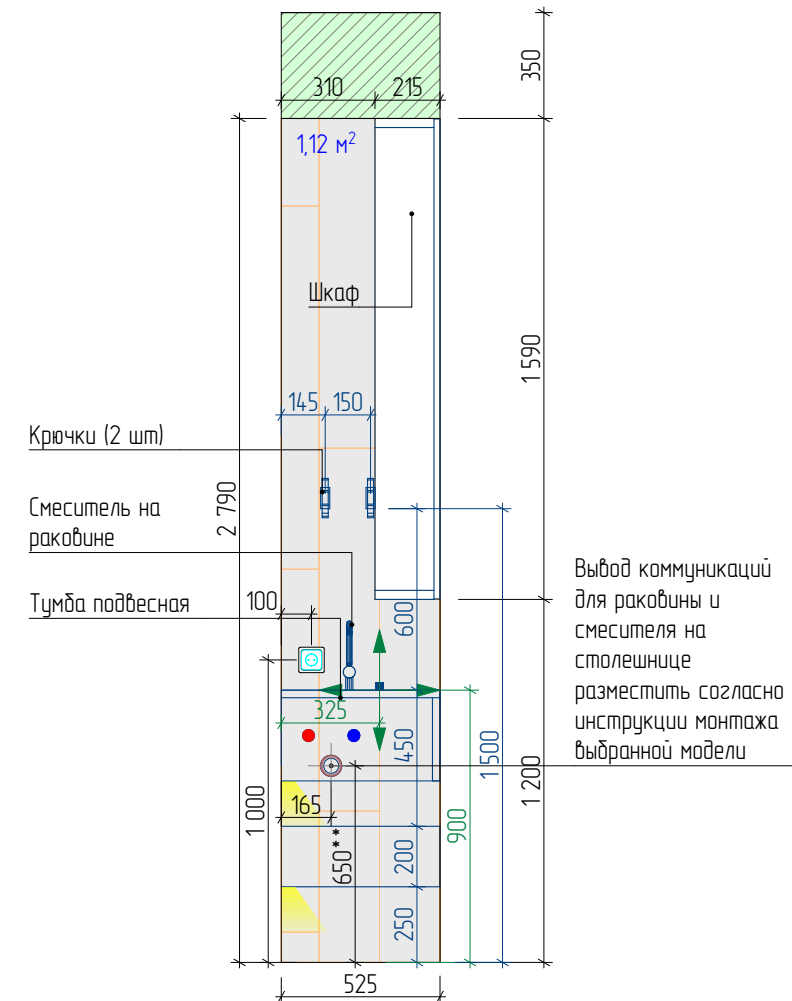

Вывод коммуникаций
для раковины и
смесителя на
столешнице
разместить согласно
инструкции монтажа
выбранной модели

-  Вывод коммуникаций (ХВС, ГВС, канал-ция)
-  Вывод электрокабеля для светодиодной ленты
-  Розетка 220 V, влагозащищенная IP44 и выше
-  Выключатель двухклавишный
-  Вывод 220 V


МСК 392.12.25-ЭП ПРЕМИУМ

Эскизный дизайн-проект интерьера квартиры в г. Москва ЖК
"Остров", ул. Нижние Мневники д. 7


Душевая.Развертки стен Г-01, Г-02, Г-03.

Дизайнер интерьера  №1 Александр Батеньков	Стадия	Лист	Листов
	ЭП	62	120
		Подп.	Дата
ГАП	Батеньков А.С.		
Гл. дизайнер	Власова В.А.		
Гл. проектиров.	Луныкова В.Н.		
Разработал	Ильина Е.Е.		

Г-04 Развертка стены 1:25

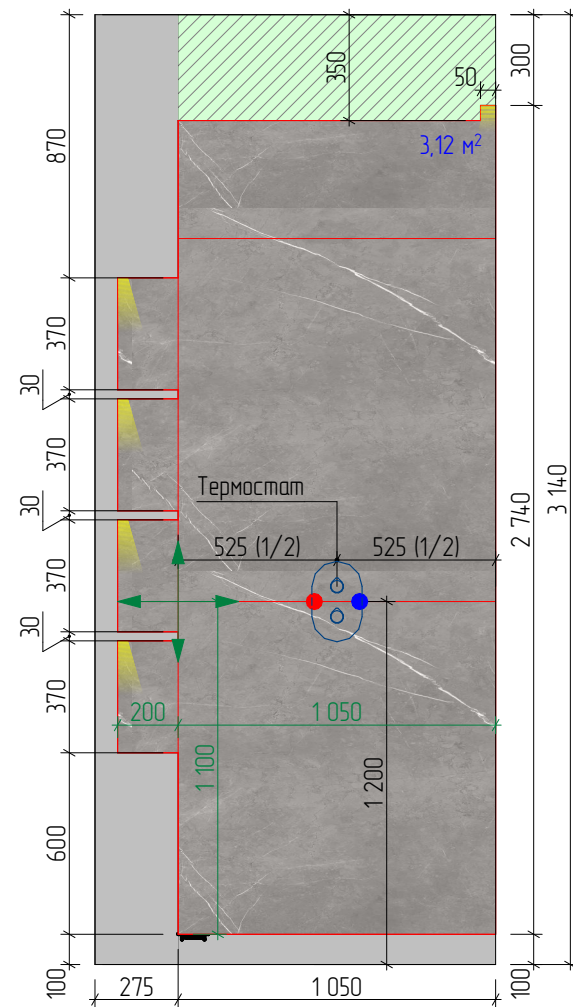

Г-05 Развертка стены 1:25

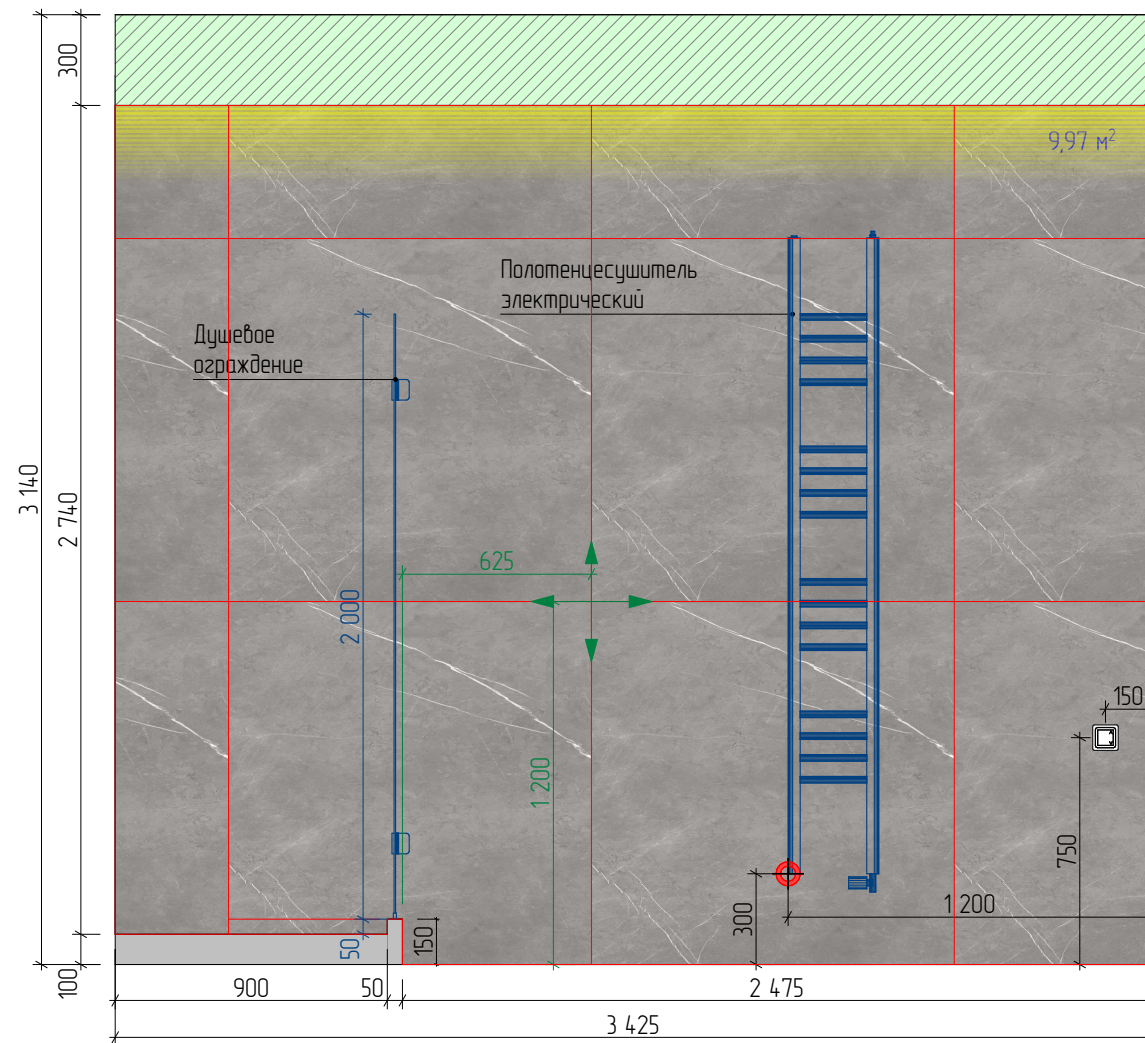

Условное обозначение:



Керамогранит №01. Керамогранит.
Исполнитель: Elegant Grey, кол-я: Forte Dei
Marmi, размер: 1200x1200 мм, толщину
уточнить при заказе.



Вывод коммуникаций (ХВС, ГВС, канал-ция)



Вывод 220 V



Резулятор теплового пола



Направление и начало укладки

Примечания:

1. * – размеры уточнить по месту после выполнения черновых отделочных работ.
3. Регуляторы теплого пола располагать от уровня чистого пола на высоте 750 мм. Исключения указаны на чертеже.
4. Розетки располагать от уровня чистого пола на высоте 300 мм. Исключения указаны на чертеже.
5. Совместить швы плитки на смежных стенах и полу.
6. Точную привязку выводов коммуникации решить после выбора оборудования по инструкции монтажа.
7. Предусмотреть гидроизоляцию пола с заведением на стену до потолка.
8. ** – размещение вывода 220V для электрического полотенцесушителя уточнить после выбора модели по технической документации.
9. ** – размер уточнить по инструкции монтажа оборудования.
10. Розетки, выключатели, регуляторы теплого пола размещать по центру керамической плитки.
11. Внутреннее наполнение мебели разработать со специалистами.
12. Серым/синим цветом показаны размеры мебели. Мебель разработать со специалистами, размеры уточнить после выполнения чистой отделки.

Ведомость отделочных материалов.

№	Обозначение	Наименование	Кол-во	Примечание
Пол:				
1		Покрытие №03. Керамогранит. Изготовитель: Nutmeg, кол-я: Woodslate Life, размер: 1200x200 мм, толщину уточнить при закупе.	4,56 26	м ² укладки шт.
Стены:				
2		Покраска №3. Влагостойкая. Выполнить по штукатуренной поверхности. Цвет при выборе образца (белый*).	3,47	м ²
3		Керамогранит №02. Керамогранит. Изготовитель: Nutmeg, кол-я: Woodslate Life, размер: 1200x200 мм, толщину уточнить при закупе.	7,32 37	м ² укладки шт.
4		Керамогранит №01. Керамогранит. Изготовитель: Elegant Grey, кол-я: Forte Dei Marmi, размер: 1200x1200 мм, толщину уточнить при закупе.	17,65 16	м ² укладки шт.
5		Зеркало №2. Разработать со специалистами (стандарт*) размеры и резка по чертежу.	1,42	м ²

МСК 392.12.25-ЭП ПРЕМИУМ

Эскизный дизайн-проект интерьера квартиры в г. Москва ЖК
"Остров", ул. Нижние Мневники д. 7

Душевая.Развертки стен Г-04, Г-05.


Дизайнер интерьера  №1 Александр Батеньков	Стадия	Лист	Листов
	ЭП	63	120
		Подп.	Дата
ГАП	Батеньков А.С.		
Гл. дизайнер	Власова В.А.		
Гл. проектиров.	Луцькова В.Н.		
Разработал	Ильина Е.Е.		



МСК 392.12.25-ЭП ПРЕМИУМ			
Эскизный дизайн-проект интерьера квартиры в г. Москва ЖК "Остров", ул. Нижние Мневники д. 7			
Спальня №1 Видовые точки.			
Дизайнер интерьера  Александр Батеньков	Стадия	Лист	Листов
	ЭП	64	120
		Подп.	Дата
ГАП	Батеньков А.С.		
Гл. дизайнер	Власова В.А.		
Гл. проектиров.	Луныкова В.Н.		
Разработал	Ильина Е.Е.		



МСК 392.12.25-ЭП ПРЕМИУМ			
Эскизный дизайн-проект интерьера квартиры в г. Москва ЖК "Остров", ул. Нижние Мневники д. 7			
Спальня №1 Видовые точки.			
Дизайнер интерьера  Александр Батеньков	Стадия	Лист	Листов
	ЭП	65	120
		Подп.	Дата
ГАП	Батеньков А.С.		
Гл. дизайнер	Власова В.А.		
Гл. проектиров.	Луныкова В.Н.		
Разработал	Ильина Е.Е.		

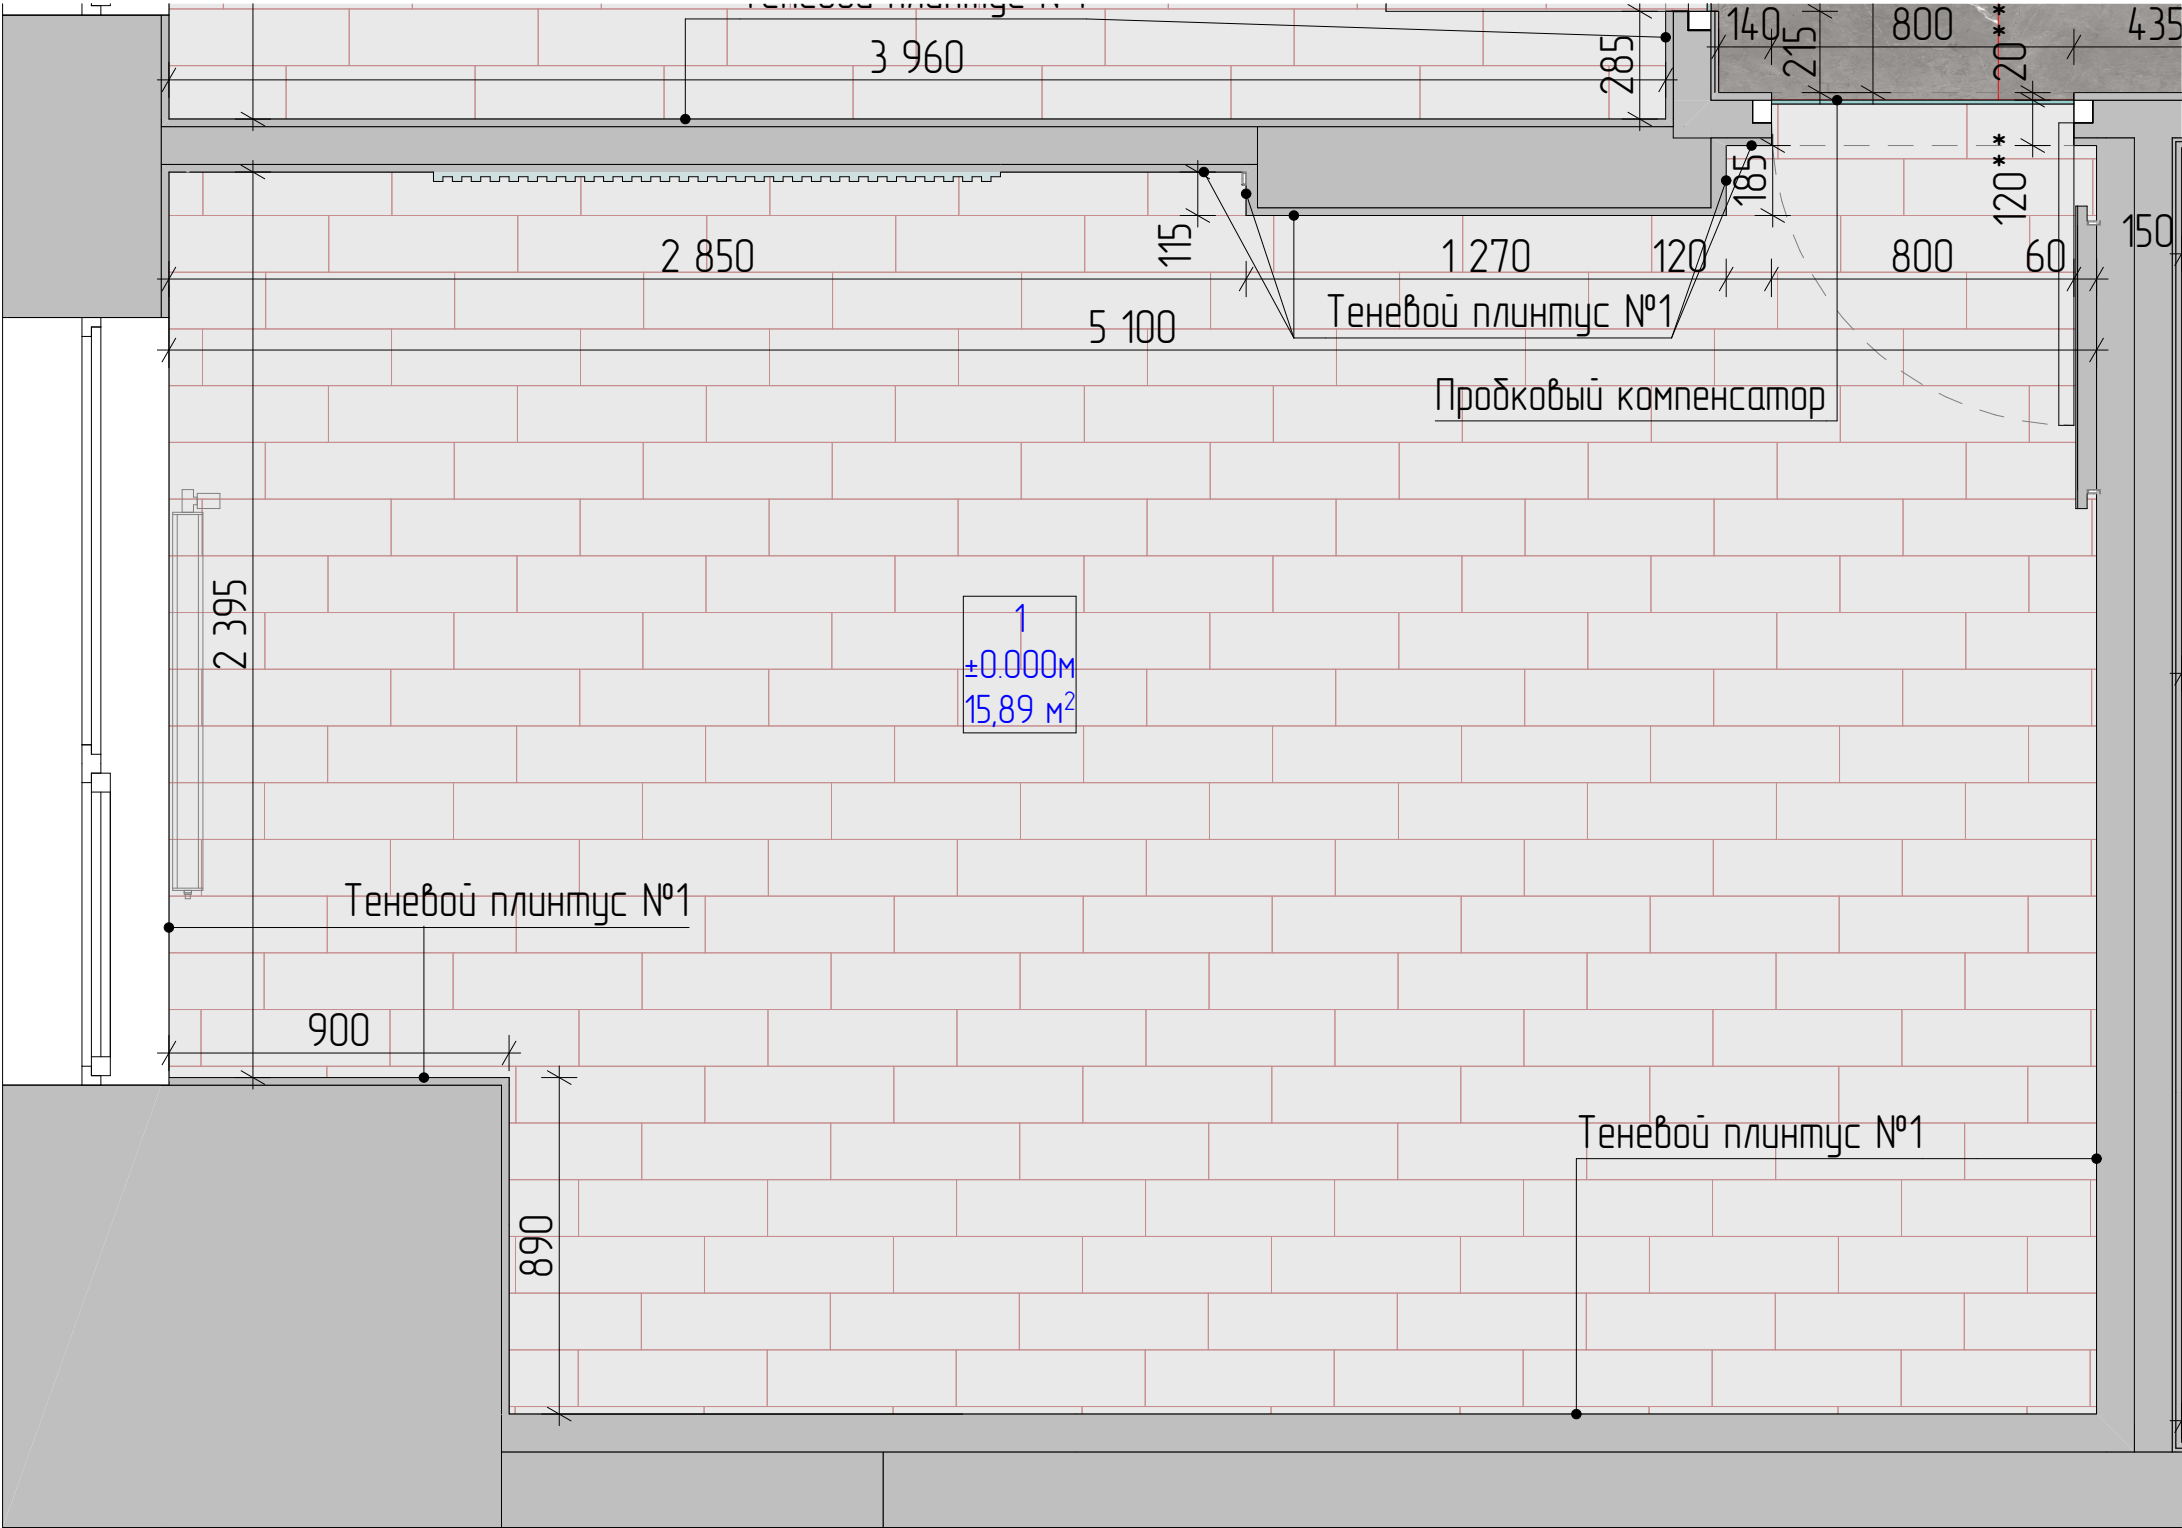

Условные обозначения:

Направление и начало укладки

Пробковый компенсатор

1

Покрывтие №01. Паркет. Изготовитель: Lab Arte, кол-я: Angle Дуб Натур, размер: 500x150 мм, точный артикул и производителя уточнить при выборе образца, толщину уточнить при покупке.

Примечания:

1. * – размеры уточнить по месту после выполнения черновых отделочных работ.


2. За отметку ±0,000 принят уровень чистого пола.

3. При монтаже напольных покрытий уточнить необходимость устройства дверных проемов с порогом.

1. * – размеры уточнить по месту после выполнения черновых отделочных работ и установки дверей со скрытой коробкой.

2. ** –размер уточнить по месту в зависимости от точного расположения полотна двери, стыковка двух разных напольных покрытий должна проходить точно по центру вдоль дверного полотна.

МСК 392.12.25–ЭП ПРЕМИУМ			
Эскизный дизайн–проект интерьера квартиры в г. Москва ЖК “Остров”, ул. Нижние Мневники д. 7			
Спальня №1.План отделки пола.			
Дизайнер интерьера №1 Александр Батеньков	Стадия	Лист	Листов
	ЭП	66	120
		Подп.	Дата
ГАП	Батеньков А.С.		
Гл. дизайнер	Власова В.А.		
Гл. проектиров.	Луцькова В.Н.		
Разработал	Ильина Е.Е.		

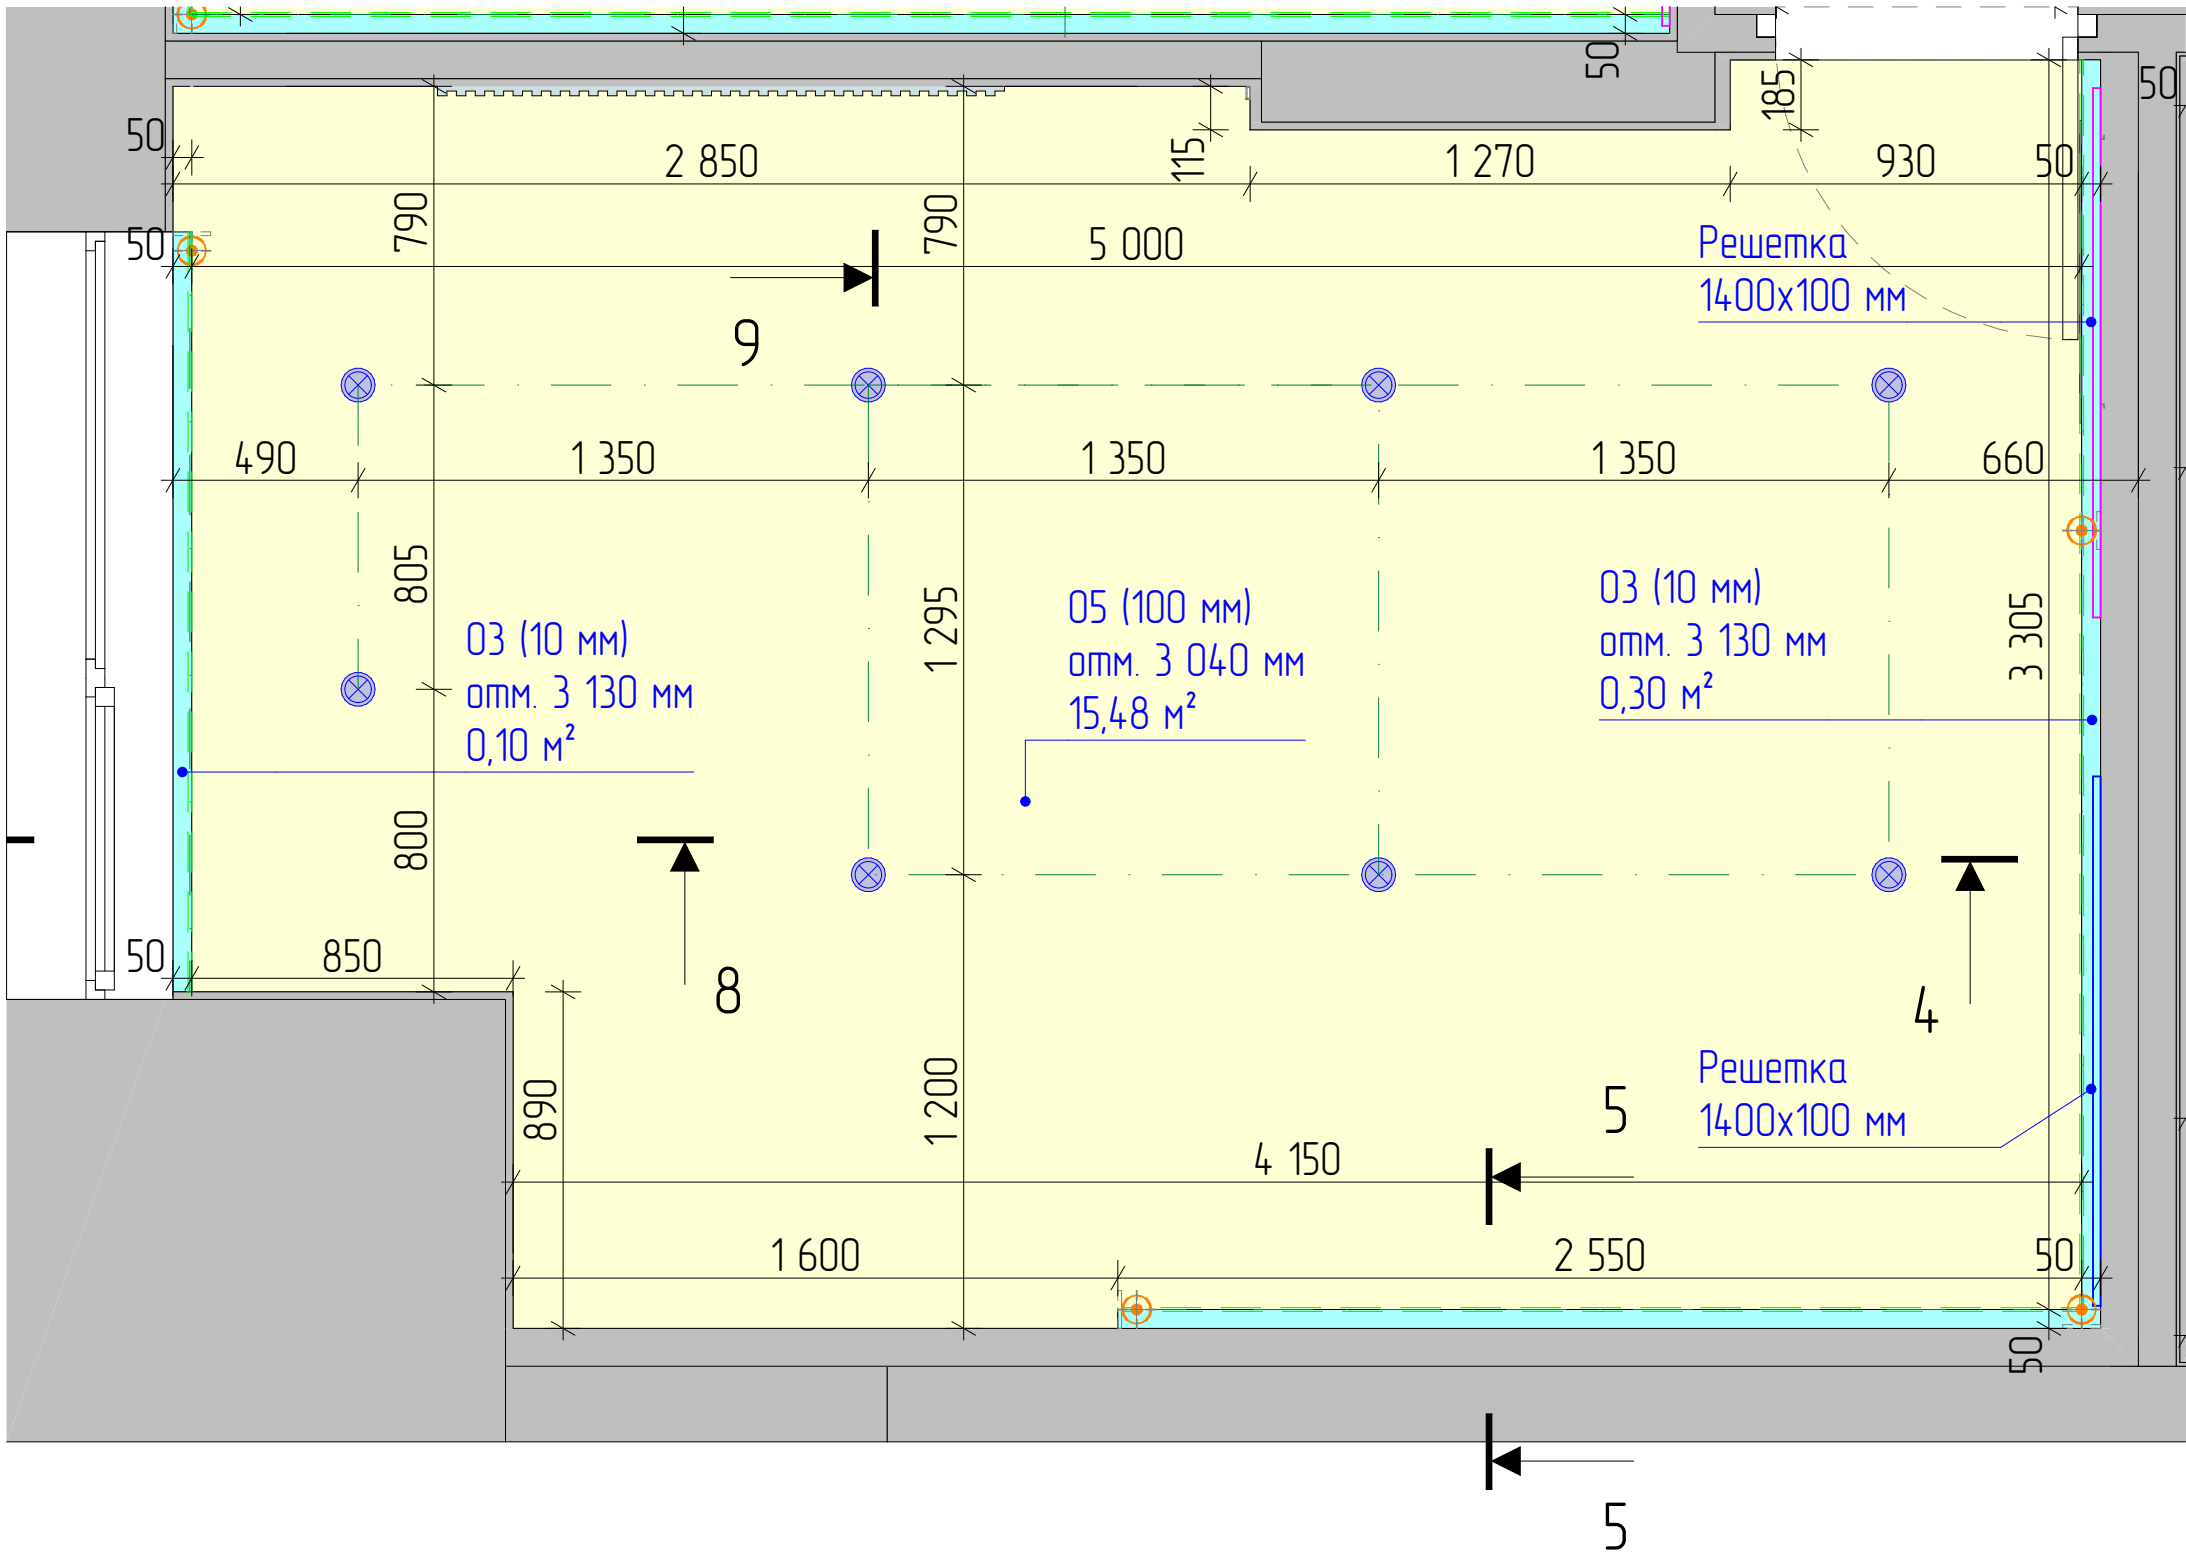

Условные обозначения:


- Выход 220V
- Выход электрокабеля для светодиодной ленты
- Светильник точечный встраиваемый
- Светодиодная лента

Примечания:

- * - размеры уточнить по месту после выполнения черновых работ.
- Выполнить уровни потолка из влагостойкого ГКЛ для предотвращения деформации потолка при затоплении.
- Высоту уровней потолка отсчитывать от существующей ж/б плиты перекрытия помещения.
- Шумоизоляцию разработать со специалистами, уточнить состав и толщину слоев шумоизоляционных материалов. Уточнить необходимость устройства с заказчиком.

Условные потолки				
№	Обозначение	Опуск	Примечания	Площадь м2
03		10	Выровнять и оштукатурить существующий потолок. Окрасить в цвет выбранного образца (белый) по армирующему материалу (стеклохолст "паутинка"). Размер ниши уточнить.	15,48
05		100	Потолок ГКЛ/В. Окрасить в цвет выбранного образца (белый) по армирующему материалу (стеклохолст "паутинка").	0,40

МСК 392.12.25-ЭП ПРЕМИУМ				
Эскизный дизайн-проект интерьера квартиры в г. Москва ЖК "Остров", ул. Нижние Мневники д. 7				
Спальня №1. План отделки потолка.				
Дизайнер интерьера №1  Александр Батеньков	Стадия	Лист	Листов	
	ЭП	67	120	
		Подп.	Дата	
ГАП	Батеньков А.С.			
Гл. дизайнер	Власова В.А.			
Гл. проектиров.	Луныкова В.Н.			
Разработал	Ильина Е.Е.			

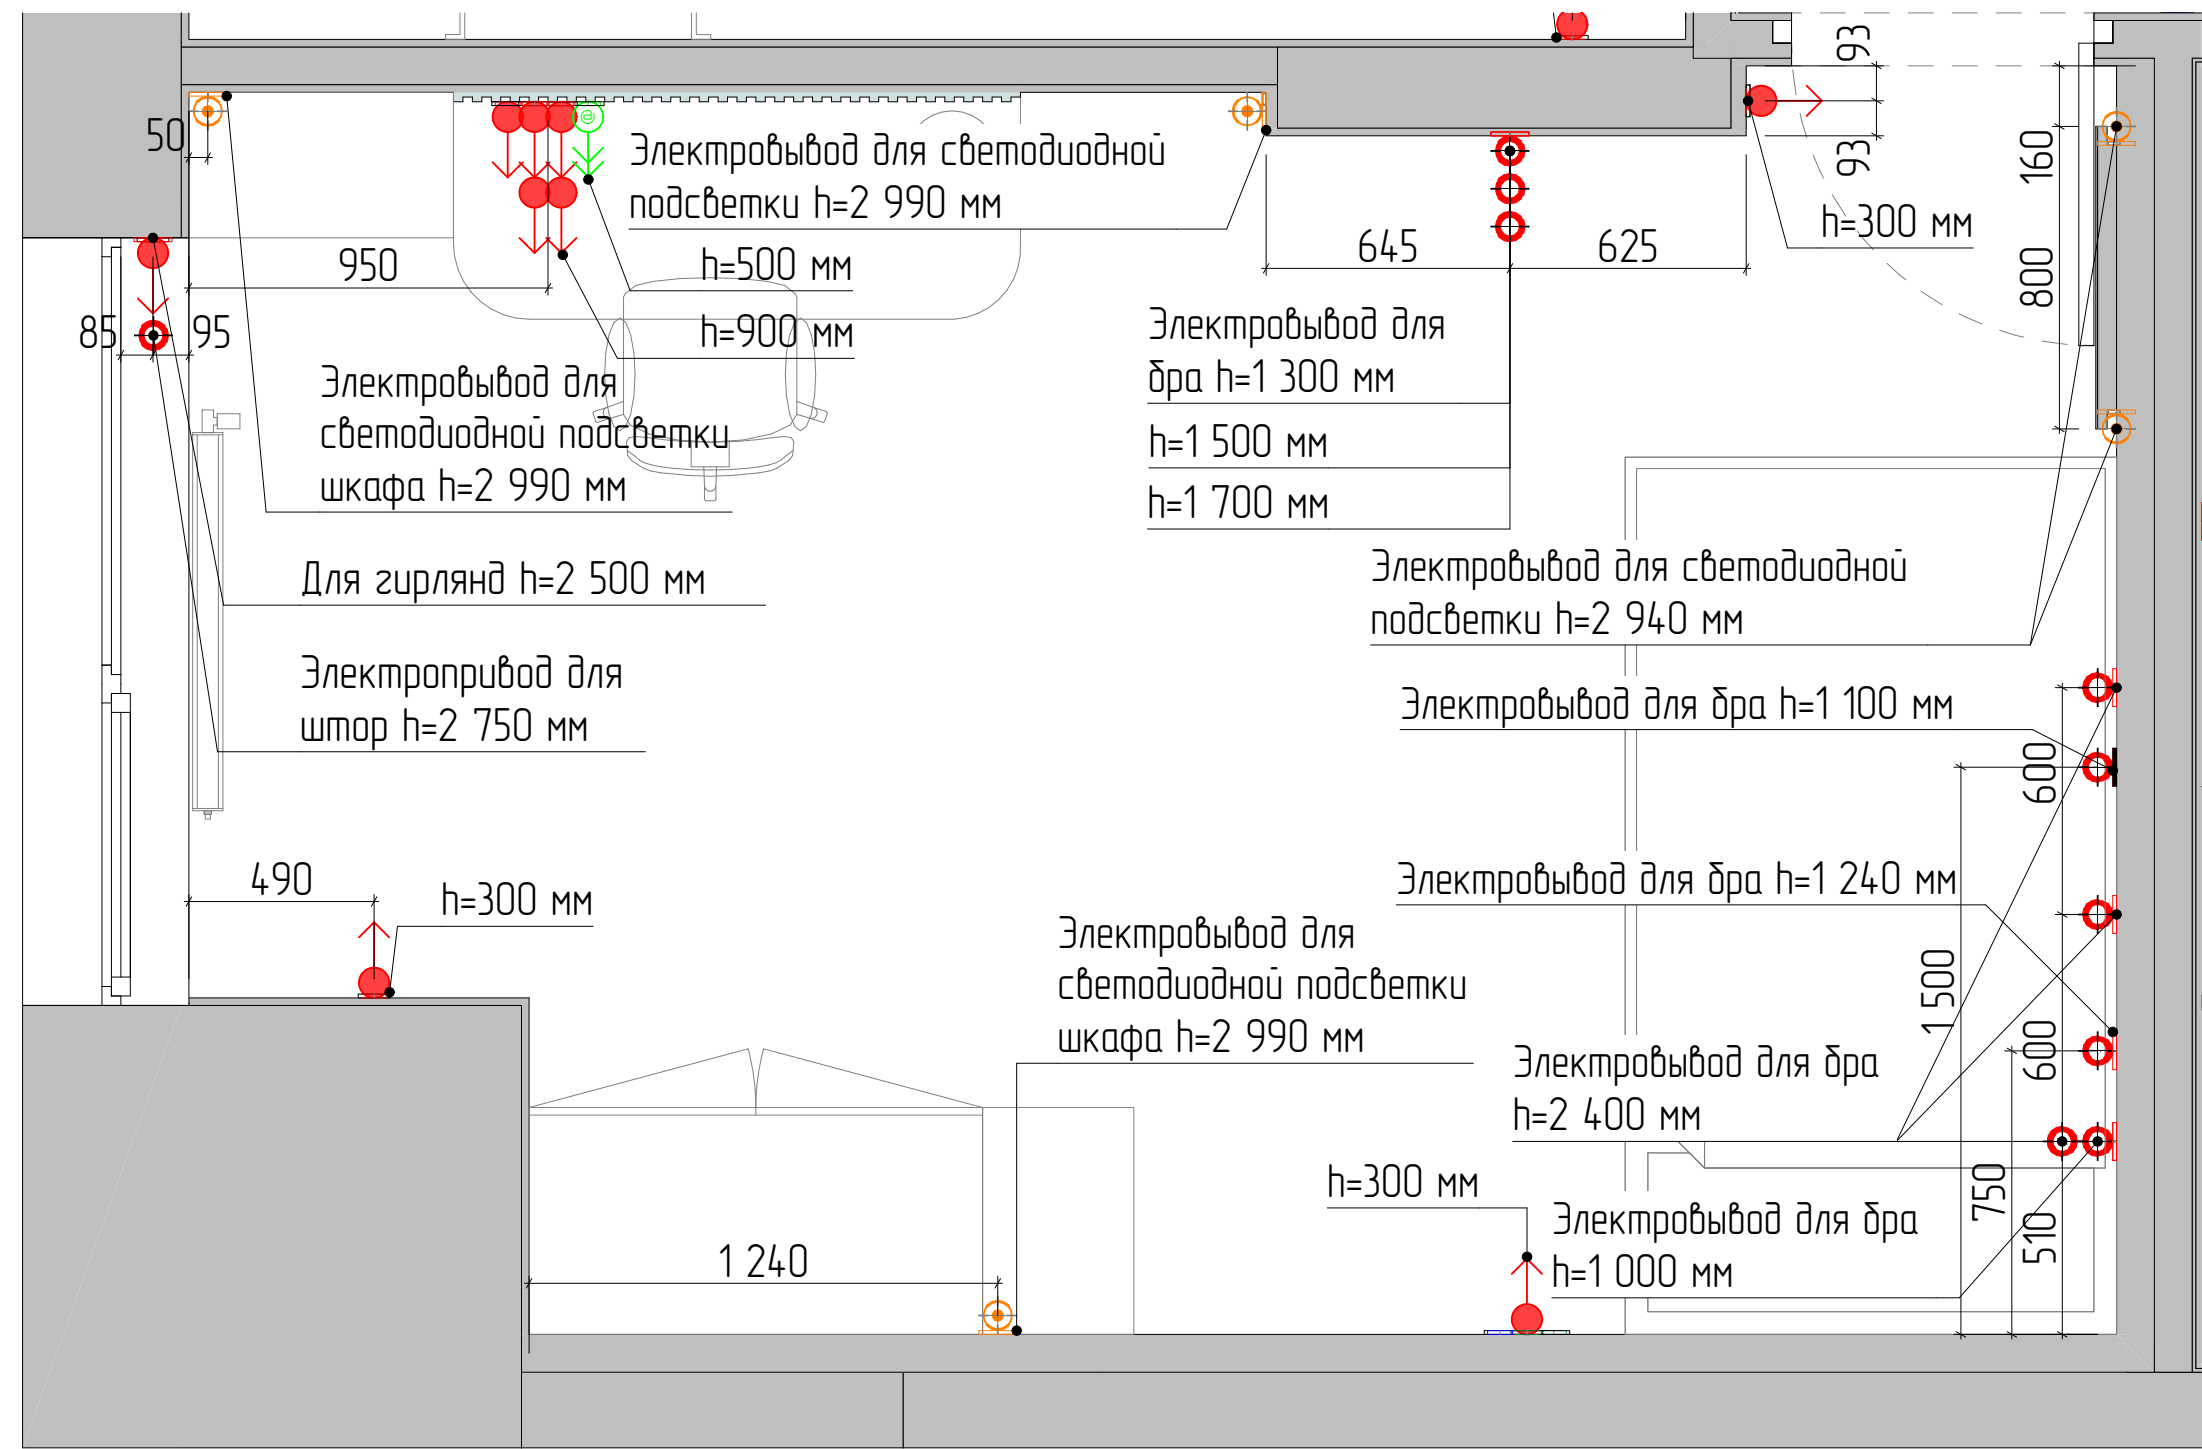

Условные обозначения:

- Разетка 220V
- Вывод электрокабеля для светодиодной ленты
- Вывод электрокабеля для варочной поверхности
- Вывод 220V


Примечания:

- * – размеры уточнить по месту.
- Розетки располагать от уровня чистого пола на высоте 0,300 м. Исключения указаны на чертеже.
- Размещение всех выводов и розеток согласовать со специалистами «Умный дом».
- Размеры и характеристики радиаторов отопления согласовать со специалистами, предусмотреть терморегуляторы.
- Датчики пожарной и охранной сигнализации и электровыводы для них разместить совместно со специалистами, предварительно вызвав их на объект.
- Размещение розеток и электровыводов по высоте см. на развертках стен.

МСК 392.12.25–ЭП ПРЕМИУМ

Эскизный дизайн–проект интерьера квартиры в г. Москва ЖК
"Остров", ул. Нижние Мневники д. 7



Спальня №1 План размещения электрооборудования.

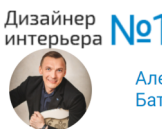

Александр
Батеньков

Стадия	Лист	Листов
ЭП	68	120
	Подп.	Дата

ГАП	Батеньков А.С.		
Гл. дизайнер	Власова В.А.		
Гл. проектиров.	Луныкова В.Н.		
Разработал	Ильина Е.Е.		

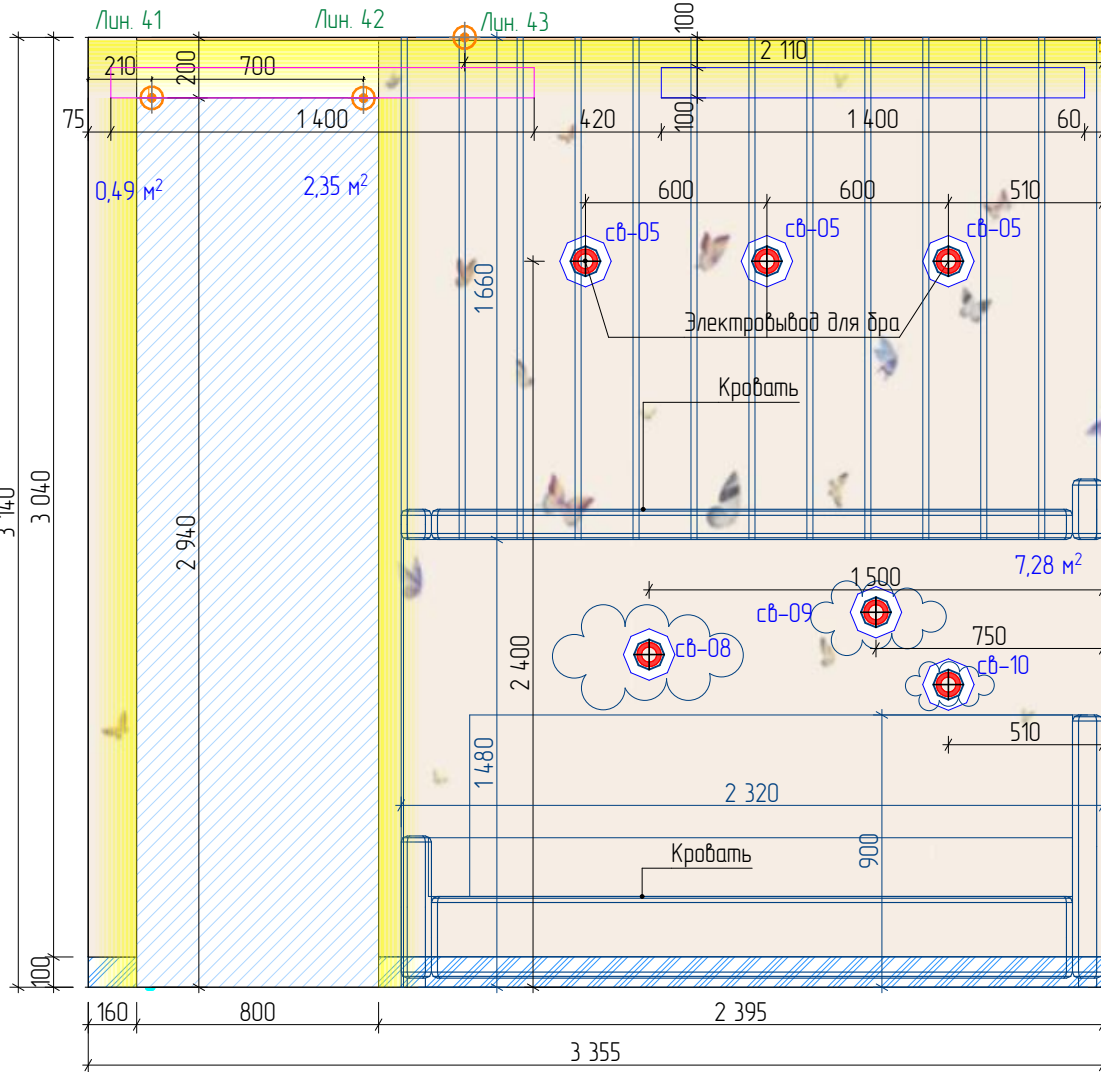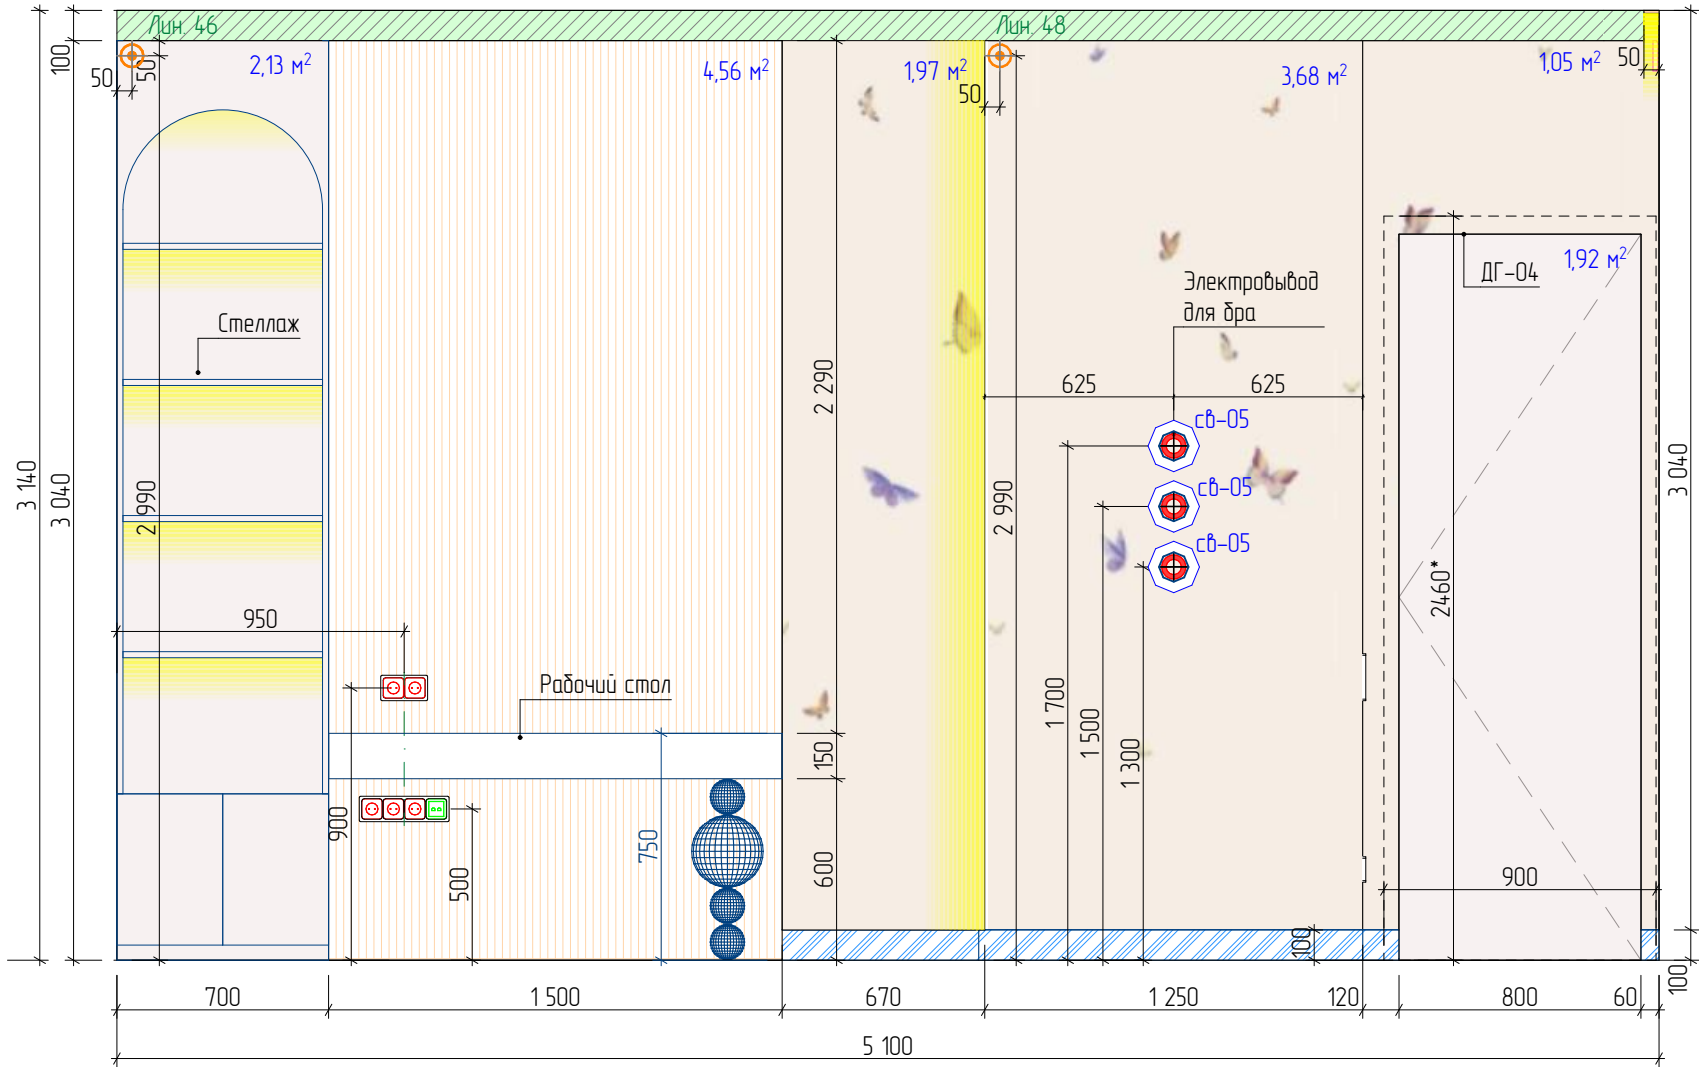








Условные обозначения:

- Обои №1. Обои ручной работы. Изготовитель: fresq, кол-я: CLASSIC, арт.: EN.01. Размер, цвет и фактура при выборе образца.
- Плинтус №1. Теневой плинтус скрытого монтажа с МДФ вставкой. Теневой зазор от пола 100 мм. Цвет при выборе образца (в цвет стен).
- Монтаж конструкций из ГКВЛ
- Зеркало №2. Разработать со специалистами (стандарт*) размеры и резка по чертежу.
- Покраска №1. Выполнить по подготовленной поверхности (стеклохолст*). Цвет при выборе образца (бежевый*).
- МДФ панель №3. 3Д панель. Цвет и фактура при выборе образца (в цвет мебели*).
- Розетка 220 V
- Интернет-розетка двойная
- Выход 220 V
- Выход электрокабеля для светодиодной ленты

Примечания:

- *- размеры уточнить по месту после выполнения черновых отделочных работ.
- Розетки располагать от уровня чистого пола на высоте 300 мм. Исключения указаны на чертеже.
- Размещение вывода 220 V для кондиционеров согласовать со специалистами.
- Цвет окрашивания плинтуса уточнить после согласования образца.
- Высоту проемов выполнить 2460 мм от уровня чистого пола. Уточнить после подбора и согласования модели дверей.
- Резку зеркала решить по месту авторским надзором.
- Плинтус подрезать по месту в местах стыковки с дверями и мебелью.
- Внутреннее наполнение мебели разработать со специалистами.
- Серым/синим цветом показаны размеры мебели. Мебель разработать со специалистами, размеры уточнить после выполнения чистовой отделки.

МСК 392.12.25-ЭП ПРЕМИУМ			
Эскизный дизайн-проект интерьера квартиры в г. Москва ЖК "Остров", ул. Нижние Мневники д. 7			
Спальня №1Развертки стен Д-01, Д-02.			
Дизайнер интерьера №1 Александр Батеньков	Стадия	Лист	Листов
	ЭП	70	120
		Подп.	Дата
ГАП	Батеньков А.С.		
Гл. дизайнер	Власова В.А.		
Гл. проектиров.	Луныкова В.Н.		
Разработал	Ильина Е.Е.		

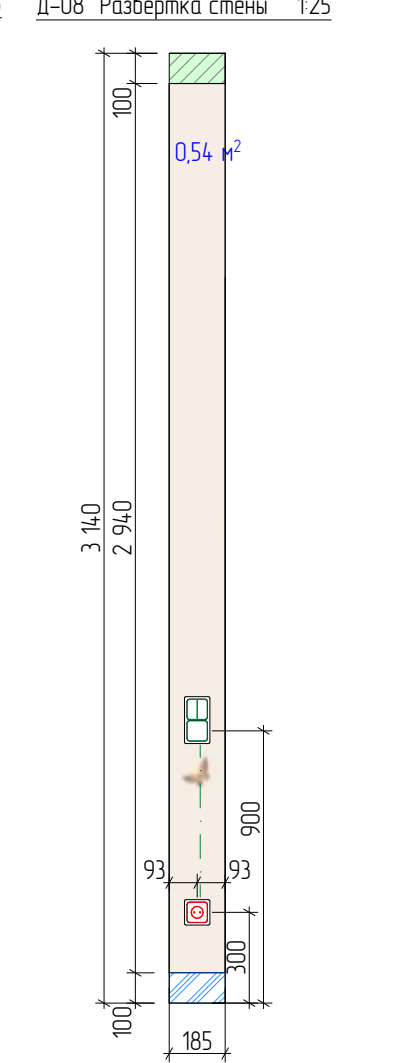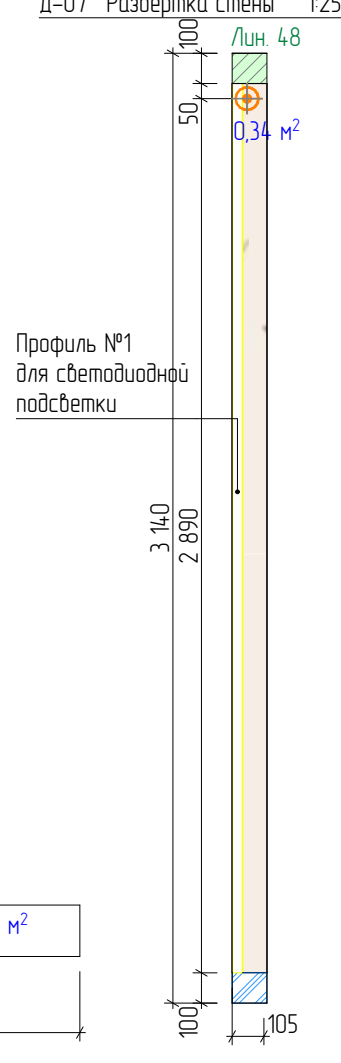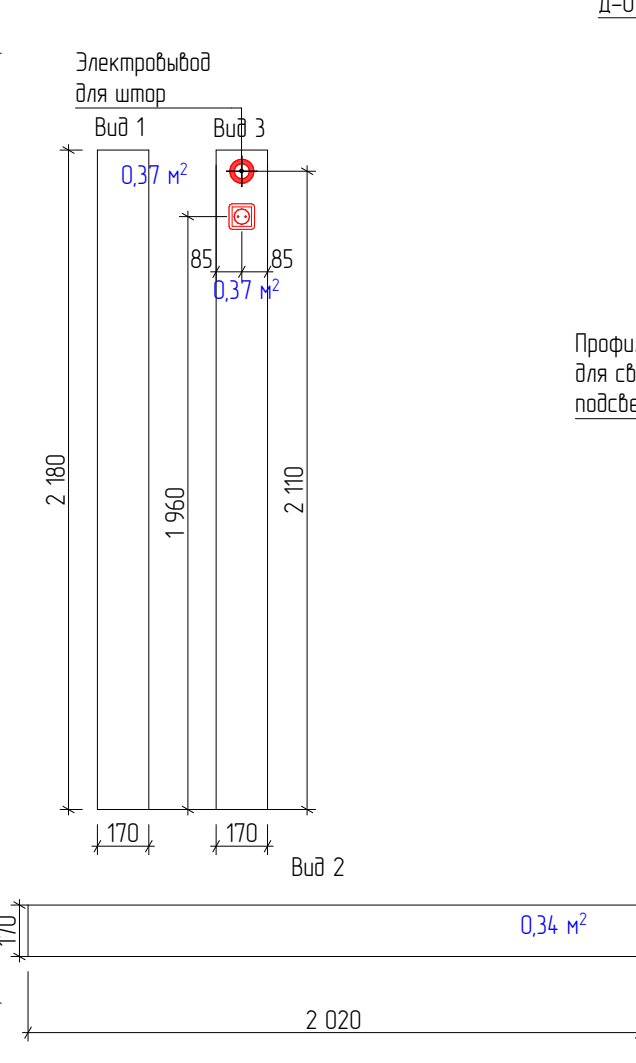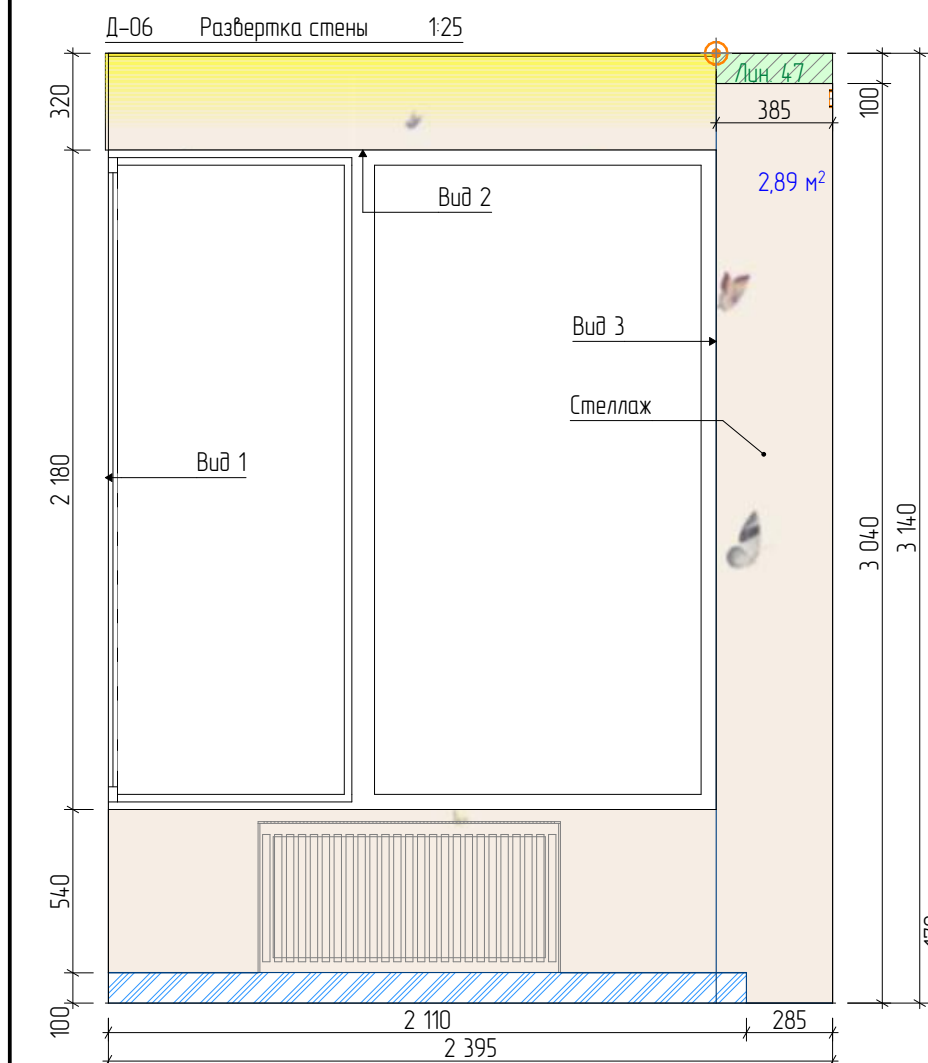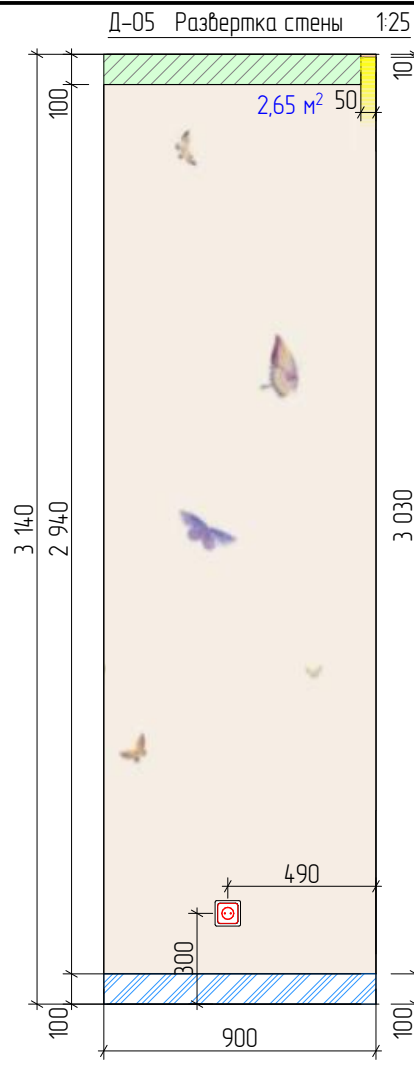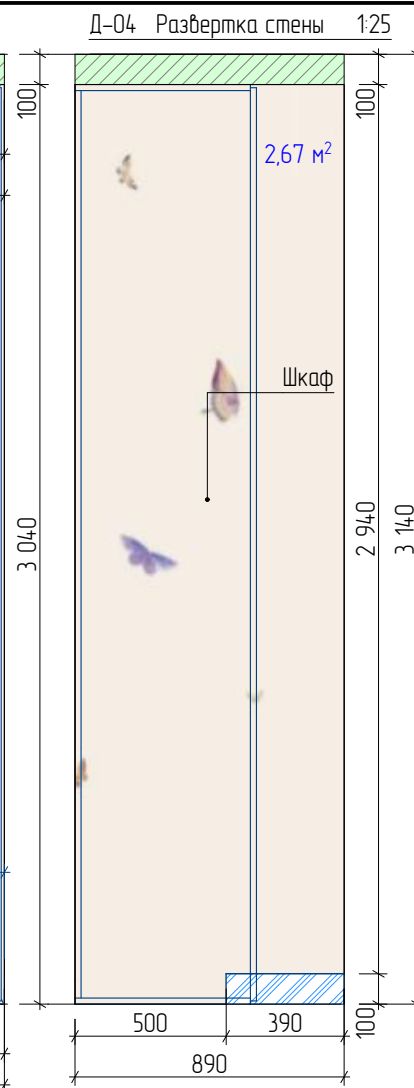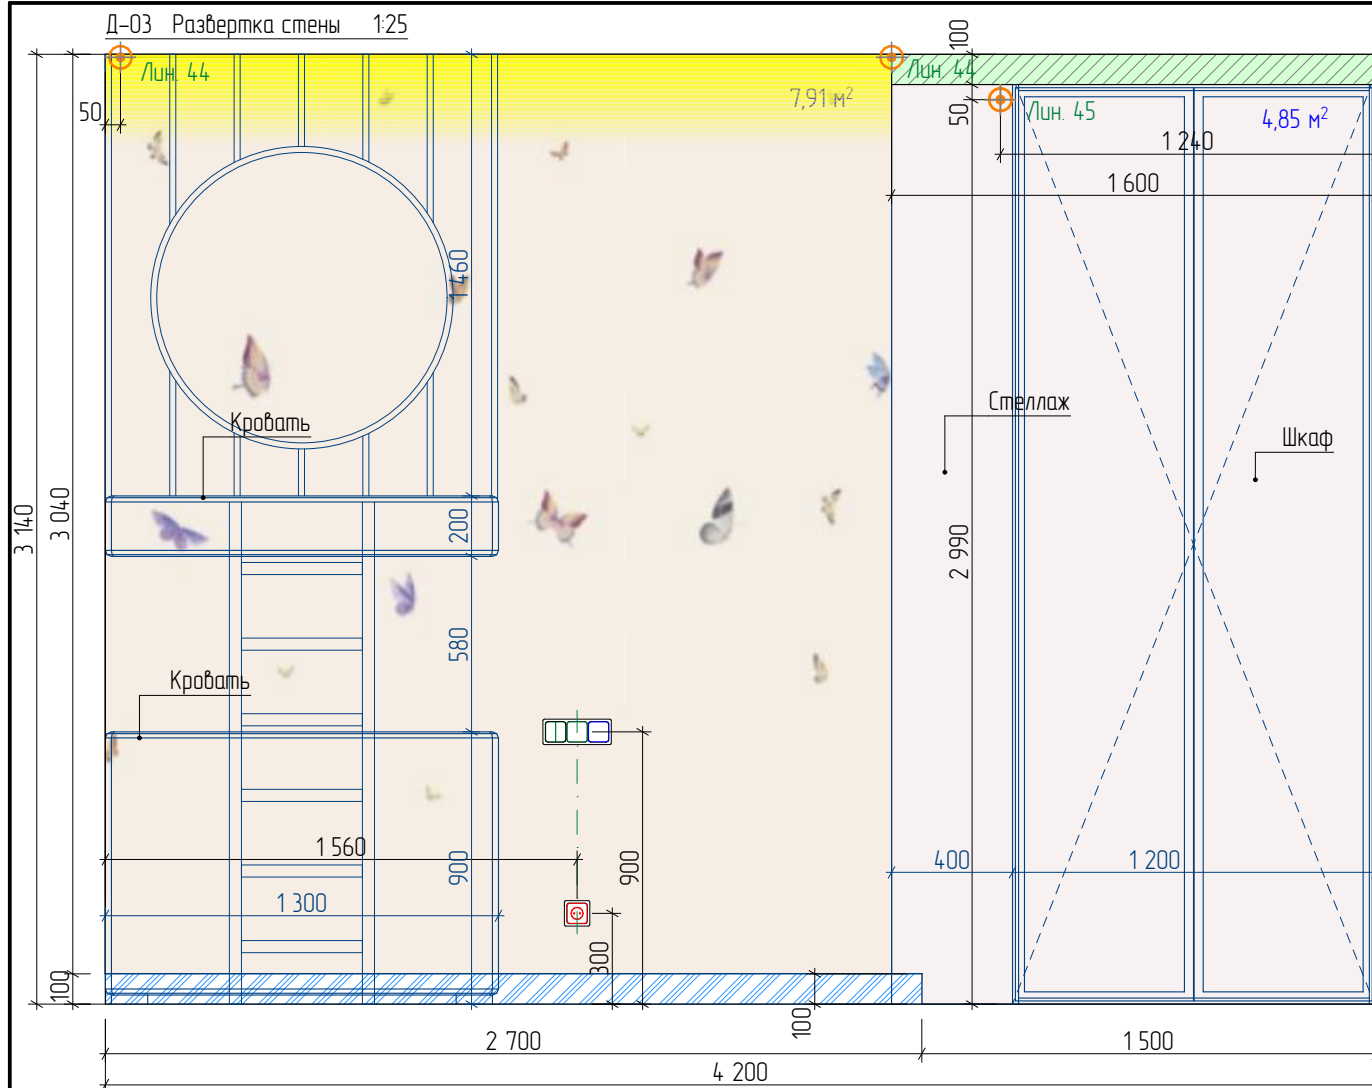

Примечания:

1. * – размеры уточнить по месту после выполнения черновых отделочных работ.
2. Выключатели располагать от уровня чистого пола на высоте 900 мм. Исключения указаны на чертеже.
3. Розетки располагать от уровня чистого пола на высоте 300 мм. Исключения указаны на чертеже.
4. Оконные откосы оклеить строительным флизелином и окрасить в белый цвет. Уточнить по месту.
5. Размещение выводов для отопления согласовать со специалистами.
6. Цвет окрашивания плитуса уточнить после согласования образца.
7. Плитус подрезать по месту в местах стыковки с дверями и мебелью.
8. Внутреннее наполнение мебели разработать со специалистами.
9. Серым/синим цветом показаны размеры мебели. Мебель разработать со специалистами, размеры уточнить после выполнения чистовой отделки.

Условные обозначения:

- | | |
|---|---|
|  | Покраска №1. Выполнить по подготовленной поверхности (стеклохолст*). Цвет при выборе образца (бежевый*). |
|  | Обои №1. Обои ручной работы. Изготовитель: fresq, кол-я: CLASSIC, арт.: EN.01. Размер, цвет и фактура при выборе образца. |
|  | Покраска №2. Выполнить по подготовленной поверхности (стеклохолст*). Цвет при выборе образца (белый*). |
|  | Плинтус №1. Теневой плинтус скрытого монтажа с МДФ вставкой. Теневой зазор от пола 100 мм. Цвет при выборе образца (в цвет стен). |
|  | Монтаж конструкций из ГКБ/Л |

-  Розетка 220 V
-  Выключатель одноклавишный
-  Переключатель одноклавишный
-  Переключатель двухклавишный
-  Вывод 220 V
-  Вывод электрокабеля для светодиодной ленты

МСК 392.12.25-ЭП ПРЕМИУМ			
Эскизный дизайн-проект интерьера к/квартиры в г. Москва ЖК "Остров", ул. Нижние Мневники д. 7			
Спальня №1 Развертки стен Д-03, Д-04, Д-05, Д-06, Д-07, Д-08.			
Дизайнер интерьера  №1 Александр Батеньков	Стандия	Лист	Листов
	ЭП	71	120
		Подп.	Дата
ГАП	Батеньков А.С.		
Гл. дизайнер	Власова В.А.		
Гл. проектиров.	Луныкова В.Н.		
Разработал	Ильина Е.Е.		

Ведомость отделочных материалов.

№	Обозначение	Наименование	Кол-во	Примечание
Пол:				
1		Покрытие №01. Паркет. Изготовитель: Lab Arte, кол-я: Angle Дуб Натур, размер: 500x150 мм, точный артикул и производителя уточнить при выборе образца, толщину уточнить при закупа..	15,89	м²
Стены:				
2		Плинтус №1. Теневой плинтус скрытого монтажа с МДФ вставкой. Теневой зазор от пола 100 мм. Цвет при выборе образца (в цвет стен).	10,92	м.п.
3		Обои №1. Обои ручной работы. Изготовитель: fresq, кол-я: CLASSIC, арт.: EN.01. Размер, цвет и фактура при выборе образца.	31,92	м²
4		Покраска №1. Выполнить по подготовленной поверхности (стеклохолст*). Цвет при выборе образца (бежевый*).	8,90	м²
5		МДФ панель №3. 3Д панель. Цвет и фактура при выборе образца (в цвет мебели*).	4,56	м²
6		Зеркало №2. Разработать со специалистами (стандарт*) размеры и резка по чертежу.	2,35	м²
Откосы:				
7		Покраска №2. Выполнить по подготовленной поверхности (стеклохолст*). Цвет при выборе образца (белый*).	1,08	м²
Подоконник:				
8		Подоконник №1. Искусственный камень. Цвет при выборе образца.	0,39	м²


МСК 392.12.25–ЭП ПРЕМИУМ			
Эскизный дизайн–проект интерьера квартиры в г. Москва ЖК “Остров”, ул. Нижние Мневники д. 7			
Спальня №1Ведомость отделочных материалов.			
Дизайнер интерьера  №1 Александр Батеньков	Стадия	Лист	Листов
	ЭП	72	120
		Подп.	Дата
ГАП	Батеньков А.С.		
Гл. дизайнер	Власова В.А.		
Гл. проектиров.	Луцькова В.Н.		
Разработал	Ильина Е.Е.		



МСК 392.12.25-ЭП ПРЕМИУМ			
Эскизный дизайн-проект интерьера квартиры в г. Москва ЖК "Остров", ул. Нижние Мневники д. 7			
Спальня №2 Видовые точки.			
Дизайнер интерьера  Александр Батеньков	Стадия	Лист	Листов
	ЭП	73	120
		Подп.	Дата
ГАП	Батеньков А.С.		
Гл. дизайнер	Власова В.А.		
Гл. проектиров.	Луныкова В.Н.		
Разработал	Ильина Е.Е.		



МСК 392.12.25-ЭП ПРЕМИУМ			
Эскизный дизайн-проект интерьера квартиры в г. Москва ЖК "Остров", ул. Нижние Мневники д. 7			
Спальня №2 Видовые точки.			
Дизайнер интерьера №1 Александр Батеньков	Стадия	Лист	Листов
	ЭП	74	120
		Подп.	Дата
ГАП	Батеньков А.С.		
Гл. дизайнер	Власова В.А.		
Гл. проектиров.	Луныкова В.Н.		
Разработал	Ильина Е.Е.		

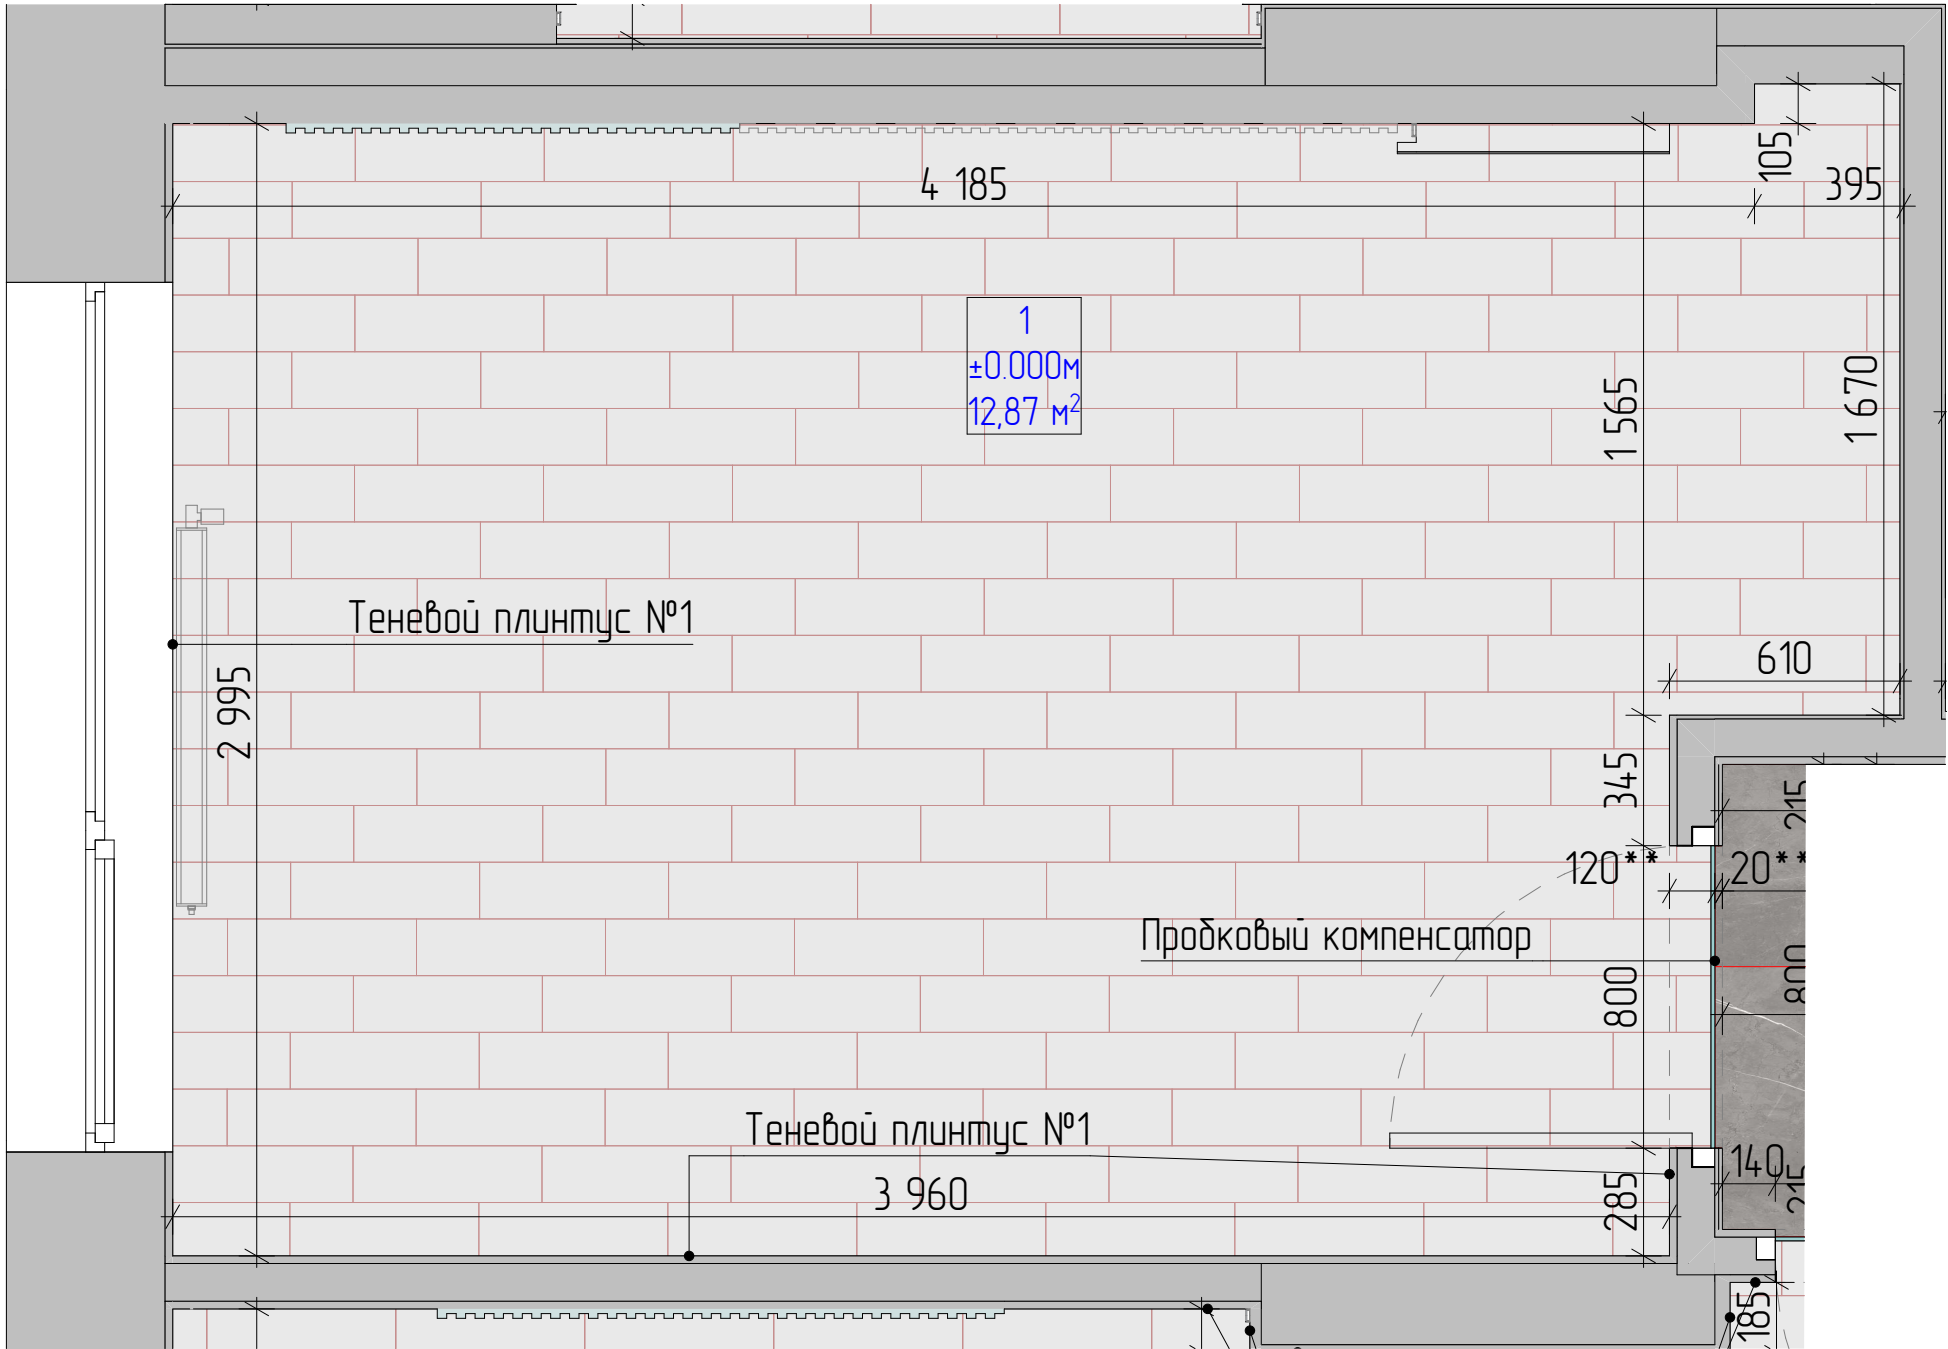

Условные обозначения:


- Направление и начало укладки
- Пробковый компенсатор

1 Покрытие №01. Паркет. Изготовитель: Lab Arte, кол-я: Angle Дуб Намур, размер: 500x150 мм, точный артикул и производителя уточнить при выборе образца, толщину уточнить при заказе.

Примечания:

- *- размеры уточнить по месту после выполнения черновых отделочных работ.
- За отметку ±0,000 принят уровень чистого пола.
- При монтаже напольных покрытий уточнить необходимость устройства дверных проемов с порогом.
- *- размеры уточнить по месту после выполнения черновых отделочных работ и установки дверей со скрытой коробкой.
- ** -размер уточнить по месту в зависимости от точного расположения полотна двери, стыковка двух разных напольных покрытий должна проходить точно по центру вдоль дверного полотна.

МСК 392.12.25-ЭП ПРЕМИУМ			
Эскизный дизайн-проект интерьера квартиры в г. Москва ЖК "Остров", ул. Нижние Мневники д. 7			
Спальня №2.План отделки пола.			
Дизайнер интерьера  №1 Александр Батеньков	Стадия	Лист	Листов
	ЭП	75	120
		Подп.	Дата
ГАП	Батеньков А.С.		
Гл. дизайнер	Власова В.А.		
Гл. проектиров.	Луныкова В.Н.		
Разработал	Ильина Е.Е.		

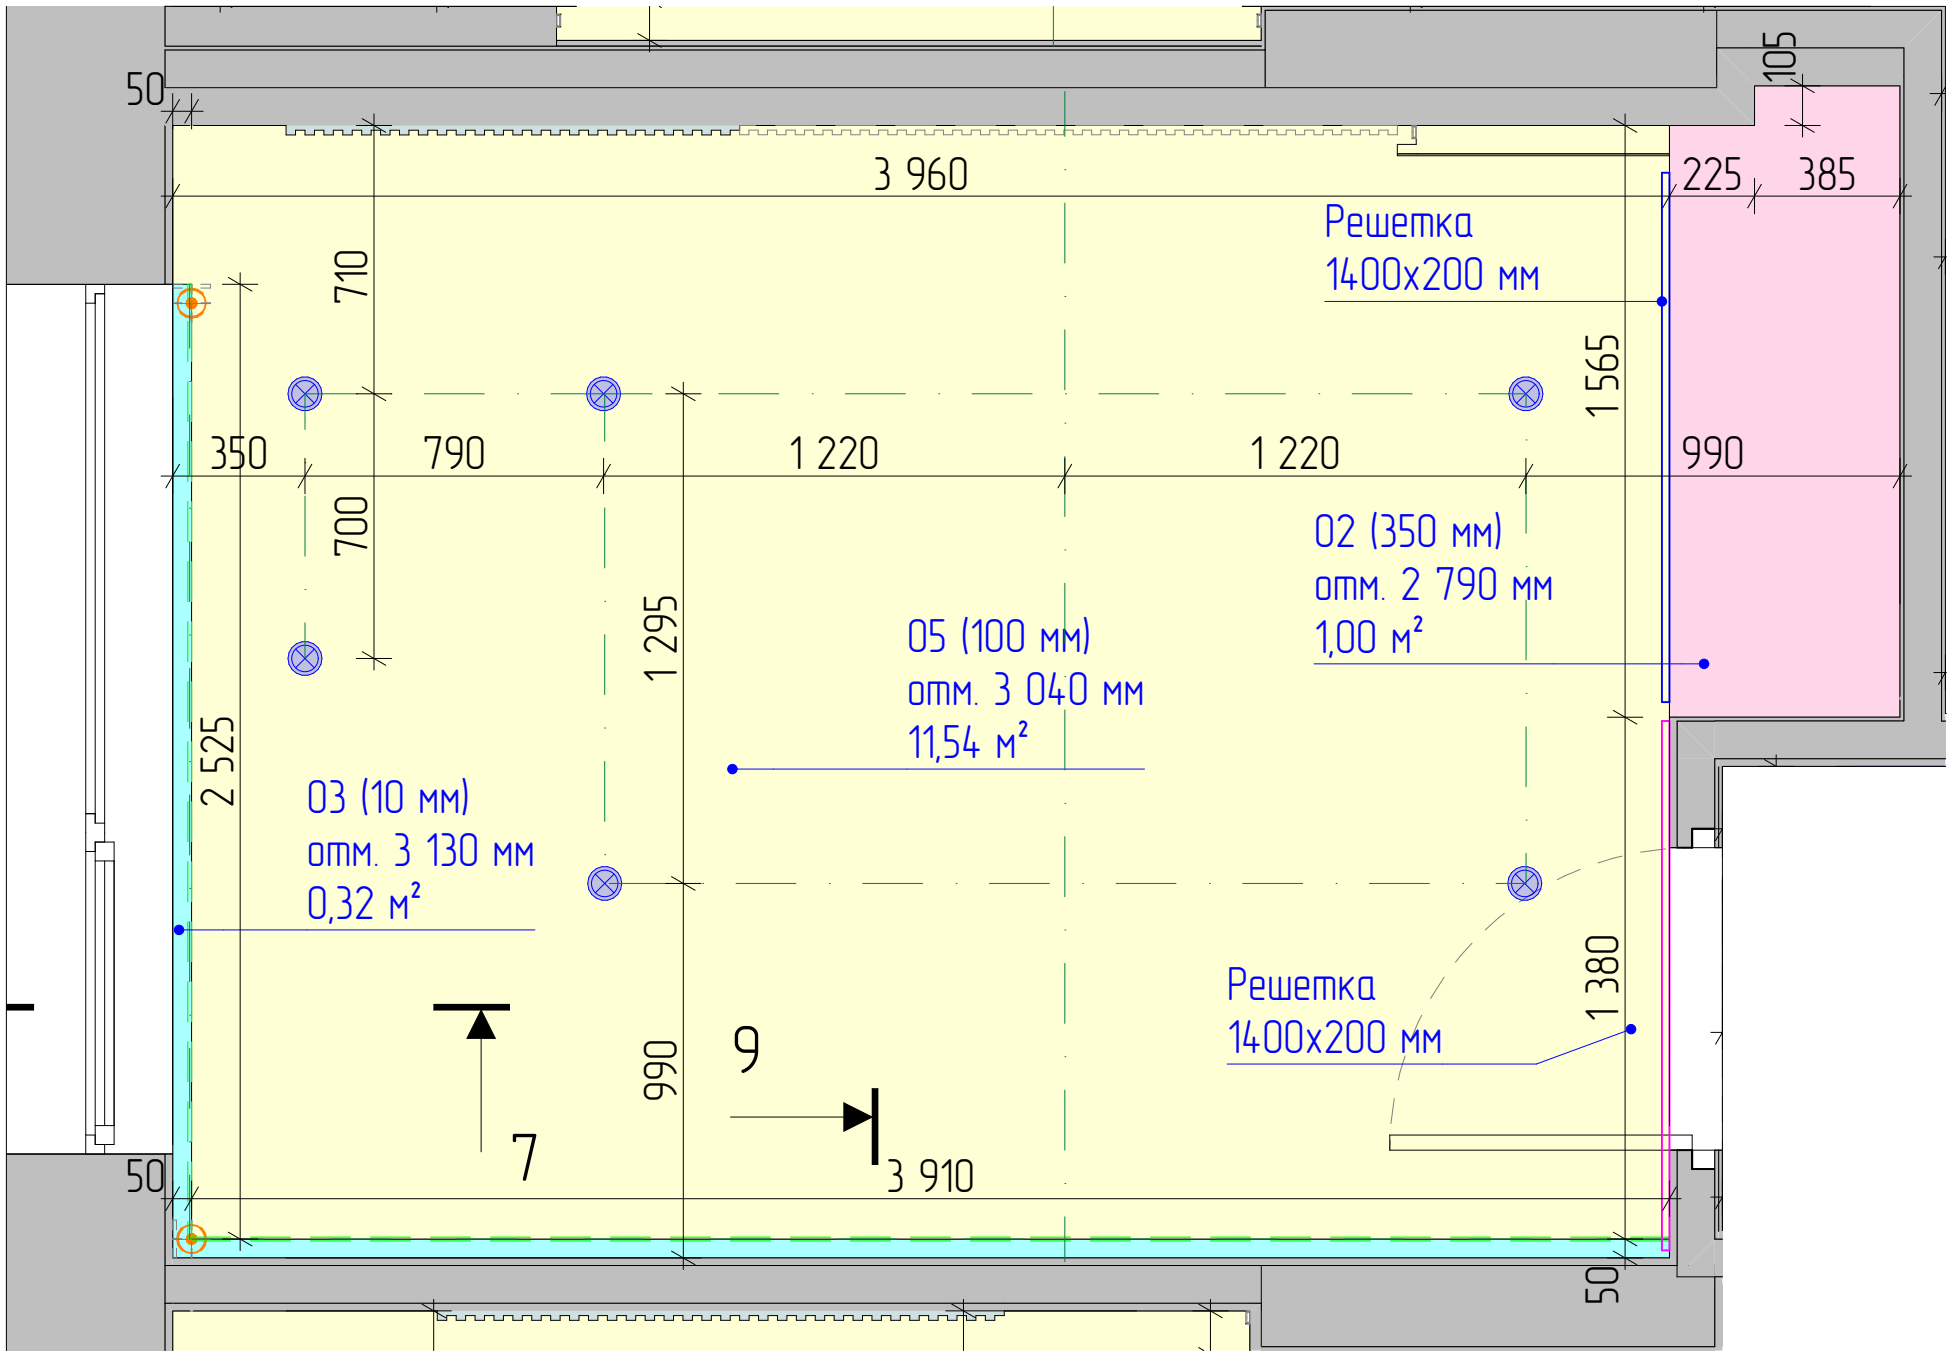


- Условные обозначения:
- Выход 220V
 - Выход электрокабеля для светодиодной ленты
 - Светильник точечный встраиваемый
 - Светодиодная лента

- Примечания:
- * – размеры уточнить по месту после выполнения черновых работ.
 - Выполнить уровни потолка из влагостойкого ГКЛ для предотвращения деформации потолка при затоплении.
 - Высоту уровней потолка отсчитывать от существующей ж/б плиты перекрытия помещения.
 - Шумоизоляцию разработать со специалистами, уточнить состав и толщину слоев шумоизоляционных материалов. Уточнить необходимость устройства с заказчиком.

Условные потолки				
№	Обозначение	Опуск	Примечания	Площадь м2
02		350	Потолок ГК/ЛВ. Окрасить в цвет выбранного образца (белый) по армирующему материалу (стеклохолст "паутинка").	1,00
05		100	Потолок ГК/ЛВ. Окрасить в цвет выбранного образца (белый) по армирующему материалу (стеклохолст "паутинка").	11,54
06		300	Потолок ГК/ЛВ. Окрасить в цвет выбранного образца (белый) по армирующему материалу (стеклохолст "паутинка").	0,32

МСК 392.12.25–ЭП ПРЕМИУМ			
Эскизный дизайн–проект интерьера квартиры в г. Москва ЖК "Остров", ул. Нижние Мневники д. 7			
Спальня №2.План отделки потолка.			
Дизайнер интерьера №1 Александр Батеньков	Стадия	Лист	Листов
	ЭП	76	120
		Подп.	Дата
ГАП	Батеньков А.С.		
Гл. дизайнер	Власова В.А.		
Гл. проектиров.	Лунькова В.Н.		
Разработал	Ильина Е.Е.		

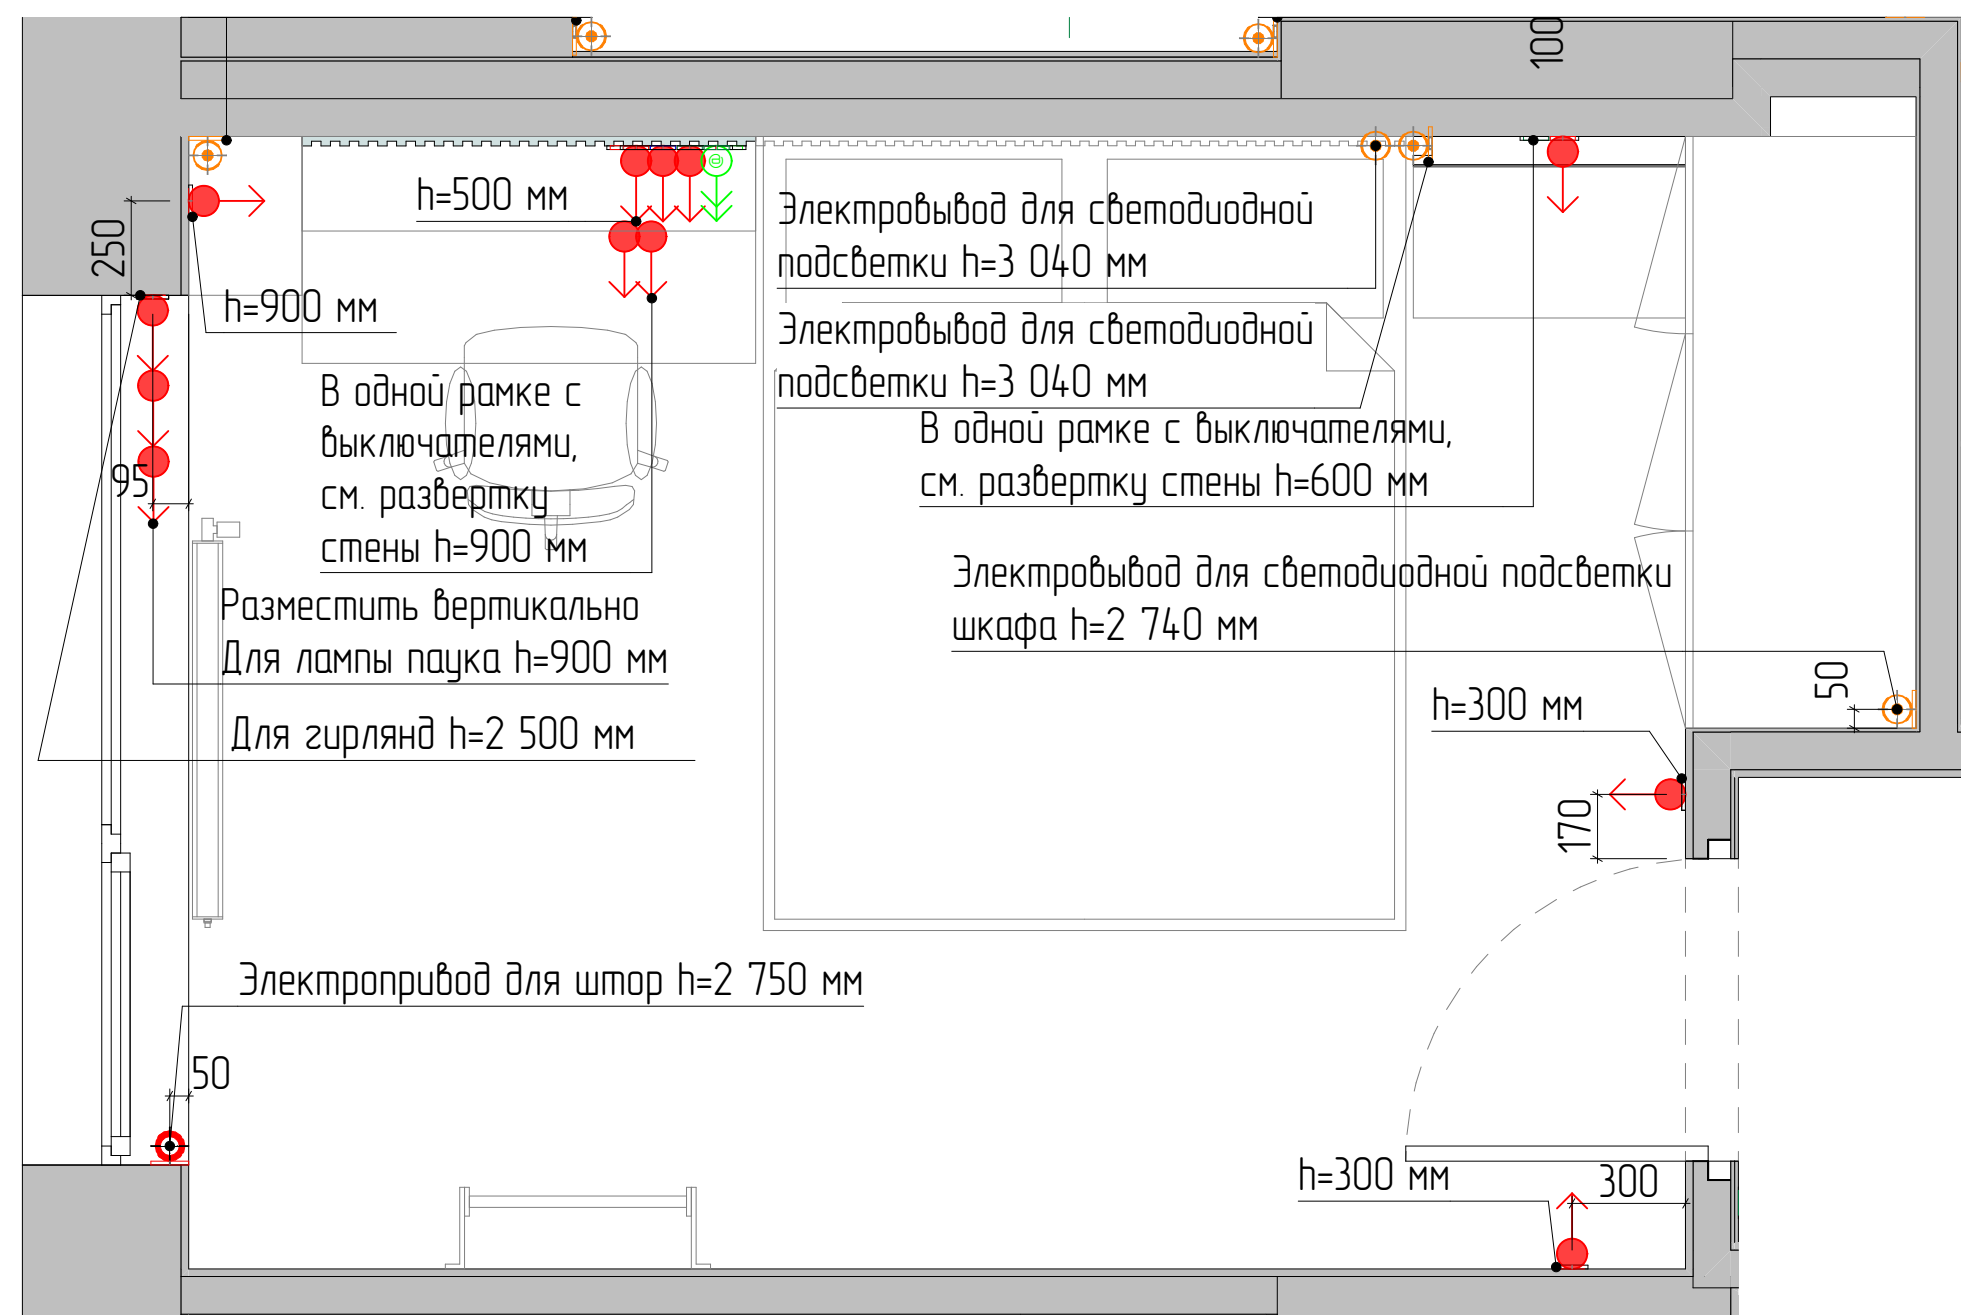


Условные обозначения:

- ←● Розетка 220V
- ⊕ Вывод электрокабеля для светодиодной ленты
- ⊗ Вывод электрокабеля для варочной поверхности
- ⊕ Вывод 220V

Примечания:

- * – размеры уточнить по месту.
- Розетки располагать от уровня чистого пола на высоте 0,300 м. Исключения указаны на чертеже.
- Размещение всех выводов и розеток согласовать со специалистами «Умный дом».
- Размеры и характеристики радиаторов отопления согласовать со специалистами, предусмотреть терморегуляторы.
- Датчики пожарной и охранной сигнализации и электровыводы для них разместить совместно со специалистами, предварительно вызвав их на объект.
- Размещение розеток и электровыводов по высоте см. на развертках стен.



МСК 392.12.25–ЭП ПРЕМИУМ			
Эскизный дизайн–проект интерьера квартиры в г. Москва ЖК "Остров", ул. Нижние Мневники д. 7			
Спальня №2. План размещения электрооборудования.			
Дизайнер интерьера №1  Александр Батеньков	Стадия	Лист	Листов
	ЭП	77	120
		Подп.	Дата
ГАП	Батеньков А.С.		
Гл. дизайнер	Власова В.А.		
Гл. проектиров.	Луцькова В.Н.		
Разработал	Ильина Е.Е.		

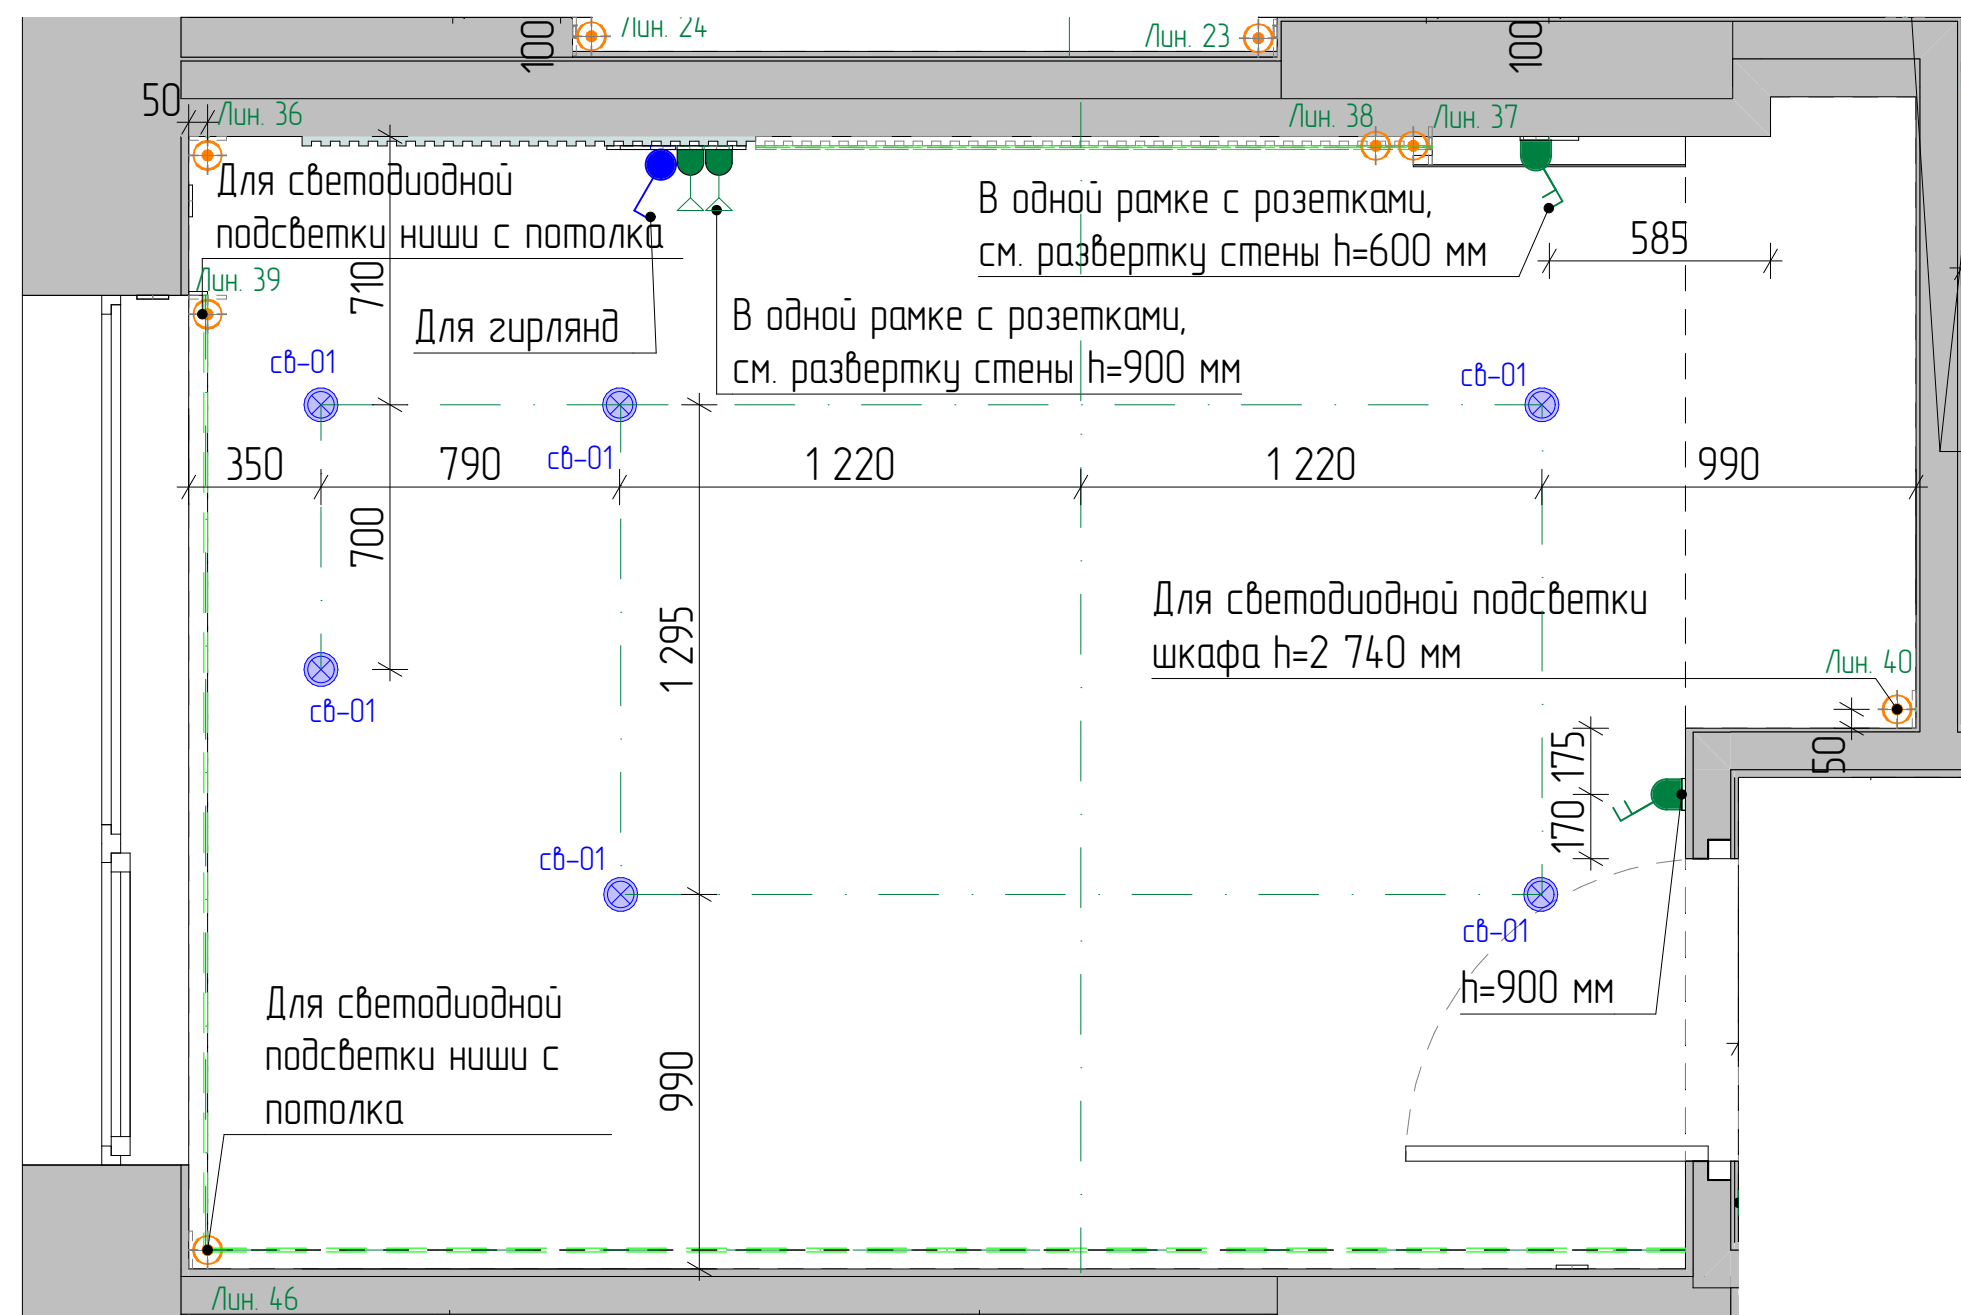

- Условные обозначения:
- Вывод 220V
 - Вывод электрокабеля для светодиодной ленты
 - Выключатель одноклавишный
 - Переключатель двухклавишный
 - Переключатель одноклавишный переходной
 - Светильник точечный встраиваемый
 - Светодиодная лента

- Примечания:
- * – размеры уточнить по месту.
 - Выключатели располагать от уровня чистого пола на высоте 0,900 м. Исключения указаны на чертеже.
 - Светильники, встраиваемые в мебель, согласовать с изготовителями мебели.

МСК 392.12.25-ЭП ПРЕМИУМ			
Эскизный дизайн-проект интерьера квартиры в г. Москва ЖК "Остров", ул. Нижние Мневники д. 7			
Спальня №2. План размещения освещения и выключателей.			
Дизайнер интерьера №1 Александр Батеньков	Стадия	Лист	Листов
	ЭП	78	120
		Подп.	Дата
ГАП	Батеньков А.С.		
Гл. дизайнер	Власова В.А.		
Гл. проектиров.	Луцькова В.Н.		
Разработал	Ильина Е.Е.		

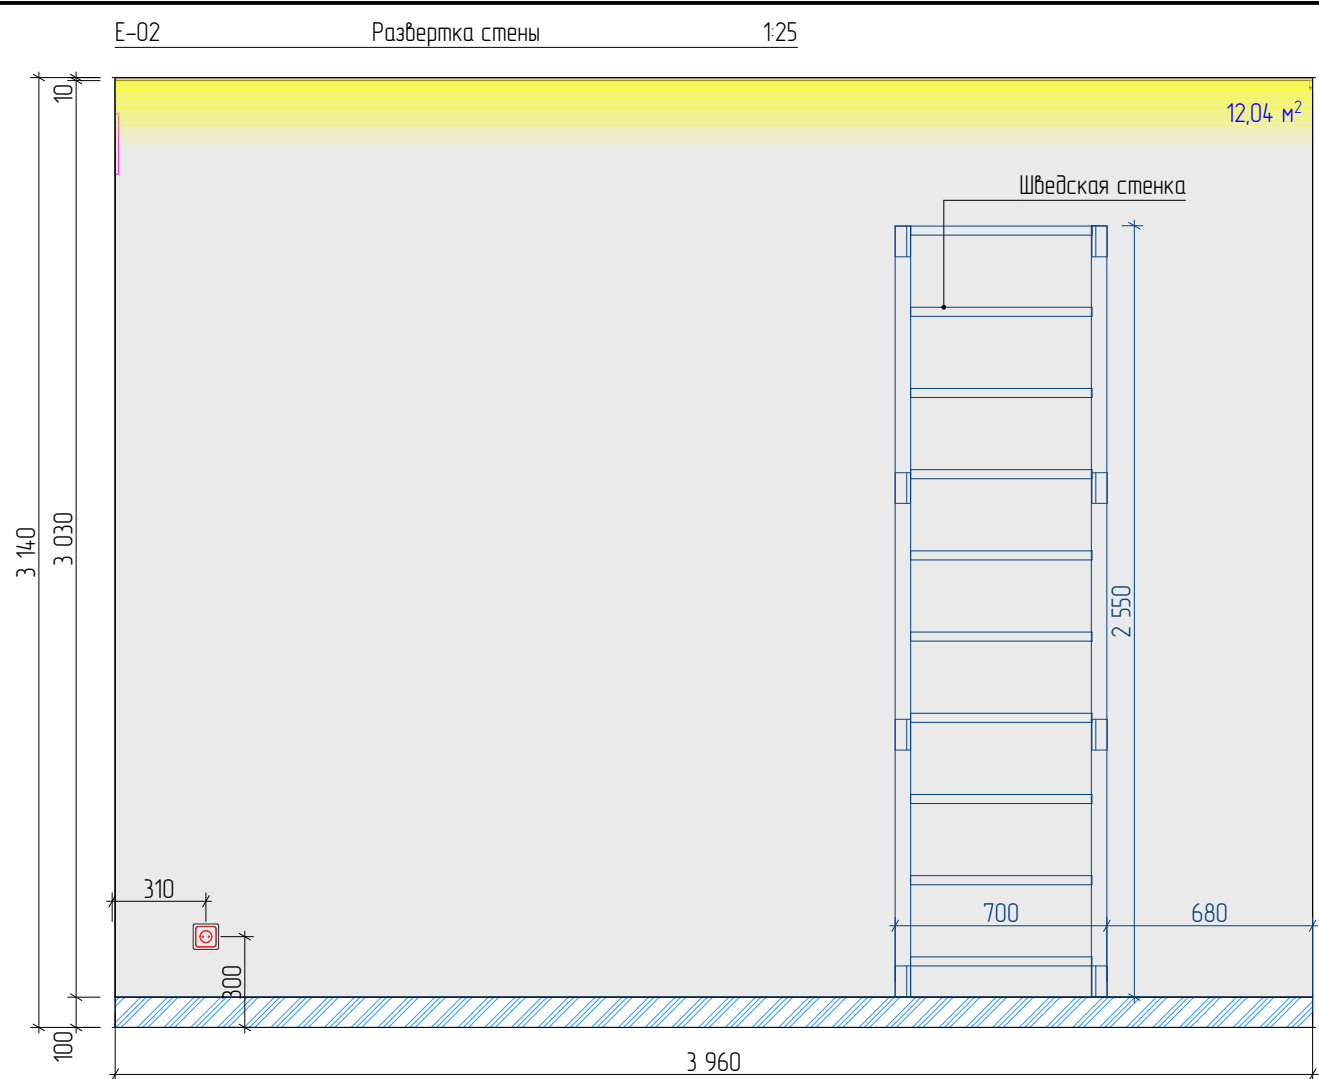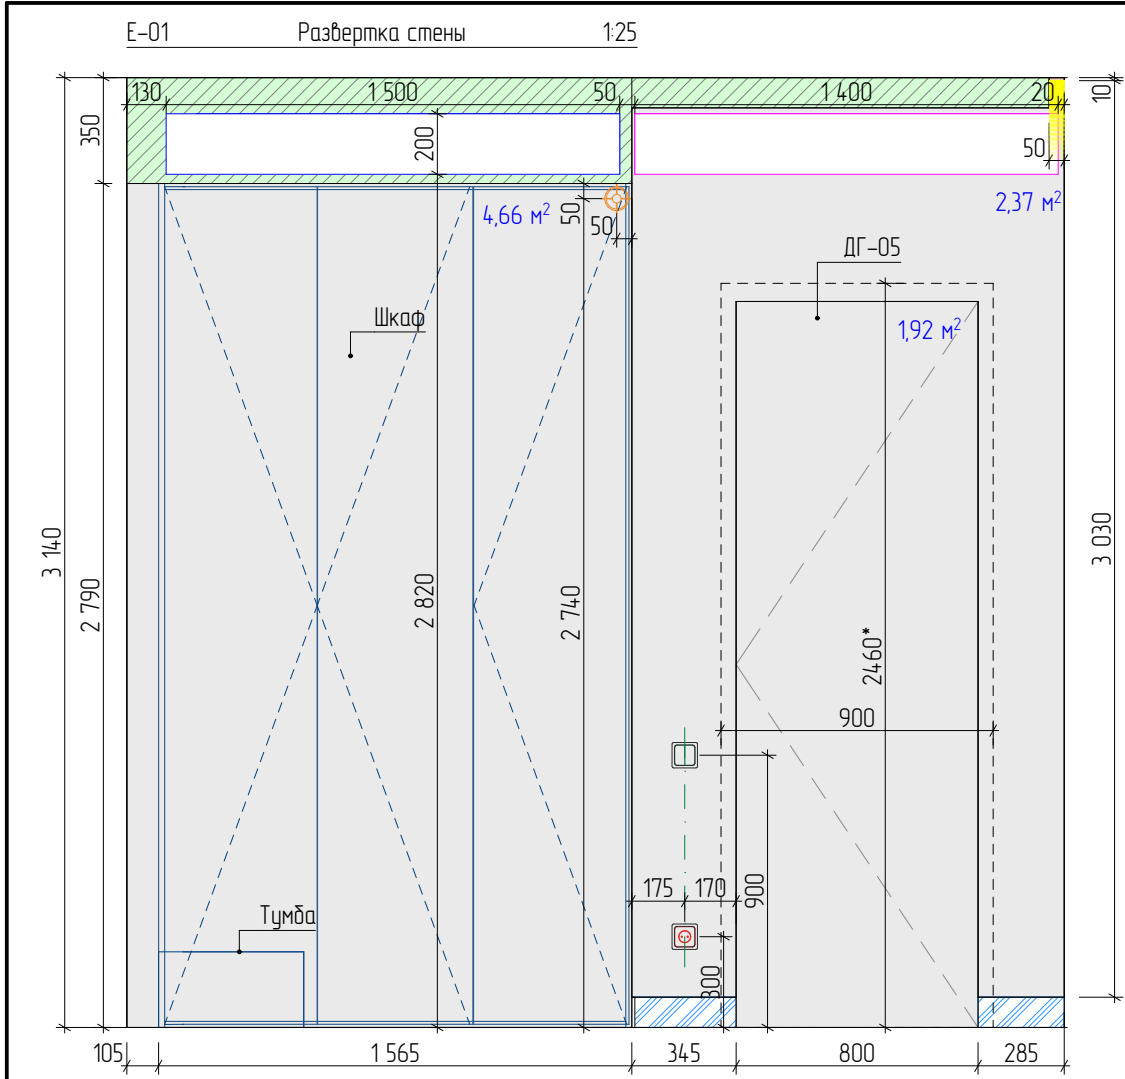



Условные обозначения:

- Плинтус №1. Теневой плинтус скрытого монтажа с МДФ вставкой. Теневой зазор от пола 100 мм. Цвет при выборе образца (в цвет стен).
- Монтаж конструкций из ГКВЛ
- Покраска №4. Выполнить по подготовленной поверхности (стеклохолст*). Цвет при выборе образца (светло серый*).
- Розетка 220 V
- Переключатель двухклавишный

Примечания:

- * - размеры уточнить по месту после выполнения черновых отделочных работ.
- Выключатели располагать от уровня чистого пола на высоте 900 мм. Исключения указаны на чертеже.
- Розетки располагать от уровня чистого пола на высоте 300 мм. Исключения указаны на чертеже.
- Цвет окрашивания плинтуса уточнить после согласования образца.
- Высоту проемов выполнить 2460 мм от уровня чистого пола. Уточнить после подбора и согласования модели дверей.
- Плинтус подрезать по месту в местах стыковки с дверями и мебелью.
- Внутреннее наполнение мебели разработать со специалистами.
- Серым/синим цветом показаны размеры мебели. Мебель разработать со специалистами, размеры уточнить после выполнения чистовой отделки.

МСК 392.12.25-ЭП ПРЕМИУМ			
Эскизный дизайн-проект интерьера квартиры в г. Москва ЖК "Остров", ул. Нижние Мневники д. 7			
Спальня №2. Развертки стен Е-01, Е-02.			
Дизайнер интерьера №1  Александр Батеньков	Стадия	Лист	Листов
	ЭП	79	120
		Подп.	Дата
ГАП	Батеньков А.С.		
Гл. дизайнер	Власова В.А.		
Гл. проектиров.	Луцькова В.Н.		
Разработал	Ильина Е.Е.		

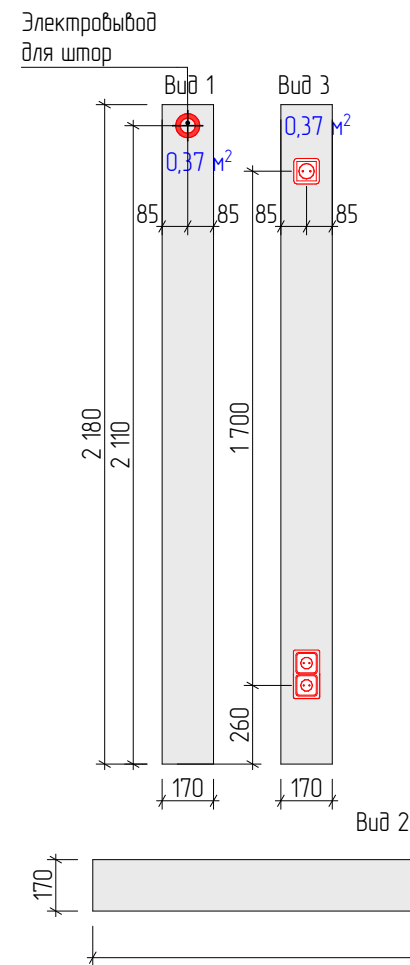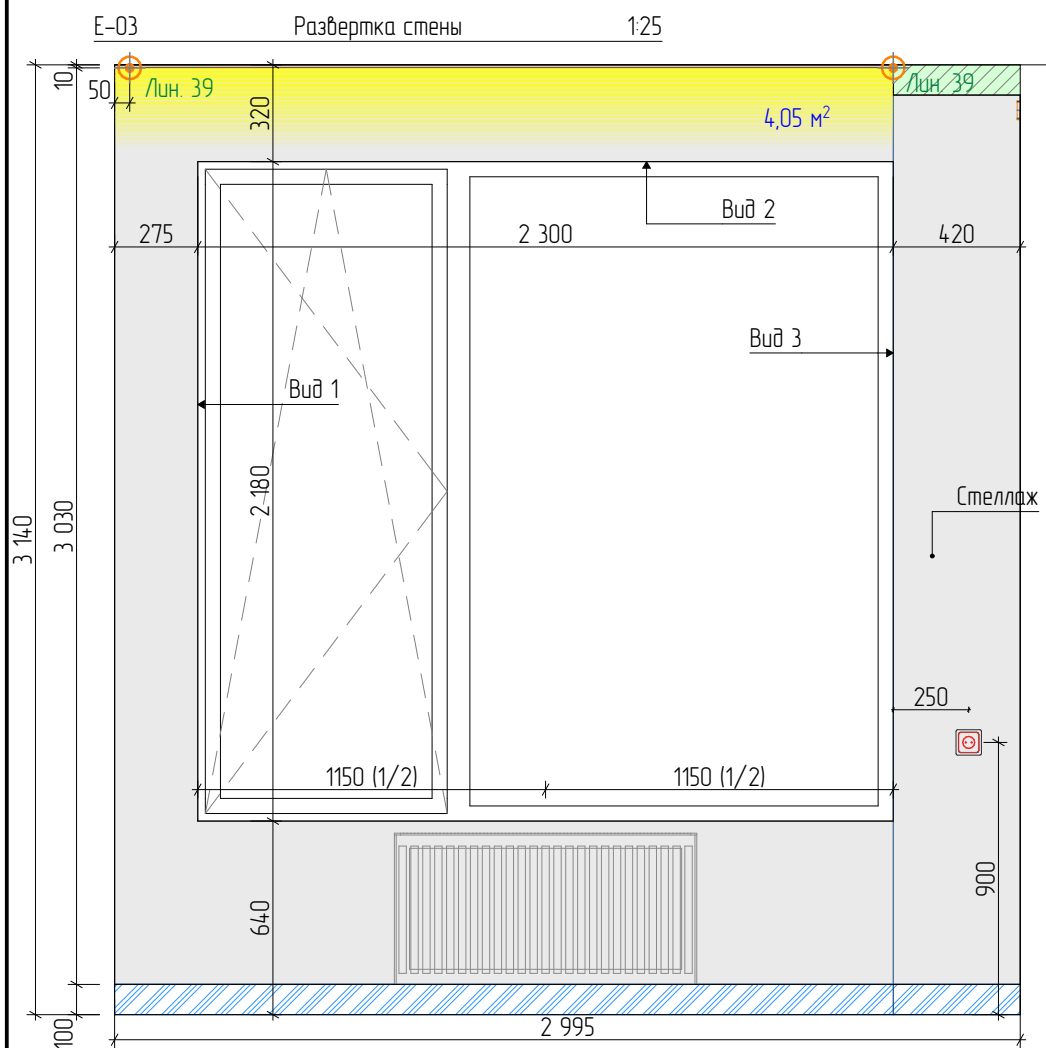


Примечания:


- * – размеры уточнить по месту после выполнения черновых отделочных работ.
- Выключатели располагать от уровня чистого пола на высоте 900 мм. Исключения указаны на чертеже.
- Разетки располагать от уровня чистого пола на высоте 300 мм. Исключения указаны на чертеже.
- Оконные откосы оклеить строительным флизелином и окрасить в белый цвет. Уточнить по месту.
- Размещение выводов для отопления согласовать со специалистами.
- Цвет окрашивания плинтуса уточнить после согласования образца.
- Резку зеркала решить по месту авторским надзором.
- Плинтус подрезать по месту в местах стыковки с дверями и мебелью.
- Внутреннее наполнение мебели разработать со специалистами.
- Серым/синим цветом показаны размеры мебели. Мебель разработать со специалистами, размеры уточнить после выполнения чистовой отделки.

Условные обозначения:


- Плинтус №1. Теневой плинтус скрытого монтажа с МДФ вставкой. Теневой зазор от пола 100 мм. Цвет при выборе образца (в цвет стен).
- Монтаж конструкций из ГКВЛ
- Зеркало №2. Разработать со специалистами (стандарт*) размеры и резка по чертежу.
- Покраска №4. Выполнить по подготовленной поверхности (стеклохолст*). Цвет при выборе образца (светло серый*).
- МДФ панель №3. 3Д панель. Цвет и фактура при выборе образца (в цвет мебели*).
- 3Д панель №1. 3Д панель с росписью. Выполнить по подготовленной поверхности (на заказ).
- Вывод 220 V
- Вывод электрокабеля для светодиодной ленты
- Разетка 220 V
- Интернет-розетка двойная
- Выключатель одноклавишный
- Переключатель одноклавишный переходной
- Переключатель двухклавишный

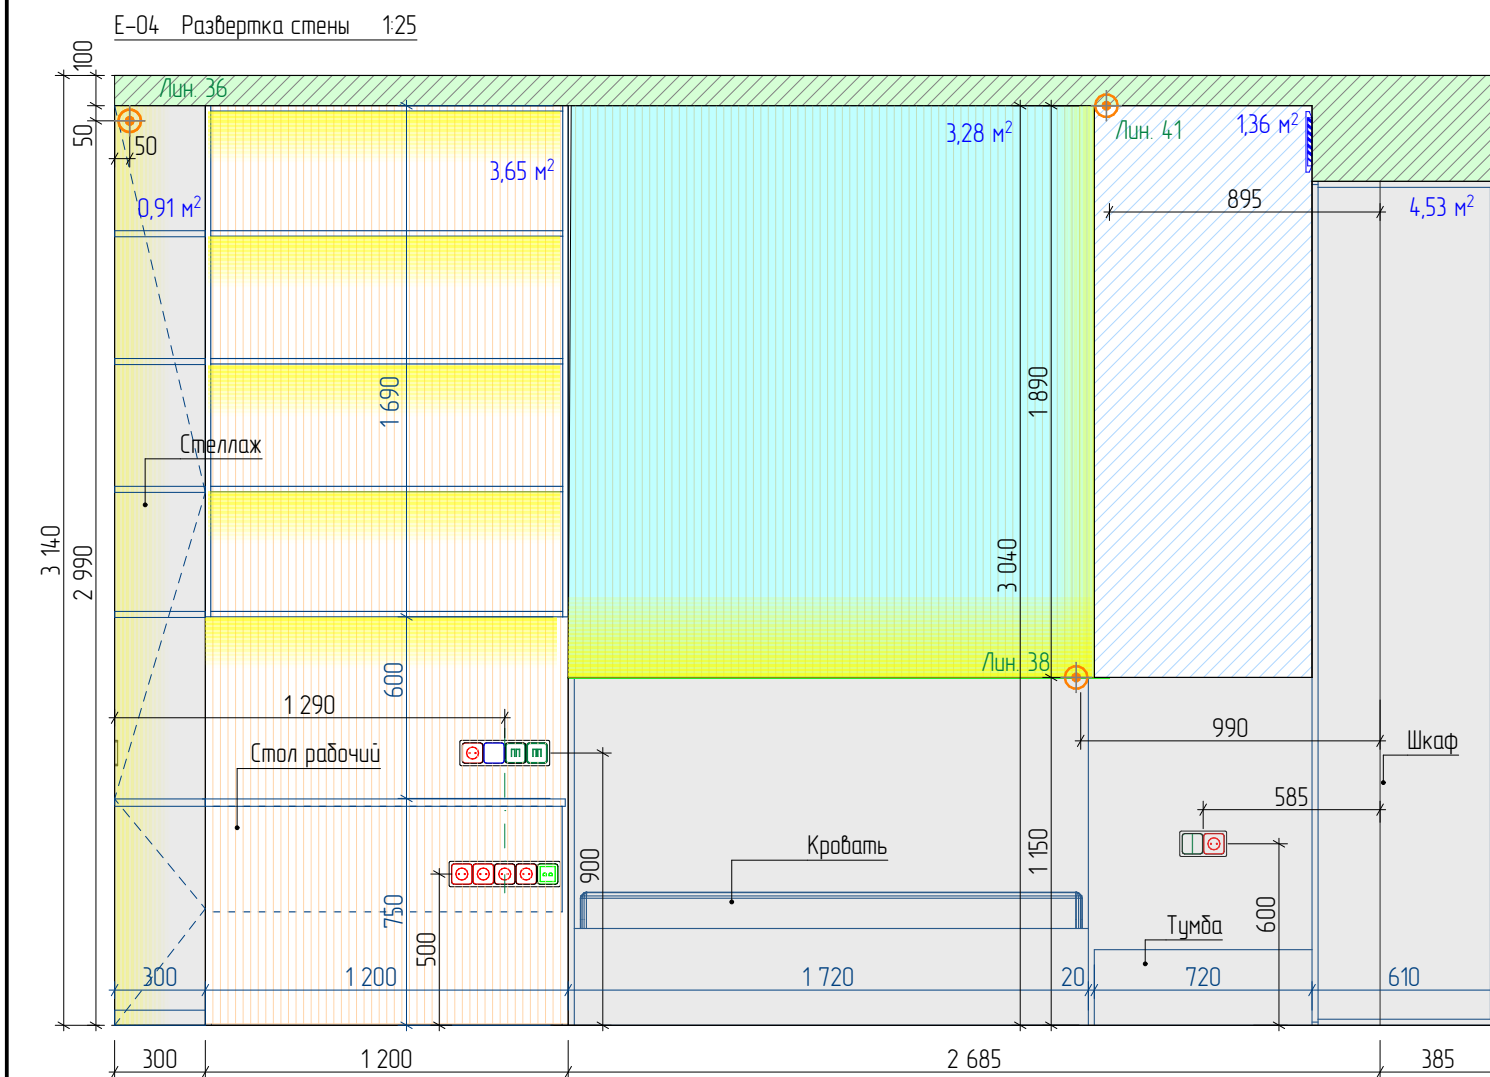

Е-05 Развертка стены 1:25

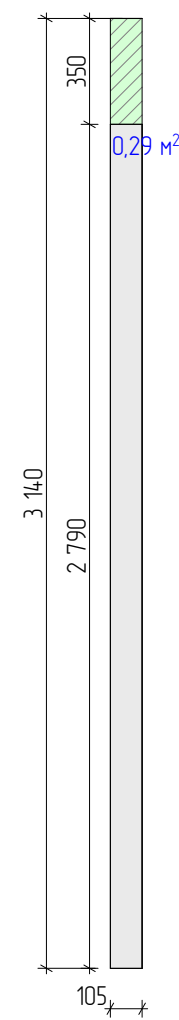

Е-06 Развертка стены 1:25

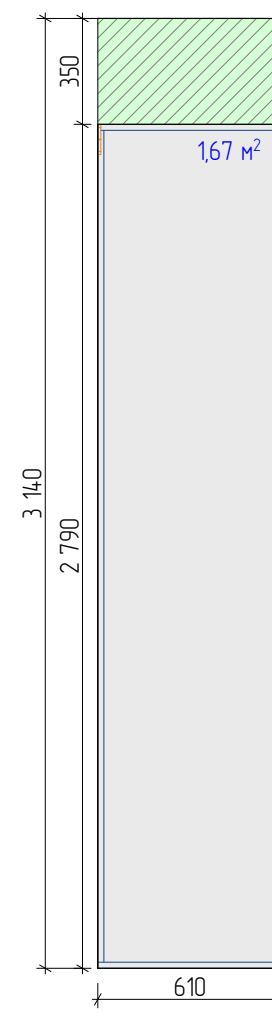

МСК 392.12.25-ЭП ПРЕМИУМ			
Эскизный дизайн-проект интерьера квартиры в г. Москва ЖК "Остров", ул. Нижние Мневники д. 7			
Спальня №2. Развертки стен Е-03, Е-04, Е-05, Е-06.			
Дизайнер интерьера №1 Александр Батеньков	Стадия	Лист	Листов
	ЭП	80	120
		Подп.	Дата
ГАП	Батеньков А.С.		
Гл. дизайнер	Власова В.А.		
Гл. проектиров.	Луныкова В.Н.		
Разработал	Ильина Е.Е.		

Ведомость отделочных материалов.

№	Обозначение	Наименование	Кол-во	Примечание
Пол:				
1		Покрытие №01. Паркет. Изготовитель: Lab Arte, кол-я: Angle Дуб Натур, размер: 500x150 мм, точный артикул и производителя уточнить при выборе образца, толщину уточнить при закупае..	12,87	м²
Стены:				
2		Плинтус №1. Теневой плинтус скрытого монтажа с МДФ вставкой. Теневой зазор от пола 100 мм. Цвет при выборе образца (в цвет стен).	7,59	м.п.
3		Покраска №4. Выполнить по подготовленной поверхности (стеклохолст*). Цвет при выборе образца (светло серый*).	27,78	м²
4		ЗД панель №1. Зд панель с росписью. Выполнить по подготовленной поверхности (на заказ).	3,28	м²
5		МДФ панель №3. ЗД панель. Цвет и фактура при выборе образца (в цвет мебели*).	3,65	м²
6		Зеркало №2. Разработать со специалистами (стандарт*) размеры и резка по чертежу.	1,36	м²
Откосы:				
7		Покраска №2. Выполнить по подготовленной поверхности. Цвет при выборе образца (белый*).	1,13	м²
Подоконник:				
8		Подоконник №1. Искусственный камень. Цвет при выборе образца.	0,34	м²

МСК 392.12.25–ЭП ПРЕМИУМ			
Эскизный дизайн–проект интерьера квартиры в г. Москва ЖК “Остров”, ул. Нижние Мневники д. 7			
Спальня №2.Ведомость отделочных материалов.			
Дизайнер интерьера  №1 Александр Батеньков	Стадия	Лист	Листов
	ЭП	81	120
		Подп.	Дата
ГАП	Батеньков А.С.		
Гл. дизайнер	Власова В.А.		
Гл. проектиров.	Луцькова В.Н.		
Разработал	Ильина Е.Е.		



МСК 392.12.25-ЭП ПРЕМИУМ			
Эскизный дизайн-проект интерьера квартиры в г. Москва ЖК "Остров", ул. Нижние Мневники д. 7			
Мастер спальни. Видовые точки.			
Дизайнер интерьера  Александр Батеньков	Стадия	Лист	Листов
	ЭП	82	120
		Подп.	Дата
ГАП	Батеньков А.С.		
Гл. дизайнер	Власова В.А.		
Гл. проектиров.	Луныкова В.Н.		
Разработал	Ильина Е.Е.		



МСК 392.12.25-ЭП ПРЕМИУМ			
Эскизный дизайн-проект интерьера квартиры в г. Москва ЖК "Остров", ул. Нижние Мневники д. 7			
Мастер спальня. Видовые точки.			
Дизайнер интерьера  Александр Батеньков	Стадия	Лист	Листов
	ЭП	83	120
		Подп.	Дата
ГАП	Батеньков А.С.		
Гл. дизайнер	Власова В.А.		
Гл. проектиров.	Луныкова В.Н.		
Разработал	Ильина Е.Е.		




МСК 392.12.25-ЭП ПРЕМИУМ			
Эскизный дизайн-проект интерьера квартиры в г. Москва ЖК "Остров", ул. Нижние Мневники д. 7			
Мастер спальня. Видовые точки.			
Дизайнер интерьера  №1 Александр Батеньков	Стадия	Лист	Листов
	ЭП	84	120
		Подп.	Дата
Г.АП	Батеньков А.С.		
Гл. дизайнер	Власова В.А.		
Гл. проектиров.	Луныкова В.Н.		
Разработал	Ильина Е.Е.		



МСК 392.12.25-ЭП ПРЕМИУМ			
Эскизный дизайн-проект интерьера квартиры в г. Москва ЖК "Остров", ул. Нижние Мневники д. 7			
Мастер спальня. Видовые точки.			
Дизайнер интерьера №1 Александр Батеньков	Стадия	Лист	Листов
	ЭП	85	120
		Подп.	Дата
ГАП	Батеньков А.С.		
Гл. дизайнер	Власова В.А.		
Гл. проектиров.	Луныкова В.Н.		
Разработал	Ильина Е.Е.		



МСК 392.12.25-ЭП ПРЕМИУМ			
Эскизный дизайн-проект интерьера квартиры в г. Москва ЖК "Остров", ул. Нижние Мневники д. 7			
Мастер спальни. Видовые точки.			
Дизайнер интерьера  Александр Батеньков	Стадия	Лист	Листов
	ЭП	86	120
		Подп.	Дата
ГАП	Батеньков А.С.		
Гл. дизайнер	Власова В.А.		
Гл. проектиров.	Луныкова В.Н.		
Разработал	Ильина Е.Е.		

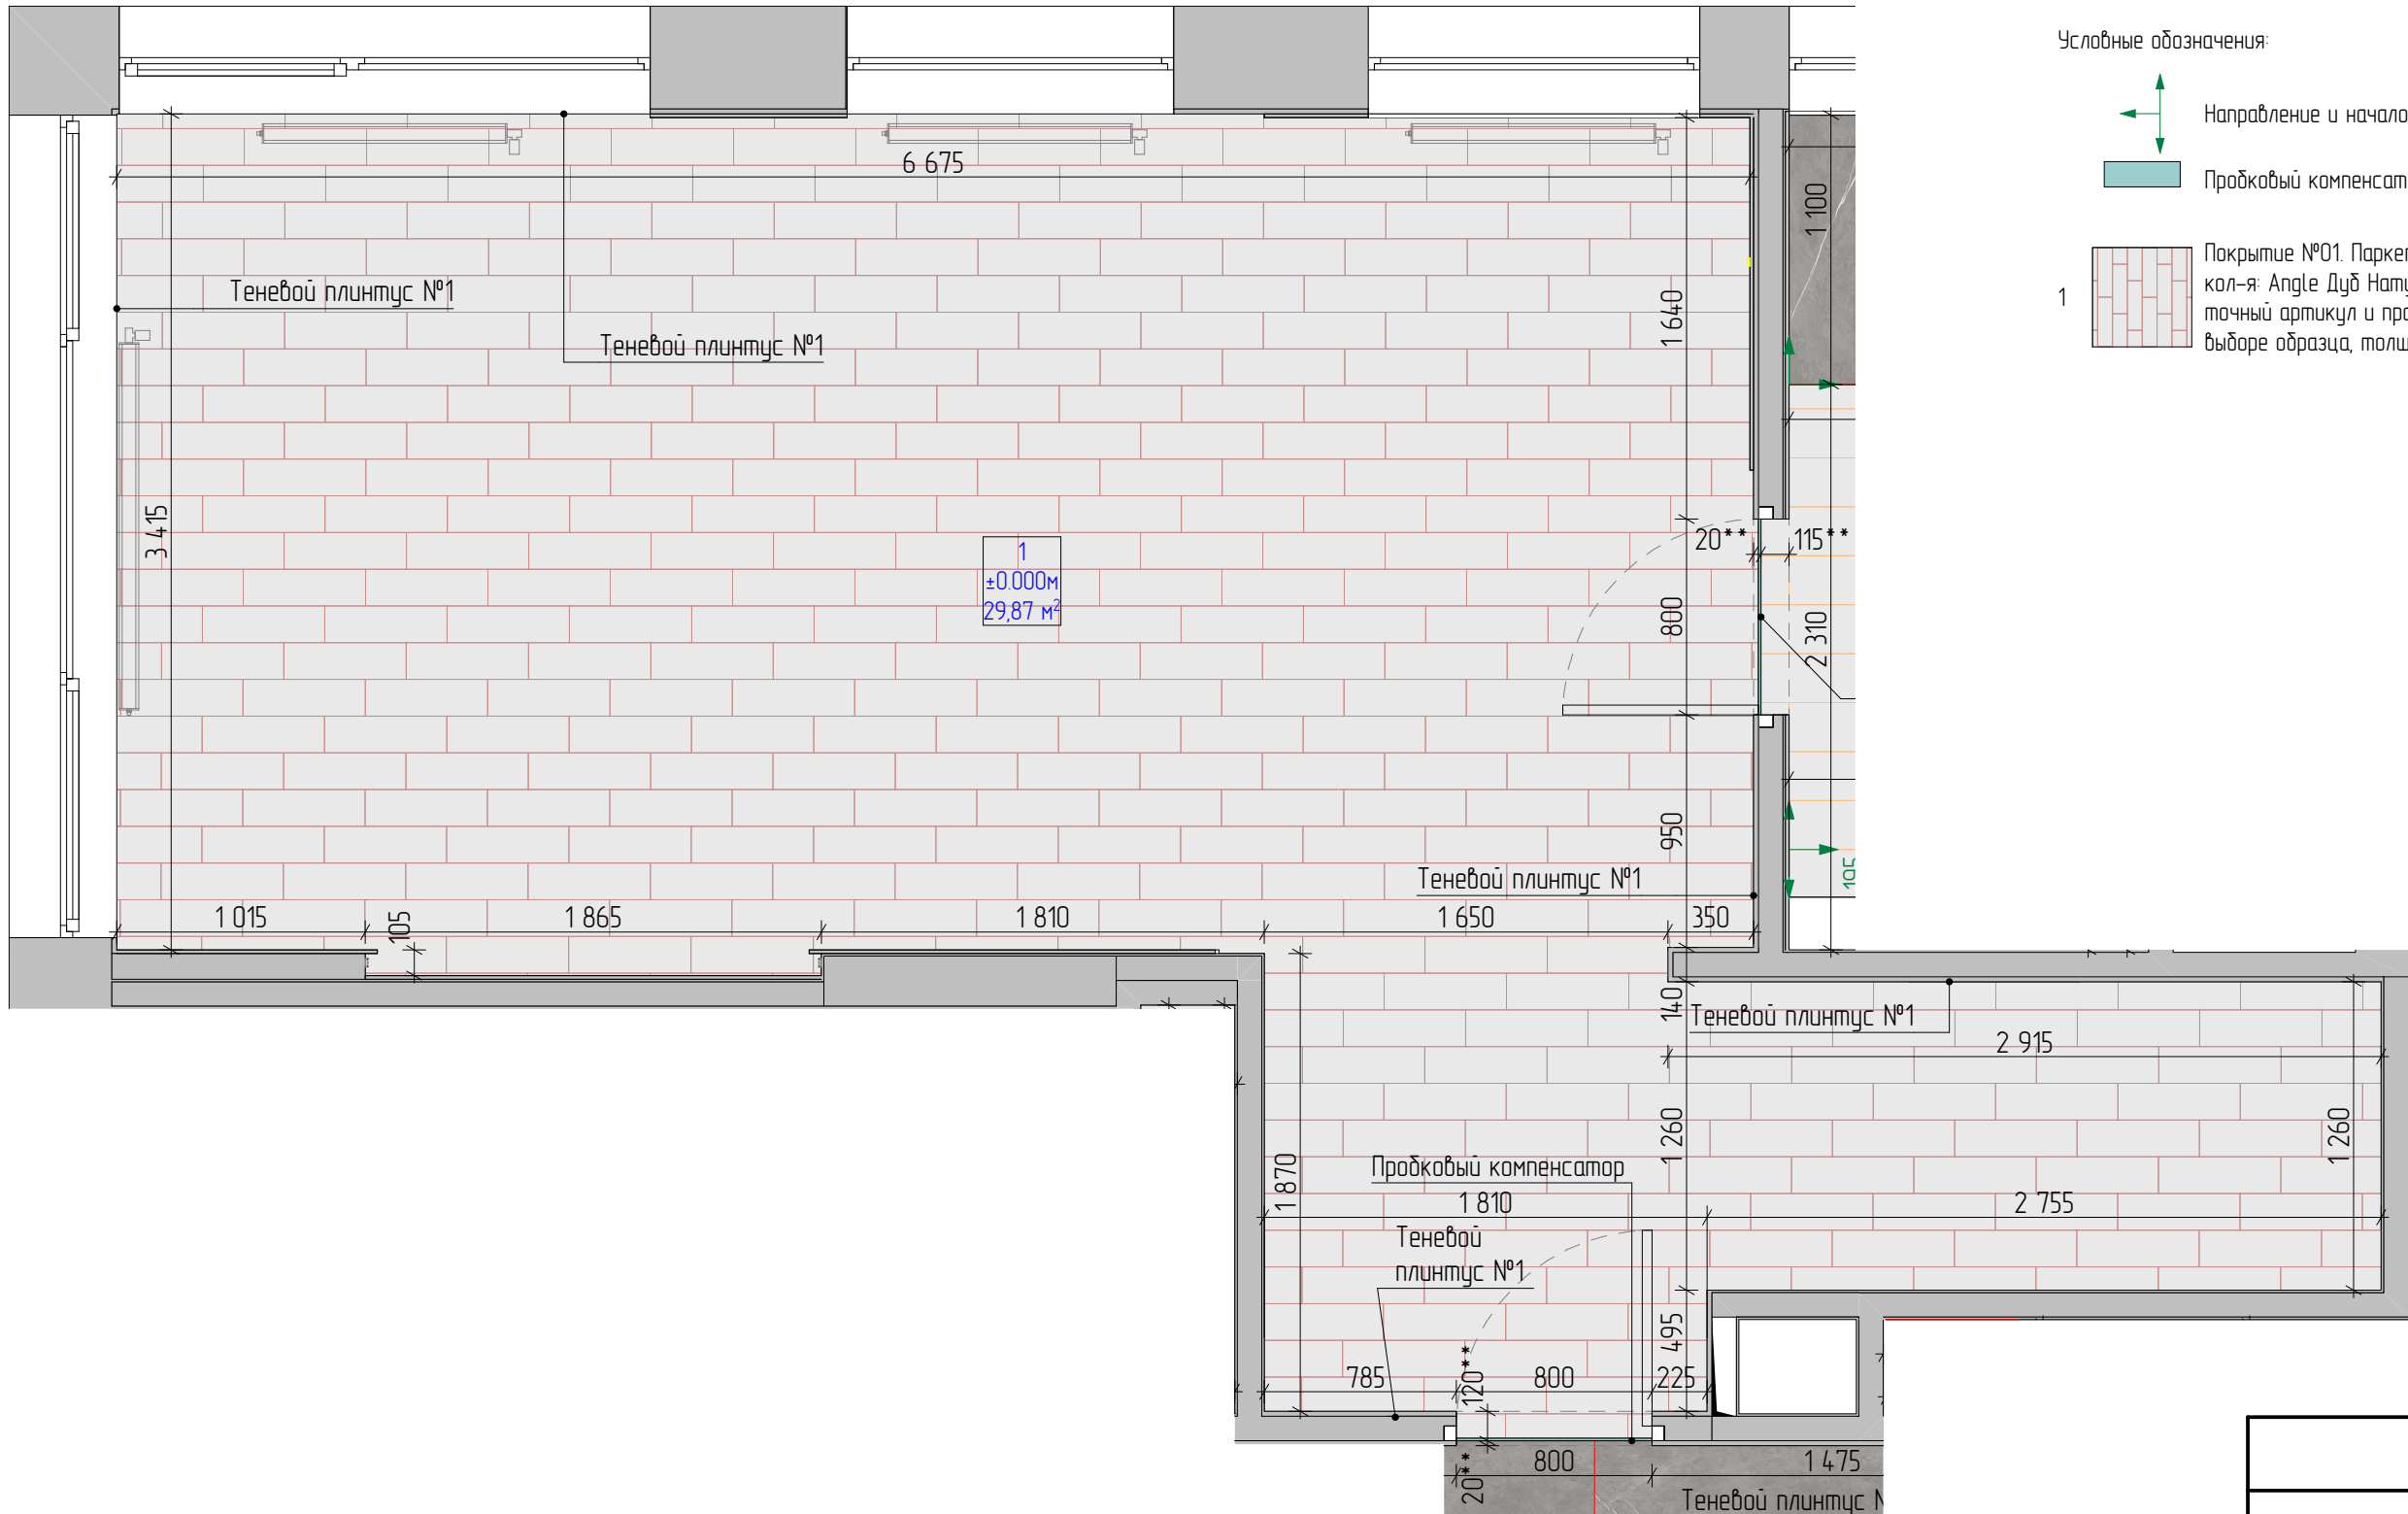

Условные обозначения:


Направление и начало укладки
Пробковый компенсатор

1
Покрывтие №01. Паркет. Изготовитель: Lab Arte, кол-я: Angle Дуб Натур, размер: 500x150 мм, точный артикул и производителя уточнить при выборе образца, толщину уточнить при заказе.

Примечания:

- * – размеры уточнить по месту после выполнения черновых отделочных работ.
- За отметку ±0,000 принят уровень чистого пола.
- При монтаже напольных покрытий уточнить необходимость устройства дверных проемов с порогом.
- * – размеры уточнить по месту после выполнения черновых отделочных работ и установки дверей со скрытой коробкой.
- ** – размер уточнить по месту в зависимости от точного расположения полотна двери, стыковка двух разных напольных покрытий должна проходить точно по центру вдоль дверного полотна.

МСК 392.12.25–ЭП ПРЕМИУМ			
Эскизный дизайн–проект интерьера квартиры в г. Москва ЖК "Остров", ул. Нижние Мневники д. 7			
Мастер спальня.План отделки пола.			
Дизайнер интерьера №1 Александр Батеньков	Стадия	Лист	Листов
	ЭП	87	120
		Подп.	Дата
ГАП	Батеньков А.С.		
Гл. дизайнер	Власова В.А.		
Гл. проектиров.	Луцкова В.Н.		
Разработал	Ильина Е.Е.		

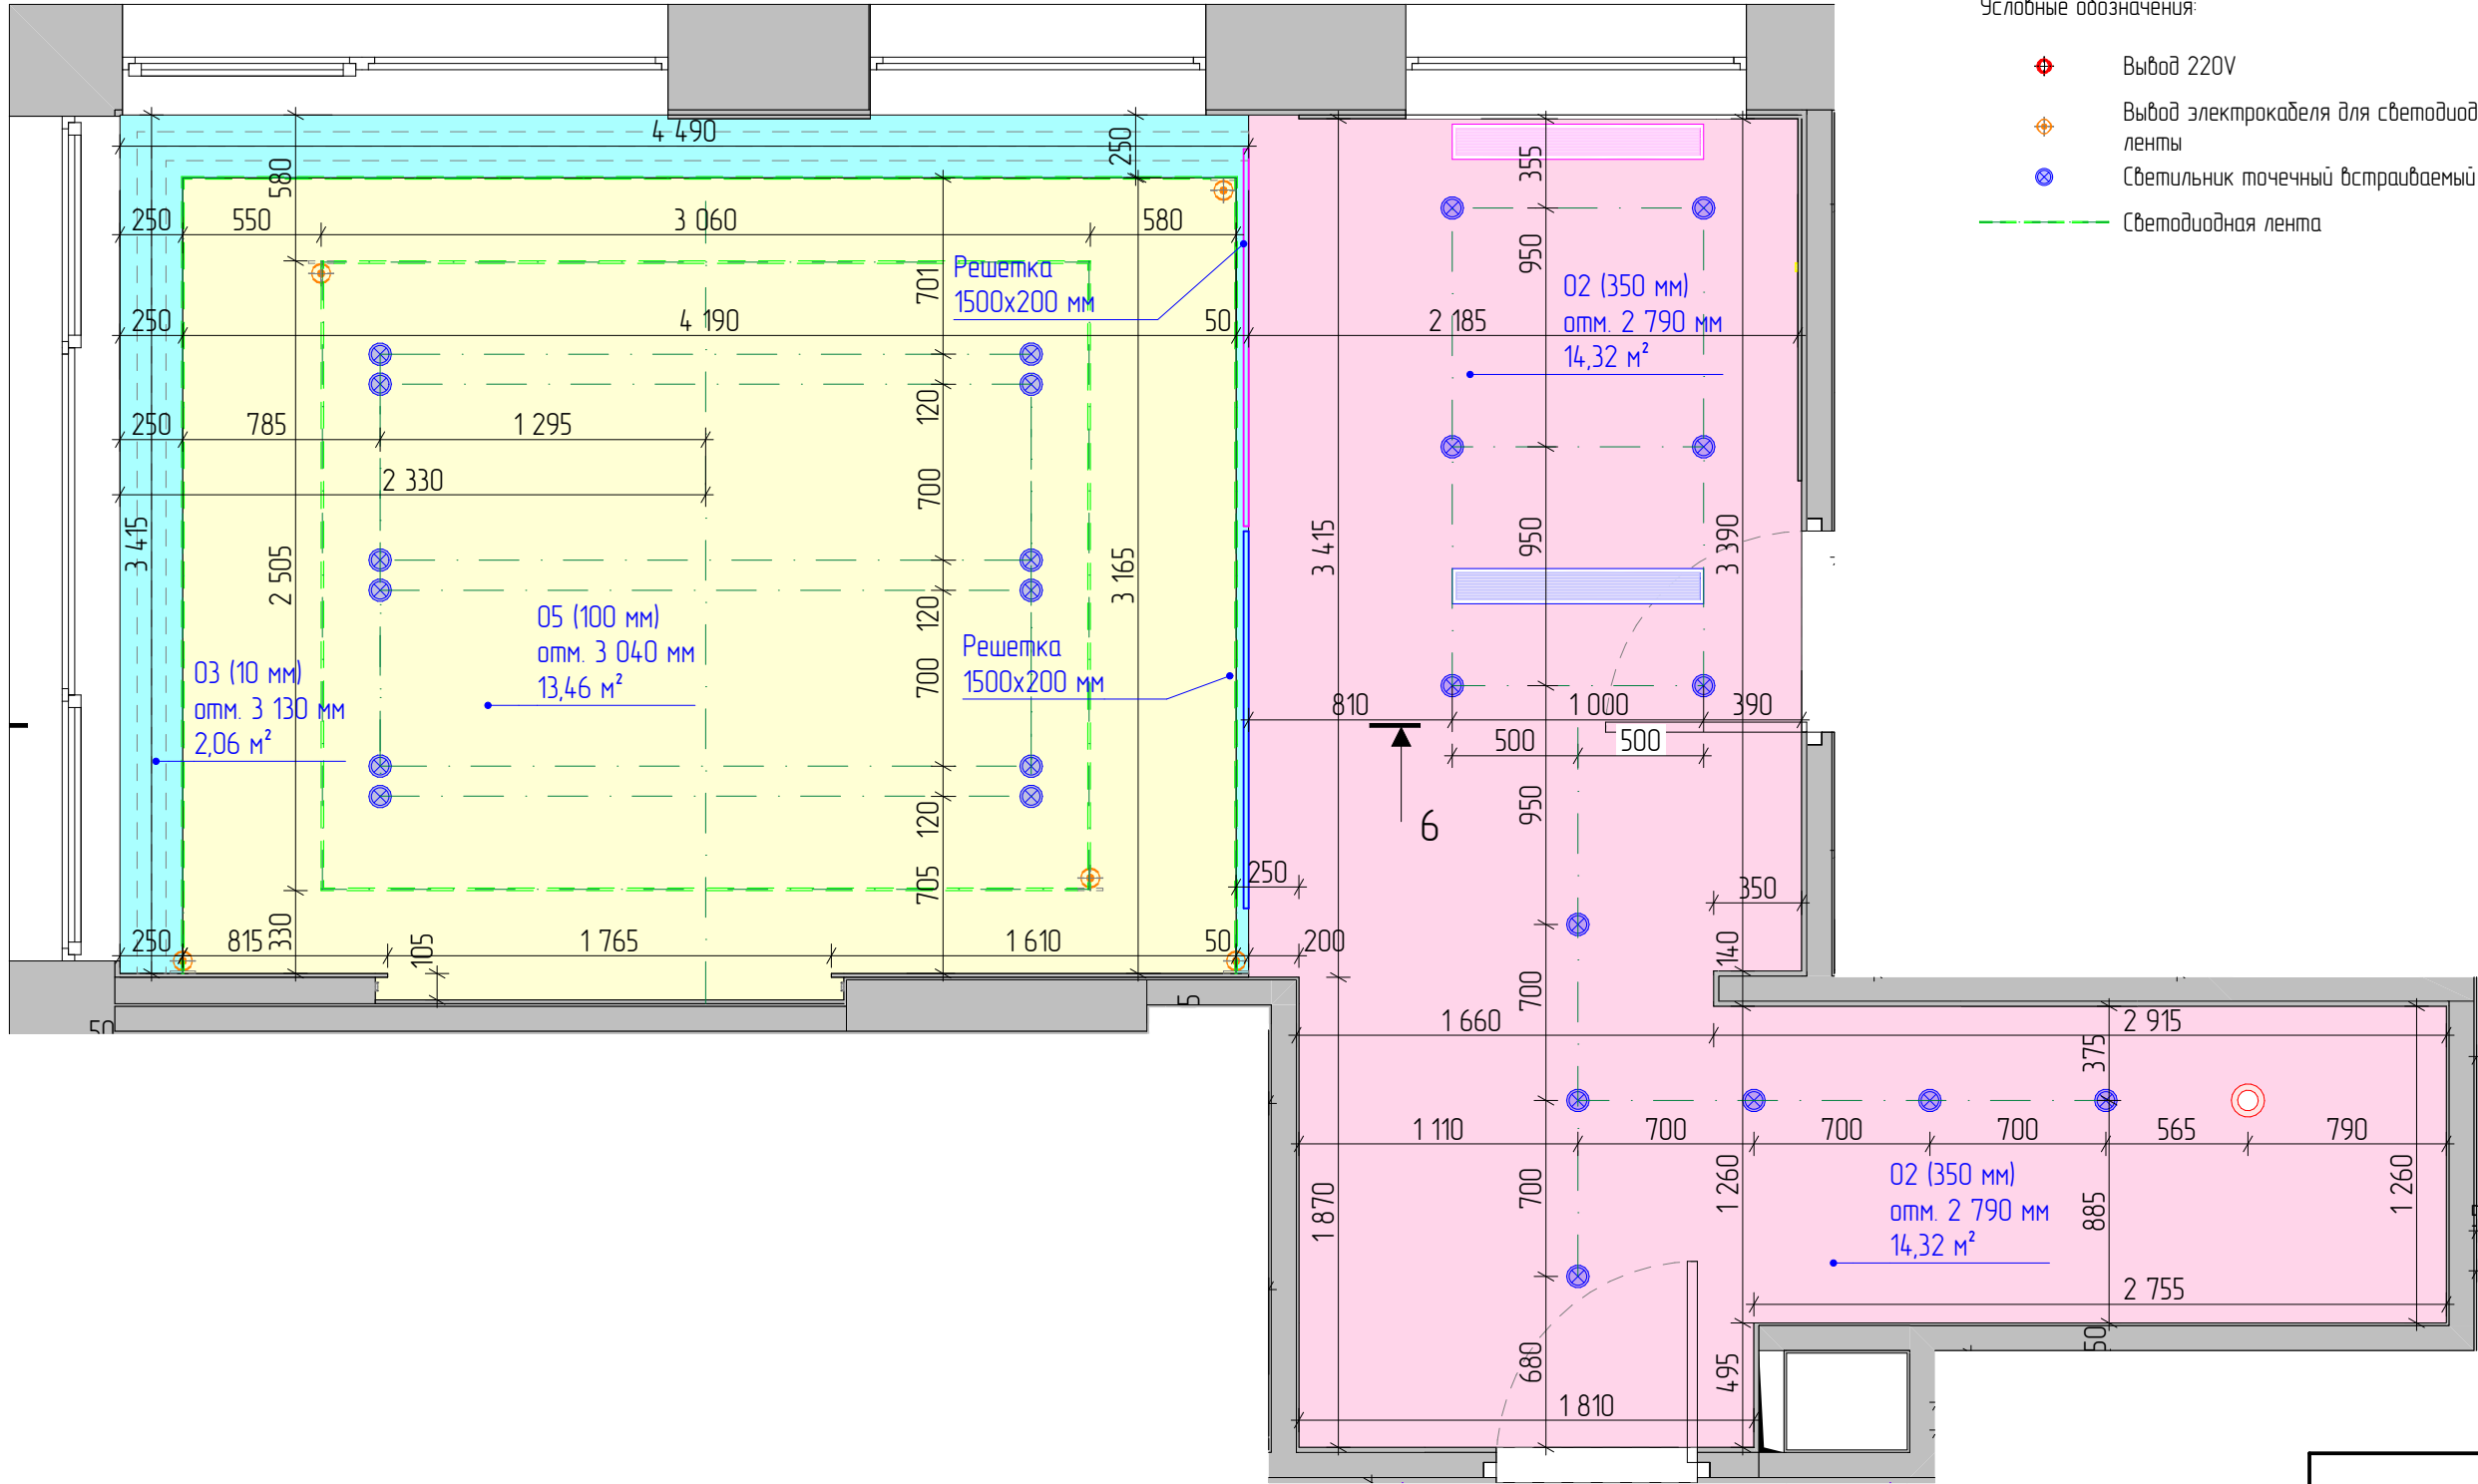


- Условные обозначения:
- Выход 220V
 - Выход электрокабеля для светодиодной ленты
 - Светильник точечный встраиваемый
 - Светодиодная лента

Примечания:

- * – размеры уточнить по месту после выполнения черновых работ.
- Выполнить уровни потолка из влагостойкого ГКЛ для предотвращения деформации потолка при затоплении.
- Высоту уровней потолка отсчитывать от существующей ж/б плиты перекрытия помещения.
- Предусмотреть усиление потолка фанерой в местах крепления потолочных карнизов для штор.
- От вытяжки провести вентиляционный короб до общедомового канала в конструкции потолка, уточнить по месту со специалистами и заказчиком.
- Шумоизоляцию разработать со специалистами, уточнить состав и толщину слоев шумоизоляционных материалов. Уточнить необходимость устройства с заказчиком.

Условные потолки				
№	Обозначение	Опуск	Примечания	Площадь м2
02		350	Потолок ГК/ЛВ. Окрасить в цвет выбранного образца (белый) по армирующему материалу (стеклохолст "паутинка").	14,32
03		10	Выворачивать и оштукатурить существующий потолок. Окрасить в цвет выбранного образца (белый) по армирующему материалу (стеклохолст "паутинка"). Размер ниши уточнить.	2,06
05		100	Потолок ГК/ЛВ. Окрасить в цвет выбранного образца (белый) по армирующему материалу (стеклохолст "паутинка").	13,46

МСК 392.12.25–ЭП ПРЕМИУМ				
Эскизный дизайн-проект интерьера квартиры в г. Москва ЖК "Остров", ул. Нижние Мневники д. 7				
Мастер спальни.План отделки потолка.				
Дизайнер интерьера №1 Александр Батеньков	Стадия	Лист	Листов	
	ЭП	88	120	
		Подп.	Дата	
ГАП	Батеньков А.С.			
Гл. дизайнер	Власова В.А.			
Гл. проектиров.	Луныкова В.Н.			
Разработал	Ильина Е.Е.			

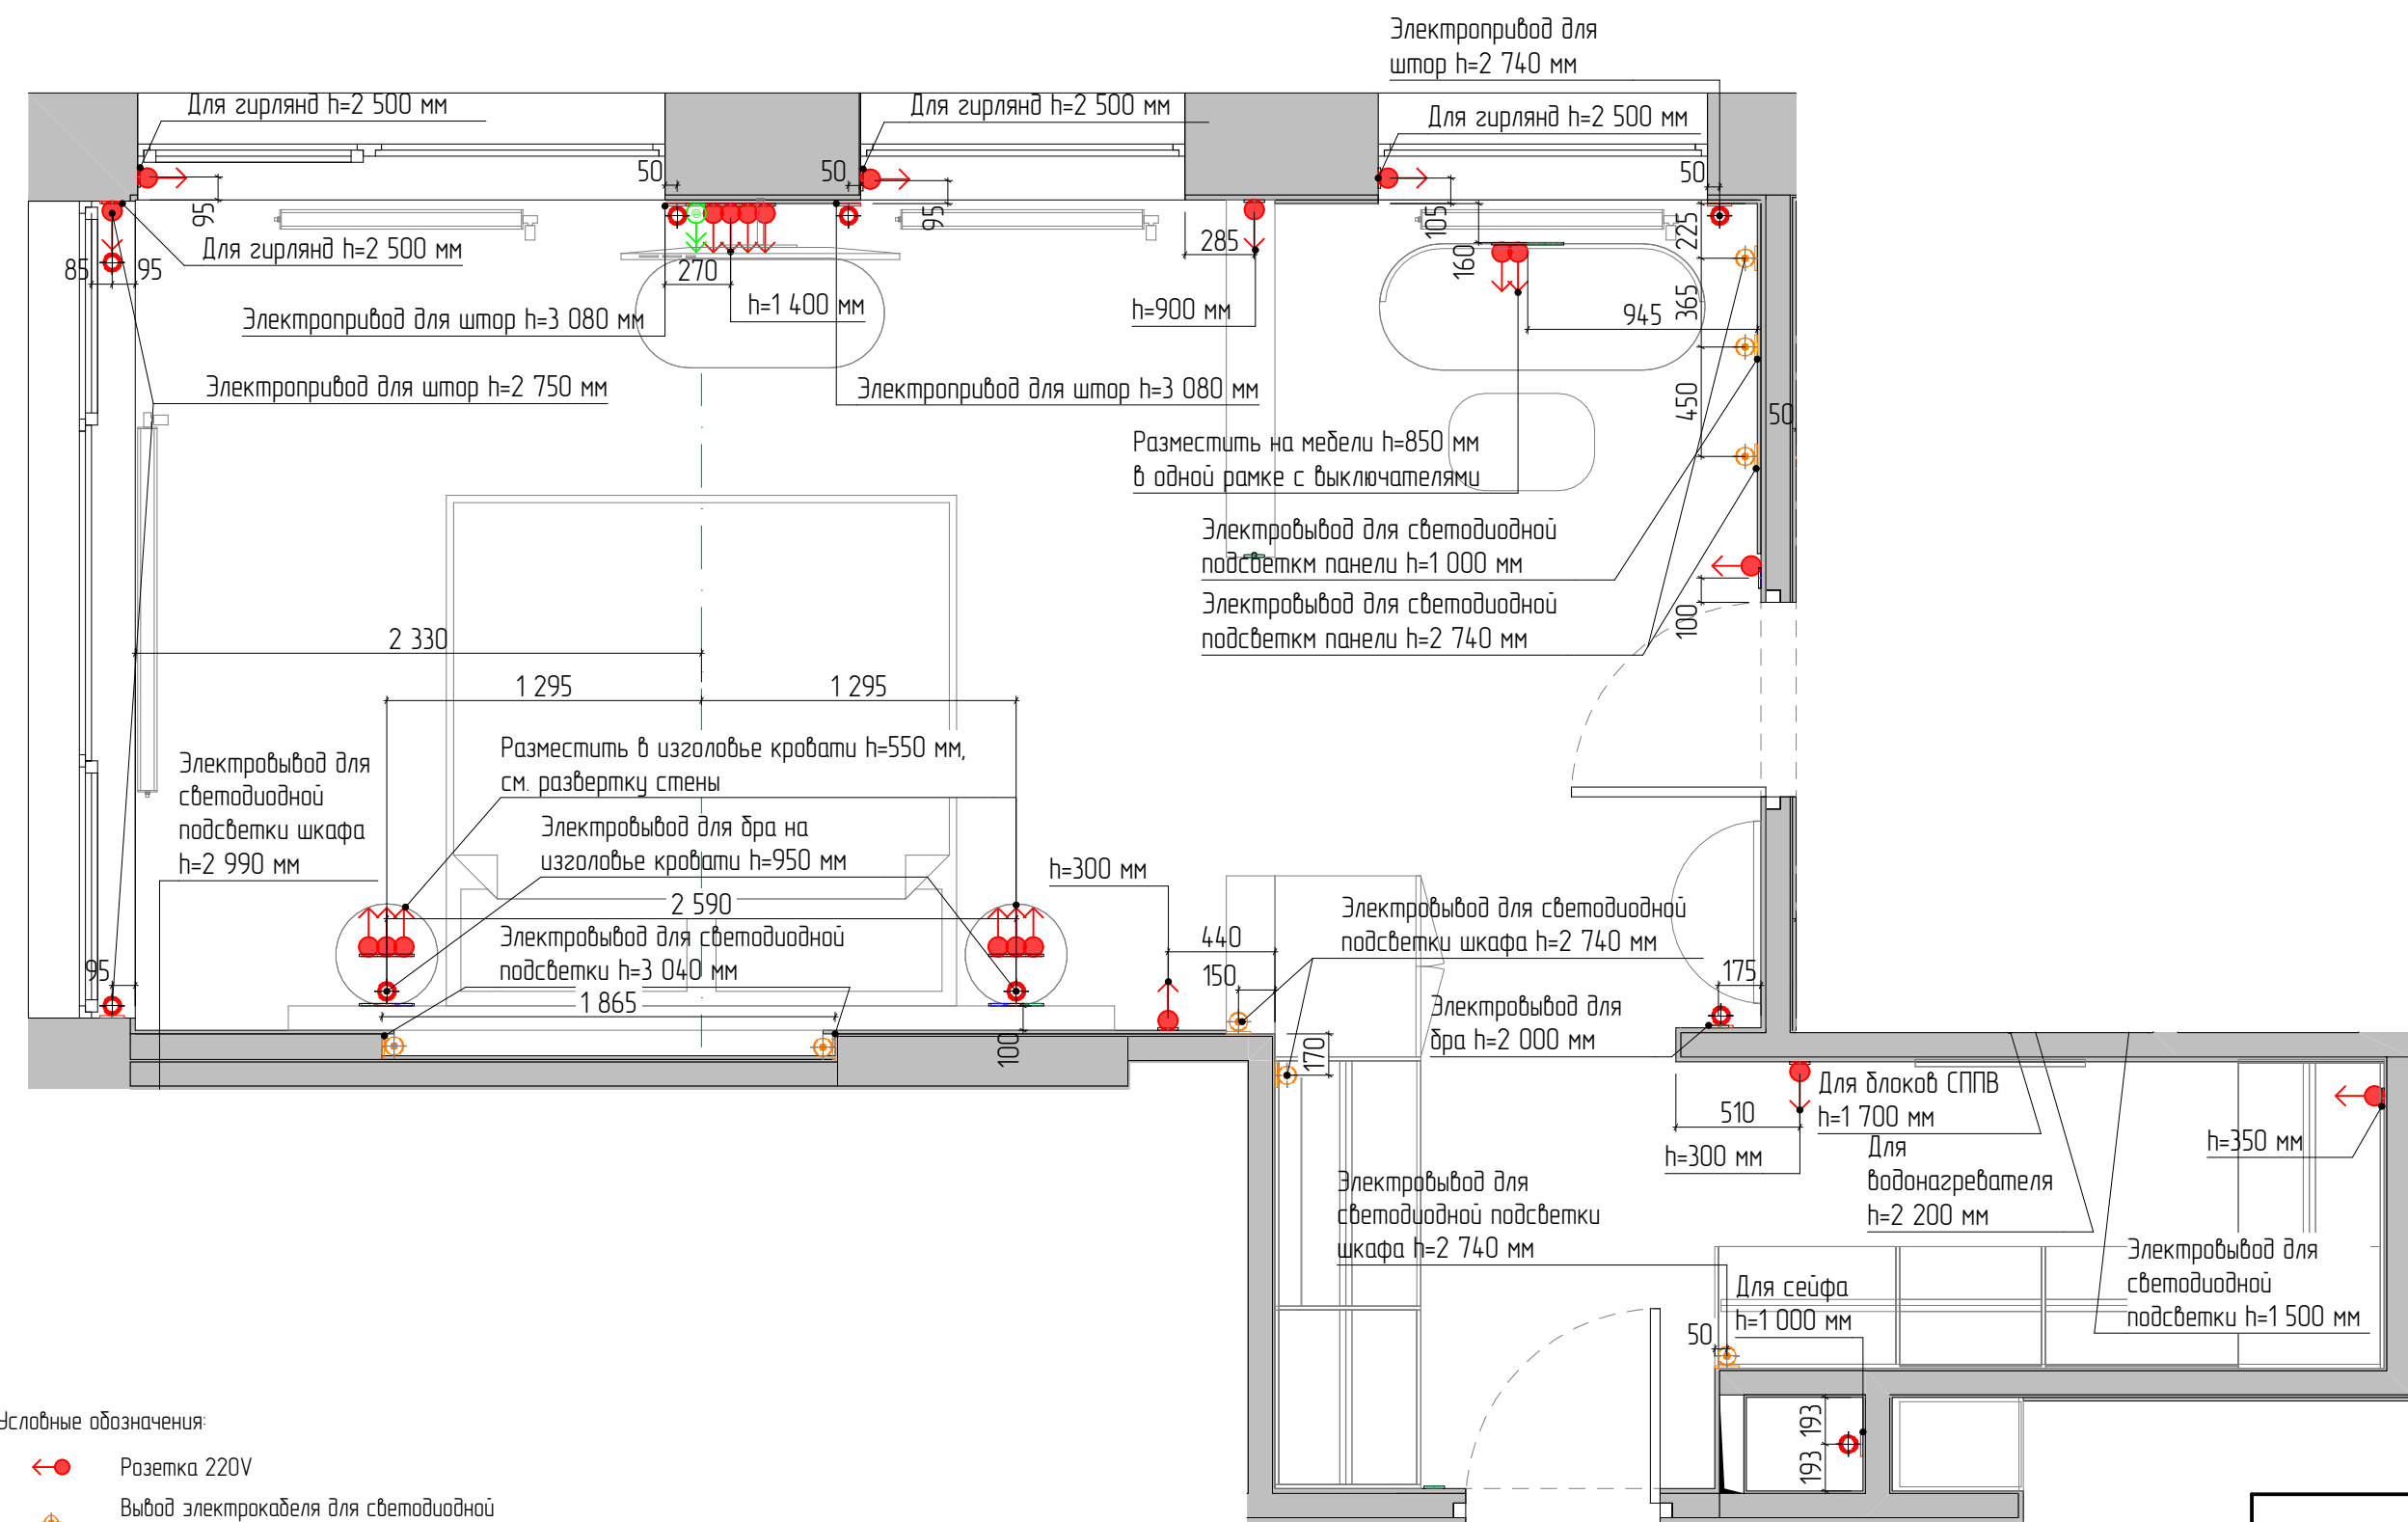

Условные обозначения:

- ←● Розетка 220V
- ◆ Вывод электрокабеля для светодиодной ленты
- ✕ Вывод электрокабеля для варочной поверхности
- ⊕ Вывод 220V

Примечания:

- * – размеры уточнить по месту.
- Розетки располагать от уровня чистого пола на высоте 0,300 м. Исключения указаны на чертеже.
- Размещение всех выводов и розеток согласовать со специалистами «Умный дом».
- Размеры и характеристики радиаторов отопления согласовать со специалистами, предусмотреть терморегуляторы.
- Датчики пожарной и охранной сигнализации и электровыводы для них разместить совместно со специалистами, предварительно вызвав их на объект.
- Размещение розеток и электровыводов по высоте см. на развертках стен.

МСК 392.12.25–ЭП ПРЕМИУМ			
Эскизный дизайн–проект интерьера квартиры в г. Москва ЖК "Остров", ул. Нижние Мневники д. 7			
Мастер спальни. План размещения электрооборудования.			
Дизайнер интерьера  №1 Александр Батеньков	Стадия	Лист	Листов
	ЭП	89	120
		Подп.	Дата
ГАП	Батеньков А.С.		
Гл. дизайнер	Власова В.А.		
Гл. проектиров.	Луныкова В.Н.		
Разработал	Ильина Е.Е.		




- Условные обозначения:
- Выход 220V
 - Выход электрокабеля для светодиодной ленты
 - Выключатель одноклавишный
 - Выключатель двухклавишный
 - Переключатель двухклавишный
 - Переключатель одноклавишный переходной
 - Светильник точечный встраиваемый
 - Светодиодная лента

Примечания:


- * – размеры уточнить по месту.
- Выключатели располагать от уровня чистого пола на высоте 0,900 м. Исключения указаны на чертеже.
- Светильники, встроенные в мебель, согласовать с изготовителями мебели.

МСК 392.12.25–ЭП ПРЕМИУМ			
Эскизный дизайн–проект интерьера квартиры в г. Москва ЖК "Остров", ул. Нижние Мневники д. 7			
Мастер спальниПлан размещения освещения и выключателей.			
Дизайнер интерьера №1 Александр Батеньков	Стадия	Лист	Листов
	ЭП	90	120
		Подп.	Дата
ГАП	Батеньков А.С.		
Гл. дизайнер	Власова В.А.		
Гл. проектиров.	Луцькова В.Н.		
Разработал	Ильина Е.Е.		

И-01 Развертка стены 1:25

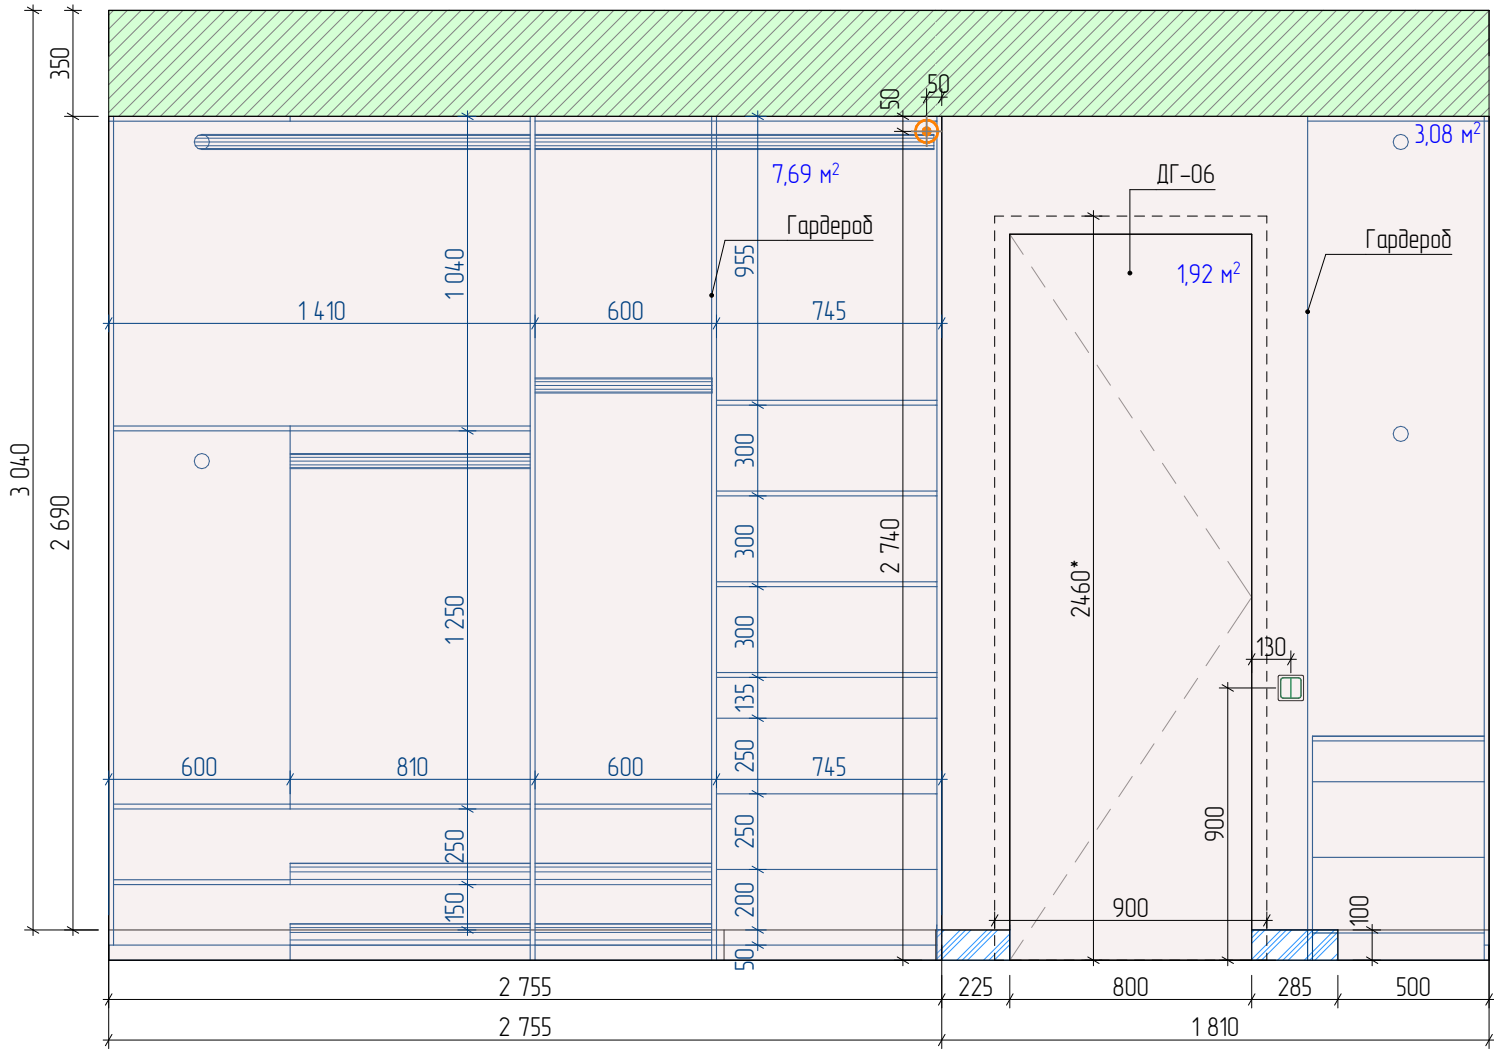

И-02 Развертка стены 1:25

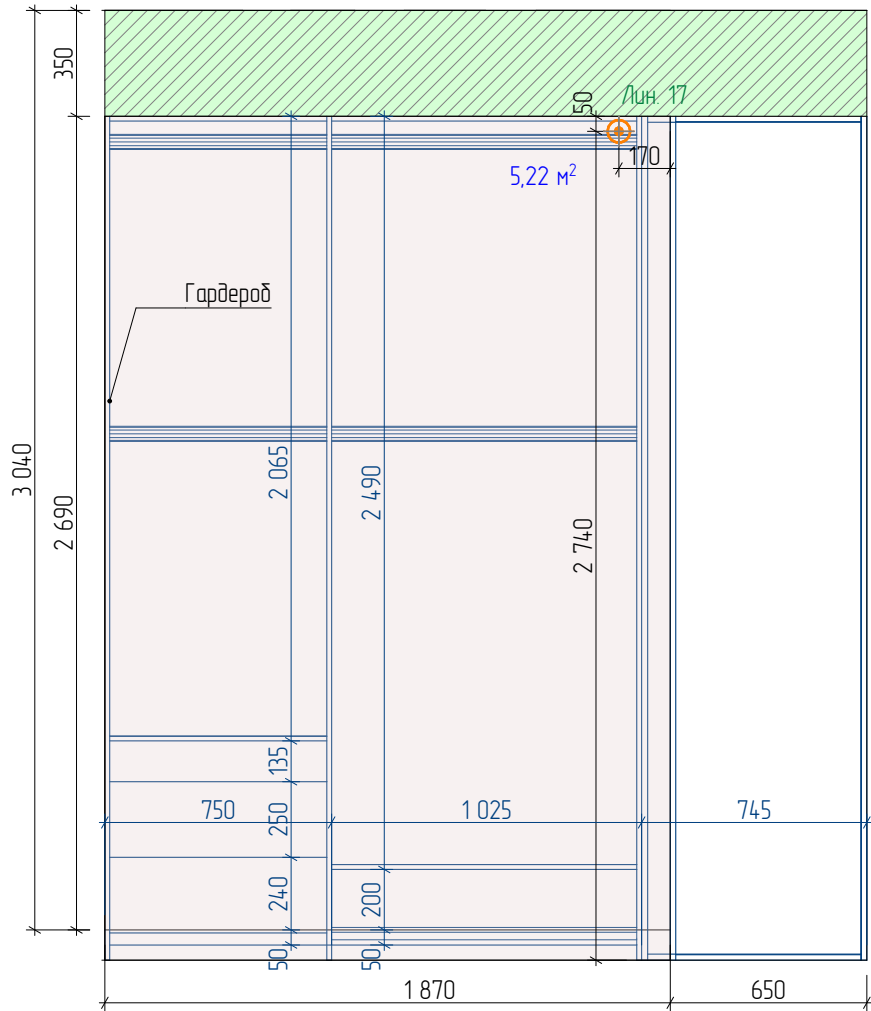

Условные обозначения:

- Плинтус №1. Теневой плинтус скрытого монтажа с МДФ вставкой. Теневой зазор от пола 100 мм. Цвет при выборе образца (в цвет стен).
- Монтаж конструкций из ГКВЛ
- Покраска №1. Выполнить по подготовленной поверхности (стеклохолст*). Цвет при выборе образца (бежевый*).
- Вывод электрокабеля для светодиодной ленты
- Переключатель двухклавишный

Примечания:



- * – размеры уточнить по месту после выполнения черновых отделочных работ.
- Выключатели располагать от уровня чистого пола на высоте 900 мм. Исключения указаны на чертеже.
- Розетки располагать от уровня чистого пола на высоте 300 мм. Исключения указаны на чертеже.
- Цвет окрашивания плинтуса уточнить после согласования образца.
- Высоту проемов выполнять 2460 мм от уровня чистого пола. Уточнить после подбора и согласования модели дверей.
- Плинтус подрезать по месту в местах стыковки с дверями и мебелью.
- Внутреннее наполнение мебели разработать со специалистами.
- Серым/синим цветом показаны размеры мебели. Мебель разработать со специалистами, размеры уточнить после выполнения чистовой отделки.

МСК 392.12.25-ЭП ПРЕМИУМ

Эскизный дизайн-проект интерьера квартиры в г. Москва ЖК "Остров", ул. Нижние Мневники д. 7

Мастер спальни.Развертки стен И-01, И-02.

Дизайнер интерьера  №1 Александр Батыков	Стадия	Лист	Листов
	ЭП	91	120
		Подп.	Дата
ГАП	Батыков А.С.		
Гл. дизайнер	Власова В.А.		
Гл. проектиров.	Луцкова В.Н.		
Разработал	Ильина Е.Е.		

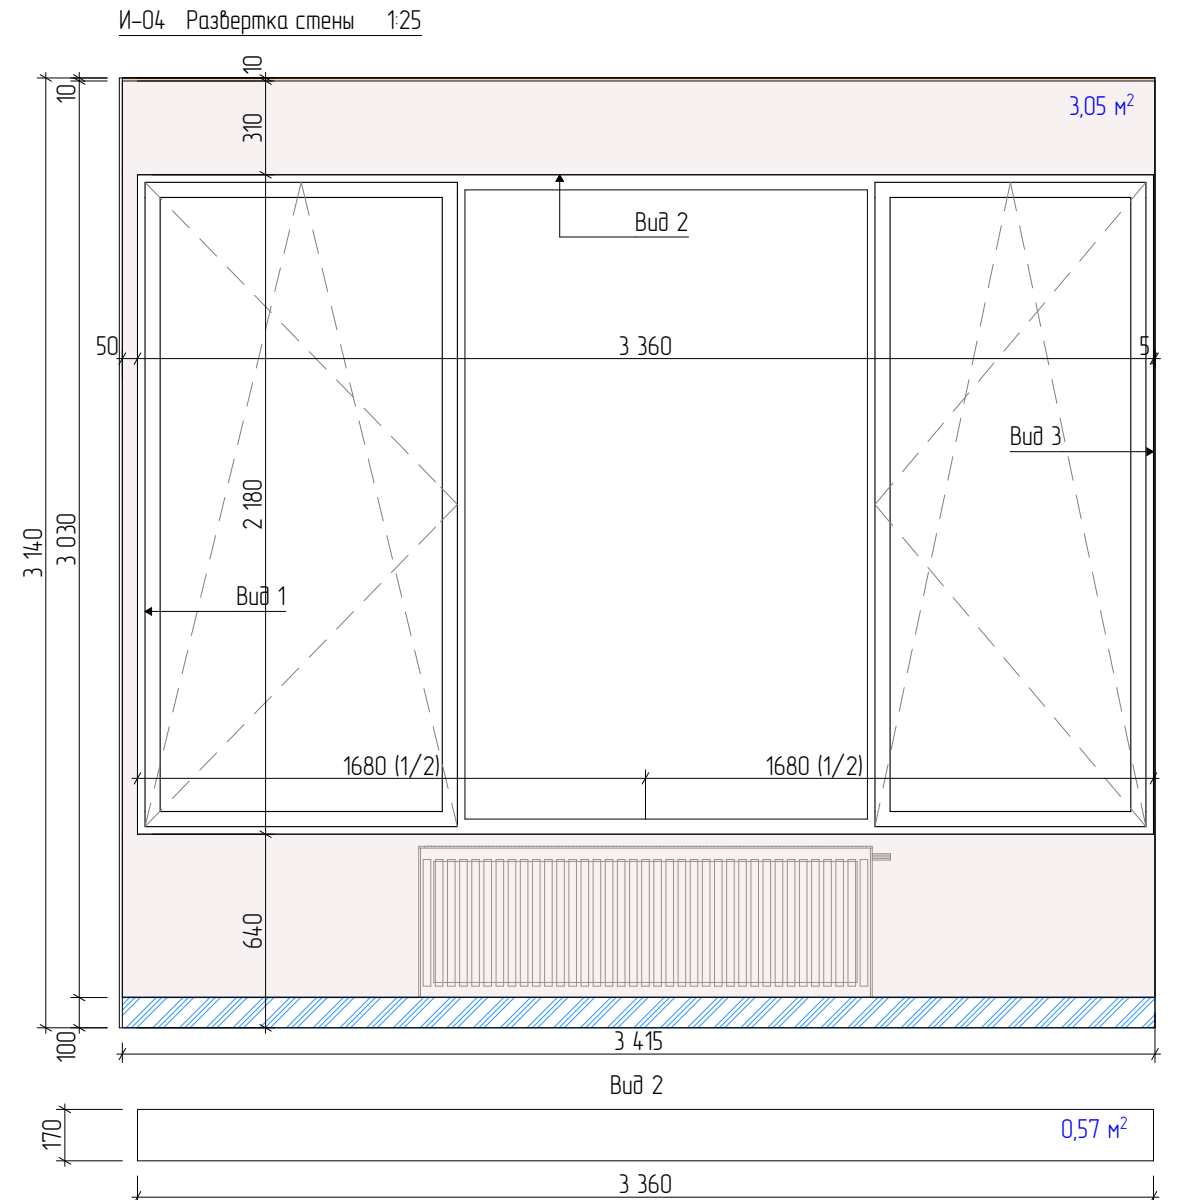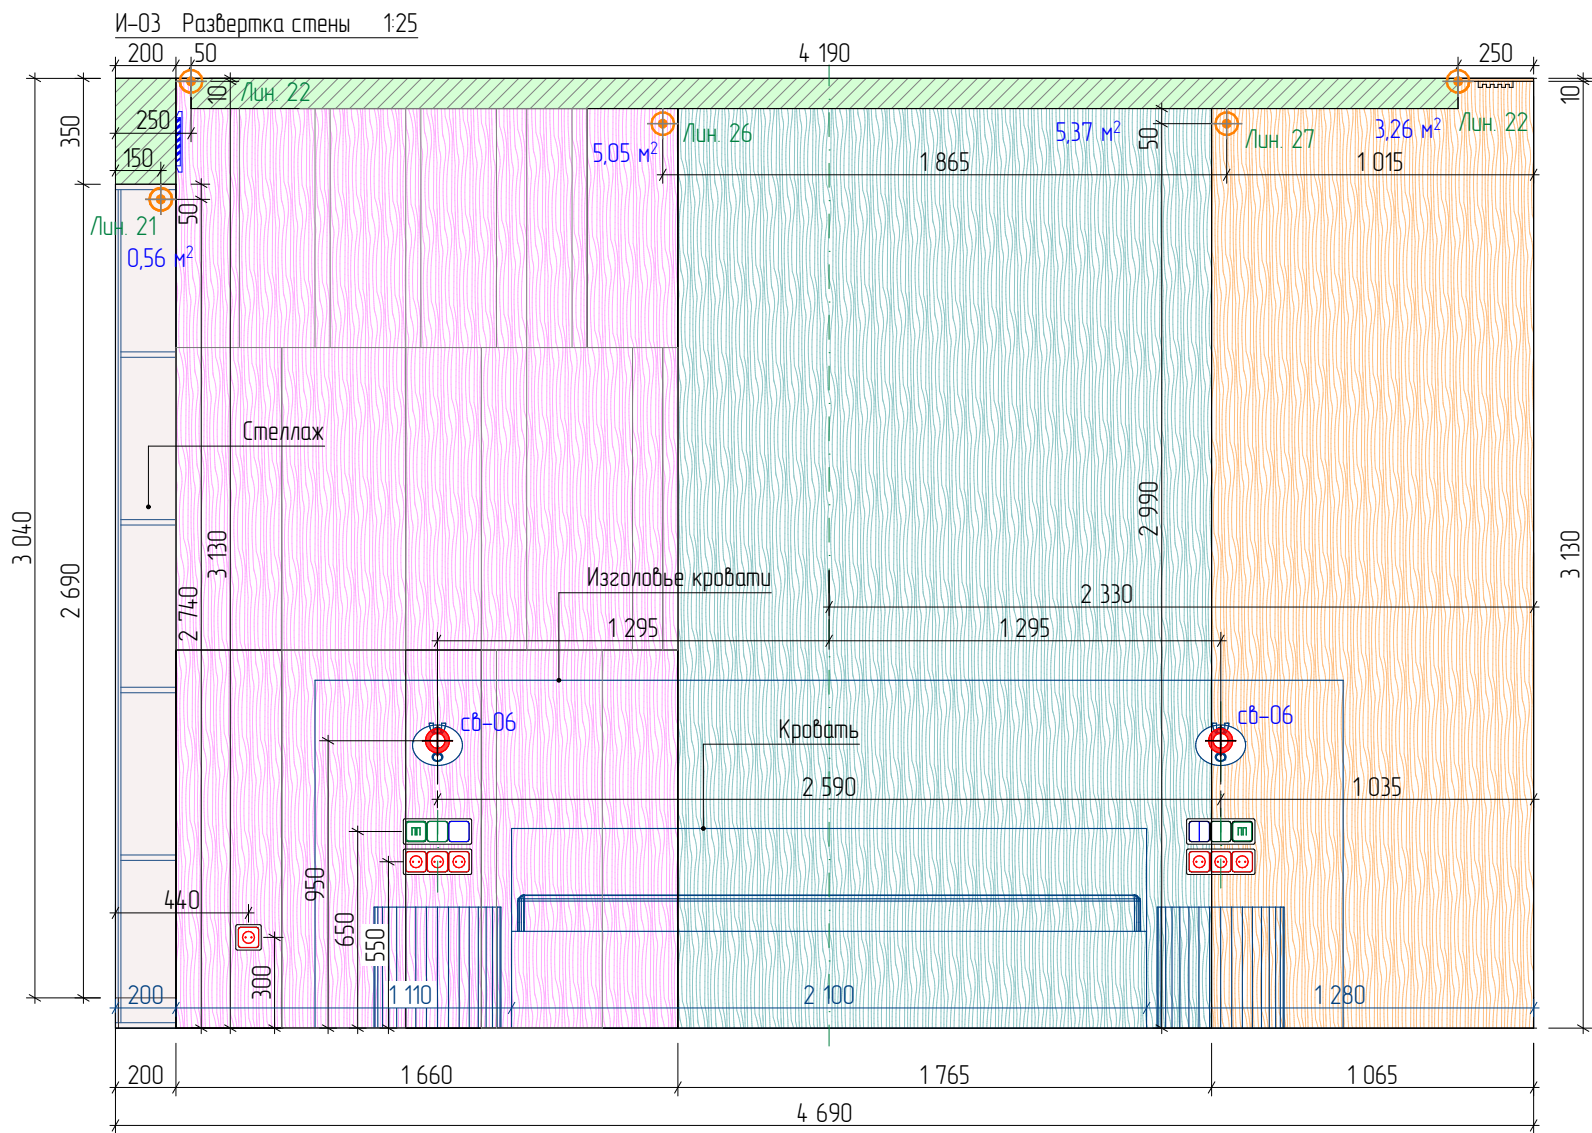


Примечания:

- * – размеры уточнить по месту после выполнения черновых отделочных работ.
- Выключатели располагать от уровня чистого пола на высоте 900 мм. Исключения указаны на чертеже.
- Розетки располагать от уровня чистого пола на высоте 300 мм. Исключения указаны на чертеже.
- Оконные откосы оклеить строительным флизелином и окрасить в белый цвет. Уточнить по месту.
- Размещение выводов для отопления согласовать со специалистами.
- Цвет окрашивания плинтуса уточнить после согласования образца.
- Внутреннее наполнение мебели разработать со специалистами.
- Серым/синим цветом показаны размеры мебели. Мебель разработать со специалистами, размеры уточнить после выполнения чистовой отделки.



Условные обозначения:

- Плинтус №1. Теневой плинтус скрытого монтажа с МДФ вставкой. Теневой зазор от пола 100 мм. Цвет при выборе образца (в цвет стен).
- Монтаж конструкций из ГКВЛ
- Покраска №1. Выполнить по подготовленной поверхности (стеклохолст*). Цвет при выборе образца (бежевый*).
- Покраска №2. Выполнить по подготовленной поверхности (стеклохолст*). Цвет при выборе образца (белый*).
- МДФ панель №4. Цвет и фактура при выборе образца (ржавый металл*).
- МДФ панель №5. Цвет и фактура при выборе образца (ржавый металл*).
- МДФ панель №6. 3д панель. Цвет и фактура при выборе образца (ржавый металл*).

- Выход 220 В
- Выход электрокабеля для светодиодной ленты
- Розетка 220 В
- Выключатель одноклавишный
- Выключатель двухклавишный
- Переключатель одноклавишный переходной
- Переключатель двухклавишный

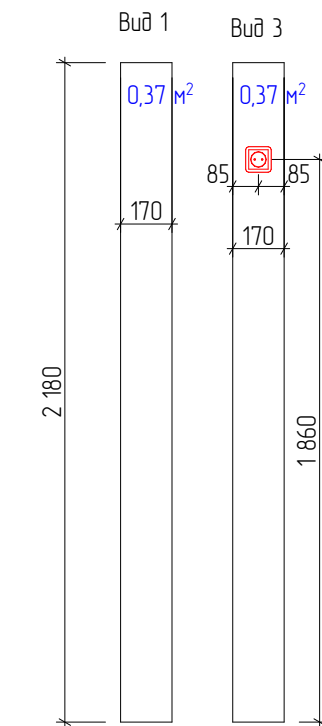

МСК 392.12.25-ЭП ПРЕМИУМ			
Эскизный дизайн-проект интерьера квартиры в г. Москва ЖК "Остров", ул. Нижние Мневники д. 7			
Мастер спальни.Развертки стен И-03, И-04.			
Дизайнер интерьера №1 Александр Батеньков	Стадия	Лист	Листов
	ЭП	92	120
		Подп.	Дата
ГАП	Батеньков А.С.		
Гл. дизайнер	Власова В.А.		
Гл. проектиров.	Луныкова В.Н.		
Разработал	Ильина Е.Е.		



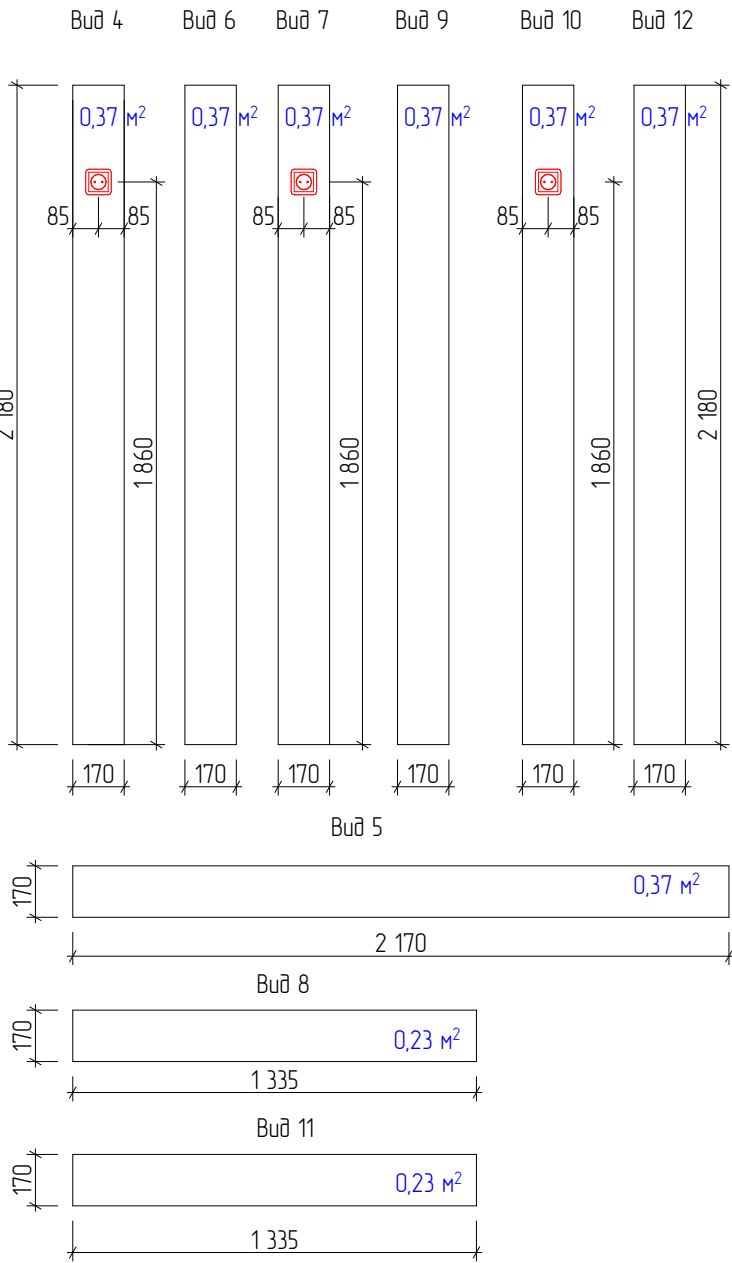
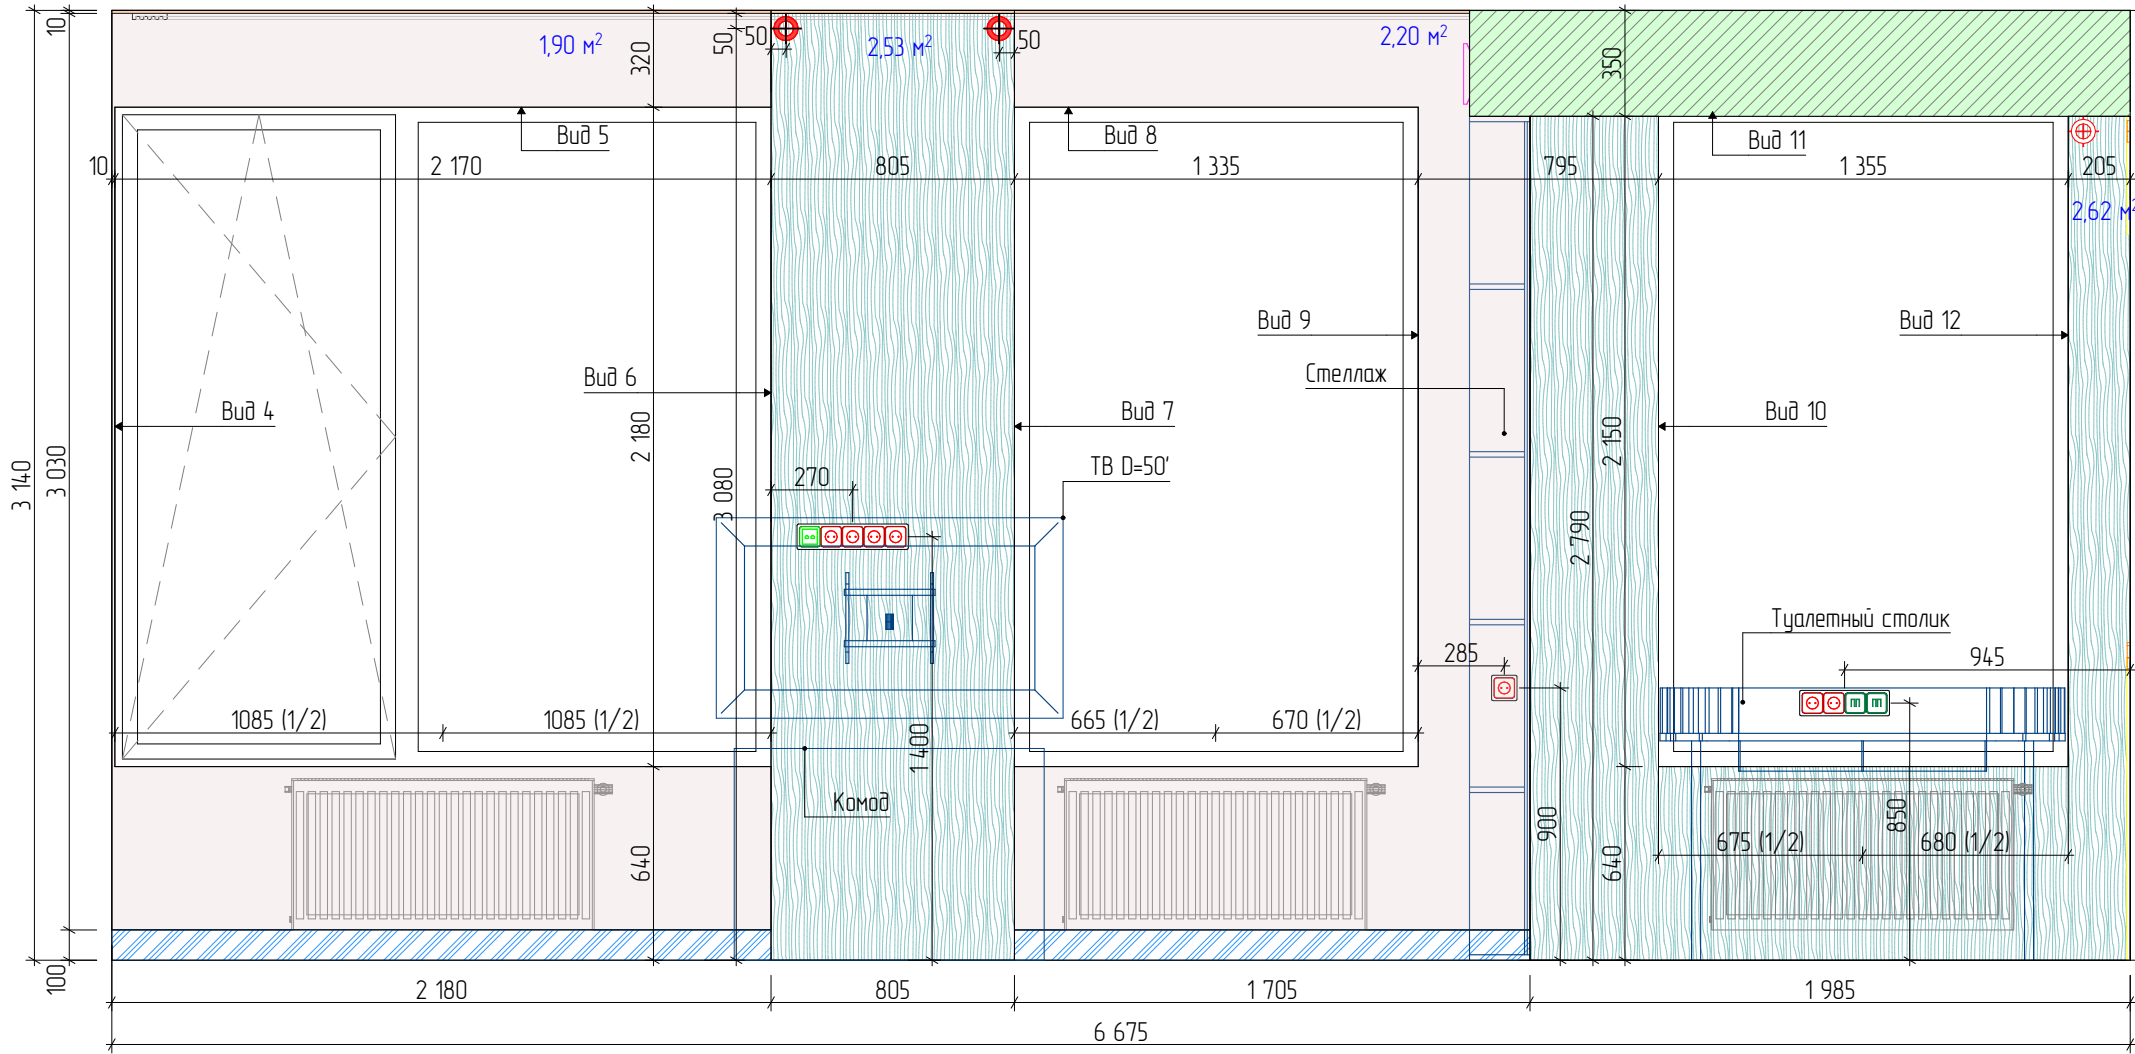


Условные обозначения:


- Плинтус №1. Теневой плинтус скрытого монтажа с МДФ вставкой. Теневой зазор от пола 100 мм. Цвет при выборе образца (в цвет стен).
- Монтаж конструкций из ГКВЛ
- Покраска №1. Выполнить по подготовленной поверхности (стеклохолст*). Цвет при выборе образца (бежевый*).
- Покраска №2. Выполнить по подготовленной поверхности (стеклохолст*). Цвет при выборе образца (белый*).
- МДФ панель №4. Цвет и фактура при выборе образца (ржавый металл*).
- Выход 220 V
- Розетка 220 V
- Переключатель одноклавишный переходной
- Переключатель двухклавишный
- Интернет-розетка двойная

Примечания:
1. *- размеры уточнить по месту после выполнения черновых отделочных работ.
2. Выключатели располагать от уровня чистого пола на высоте 900 мм. Исключения указаны на чертеже.
3. Розетки располагать от уровня чистого пола на высоте 300 мм. Исключения указаны на чертеже.
4. Оконные откосы оклеить строительным флизелином и окрасить в белый цвет. Уточнить по месту.
5. Размещение выводов для отопления согласовать со специалистами.
6. Цвет окрашивания плинтуса уточнить после согласования образца.
7. Плинтус подрезать по месту в местах стыковки с дверями и мебелью.
8. Внутреннее наполнение мебели разработать со специалистами.
9. Серым/синим цветом показаны размеры мебели. Мебель разработать со специалистами, размеры уточнить после выполнения чистовой отделки.

МСК 392.12.25-ЭП ПРЕМИУМ			
Эскизный дизайн-проект интерьера квартиры в г. Москва ЖК "Остров", ул. Нижние Мневники д. 7			
Мастер спальни.Развертка стен И-05.			
Дизайнер интерьера №1 Александр Батеньков	Стадия	Лист	Листов
	ЭП	93	120
		Подп.	Дата
ГАП	Батеньков А.С.		
Гл. дизайнер	Власова В.А.		
Гл. проектиров.	Луцькова В.Н.		
Разработал	Ильина Е.Е.		

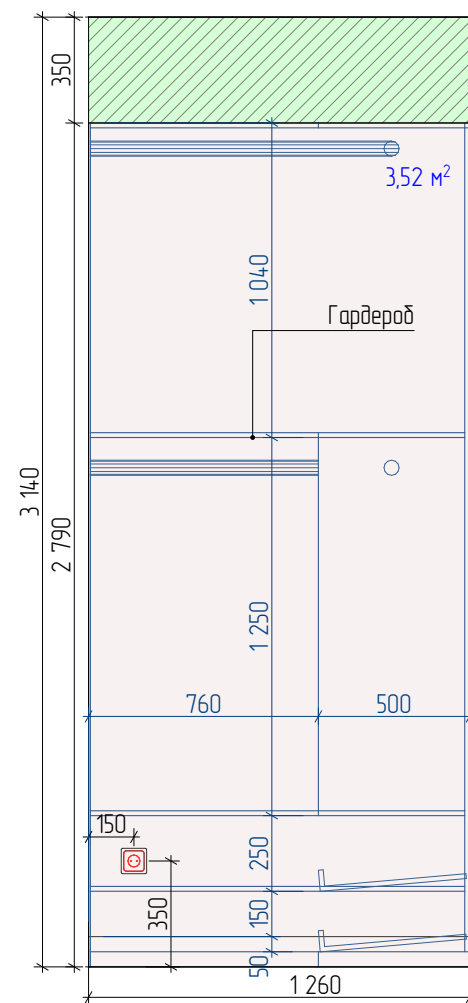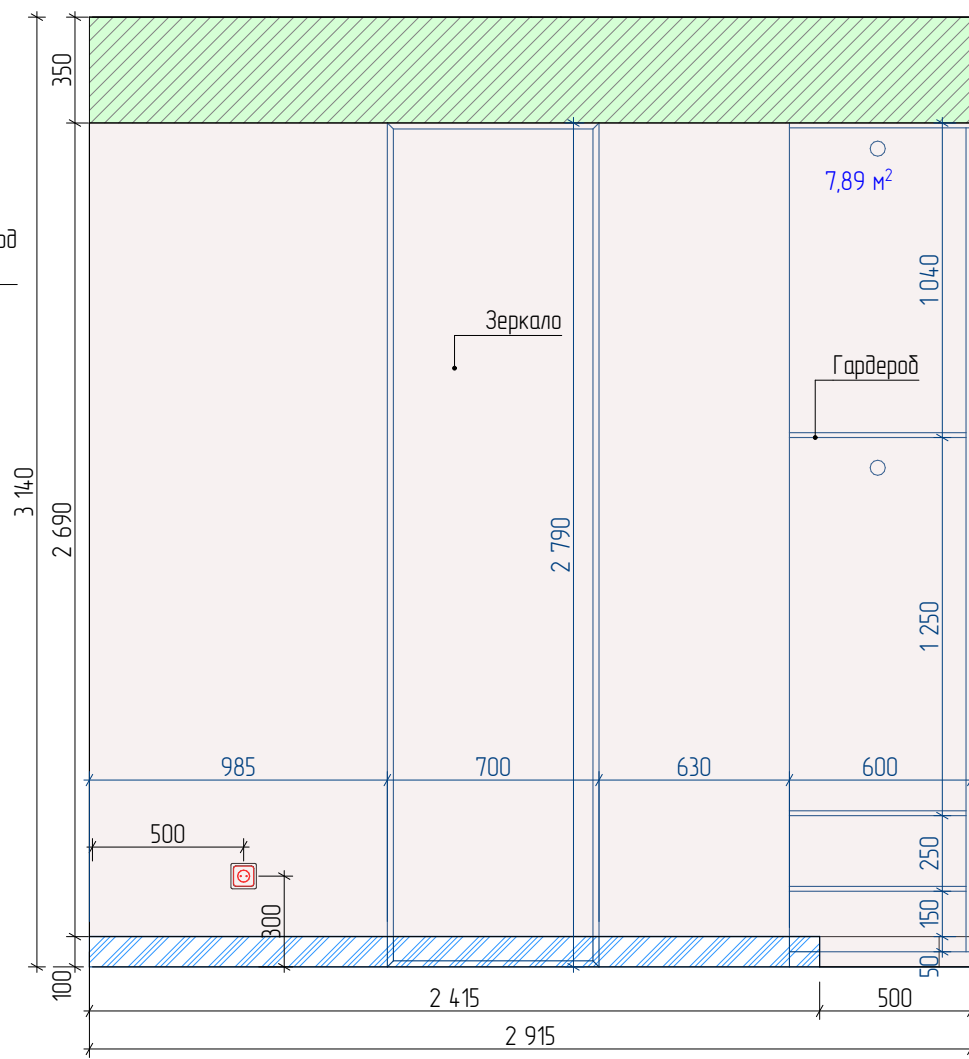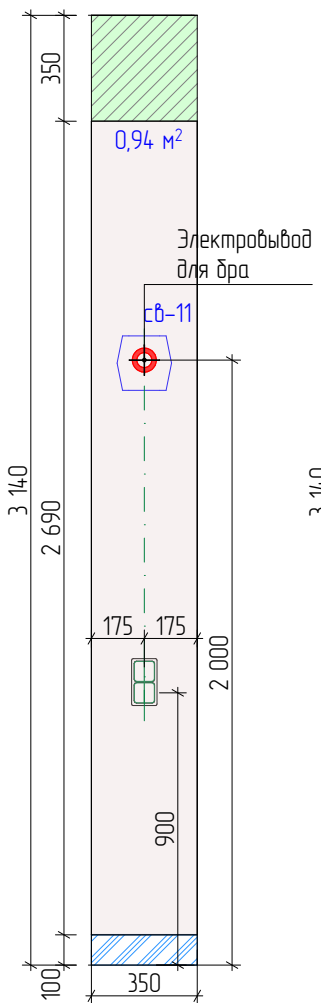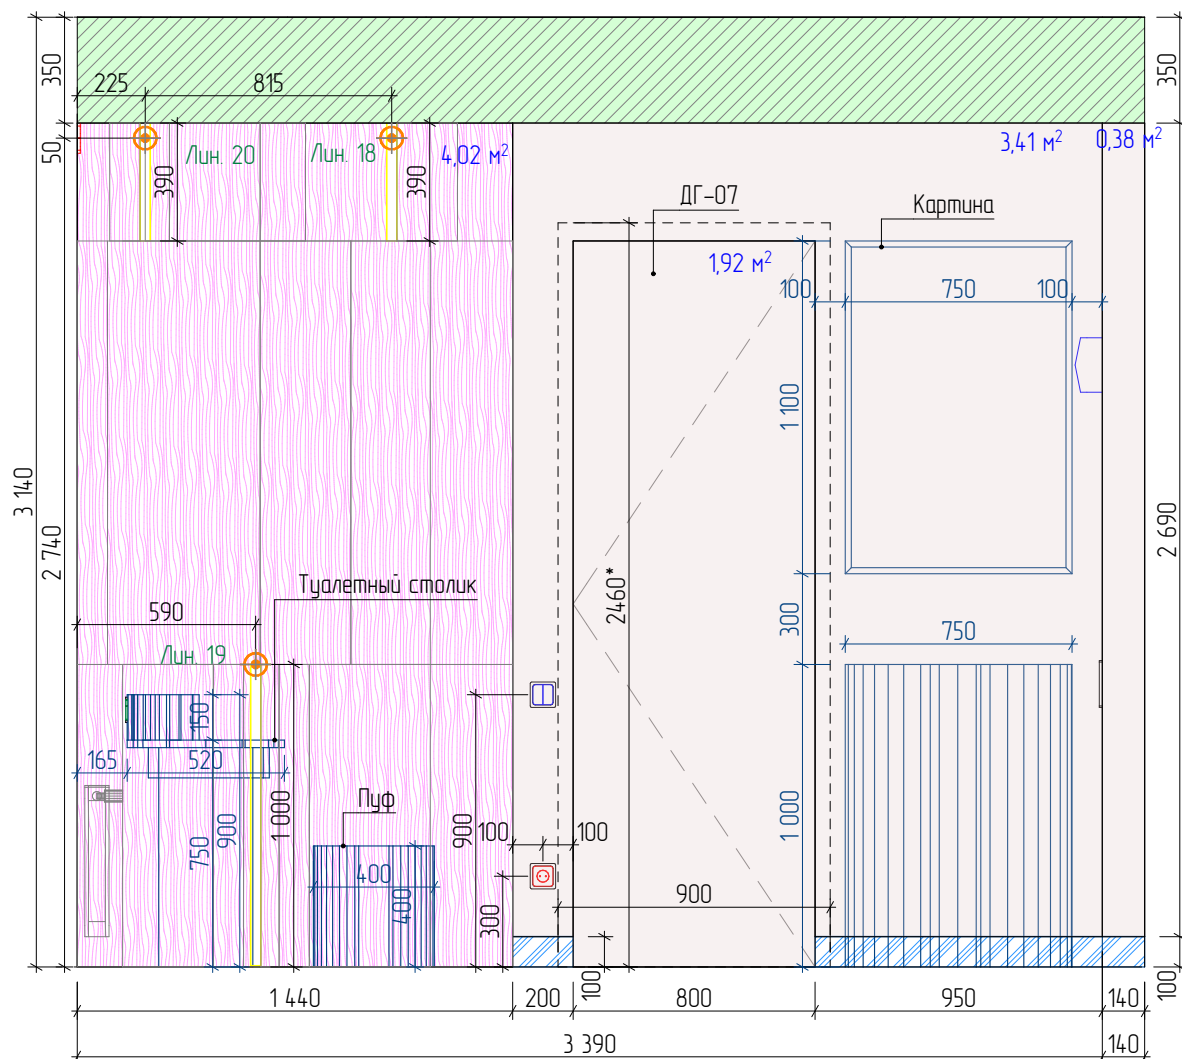

И-10 Развертка стены 1:25

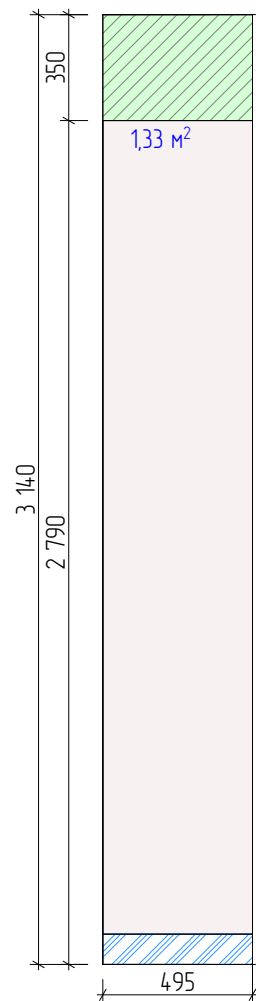

Условные обозначения:

- Плинтус №1. Теневой плинтус скрытого монтажа с МДФ вставкой. Теневой зазор от пола 100 мм. Цвет при выборе образца (в цвет стен).
- Монтаж конструкций из ГКВЛ
- Покраска №1. Выполнить по подготовленной поверхности (стеклохолст*). Цвет при выборе образца (бежевый*).
- МДФ панель №5. Цвет и фактура при выборе образца (ржавый металл*).
- Розетка 220 V
- Переключатель двухклавишный
- Выключатель двухклавишный
- Вывод 220 V
- Вывод электрокабеля для светодиодной ленты

Примечания:

- *- размеры уточнить по месту после выполнения черновых отделочных работ.
- Выключатели располагать от уровня чистого пола на высоте 900 мм. Исключения указаны на чертеже.
- Розетки располагать от уровня чистого пола на высоте 300 мм. Исключения указаны на чертеже.
- Цвет окрашивания плинтуса уточнить после согласования образца.
- Высоту проемов выполнить 2460 мм от уровня чистого пола. Уточнить после подбора и согласования модели дверей.
- Плинтус подрезать по месту в местах стыковки с дверями и мебелью.
- Внутреннее наполнение мебели разработать со специалистами.
- Серым/синим цветом показаны размеры мебели. Мебель разработать со специалистами, размеры уточнить после выполнения чистовой отделки.

МСК 392.12.25-ЭП ПРЕМИУМ			
Эскизный дизайн-проект интерьера квартиры в г. Москва ЖК "Остров", ул. Нижние Мневники д. 7			
Мастер спальниРазвертки стен И-06, И-07, И-08, И-09, И-10.			
Дизайнер интерьера Александр Батеньков	Стадия	Лист	Листов
	ЭП	94	120
		Подп.	Дата
ГАП	Батеньков А.С.		
Гл. дизайнер	Власова В.А.		
Гл. проектиров.	Луныкова В.Н.		
Разработал	Ильина Е.Е.		

Ведомость отделочных материалов.

№	Обозначение	Наименование	Кол-во	Примечание
Пол:				
1		Пробковый компенсатор	0,8	м.п.
2		Покрытие №01. Паркет. Изготовитель: Lab Arte, кол-я: Angle Дуб Натур, размер: 500x150 мм, точный артикул и производителя уточнить при выборе образца, толщину уточнить при закупе.	29,87	м²
Стены:				
3		Плинтус №1. Теневой плинтус скрытого монтажа с МДФ вставкой. Теневой зазор от пола 100 мм. Цвет при выборе образца (в цвет стен).	11,86	м.п.
4		Покраска №1. Выполнить по подготовленной поверхности (стеклохолст*). Цвет при выборе образца (бежевый*).	45,01	м²
5		МДФ панель №4. Цвет и фактура при выборе образца (ржавый металл*).	10,52	м²
6		МДФ панель №5. Цвет и фактура при выборе образца (ржавый металл*).	9,07	м²
7		МДФ панель №6. 3д панель. Цвет и фактура при выборе образца (ржавый металл*).	3,26	м²
Откосы:				
8		Покраска №2. Выполнить по подготовленной поверхности (стеклохолст*). Цвет при выборе образца (белый*).	3,56	м²
Подоконник:				
9		Подоконник №1. Искусственный камень. Цвет при выборе образца.	1,42	м²


МСК 392.12.25–ЭП ПРЕМИУМ			
Эскизный дизайн–проект интерьера квартиры в г. Москва ЖК “Остров”, ул. Нижние Мневники д. 7			
Мастер спальниВедомость отделочных материалов.			
Дизайнер интерьера  №1 Александр Батеньков	Стадия	Лист	Листов
	ЭП	95	120
		Подп.	Дата
Г.АП	Батеньков А.С.		
Гл. дизайнер	Власова В.А.		
Гл. проектиров.	Луныкова В.Н.		
Разработал	Ильина Е.Е.		



МСК 392.12.25-ЭП ПРЕМИУМ			
Эскизный дизайн-проект интерьера квартиры в г. Москва ЖК "Остров", ул. Нижние Мневники д. 7			
Мастер ваннаяВидовые точки.			
Дизайнер интерьера  Александр Батеньков	Стадия	Лист	Листов
	ЭП	96	120
		Подп.	Дата
ГАП	Батеньков А.С.		
Гл. дизайнер	Власова В.А.		
Гл. проектиров.	Луныкова В.Н.		
Разработал	Ильина Е.Е.		





МСК 392.12.25-ЭП ПРЕМИУМ			
Эскизный дизайн-проект интерьера квартиры в г. Москва ЖК "Остров", ул. Нижние Мневники д. 7			
Мастер ваннаяВидовые точки.			
Дизайнер интерьера  Александр Батеньков	Стадия	Лист	Листов
	ЭП	97	120
		Подп.	Дата
ГАП	Батеньков А.С.		
Гл. дизайнер	Власова В.А.		
Гл. проектиров.	Луныкова В.Н.		
Разработал	Ильина Е.Е.		

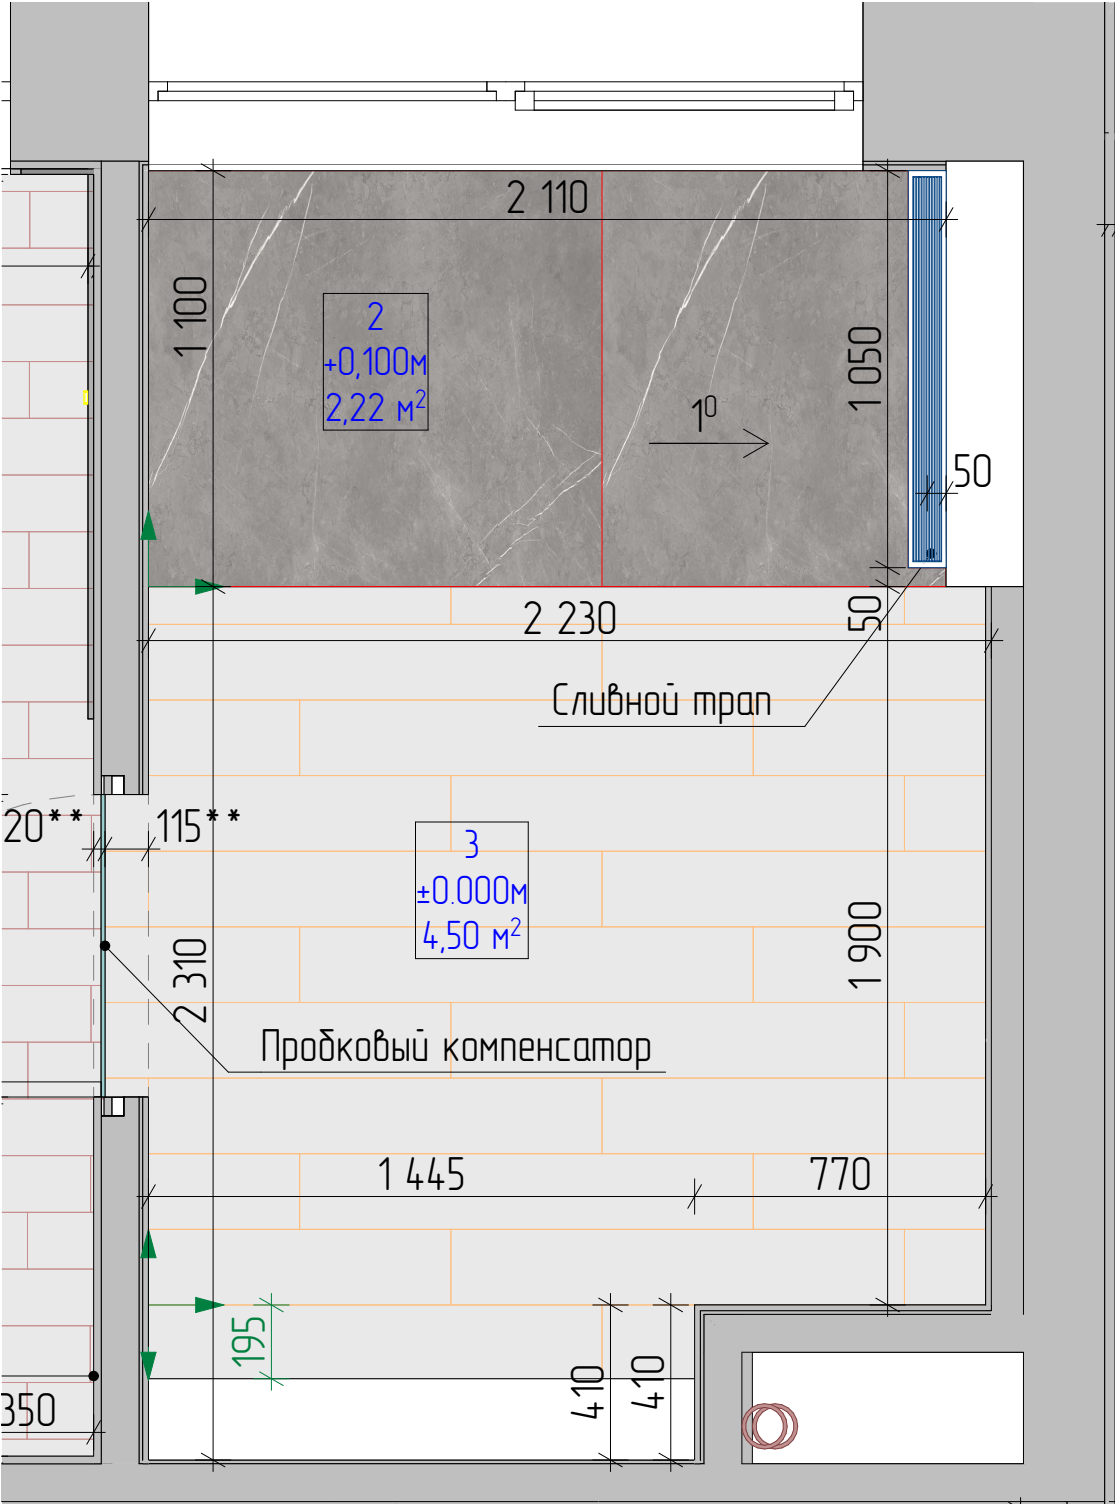

Условные обозначения:


↑ ↓
Направление и начало укладки

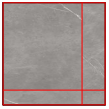2  Покрытие №02. Керамогранит. Изготовитель: Elegant Grey, кол-я: Forte Dei Marmi, размер: 1200x1200 мм, толщину уточнить при закупке.

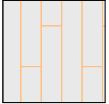3  Покрытие №03. Керамогранит. Изготовитель: Nutmeg, кол-я: Woodslate Life, размер: 1200x200 мм, толщину уточнить при закупке.

- Примечания:
- *– размеры уточнить по месту после выполнения черновых отделочных работ.
 - За отметку ±0,000 принят уровень чистого пола.
 - Во влажных помещениях предусмотреть гидроизоляцию пола с заведением на стены на 150 мм.
 - Совместить швы плитки на подиумах и основном полу.
 - При монтаже напольных покрытий уточнить необходимость устройства дверных проемов с порогами.
 - *– размеры уточнить по месту после выполнения черновых отделочных работ и установки дверей со скрытой коробкой.
 - **–размер уточнить по месту в зависимости от точного расположения полотна двери, стыковка двух разных напольных покрытий должна проходить точно по центру вдоль дверного полотна.

МСК 392.12.25–ЭП ПРЕМИУМ			
Эскизный дизайн–проект интерьера квартиры в г. Москва ЖК "Остров", ул. Нижние Мневники д. 7			
Мастер ваннаяПлан отделки пола.			
Дизайнер интерьера  №1 Александр Батеньков	Стадия	Лист	Листов
	ЭП	98	120
		Подп.	Дата
ГАП	Батеньков А.С.		
Гл. дизайнер	Власова В.А.		
Гл. проектиров.	Луцькова В.Н.		
Разработал	Ильина Е.Е.		

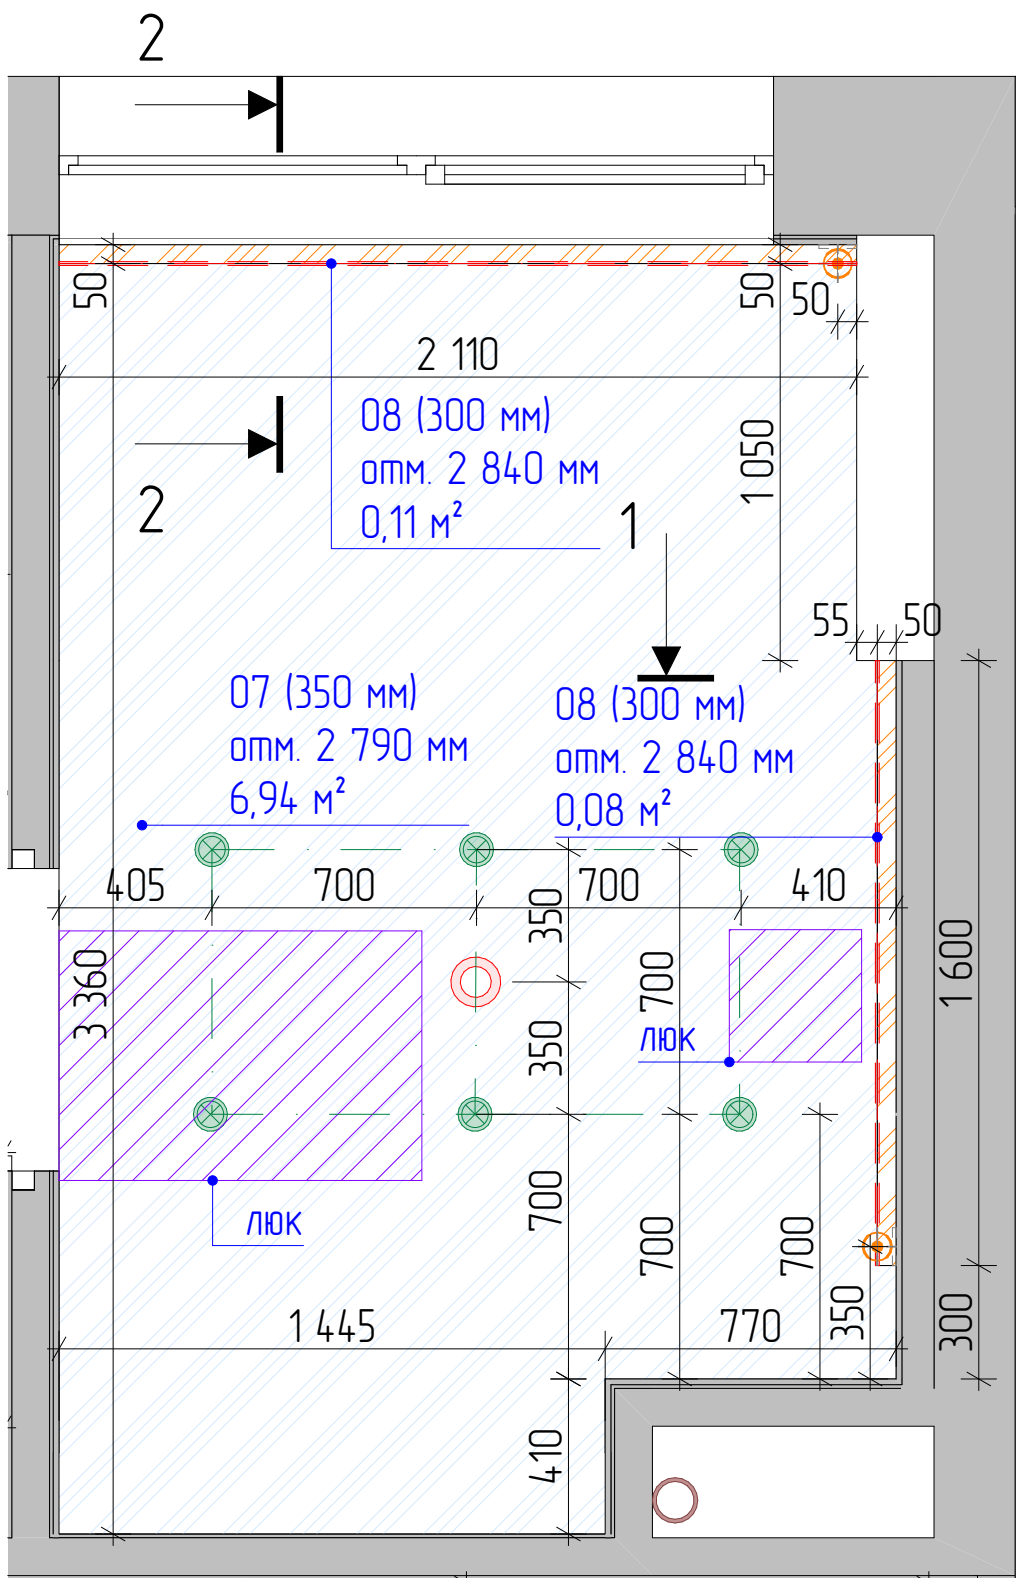

- Условные обозначения:
- Выход 220V
 - Выход электрокабеля для светодиодной ленты
 - Диффузор, вытяжка
 - Светильник точечный встраиваемый влагозащищенный
 - Светодиодная лента, влагозащищенная
 - Люк доступа

- Примечания:
- * – размеры уточнить по месту после выполнения черновых работ.
 - Выполнить уровни потолка из влагостойкого ГКЛ для предотвращения деформации потолка при затоплении.
 - Высоту уровней потолка отсчитывать от существующей ж/б плиты перекрытия помещения.
 - Во влажных помещениях обои под покраску на потолок не клеить, заменить на оштукатуривание по армирующей сетке, согласовать со специалистами.
 - От вытяжки провести вентиляционный короб до общедомового канала в конструкции потолка, уточнить по месту со специалистами и заказчиком.
 - Шумоизоляцию разработать со специалистами, уточнить состав и толщину слоев шумоизоляционных материалов. Уточнить необходимость устройства с заказчиком.

МСК 392.12.25–ЭП ПРЕМИУМ

Эскизный дизайн–проект интерьера квартиры в г. Москва ЖК "Остров", ул. Нижние Мневники д. 7

Мастер ваннаяПлан отделки потолка.

Дизайнер интерьера №1 Александр Батеньков	Стадия	Лист	Листов
	ЭП	99	120
		Подп.	Дата
ГАП	Батеньков А.С.		
Гл. дизайнер	Власова В.А.		
Гл. проектиров.	Луныкова В.Н.		
Разработал	Ильина Е.Е.		

Условные потолки				
№	Обозначение	Опуск	Примечания	Площадь м2
07		350	Потолок ГКЛ/В, Окрасить в цвет выбранного образца (белый) по оштукатуренной поверхности.	6,94
08		300	Потолок ГКЛ/В, Окрасить в цвет выбранного образца (белый) по оштукатуренной поверхности.	0,19

Электровывод для
светодиодной подсветки полок
h=1 260 мм, h=1 650 мм, h=2 040 мм

Электропривод для штор h=2 990 мм

Электровывод для светодиодной
подсветки подиума h=50 мм

Разместить вертикально
в одной рамке с выключателями,
см. развертку стены h=1 000 мм

Электровывод для светодиодной
подсветки зеркала h=2 500 мм

Для холодильника
косметики h=500 мм

Для унитаза h=220* мм,
см. ТУ подключения
унитаза

h=500 мм

h=1 000 мм

Для блоков СППВ
h=1 700 мм

Для
водонагревателя
h=2 200 мм

h=350 мм


Электровывод для
светодиодной
подсветки h=1 500 мм

я сейфа
1 000 мм

- Условные обозначения:
- Розетка 220V влагозащищенная
 - Вывод электрокабеля для варочной поверхности
 - Вывод 220V

- Примечания:
- * – размеры уточнить по месту.
 - Розетки располагать от уровня чистого пола на высоте 0,300 м. Исключения указаны на чертеже.
 - Размещение всех выводов и розеток согласовать со специалистами «Умный дом».
 - Размеры и характеристики радиаторов отопления согласовать со специалистами, предусмотреть терморегуляторы.
 - Датчики пожарной и охранной сигнализации и электровыводы для них разместить совместно со специалистами, предварительно вызвав их на объект.
 - Размещение розеток и электровыводов по высоте см. на развертках стен.

МСК 392.12.25–ЭП ПРЕМИУМ			
Эскизный дизайн–проект интерьера квартиры в г. Москва ЖК "Остров", ул. Нижние Мневники д. 7			
Мастер ваннаяПлан размещения электрооборудования.			
Дизайнер интерьера  №1 Александр Батеньков	Стадия	Лист	Листов
	ЭП	100	120
		Подп.	Дата
ГАП	Батеньков А.С.		
Гл. дизайнер	Власова В.А.		
Гл. проектиров.	Луцькова В.Н.		
Разработал	Ильина Е.Е.		

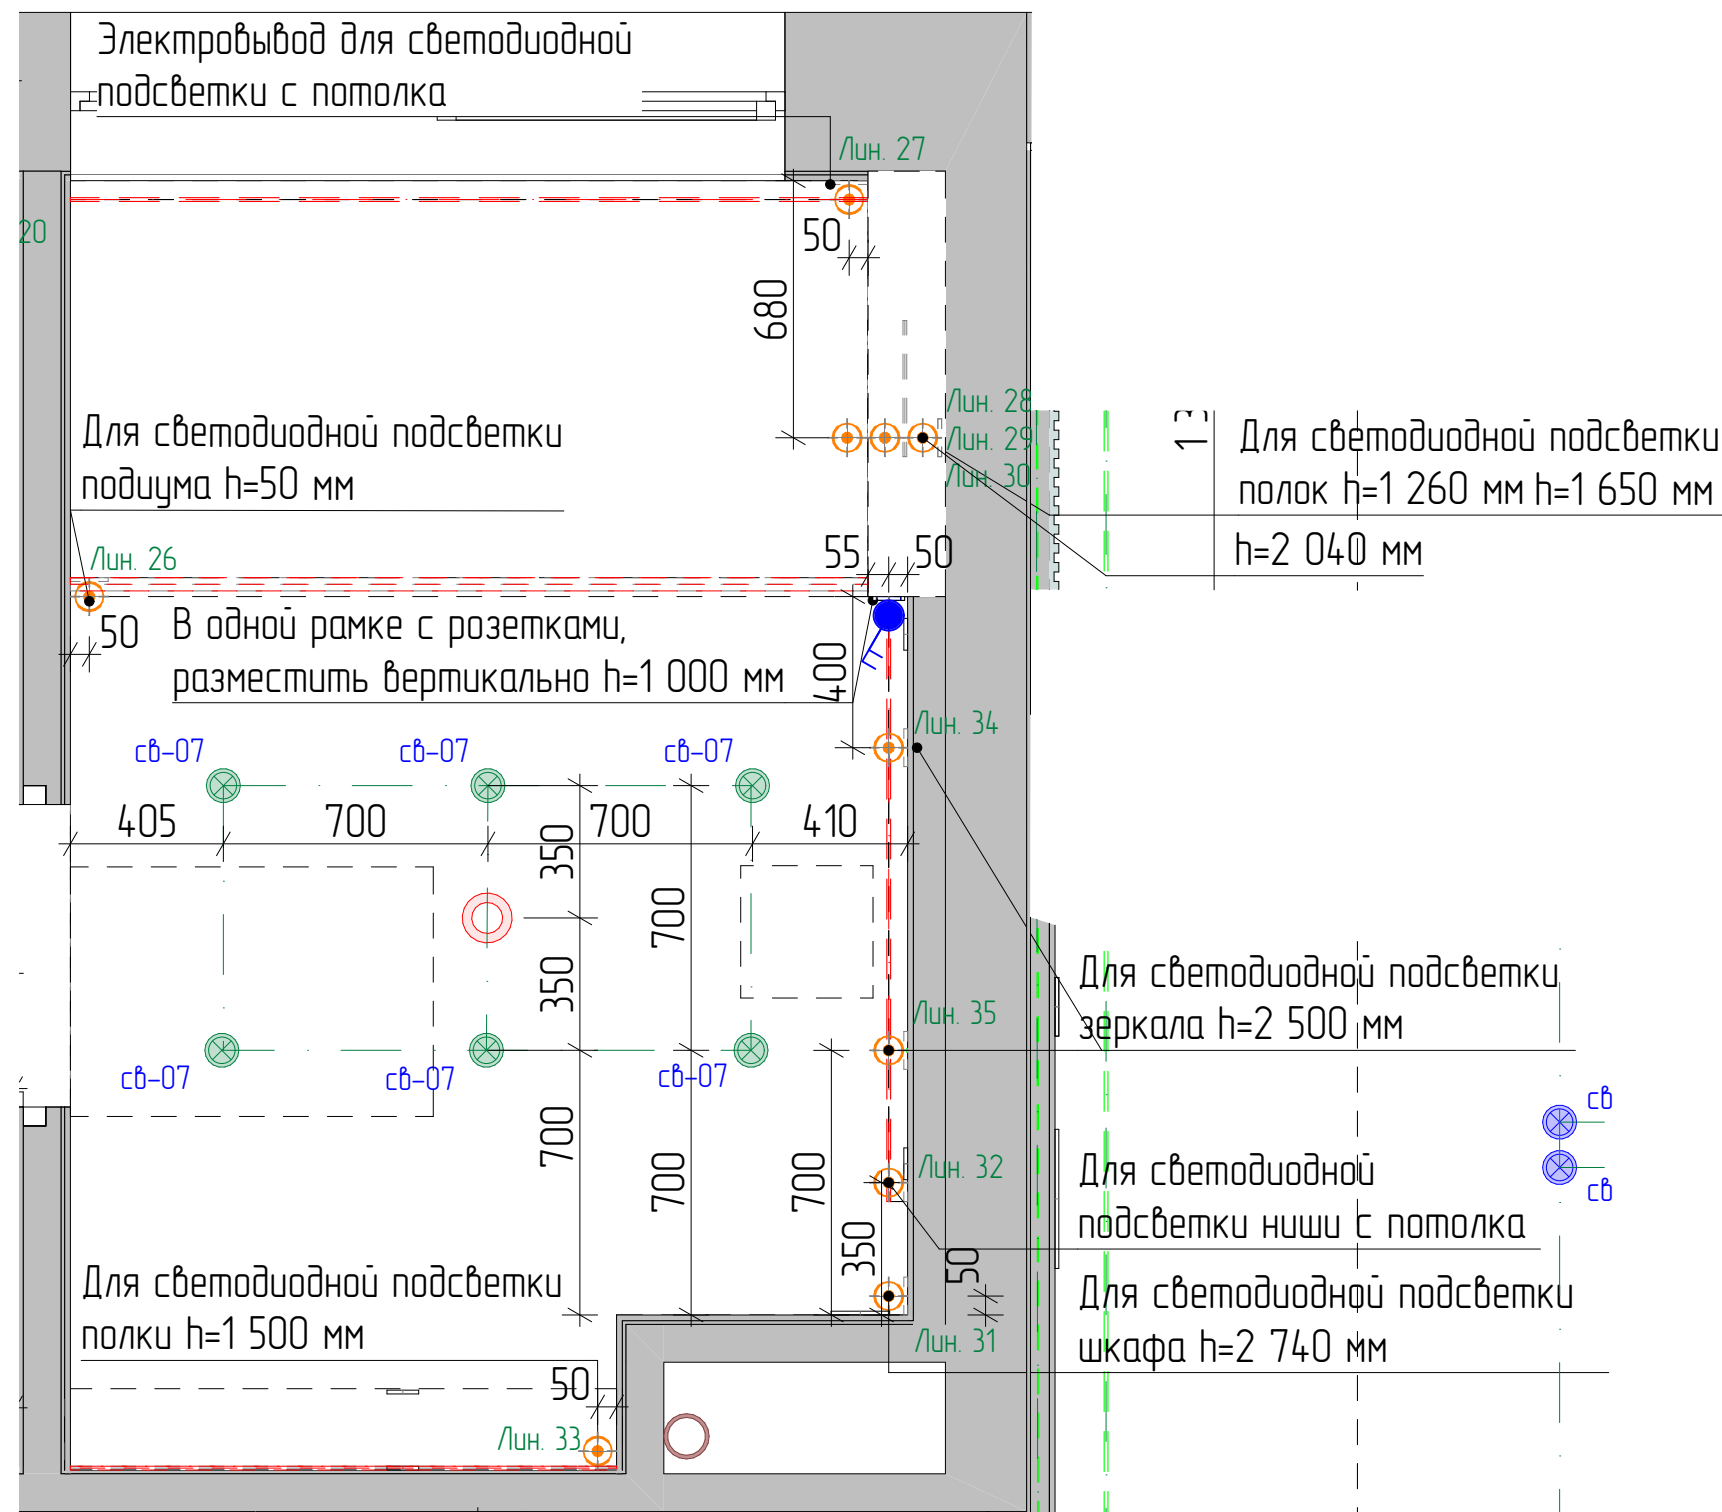


- Условные обозначения:
- Выход 220V
 - Выход электрокабеля для светодиодной ленты
 - Диффузор, вытяжка
 - Светильник точечный встраиваемый влагозащищенный
 - Светодиодная лента, влагозащищенная
 - Выключатель двухклавишный

Примечания:


- * – размеры уточнить по месту.
- Выключатели располагать от уровня чистого пола на высоте 0,900 м. Исключения указаны на чертеже.
- Светильники, встраиваемые в мебель, согласовать с изготовителями мебели.

МСК 392.12.25-ЭП ПРЕМИУМ			
Эскизный дизайн-проект интерьера квартиры в г. Москва ЖК "Остров", ул. Нижние Мневники д. 7			
Мастер ваннаяПлан размещения освещения и выключателей.			
Дизайнер интерьера №1  Александр Батеньков	Стадия	Лист	Листов
	ЭП	101	120
		Подп.	Дата
ГАП	Батеньков А.С.		
Гл. дизайнер	Власова В.А.		
Гл. проектиров.	Луныкова В.Н.		
Разработал	Ильина Е.Е.		

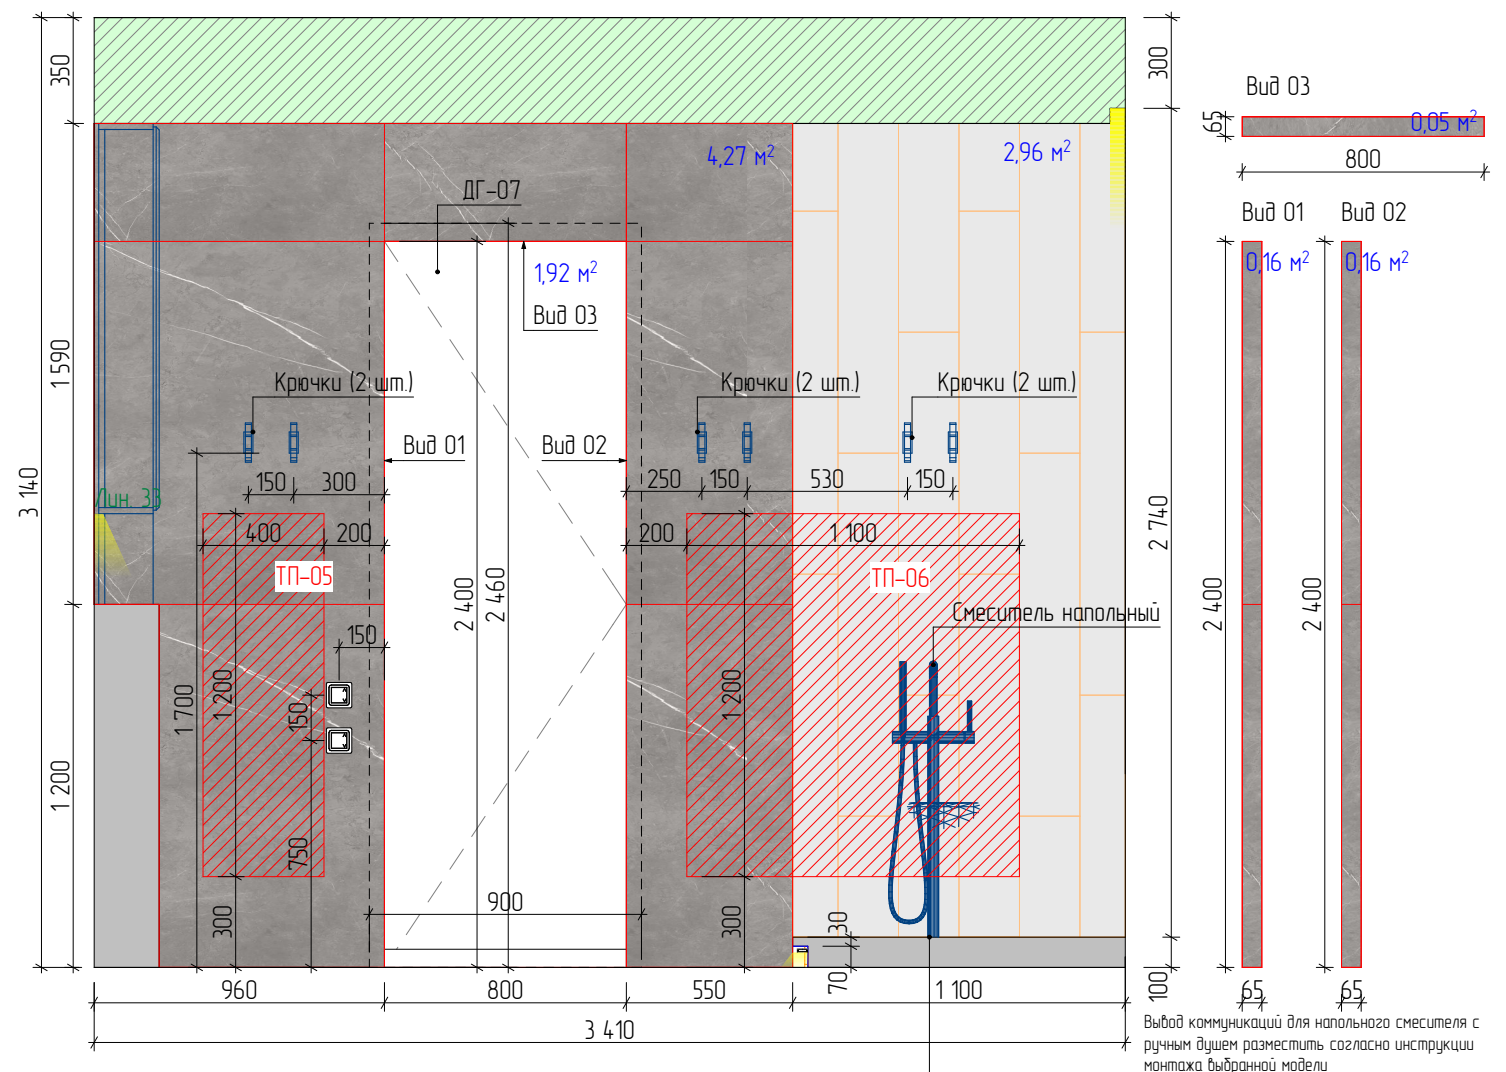

Условное обозначение:






-  Керамогранит №01. Керамогранит. Изготовитель: Elegant Grey, кол-я: Forte Dei Marmi, размер: 1200x1200 мм, толщину уточнить при заказе.
 -  Керамогранит №02. Керамогранит. Изготовитель: Nutmeg, кол-я: Woodslate Life, размер: 1200x200 мм, толщину уточнить при заказе.
 -  Направление и начало укладки
 -  Вывод коммуникаций (ХВС, ГВС, канал-ция)
 -  Вывод электрокабеля для светодиодной ленты
 -  Регулятор теплого пола
 -  Теплый пол, электрические маты

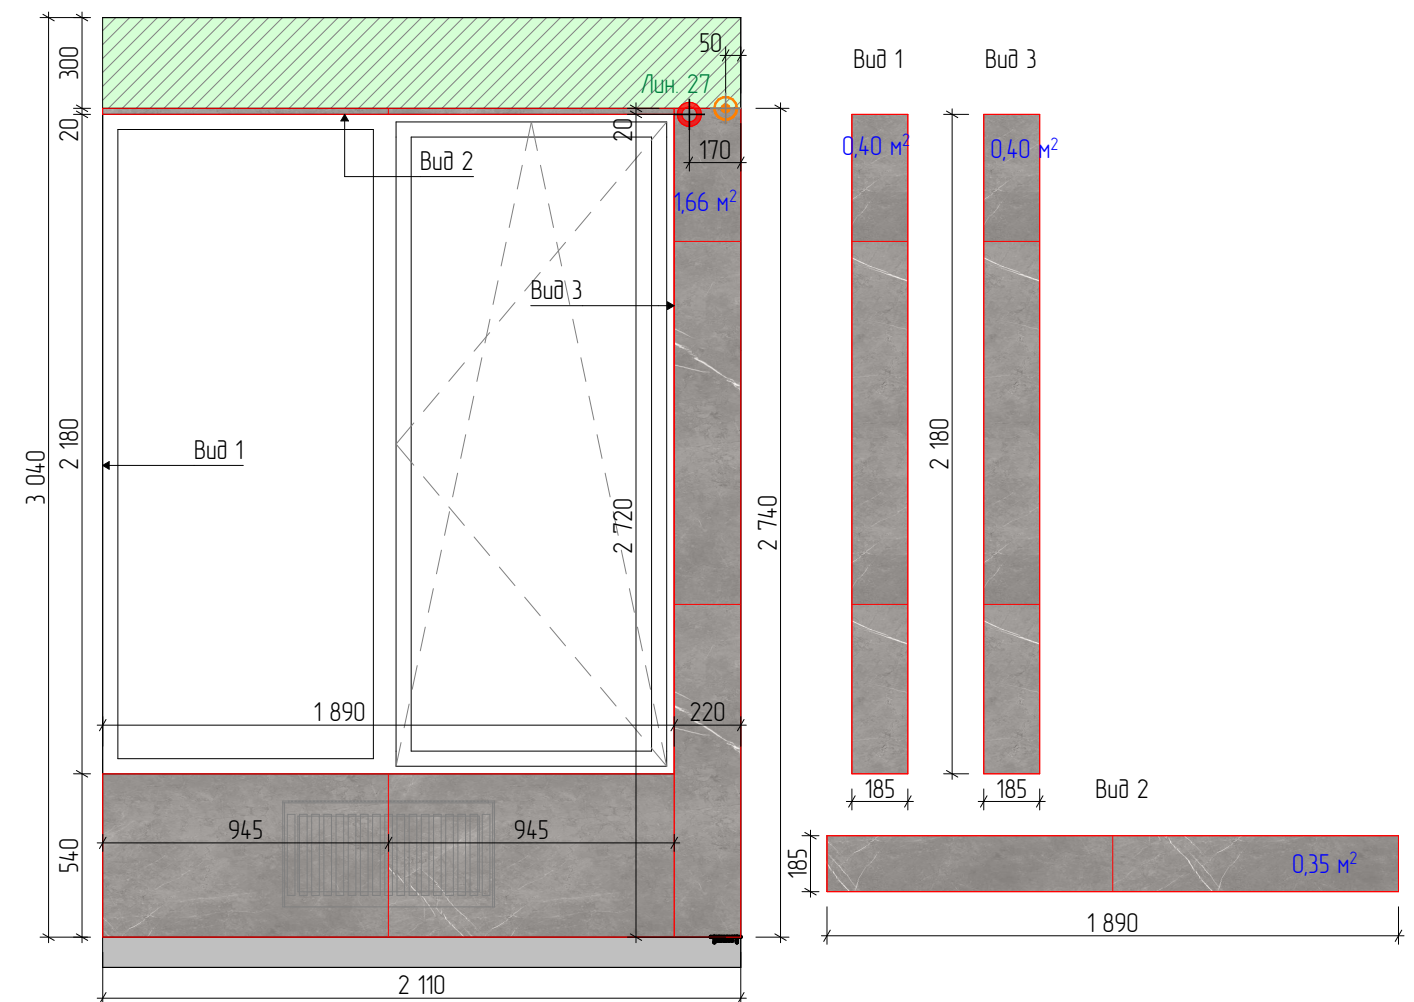

Примечания:


1. * – размеры уточнить по месту после выполнения черновых отделочных работ.
2. Регуляторы теплого пола располагать от уровня чистого пола на высоте 750 мм. Исключения указаны на чертеже.
3. Размещение выводов для отопления согласовать со специалистами.
4. Предусмотреть люк скрытого монтажа для доступа к коммуникациям, размещение уточнить по месту.
5. Совместить швы плитки на смежных стенах и полу.
6. Точную привязку выводов коммуникаций решить после выбора оборудования по инструкции монтажа.
7. Предусмотреть гидроизоляцию пола с заведением на стену до потолка.
8. ** – размер уточнить по инструкции монтажа оборудования.
9. Розетки, выключатели, регуляторы теплого пола размещать по центру керамической плитки.
10. Высоту проемов выполнить 2460 мм от уровня чистого пола. Уточнить после подбора и согласования модели дверей.
11. Внутреннее наполнение мебели разработать со специалистами.
12. Серым/синим цветом показаны размеры мебели. Мебель разработать со специалистами, размеры уточнить после выполнения чистовой отделки.

МСК 392.12.25-ЭП ПРЕМИУМ			
Эскизный дизайн-проект интерьера квартиры в г. Москва ЖК "Остров", ул. Нижние Мневники д. 7			
Мастер ваннаяРазвертки стен К-01, К-02.			
Дизайнер интерьера №1  Александр Батеньков	Студия	Лист	Листов
	ЭП	102	120
		Подп.	Дата
ГАП	Батеньков А.С.		
Гл. дизайнер	Власова В.А.		
Гл. проектиров.	Луныкова В.Н.		
Разработал	Ильина Е.Е.		

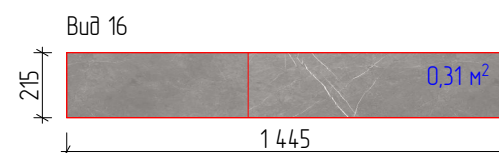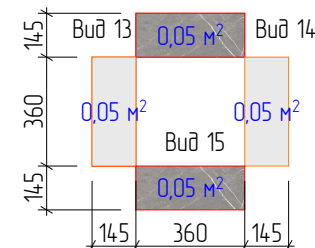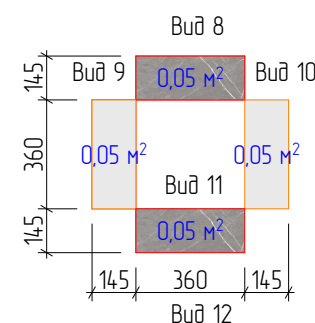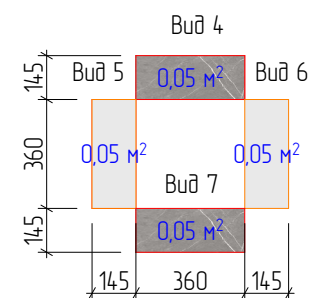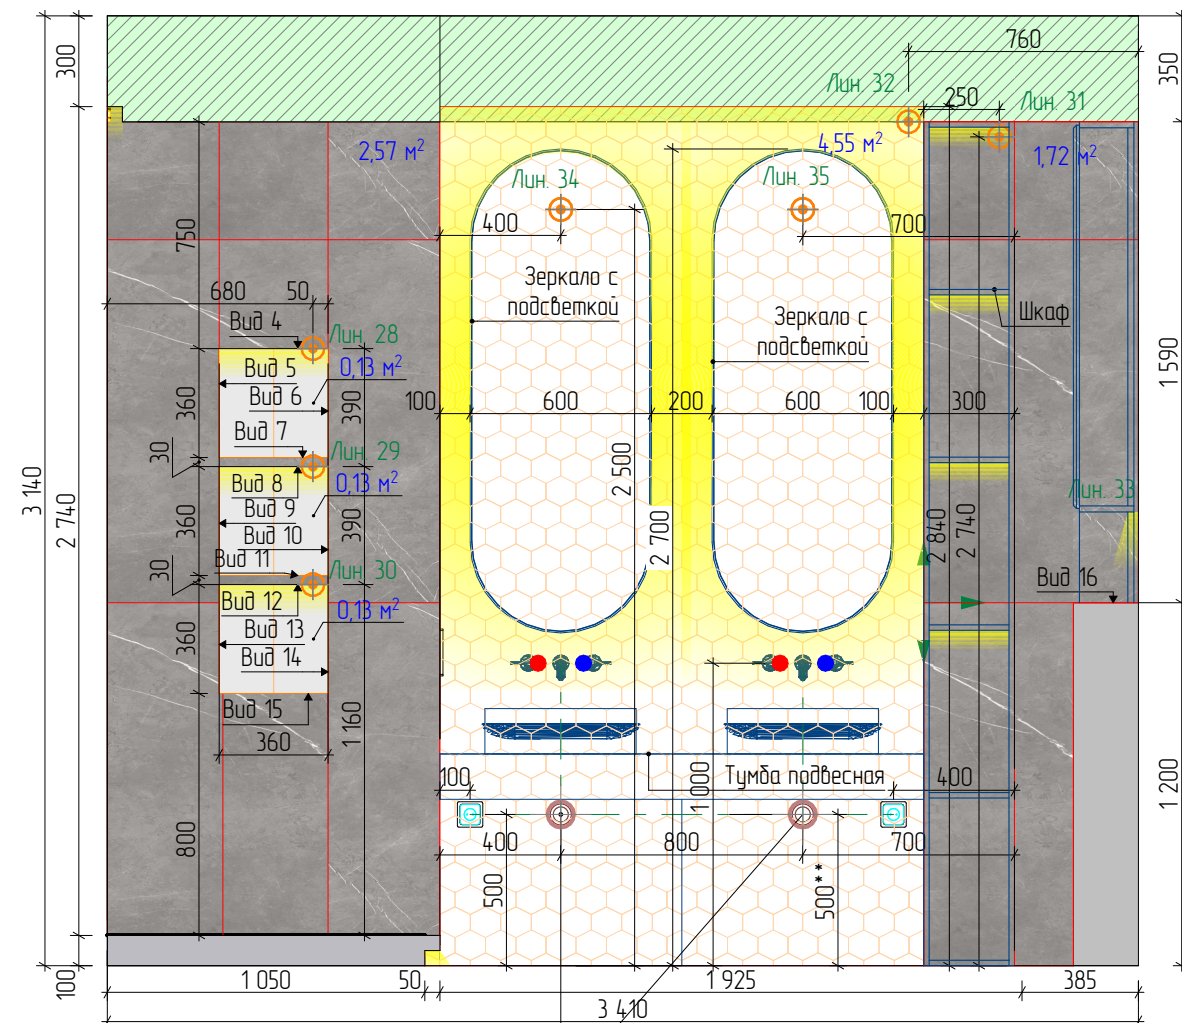


Примечания:

1. * – размеры уточнить по месту после выполнения черновых отделочных работ.
2. Выключатели располагать от уровня чистого пола на высоте 900 мм. Исключения указаны на чертеже.
3. Розетки располагать от уровня чистого пола на высоте 300 мм. Исключения указаны на чертеже.
4. Предусмотреть люк скрытого монтажа для доступа к коммуникациям, размещение уточнить по месту.
5. Совместить швы плитки на смежных стенах и полу.
6. Точную привязку выводов коммуникаций решить после выбора оборудования по инструкции монтажа.
7. Предусмотреть гидроизоляцию пола с заведением на стену до потолка.
8. ** – размещение вывода 220V для электрического полотенцесушителя уточнить после подбора модели по технической документации.
9. ** – размер уточнить по инструкции монтажа оборудования.
10. Розетки, выключатели, регуляторы теплого пола размещать по центру керамической плитки.
11. Внутреннее наполнение мебели разработать со специалистами.
12. Серым/синим цветом показаны размеры мебели. Мебель разработать со специалистами, размеры уточнить после выполнения чистовой отделки.

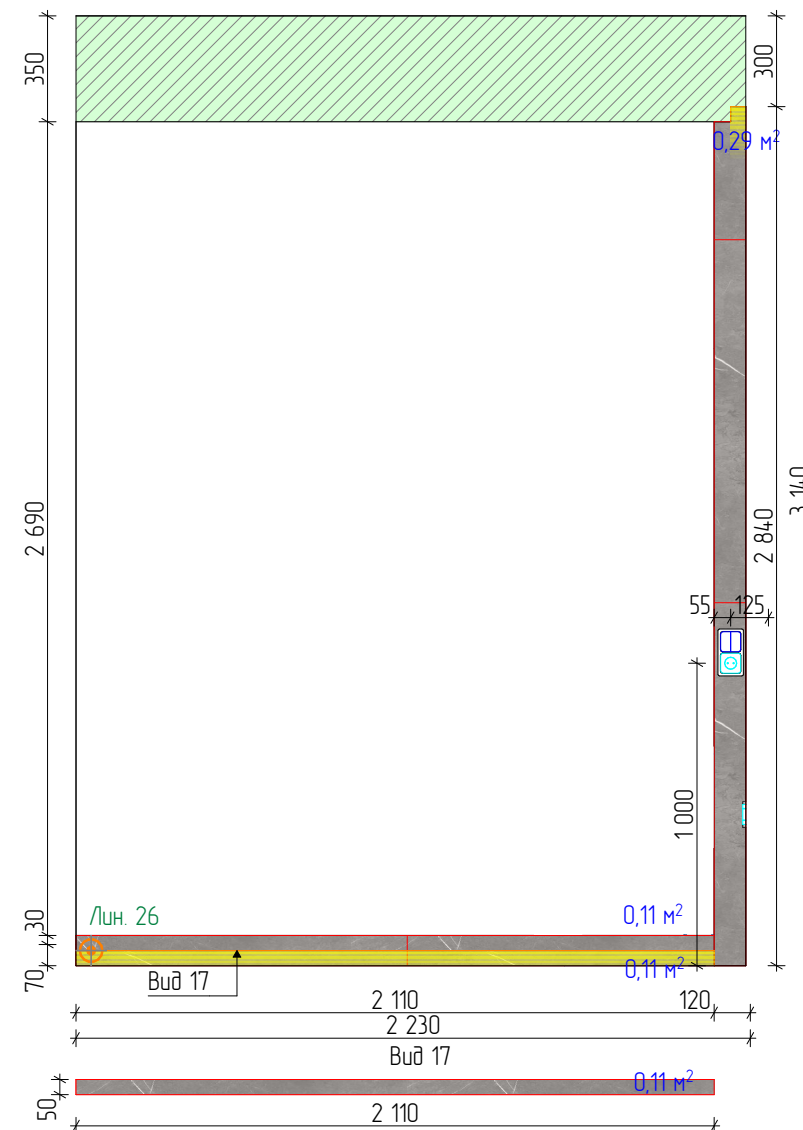

Условное обозначение:

-  Керамогранит №01. Керамогранит. Изготовитель: Elegant Grey, кол-я: Forte Dei Marmi, размер: 1200x1200 мм, толщину уточнить при заказе.
-  Керамогранит №02. Керамогранит. Изготовитель: Nutmeg, кол-я: Woodslate Life, размер: 1200x200 мм, толщину уточнить при заказе.
-  Керамогранит №03. Керамогранит, размер и толщину уточнить при заказе.
-  Покраска №2. Выполнить по подготовленной поверхности (стеклохолст*). Цвет при выборе образца (белый*).
-  Направление и начало укладки
-  Вывод коммуникаций (ХВС, ГВС, канал-ция)
-  Вывод электрокабеля для светодиодной ленты
-  Розетка 220 V, влагозащищенная IP44 и выше
-  Выключатель двухклавишный
-  Вывод 220 V

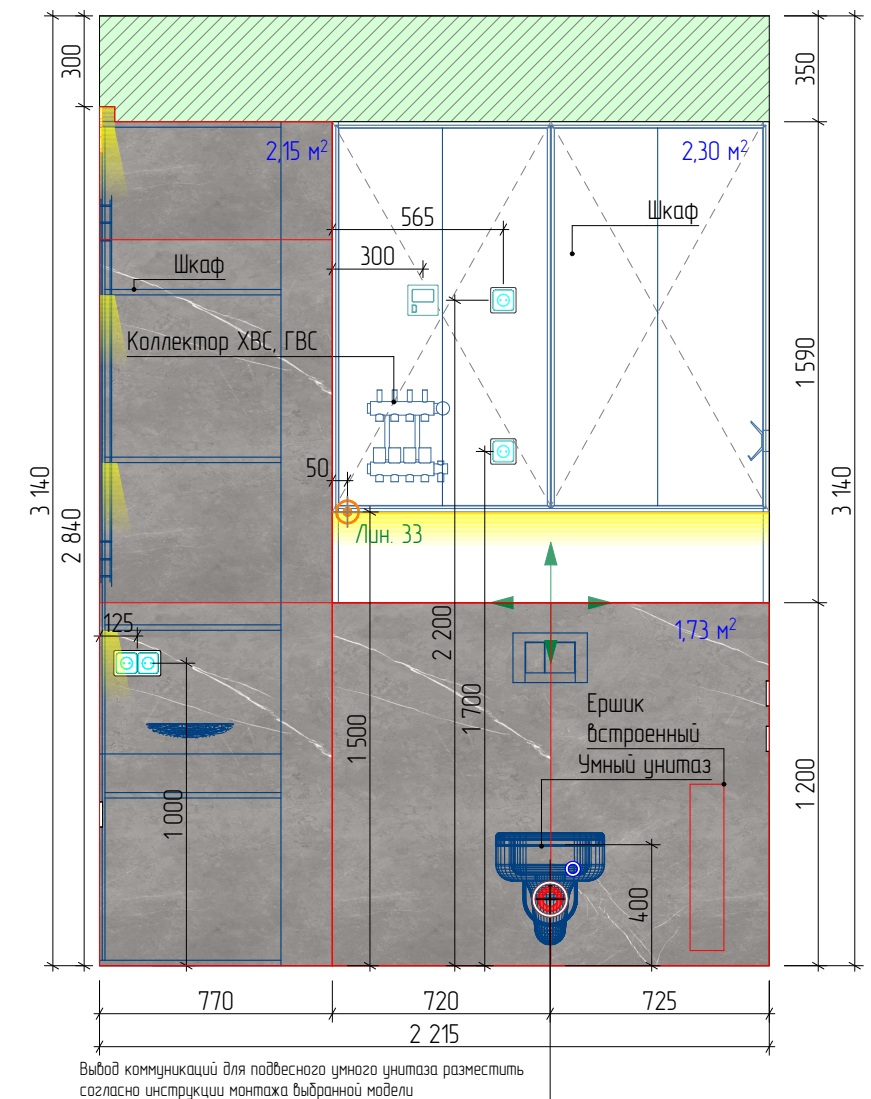

МСК 392.12.25-ЭП ПРЕМИУМ			
Эскизный дизайн-проект интерьера квартиры в г. Москва ЖК "Остров", ул. Нижние Мневники д. 7			
Мастер баннаяРазвертки стен К-03, К-04, К-05.			
Дизайнер интерьера №1  Александр Батеньков	Студия	Лист	Листов
	ЭП	103	120
		Подп.	Дата
ГАП	Батеньков А.С.		
Гл. дизайнер	Власова В.А.		
Гл. проектиров.	Луныкова В.Н.		
Разработал	Ильина Е.Е.		

Ведомость отделочных материалов.

№	Обозначение	Наименование	Кол-во	Примечание
Пол:				
1		Покрытие №03. Керамогранит. Изготовитель: Nutmeg, кол-я: Woodslate Life, размер: 1200х200 мм, толщину уточнить при закупе.	4,50 22	м² укладки шт.
2		Покрытие №02. Керамогранит. Изготовитель: Elegant Grey, кол-я: Forte Dei Marmi, размер: 1200х1200 мм, толщину уточнить при закупе.	2,22 2	м² укладки шт.
Стены:				
3		Покраска №3. Влагостойкая. Выполнить по оштукатуренной поверхности. Цвет при выборе образца (белый*).	2,30	м²
4		Керамогранит №02. Керамогранит. Изготовитель: Nutmeg, кол-я: Woodslate Life, размер: 1200х200 мм, толщину уточнить при закупе.	3,65 19	м² укладки шт.
5		Керамогранит №01. Керамогранит. Изготовитель: Elegant Grey, кол-я: Forte Dei Marmi, размер: 1200х1200 мм, толщину уточнить при закупе.	16,49 18*	м² укладки шт.
6		Керамогранит №03. Керамогранит, размер и толщину уточнить при закупе.	4,55	м² укладки
Подоконник:				
7		Подоконник №1. Искусственный камень. Цвет при выборе образца.	0,35	м²

МСК 392.12.25–ЭП ПРЕМИУМ			
Эскизный дизайн–проект интерьера квартиры в г. Москва ЖК “Остров”, ул. Нижние Мневники д. 7			
Мастер ваннаяВедомость отделочных материалов.			
Дизайнер интерьера  №1 Александр Батеньков	Стадия	Лист	Листов
	ЭП	104	120
		Подп.	Дата
ГАП	Батеньков А.С.		
Гл. дизайнер	Власова В.А.		
Гл. проектиров.	Луцькова В.Н.		
Разработал	Ильина Е.Е.		

Примечания.

[illegible]

МСК 392.12.25-ЭП ПРЕМИУМ			
Эскизный дизайн-проект интерьера квартиры в г. Москва ЖК "Остров", ул. Нижние Мневники д. 7			
Примечания.			
Дизайнер интерьера №1  Александр Батеньков	Стандия	Лист	Листов
	ЭП	105	120
		Подп.	Дата
ГАП	Батеньков А.С.		
Гл. дизайнер	Власова В.А.		
Гл. проектиров.	Луныкова В.Н.		