



ООО "СтройПроект"

*Свидетельство о допуске к определенному виду работ, которые оказывают
влияние на безопасность объектов капитального строительства
№СРО-П-179-12122012*

ИСПОЛНИТЕЛЬНАЯ ДОКУМЕНТАЦИЯ

Электротехническая часть

Заказчик: частное лицо

Объект: Жилая квартира

Адрес: г.Москва, ул.Нижние Мневники, д.7, кв.Сачук Ю.Е.

Директор ООО "СтройПроект" _____ Хаустова Н.В.

Москва 2026г.

7722710940-20260202-1020

(регистрационный номер выписки)

02.02.2026

(дата формирования выписки)

ВЫПИСКА

из единого реестра сведений о членах саморегулируемых организаций в области инженерных изысканий и в области архитектурно-строительного проектирования и их обязательствах

Настоящая выписка содержит сведения о юридическом лице (индивидуальном предпринимателе), осуществляющем подготовку проектной документации:

Общество с ограниченной ответственностью «СтройПроект»

(полное наименование юридического лица/ФИО индивидуального предпринимателя)

1107746171356

(основной государственный регистрационный номер)

1. Сведения о члене саморегулируемой организации:

1.1	Идентификационный номер налогоплательщика	7722710940
1.2	Полное наименование юридического лица (Фамилия Имя Отчество индивидуального предпринимателя)	Общество с ограниченной ответственностью «СтройПроект»
1.3	Сокращенное наименование юридического лица	ООО «СтройПроект»
1.4	Адрес юридического лица Место фактического осуществления деятельности (для индивидуального предпринимателя)	111024, Россия, Москва, Москва, Андроновское ш, 26, корп 6, оф 55
1.5	Является членом саморегулируемой организации	Ассоциация «Объединение проектировщиков «УниверсалПроект» (СРО-П-179-12122012)
1.6	Регистрационный номер члена саморегулируемой организации	П-179-007722710940-0663
1.7	Дата вступления в силу решения о приеме в члены саморегулируемой организации	13.02.2018
1.8	Дата и номер решения об исключении из членов саморегулируемой организации, основания исключения	

2. Сведения о наличии у члена саморегулируемой организации права осуществлять подготовку проектной документации:

2.1 в отношении объектов капитального строительства (кроме особо опасных, технически сложных и уникальных объектов, объектов использования атомной энергии) (дата возникновения/изменения права)	2.2 в отношении особо опасных, технически сложных и уникальных объектов капитального строительства (кроме объектов использования атомной энергии) (дата возникновения/изменения права)	2.3 в отношении объектов использования атомной энергии (дата возникновения/изменения права)
Да, 13.02.2018	Да, 09.01.2018	Нет



3. Компенсационный фонд возмещения вреда		
3.1	Уровень ответственности члена саморегулируемой организации по обязательствам по договору подряда на подготовку проектной документации, в соответствии с которым указанным членом внесен взнос в компенсационный фонд возмещения вреда	Первый уровень ответственности (не превышает двадцать пять миллионов рублей)
3.2	Сведения о приостановлении / прекращении права осуществлять подготовку проектной документации объектов капитального строительства	
4. Компенсационный фонд обеспечения договорных обязательств		
4.1	Дата, с которой член саморегулируемой организации имеет право осуществлять подготовку проектной документации по договорам подряда, заключаемым с использованием конкурентных способов заключения договоров, в соответствии с которым указанным членом внесен взнос в компенсационный фонд обеспечения договорных обязательств	Нет
4.2	Уровень ответственности члена саморегулируемой организации по обязательствам по договорам подряда на подготовку проектной документации, заключаемым с использованием конкурентных способов заключения договоров, в соответствии с которым указанным членом внесен взнос в компенсационный фонд обеспечения договорных обязательств	
4.3	Дата уплаты дополнительного взноса	Нет
4.4	Сведения о приостановлении / прекращении права осуществлять подготовку проектной документации по договорам подряда, заключаемым с использованием конкурентных способов заключения договоров	
5. Фактический совокупный размер обязательств		
5.1	Фактический совокупный размер обязательств по договорам подряда на подготовку проектной документации, заключаемым с использованием конкурентных способов заключения договоров на дату выдачи выписки	Нет

Руководитель аппарата



А.О. Кожуховский



Ведомость рабочих чертежей основного комплекта ЭОМ

№ п/п	Наименование	Примечание
1	Общие данные	
2-3	Однолинейная расчетная схема ЩР	
4	Сеть освещения. План.	
5	Розеточная сеть. План.	
6	Схема дополнительной системы уравнивания потенциалов	

Ведомость прилагаемых и ссылочных документов

Обозначение	Наименование	Примечание
Прилагаемые документы		
- -	Спецификация	- -
Ссылочные документы		
ПУЭ изд. 6, 7	Правила устройства электроустановок	
СП 76.13330.2016	Электротехнические устройства	
СП 256.1325800.2016	Свод правил по проектированию и строительству	

Общие данные

Исполнительная документация электроосвещения и электрооборудования квартиры выполнена на основании разрешения на присоединение мощности, задания заказчика и дизайн-проекта.

Потребителями энергии являются: электрическое освещение, бытовые электроприборы, подключаемые к розеткам.

Электроснабжение квартиры осуществляется от существующего щита этажного по существующему вводу (см. лист 2). Тип системы заземления TN-C-S.

Напряжение питающей сети 230/400В переменного тока частотой 50 Гц. Нейтраль питающего трансформатора глухозаземленная.

В качестве защиты от поражения электрическим током предусматривается: защитное заземление электроустановки, установка УЗО и дополнительная система уравнивания потенциалов согласно ПУЭ п.7.1.88 в ванной и сан. узле с установкой коробки уравнивания потенциалов в трубном сантехническом стояке.

Групповые сети (силовая и осветительная) выполнить кабелем марки ВВГнг(А)-LS, прокладываемым в ПВХ трубах за подвесным потолком, в слое подготовки пола и в штробах стен в слое штукатурки. В ванных комнатах, санузлах, душевых, как правило, должна применяться скрытая электропроводка. (ПУЭ п.7.1.40).

В розеточной сети выполнить фазные и нулевые соединения шлейфом, соединение заземляющих проводников выполнить отдельным ответвлением при помощи клемм Wago. Соединение проводов в сети освещения выполнить в углубленных подрозетниках при помощи клемм Wago. Подключение светильников, не имеющих своей коммутационной коробки, выполнить в распаечной коробке при помощи отдельного ответвления. Все бытовые розетки должны быть с защитным контактом и рассчитаны на ток 16А. Розетки и выключатели скрытой проводки.

Установка электрооборудования допускается только при соблюдении требований главы 7.1 ПУЭ. Подключение должно выполняться в соответствии с заводской инструкцией. Степени защиты светильников и розеток, устанавливаемых в сан. узлах, должны составлять не ниже IP44. Установка розеток в сан. узлах должна выполняться в зоне 3 согласно ГОСТ Р 50571.7.701-2024. Высота установки светильников, размещаемых над зоной 1, в сан. узлах должна быть не менее 2,250 м от пола. Установка распаечных коробок в зонах 1 и 2 указанных помещений не допускается, при установке коробок в зоне 3 - они должны иметь степень защиты не ниже IP44.

Трубы должны иметь сертификат пожарной безопасности в соответствии с ГОСТ ИЕС 60754-2-2015. Расстояние между креплениями труб не более 50см.

Горизонтальное и диагональное штробление запрещено. Штробление монолитных и несущих конструкций запрещено.

Подключение электрооборудования, разрешенного к установке в зоне 1 ванных комнат, должно производиться кабелем через сальниковый ввод, обеспечивающий степень защиты не ниже IP55 (ГОСТ Р 50571.7.701-2024).

Открытые и сторонние проводящие части изделий и оборудования, а также защитные проводники должны быть подключены к дополнительной системе уравнивания потенциалов.

В зоне укладки теплого пола трассы с электропроводкой не прокладывать.

Розетки должны иметь защитное устройство, автоматически закрывающее гнезда штепсельной розетки при вынутой вилке (ПУЭ п. 7.1.49).

Расцветка изоляции жил кабелей согласно ПУЭ п. 2.1.31.

Высота установки электрооборудования от чистого пола, кроме особо оговоренных на чертежах:

ЩР - 1,8 м до верха; выключатели - 0,9 м до оси; розетки - 0,3 м до оси.

Точную привязку розеток, светильников, выключателей и электрооборудования см. дизайн-проект.

Заготовку труб и кабелей производить после контрольного промера длины трассы.

Прокладку труб уточнить при монтаже.

Все оборудование: шкафы, щиты, распаечные коробки, кабели должны быть промаркированы (ПУЭ п.4.1.3, 3.1.7, 3.4.9)

Монтаж электрооборудования выполнить в соответствии со ссылочными документами.



Все изделия должны иметь сертификат соответствия Госстандарта РФ.

Оборудование и материалы, указанные в проекте, могут быть заменены на аналогичные, сертифицированные.

Запрещается:

- Штробление монолитных и несущих конструкций , а также вент.шахт.
- Установка розеток и выключателей на вент.шахтах.

						ИСПОЛНИТЕЛЬНАЯ ДОКУМЕНТАЦИЯ				
						Заказчик: <u>частное лицо</u>				
Изм	Кол.	Лист	№ док	Подп.	Дата	Жилая квартира по адресу: <u>г.Москва, ул.Нижние Мневники, д.7, кв.Сачук Ю.Е.</u>		Стадия	Лист	Листов
								ИД	1	6
ГИП		Сарафонов				Общие данные		ООО "СтройПроект"		
Исполн.		Салюк								
Проверил		Загуменная								

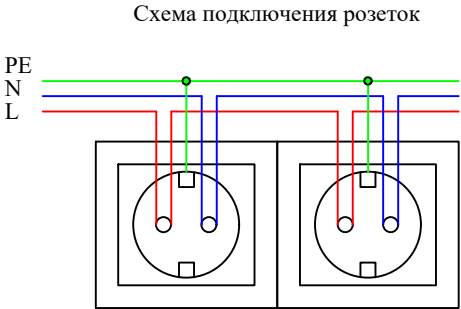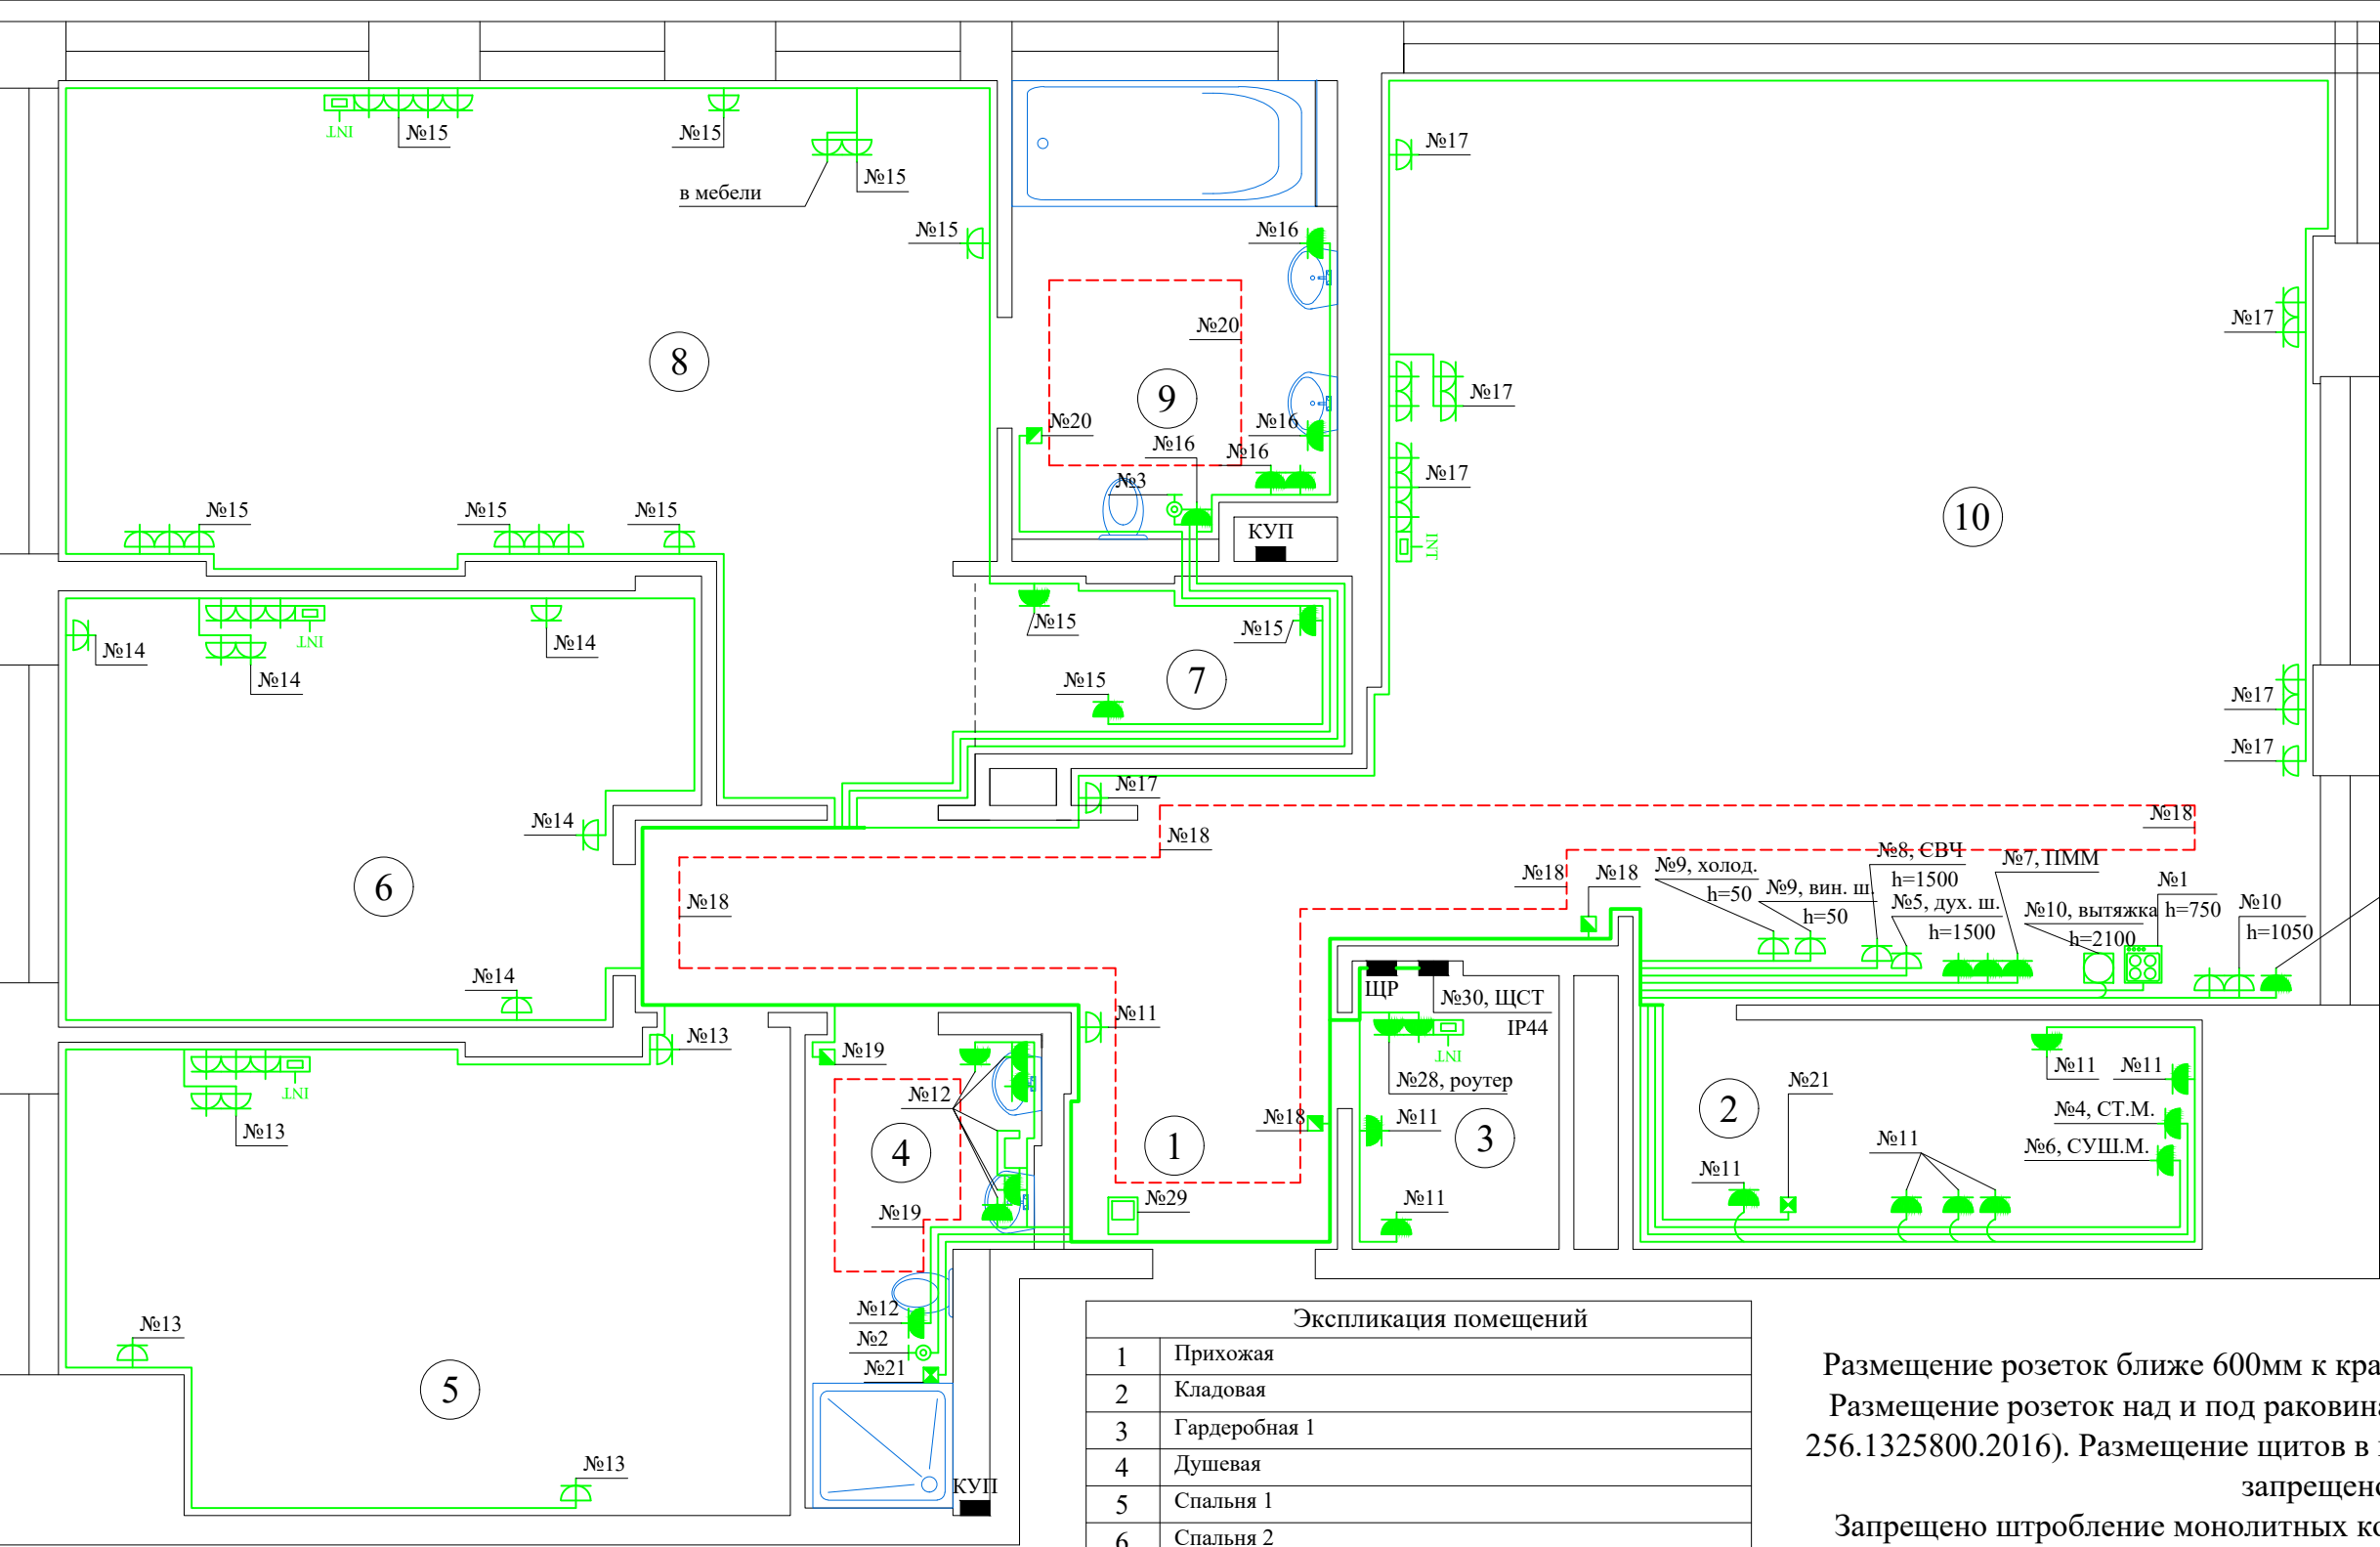


Экспликация помещений	
1	Прихожая
2	Кладовая
3	Гардеробная 1
4	Душевая
5	Спальня 1
6	Спальня 2
7	Гардеробная 2
8	Мастер спальня
9	Мастер ванная
10	Кухня гостиная

Размещение розеток ближе 600мм к краю ванной, душевой запрещено.
Размещение розеток над и под раковинами и мойками запрещено (СП 256.1325800.2016). Размещение щитов в гардеробных, кладовых, шкафах запрещено.
Запрещено штробление монолитных конструкций, а также вентшахт.
При установке розеток и оборудования на вент.короб, нарастить его стену гипсовыми блоками. Установить розетки не повреждая вент.короб.
Обеспечить целостность вент.коробов.

Условные обозначения	
	Розетка штепсельная двухполюсная, с защитным контактом, скрытой установки
	Розетка штепсельная двухполюсная, с защитным контактом, скрытой установки, влагозащищенная, IP44
	Щит распределительный
	Щит слабых токов
	Номер группы по однолинейной схеме
	Коробка уравнивания потенциалов
	Розетка интернет
	Регулятор теплого пола
	Участок теплого пола

Условные обозначения	
	Водонагреватель
	Система от протечки воды и отопления
	Видеодомофон
	Полотенцесушитель

						ИСПОЛНИТЕЛЬНАЯ ДОКУМЕНТАЦИЯ			
						Заказчик: <u>частное лицо</u>			
Изм	Кол.	Лист	№ док	Подп.	Дата	Жилая квартира по адресу: <u>г.Москва, ул.Нижние Мневники, д.7, кв.Сачук Ю.Е.</u>	Стадия	Лист	Листов
ГИП		Сарафонов					ИД	5	6
Исполн.		Салюк							
Проверил		Загуменная				Розеточная сеть. План.	ООО "СтройПроект"		

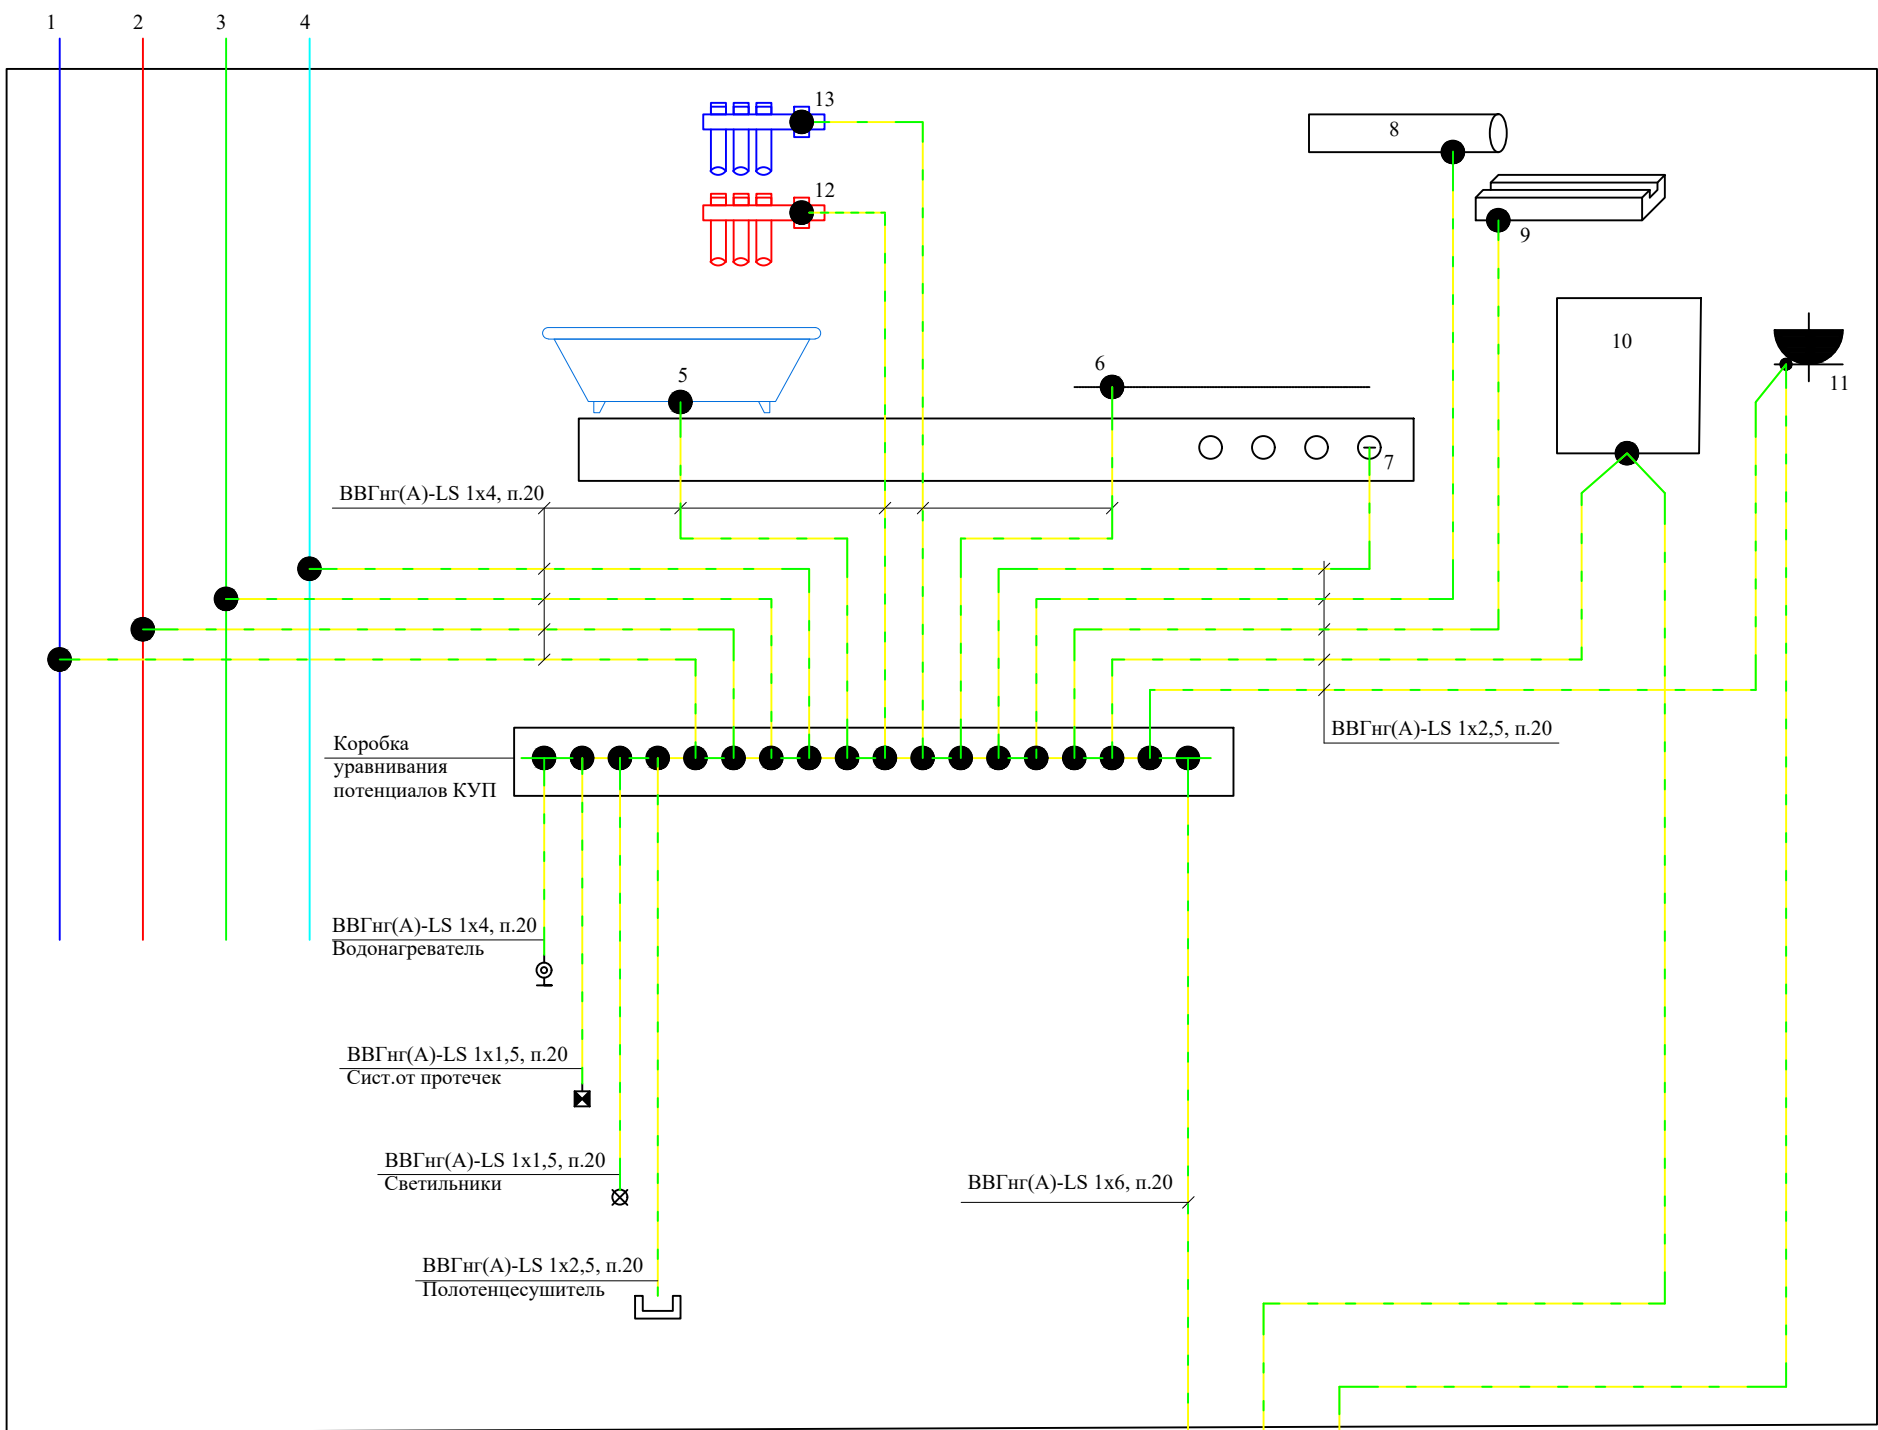

- Сторонние проводящие части (1-6):
- металлический трубопровод холодного водоснабжения (1);
 - металлический трубопровод горячего водоснабжения (2);
 - металлическая труба канализации (3);
 - металлические транзитные трубы (4);
 - металлическая ванна или металлический поддон (5);
 - металлическая сетка (6), закрывающая сверху нагревательный элемент или металлическая оболочка нагревательного кабеля теплого пола (7)
 - металлические воздуховоды (8);
 - металлические каркасы потолка, стен (9)

Открытые проводящие части и нулевые защитные проводники всех стационарных электроприемников (10).



Нулевые защитные проводники штепсельных розеток (11).

Гребенка ХВС (12).
Гребенка ГВС (13).

ПРИМЕЧАНИЕ

Система дополнительного уравнивания потенциалов должна соединять между собой все одновременно доступные прикосновению открытые проводящие части стационарного электро оборудования и сторонние проводящие части, включая доступные прикосновению металлические части строительных конструкций здания, а также нулевые защитные проводники в системе TN, включая защитные проводники штепсельных розеток (ПУЭ 1.7.83).
Для ванных и душевых помещений дополнительная система уравнивания потенциалов является обязательной и должна предусматривать, в том числе подключение сторонних проводящих частей, выходящих за пределы помещений (ПУЭ 7.1.88).
Соединения и присоединения заземляющих защитных проводников системы уравнивания потенциалов должны быть доступны для осмотра и выполнения испытаний (1.7.140).

Крепление проводника системы уравнивания потенциалов к металлической трубе

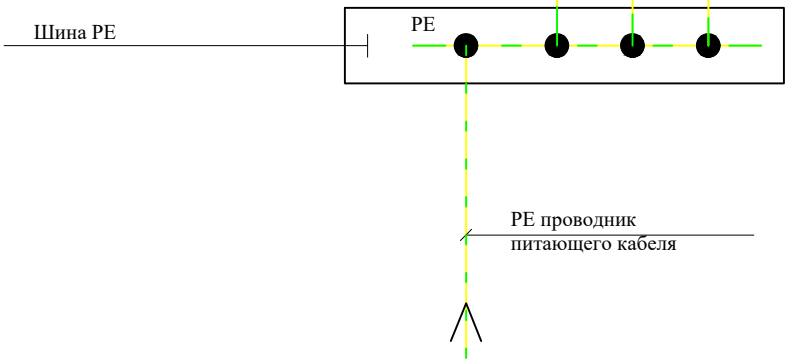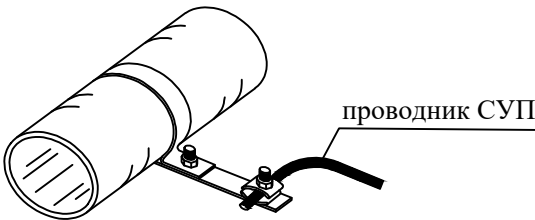

						ИСПОЛНИТЕЛЬНАЯ ДОКУМЕНТАЦИЯ			
						Заказчик: <i>частное лицо</i>			
Изм	Кол.	Лист	№ док	Подп.	Дата	Жилая квартира по адресу: <i>г.Москва, ул.Нижние Мневники, д.7, кв.Сачук Ю.Е.</i>	Стадия	Лист	Листов
ГИП		<i>Сарафонов</i>					ИД	6	6
Исполн.		<i>Салюк</i>							
Проверил		<i>Загуменная</i>				Схема дополнительной системы уравнивания потенциалов	ООО "СтройПроект"		

Позиция	Наименование и техническая характеристика	Тип, марка, обозначение документа, опросного листа	Код продукции	Поставщик	Ед. измерения	Кол-во	Масса 1ед. в кг	Примечание
1	2	3	4	5	6	7	8	9
	Электрооборудование ЦР							
1	Щит распределительный скрытой установки, 96 модулей, с комплектом шин IP44	ABB			шт	1		
2	Выключатель автоматический, SH203, C32A	ABB			шт	1		
3	Выключатель автоматический, SH203, C20A	ABB			шт	3		
4	Устройство защитного отключения, FH204, 25A, 30мА	ABB			шт	2		
5	Выключатель автоматический, дифференциальный, DSH201, C16A, 30мА	ABB			шт	15		
6	Выключатель автоматический, дифференциальный, DSH201, C10A, 30мА	ABB			шт	4		
7	Выключатель автоматический, SH201, C16A	ABB			шт	0		
8	Выключатель автоматический, SH201, C10A	ABB			шт	8		
9	Выключатель автоматический, SH201, C6A	ABB			шт	1		
10	Контактор, ESB40-40, 40A	ABB			шт	1		
	Осветительное оборудование							
1	Светильники				шт	см.дизайн		
	Кабельные изделия							
1	ВВГнг(А)-LS 5х4	Конкорд			метр	35		
2	ВВГнг(А)-LS 3х4	Конкорд			метр	10		
3	ВВГнг(А)-LS 3х2,5	Конкорд			метр	370		
4	ВВГнг(А)-LS 3х1,5	Конкорд			метр	580		
5	ВВГнг(А)-LS 2х1,5	Конкорд			метр	5		
6	ВВГнг(А)-LS 1х6	Конкорд			метр	20		
7	ВВГнг(А)-LS 1х4	Конкорд			метр	20		

						ИСПОЛНИТЕЛЬНАЯ ДОКУМЕНТАЦИЯ					
						Заказчик: <u>частное лицо</u>					
Изм	Кол.	Лист	№док	Подп.	Дата				Стадия	Лист	Листов
						Жилая квартира по адресу: <u>г.Москва, ул.Нижние Мневники, д.7, кв.Сачук Ю.Е.</u>			ИД	1	2
ГИП		<u>Сарафонов</u>									
Исполн.		<u>Салюк</u>							ООО "СтройПроект"		
Проверил		<u>Загуменная</u>									
						Спецификация оборудования и материалов					

Позиция	Наименование и техническая характеристика	Тип, марка, обозначение документа, опросного листа	Код продукции	Поставщик	Ед. измерения	Кол-во	Масса 1ед. в кг	Примечание	
1	2	3	4	5	6	7	8	9	
8	ВВГнг(А)-LS 1х2,5	Конкорд			метр	20	
9	ВВГнг(А)-LS 1х1,5	Конкорд			метр	20	
	Электромонтажные устройства и изделия	
1	Розетка штепсельная двухполюсная, с защитным контактом, скрытой установки				шт	см.дизайн	
2	Розетка штепсельная двухполюсная, с защитным контактом, скрытой установки, влагозащищенная, IP44				шт	см.дизайн	
3	Розетка интернет				шт	см.дизайн	
4	Розетка телевизионная				шт	см.дизайн	
5	Регулятор тёплого пола				шт	см.дизайн	
6	Выключатель одноклавишный, скрытой установки				шт	см.дизайн	
7	Выключатель двухклавишный, скрытой установки				шт	см.дизайн	
8	Переключатель однополюсный, скрытой установки				шт	см.дизайн	
9	Переключатель двухполюсный, скрытой установки				шт	см.дизайн	
10	Переключатель перекрестный, скрытой установки				шт	см.дизайн	
11	Переключатель перекрестный, двухполюсный, скрытой установки				шт	см.дизайн	
12	Подрозетник				шт	см.дизайн	
13	Распаечная коробка				шт	64	
14	Коробка уравнивания потенциалов				шт	2	
	Материалы	
1	Труба гофрированная, ПВХ, диам.25				метр	35	
2	Крепежная скоба, Ф25				шт	70	
3	Труба гофрированная, ПВХ, диам.20				метр	1045	
4	Крепежная скоба, Ф20				шт	2090	
<table><tr><td></td><td></td><td></td><td></td><td></td><td></td><td colspan="3" rowspan="3">ИСПОЛНИТЕЛЬНАЯ ДОКУМЕНТАЦИЯ</td></tr><tr><td></td><td></td><td></td><td></td><td></td><td></td></tr><tr><td></td><td></td><td></td><td></td><td></td><td></td></tr><tr><td></td><td></td><td></td><td></td><td></td><td></td><td colspan="3">Заказчик: <u>частное лицо</u></td></tr><tr><td></td><td></td><td></td><td></td><td></td><td></td><td colspan="2" rowspan="2">Жилая квартира по адресу: <u>г.Москва, ул.Нижние Мневники, д.7, кв.Сачук Ю.Е.</u></td><td>Стадия</td><td>Лист</td><td>Листов</td></tr><tr><td>ГИП</td><td></td><td><u>Сарафонов</u></td><td></td><td></td><td></td><td>ИД</td><td>2</td><td>2</td></tr><tr><td>Исполн.</td><td></td><td><u>Салюк</u></td><td></td><td></td><td></td><td colspan="2" rowspan="3">Спецификация оборудования и материалов</td><td colspan="3" rowspan="3">ООО "СтройПроект"</td></tr><tr><td>Проверил</td><td></td><td><u>Загуменная</u></td><td></td><td></td><td></td></tr><tr><td></td><td></td><td></td><td></td><td></td><td></td></tr><tr><td></td><td></td><td></td><td></td><td></td><td></td><td colspan="2"></td><td colspan="3"></td></tr></table>															ИСПОЛНИТЕЛЬНАЯ ДОКУМЕНТАЦИЯ																					Заказчик: <u>частное лицо</u>									Жилая квартира по адресу: <u>г.Москва, ул.Нижние Мневники, д.7, кв.Сачук Ю.Е.</u>		Стадия	Лист	Листов	ГИП		<u>Сарафонов</u>				ИД	2	2	Исполн.		<u>Салюк</u>				Спецификация оборудования и материалов		ООО "СтройПроект"			Проверил		<u>Загуменная</u>																				
						ИСПОЛНИТЕЛЬНАЯ ДОКУМЕНТАЦИЯ	
						Заказчик: <u>частное лицо</u>	
						Жилая квартира по адресу: <u>г.Москва, ул.Нижние Мневники, д.7, кв.Сачук Ю.Е.</u>		Стадия	Лист	Листов	
ГИП		<u>Сарафонов</u>						ИД	2	2	
Исполн.		<u>Салюк</u>				Спецификация оборудования и материалов		ООО "СтройПроект"	
Проверил		<u>Загуменная</u>	