


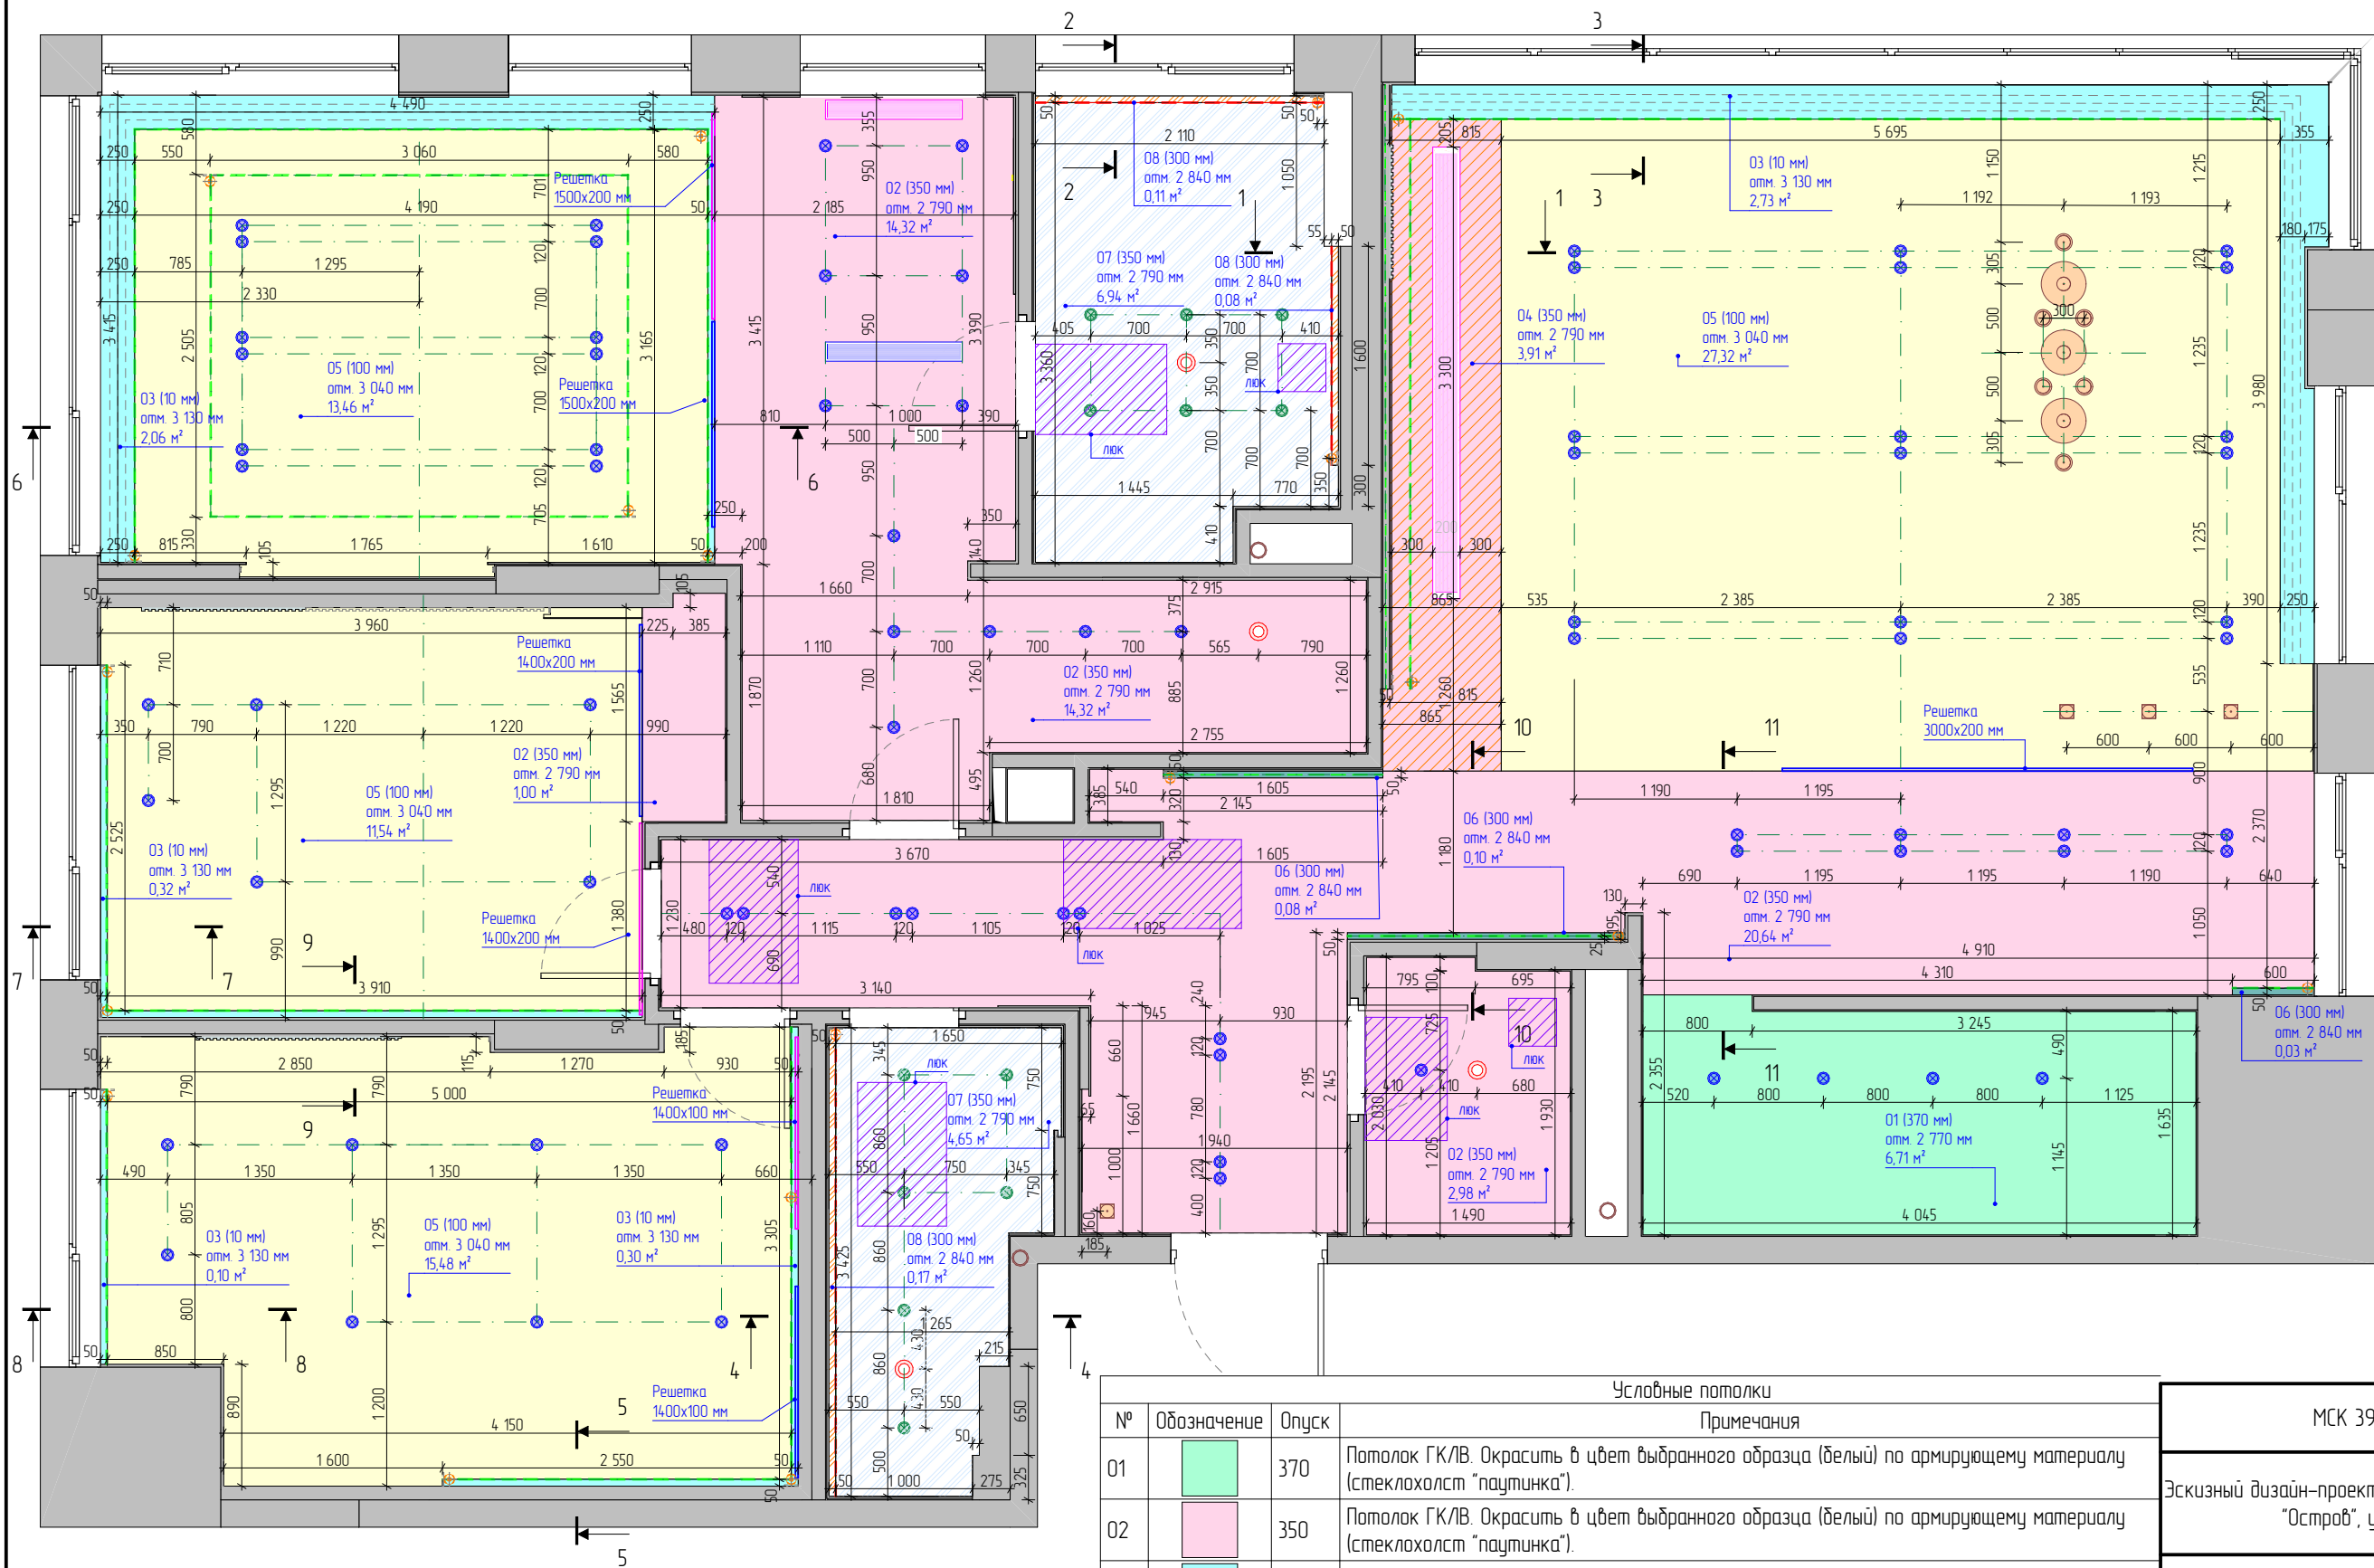

Примечания:

- * – размеры уточнить по месту после выполнения черновых работ.
- Выполнить уровни потолка из влагостойкого ГКЛ для предотвращения деформации потолка при затоплении.
- Высоту уровней потолка отсчитывать от существующей ж/б плиты перекрытия помещения.
- Предусмотреть усиление потолка фанерой в местах крепления потолочных карнизов для штор.
- Во влажных помещениях обои под покраску на потолок не клеить, заменить на оштукатуривание по армирующей сетке, согласовать со специалистами.
- От вытяжки провести вентиляционный короб до общедомового канала в конструкции потолка, уточнить по месту со специалистами и заказчиком.
- Шумоизоляцию разработать со специалистами, уточнить состав и толщину слоев шумоизоляционных материалов. Уточнить необходимость устройства с заказчиком.

Условные обозначения:


- Выход 220V
- Выход электрокабеля для светодиодной ленты
- Диффузор, вытяжка
- Люстра подвесная потолочная
- Светильник точечный встраиваемый
- Светильник точечный встраиваемый влагозащищенный
- Светодиодная лента
- Светодиодная лента, влагозащищенная
- Люк доступа

Условные потолки			
№	Обозначение	Опуск	Примечания
01		370	Потолок ГК/В. Окрасить в цвет выбранного образца (белый) по армирующему материалу (стеклохолст "паутинка").
02		350	Потолок ГК/В. Окрасить в цвет выбранного образца (белый) по армирующему материалу (стеклохолст "паутинка").
03		10	Выводить и оштукатурить существующий потолок. Окрасить в цвет выбранного образца (белый) по армирующему материалу (стеклохолст "паутинка"). Размер ниши уточнить.
04		350	Потолок ГК/В с МДФ панелью. Цвет выбранного образца (*коричневый) уточнить при закупке.
05		100	Потолок ГК/В. Окрасить в цвет выбранного образца (белый) по армирующему материалу (стеклохолст "паутинка").
06		300	Потолок ГК/В. Окрасить в цвет выбранного образца (белый) по армирующему материалу (стеклохолст "паутинка").
07		350	Потолок ГК/В, Окрасить в цвет выбранного образца (белый) по оштукатуренной поверхности.
08		300	Потолок ГК/В, Окрасить в цвет выбранного образца (белый) по оштукатуренной поверхности.

МСК 392.12.25-ЭП ПРЕМИУМ

Эскизный дизайн-проект интерьера квартиры в г. Москва ЖК "Остров", ул. Нижние Мневники д. 7

Общий план конструкций и отделки потолка

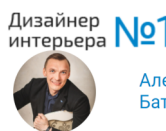

Александр Батеньков

Стадия	Лист	Листов
ЭП	31	120
Подп.	Дата	

ГАП	Батеньков А.С.		
Гл. дизайнер	Власова В.А.		
Гл. проектиров.	Луныкова В.Н.		