


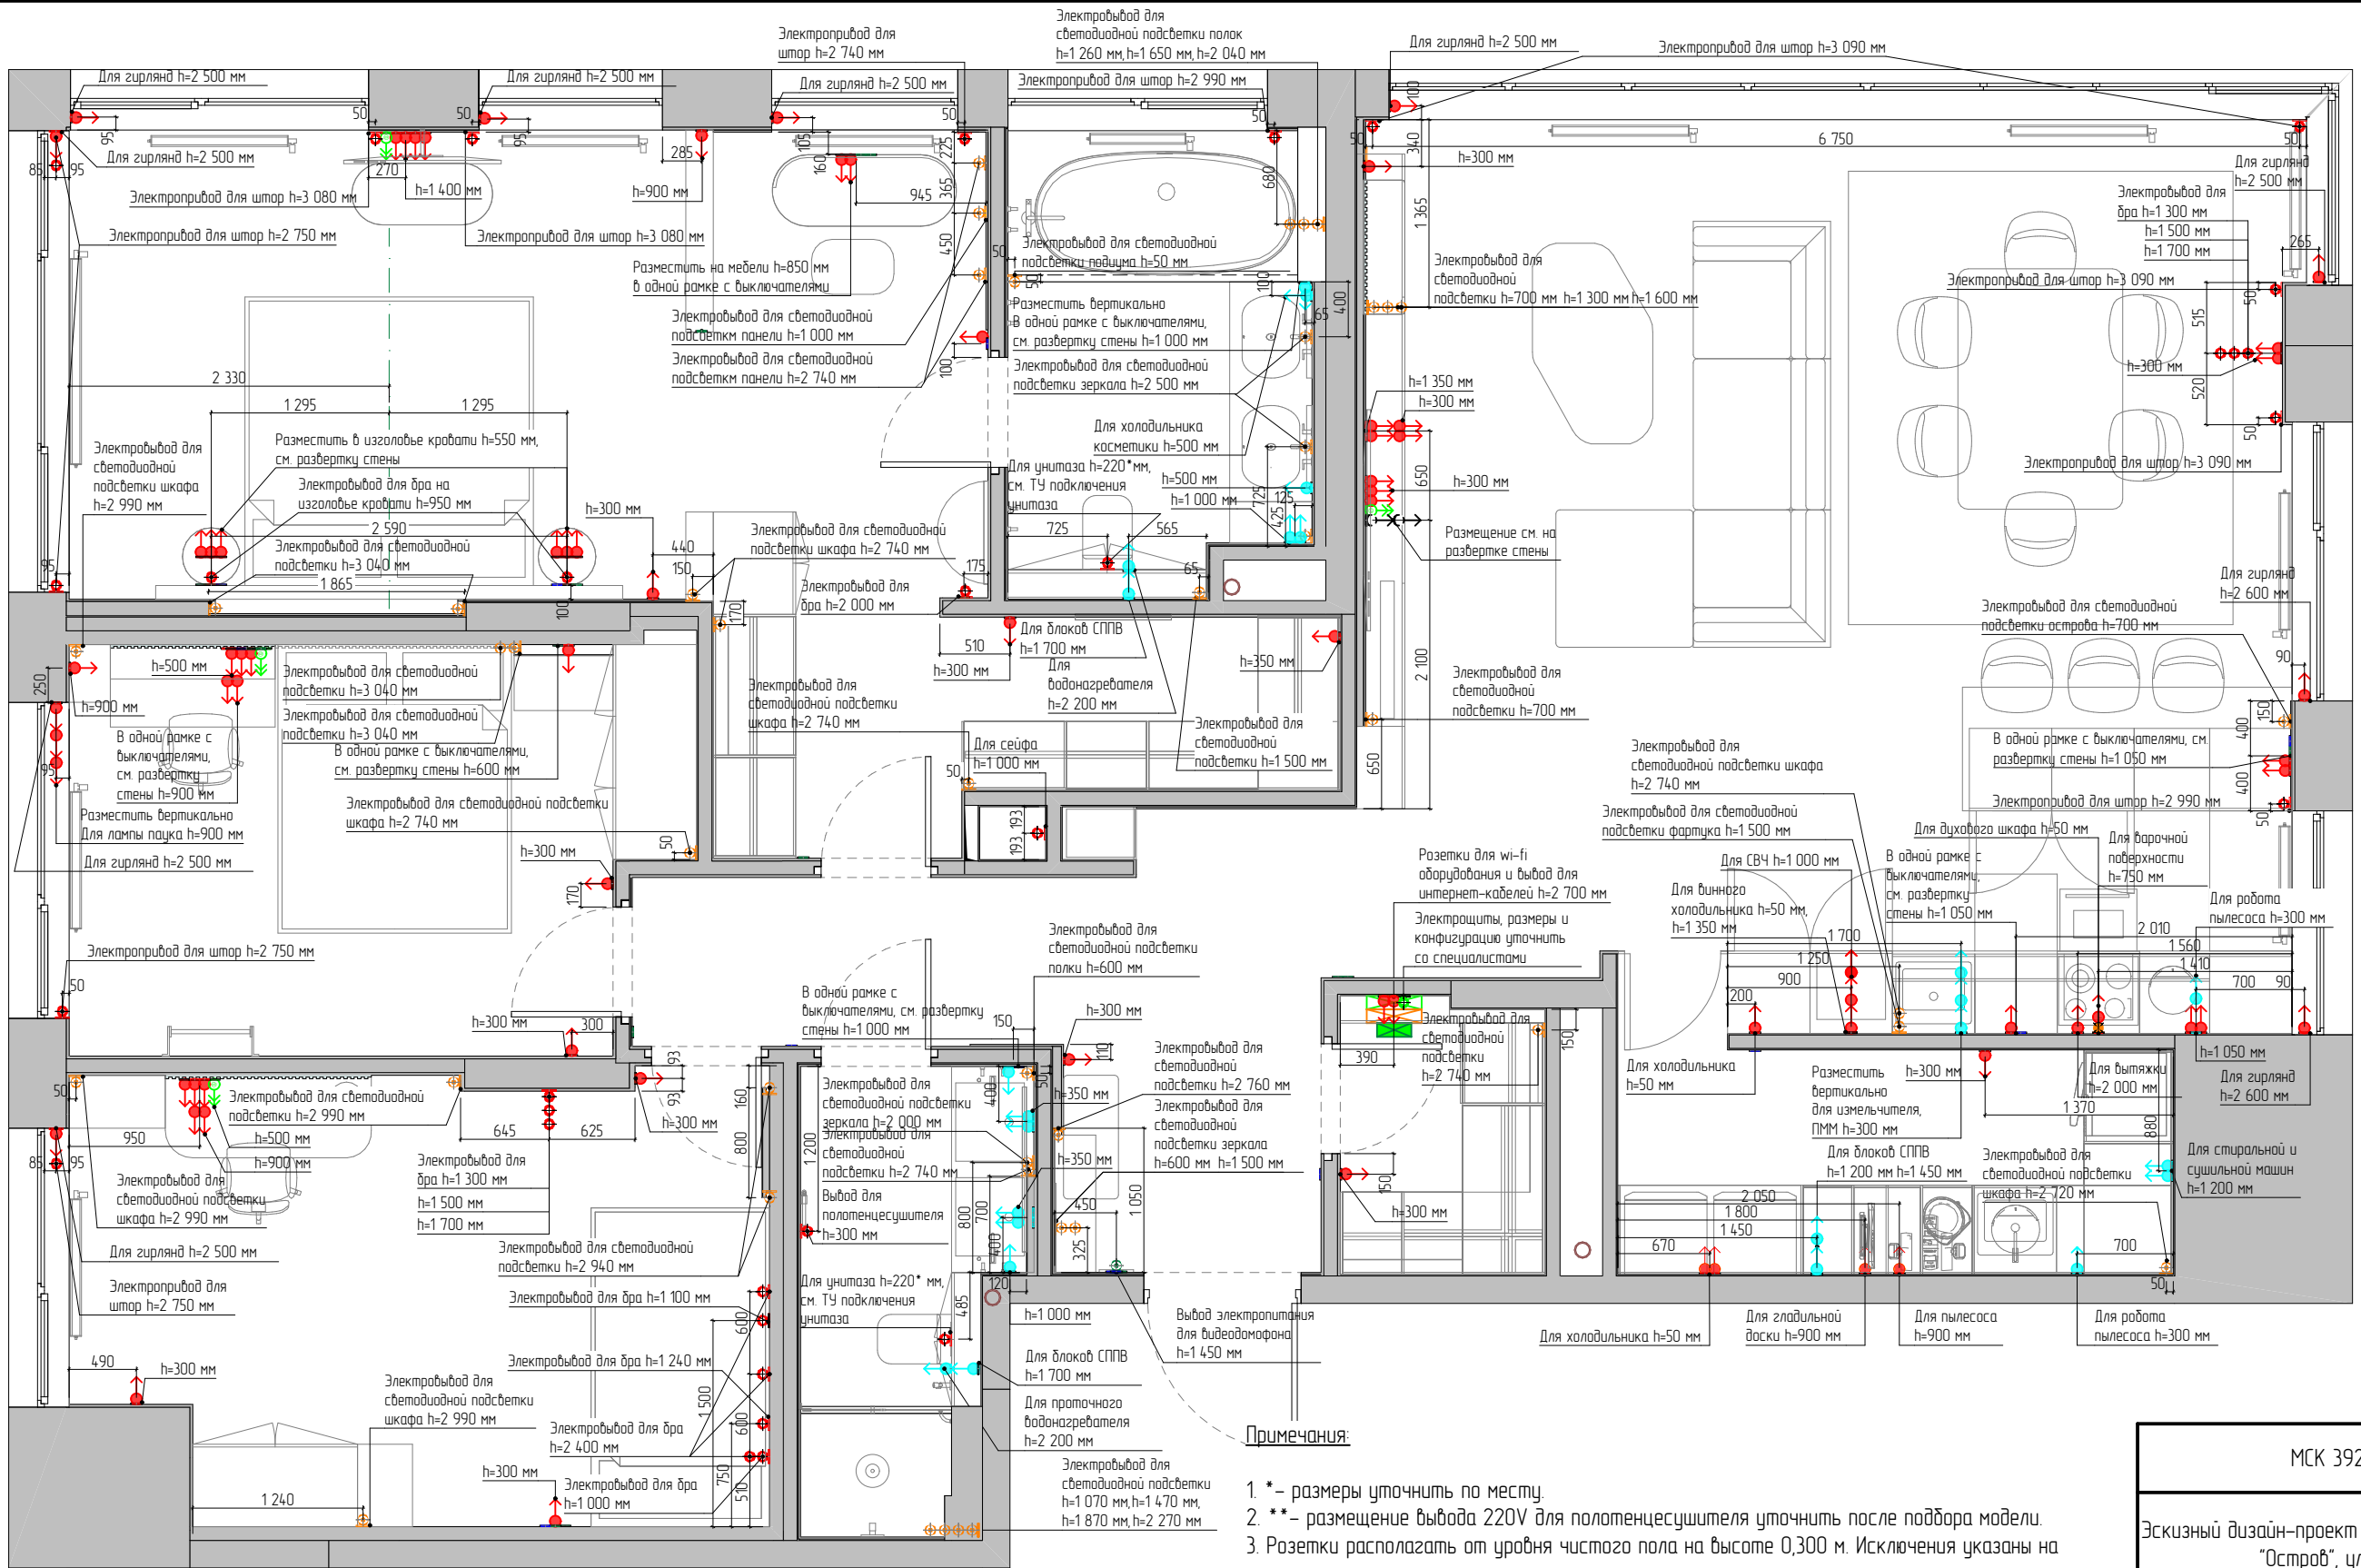

Условные обозначения:

- Электрощит
- Слаботочный щит
- Розетка 220V влагозащитенная
- Розетка 220V

- Выход электрокабеля для светодиодной ленты
- Выход электрокабеля для варочной поверхности
- Выход спец. кабеля
- Выход интернет кабеля
- Выход 220V
- wi-fi оборудование

Примечания:

- * - размеры уточнить по месту.
- ** - размещение вывода 220V для полотенцесушителя уточнить после подбора модели.
- Розетки располагать от уровня чистого пола на высоте 0,300 м. Исключения указаны на чертеже.
- Приязку и размещение розеток и выводов кухонного гарнитура согласовать с изготовителями после подбора мебели заказчиком.
- Размещение и габаритные размеры электрощита согласовать со специалистами.
- Предусмотреть совместимость видеодомофона квартиры с общедомовой системой.
- К WI-FI оборудованию подвести 5 выводов интернет-кабеля из расчета: общее количество интернет выводов и розеток + один (вывод в квартиру из подъезда). Размещение wi-fi оборудования и усилителей для него определить по месту, вызов предварительно на объект специалистов.
- Размещение всех выводов и розеток согласовать со специалистами «Умный дом».
- Размеры и характеристики радиаторов отопления согласовать со специалистами, предусмотреть терморегуляторы.
- Датчики пожарной и охранной сигнализации и электропроводы для них разместить совместно со специалистами, предварительно вызвав их на объект.
- Размещение и монтаж стабилизатора напряжения согласовать со специалистами.
- Размещение розеток и электропроводов по высоте см. на развертках стен.

МСК 392.12.25-ЭП ПРЕМИУМ

Эскизный дизайн-проект интерьера квартиры в г. Москва ЖК "Остров", ул. Нижние Мневники д. 7

План размещения электрооборудования с мебелью.

Дизайнер интерьера №1 Александр Батеньков	Стадия	Лист	Листов
	ЭП	18	120
		Подп.	Дата
ГАП	Батеньков А.С.		
Гл. дизайнер	Власова В.А.		
Гл. проектиров.	Лунькова В.Н.		