


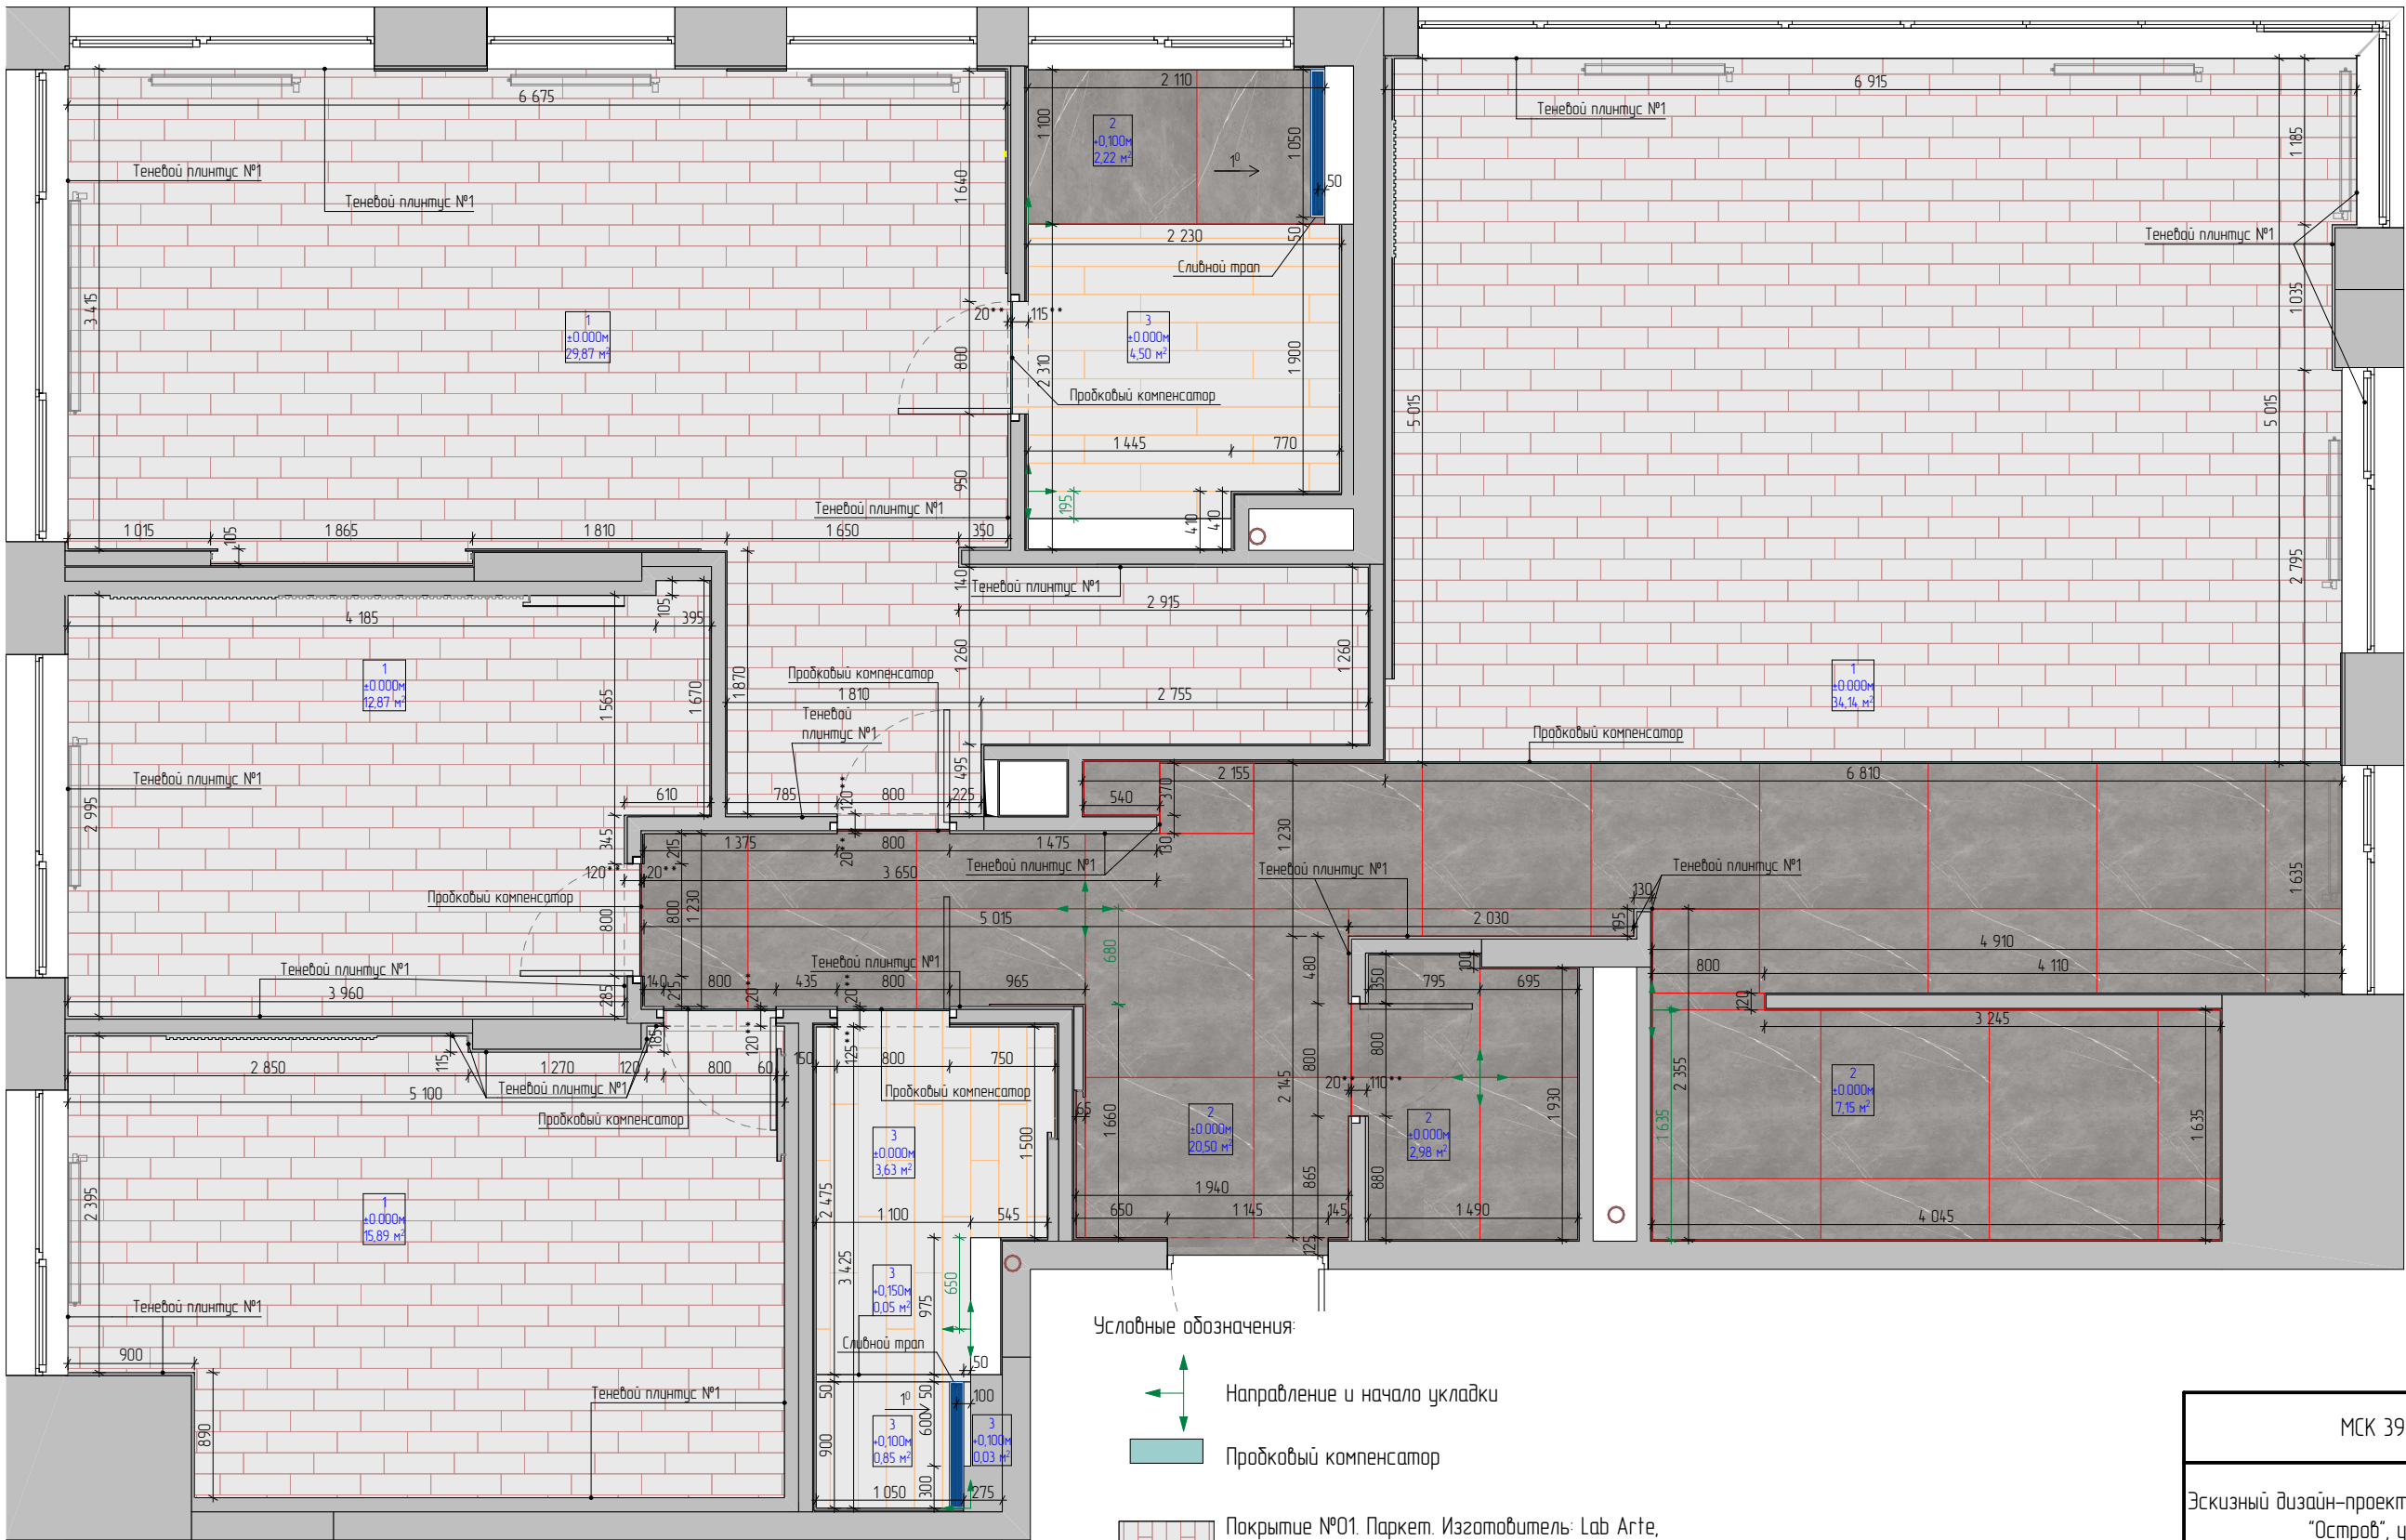

Примечания:

- *- размеры уточнить по месту после выполнения черновых отделочных работ.
- За отметку $\pm 0,000$ принят уровень чистого пола.
- Во влажных помещениях предусмотреть гидроизоляцию пола с заведением на стены до потолка.
- Совместить швы плитки на подиумах и основном полу.
- При монтаже напольных покрытий уточнить необходимость устройства дверных проемов с порогами.
- *- размеры уточнить по месту после выполнения черновых отделочных работ и установки дверей со скрытой коробкой.
- **—размер уточнить по месту в зависимости от точного расположения полотна двери, стыковка двух разных напольных покрытий должна проходить точно по центру вдоль дверного полотна.

Условные обозначения:

- Направление и начало укладки
- Пробковый компенсатор
- Покровие №01. Паркет. Изготовитель: Lab Arte, кол-я: Angle Дуб Натур, размер: 500x150 мм, точный артикул и производителя уточнить при выборе образца, толщину уточнить при закупке.
- Покровие №02. Керамогранит. Изготовитель: Elegant Grey, кол-я: Forte Dei Marmi, размер: 1200x1200 мм, толщину уточнить при закупке.
- Покровие №03. Керамогранит. Изготовитель: Nutmeg, кол-я: Woodslate Life, размер: 1200x200 мм, толщину уточнить при закупке.

МСК 392.12.25-ЭП ПРЕМИУМ			
Эскизный дизайн-проект интерьера квартиры в г. Москва ЖК "Остров", ул. Нижние Мневники д. 7			
Общий план покрытий полов.			
Дизайнер интерьера  №1 Александр Батеньков	Стадия	Лист	Листов
	ЭП	29	120
		Подп.	Дата
ГАП	Батеньков А.С.		
Гл. дизайнер	Власова В.А.		
Гл. проектиров.	Луныкова В.Н.		