


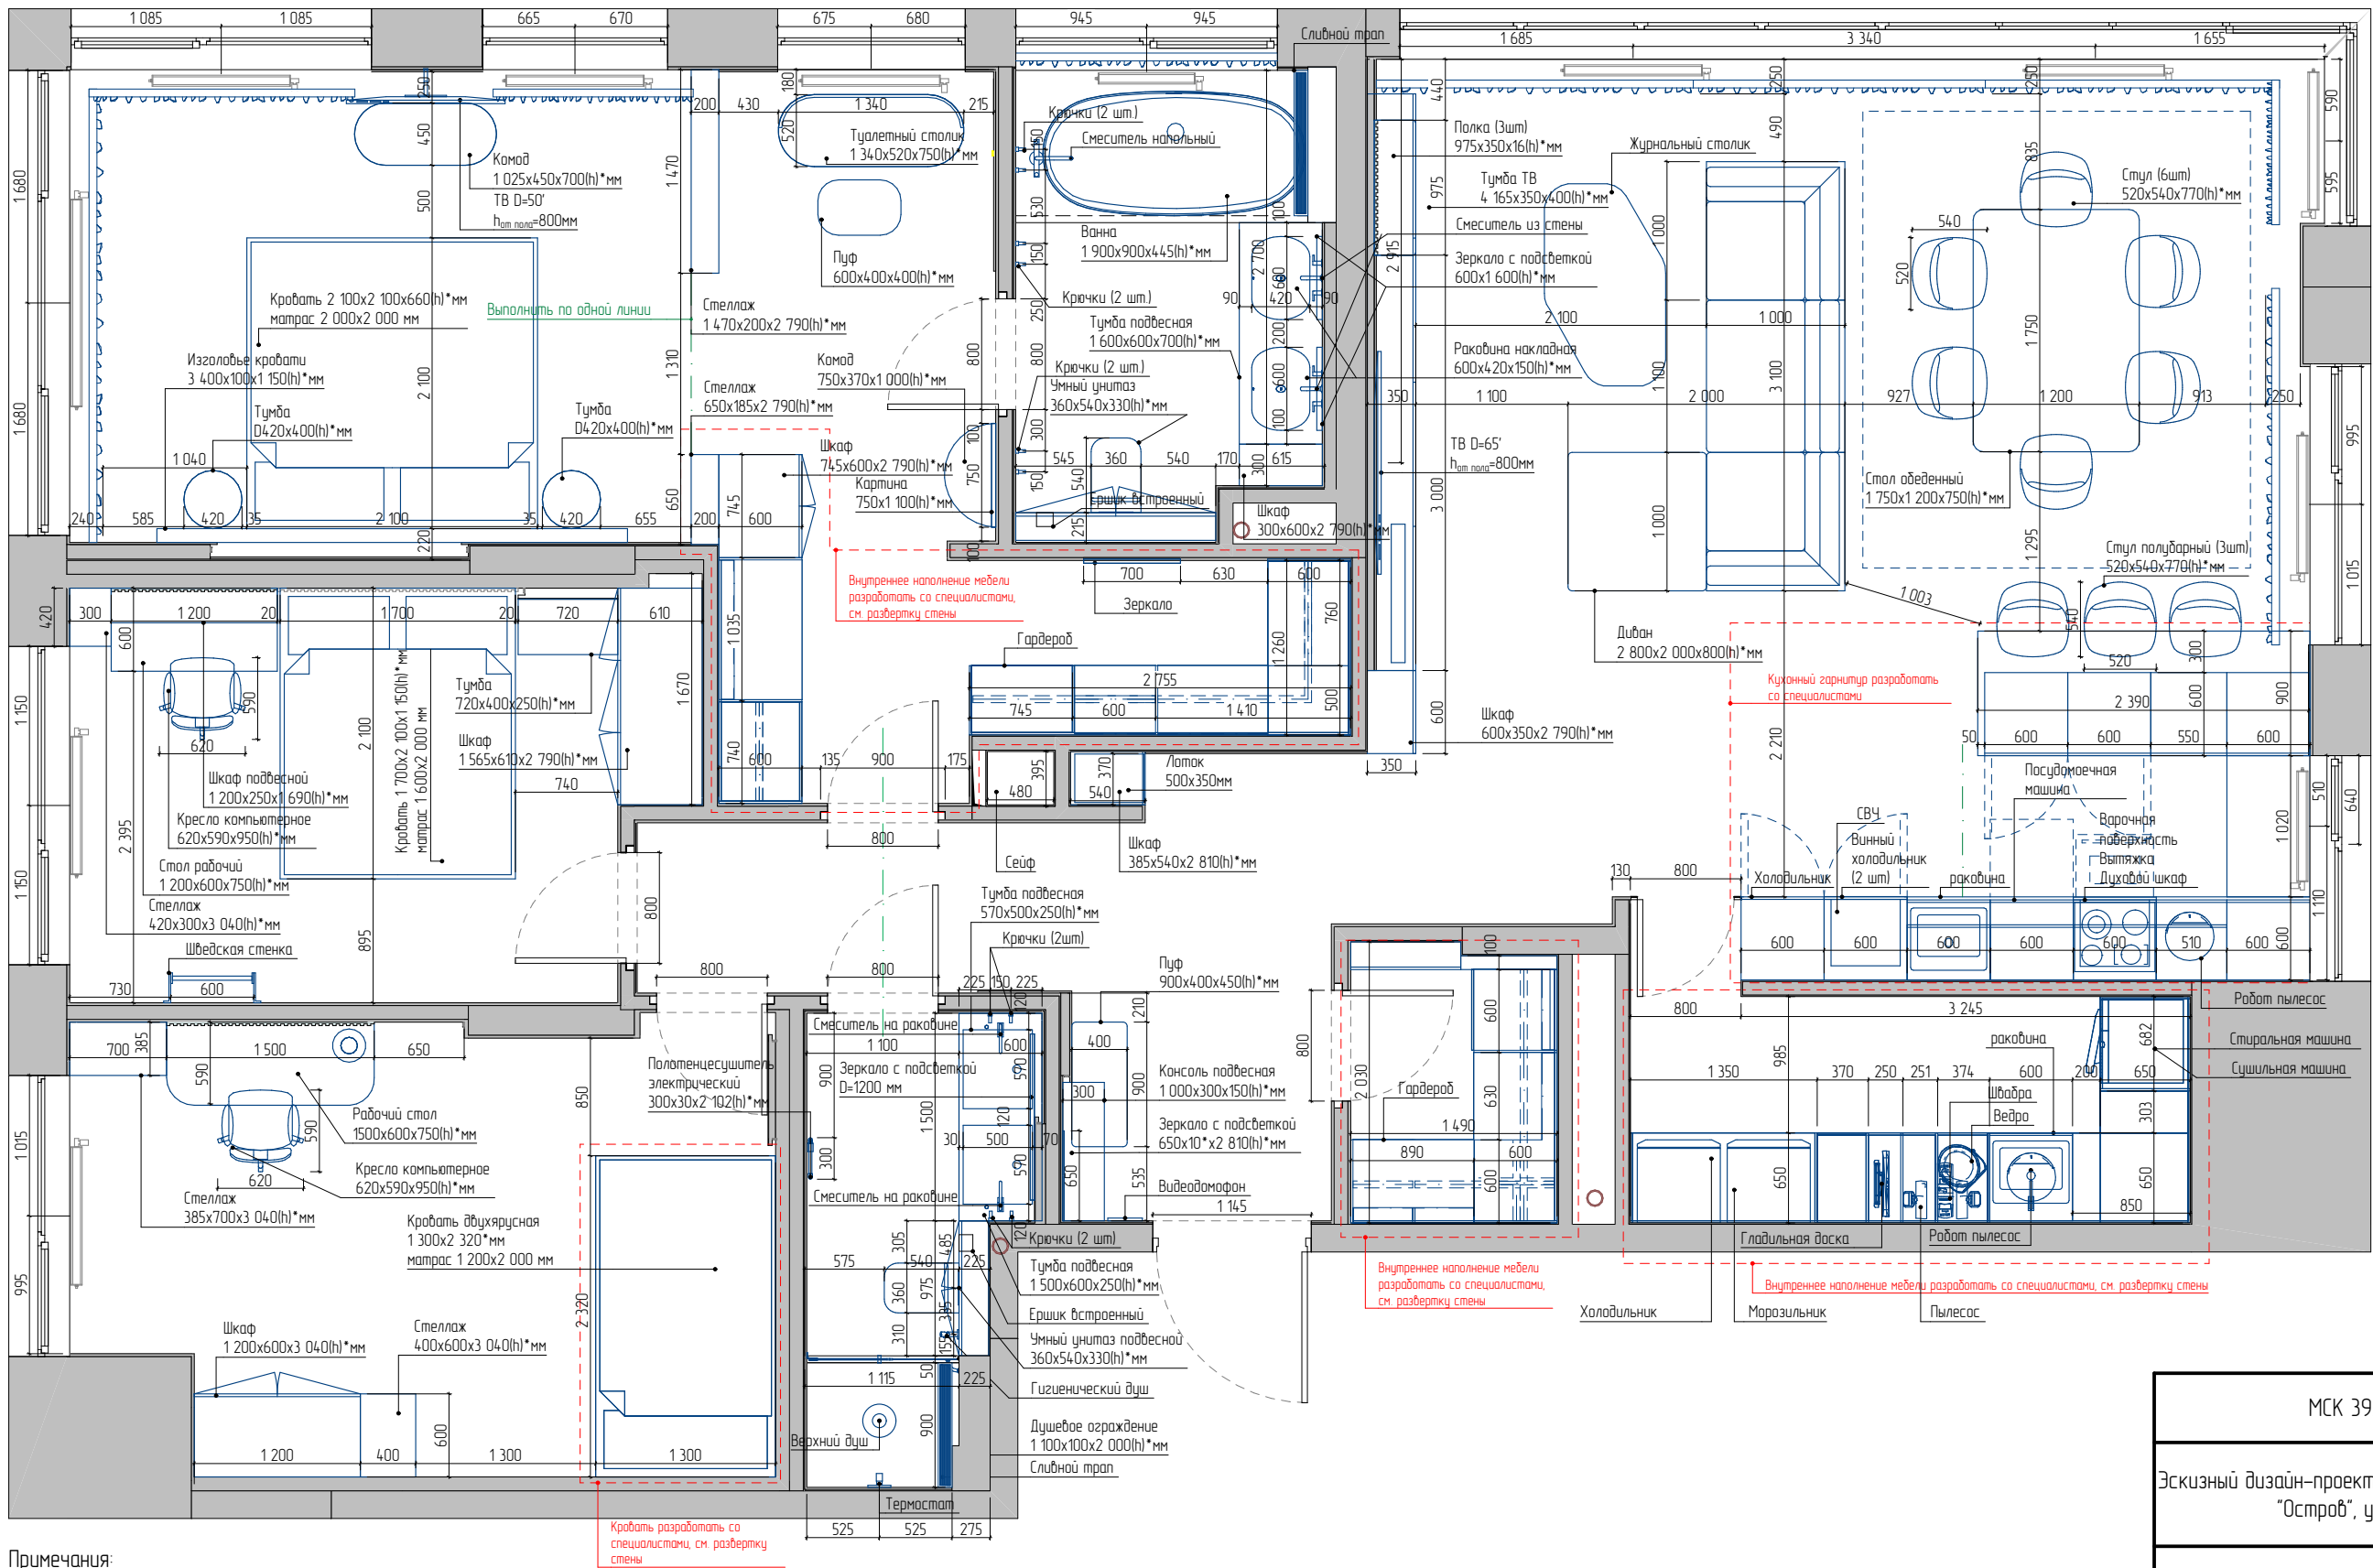

Примечания:

- * – размеры уточнить по месту после выполнения черновых отделочных работ.
- Размеры, привязки и характеристики кухонного гарнитура согласовать со специалистами после выбора модели.
- Размеры и характеристики радиаторов отопления согласовать со специалистами, предусмотреть терморегуляторы.
- Привязку вывода коммуникаций уточнить после подбора сан.тех. оборудования. Выполнить по инструкции монтажа.
- Вывод коммуникаций для посудомоечной машины провести гибкими шлангами в цоколе кухонного гарнитура, разработать со специалистами.
- Предусмотреть фильтры для очистки водопроводной воды на магистрали водопровода.
- ** – размеры уточнить у изготовителей мебели.
- Предусмотреть люки скрытого монтажа для доступа к коммуникациям, размещение уточнить по месту.
- Привязки выводов коммуникаций даны чистовые, с учетом толщины финишной отделки стен.
- Габаритные размеры сан.тех. оборудования уточнить при выборе модели и покупке. Выводы коммуникаций выполнить по инструкции монтажа.

МСК 392.12.25-ЭП ПРЕМИУМ

Эскизный дизайн-проект интерьера квартиры в г. Москва ЖК "Остров", ул. Нижние Мневники д. 7

План расстановки мебели и сан.тех.оборудования.

Дизайнер интерьера  Александр Батеньков	Стадия	Лист	Листов
	ЭП	13	120
		Подп.	Дата
Г.АП	Батеньков А.С.		
Гл. дизайнер	Власова В.А.		
Гл. проектиров.	Луцькова В.Н.		