


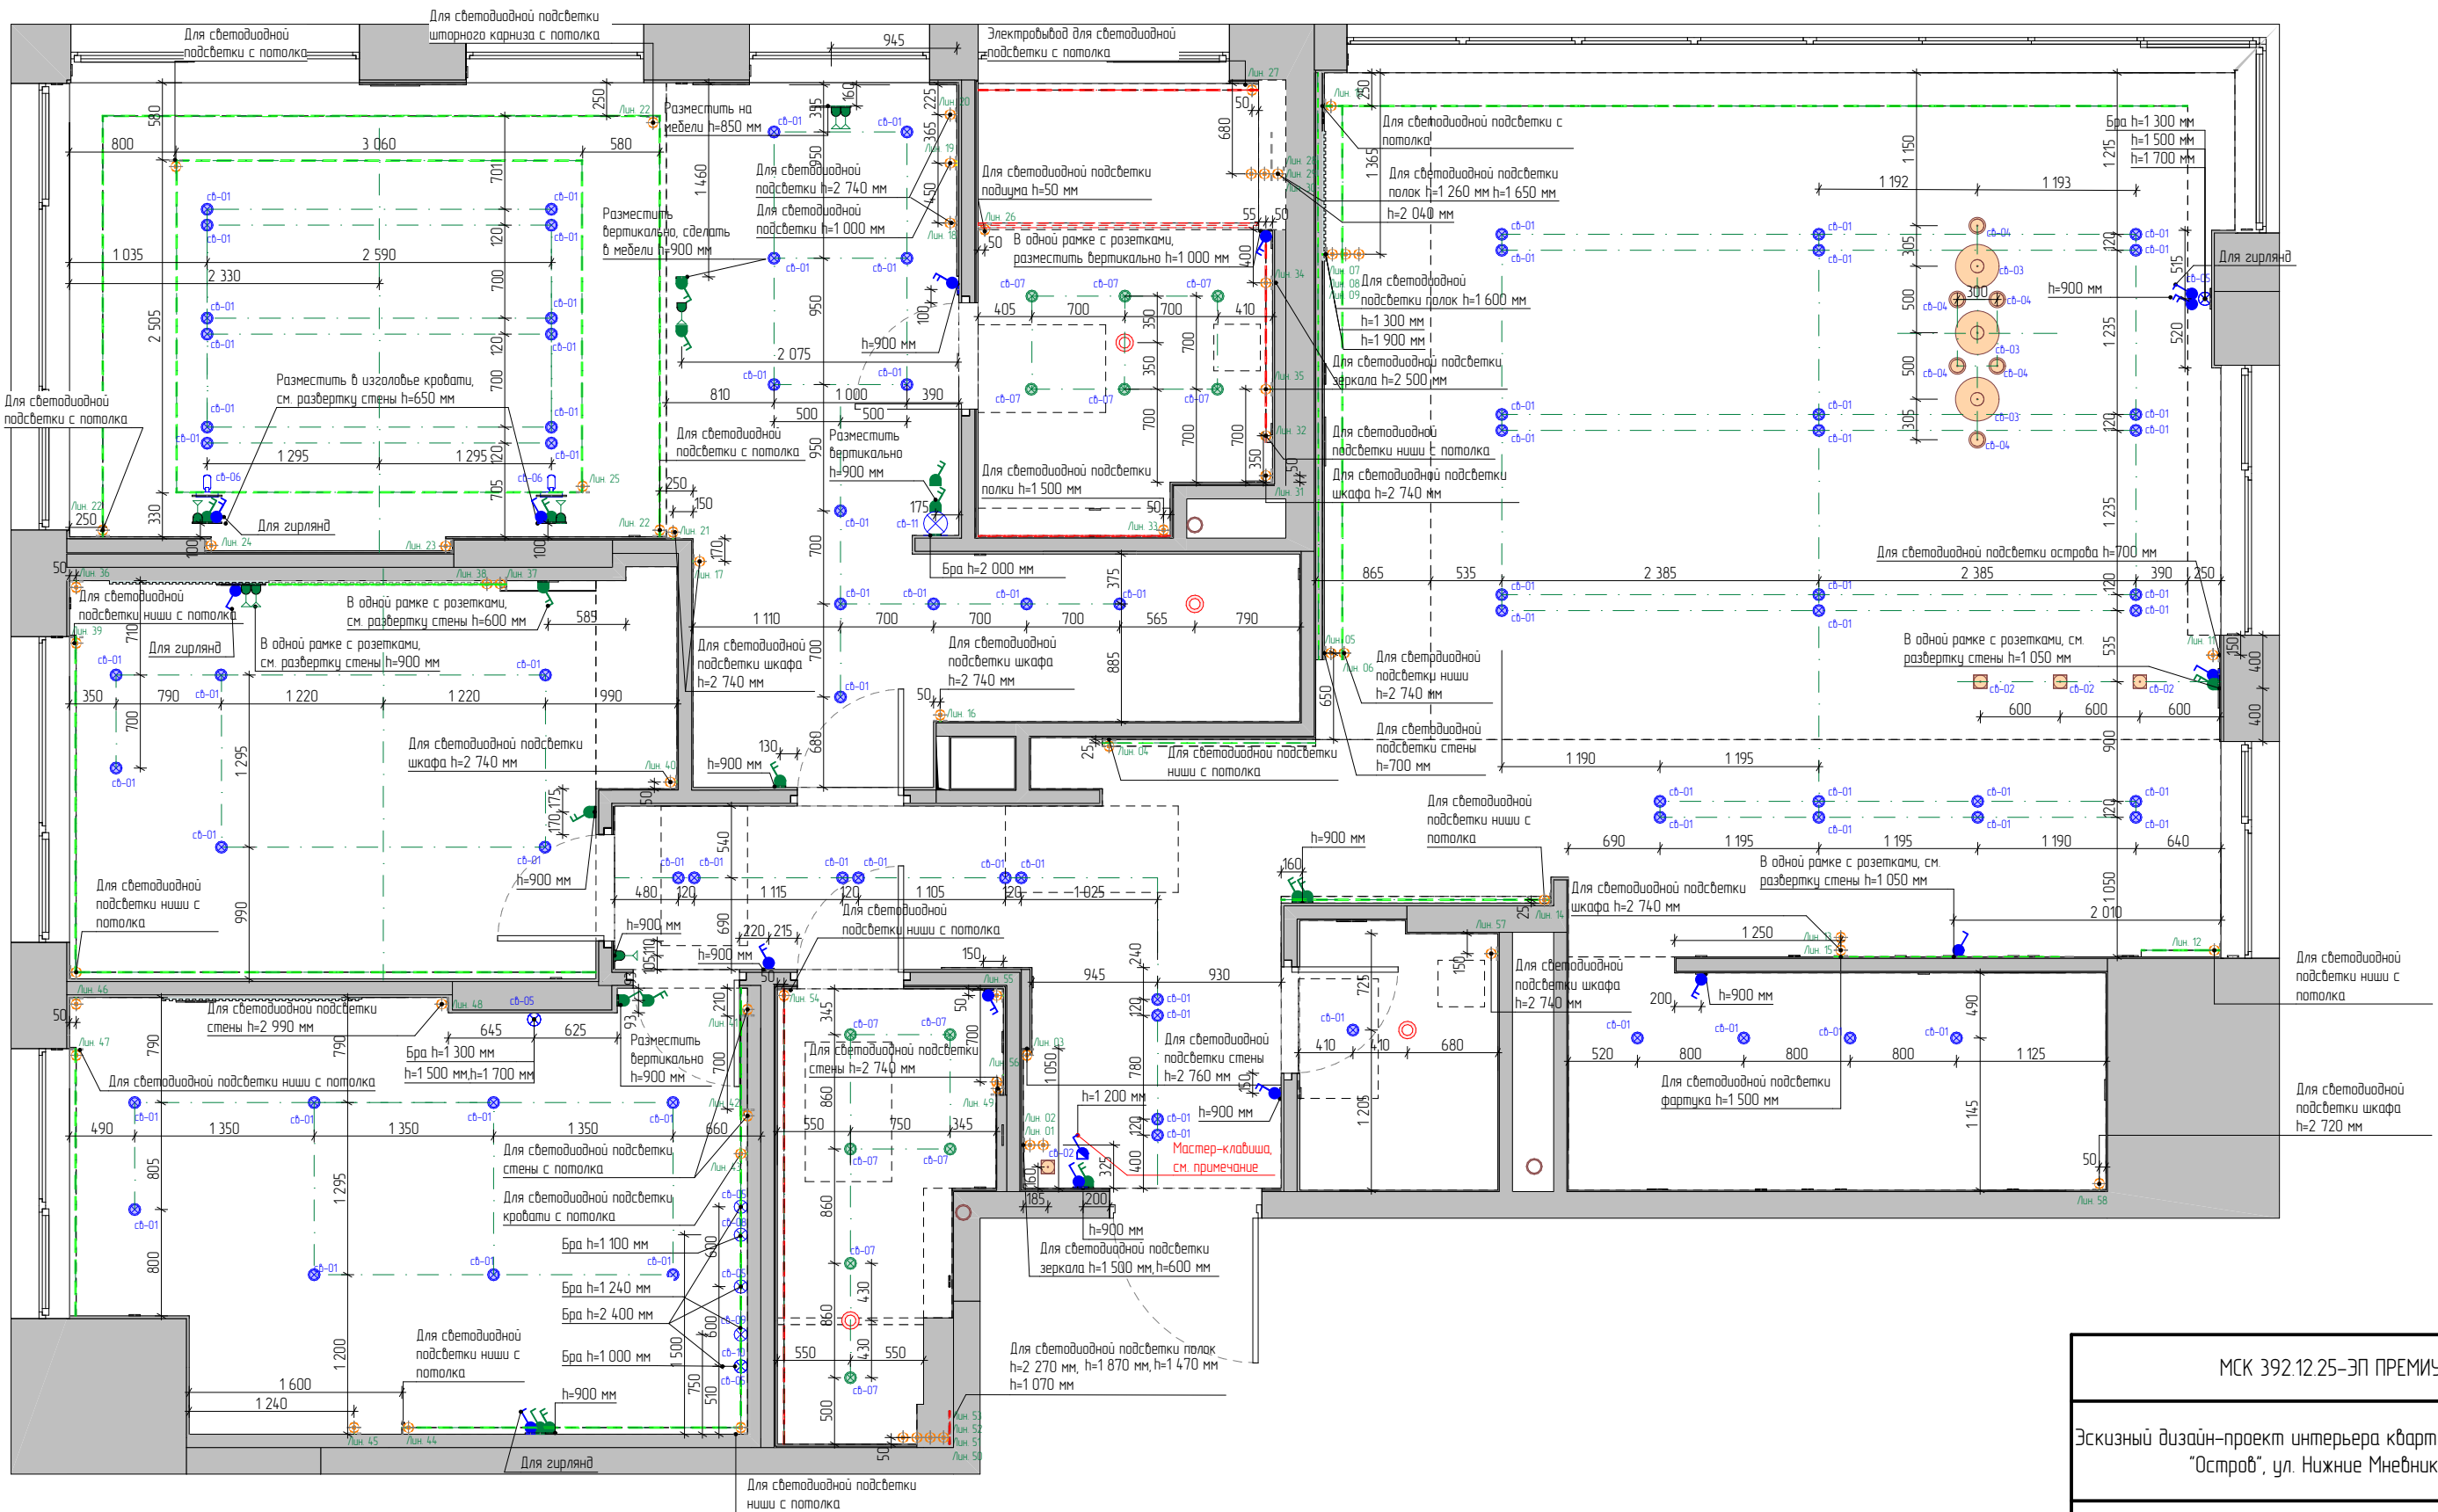

Условные обозначения:

- | | | | |
|--|--|--|--|
| | Выход 220V | | Мастер-клавиша |
| | Выход электрокабеля для светодиодной ленты | | Выключатель двухклавишный |
| | Выключатель одноклавишный | | Переключатель одноклавишный переходной |
| | Диффузор, вытяжка | | Светильник точечный встраиваемый |
| | Люстра подвесная потолочная | | Светильник точечный встраиваемый влагозащитный |
| | Переключатель двухклавишный | | Светодиодная лента |
| | | | Светодиодная лента, влагозащитная |

Примечания:

- * - размеры уточнить по месту.
- Выключатели располагать от уровня чистого пола на высоте 0,900 м. Исключения указаны на чертеже.
- Светильники, встроенные в мебель, согласовать с изготовителями мебели.
- Мастер клавиши:
№1 - выключение всего освещения квартиры, размещение согласовать с заказчиком при начале строительных работ;
№2 - выключение электропитания (розетки) кроме холодильника, морозильных камер, охранной сигнализации, датчиков протечки и др. по согласованию с заказчиком непосредственно на объекте.

МСК 392.12.25-ЭП ПРЕМИУМ

Эскизный дизайн-проект интерьера квартиры в г. Москва ЖК "Остров", ул. Нижние Мневники д. 7

План размещения освещения и выключателей.

Дизайнер интерьера Александр Батеньков	Стадия	Лист	Листов
	ЭП	21	120
		Подп.	Дата
ГАП	Батеньков А.С.		
Гл. дизайнер	Власова В.А.		
Гл. проектиров.	Луныкова В.Н.		