


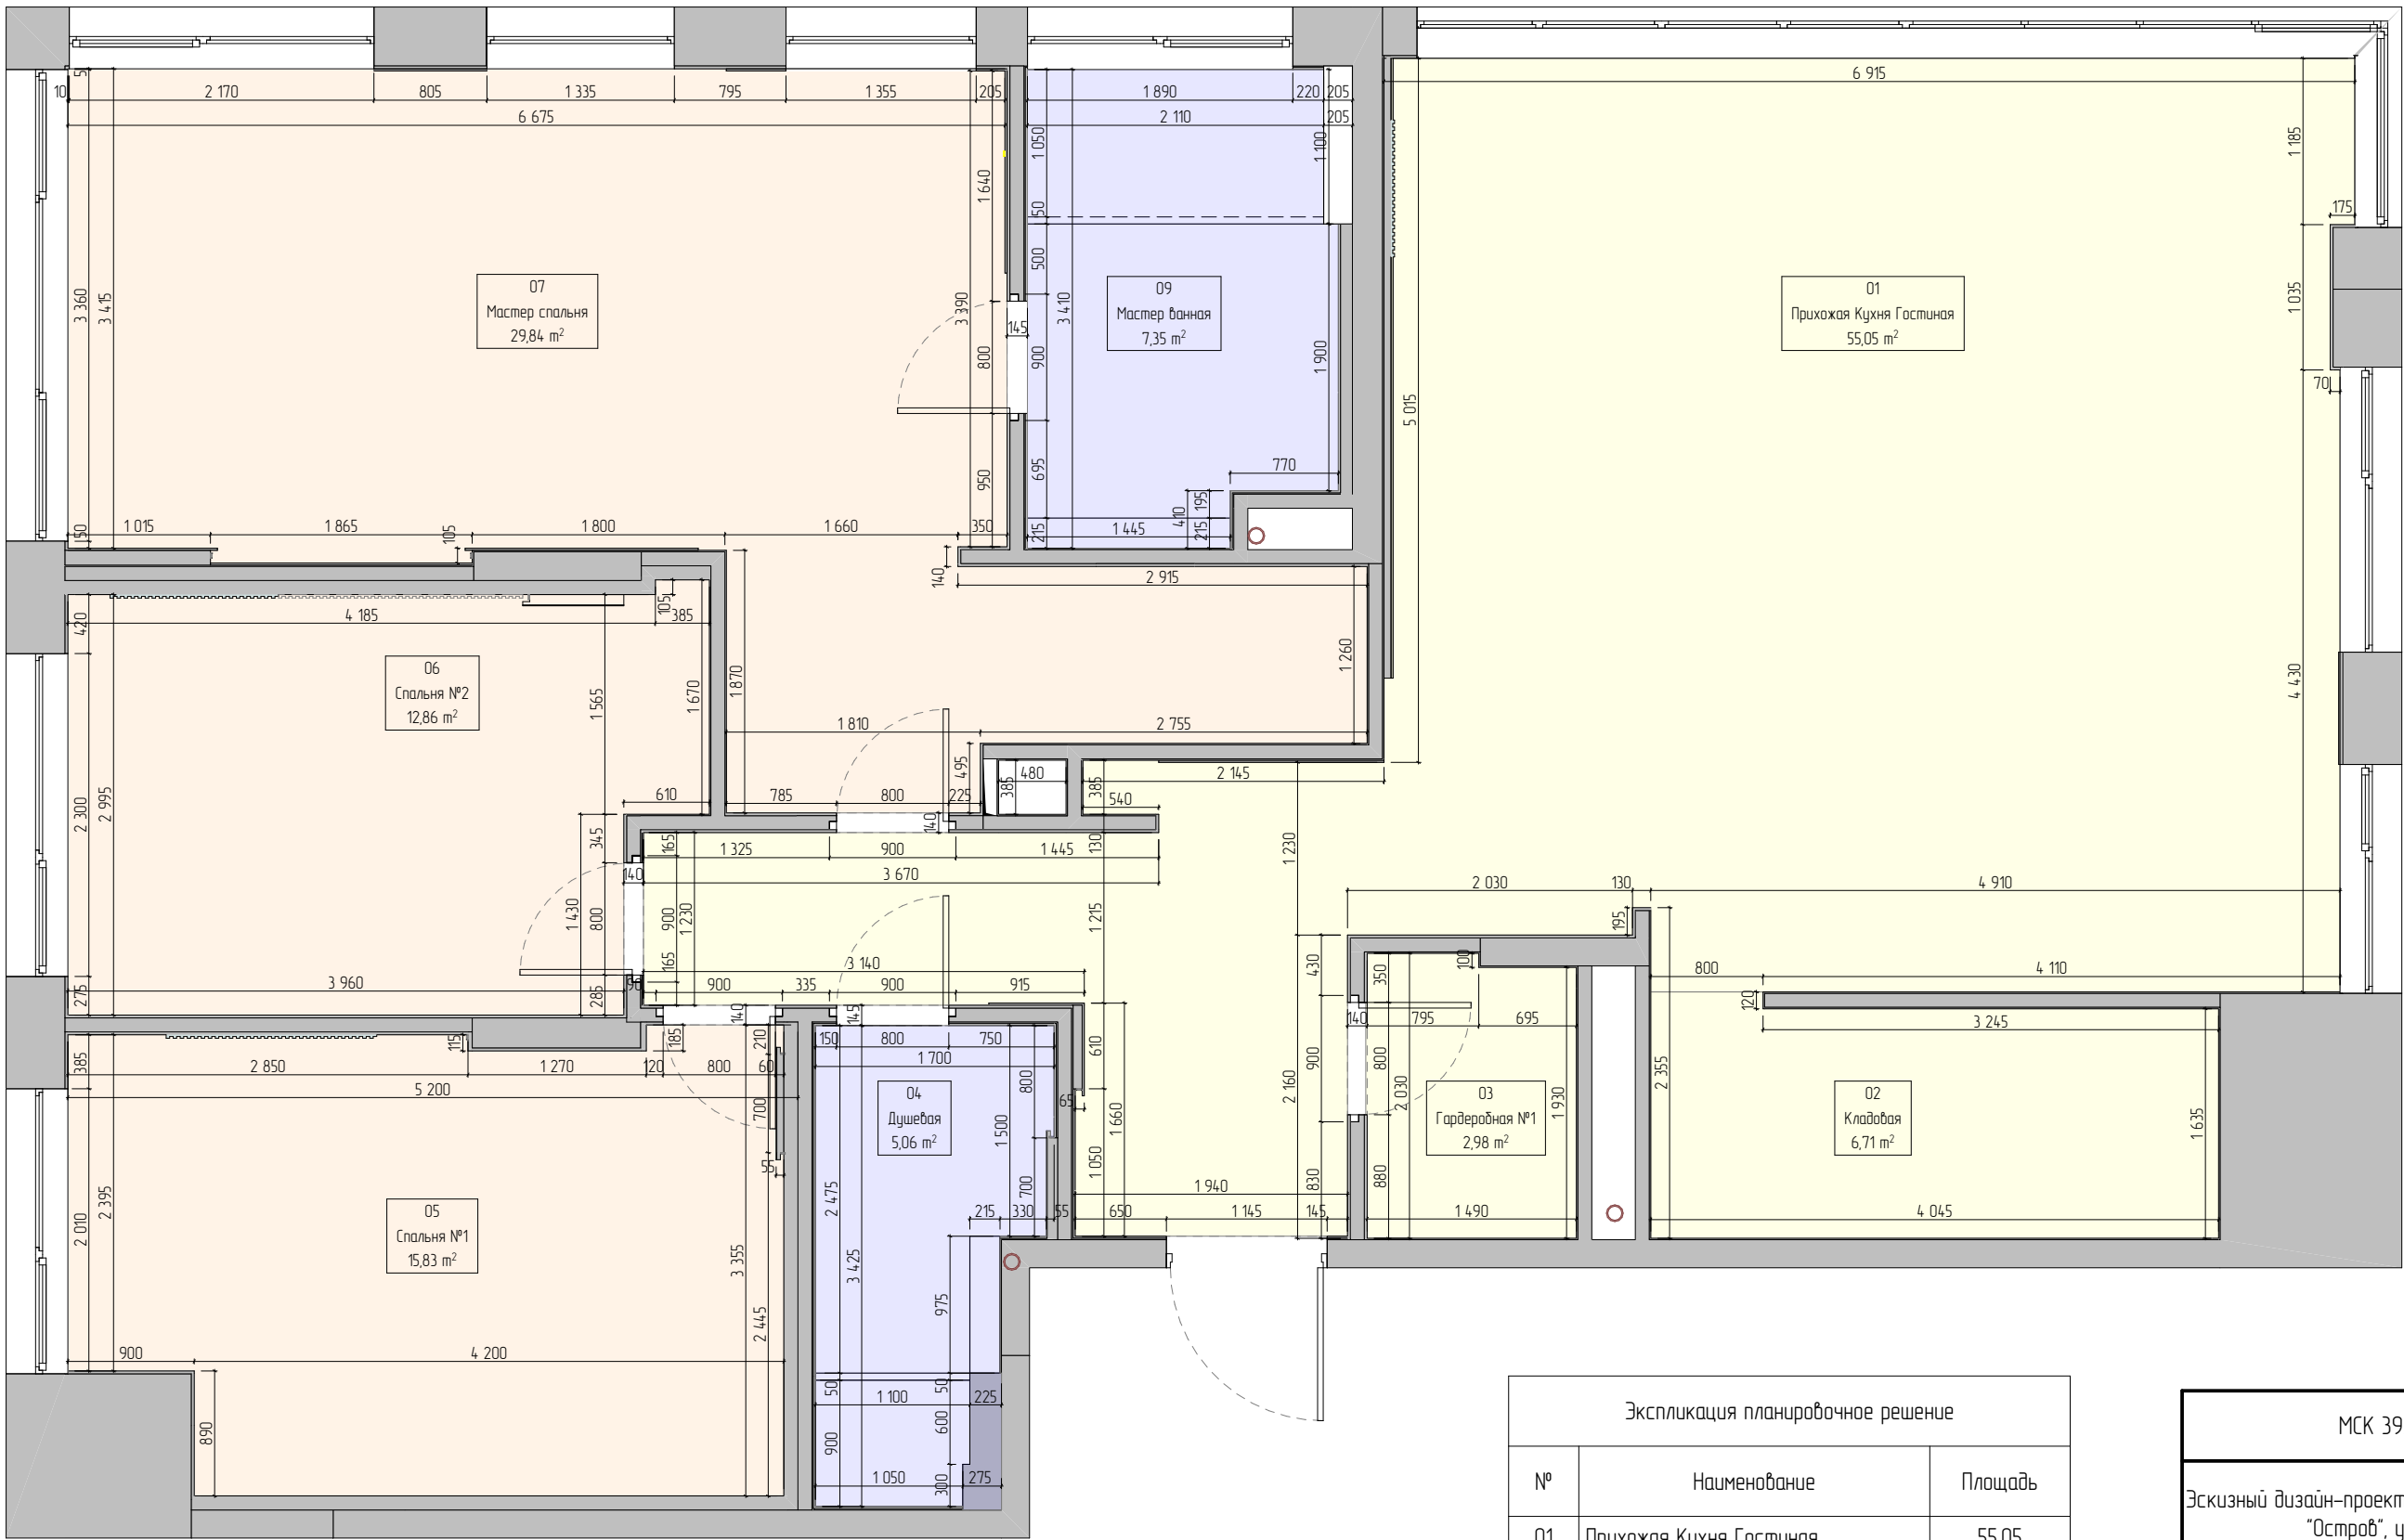

Экспликация планировочное решение		
№	Наименование	Площадь
01	Прихожая Кухня Гостиная	55,05
02	Кладовая	6,71
03	Гардеробная №1	2,98
04	Душевая	5,06
05	Спальня №1	15,83
06	Спальня №2	12,86
07	Мастер спальня	29,84
09	Мастер ванная	7,35
		135,68 м²

МСК 392.12.25-ЭП ПРЕМИУМ			
Эскизный дизайн-проект интерьера квартиры в г. Москва ЖК "Остров", ул. Нижние Мневники д. 7			
План помещений после перепланировки.			
Дизайнер интерьера  №1 Александр Батеньков	Стадия	Лист	Листов
	ЭП	12	120
		Подп.	Дата
ГАП	Батеньков А.С.		
Гл. дизайнер	Власова В.А.		
Гл. проектиров.	Луцькова В.Н.		