


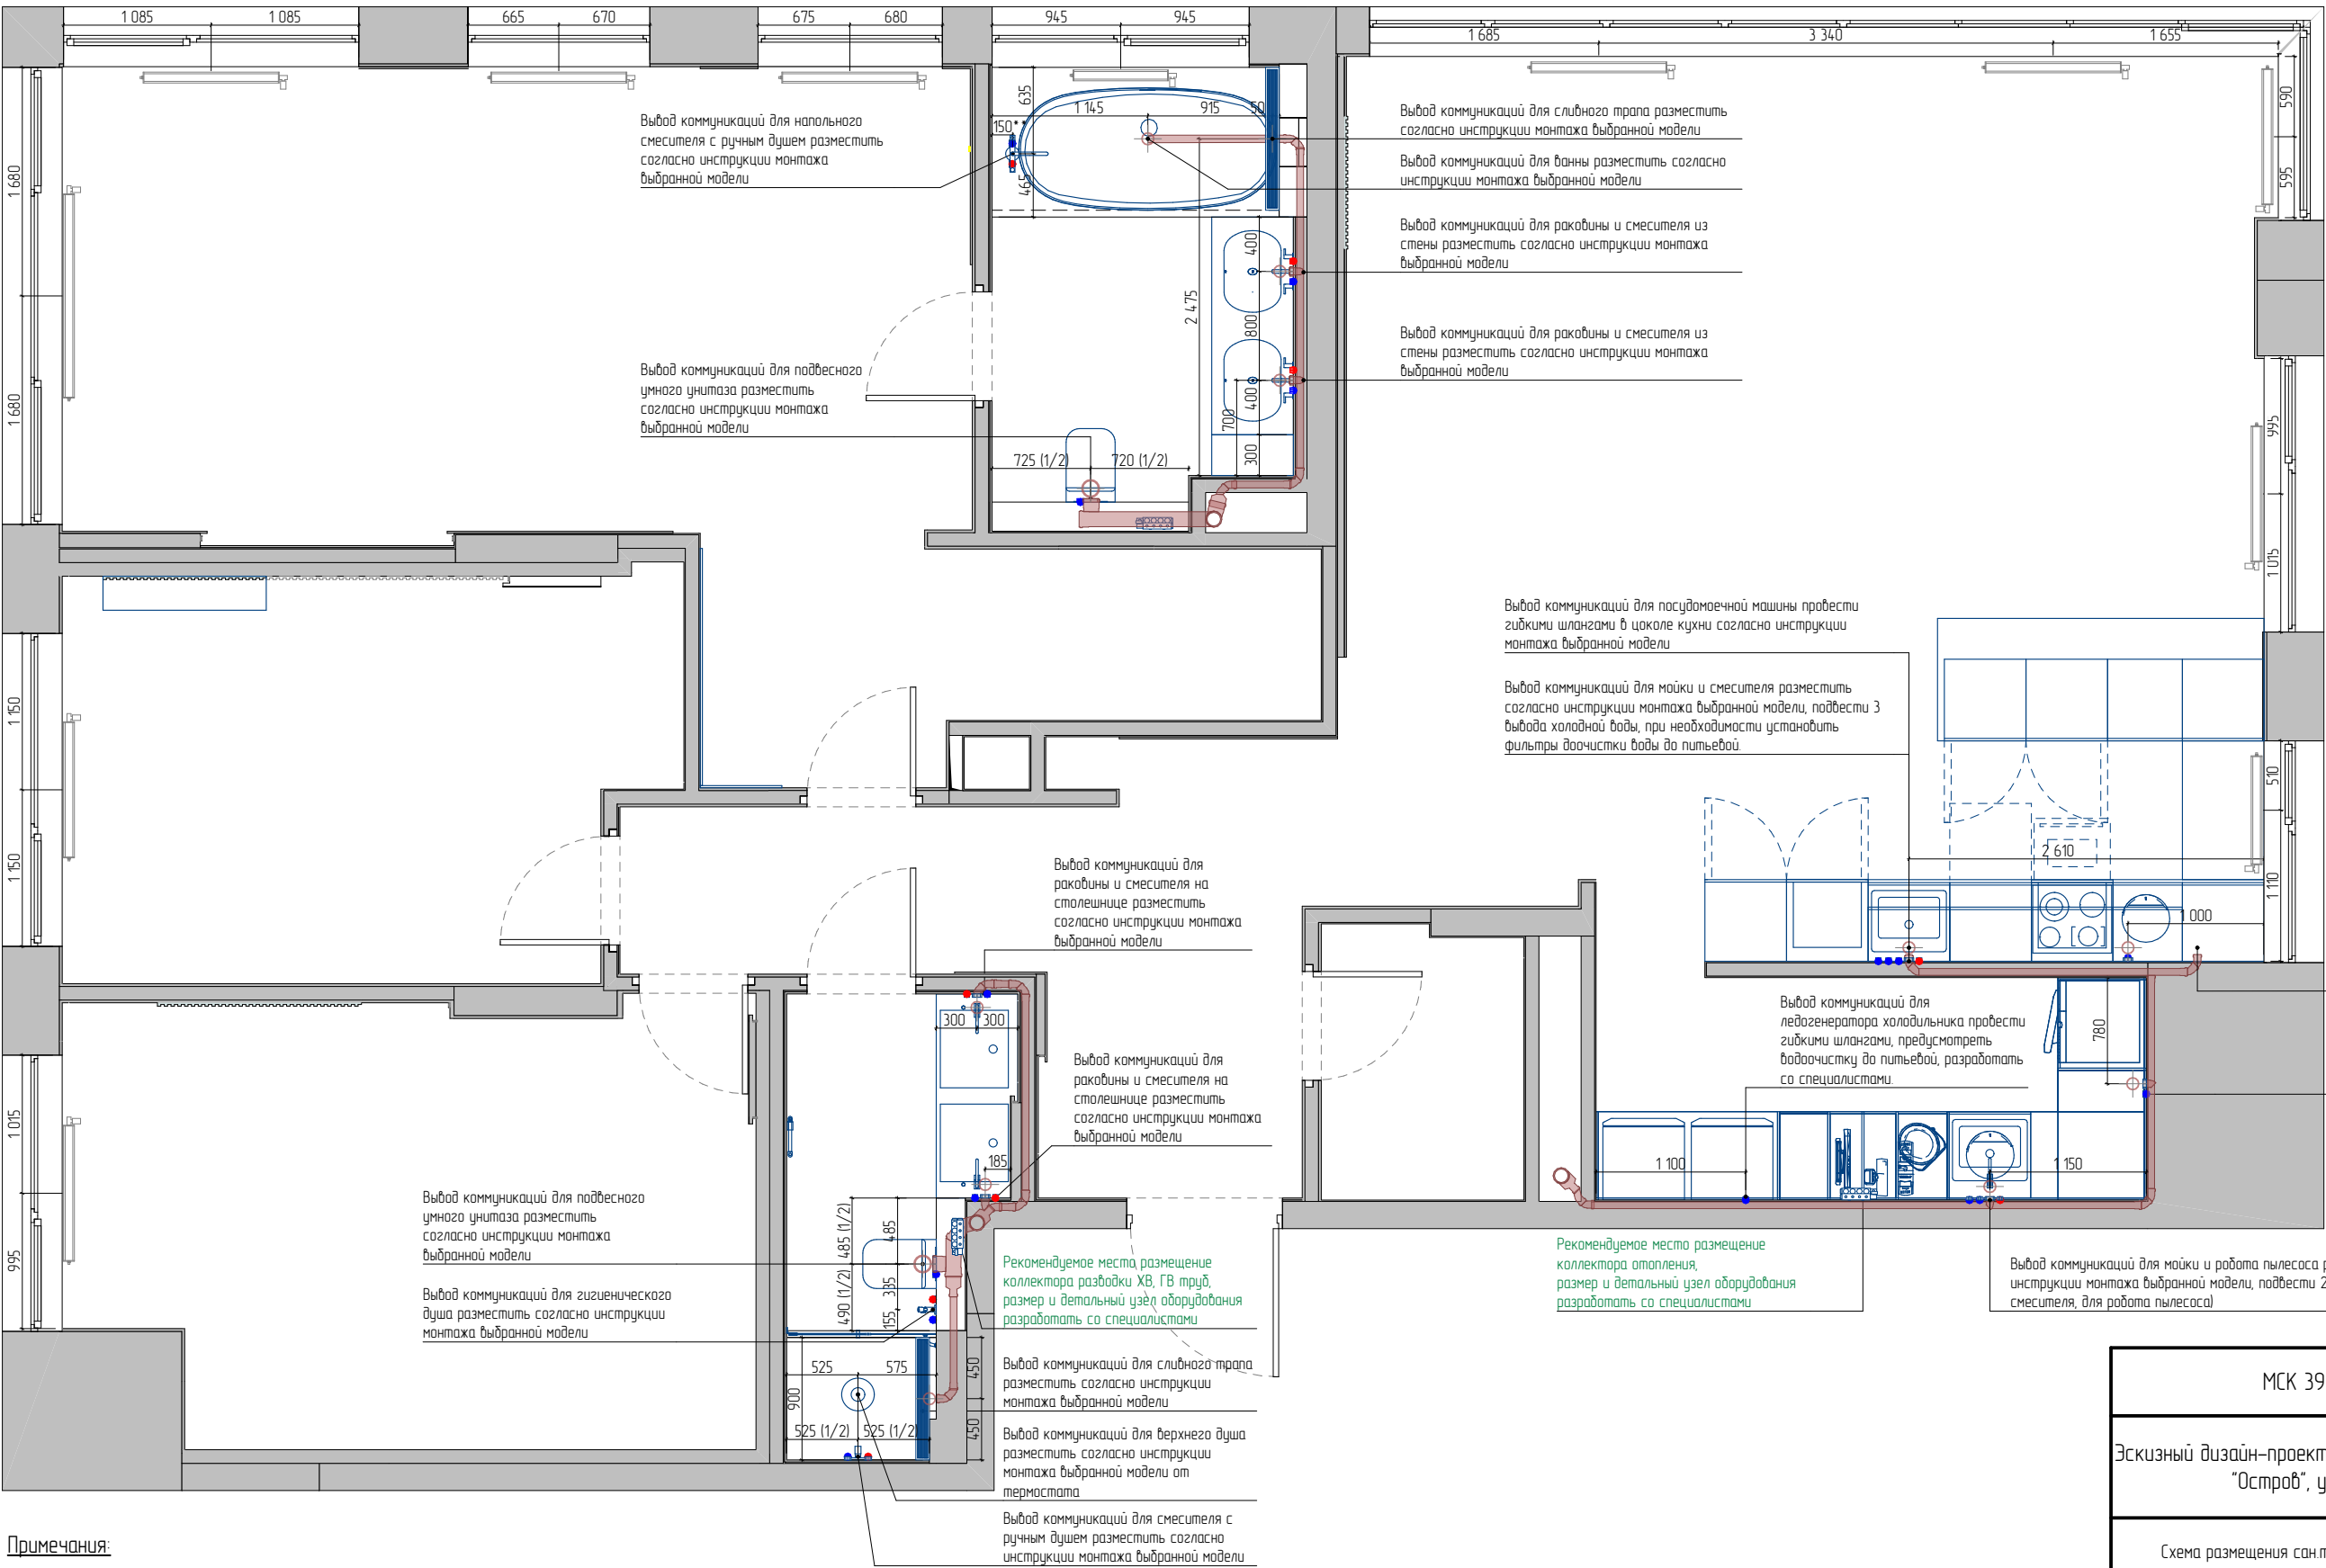

- Условные обозначения:
- Конструкции наружных стен
 - Трубы канализации
 - Радиатор отопления
 - Выход коммуникаций (ХВС, ГВС, канал-ция)

Примечания:

- Привязку вывода коммуникаций уточнить после подбора сан.тех. оборудования. Выполнить по инструкции монтажа.
- Вывод коммуникаций для посудомоечной машины провести гибкими шлангами в цоколе кухонного гарнитура, разработать со специалистами.
- Предусмотреть фильтры для очистки водопроводной воды на магистрали водопровода.
- Предусмотреть люки скрытого монтажа для доступа к коммуникациям, размещение определить по месту, согласовать с сантехниками.
- Уклон канализационных труб выполнить минимально допустимой величины (1 см на 1 метр трубы).
- Согласовать схему канализации со специалистами.
- Выводы коммуникаций для радиаторов отопления согласовать со специалистами.
- * – размеры уточнить по месту.
- Размеры и характеристики радиаторов отопления согласовать со специалистами, предусмотреть терморегуляторы.
- Данный лист требует доработки в соответствии с техническими схемами и схемами размещения сантехнических выпусков под конкретное сантехническое оборудование, которое будет выдано поставщиками сантехнического оборудования после закупки данного оборудования.

МСК 392.12.25–ЭП ПРЕМИУМ			
Эскизный дизайн–проект интерьера квартиры в г. Москва ЖК "Остров", ул. Нижние Мневники д. 7			
Схема размещения сан.тех.оборудования, канализации, ХВС, ГВС.			
Дизайнер интерьера №1 Александр Батеньков	Стадия	Лист	Листов
	ЭП	16	120
		Подп.	Дата
ГАП	Батеньков А.С.		
Гл. дизайнер	Власова В.А.		
Гл. проектиров.	Луныкова В.Н.		