


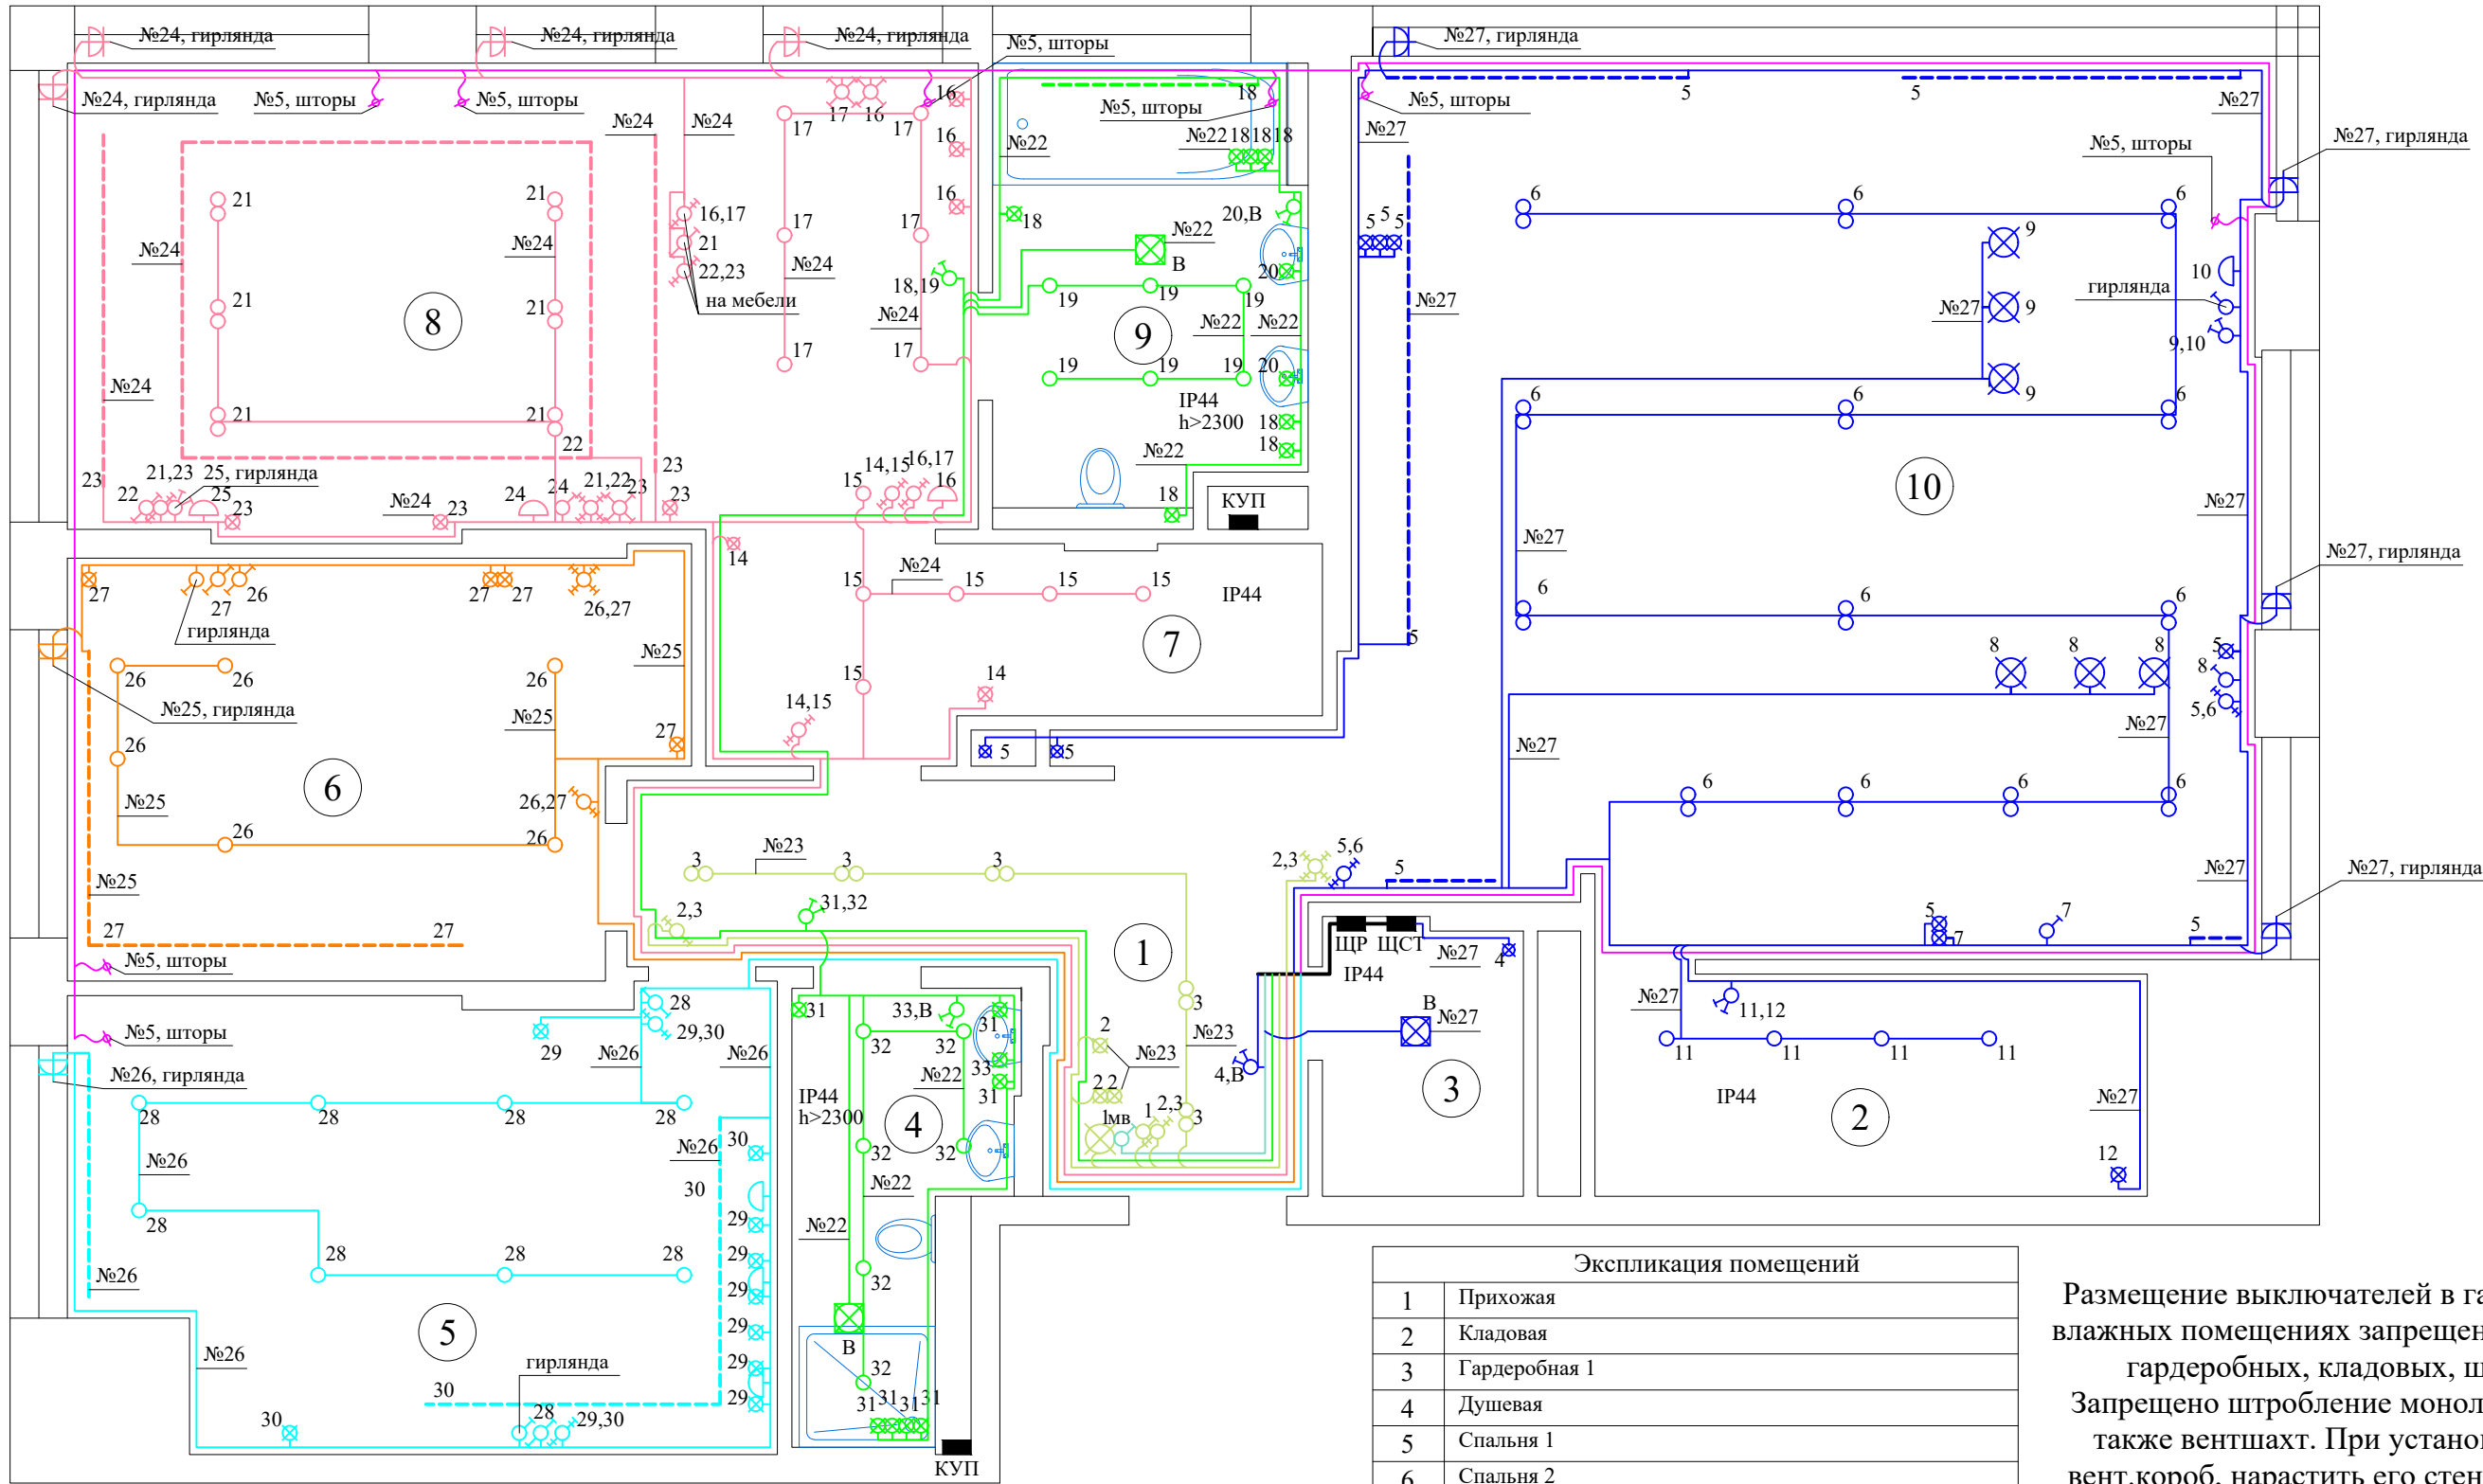

Экспликация помещений	
1	Прихожая
2	Кладовая
3	Гардеробная 1
4	Душевая
5	Спальня 1
6	Спальня 2
7	Гардеробная 2
8	Мастер спальня
9	Мастер ванная
10	Кухня гостиная

Размещение выключателей в гардеробных, кладовых, влажных помещениях запрещено. Размещение щитов в гардеробных, кладовых, шкафах запрещено. Запрещено штробление монолитных конструкций, а также вентшахт. При установке оборудования на вент.короб, нарастить его стену гипсовыми блоками. Установить оборудование не повреждая вент.короб. Обеспечить целостность вент.коробов.

						ИСПОЛНИТЕЛЬНАЯ ДОКУМЕНТАЦИЯ			
						Заказчик: <u>частное лицо</u>			
Изм	Кол.	Лист	№ док	Подп.	Дата	Жилая квартира по адресу: <u>г.Москва, ул.Нижние Мневники, д.7, кв.Сачук Ю.Е.</u>	Стадия	Лист	Листов
ГИП		<i>Сарафонов</i>					ИД	4	6
Исполн.		<i>Салюк</i>							
Проверил		<i>Загуменная</i>							
						Сеть освещения. План.	ООО "СтройПроект"		

Условные обозначения	
	Выключатель однополюсный, скрытой установки
	Выключатель однополюсный, сдвоенный, скрытой уст-ки
	Переключатель однополюсный, скрытой установки
	Переключатель двухполюсный, скрытой установки
	Переключатель перекрестный, скрытой установки
	Переключатель перекрестный, двухполюсный, скрытой установки
	Соотв. выключателей с управляемыми им светильниками
<u>№1</u>	Номер группы по однолинейной схеме
	Светильник подвесной, 220 В
	Подсветка, 220 В

Условные обозначения	
	Светильник светодиодный, "точка", встроенный в потолок
	Светодиодная подсветка
	ЩР Щит распределительный
	ЩСТ Щит слабых токов
	КУП Коробка уравнивания потенциалов
	Светильник настенный, бра, 220 В
	Вентилятор, 220В
	Вывод кабеля