


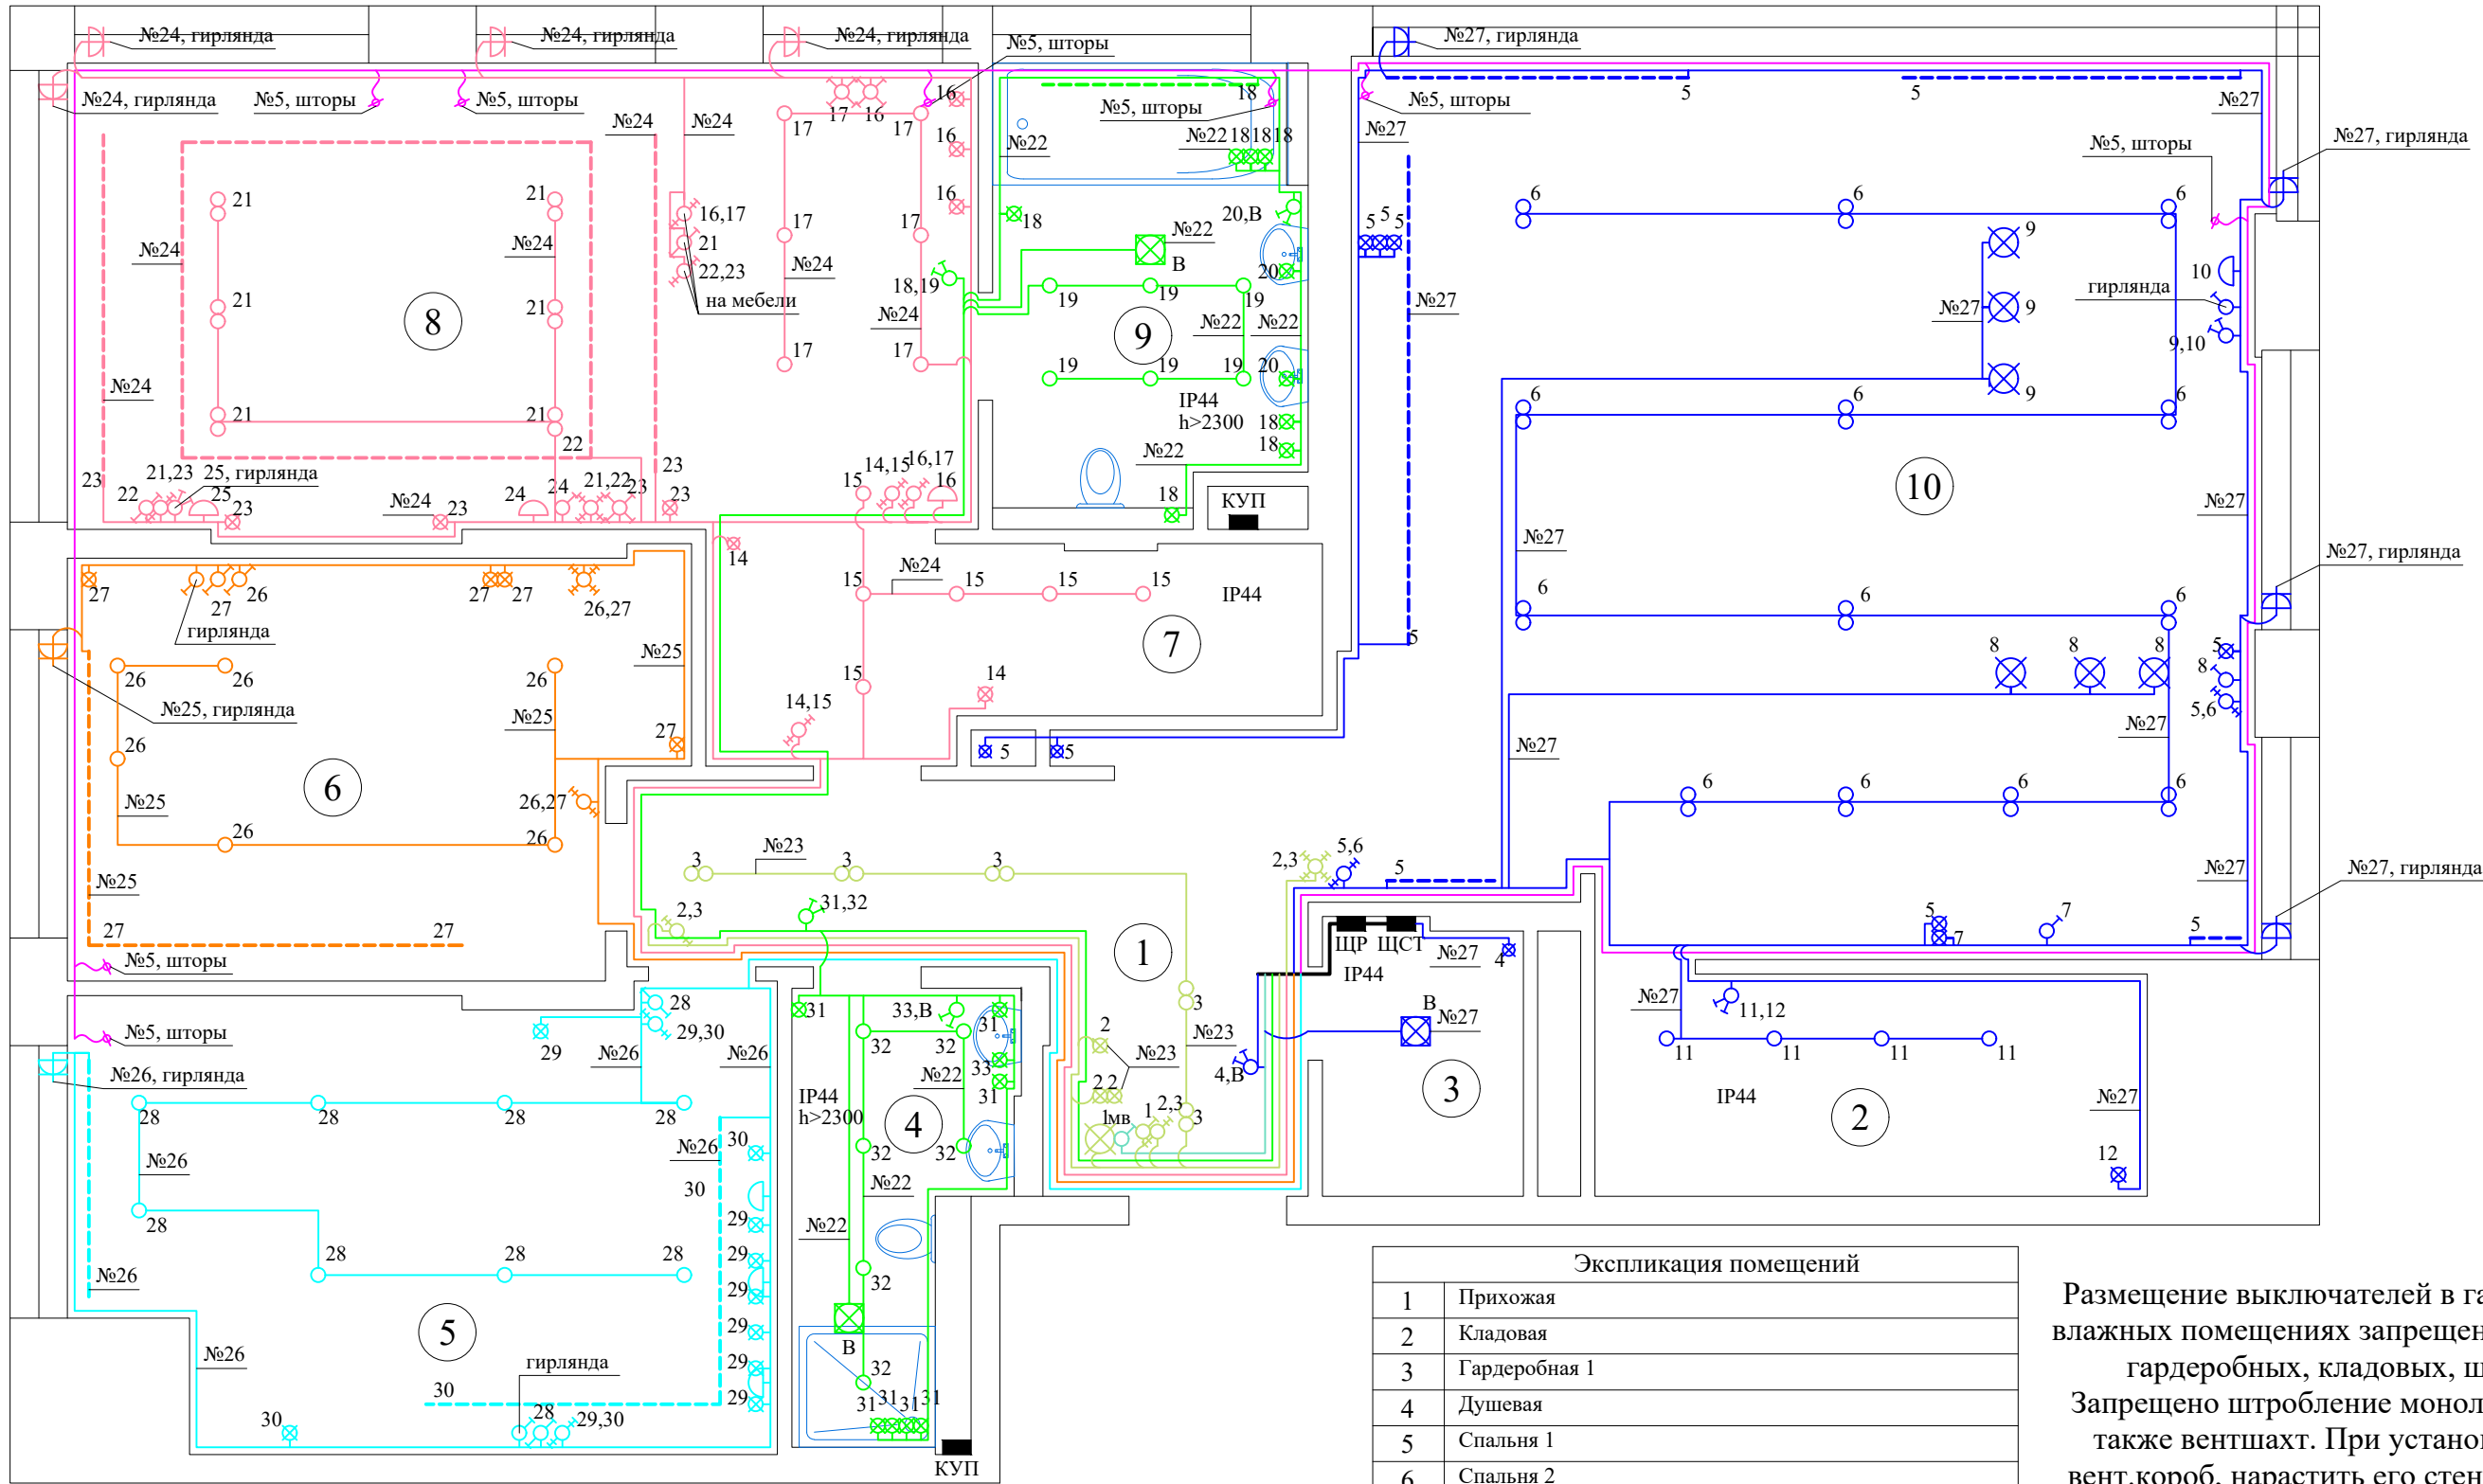

Экспликация помещений	
1	Прихожая
2	Кладовая
3	Гардеробная 1
4	Душевая
5	Спальня 1
6	Спальня 2
7	Гардеробная 2
8	Мастер спальня
9	Мастер ванная
10	Кухня гостиная

Размещение выключателей в гардеробных, кладовых, влажных помещениях запрещено. Размещение щитов в гардеробных, кладовых, шкафах запрещено. Запрещено штробление монолитных конструкций, а также вентшахт. При установке оборудования на вент.короб, нарастить его стену гипсовыми блоками. Установить оборудование не повреждая вент.короб. Обеспечить целостность вент.коробов.

Исполнительная документация					
Заказчик: <i>частное лицо</i>					
Изм	Кол.	Лист	№док	Подп.	Дата
ГИП		<i>Сарафонов</i>			Жилая квартира по адресу: <i>г.Москва, ул.Нижние Мневники, д.7, кв.Сачук Ю.Е.</i>
Исполн.		<i>Салюк</i>			Стадия
Проверил		<i>Загуменная</i>			Лист
Сеть освещения. План.					
Листов					
ИД					
4					
6					
ООО "СтройПроект"					

Условные обозначения	
	Выключатель однополюсный, скрытой установки
	Выключатель однополюсный, сдвоенный, скрытой уст-ки
	Переключатель однополюсный, скрытой установки
	Переключатель двухполюсный, скрытой установки
	Переключатель перекрестный, скрытой установки
	Переключатель перекрестный, двухполюсный, скрытой установки
	Соотв. выключателей с управляемыми им светильниками
	№1 Номер группы по однолинейной схеме
	Светильник подвесной, 220 В
	Подсветка, 220 В

Условные обозначения	
	Светильник светодиодный, "точка", встроенный в потолок
	Светодиодная подсветка
	ЩР Щит распределительный
	ЩСТ Щит слабых токов
	КУП Коробка уравнивания потенциалов
	Светильник настенный, бра, 220 В
	Вентилятор, 220В
	Вывод кабеля

