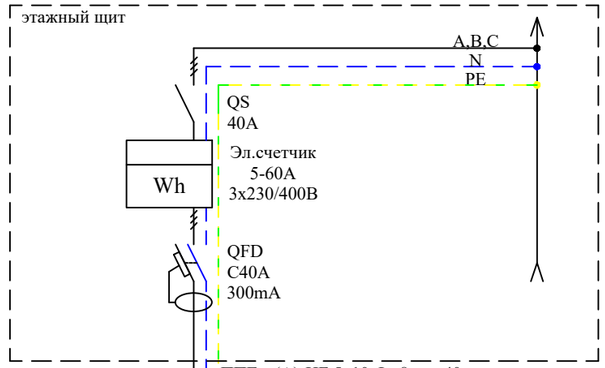


ЩР, IP31

ППГнг(А)-HF 5х10, L=8м, п.40

Ру=39,9кВт
Рр=20,0кВт
Iр=31,1А
cosφ=0,93
ΔUmax ≤ 1.5 %
230/400В, 50Гц

Фаза А - 7,2кВт
Фаза В - 7,5кВт
Фаза С - 7,2кВт

SH203 C32A

A,B,C
N
PE

Распределительный пункт			SH203 C20A	SH203 C20A	SH203 C20A	DSH201 C16A 30mA	DSH201 C16A 30mA	DSH201 C16A 30mA	DSH201 C16A 30mA	DSH201 C16A 30mA	DSH201 C16A 30mA	DSH201 C16A 30mA	DSH201 C16A 30mA	DSH201 C16A 30mA	DSH201 C16A 30mA	DSH201 C16A 30mA	DSH201 C16A 30mA	DSH201 C16A 30mA	DSH201 C16A 30mA	DSH201 C16A 30mA
	Данные питающей сети																			
	Счетчик																			
	Руст, Рр, Iр, cosφ, ΔUmax	Аппарат ввода; Тип; Iн, А; Расцепитель																		
	Автомат отходящей линии	Тип расцепителя Iн, А;		FH204 25А 30мА	FH204 25А 30мА															
	Марка и сечение проводника	Маркировка, длина участка	ВВГнг(А)-LS 5х4 L=10м, п.25	ВВГнг(А)-LS 5х4 L=10м, п.25	ВВГнг(А)-LS 5х4 L=15м, п.25	ВВГнг(А)-LS 3х2,5 L=10м, п.20	ВВГнг(А)-LS 3х4 L=10м, п.20	ВВГнг(А)-LS 3х2,5 L=10м, п.20	ВВГнг(А)-LS 3х2,5 L=10м, п.20	ВВГнг(А)-LS 3х2,5 L=10м, п.20	ВВГнг(А)-LS 3х2,5 L=15м, п.20	ВВГнг(А)-LS 3х2,5 L=25м, п.20	ВВГнг(А)-LS 3х2,5 L=30м, п.20	ВВГнг(А)-LS 3х2,5 L=20м, п.20	ВВГнг(А)-LS 3х2,5 L=30м, п.20	ВВГнг(А)-LS 3х2,5 L=40м, п.20	ВВГнг(А)-LS 3х2,5 L=75м, п.20	ВВГнг(А)-LS 3х2,5 L=25м, п.20	ВВГнг(А)-LS 3х2,5 L=55м, п.20	ВВГнг(А)-LS 3х2,5 L=15м, п.20
Электроприемник	Условное обозначение																			
	Маркировка		№1	№2	№3	№4	№5	№6	№7	№8	№9	№10	№11	№12	№13	№14	№15	№16	№17	№18
	Фаза		A,B,C	A,B,C	A,B,C	A	B	C	A	B	C	A	B	C	A	B	C	A	B	C
	Рн, кВт		6,0	6,0	6,0	1,5	2,5	1,5	1,5	1,0	0,3	2,0	0,9	0,8	0,8	0,9	1,8	0,5	1,4	1,7
	Iн, А		9,1	9,1	9,1	6,8	11,4	6,8	6,8	4,5	1,4	9,1	4,1	3,6	3,6	4,1	8,2	2,3	6,4	7,7
	Наименование электроприемника		Варочная панель	Водонагреватель проточный: душевая	Водонагреватель проточный: мастер ванная	Стиральная машина	Духовой шкаф	Сушильная машина	Посудомоечная машина	Микроволновая печь (СВЧ)	Холодильник, вин.ш.	Розетки: кухня (фартук); вытяжка	Розетки: прихожая, кладовая, гардеробная	Розетки: душевая	Розетки: спальня 1	Розетки: спальня 2	Розетки: гардеробная 2, мастер спальня	Розетки: мастер ванная	Розетки: кухня гостиная	Теплый пол: : кухня гостиная, прихожая

Изм	Кол.	Лист	№док	Подп.	Дата
ГИП		*Сарафонов*			
Исполн.		*Салюк*			
Проверил		*Загуменная*			

ИСПОЛНИТЕЛЬНАЯ ДОКУМЕНТАЦИЯ

Заказчик: *частное лицо*

Жилая квартира по адресу: *г.Москва, ул.Нижние Мневники, д.7, кв.Сачук Ю.Е.*

Стадия	Лист	Листов
ИД	2	6

Однолинейная расчетная схема ЩР

ООО "СтройПроект"