
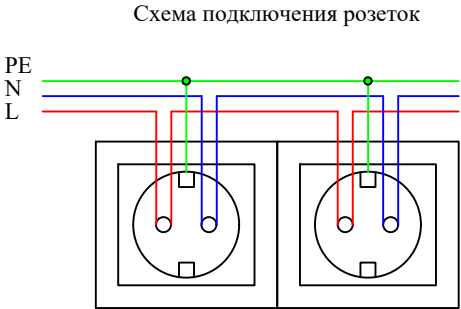


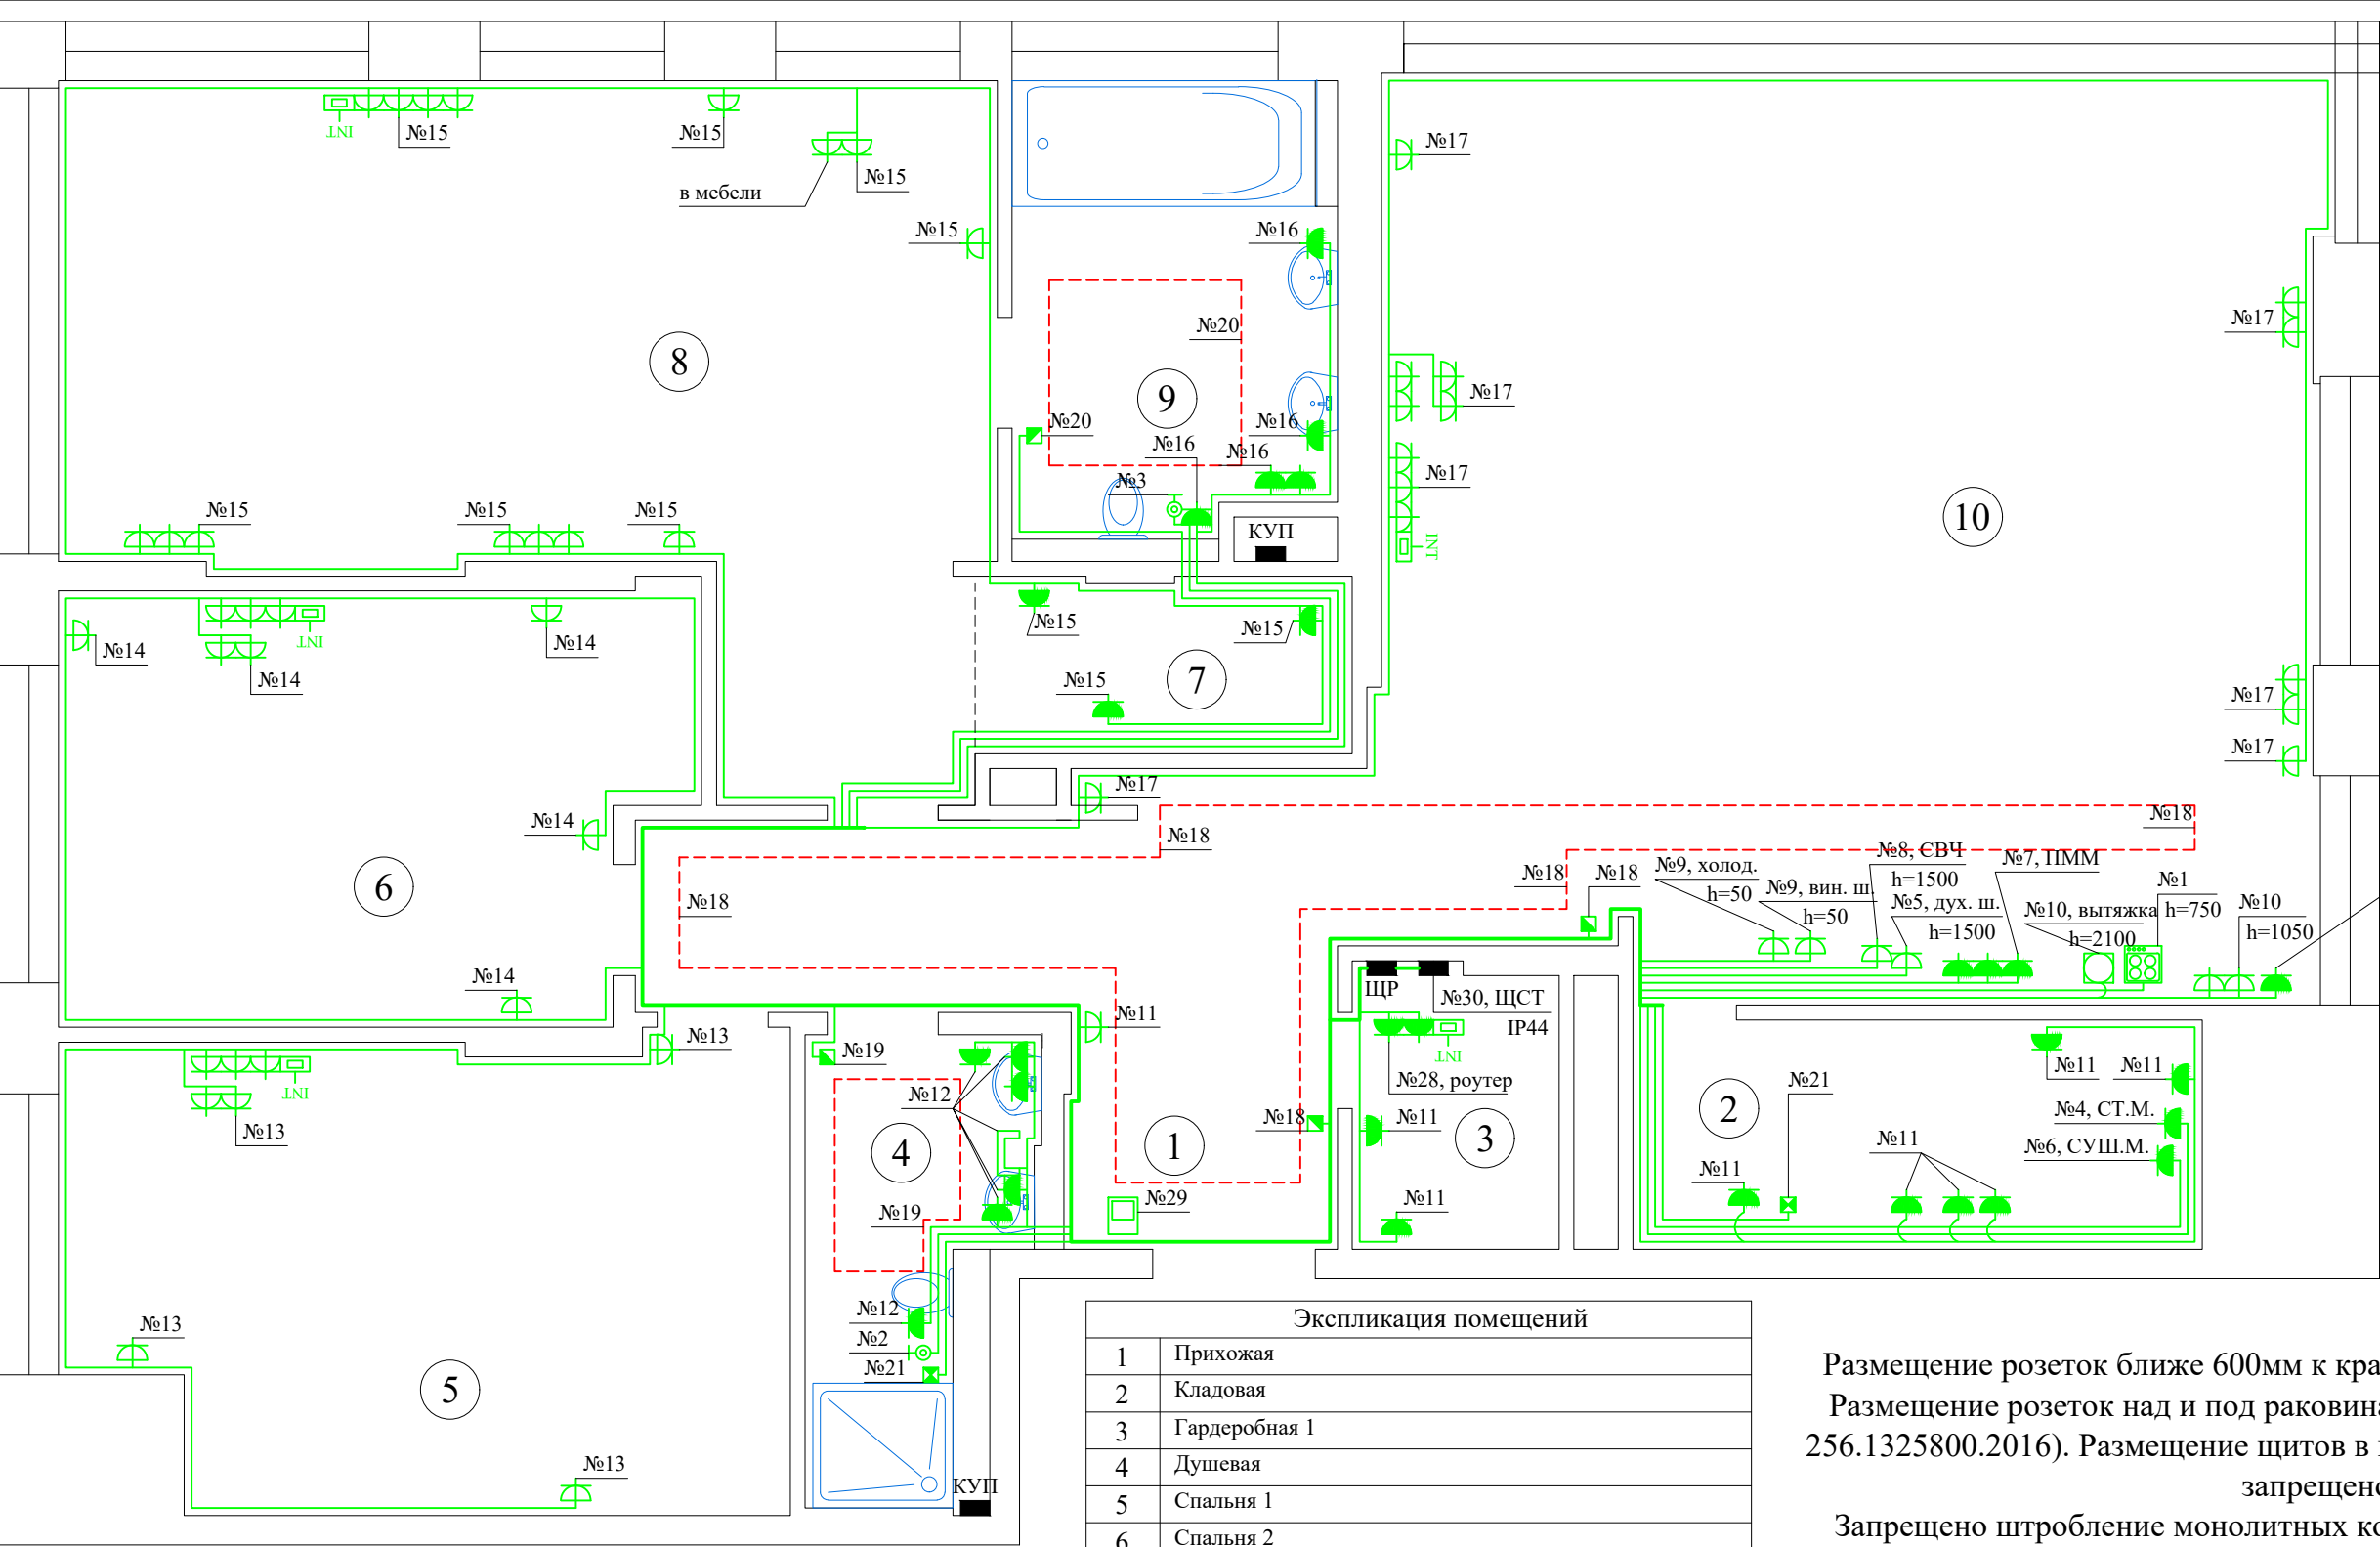

Экспликация помещений	
1	Прихожая
2	Кладовая
3	Гардеробная 1
4	Душевая
5	Спальня 1
6	Спальня 2
7	Гардеробная 2
8	Мастер спальня
9	Мастер ванная
10	Кухня гостиная

Размещение розеток ближе 600мм к краю ванной, душевой запрещено.
Размещение розеток над и под раковинами и мойками запрещено (СП 256.1325800.2016). Размещение щитов в гардеробных, кладовых, шкафах запрещено.

Запрещено штробление монолитных конструкций, а также вентшахт.
При установке розеток и оборудования на вент.короб, нарастить его стену гипсовыми блоками. Установить розетки не повреждая вент.короб.
Обеспечить целостность вент.коробов.

Условные обозначения	
	Розетка штепсельная двухполюсная, с защитным контактом, скрытой установки
	Розетка штепсельная двухполюсная, с защитным контактом, скрытой установки, влагозащищенная, IP44
	Щит распределительный
	Щит слабых токов
	Номер группы по однолинейной схеме
	Коробка уравнивания потенциалов
	Розетка интернет
	Регулятор теплого пола
	Участок теплого пола

Условные обозначения	
	Водонагреватель
	Система от протечки воды и отопления
	Видеодомофон
	Полотенцесушитель

						ИСПОЛНИТЕЛЬНАЯ ДОКУМЕНТАЦИЯ				
						Заказчик: <u>частное лицо</u>				
Изм	Кол.	Лист	№док	Подп.	Дата	Жилая квартира по адресу: <u>г.Москва, ул.Нижние Мневники, д.7, кв.Сачук Ю.Е.</u>		Стадия	Лист	Листов
ГИП		<i>Сарафонов</i>						ИД	5	6
Исполн.		<i>Салюк</i>				Розеточная сеть. План.		ООО "СтройПроект"		
Проверил		<i>Загуменная</i>								