


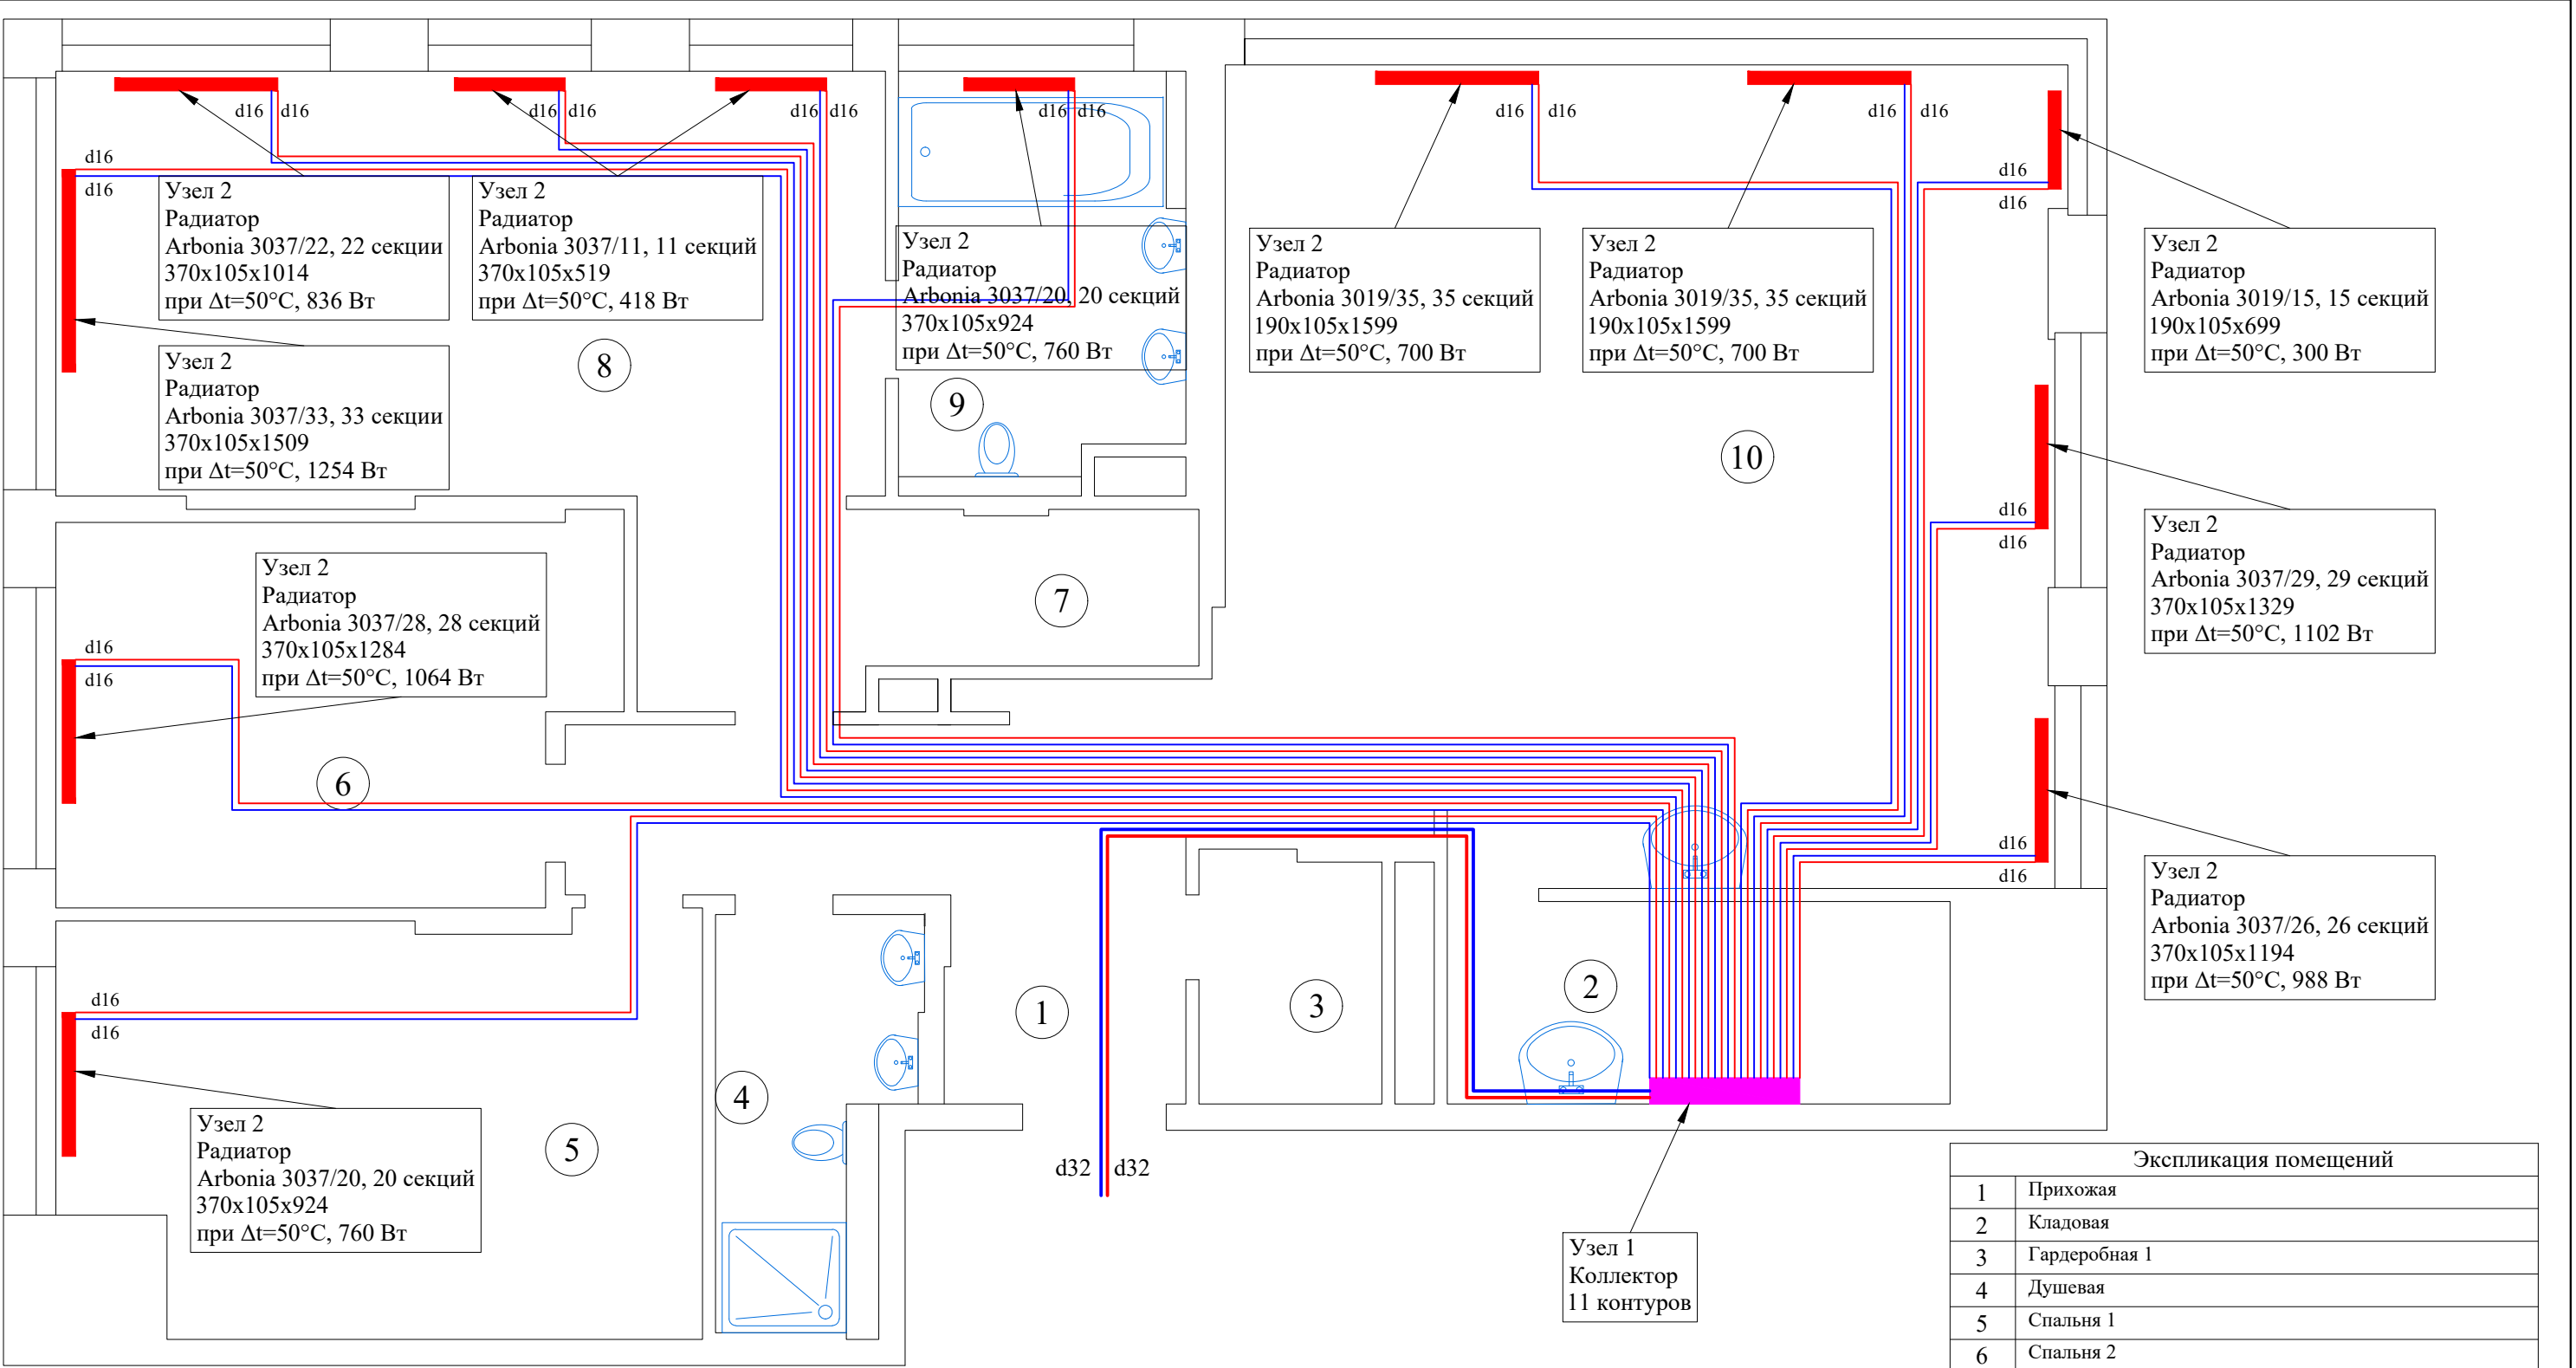

Покупку приборов отопления производить после согласования проекта в Управляющей компании

Выделенная тепловая мощность	9210 Вт
Мощность новых отопительных приборов	9300 Вт

УСЛОВНЫЕ ОБОЗНАЧЕНИЯ		
— T11 —	Подводящий трубопровод системы отопления	80° С
— T21 —	Обратный трубопровод системы отопления	60° С

Экспликация помещений	
1	Прихожая
2	Кладовая
3	Гардеробная 1
4	Душевая
5	Спальня 1
6	Спальня 2
7	Гардеробная 2
8	Мастер спальня
9	Мастер ванная
10	Кухня гостиная

						ОВ			
						Заказчик: <u>частное лицо</u>			
Изм	Кол.	Лист	№док	Подп.	Дата	Жилая квартира по адресу: <u>г.Москва, ул.Нижние Мневники, д.7, кв.Сачук Ю.Е.</u>	Стадия	Лист	Листов
ГИП		<i>Сарафонов</i>					Р	3	6
Исполн.		<i>Салюк</i>							
Проверил		<i>Загуменная</i>				Отопление. План. Устанавливаемые приборы отопления. Новая коллекторная система разводки.	ООО "СтройПроект"		