
План квартиры. М1:100

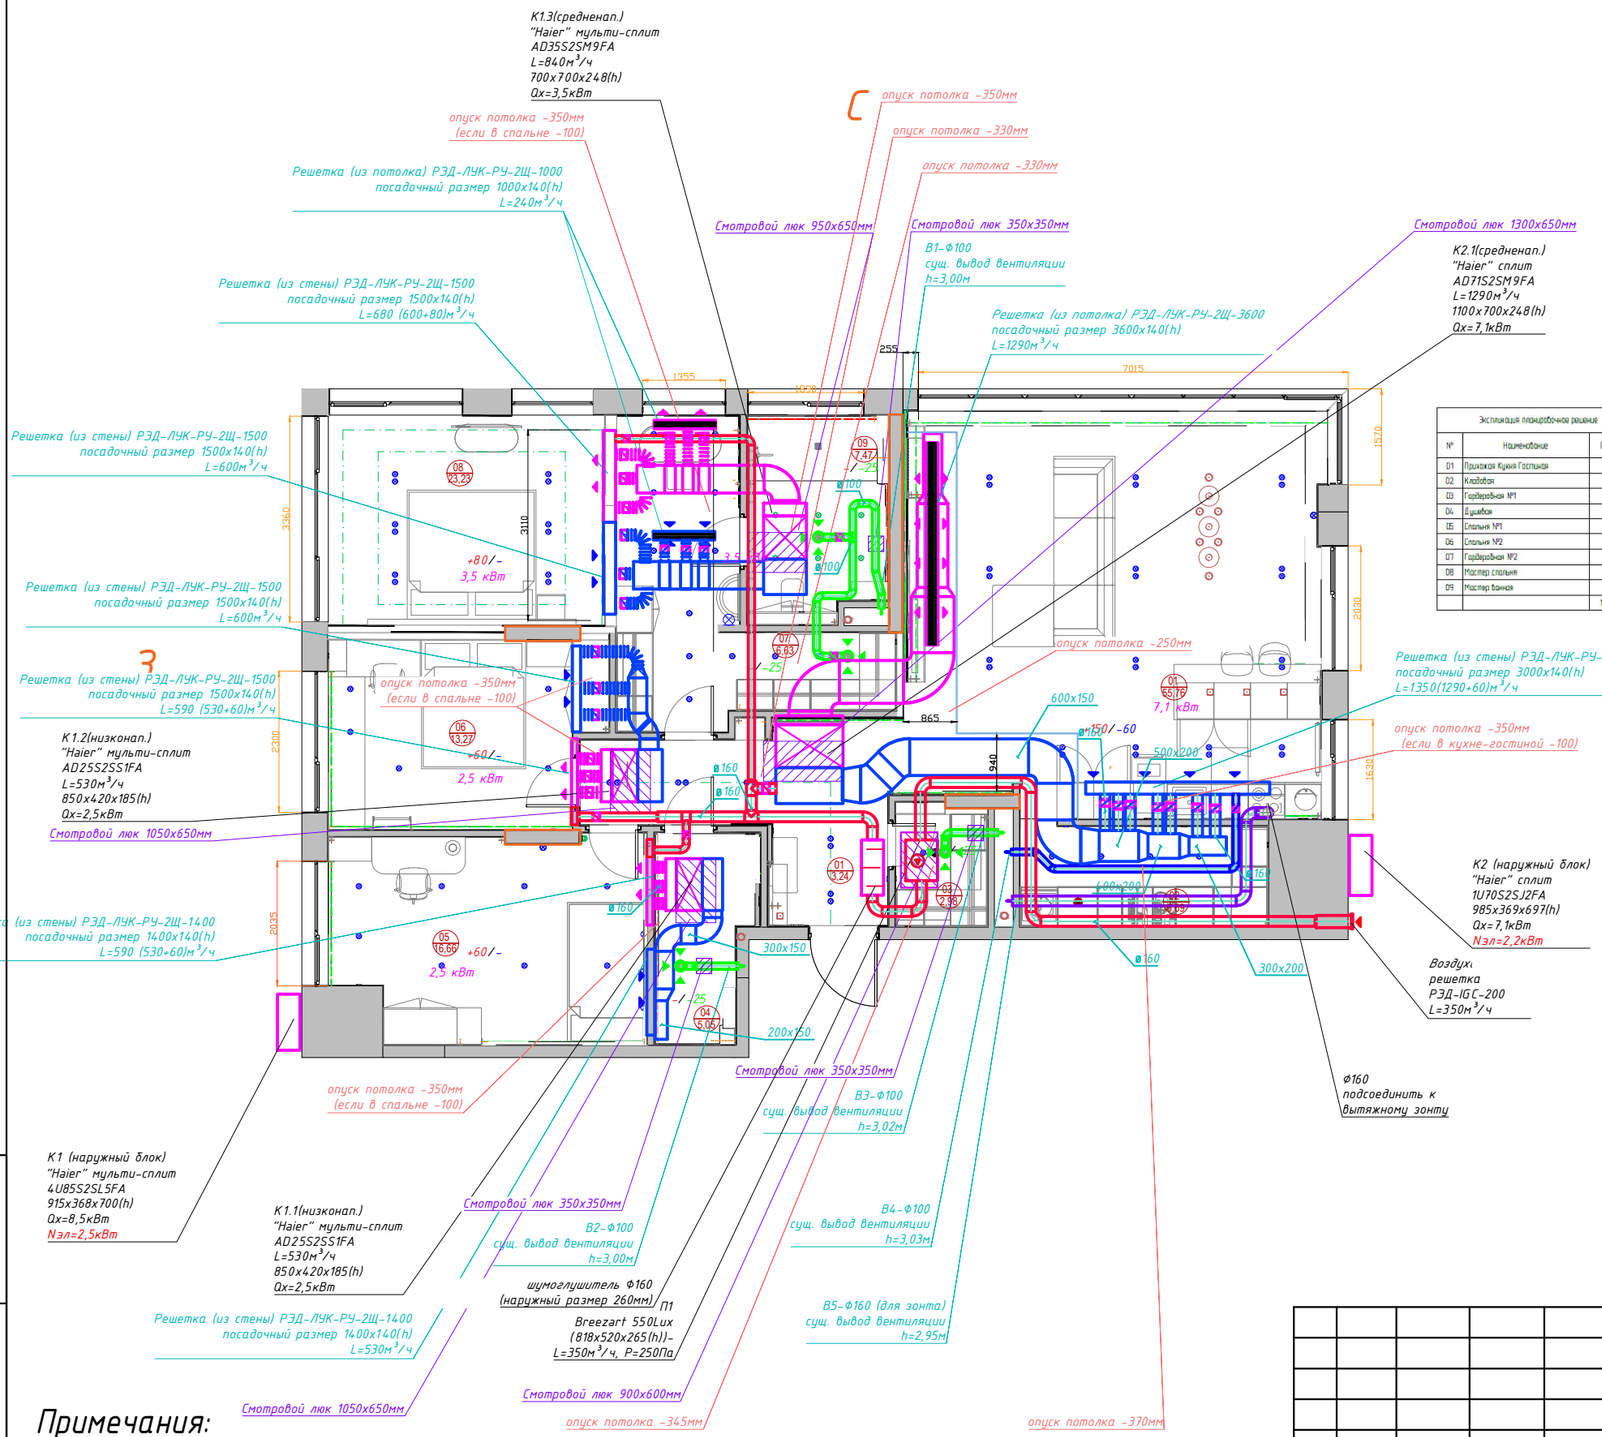

Условные обозначения

Обозначение	Наименование
-/-50	Расход воздуха(приток/вытяжка)
	Прямоугольный воздуховод
	Круглый воздуховод
	Смотровой люк
	Внутренний блок кондиционера (канальный тип)
	Воздухораспределители
	Адаптеры под решетки
Ду32	Трубы для дренажа кондиционеров, типоразмер
Ф6,35 (1/4") Ф9,52(3/8")	Трубы для холодоснабжения кондиционера, типоразмер
	Дроссель-клапан, обратный клапан

Примечания:

1. Опуск потолка указан с учетом конструкции потолка 50мм.
2. Подвод питания производится к наружным блокам мульти-сплит систем (расположеным в специальных нишах на фасаде здания) и к приточной установке.

Изм.	Кол. уч.	Лист	№ док.	Подпись	Дата
Нач. отдела		Дранкеевич А.М.			09.2026
Проверил		Дранкеевич А.М.			09.2026
Разработал		Матвеева О.Ю.			09.2026
Н. контроль		Дранкеевич А.М.			09.2026

09-03/2026-ОВ

Квартира по адресу: г. Москва, ЖК "Остров", ул. Нижние Мневники, д.7.

Вентиляция и кондиционирование

Стадия	Лист	Листов
РД	2	8

План 1 этажа (сводный план). М 1:100

Вентиляция и кондиционирование.

ООО "ИРВЕНТ"

Взаим.инв.№ | Подпись и дата | Инв.№подл.

Формат А3