


План квартиры. М1:100

Условные обозначения

Обозначение	Наименование
-/-50	Расход воздуха(приток/вытяжка)
	Прямоугольный воздуховод
	Круглый воздуховод
	Смотровой люк
	Внутренний блок кондиционера (канальный тип)
	Воздухораспределители
	Адаптеры под решетки
	Трубы для дренажа кондиционеров, типоразмер
	Трубы для холодоснабжения кондиционера, типоразмер
	Дроссель-клапан, обратный клапан

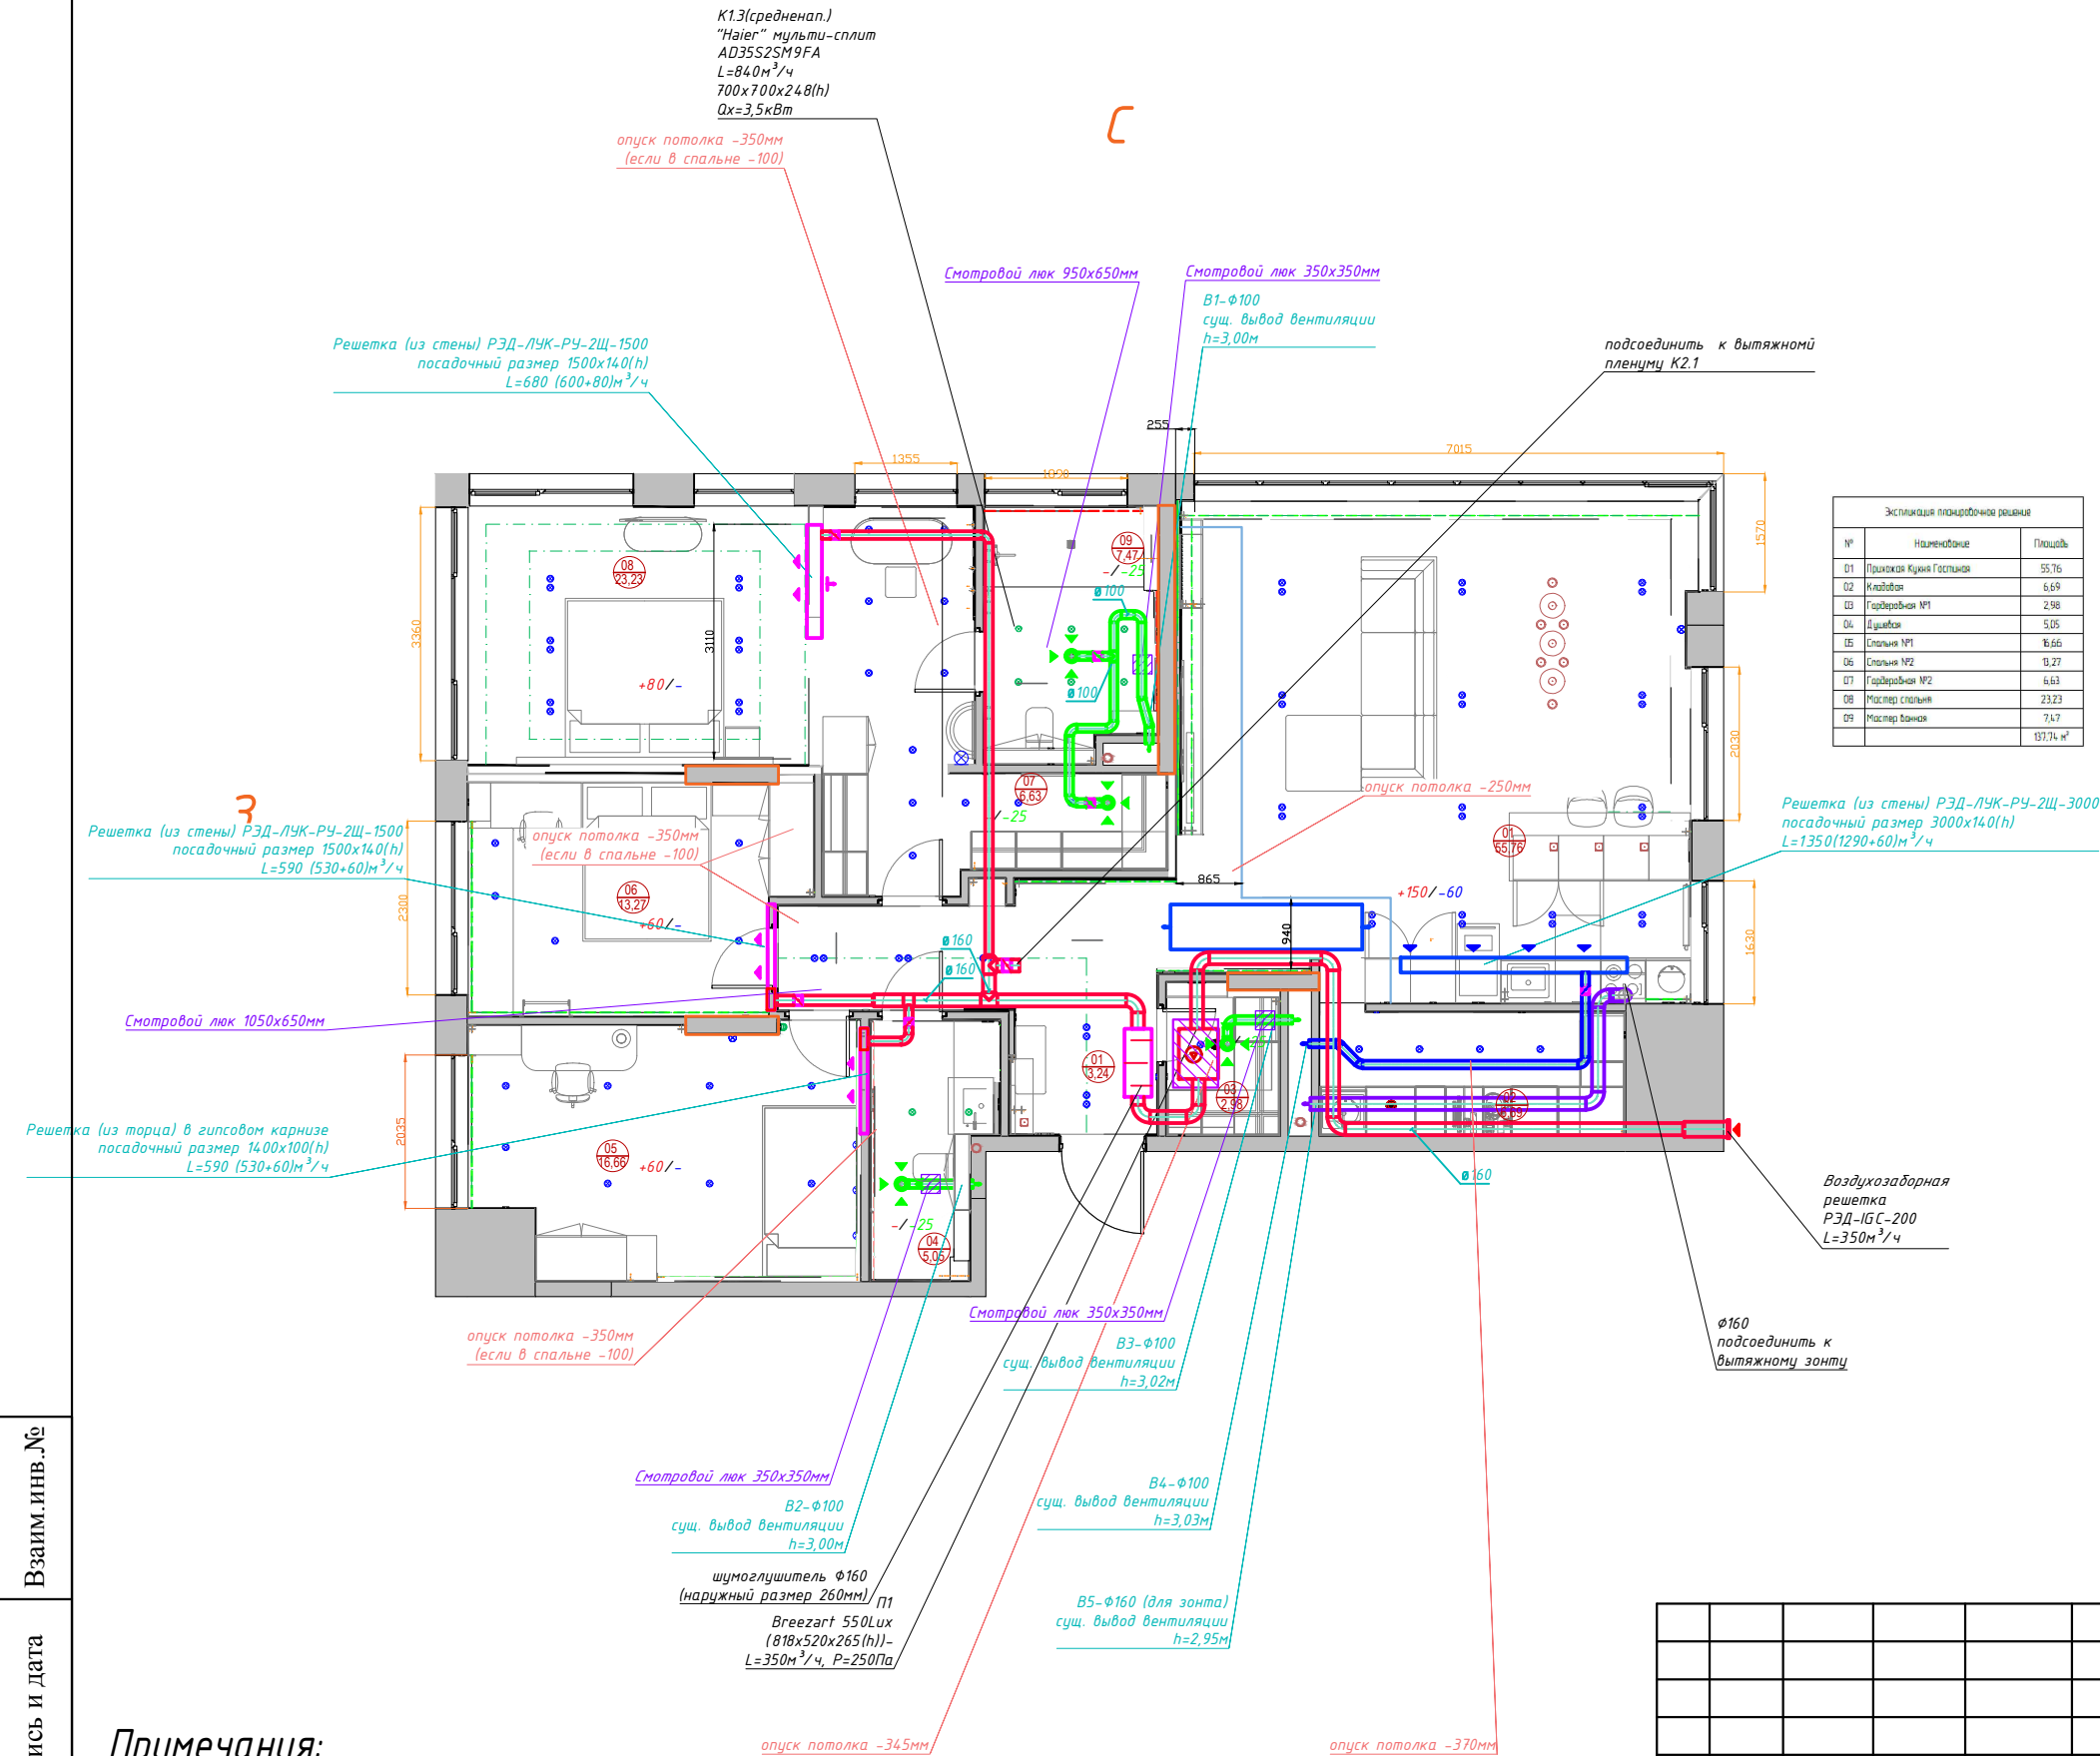

Примечания:

- Опуск потолка указан с учетом конструкции потолка 50мм.
- Подвод питания производится к наружным блокам мульти-сплит систем (расположенным в специальных нишах на фасаде здания) и к приточной установке.

09-03/2026-0В


Квартира по адресу: г. Москва, ЖК "Остров",
ул. Нижние Мневники, д.7.

Изм.	Кол. уч.	Лист	№ док.	Подпись	Дата			
						Вентиляция и кондиционирование	Стадия	Лист
							РД	3
								Листов
								8
Нач. отдела				Дранкеевич А.М.	09.2026	План 1 этажа. М 1:100 Вентиляция и кондиционирование.	ООО "ИРВЕНТ"	
Проверил				Дранкеевич А.М.	09.2026			
Разработал				Матвеева О.Ю.	09.2026			
Н. контроль				Дранкеевич А.М.	09.2026			

План квартиры. М1:100

Условные обозначения

Обозначение	Наименование
- / -50	Расход воздуха (приток / вытяжка)
	Прямоугольный воздуховод
	Круглый воздуховод
	Смотровой люк
	Внутренний блок кондиционера (канальный тип)
	Воздухораспределители
	Адаптеры под решетки
	Трубы для дренажа кондиционеров, типоразмер
	Трубы для холодоснабжения кондиционера, типоразмер
	Дроссель-клапан, обратный клапан

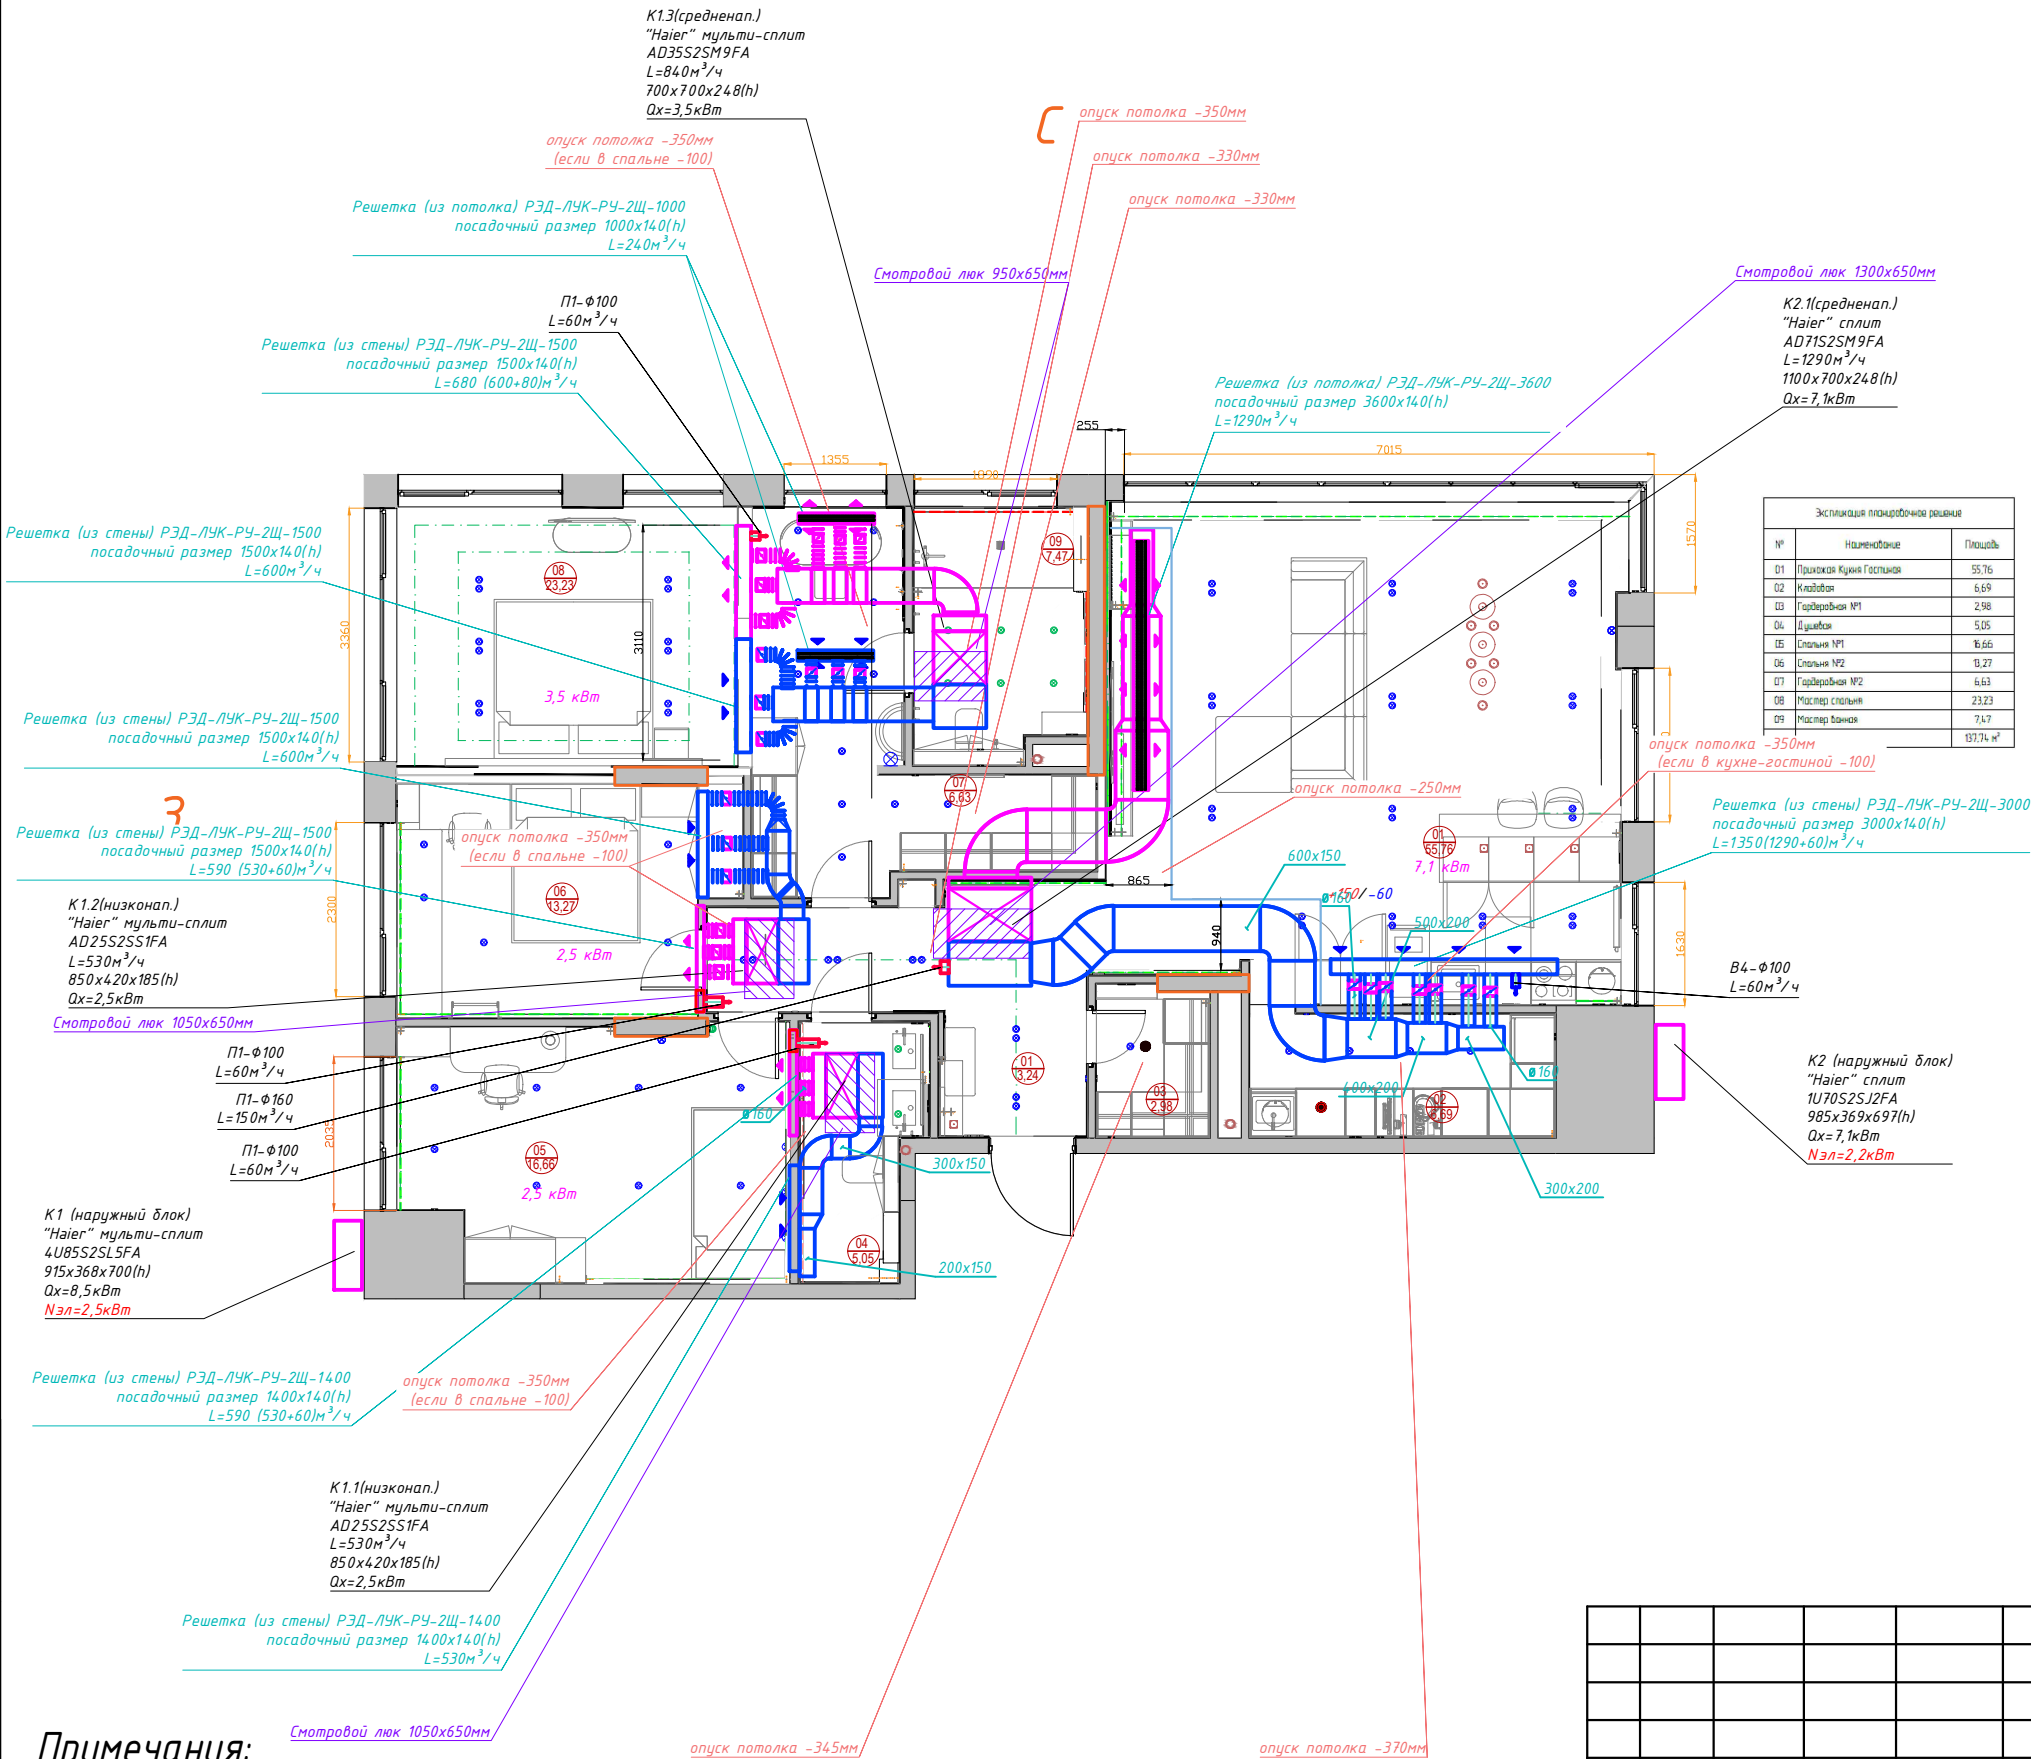

Примечания:

- Опуск потолка указан с учетом конструкции потолка 50мм.
- Подвод питания производится к наружным блокам мульти-сплит систем (расположенным в специальных нишах на фасаде здания) и к приточной установке.

09-03/2026-0В


Квартира по адресу: г. Москва, ЖК "Остров",
ул. Нижние Мневники, д.7.

						09-03/2026-0В			
						Квартира по адресу: г. Москва, ЖК "Остров", ул. Нижние Мневники, д.7.			
Изм.	Кол. уч.	Лист	№ док.	Подпись	Дата				
						Вентиляция и кондиционирование	Стадия	Лист	Листов
Нач. отдела	Дранкеевич А.М.			09.2026			РД	4	8
Проверил	Дранкеевич А.М.			09.2026					
Разработал	Матвеева О.Ю.			09.2026					
Н. контроль	Дранкеевич А.М.			09.2026					
						План 1 этажа. М 1:100 Кондиционирование.	ООО "ИРВЕНТ"		

План квартиры. М1:100

Условные обозначения

Обозначение	Наименование
- / -50	Расход воздуха(приток/вытяжка)
	Прямоугольный воздуховод
	Круглый воздуховод
	Смотровой люк
	Внутренний блок кондиционера (канальный тип)
	Воздухораспределители
	Адаптеры под решетки
	Трубы для дренажа кондиционеров, типоразмер Ду32
	Трубы для холодоснабжения кондиционера, типоразмер $\phi 6,35 (1/4")$ $\phi 9,52(3/8")$
	Дроссель-клапан, обратный клапан

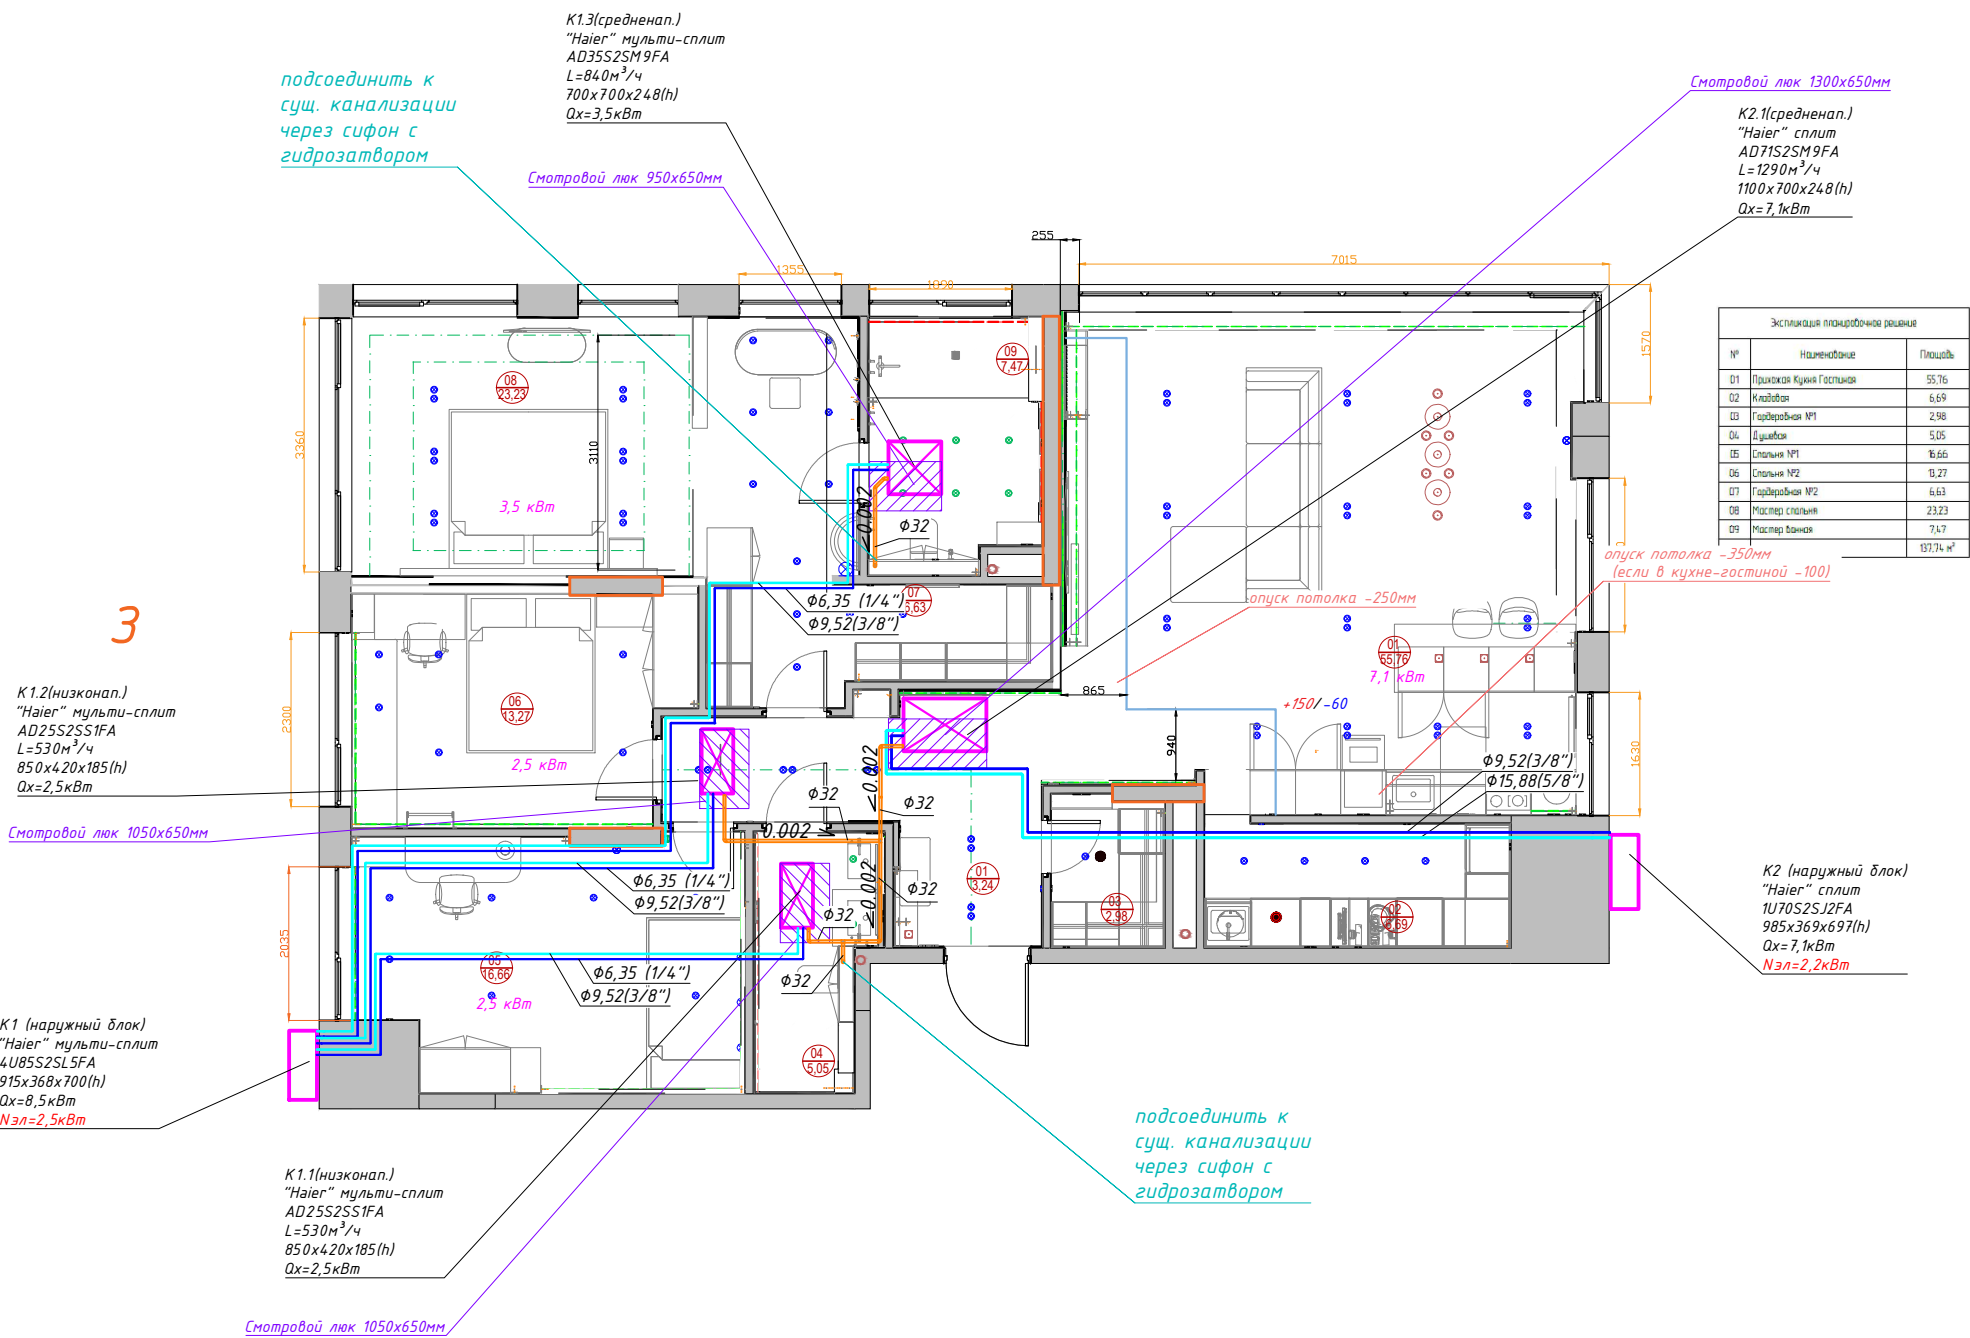

Примечания:

1. Опуск потолка указан с учетом конструкции потолка 50мм.
2. Подвод питания производится к наружным блокам мульти-сплит систем (расположенным в специальных нишах на фасаде здания) и к приточной установке.

						09-03/2026-0В			
						Квартира по адресу: г. Москва, ЖК "Остров", ул. Нижние Мневники, д.7.			
Изм.	Кол. уч.	Лист	№ док.	Подпись	Дата	Вентиляция и кондиционирование	Стадия	Лист	Листов
Нач. отдела	Дранкеевич А.М.			09.2026			РД	5	8
Проверил	Дранкеевич А.М.			09.2026					
Разработал	Матвеева О.Ю.			09.2026					
Н. контроль	Дранкеевич А.М.			09.2026					
						План 1 этажа. М 1:100 Кондиционирование.	ООО "ИРВЕНТ"		