


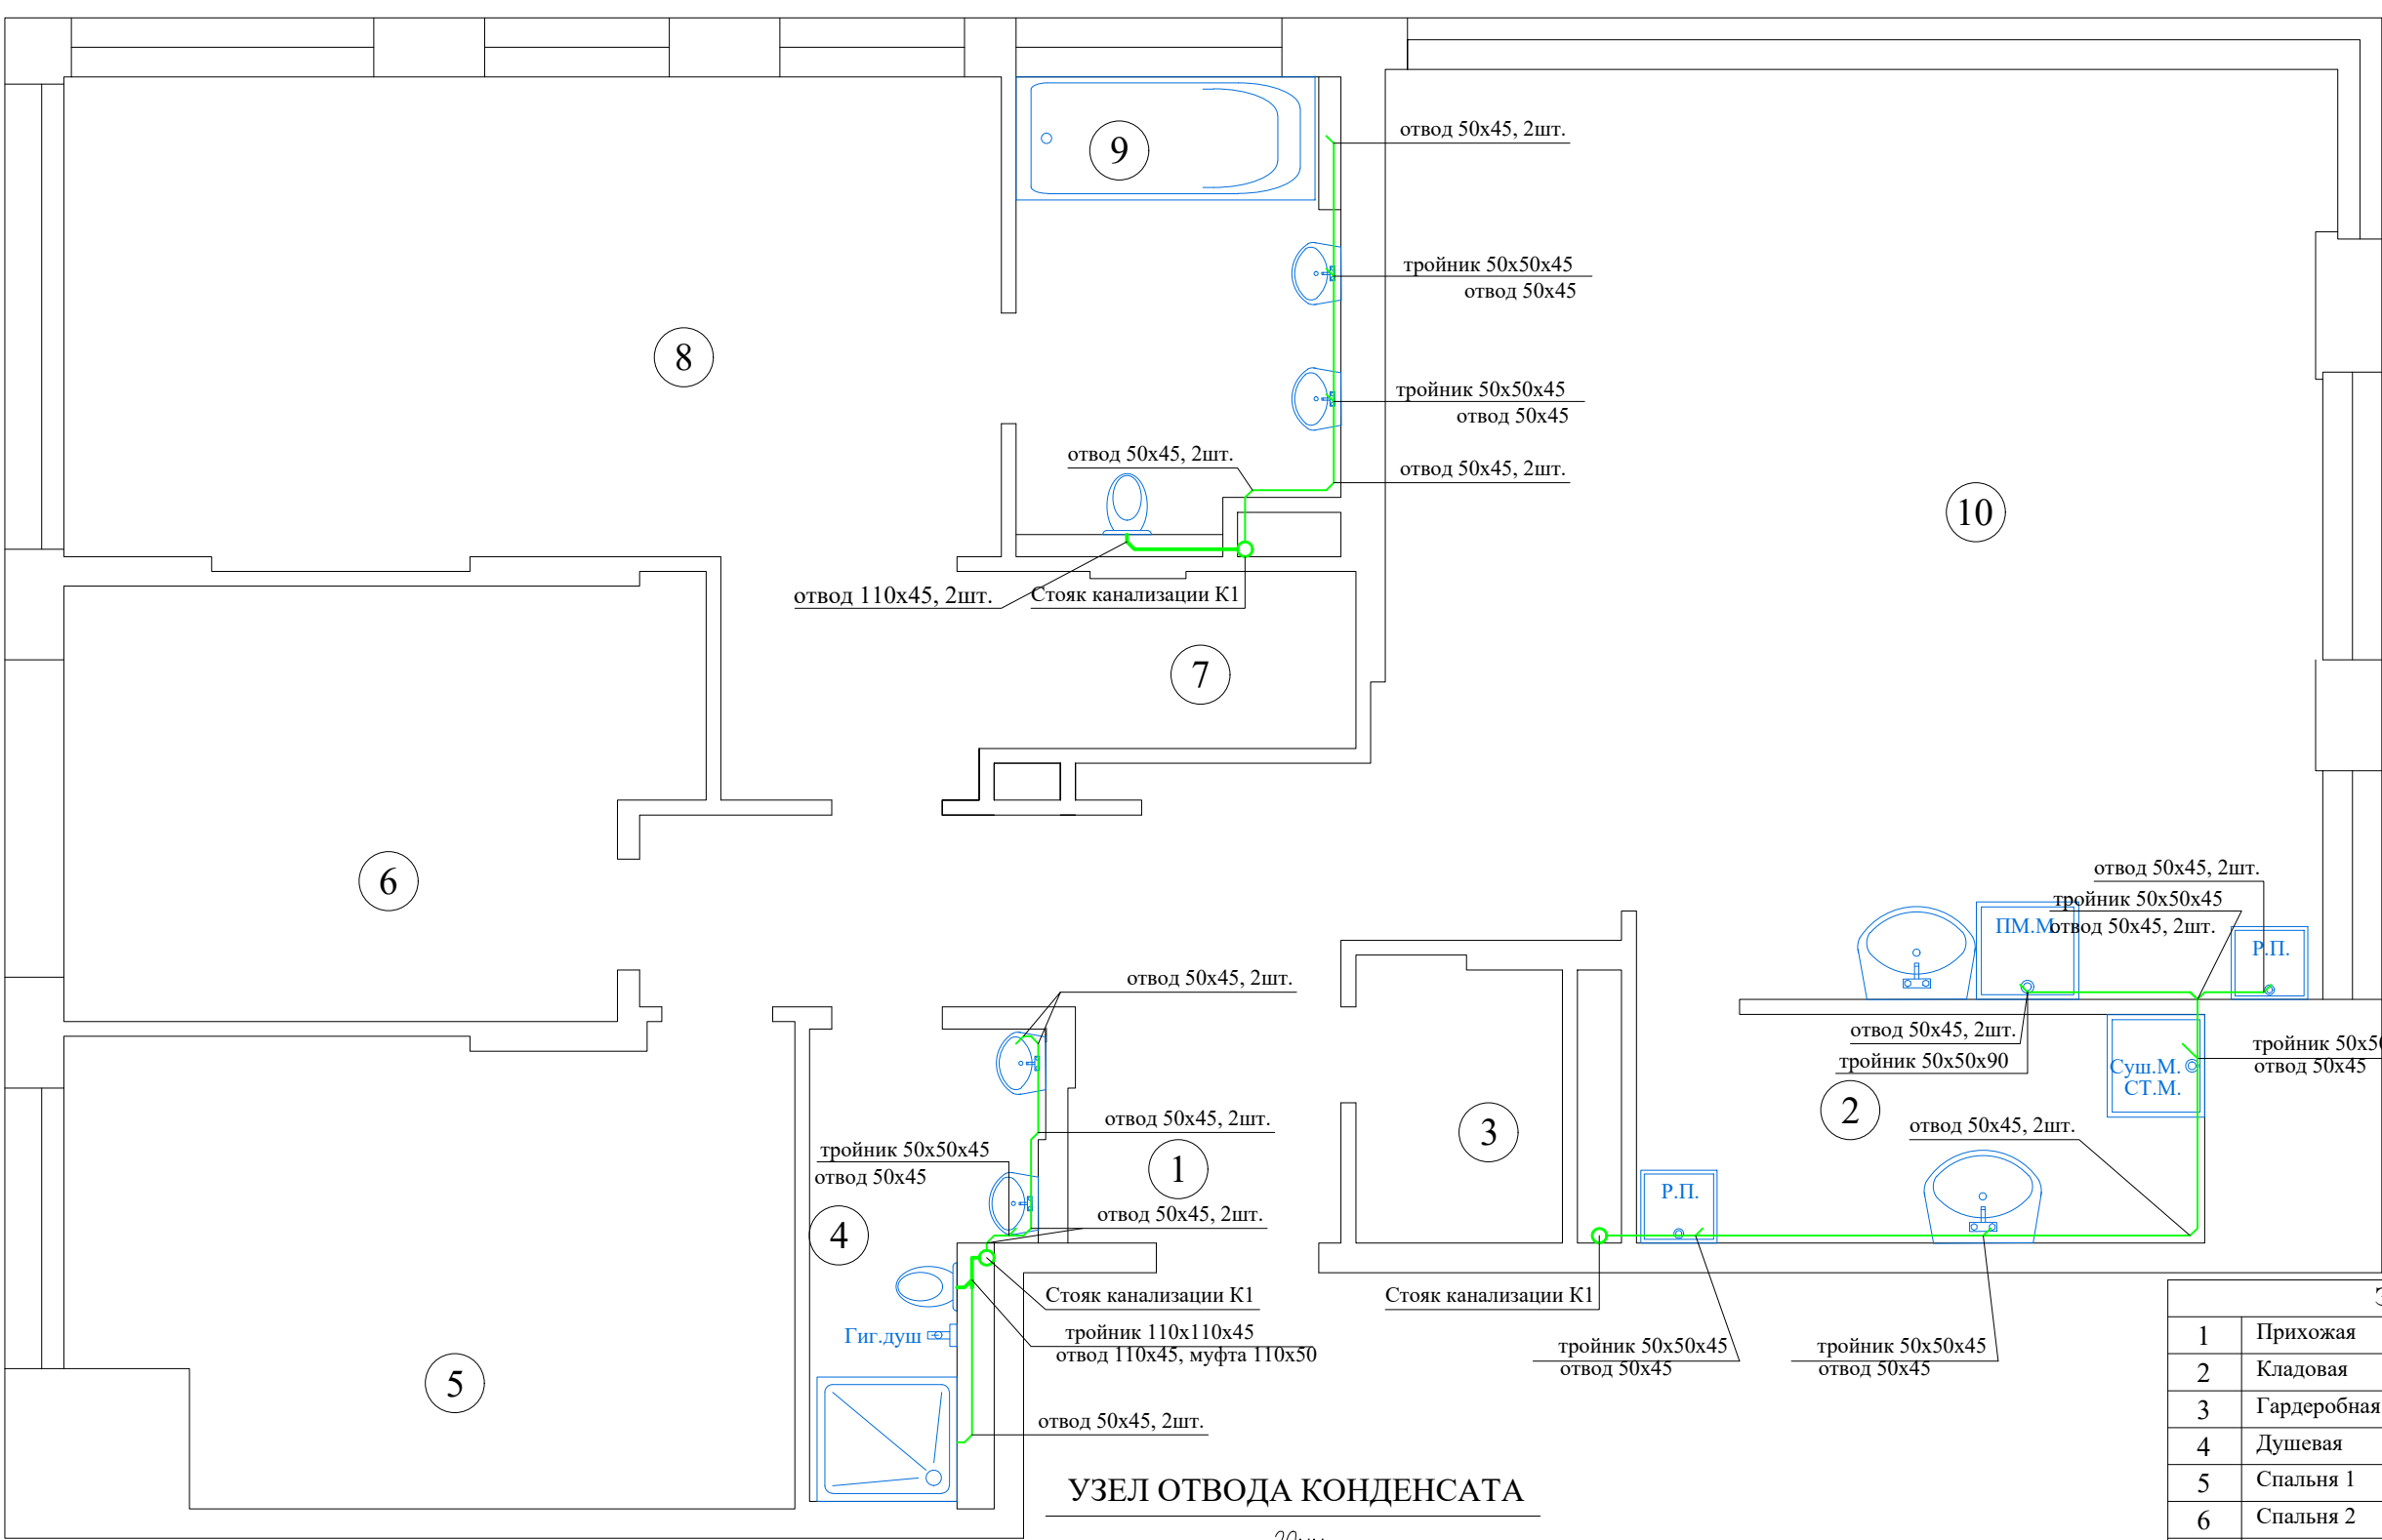

Экспликация помещений	
1	Прихожая
2	Кладовая
3	Гардеробная 1
4	Душевая
5	Спальня 1
6	Спальня 2
7	Гардеробная 2
8	Мастер спальня
9	Мастер ванная
10	Кухня гостиная

Запрещено:

- Штробление монолитных и несущих конструкций, а также вент.шахт.
- Устанавливать систему теплый пол от ГВС и отопления.

1. Предусмотреть люк для доступа к коммуникациям 400х600

Условные обозначения	
	Трубопровод канализации (K1), d.110
	Трубопровод канализации (K1), d.50

						ВК			
						Заказчик: <i>частное лицо</i>			
Изм	Кол.	Лист	№док	Подп.	Дата	Жилая квартира по адресу: <i>г.Москва, ул.Нижние Мневники, д.7, кв.Сачук Ю.Е.</i>	Стадия	Лист	Листов
ГИП		<i>Сарафонов</i>					Р	8	10
Исполн.		<i>Салюк</i>							
Проверил		<i>Загуменная</i>				Канализация. План.	ООО "СтройПроект"		