


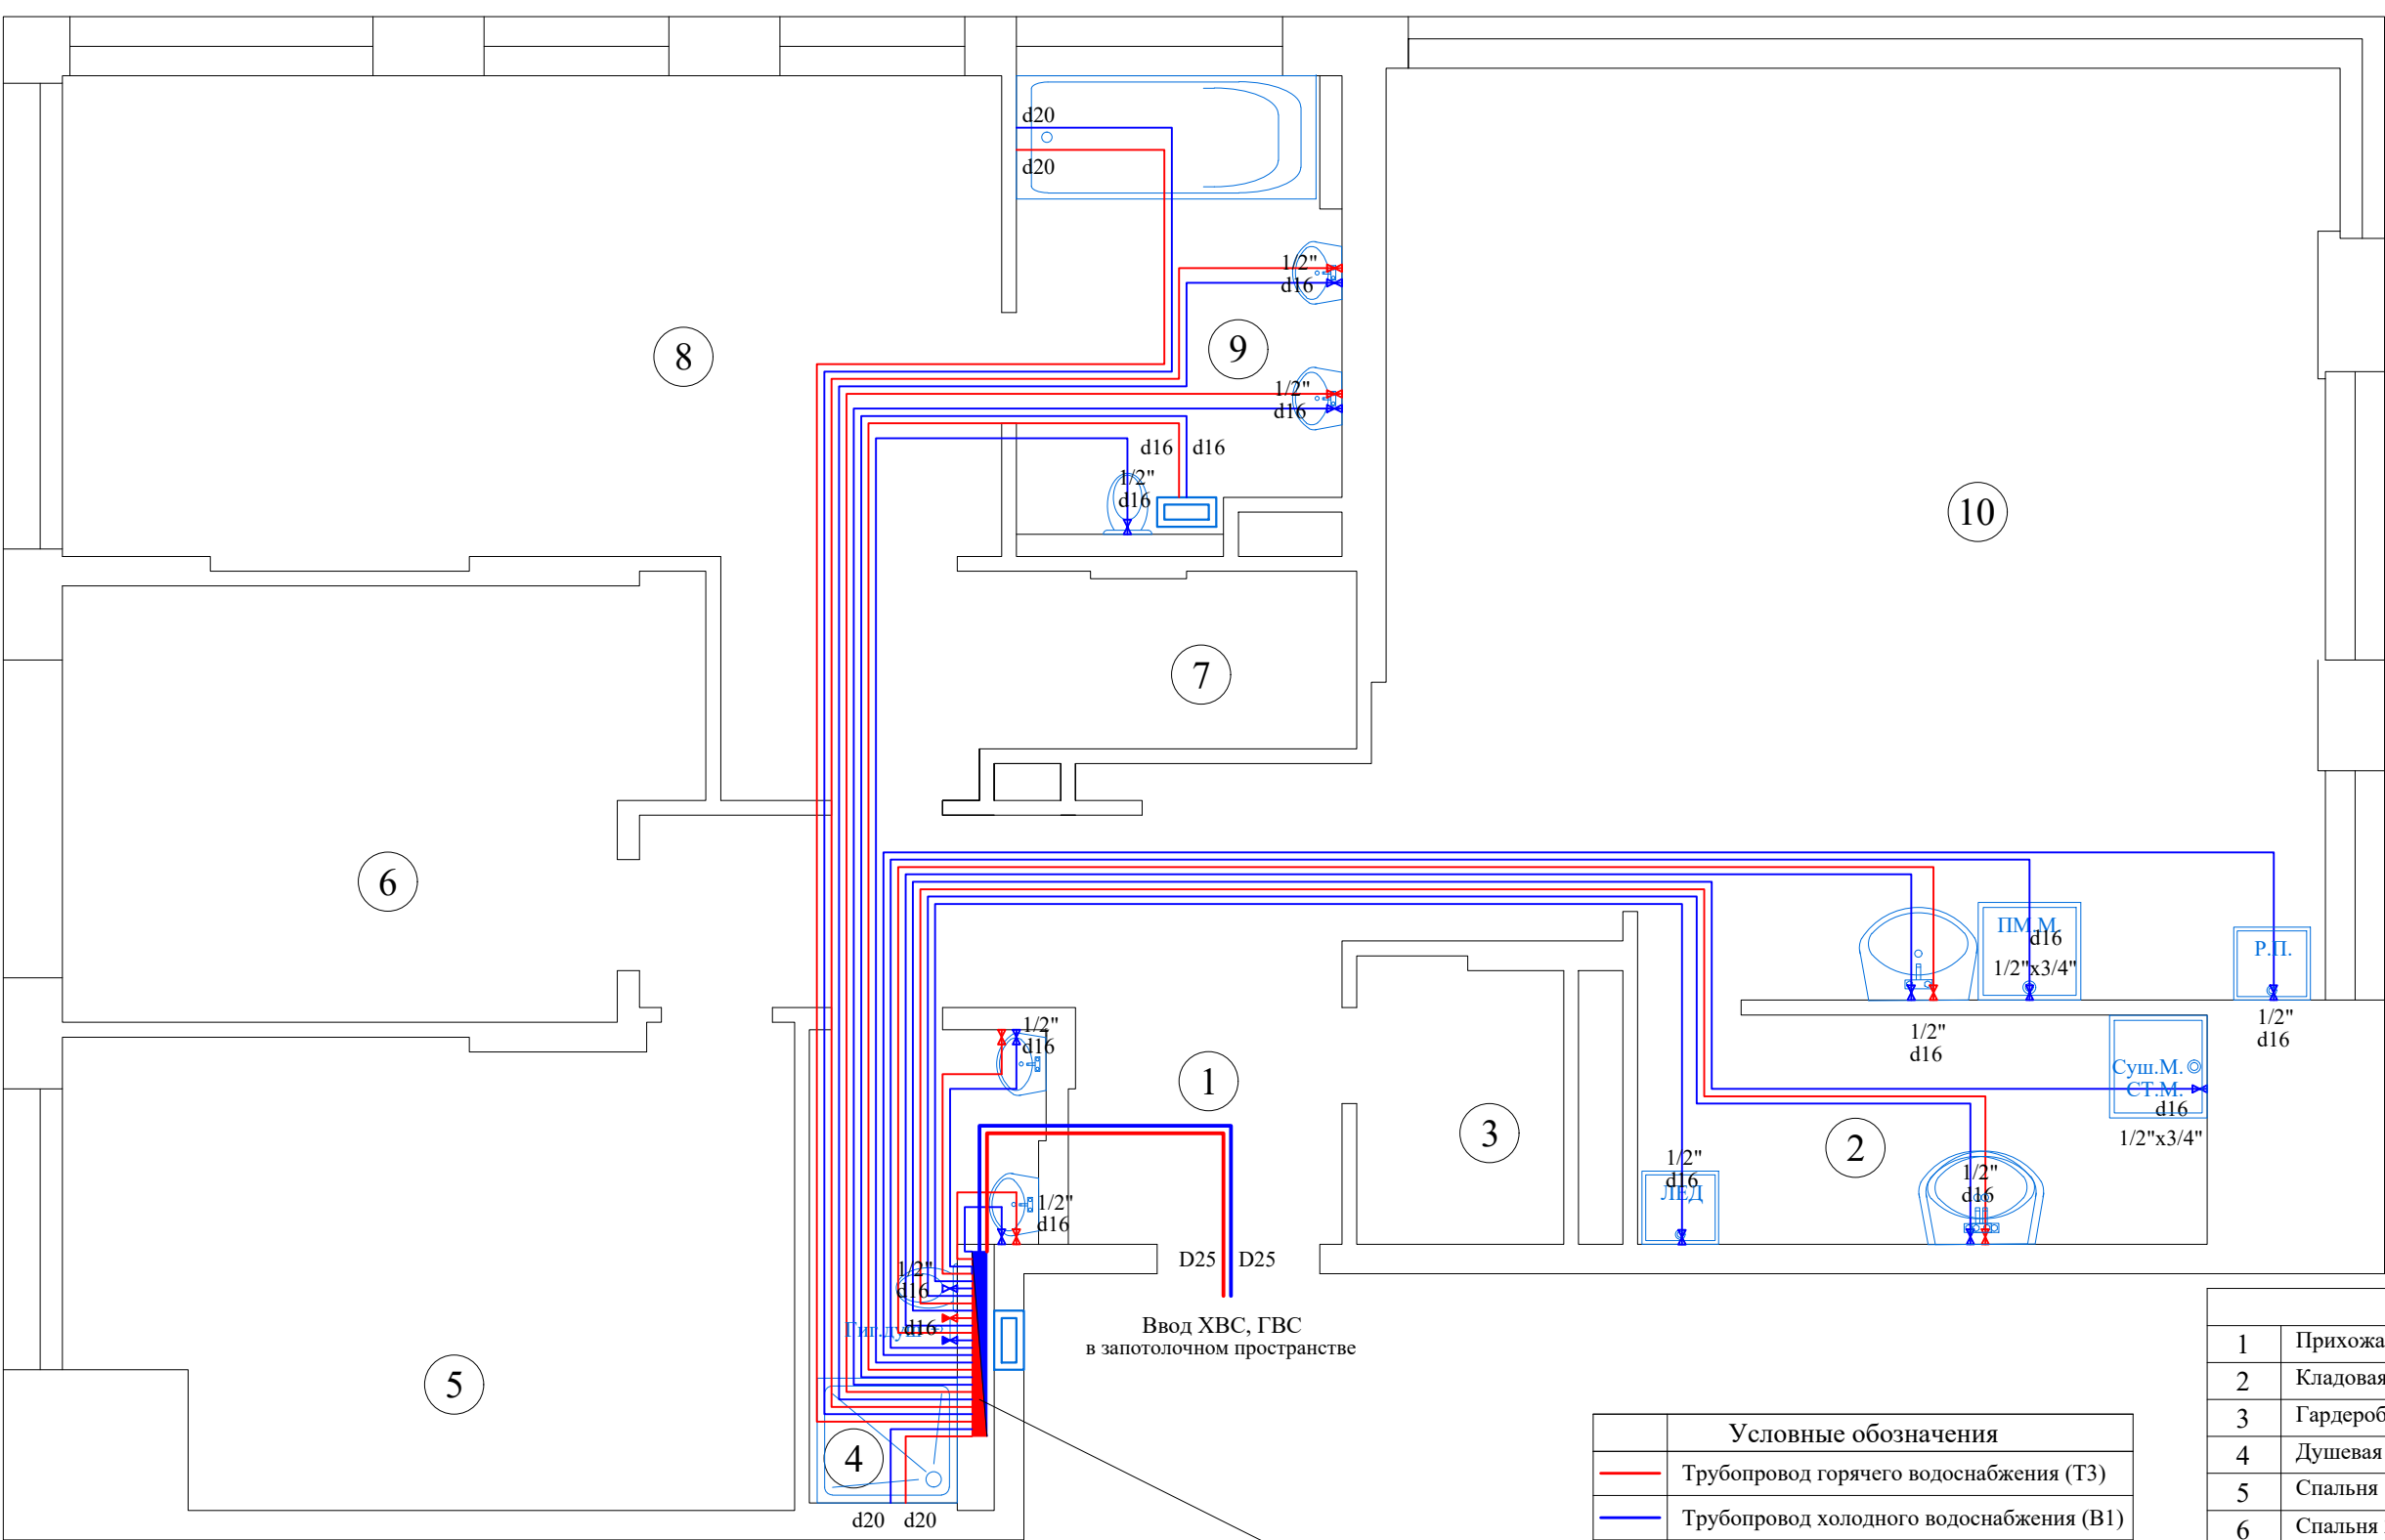

Узел 1
Гребенка ХВС, 1", 15 контуров
Гребенка ГВС, 1", 9 контуров

	Условные обозначения
—	Трубопровод горячего водоснабжения (ТЗ)
—	Трубопровод холодного водоснабжения (В1)
X	Кран шаровый
X	Обратный клапан

Экспликация помещений	
1	Прихожая
2	Кладовая
3	Гардеробная 1
4	Душевая
5	Спальня 1
6	Спальня 2
7	Гардеробная 2
8	Мастер спальня
9	Мастер ванная
10	Кухня гостиная

Предусмотреть люк для доступа к коммуникациям 400х600

- Запрещено:
- Штробление монолитных и несущих конструкций, а также вент.шахт.
 - Устанавливать систему теплый пол от ГВС и отопления.

						ВК			
						Заказчик: <u>частное лицо</u>			
Изм	Кол.	Лист	№док	Подп.	Дата	Жилая квартира по адресу: <u>г.Москва, ул.Нижние Мневники, д.7, кв.Сачук Ю.Е.</u>	Стадия	Лист	Листов
ГИП		Сарафонов					Р	5	10
Исполн.		Салюк							
Проверил		Загуменная				Водоснабжение. План.	ООО "СтройПроект"		