




МСК 392.12.25-ЭП ПРЕМИУМ			
Эскизный дизайн-проект интерьера квартиры в г. Москва ЖК "Остров", ул. Нижние Мневники д. 7			
Спальня №1 Видовые точки.			
Дизайнер интерьера №1 Александр Батеньков	Стадия	Лист	Листов
	ЭП	64	120
		Подп.	Дата
ГАП	Батеньков А.С.		
Гл. дизайнер	Власова В.А.		
Гл. проектиров.	Луныкова В.Н.		
Разработал	Ильина Е.Е.		



МСК 392.12.25-ЭП ПРЕМИУМ			
Эскизный дизайн-проект интерьера квартиры в г. Москва ЖК "Остров", ул. Нижние Мневники д. 7			
Спальня №1 Видовые точки.			
Дизайнер интерьера №1 Александр Батеньков	Стадия	Лист	Листов
	ЭП	65	120
		Подп.	Дата
ГАП	Батеньков А.С.		
Гл. дизайнер	Власова В.А.		
Гл. проектиров.	Луныкова В.Н.		
Разработал	Ильина Е.Е.		

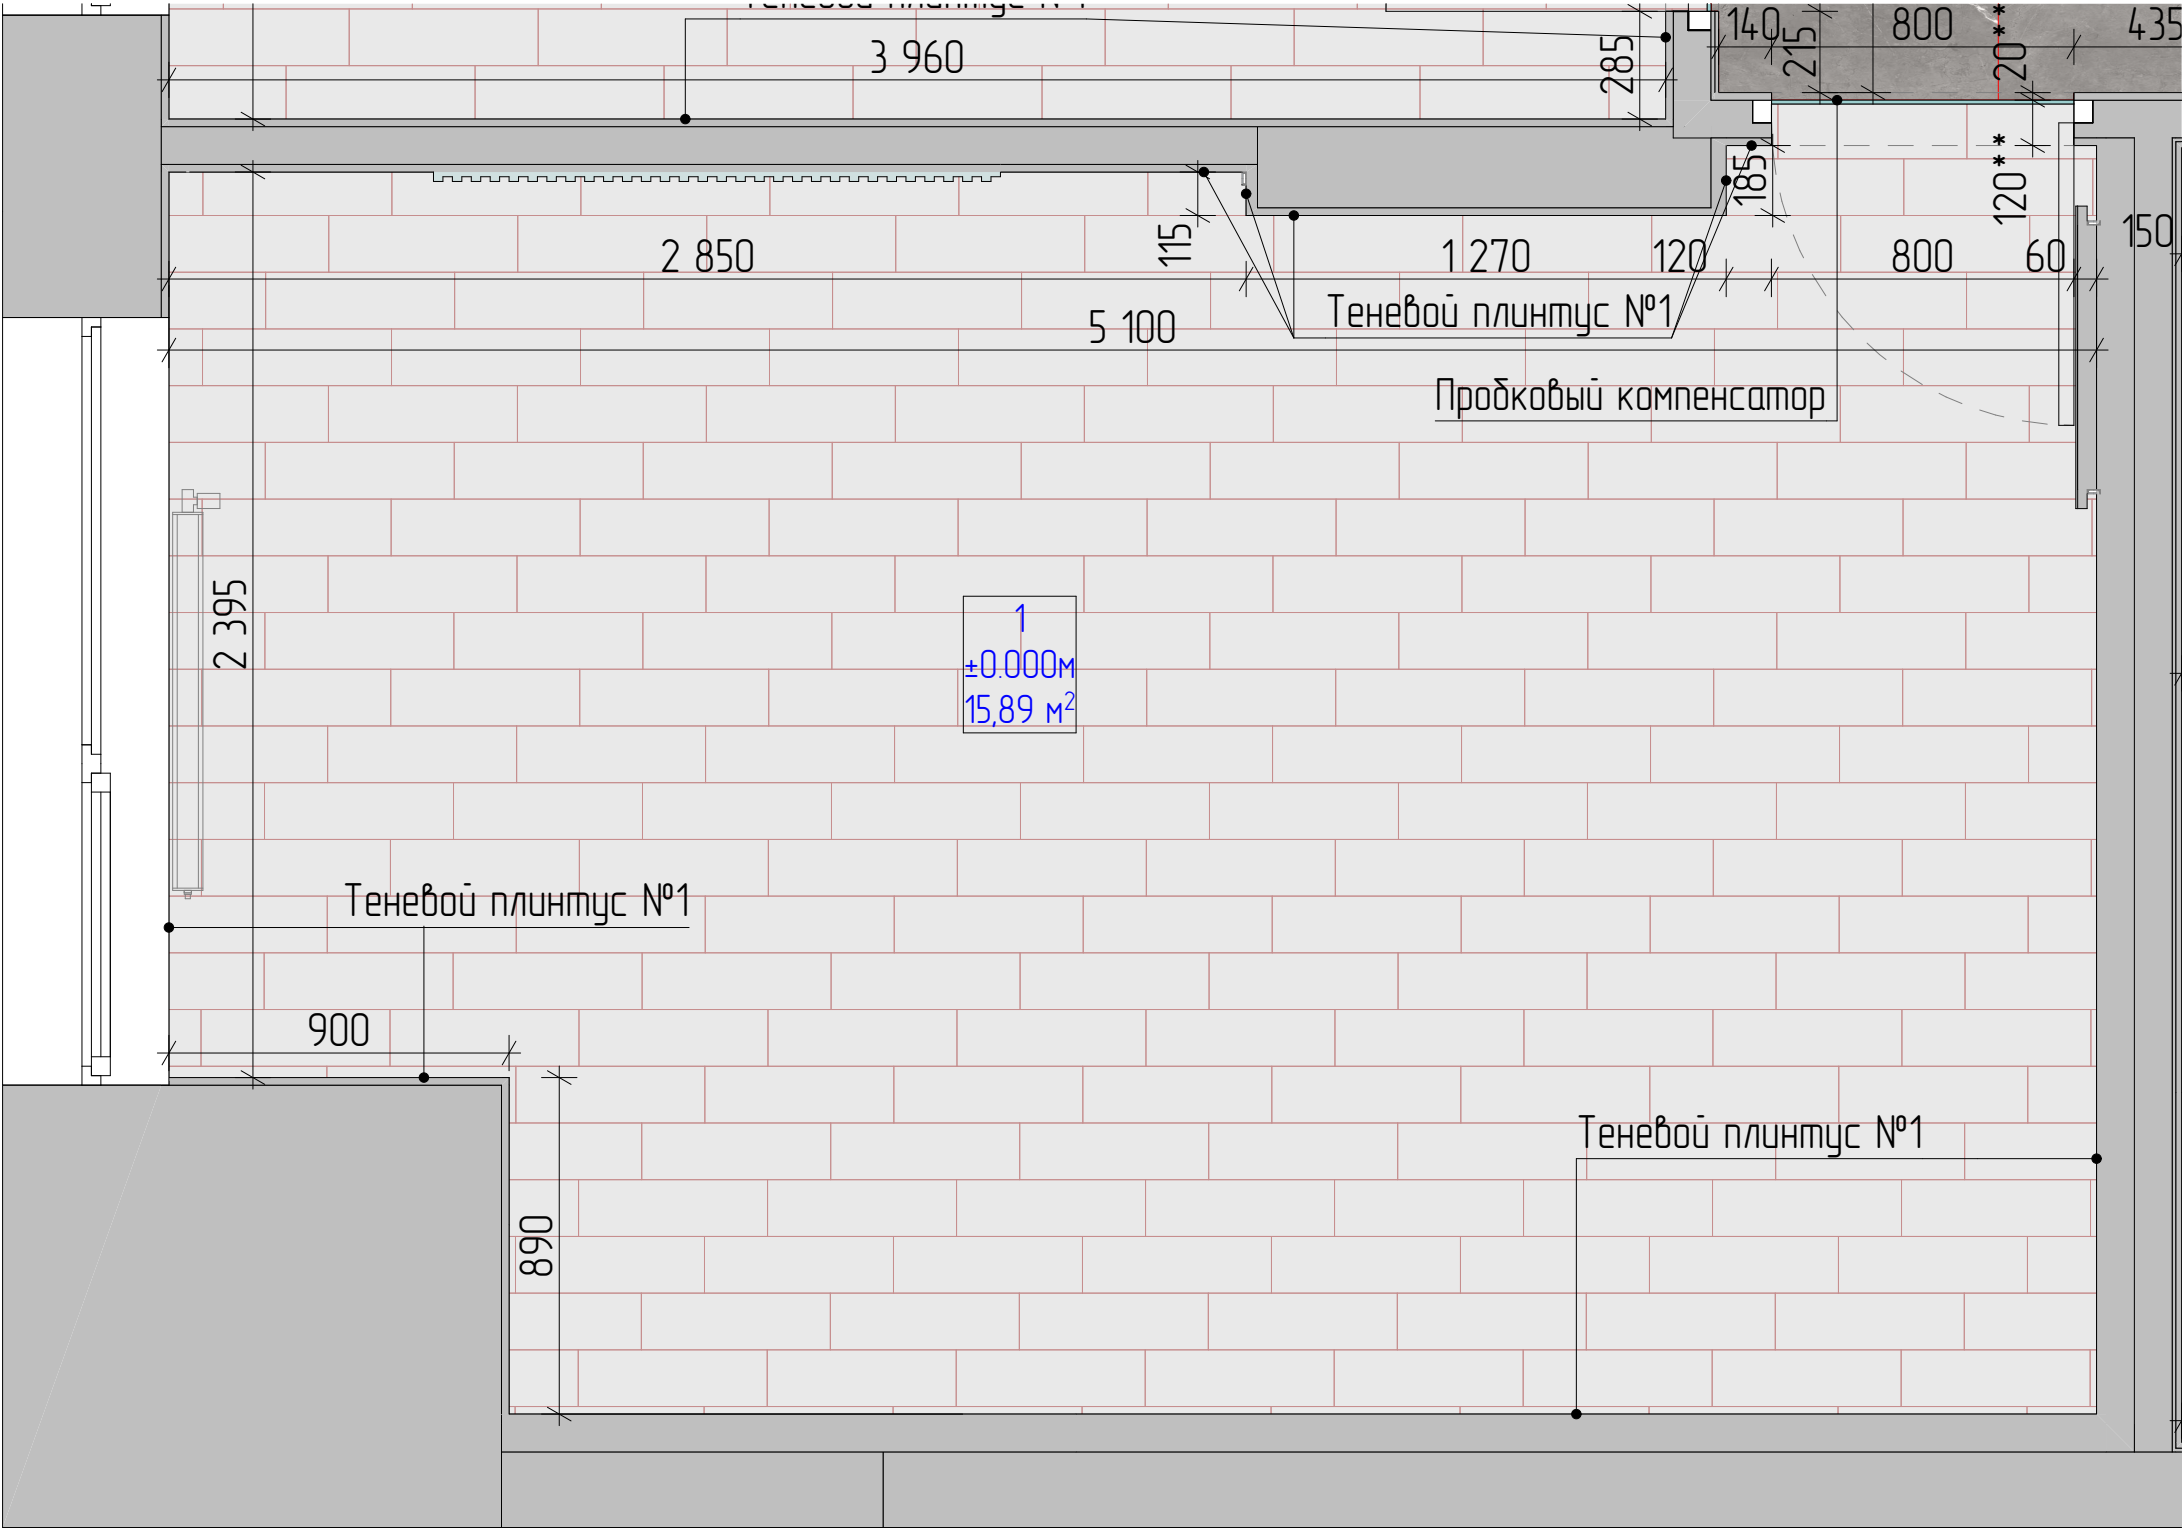

Условные обозначения:

Направление и начало укладки

Пробковый компенсатор

1

Покрывтие №01. Паркет. Изготовитель: Lab Arte, кол-я: Angle Дуб Натур, размер: 500x150 мм, точный артикул и производителя уточнить при выборе образца, толщину уточнить при покупке.

Примечания:

1. * – размеры уточнить по месту после выполнения черновых отделочных работ.


2. За отметку ±0,000 принят уровень чистого пола.

3. При монтаже напольных покрытий уточнить необходимость устройства дверных проемов с порогом.

1. * – размеры уточнить по месту после выполнения черновых отделочных работ и установки дверей со скрытой коробкой.

2. ** –размер уточнить по месту в зависимости от точного расположения полотна двери, стыковка двух разных напольных покрытий должна проходить точно по центру вдоль дверного полотна.


МСК 392.12.25–ЭП ПРЕМИУМ			
Эскизный дизайн–проект интерьера квартиры в г. Москва ЖК "Остров", ул. Нижние Мневники д. 7			
Спальня №1.План отделки пола.			
Дизайнер интерьера №1 Александр Батеньков	Стадия	Лист	Листов
	ЭП	66	120
		Подп.	Дата
ГАП	Батеньков А.С.		
Гл. дизайнер	Власова В.А.		
Гл. проектиров.	Луныкова В.Н.		
Разработал	Ильина Е.Е.		

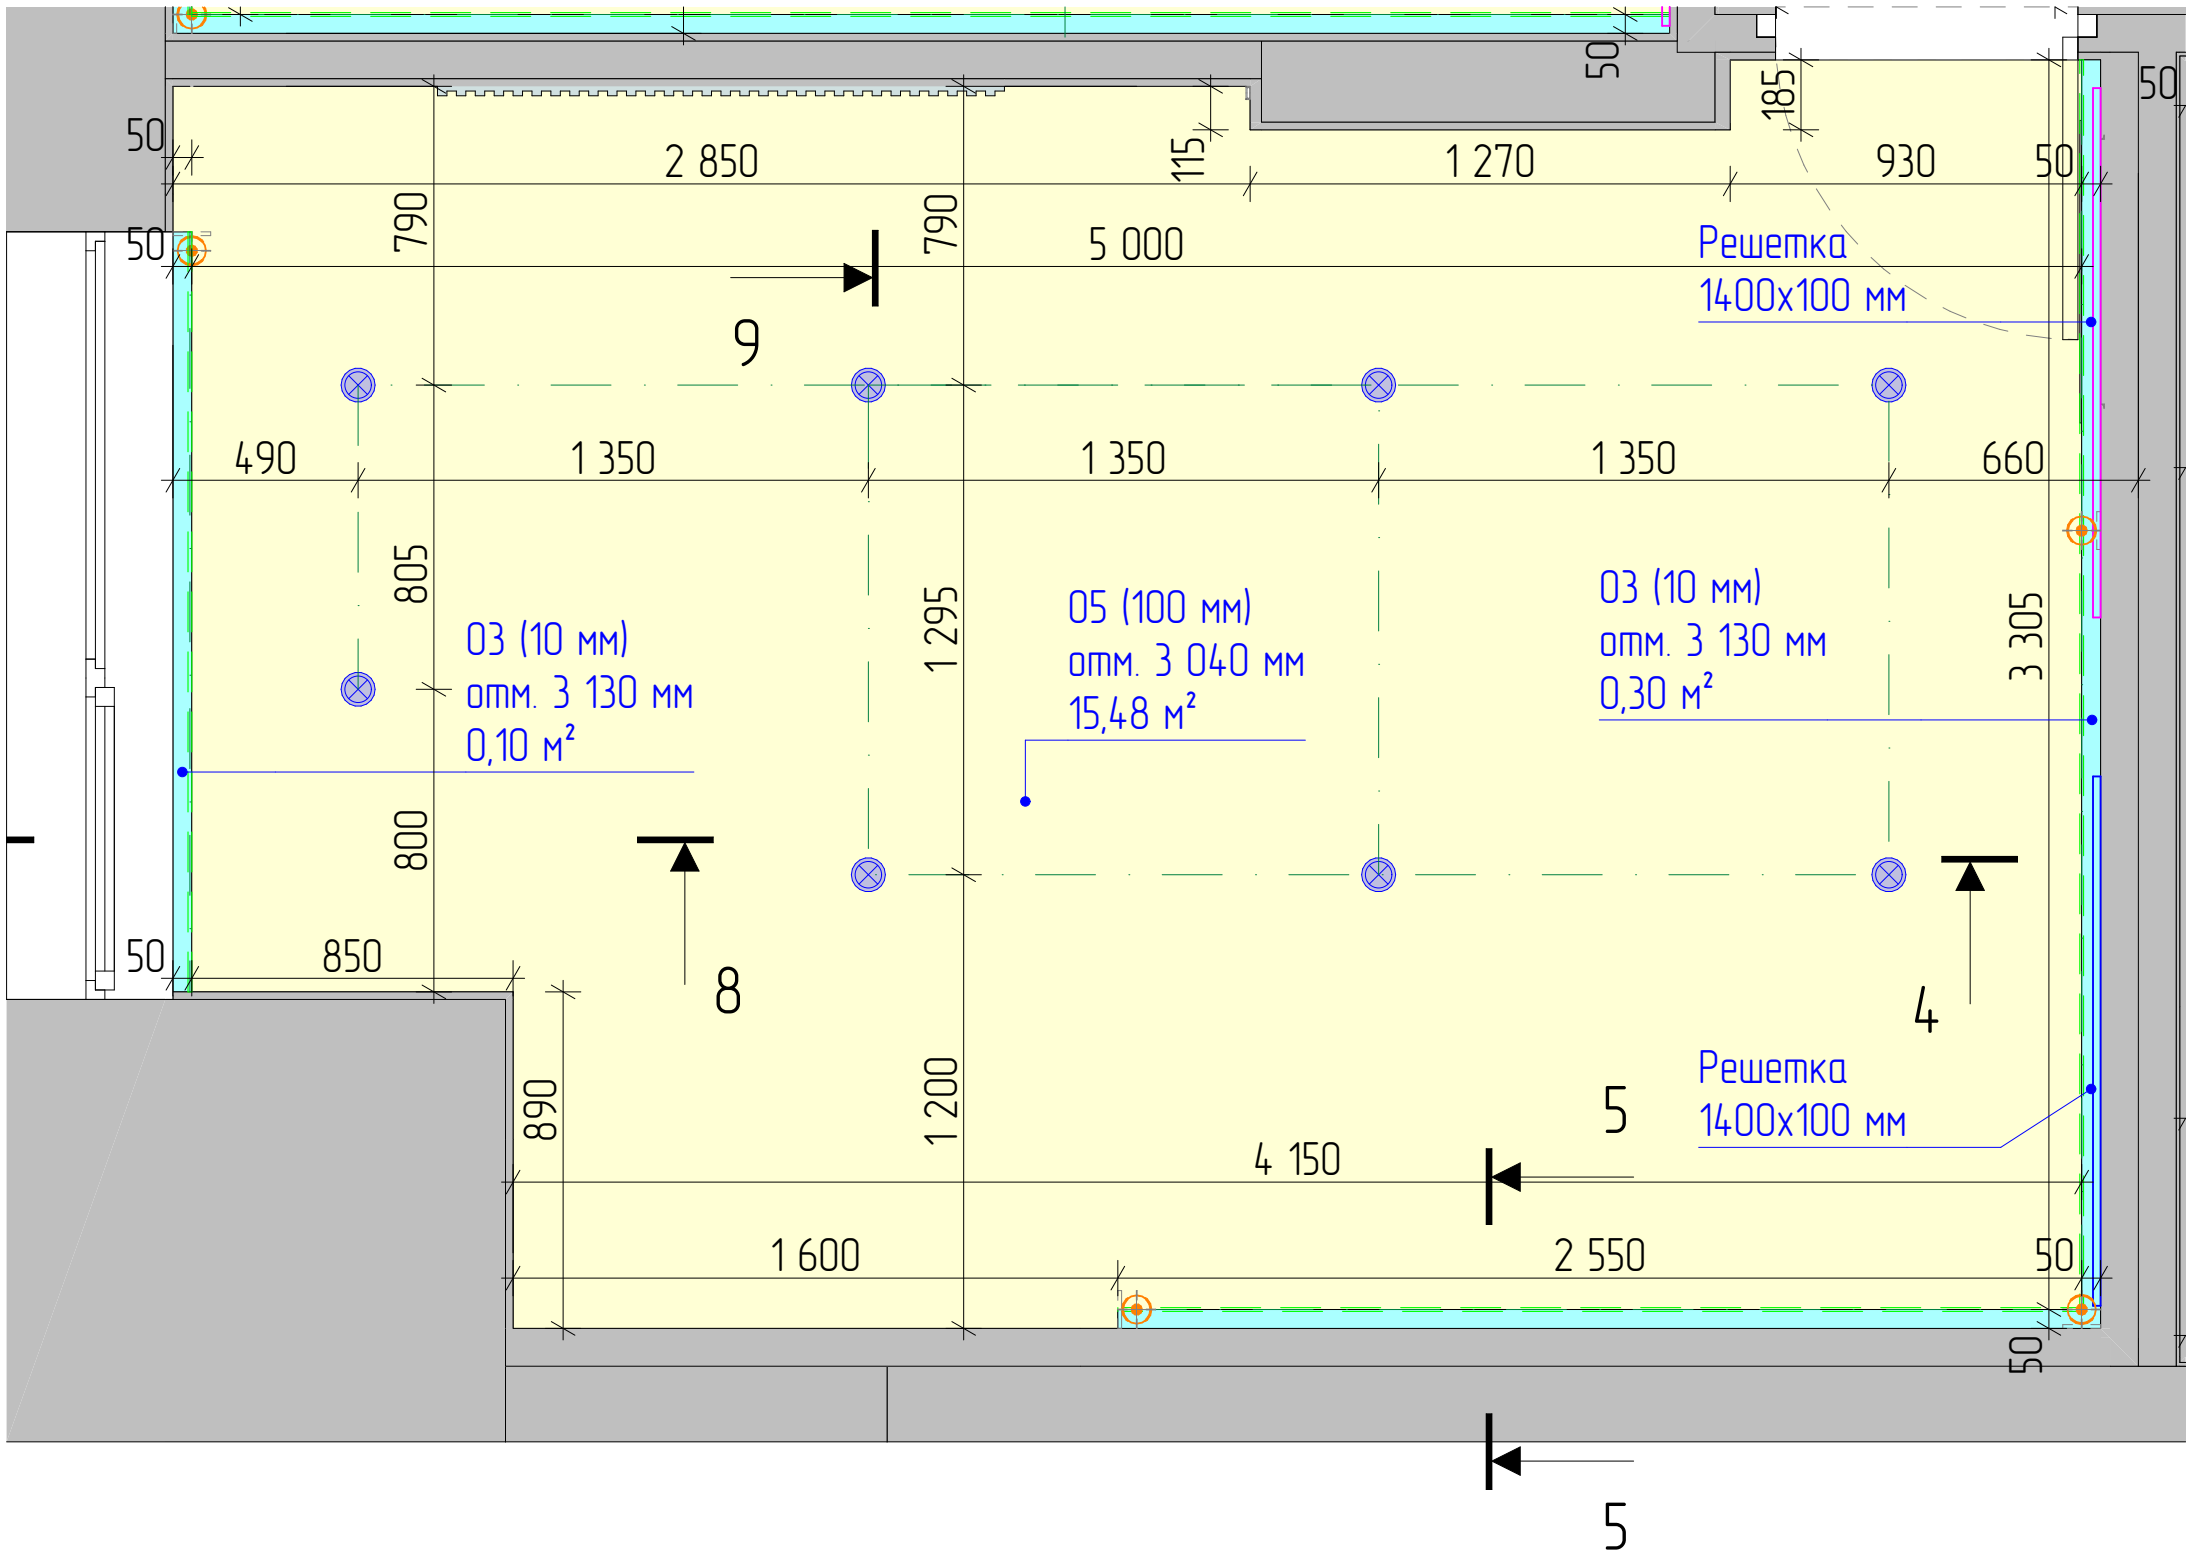

- Условные обозначения:
- ⊕ Вывод 220V
 - ⊕ Вывод электрокабеля для светодиодной ленты
 - ⊗ Светильник точечный встраиваемый
 - Светодиодная лента
- Примечания:
- * - размеры уточнить по месту после выполнения черновых работ.
 - Выполнить уровни потолка из влагостойкого ГКЛ для предотвращения деформации потолка при затоплении.
 - Высоту уровней потолка отсчитывать от существующей ж/б плиты перекрытия помещения.
 - Шумоизоляцию разработать со специалистами, уточнить состав и толщину слоев шумоизоляционных материалов. Уточнить необходимость устройства с заказчиком.

Условные потолки				
№	Обозначение	Опуск	Примечания	Площадь м2
03		10	Выровнять и оштукатурить существующий потолок. Окрасить в цвет выбранного образца (белый) по армирующему материалу (стеклохолст "паутинка"). Размер ниши уточнить.	15,48
05		100	Потолок ГКЛ/В. Окрасить в цвет выбранного образца (белый) по армирующему материалу (стеклохолст "паутинка").	0,40

МСК 392.12.25-ЭП ПРЕМИУМ			
Эскизный дизайн-проект интерьера квартиры в г. Москва ЖК "Остров", ул. Нижние Мневники д. 7			
Спальня №1. План отделки потолка.			
Дизайнер интерьера №1  Александр Батеньков	Стадия	Лист	Листов
	ЭП	67	120
		Подп.	Дата
ГАП	Батеньков А.С.		
Гл. дизайнер	Власова В.А.		
Гл. проектиров.	Луныкова В.Н.		
Разработал	Ильина Е.Е.		

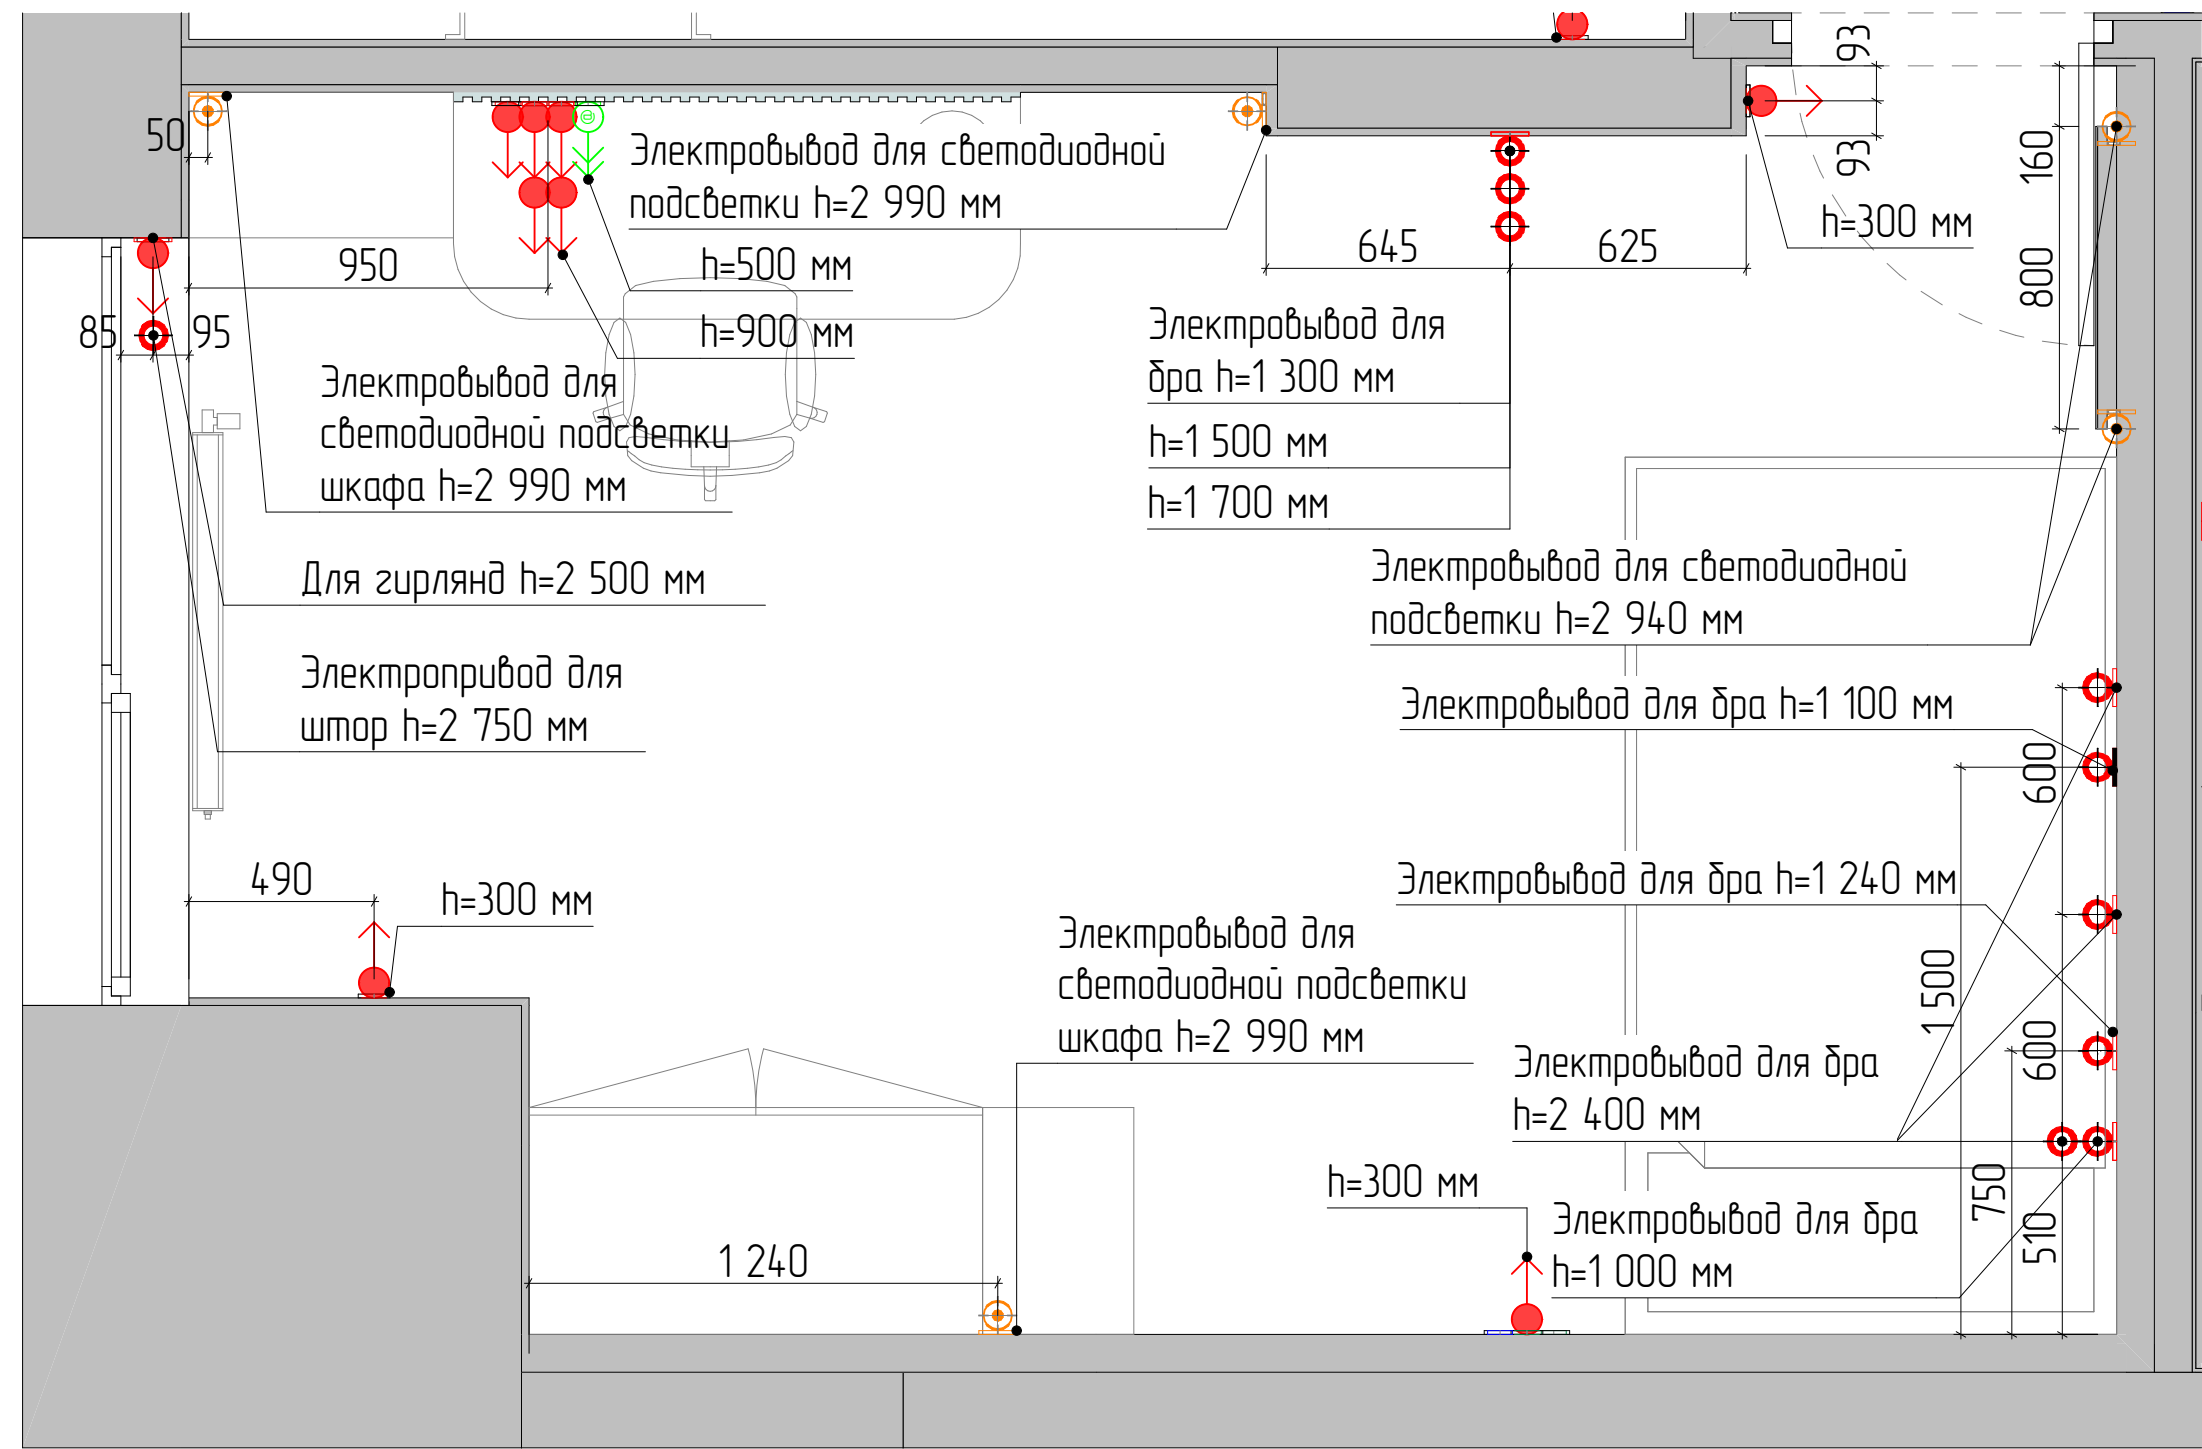

Условные обозначения:

- Разетка 220V
- Вывод электрокабеля для светодиодной ленты
- Вывод электрокабеля для варочной поверхности
- Вывод 220V


Примечания:

- * – размеры уточнить по месту.
- Розетки располагать от уровня чистого пола на высоте 0,300 м. Исключения указаны на чертеже.
- Размещение всех выводов и розеток согласовать со специалистами «Умный дом».
- Размеры и характеристики радиаторов отопления согласовать со специалистами, предусмотреть терморегуляторы.
- Датчики пожарной и охранной сигнализации и электровыводы для них разместить совместно со специалистами, предварительно вызвав их на объект.
- Размещение розеток и электровыводов по высоте см. на развертках стен.

МСК 392.12.25-ЭП ПРЕМИУМ

Эскизный дизайн-проект интерьера квартиры в г. Москва ЖК "Остров", ул. Нижние Мневники д. 7


Спальня №1 План размещения электрооборудования.

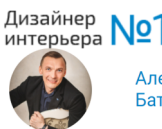

Александр Батеньков

Стадия	Лист	Листов
ЭП	68	120
	Подп.	Дата

ГАП	Батеньков А.С.		
Гл. дизайнер	Власова В.А.		
Гл. проектиров.	Луныкова В.Н.		
Разработал	Ильина Е.Е.		


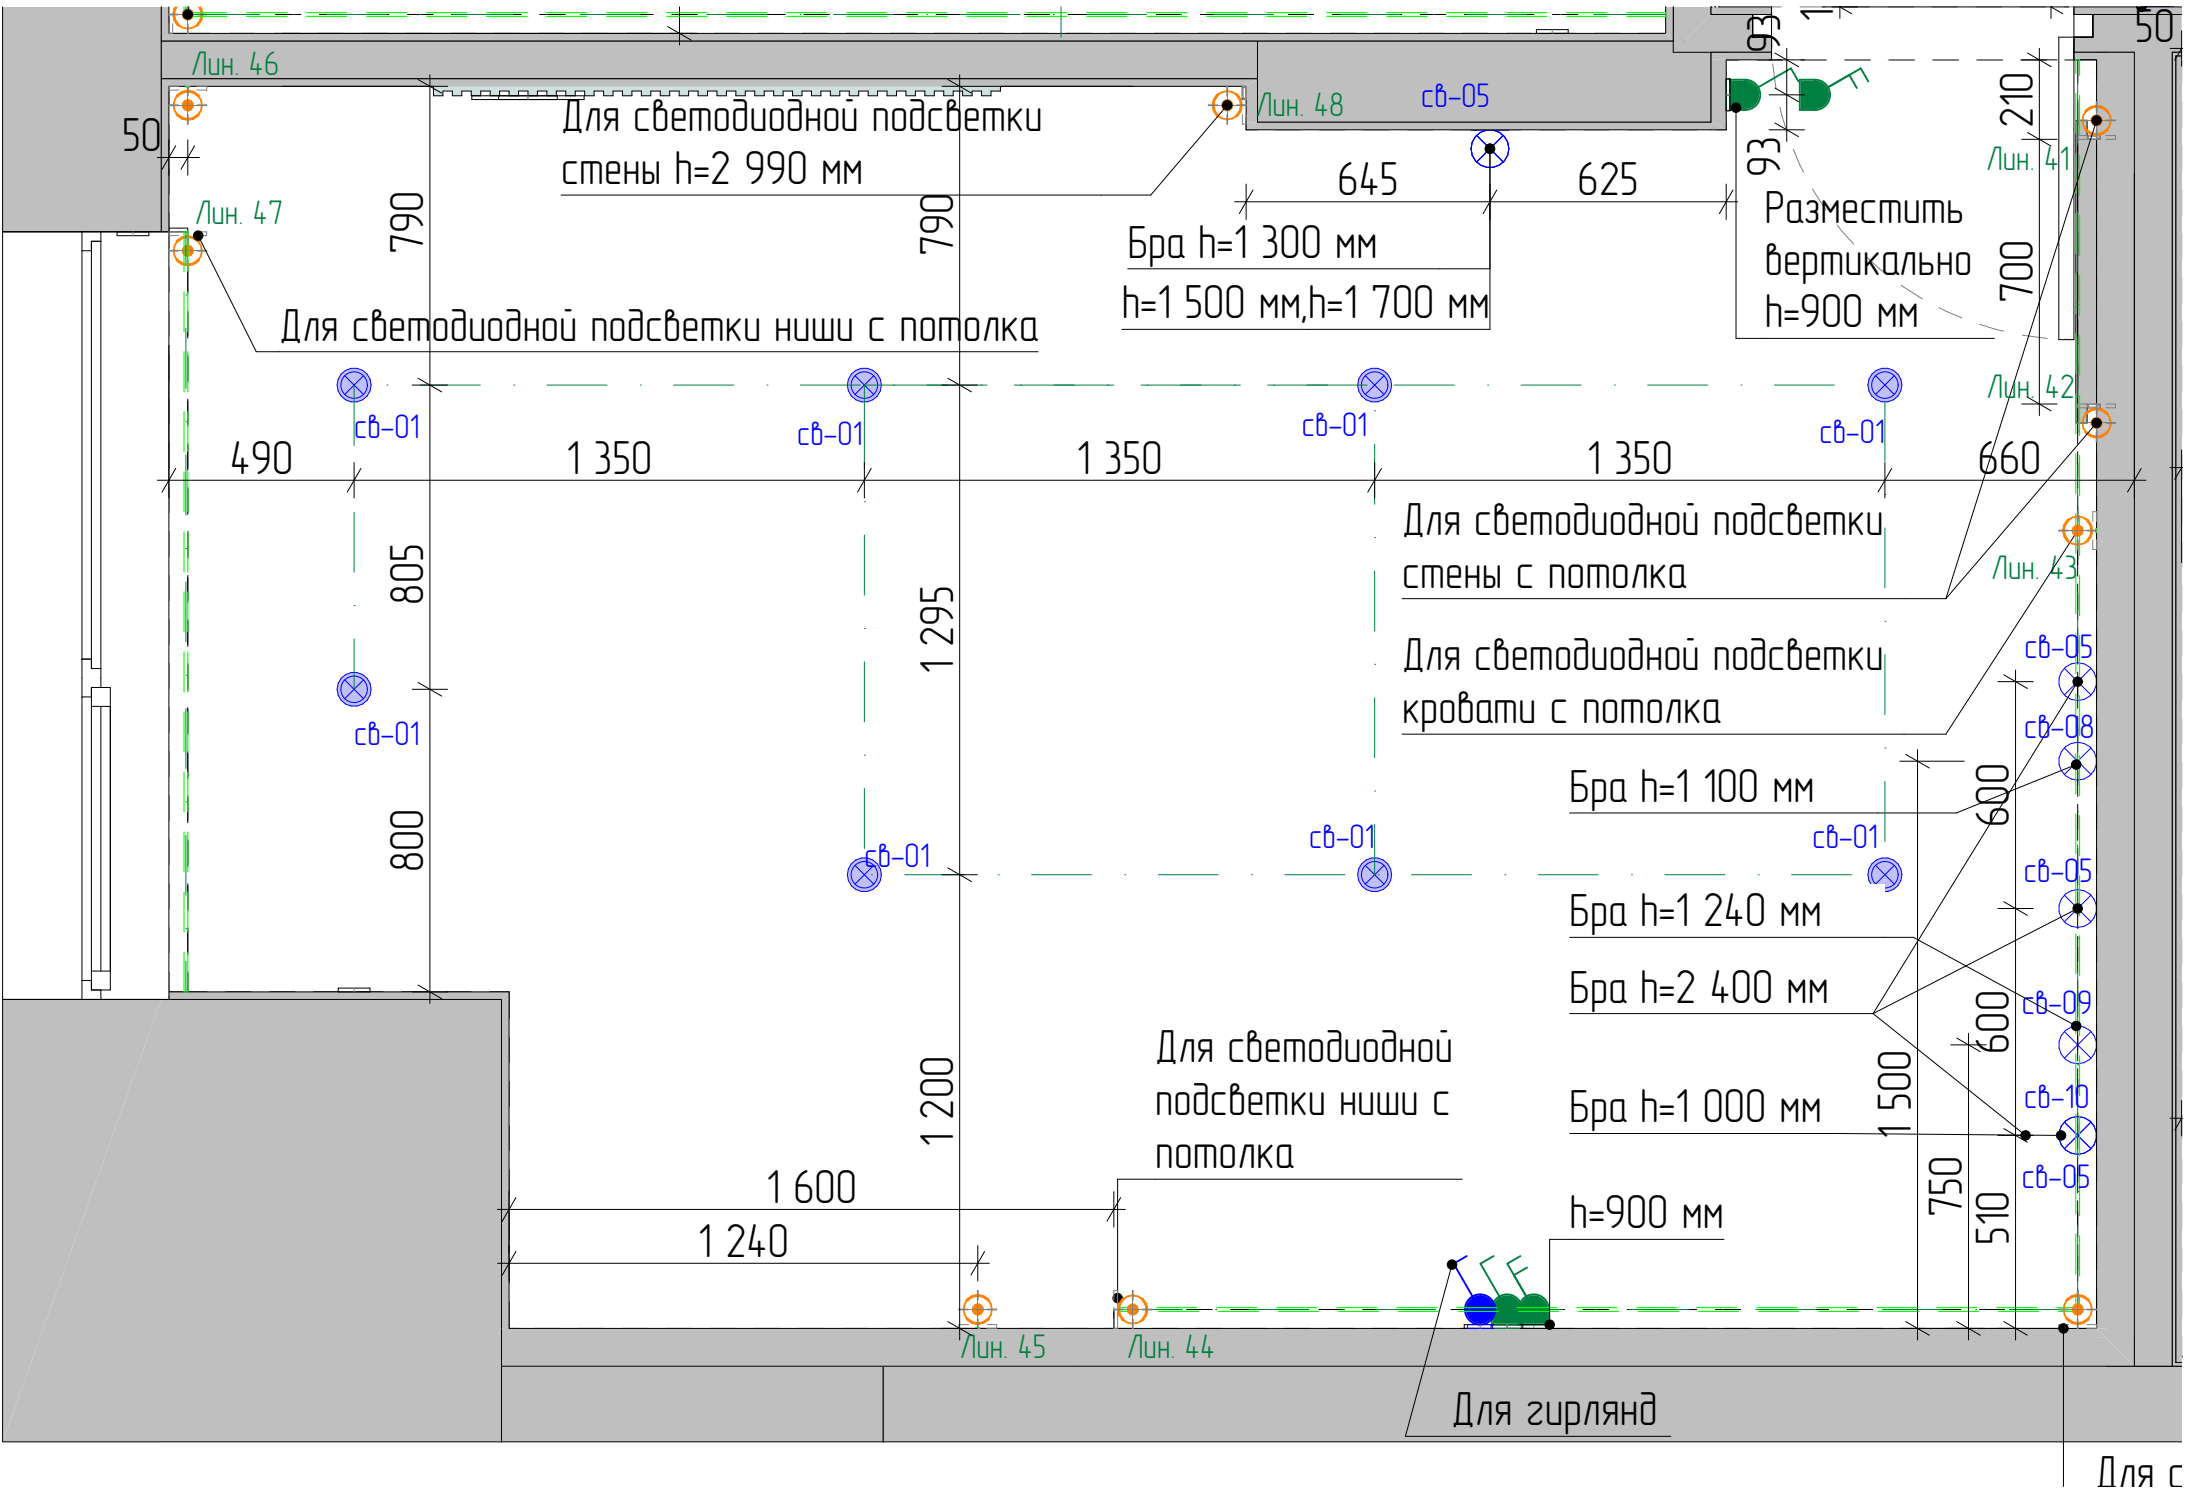


- Условные обозначения:
- Вывод 220V
 - Вывод электрокабеля для светодиодной ленты
 - Выключатель одноклавишный
 - Переключатель двухклавишный
 - Светильник точечный встраиваемый
 - Светодиодная лента

Примечания:

- * – размеры уточнить по месту.
- Выключатели располагать от уровня чистого пола на высоте 0,900 м. Исключения указаны на чертеже.
- Светильники, встроены в мебель, согласовать с изготовителями мебели.

МСК 392.12.25-ЭП ПРЕМИУМ			
Эскизный дизайн-проект интерьера квартиры в г. Москва ЖК "Остров", ул. Нижние Мневники д. 7			
Спальня №1 План размещения освещения и выключателей.			
Дизайнер интерьера №1  Александр Батеньков	Стадия	Лист	Листов
	ЭП	69	120
		Подп.	Дата
ГАП	Батеньков А.С.		
Гл. дизайнер	Власова В.А.		
Гл. проектиров.	Луныкова В.Н.		
Разработал	Ильина Е.Е.		

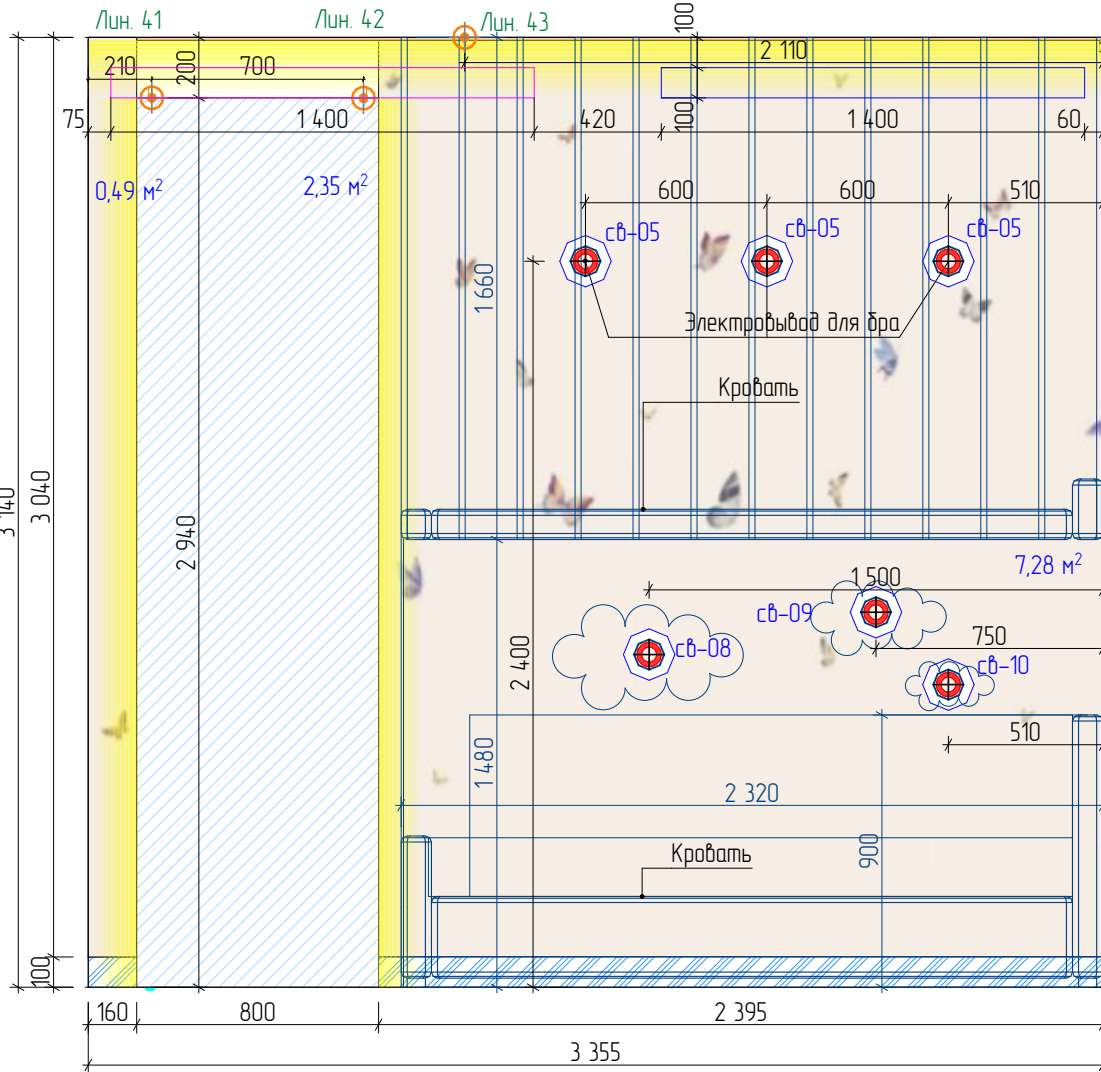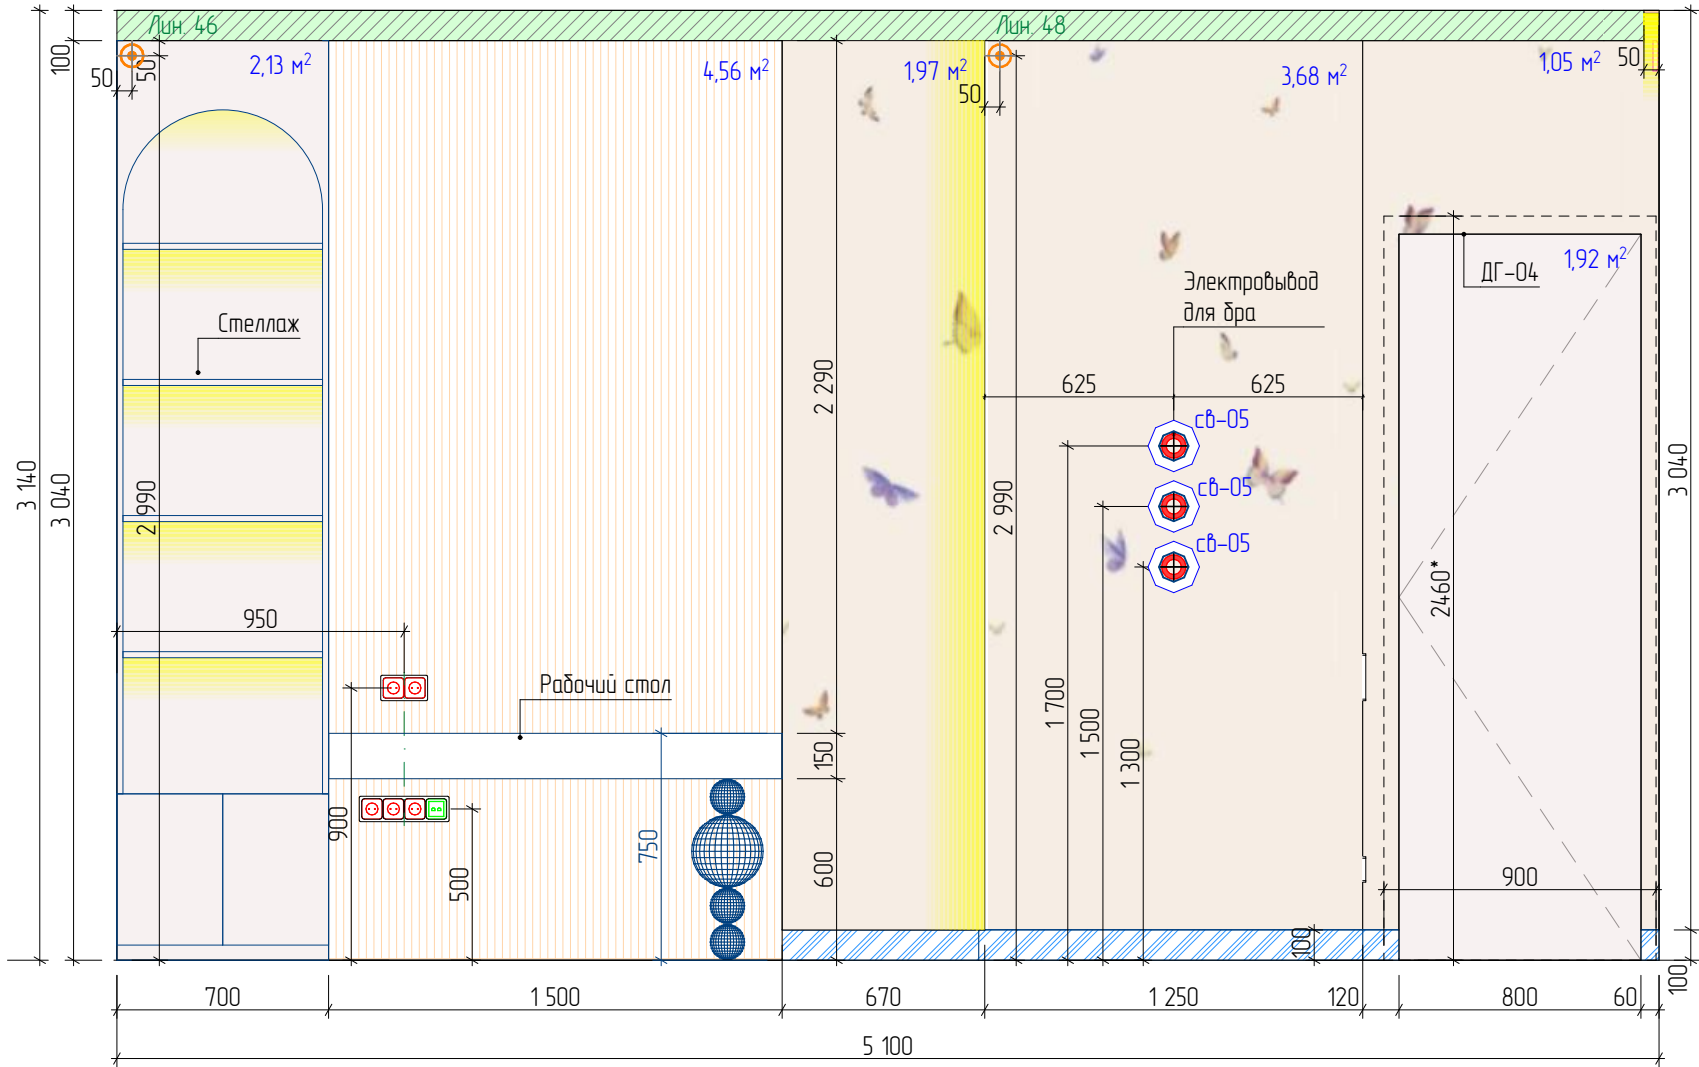








Условные обозначения:

- Обои №1. Обои ручной работы. Изготовитель: fresq, кол-я: CLASSIC, арт.: EN.01. Размер, цвет и фактура при выборе образца.
- Плинтус №1. Теневой плинтус скрытого монтажа с МДФ вставкой. Теневой зазор от пола 100 мм. Цвет при выборе образца (в цвет стен).
- Монтаж конструкций из ГКВЛ
- Зеркало №2. Разработать со специалистами (стандарт*) размеры и резка по чертежу.
- Покраска №1. Выполнить по подготовленной поверхности (стеклохолст*). Цвет при выборе образца (бежевый*).
- МДФ панель №3. 3Д панель. Цвет и фактура при выборе образца (в цвет мебели*).
- Розетка 220 V
- Интернет-розетка двойная
- Выход 220 V
- Выход электрокабеля для светодиодной ленты

Примечания:

- *- размеры уточнить по месту после выполнения черновых отделочных работ.
- Розетки располагать от уровня чистого пола на высоте 300 мм. Исключения указаны на чертеже.
- Размещение вывода 220 V для кондиционеров согласовать со специалистами.
- Цвет окрашивания плинтуса уточнить после согласования образца.
- Высоту проемов выполнить 2460 мм от уровня чистого пола. Уточнить после подбора и согласования модели дверей.
- Резку зеркала решить по месту авторским надзором.
- Плинтус подрезать по месту в местах стыковки с дверями и мебелью.
- Внутреннее наполнение мебели разработать со специалистами.
- Серым/синим цветом показаны размеры мебели. Мебель разработать со специалистами, размеры уточнить после выполнения чистовой отделки.

МСК 392.12.25-ЭП ПРЕМИУМ			
Эскизный дизайн-проект интерьера квартиры в г. Москва ЖК "Остров", ул. Нижние Мневники д. 7			
Спальня №1Развертки стен Д-01, Д-02.			
Дизайнер интерьера №1 Александр Батеньков	Стадия	Лист	Листов
	ЭП	70	120
		Подп.	Дата
ГАП	Батеньков А.С.		
Гл. дизайнер	Власова В.А.		
Гл. проектиров.	Луныкова В.Н.		
Разработал	Ильина Е.Е.		

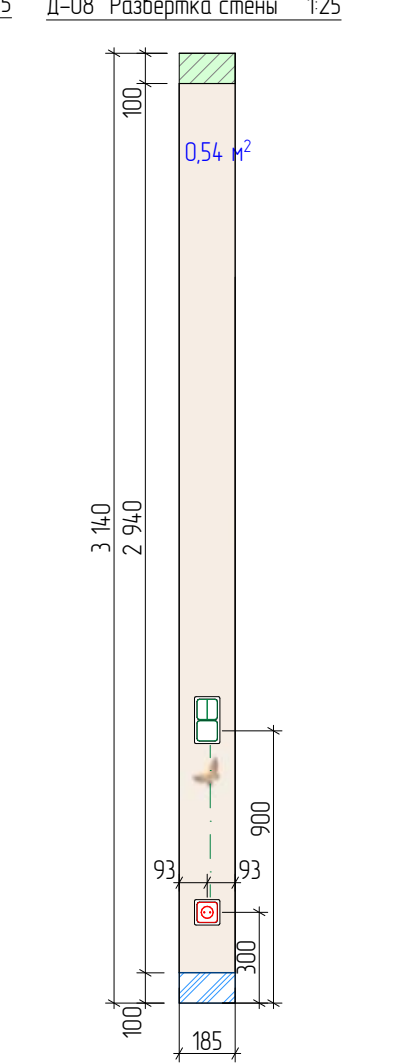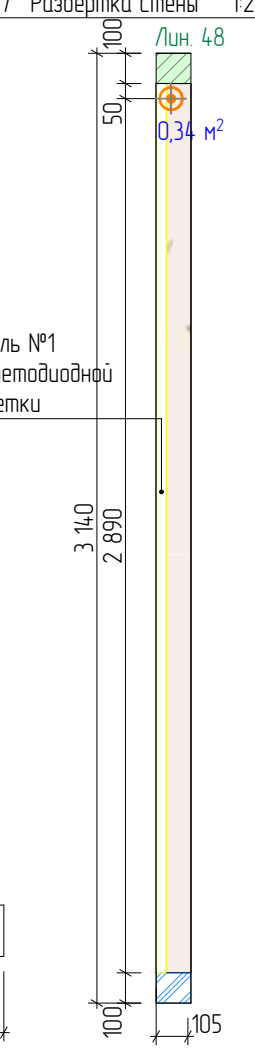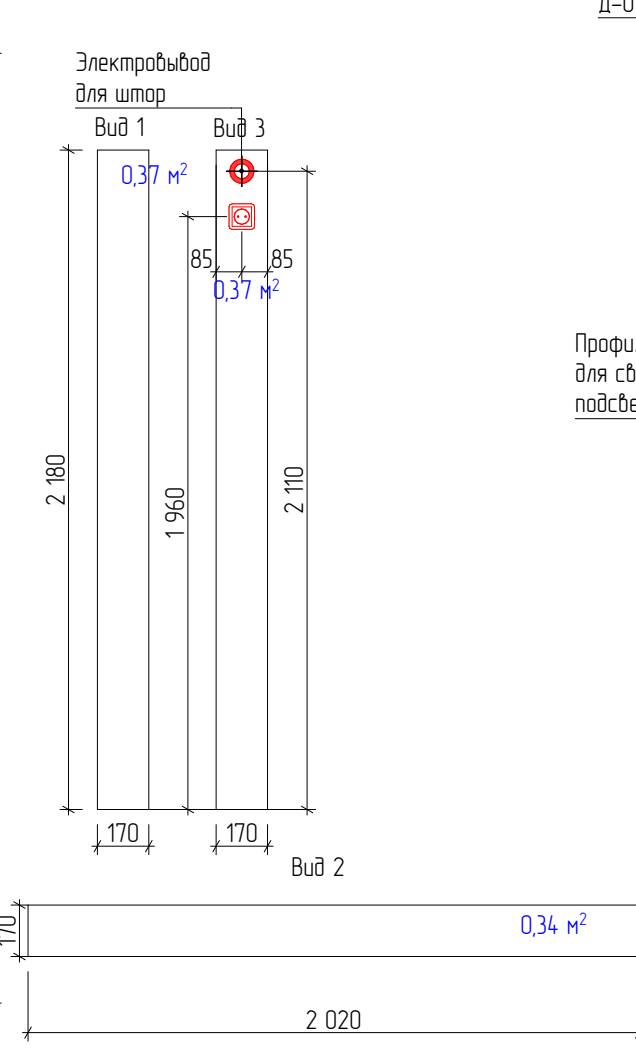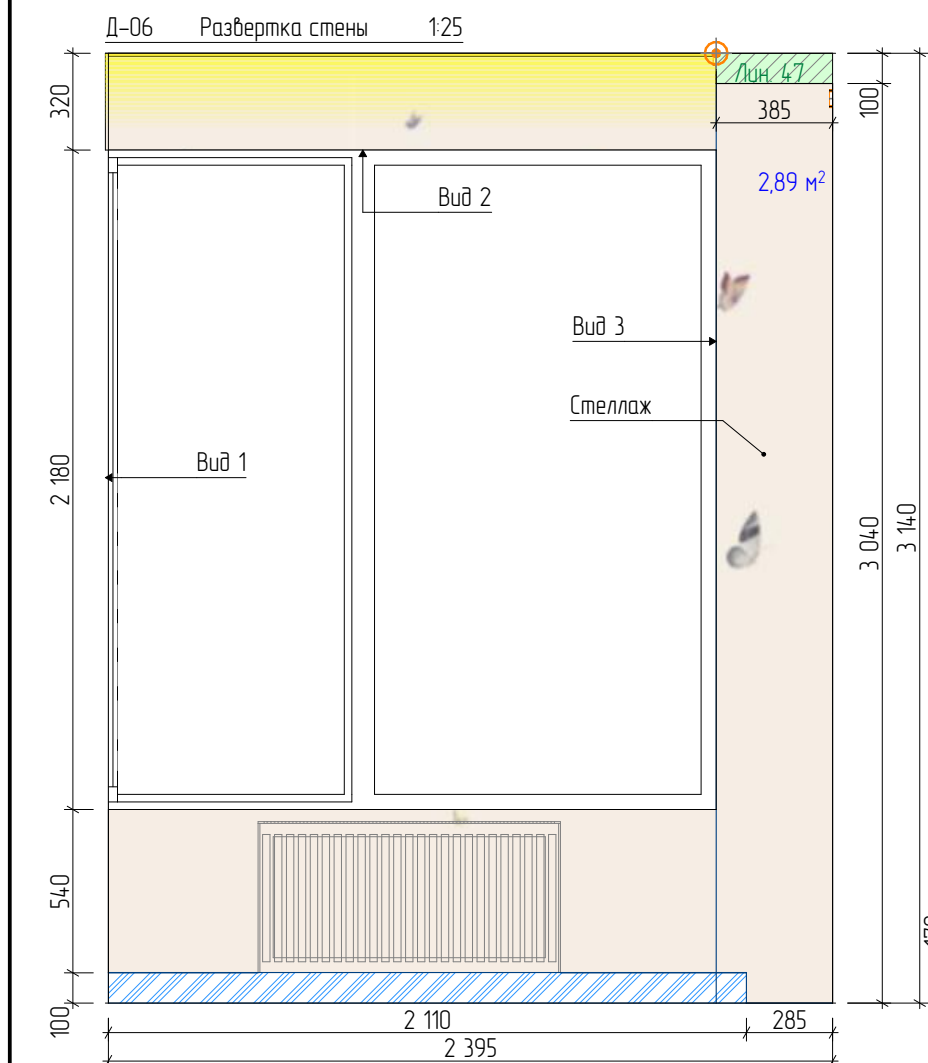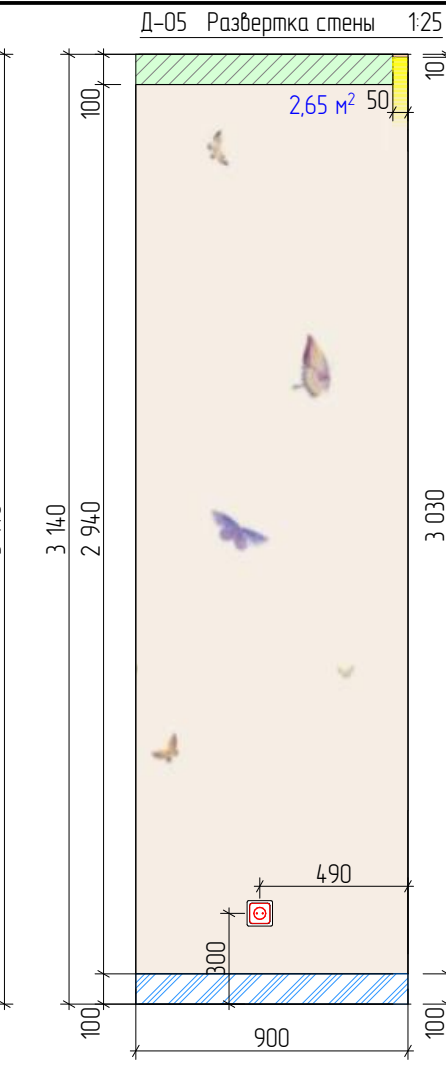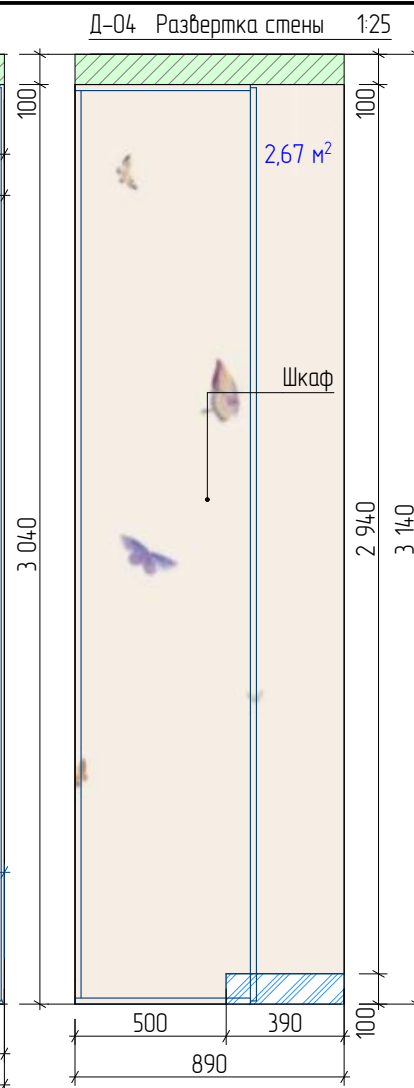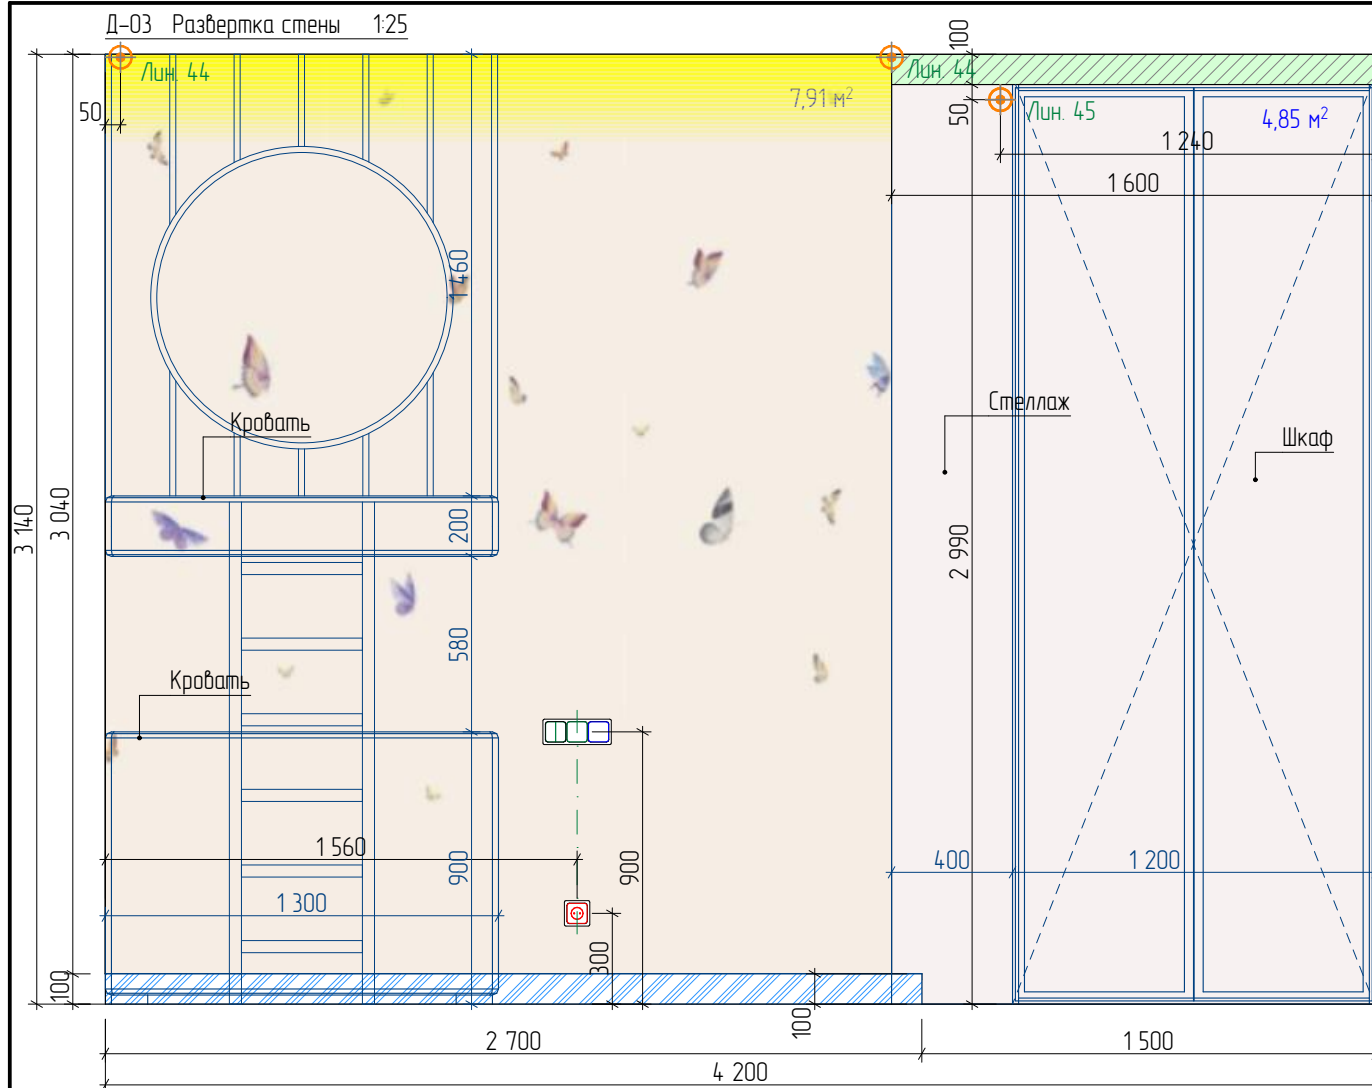

Примечания:

1. * – размеры уточнить по месту после выполнения черновых отделочных работ.
2. Выключатели располагать от уровня чистого пола на высоте 900 мм. Исключения указаны на чертеже.
3. Розетки располагать от уровня чистого пола на высоте 300 мм. Исключения указаны на чертеже.
4. Оконные откосы оклеить строительным флизелином и окрасить в белый цвет. Уточнить по месту.
5. Размещение выводов для отопления согласовать со специалистами.
6. Цвет окрашивания плитуса уточнить после согласования образца.
7. Плитус подрезать по месту в местах стыковки с дверями и мебелью.
8. Внутреннее наполнение мебели разработать со специалистами.
9. Серым/синим цветом показаны размеры мебели. Мебель разработать со специалистами, размеры уточнить после выполнения чистовой отделки.

Условные обозначения:

- | | |
|---|---|
|  | Покраска №1. Выполнить по подготовленной поверхности (стеклохолст*). Цвет при выборе образца (бежевый*). |
|  | Обои №1. Обои ручной работы. Изготовитель: fresq, кол-я: CLASSIC, арт.: EN01. Размер, цвет и фактура при выборе образца. |
|  | Покраска №2. Выполнить по подготовленной поверхности (стеклохолст*). Цвет при выборе образца (белый*). |
|  | Плинтус №1. Теневой плинтус скрытого монтажа с МДФ вставкой. Теневой зазор от пола 100 мм. Цвет при выборе образца (в цвет стен). |
|  | Монтаж конструкций из ГКВЛ |

- | | |
|---|--|
|  | Розетка 220 V |
|  | Выключатель одноклавишный |
|  | Переключатель одноклавишный |
|  | Переключатель двухклавишный |
|  | Вывод 220 V |
|  | Вывод электрокабеля для светодиодной ленты |

МСК 392.12.25-ЭП ПРЕМИУМ				
Эскизный дизайн-проект интерьера квартиры в г. Москва Ж "Остров", ул. Нижние Мневники д. 7				
Спальня №1Развертки стен Д-03, Д-04, Д-05, Д-06, Д-07, Д-08				
Дизайнер интерьера 	№1 Александр Батеньков	Стадия	Лист	Листов
		ЭП	71	120
			Подп.	Дата
ГАП	Батеньков А.С.			
Гл. дизайнер	Власова В.А.			
Гл. проектиров.	Луныкова В.Н.			
Разработал	Ильина Е.Е.			

Ведомость отделочных материалов.

№	Обозначение	Наименование	Кол-во	Примечание
Пол:				
1		Покрытие №01. Паркет. Изготовитель: Lab Arte, кол-я: Angle Дуб Натур, размер: 500x150 мм, точный артикул и производителя уточнить при выборе образца, толщину уточнить при закупа..	15,89	м²
Стены:				
2		Плинтус №1. Теневой плинтус скрытого монтажа с МДФ вставкой. Теневой зазор от пола 100 мм. Цвет при выборе образца (в цвет стен).	10,92	м.п.
3		Обои №1. Обои ручной работы. Изготовитель: fresq, кол-я: CLASSIC, арт.: EN.01. Размер, цвет и фактура при выборе образца.	31,92	м²
4		Покраска №1. Выполнить по подготовленной поверхности (стеклохолст*). Цвет при выборе образца (бежевый*).	8,90	м²
5		МДФ панель №3. 3Д панель. Цвет и фактура при выборе образца (в цвет мебели*).	4,56	м²
6		Зеркало №2. Разработать со специалистами (стандарт*) размеры и резка по чертежу.	2,35	м²
Откосы:				
7		Покраска №2. Выполнить по подготовленной поверхности (стеклохолст*). Цвет при выборе образца (белый*).	1,08	м²
Подоконник:				
8		Подоконник №1. Искусственный камень. Цвет при выборе образца.	0,39	м²

МСК 392.12.25–ЭП ПРЕМИУМ			
Эскизный дизайн–проект интерьера квартиры в г. Москва ЖК “Остров”, ул. Нижние Мневники д. 7			
Спальня №1Ведомость отделочных материалов.			
Дизайнер интерьера  №1 Александр Батеньков	Стадия	Лист	Листов
	ЭП	72	120
		Подп.	Дата
ГАП	Батеньков А.С.		
Гл. дизайнер	Власова В.А.		
Гл. проектиров.	Луныкова В.Н.		
Разработал	Ильина Е.Е.		