




МСК 392.12.25-ЭП ПРЕМИУМ			
Эскизный дизайн-проект интерьера квартиры в г. Москва ЖК "Остров", ул. Нижние Мневники д. 7			
Спальня №2. Видовые точки.			
Дизайнер интерьера №1 Александр Батеньков	Стадия	Лист	Листов
	ЭП	73	120
		Подп.	Дата
ГАП	Батеньков А.С.		
Гл. дизайнер	Власова В.А.		
Гл. проектиров.	Луныкова В.Н.		
Разработал	Ильина Е.Е.		



МСК 392.12.25-ЭП ПРЕМИУМ			
Эскизный дизайн-проект интерьера квартиры в г. Москва ЖК "Остров", ул. Нижние Мневники д. 7			
Спальня №2 Видовые точки.			
Дизайнер интерьера №1 Александр Батеньков	Стадия	Лист	Листов
	ЭП	74	120
		Подп.	Дата
ГАП	Батеньков А.С.		
Гл. дизайнер	Власова В.А.		
Гл. проектиров.	Луныкова В.Н.		
Разработал	Ильина Е.Е.		

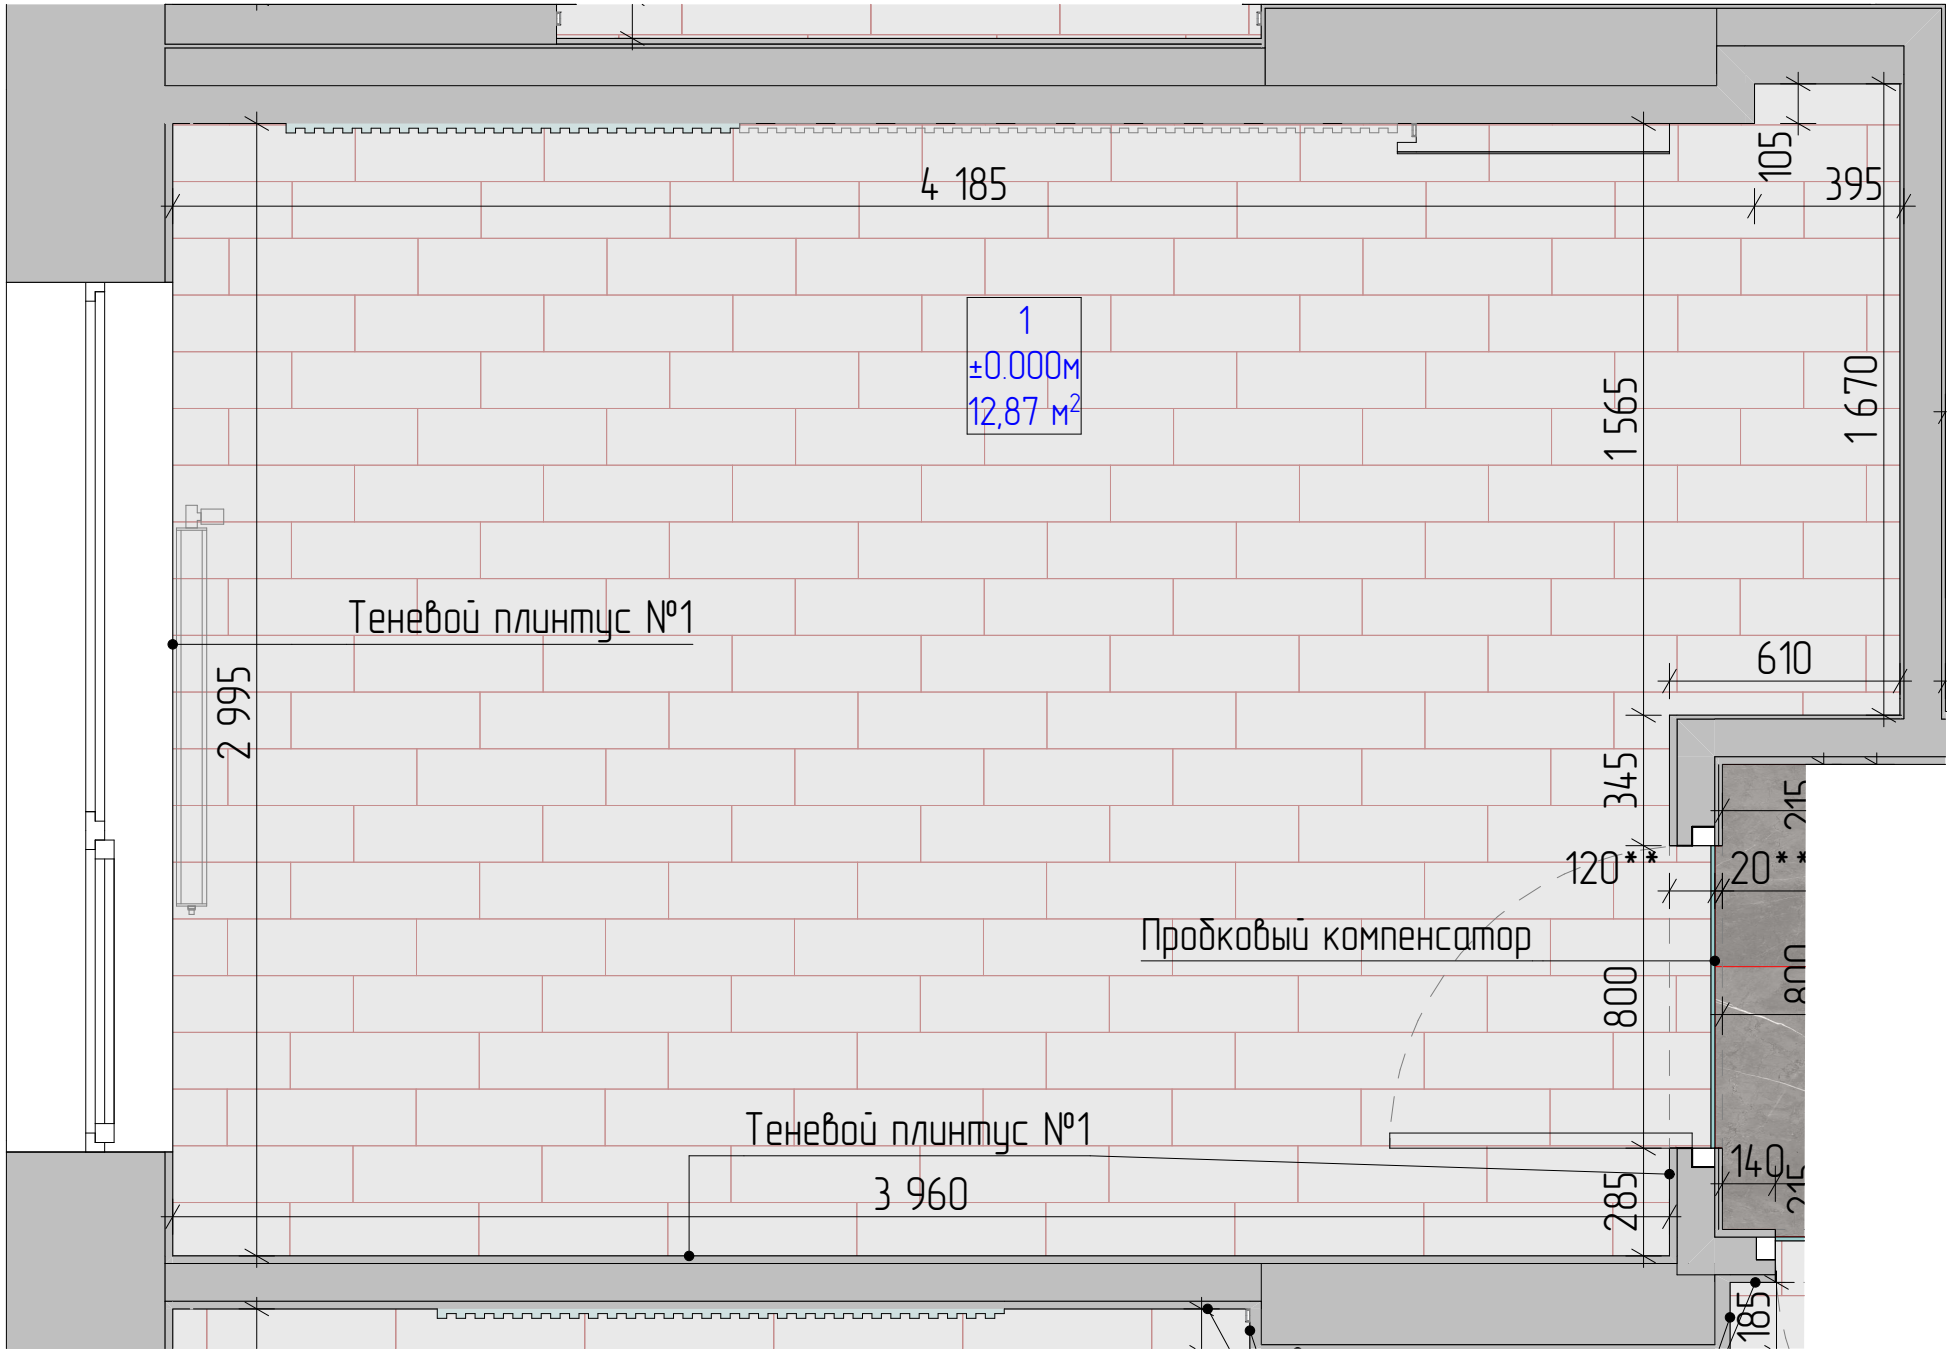

Условные обозначения:


- Направление и начало укладки
- Пробковый компенсатор

1 Покрытие №01. Паркет. Изготовитель: Lab Arte, кол-я: Angle Дуб Намур, размер: 500x150 мм, точный артикул и производителя уточнить при выборе образца, толщину уточнить при заказе.

Примечания:

- *- размеры уточнить по месту после выполнения черновых отделочных работ.
- За отметку ±0,000 принят уровень чистого пола.
- При монтаже напольных покрытий уточнить необходимость устройства дверных проемов с порогом.
- *- размеры уточнить по месту после выполнения черновых отделочных работ и установки дверей со скрытой коробкой.
- ** -размер уточнить по месту в зависимости от точного расположения полотна двери, стыковка двух разных напольных покрытий должна проходить точно по центру вдоль дверного полотна.

МСК 392.12.25-ЭП ПРЕМИУМ			
Эскизный дизайн-проект интерьера квартиры в г. Москва ЖК "Остров", ул. Нижние Мневники д. 7			
Спальня №2.План отделки пола.			
Дизайнер интерьера №1 Александр Батеньков	Стадия	Лист	Листов
	ЭП	75	120
		Подп.	Дата
ГАП	Батеньков А.С.		
Гл. дизайнер	Власова В.А.		
Гл. проектиров.	Луцькова В.Н.		
Разработал	Ильина Е.Е.		

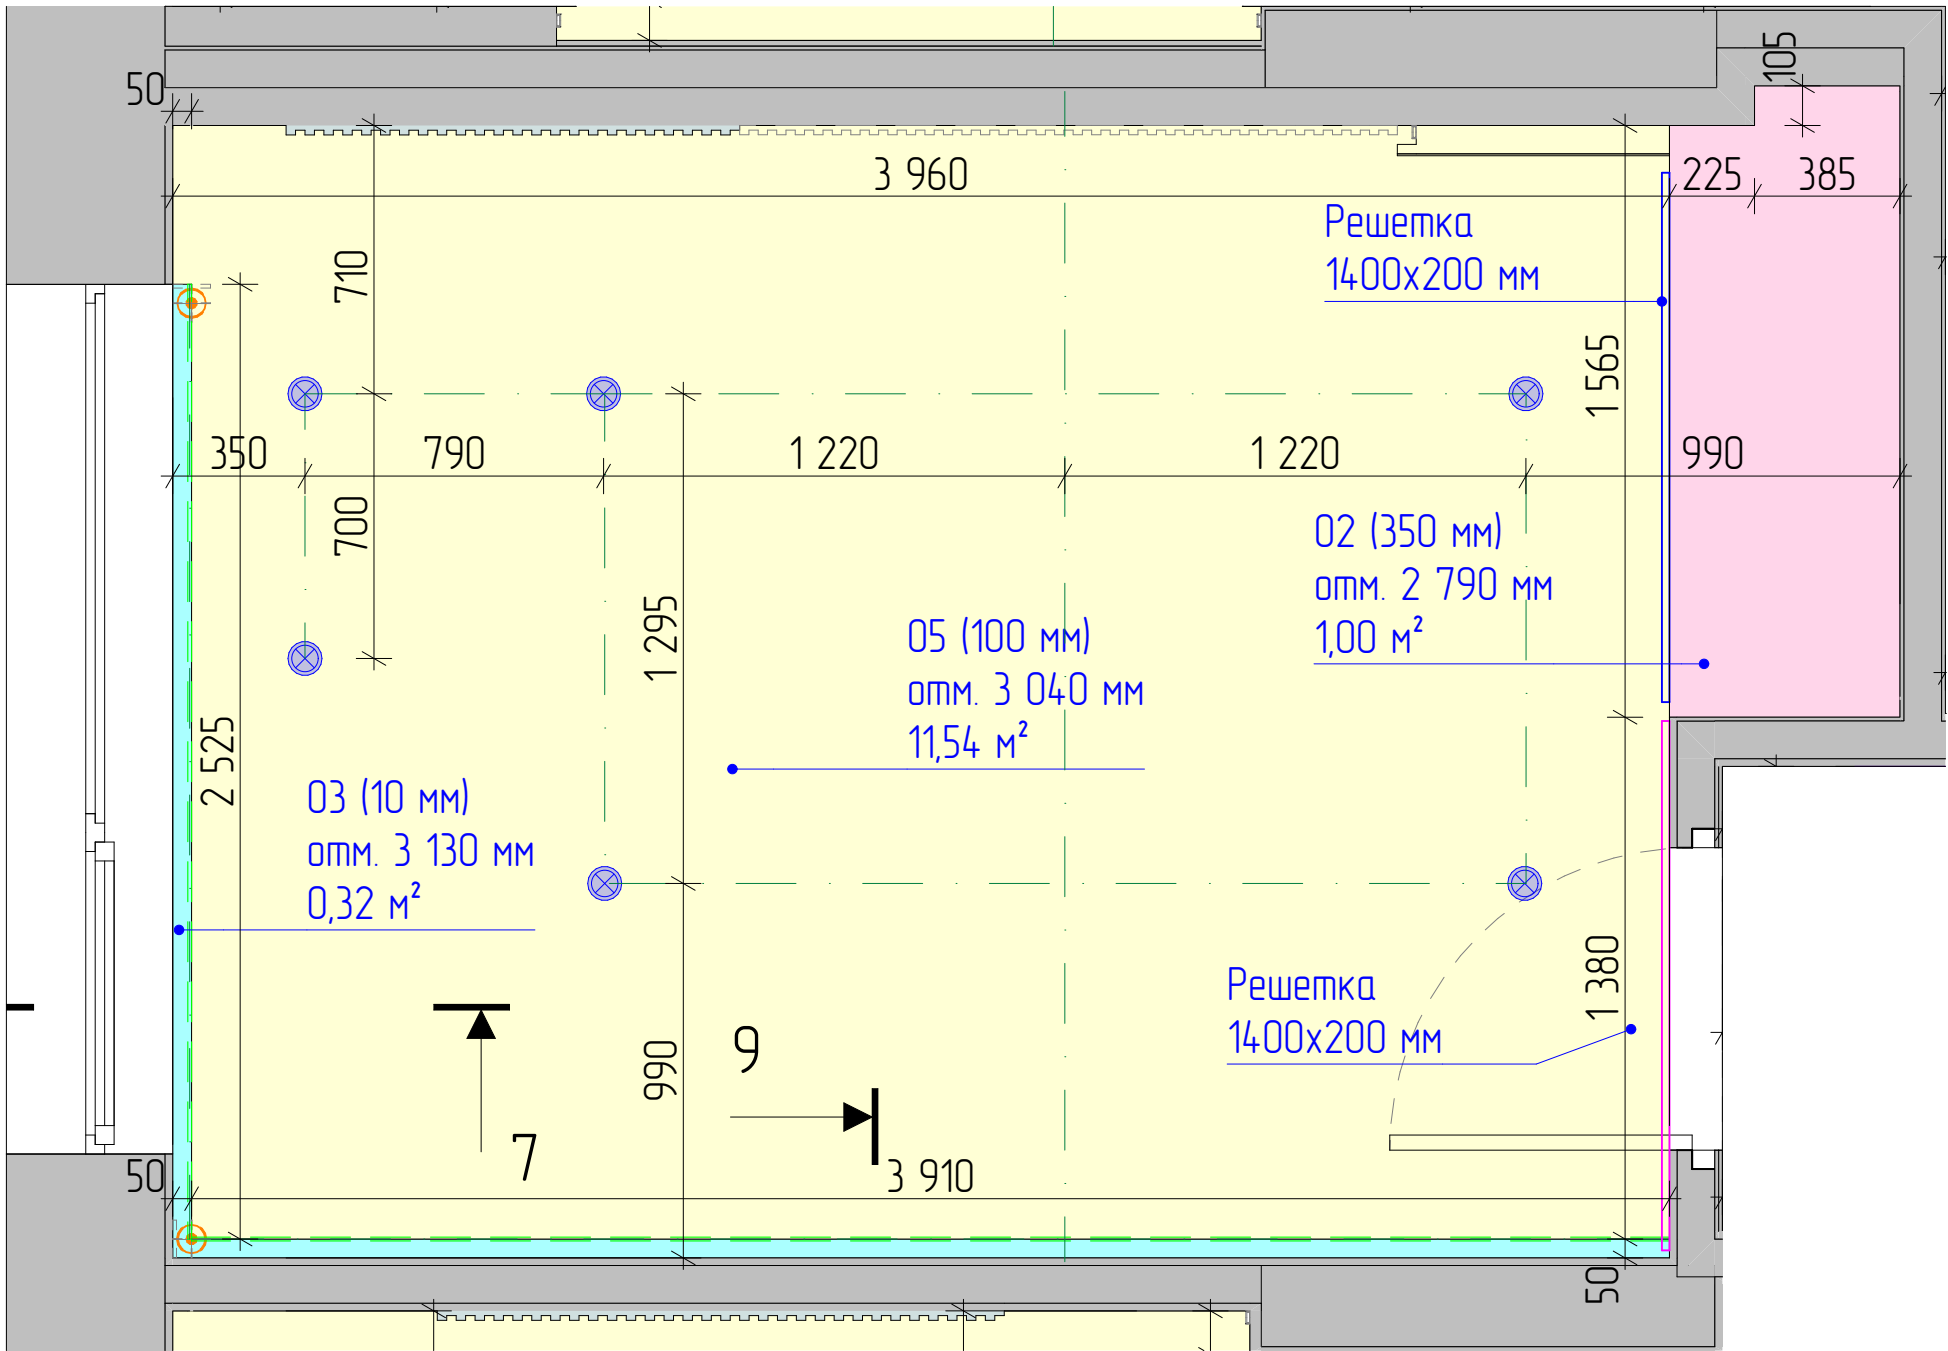


- Условные обозначения:
- Выход 220V
 - Выход электрокабеля для светодиодной ленты
 - Светильник точечный встраиваемый
 - Светодиодная лента

- Примечания:
- * – размеры уточнить по месту после выполнения черновых работ.
 - Выполнить уровни потолка из влагостойкого ГКЛ для предотвращения деформации потолка при затоплении.
 - Высоту уровней потолка отсчитывать от существующей ж/б плиты перекрытия помещения.
 - Шумоизоляцию разработать со специалистами, уточнить состав и толщину слоев шумоизоляционных материалов. Уточнить необходимость устройства с заказчиком.

Условные потолки				
№	Обозначение	Опуск	Примечания	Площадь м2
02		350	Потолок ГК/ЛВ. Окрасить в цвет выбранного образца (белый) по армирующему материалу (стеклохолст "паутинка").	1,00
05		100	Потолок ГК/ЛВ. Окрасить в цвет выбранного образца (белый) по армирующему материалу (стеклохолст "паутинка").	11,54
06		300	Потолок ГК/ЛВ. Окрасить в цвет выбранного образца (белый) по армирующему материалу (стеклохолст "паутинка").	0,32

МСК 392.12.25–ЭП ПРЕМИУМ			
Эскизный дизайн–проект интерьера квартиры в г. Москва ЖК "Остров", ул. Нижние Мневники д. 7			
Спальня №2.План отделки потолка.			
Дизайнер интерьера №1 Александр Батеньков	Стадия	Лист	Листов
	ЭП	76	120
		Подп.	Дата
ГАП	Батеньков А.С.		
Гл. дизайнер	Власова В.А.		
Гл. проектиров.	Лунькова В.Н.		
Разработал	Ильина Е.Е.		


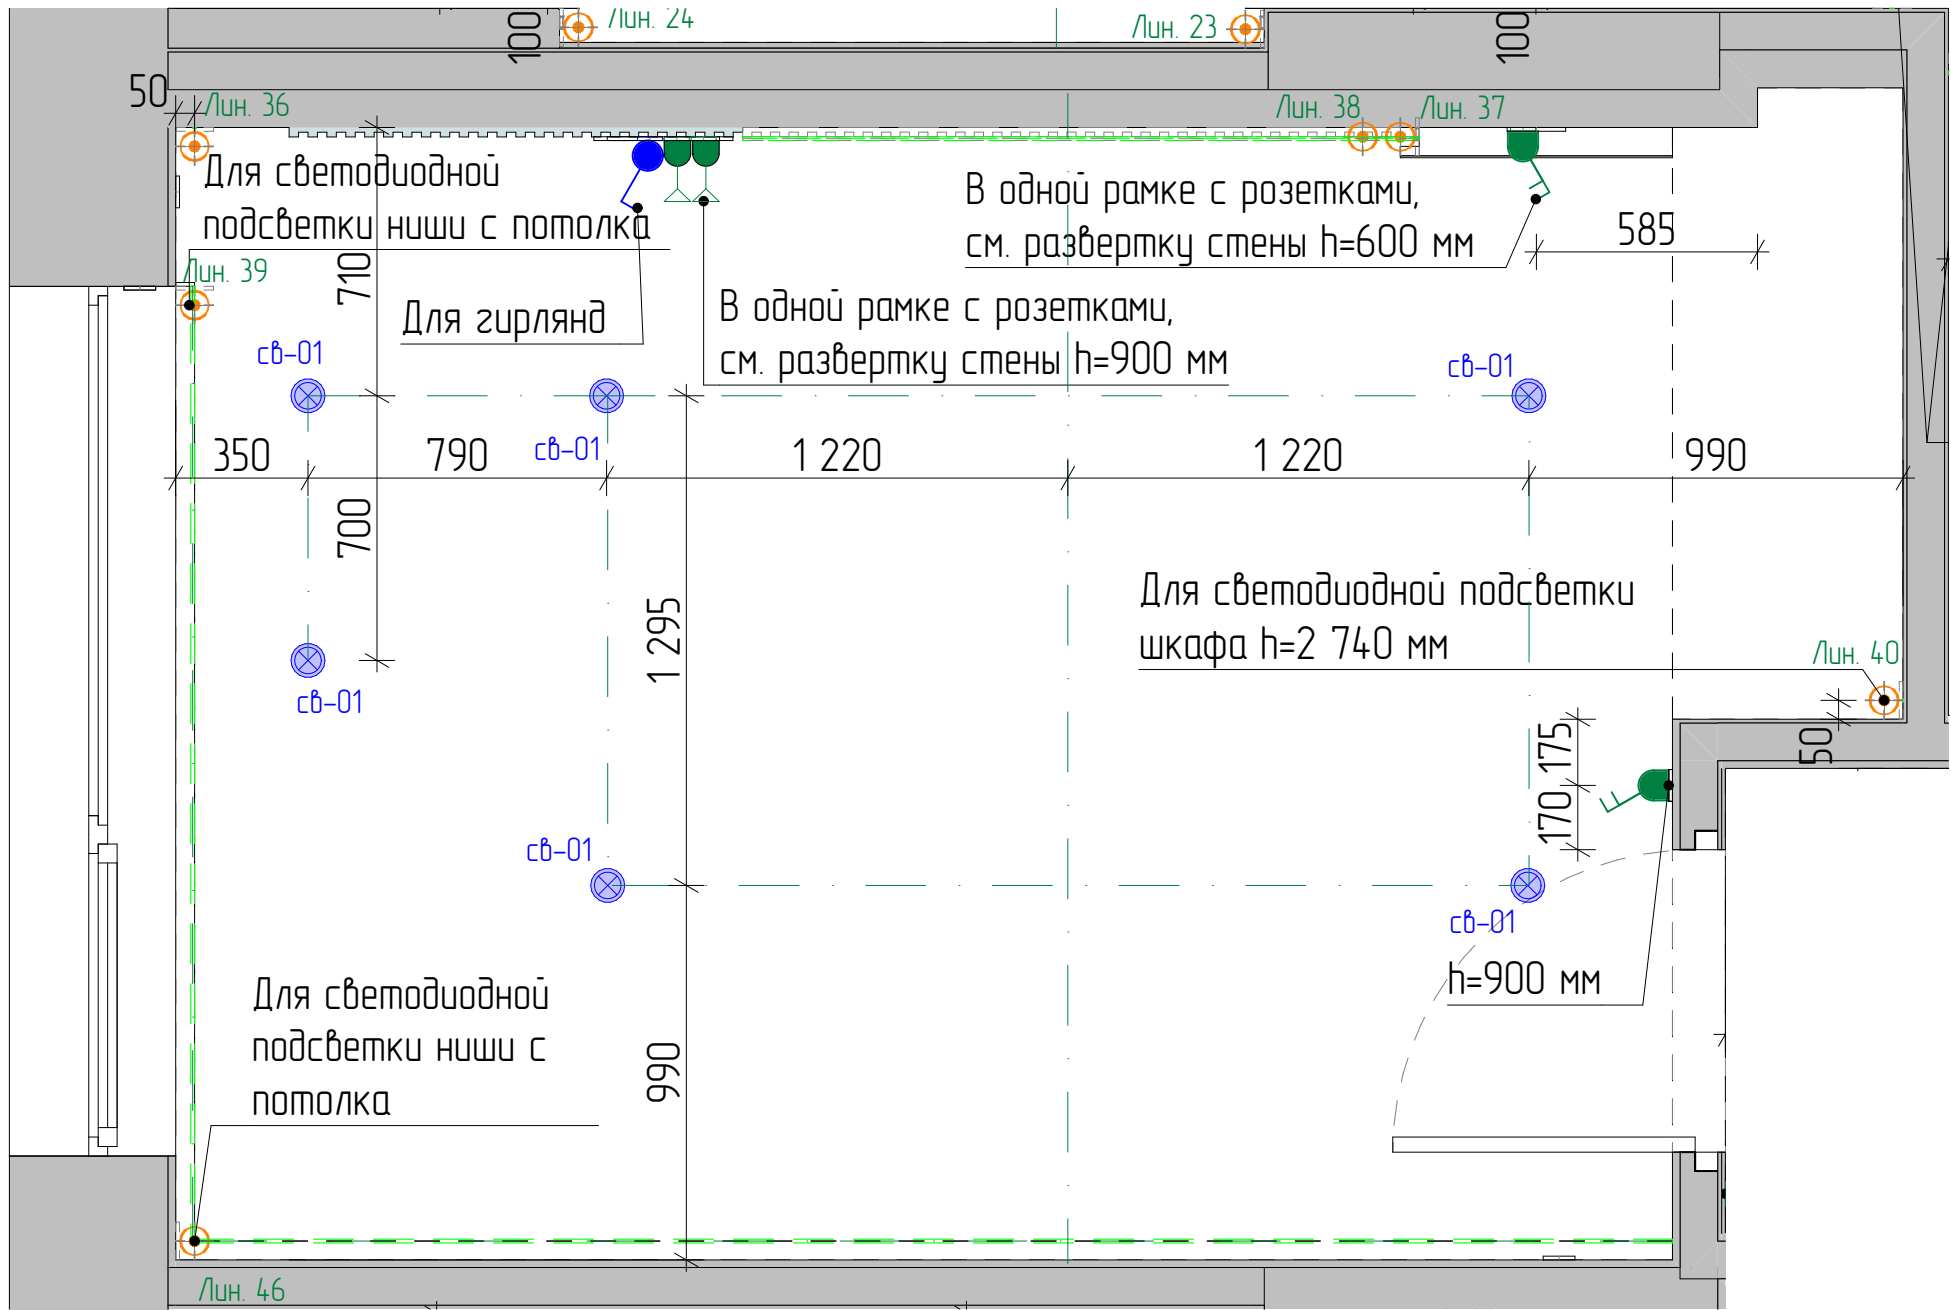


- Условные обозначения:
- Вывод 220V
 - Вывод электрокабеля для светодиодной ленты
 - Выключатель одноклавишный
 - Переключатель двухклавишный
 - Переключатель одноклавишный переходной
 - Светильник точечный встраиваемый
 - Светодиодная лента

Примечания:

- * – размеры уточнить по месту.
- Выключатели располагать от уровня чистого пола на высоте 0,900 м. Исключения указаны на чертеже.
- Светильники, встроенные в мебель, согласовать с изготовителями мебели.

МСК 392.12.25–ЭП ПРЕМИУМ			
Эскизный дизайн–проект интерьера квартиры в г. Москва ЖК "Остров", ул. Нижние Мневники д. 7			
Спальня №2. План размещения освещения и выключателей.			
Дизайнер интерьера №1 Александр Батеньков	Стадия	Лист	Листов
	ЭП	78	120
		Подп.	Дата
ГАП	Батеньков А.С.		
Гл. дизайнер	Власова В.А.		
Гл. проектиров.	Луцькова В.Н.		
Разработал	Ильина Е.Е.		

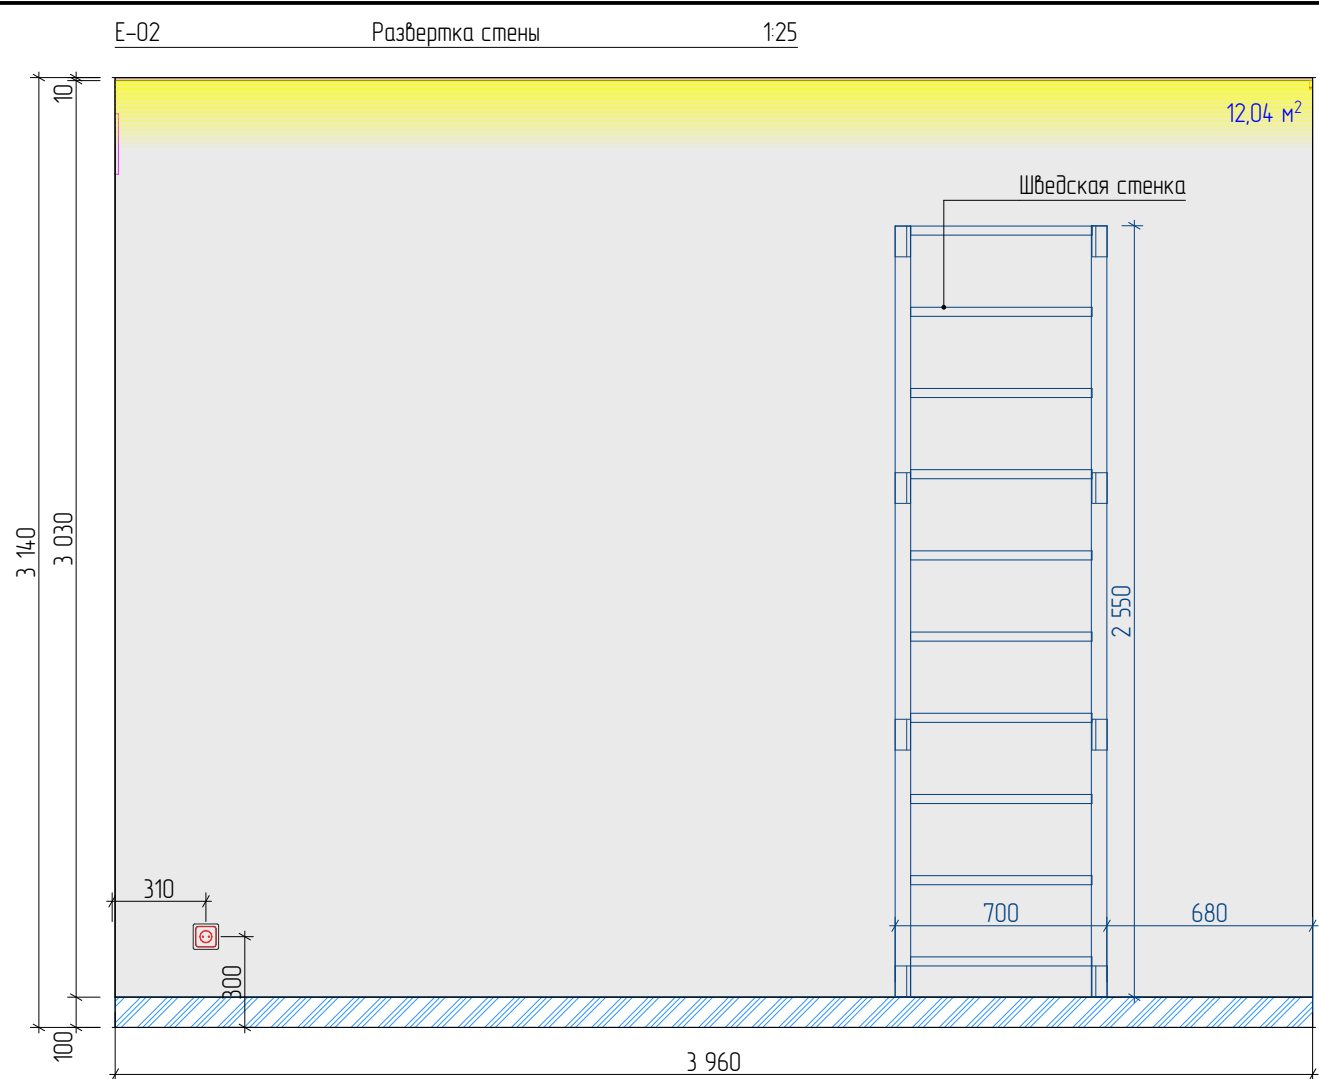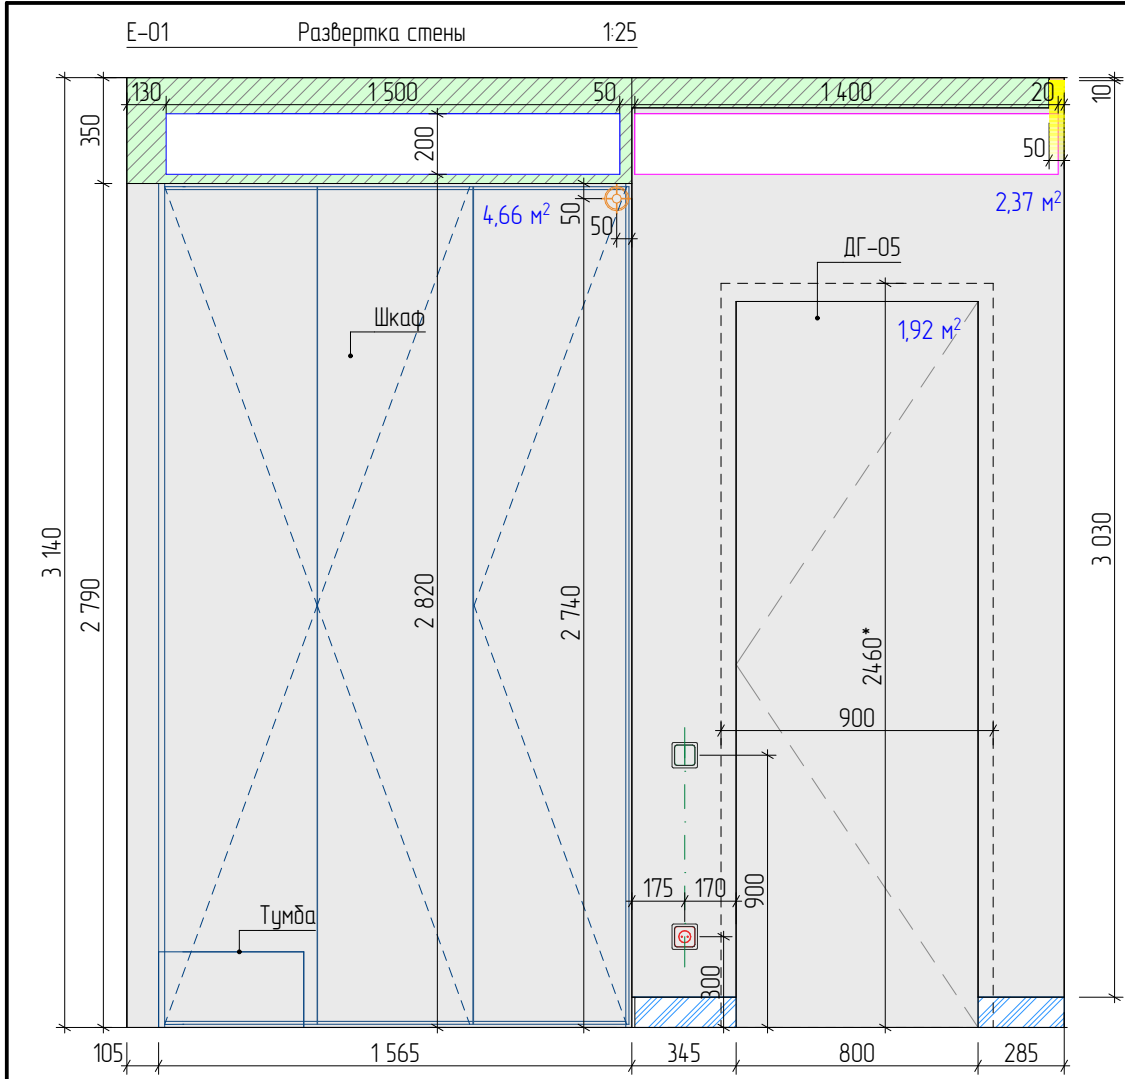



Условные обозначения:

- Плинтус №1. Теневой плинтус скрытого монтажа с МДФ вставкой. Теневой зазор от пола 100 мм. Цвет при выборе образца (в цвет стен).
- Монтаж конструкций из ГКВЛ
- Покраска №4. Выполнить по подготовленной поверхности (стеклохолст*). Цвет при выборе образца (светло серый*).
- Розетка 220 V
- Переключатель двухклавишный

Примечания:

- * - размеры уточнить по месту после выполнения черновых отделочных работ.
- Выключатели располагать от уровня чистого пола на высоте 900 мм. Исключения указаны на чертеже.
- Розетки располагать от уровня чистого пола на высоте 300 мм. Исключения указаны на чертеже.
- Цвет окрашивания плинтуса уточнить после согласования образца.
- Высоту проемов выполнить 2460 мм от уровня чистого пола. Уточнить после подбора и согласования модели дверей.
- Плинтус подрезать по месту в местах стыковки с дверями и мебелью.
- Внутреннее наполнение мебели разработать со специалистами.
- Серым/синим цветом показаны размеры мебели. Мебель разработать со специалистами, размеры уточнить после выполнения чистовой отделки.

МСК 392.12.25-ЭП ПРЕМИУМ			
Эскизный дизайн-проект интерьера квартиры в г. Москва ЖК "Остров", ул. Нижние Мневники д. 7			
Спальня №2. Развертки стен Е-01, Е-02.			
Дизайнер интерьера №1  Александр Батеньков	Стадия	Лист	Листов
	ЭП	79	120
		Подп.	Дата
ГАП	Батеньков А.С.		
Гл. дизайнер	Власова В.А.		
Гл. проектиров.	Луныкова В.Н.		
Разработал	Ильина Е.Е.		

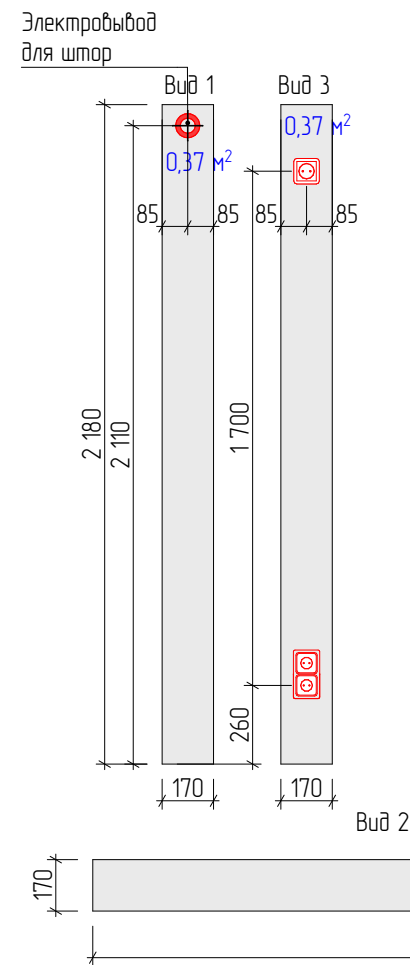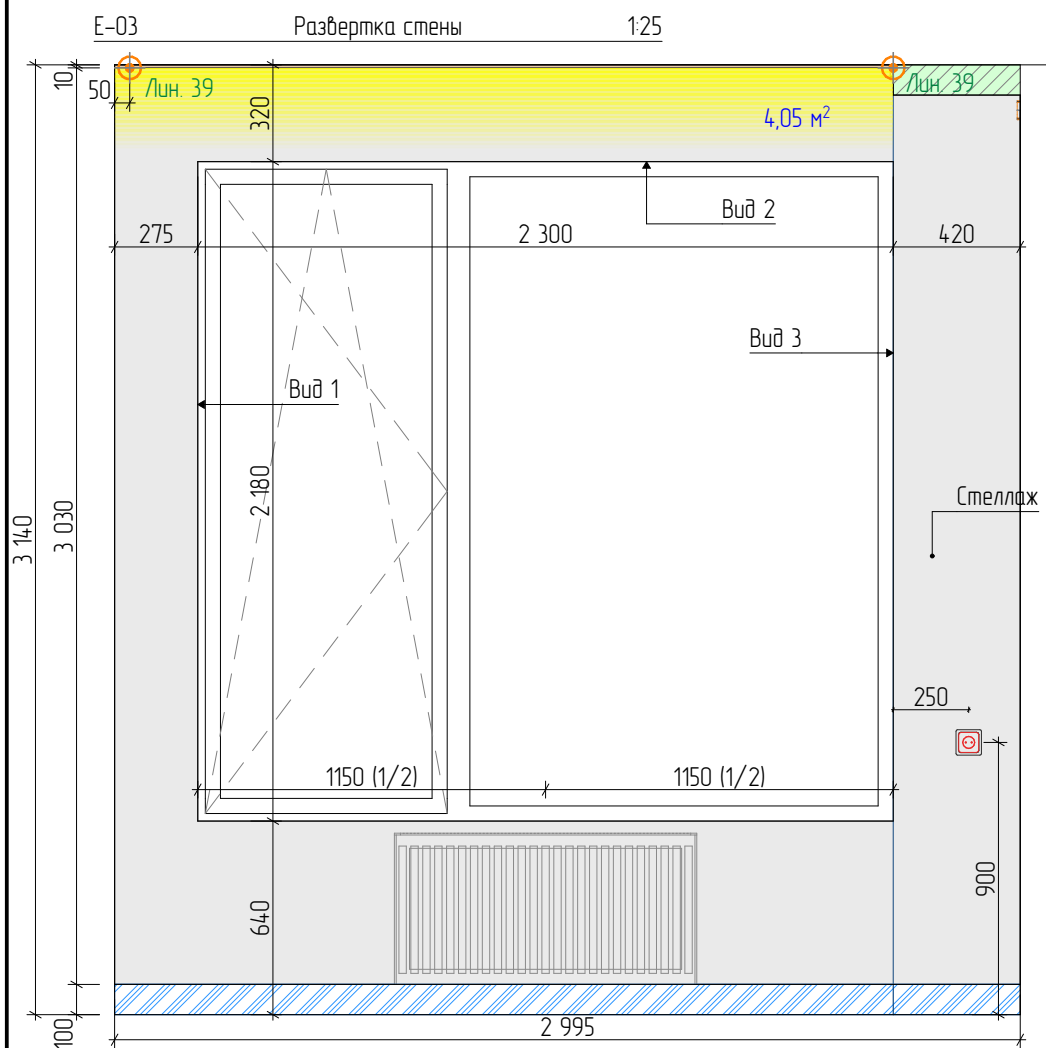


Примечания:


1. * – размеры уточнить по месту после выполнения черновых отделочных работ.
2. Выключатели располагать от уровня чистого пола на высоте 900 мм. Исключения указаны на чертеже.
3. Розетки располагать от уровня чистого пола на высоте 300 мм. Исключения указаны на чертеже.
4. Оконные откосы оклеить строительным флизелином и окрасить в белый цвет. Уточнить по месту.
5. Размещение выводов для отопления согласовать со специалистами.
6. Цвет окрашивания плинтуса уточнить после согласования образца.
7. Резку зеркала решить по месту авторским надзором.
8. Плинтус подрезать по месту в местах стыковки с дверями и мебелью.
9. Внутреннее наполнение мебели разработать со специалистами.
10. Серым/синим цветом показаны размеры мебели. Мебель разработать со специалистами, размеры уточнить после выполнения чистовой отделки.

Условные обозначения:


- Плинтус №1. Теневой плинтус скрытого монтажа с МДФ вставкой. Теневой зазор от пола 100 мм. Цвет при выборе образца (в цвет стен).
- Монтаж конструкций из ГКВЛ
- Зеркало №2. Разработать со специалистами (стандарт*) размеры и резка по чертежу.
- Покраска №4. Выполнить по подготовленной поверхности (стеклохолст*). Цвет при выборе образца (светло серый*).
- МДФ панель №3. 3Д панель. Цвет и фактура при выборе образца (в цвет мебели*).
- 3Д панель №1. 3Д панель с росписью. Выполнить по подготовленной поверхности (на заказ).
- Вывод 220 V
- Вывод электрокабеля для светодиодной ленты
- Розетка 220 V
- Интернет-розетка двойная
- Выключатель одноклавишный
- Переключатель одноклавишный переходной
- Переключатель двухклавишный

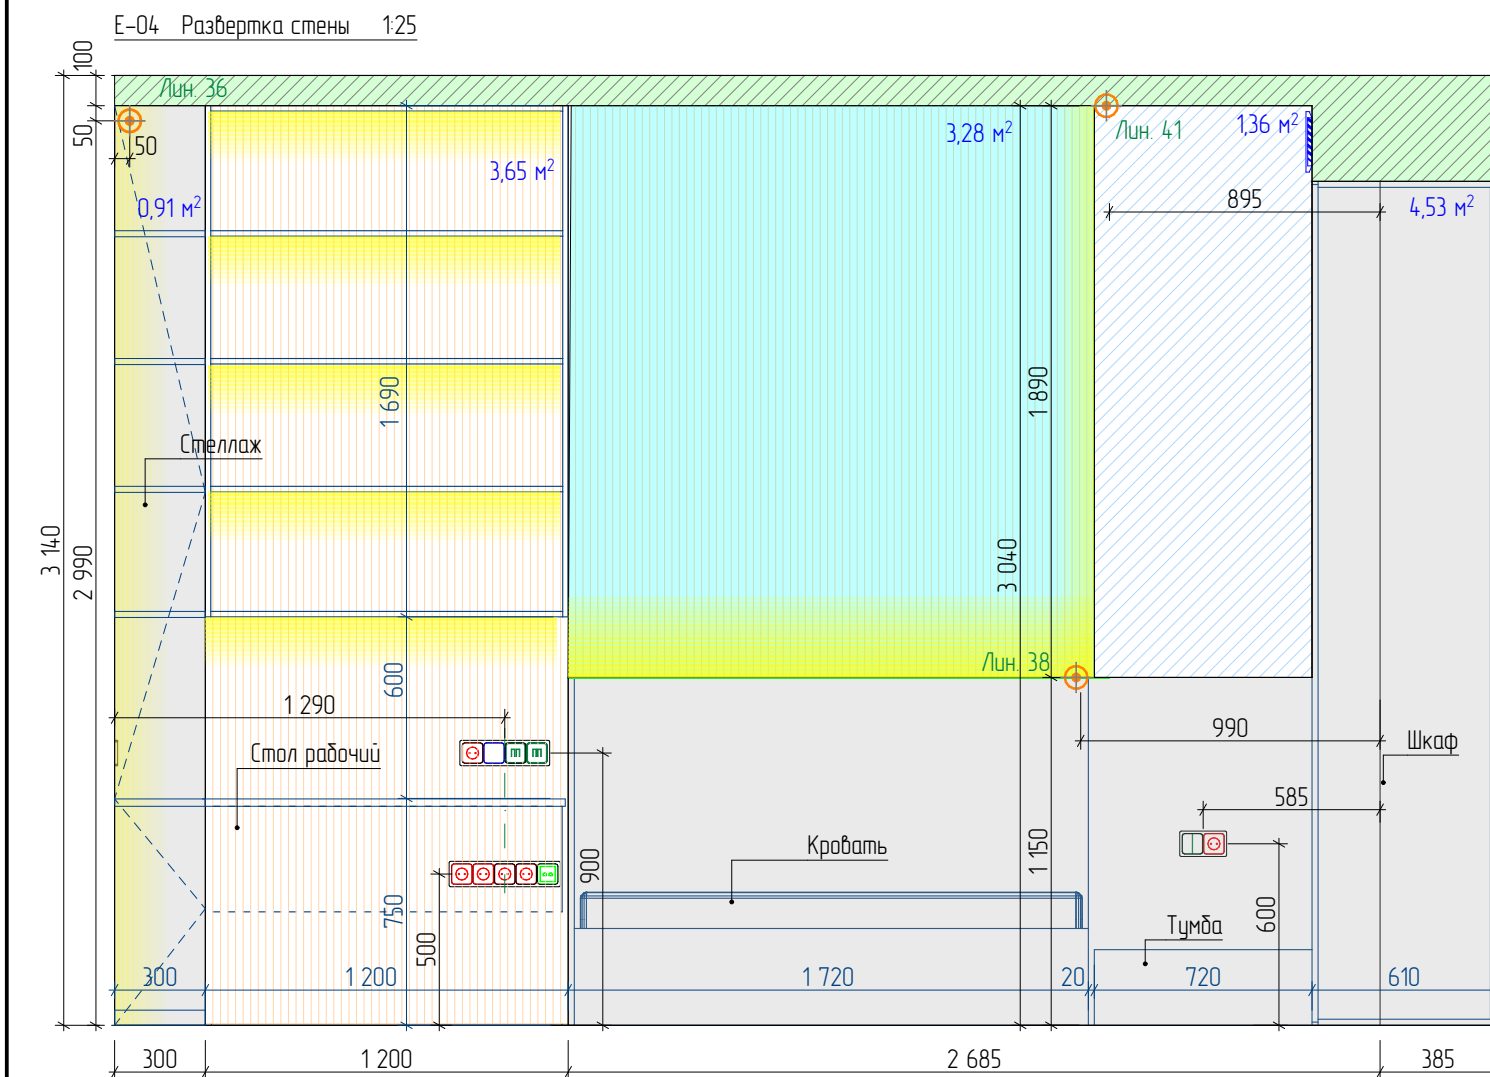

Е-05 Развертка стены 1:25

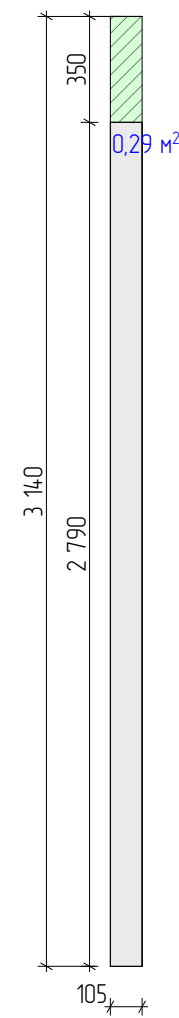

Е-06 Развертка стены 1:25

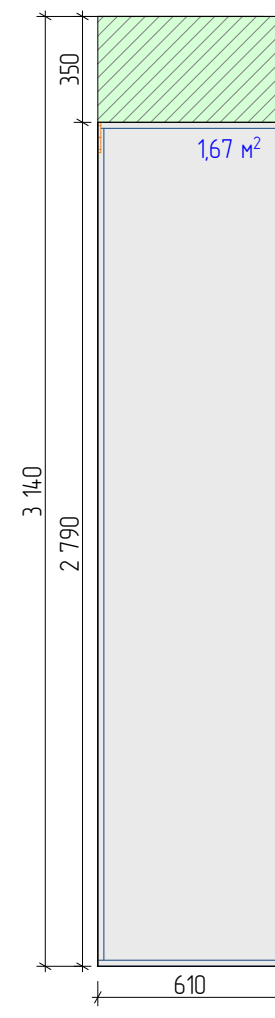

МСК 392.12.25-ЭП ПРЕМИУМ			
Эскизный дизайн-проект интерьера квартиры в г. Москва ЖК "Остров", ул. Нижние Мневники д. 7			
Спальня №2. Развертки стен Е-03, Е-04, Е-05, Е-06.			
Дизайнер интерьера №1 Александр Батеньков	Стадия	Лист	Листов
	ЭП	80	120
		Подп.	Дата
ГАП	Батеньков А.С.		
Гл. дизайнер	Власова В.А.		
Гл. проектиров.	Луныкова В.Н.		
Разработал	Ильина Е.Е.		

Ведомость отделочных материалов.

№	Обозначение	Наименование	Кол-во	Примечание
Пол:				
1		Покрытие №01. Паркет. Изготовитель: Lab Arte, кол-я: Angle Дуб Натур, размер: 500x150 мм, точный артикул и производителя уточнить при выборе образца, толщину уточнить при закупае..	12,87	м²
Стены:				
2		Плинтус №1. Теневой плинтус скрытого монтажа с МДФ вставкой. Теневой зазор от пола 100 мм. Цвет при выборе образца (в цвет стен).	7,59	м.п.
3		Покраска №4. Выполнить по подготовленной поверхности (стеклохолст*). Цвет при выборе образца (светло серый*).	27,78	м²
4		ЗД панель №1. Зд панель с росписью. Выполнить по подготовленной поверхности (на заказ).	3,28	м²
5		МДФ панель №3. ЗД панель. Цвет и фактура при выборе образца (в цвет мебели*).	3,65	м²
6		Зеркало №2. Разработать со специалистами (стандарт*) размеры и резка по чертежу.	1,36	м²
Откосы:				
7		Покраска №2. Выполнить по подготовленной поверхности. Цвет при выборе образца (белый*).	1,13	м²
Подоконник:				
8		Подоконник №1. Искусственный камень. Цвет при выборе образца.	0,34	м²

МСК 392.12.25–ЭП ПРЕМИУМ			
Эскизный дизайн–проект интерьера квартиры в г. Москва ЖК “Остров”, ул. Нижние Мневники д. 7			
Спальня №2.Ведомость отделочных материалов.			
Дизайнер интерьера  №1 Александр Батеньков	Стадия	Лист	Листов
	ЭП	81	120
		Подп.	Дата
ГАП	Батеньков А.С.		
Гл. дизайнер	Власова В.А.		
Гл. проектиров.	Луцькова В.Н.		
Разработал	Ильина Е.Е.		