




МСК 392.12.25-ЭП ПРЕМИУМ			
Эскизный дизайн-проект интерьера квартиры в г. Москва ЖК "Остров", ул. Нижние Мневники д. 7			
Мастер ваннаяВидовые точки.			
Дизайнер интерьера  Александр Батеньков	Стадия	Лист	Листов
	ЭП	96	120
		Подп.	Дата
ГАП	Батеньков А.С.		
Гл. дизайнер	Власова В.А.		
Гл. проектиров.	Луныкова В.Н.		
Разработал	Ильина Е.Е.		



МСК 392.12.25-ЭП ПРЕМИУМ			
Эскизный дизайн-проект интерьера квартиры в г. Москва ЖК "Остров", ул. Нижние Мневники д. 7			
Мастер ваннаяВидовые точки.			
Дизайнер интерьера №1 Александр Батеньков	Стадия	Лист	Листов
	ЭП	97	120
		Подп.	Дата
ГАП	Батеньков А.С.		
Гл. дизайнер	Власова В.А.		
Гл. проектиров.	Луныкова В.Н.		
Разработал	Ильина Е.Е.		

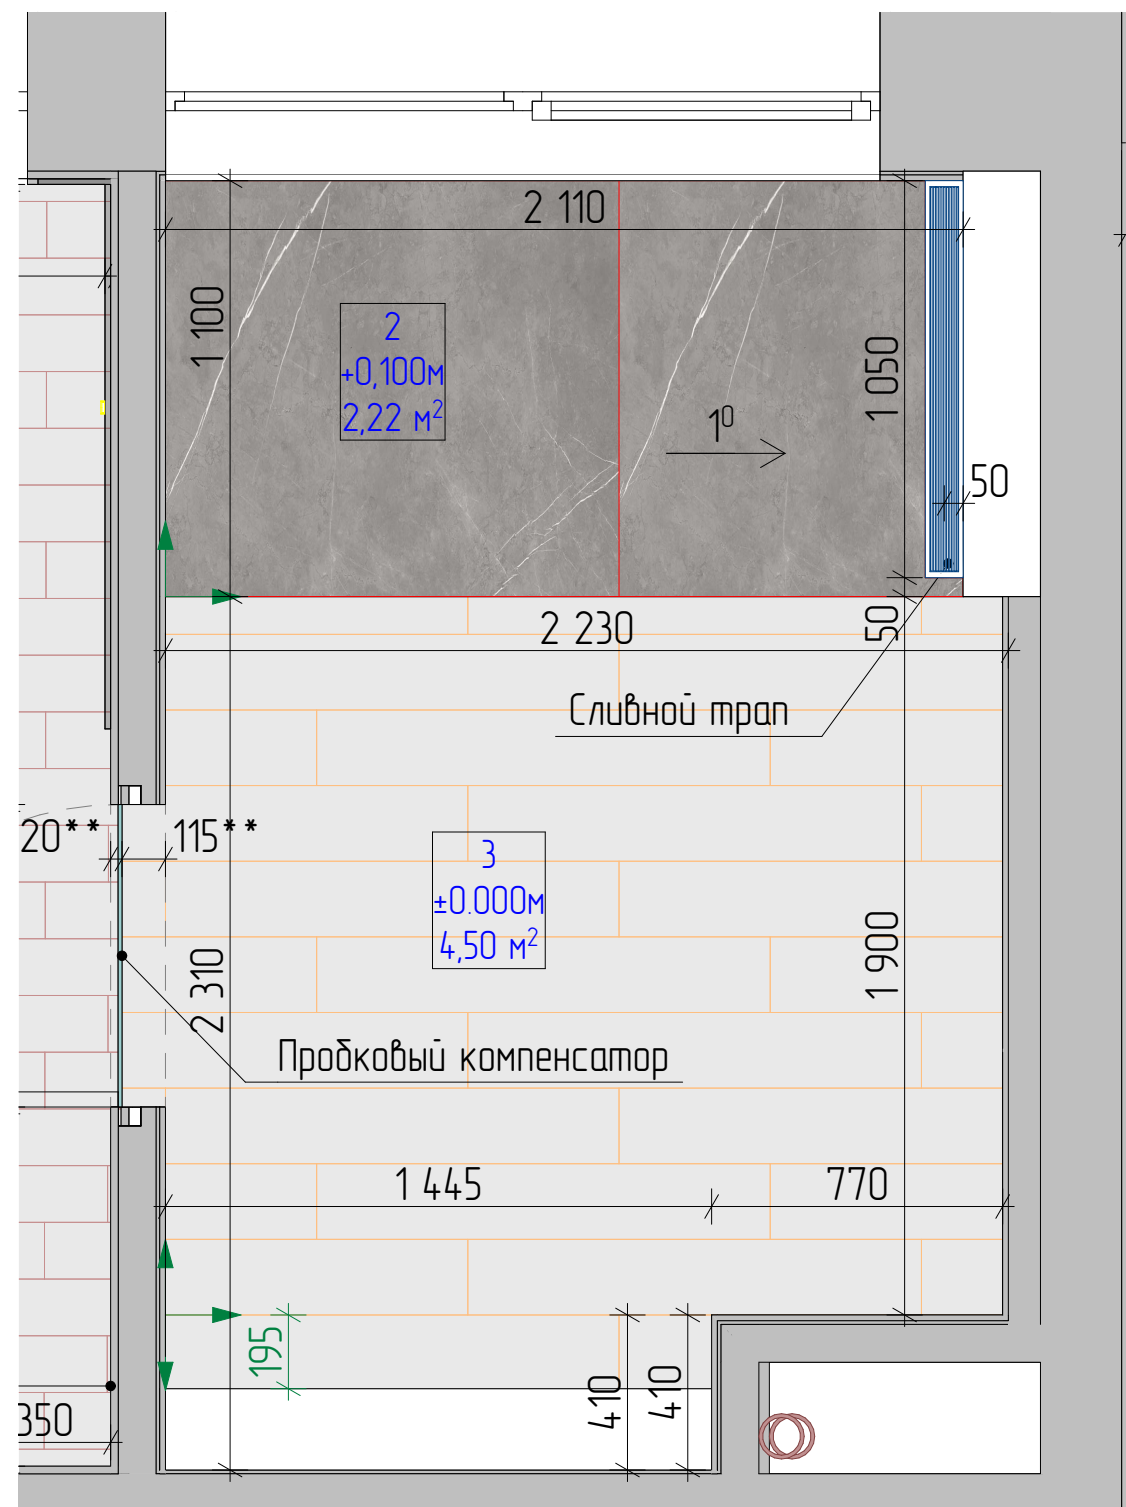


Условные обозначения:




Направление и начало укладки

4

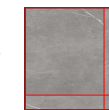

Покрытие №02. Керамогранит. Изготовитель:
Elegant Grey, кол-я: Forte Dei Marmi, размер:
1200x1200 мм, толщину уточнить при заказе.

3.

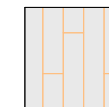


Покрывшее №03. Керамогранит. Изготовитель:
Nutmeg, кол-я: Woodslate Life, размер: 1200x200
мм, толщину уточнить при заказе.

Примечания:

1. * – размеры уточнить по месту после выполнения черновых отделочных работ.
2. За отметку $\pm 0,000$ принят уровень чистого пола.
3. Во влажных помещениях предусмотреть гидроизоляцию пола с заведением на стены на 150 мм.
4. Соединить швы плитки на подиумах и основном полу.
5. При монтаже напольных покрытий уточнить необходимость устройства дверных проемов с порогом.
1. * – размеры уточнить по месту после выполнения черновых отделочных работ и установки дверей со скрытой коробкой.
2. ** – размер уточнить по месту в зависимости от точного расположения полотна двери, стыковка двух разных напольных покрытий должна проходить точно по центру вдоль дверного полотна.

МСК 392.12.25-ЭП ПРЕМИУМ			
Эскизный дизайн-проект интерьера квартиры в г. Москва ЖК "Остров", ул. Нижние Мневники д. 7			
Мастер ванная План отделки пола.			
Дизайнер интерьера  №1 Александр Батеньков	Стандия	Лист	Листов
	ЭП	98	120
		Подп.	Дата
ГАП	Батеньков А.С.		
Гл. дизайнер	Власова В.А.		
Гл. проектиров.	Луцькова В.Н.		
Разработал	Ильина Е.Е.		

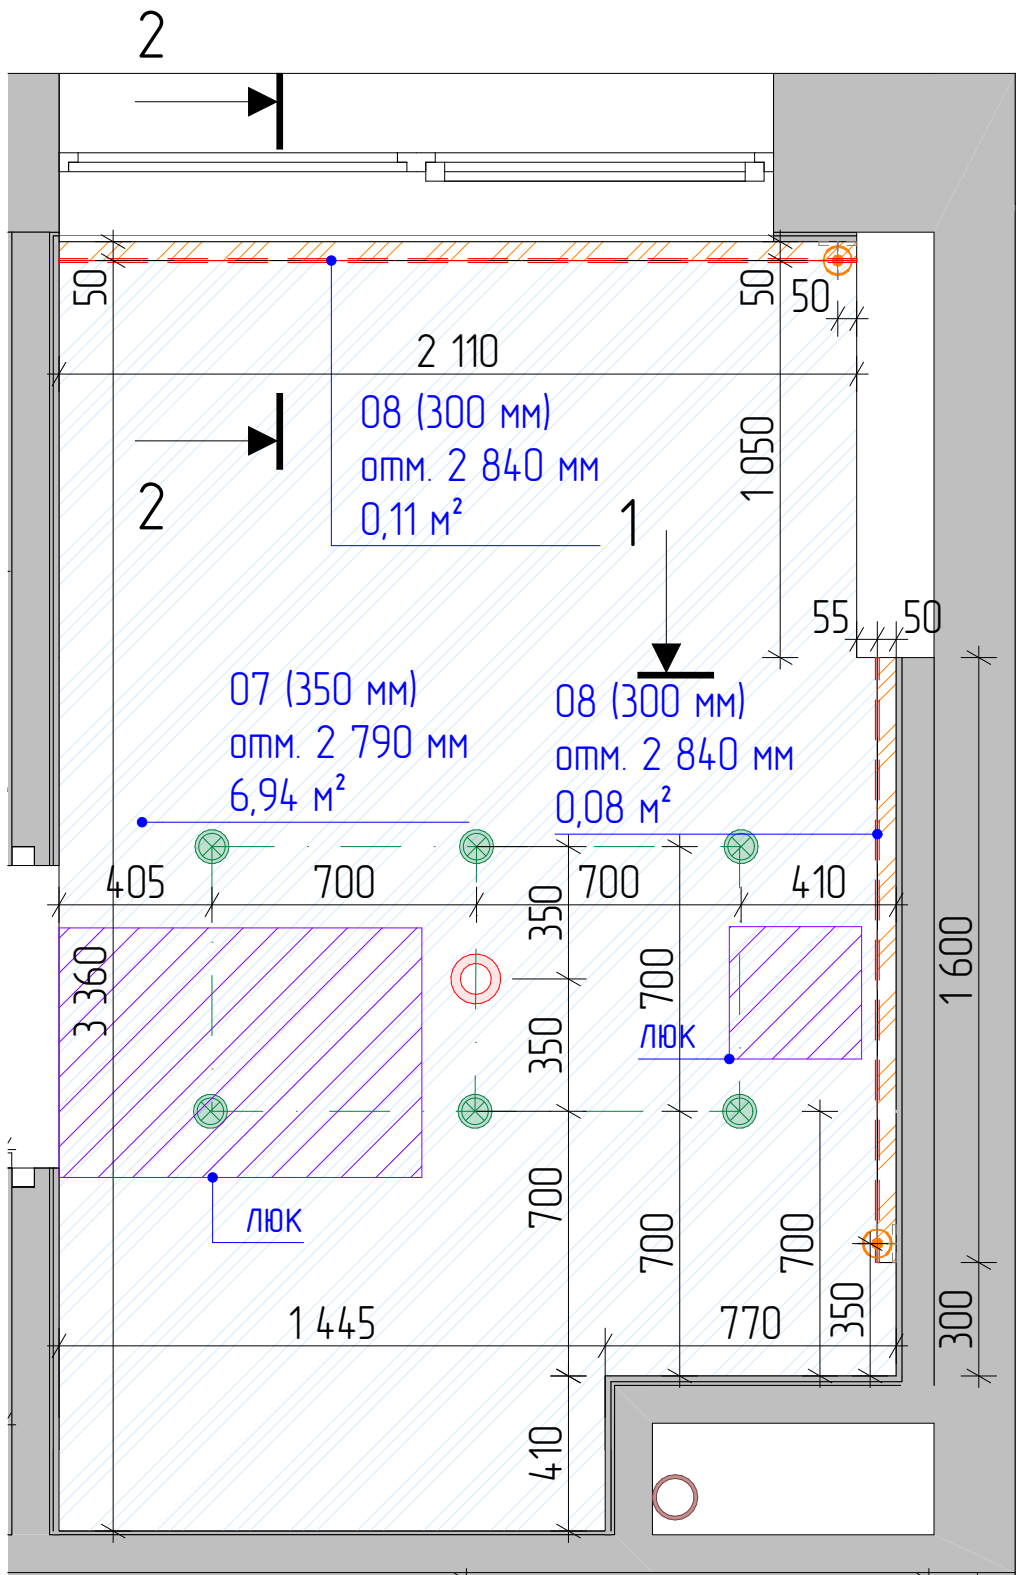

- Условные обозначения:
- Выход 220V
 - Выход электрокабеля для светодиодной ленты
 - Диффузор, вытяжка
 - Светильник точечный встраиваемый влагозащищенный
 - Светодиодная лента, влагозащищенная
 - Люк доступа

- Примечания:
- * – размеры уточнить по месту после выполнения черновых работ.
 - Выполнить уровни потолка из влагостойкого ГКЛ для предотвращения деформации потолка при затоплении.
 - Высоту уровней потолка отсчитывать от существующей ж/б плиты перекрытия помещения.
 - Во влажных помещениях обои под покраску на потолок не клеить, заменить на оштукатуривание по армирующей сетке, согласовать со специалистами.
 - От вытяжки провести вентиляционный короб до общедомового канала в конструкции потолка, уточнить по месту со специалистами и заказчиком.
 - Шумоизоляцию разработать со специалистами, уточнить состав и толщину слоев шумоизоляционных материалов. Уточнить необходимость устройства с заказчиком.


МСК 392.12.25–ЭП ПРЕМИУМ

Эскизный дизайн–проект интерьера квартиры в г. Москва ЖК "Остров", ул. Нижние Мневники д. 7

Мастер ваннаяПлан отделки потолка.

Дизайнер интерьера №1 Александр Батеньков	Стадия	Лист	Листов
	ЭП	99	120
		Подп.	Дата
ГАП	Батеньков А.С.		
Гл. дизайнер	Власова В.А.		
Гл. проектиров.	Луныкова В.Н.		
Разработал	Ильина Е.Е.		


Условные потолки				
№	Обозначение	Опуск	Примечания	Площадь м2
07		350	Потолок ГКЛ/В, Окрасить в цвет выбранного образца (белый) по оштукатуренной поверхности.	6,94
08		300	Потолок ГКЛ/В, Окрасить в цвет выбранного образца (белый) по оштукатуренной поверхности.	0,19

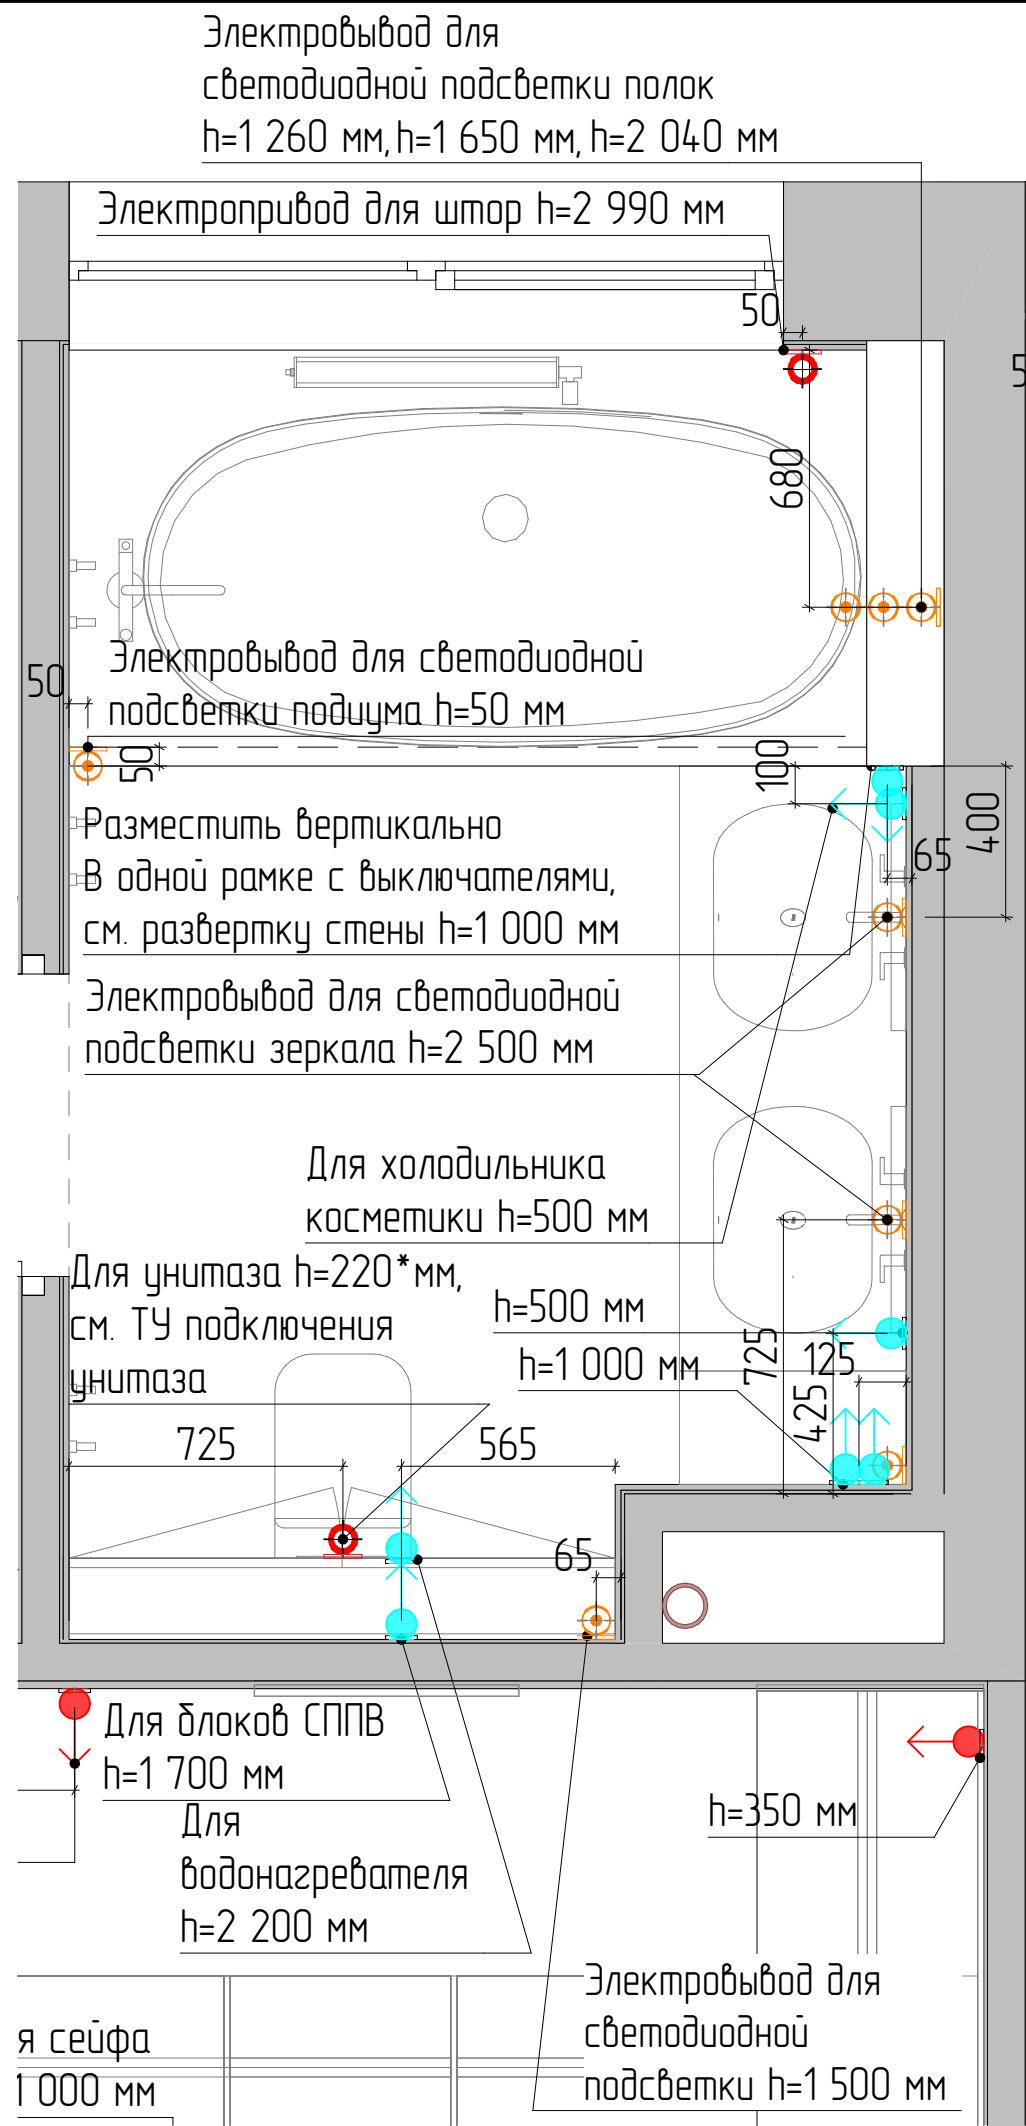

- Условные обозначения:
- Розетка 220V влагозащищенная
 - Вывод электрокабеля для варочной поверхности
 - Вывод 220V

- Примечания:
- * – размеры уточнить по месту.
 - Розетки располагать от уровня чистого пола на высоте 0,300 м. Исключения указаны на чертеже.
 - Размещение всех выводов и розеток согласовать со специалистами «Умный дом».
 - Размеры и характеристики радиаторов отопления согласовать со специалистами, предусмотреть терморегуляторы.
 - Датчики пожарной и охранной сигнализации и электровыводы для них разместить совместно со специалистами, предварительно вызвав их на объект.
 - Размещение розеток и электровыводов по высоте см. на развертках стен.

МСК 392.12.25–ЭП ПРЕМИУМ			
Эскизный дизайн–проект интерьера квартиры в г. Москва ЖК "Остров", ул. Нижние Мневники д. 7			
Мастер ваннаяПлан размещения электрооборудования.			
Дизайнер интерьера №1 Александр Батеньков	Стадия	Лист	Листов
	ЭП	100	120
		Подп.	Дата
ГАП	Батеньков А.С.		
Гл. дизайнер	Власова В.А.		
Гл. проектиров.	Луцькова В.Н.		
Разработал	Ильина Е.Е.		


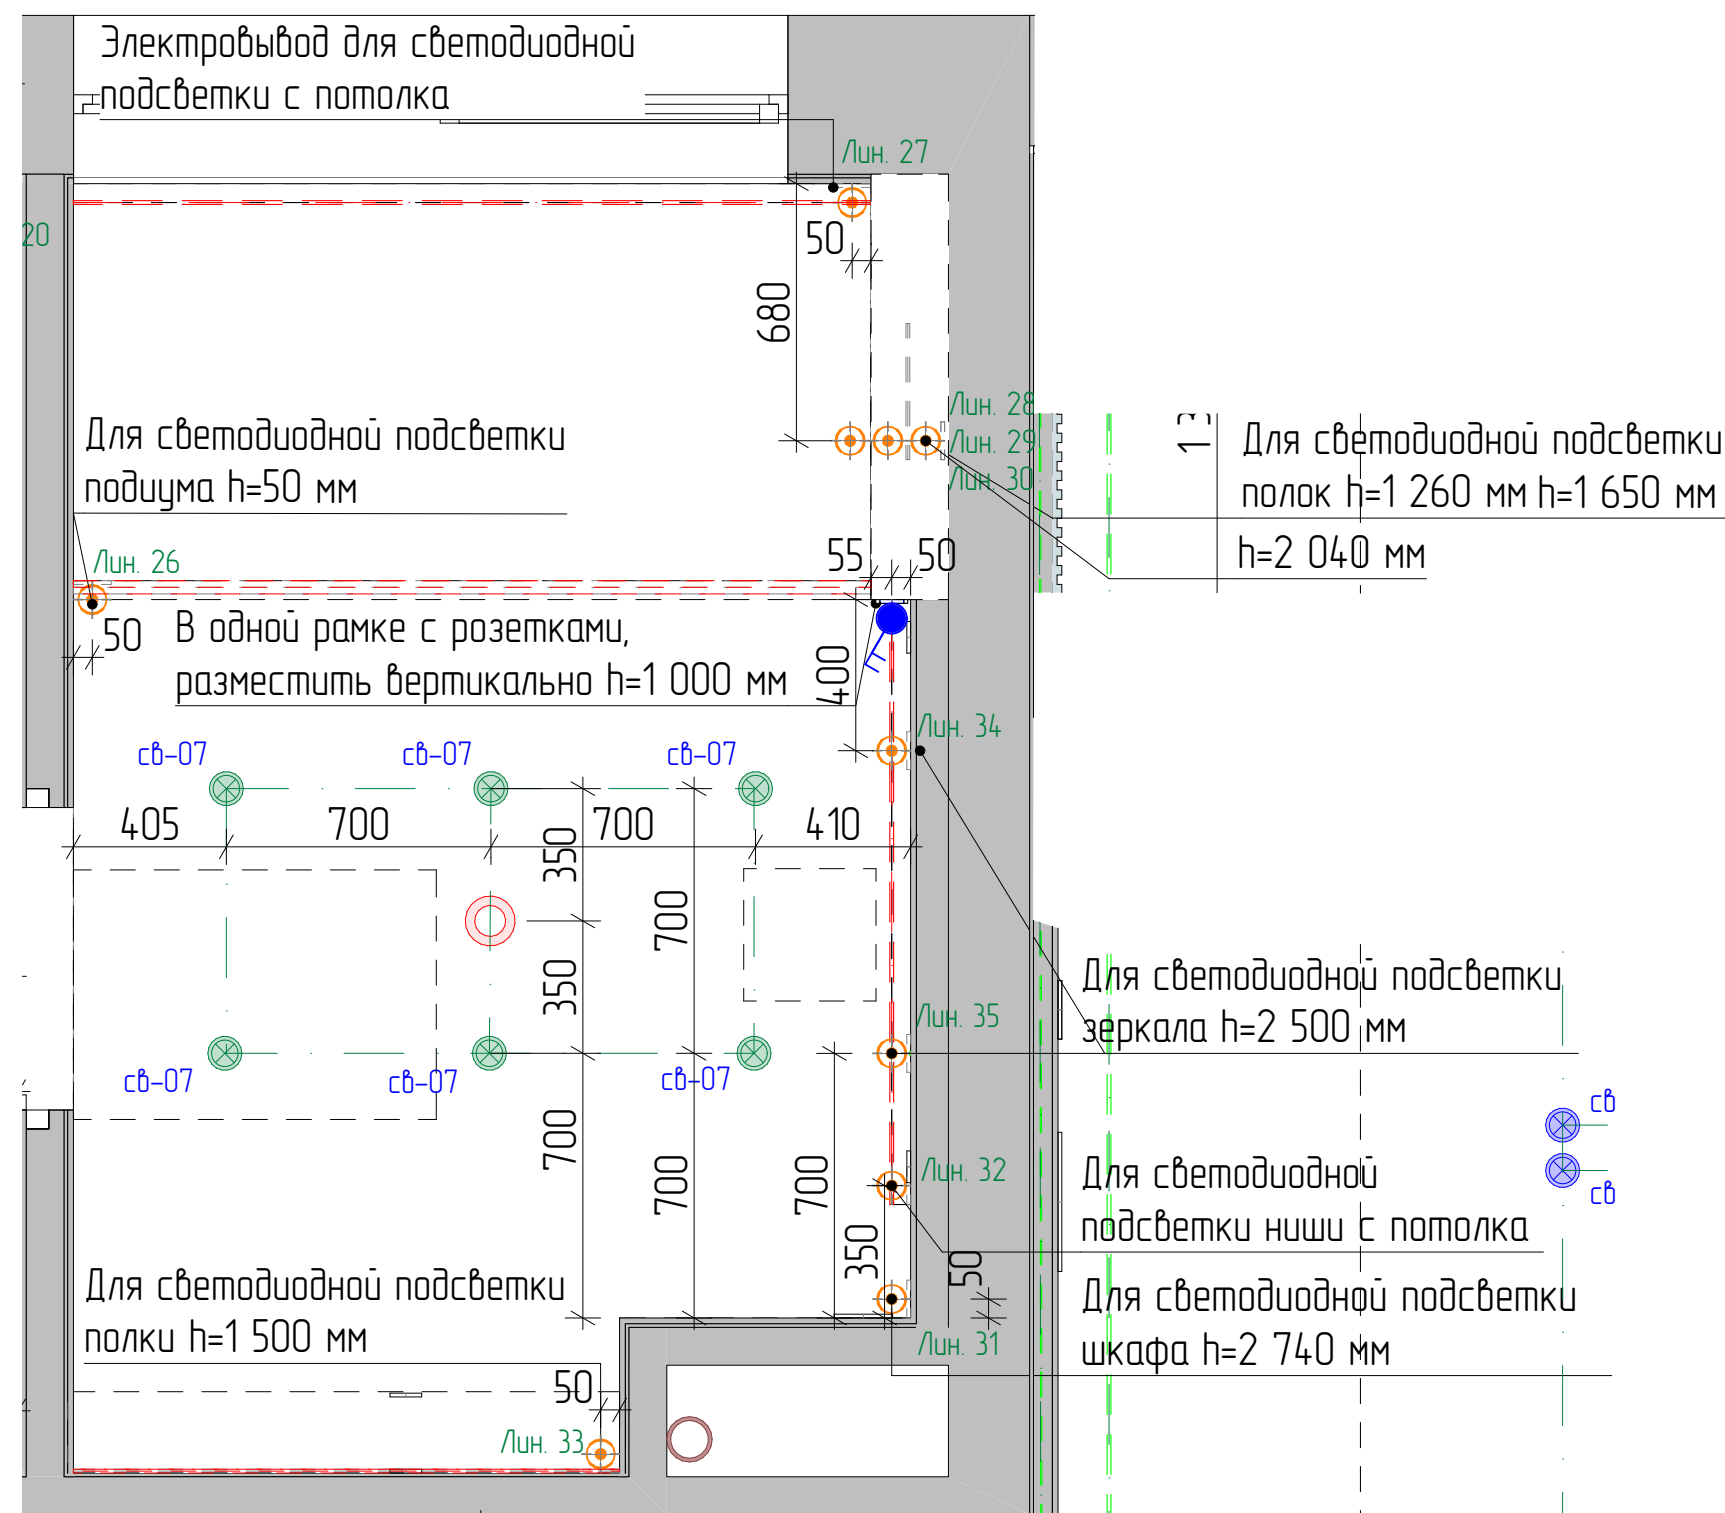


- Условные обозначения:
- Выход 220V
 - Выход электрокабеля для светодиодной ленты
 - Диффузор, вытяжка
 - Светильник точечный встраиваемый влагозащищенный
 - Светодиодная лента, влагозащищенная
 - Выключатель двухклавишный

Примечания:

- * – размеры уточнить по месту.
- Выключатели располагать от уровня чистого пола на высоте 0,900 м. Исключения указаны на чертеже.
- Светильники, встраиваемые в мебель, согласовать с изготовителями мебели.

МСК 392.12.25-ЭП ПРЕМИУМ			
Эскизный дизайн-проект интерьера квартиры в г. Москва ЖК "Остров", ул. Нижние Мневники д. 7			
Мастер ванная/План размещения освещения и выключателей.			
Дизайнер интерьера №1  Александр Батеньков	Стадия	Лист	Листов
	ЭП	101	120
		Подп.	Дата
ГАП	Батеньков А.С.		
Гл. дизайнер	Власова В.А.		
Гл. проектиров.	Луныкова В.Н.		
Разработал	Ильина Е.Е.		

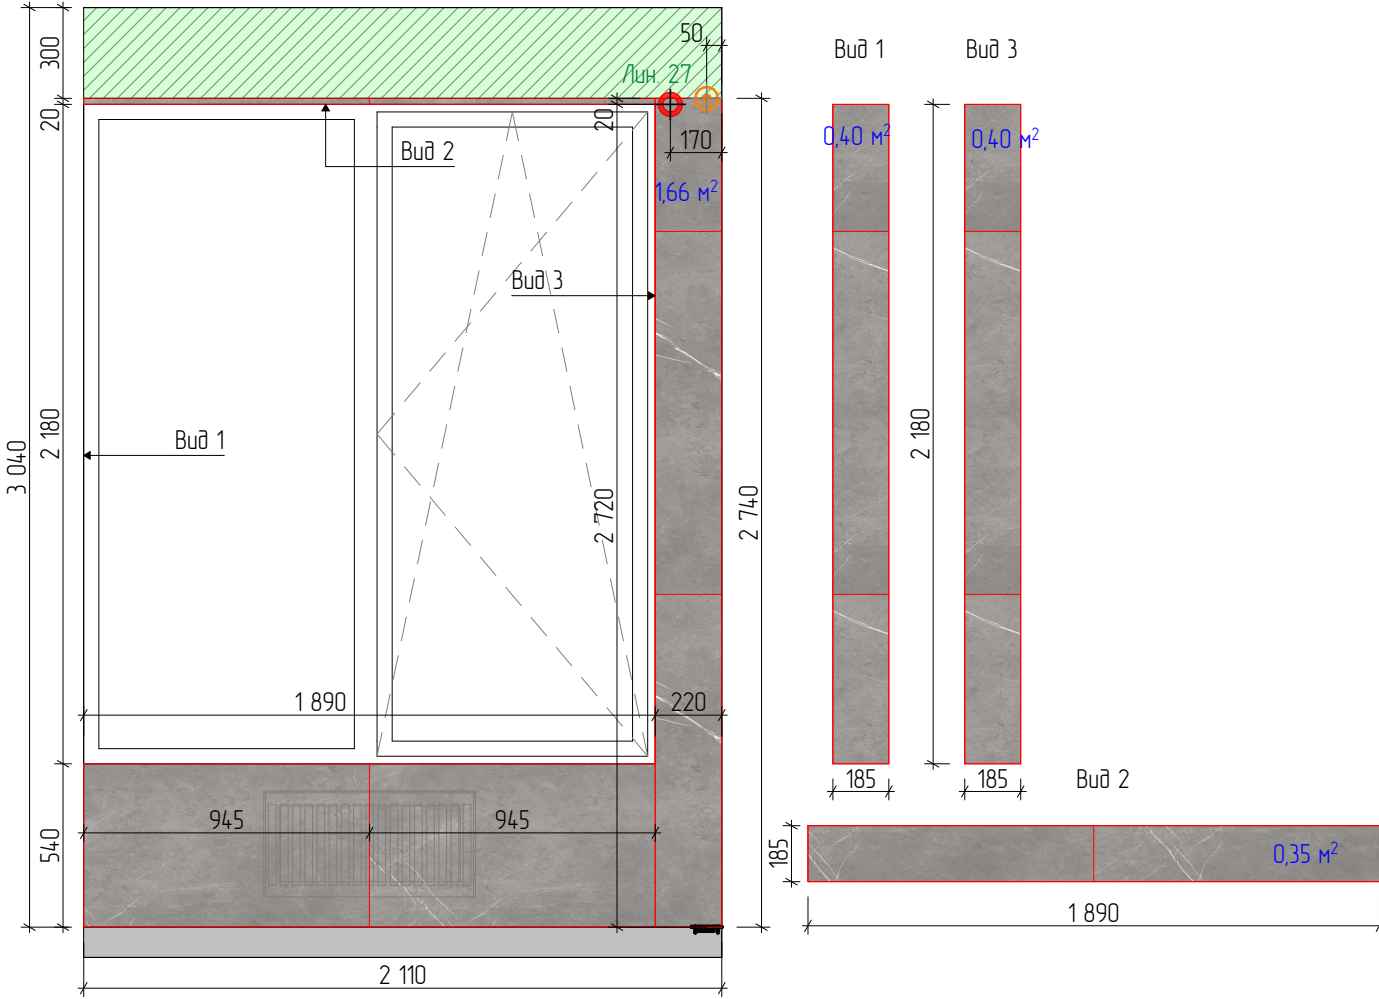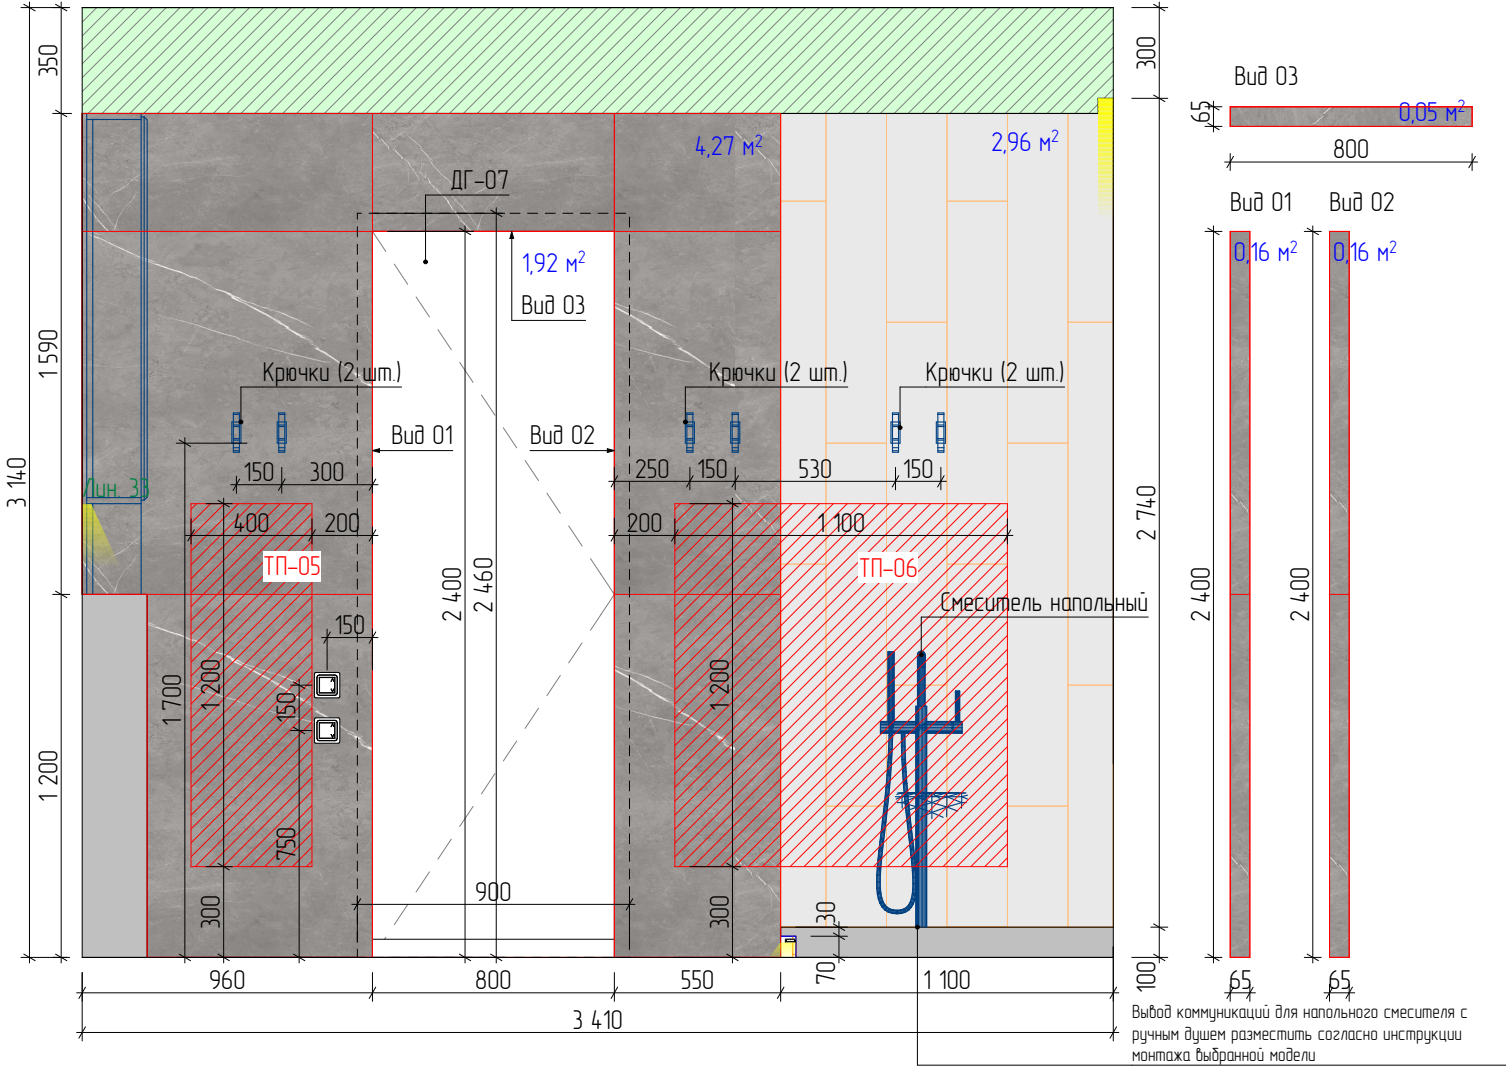






Условное обозначение:

- Керамогранит №01. Керамогранит. Изготовитель: Elegant Grey, кол-я: Forte Dei Marini, размер: 1200x1200 мм, толщину уточнить при закупе.
- Керамогранит №02. Керамогранит. Изготовитель: Nutmeg, кол-я: Woodslate Life, размер: 1200x200 мм, толщину уточнить при закупе.
- Направление и начало укладки
- Выход коммуникаций (ХВС, ГВС, канал-ция)
- Выход электрокабеля для светодиодной ленты
- Регулятор теплого пола
- Теплый пол, электрические маты

Примечания:


- *- размеры уточнить по месту после выполнения черновых отделочных работ.
- Регуляторы теплого пола располагать от уровня чистого пола на высоте 750 мм. Исключения указаны на чертеже.
- Размещение выводов для отопления согласовать со специалистами.
- Предусмотреть люк скрытого монтажа для доступа к коммуникациям, размещение уточнить по месту.
- Совместить швы плитки на смежных стенах и полу.
- Точную привязку выводов коммуникаций решить после выбора оборудования по инструкции монтажа.
- Предусмотреть гидроизоляцию пола с заведением на стену до потолка.
- ** - размер уточнить по инструкции монтажа оборудования.
- Розетки, выключатели, регуляторы теплого пола размещать по центру керамической плитки.
- Высоту проемов выполнить 2460 мм от уровня чистого пола. Уточнить после подбора и согласования модели дверей.
- Внутреннее наполнение мебели разработать со специалистами.
- Серым/синим цветом показаны размеры мебели. Мебель разработать со специалистами, размеры уточнить после выполнения чистовой отделки.

МСК 392.12.25-ЭП ПРЕМИУМ			
Эскизный дизайн-проект интерьера квартиры в г. Москва ЖК "Остров", ул. Нижние Мневники д. 7			
Мастер ваннаяРазвертки стен К-01, К-02.			
Дизайнер интерьера №1 Александр Батеньков	Стадия	Лист	Листов
	ЭП	102	120
		Подп.	Дата
ГАП	Батеньков А.С.		
Гл. дизайнер	Власова В.А.		
Гл. проектиров.	Луныкова В.Н.		
Разработал	Ильина Е.Е.		

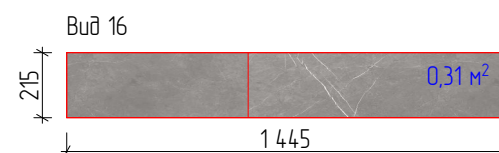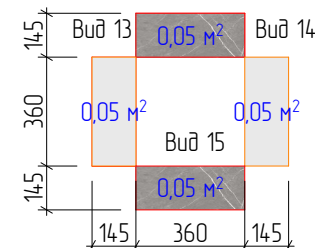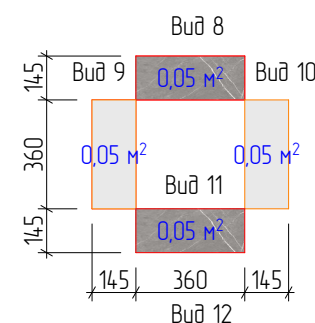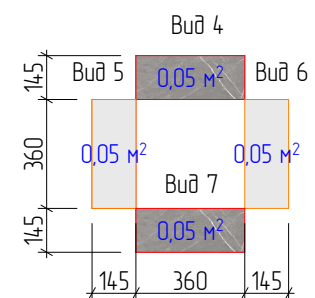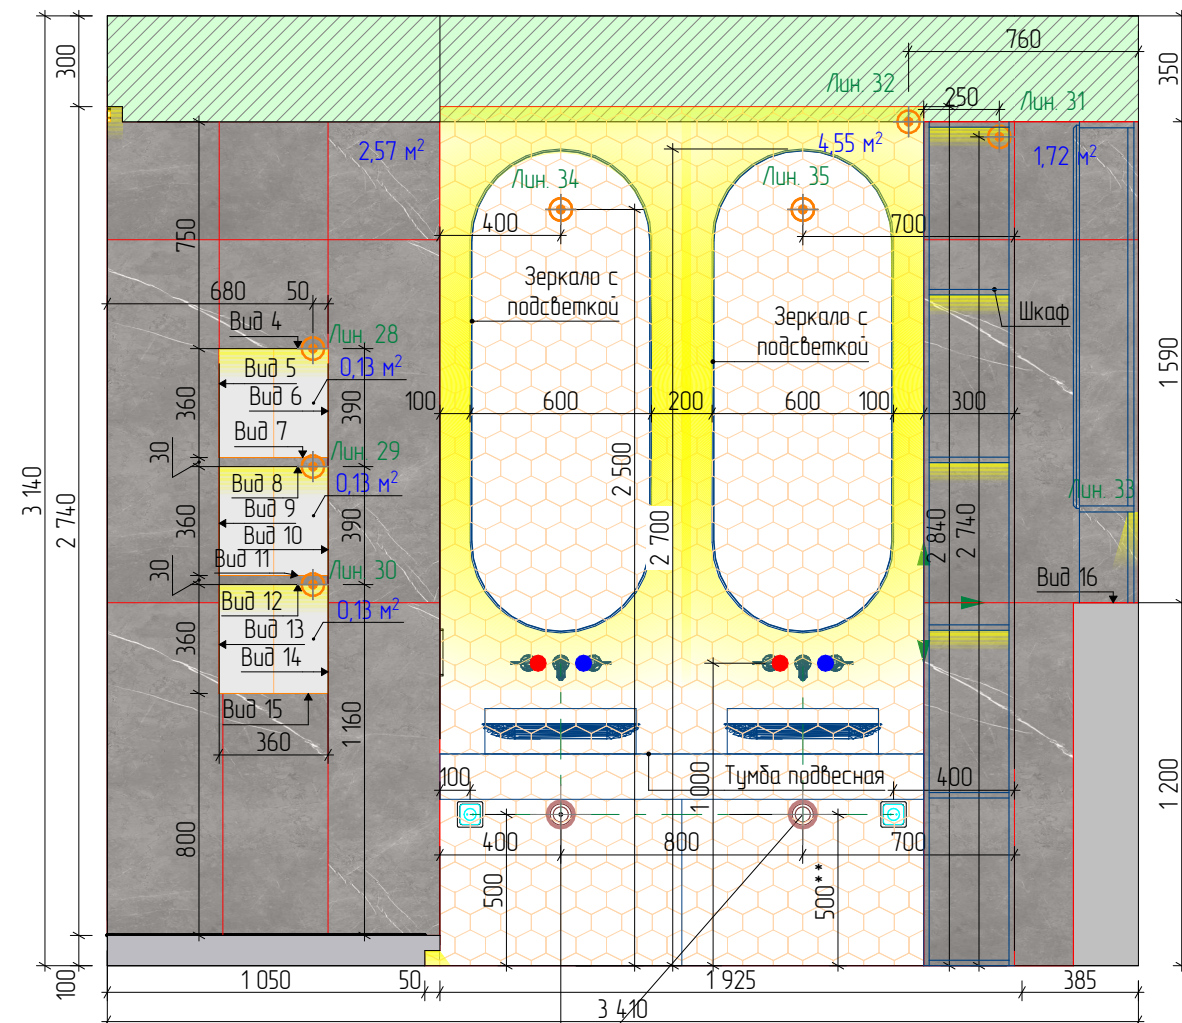


Примечания:

1. * – размеры уточнить по месту после выполнения черновых отделочных работ.
2. Выключатели располагать от уровня чистого пола на высоте 900 мм. Исключения указаны на чертеже.
3. Розетки располагать от уровня чистого пола на высоте 300 мм. Исключения указаны на чертеже.
4. Предусмотреть люк скрытого монтажа для доступа к коммуникациям, размещение уточнить по месту.
5. Совместить швы плитки на смежных стенах и полу.
6. Точную привязку выводов коммуникаций решить после выбора оборудования по инструкции монтажа.
7. Предусмотреть гидроизоляцию пола с заведением на стену до потолка.
8. ** – размещение вывода 220V для электрического полотенцесушителя уточнить после подбора модели по технической документации.
9. ** – размер уточнить по инструкции монтажа оборудования.
10. Розетки, выключатели, регуляторы теплого пола размещать по центру керамической плитки.
11. Внутреннее наполнение мебели разработать со специалистами.
12. Серым/синим цветом показаны размеры мебели. Мебель разработать со специалистами, размеры уточнить после выполнения чистовой отделки.

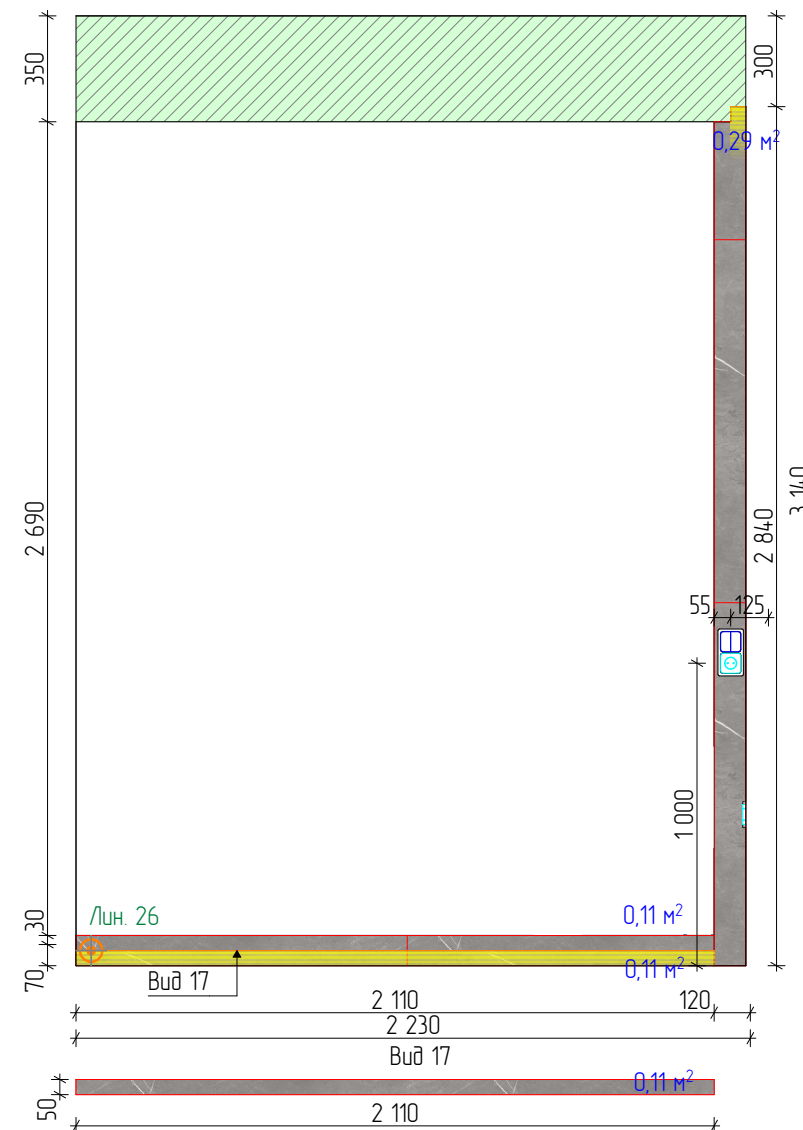

Условное обозначение:

-  Керамогранит №01. Керамогранит. Изготовитель: Elegant Grey, кол-я: Forte Dei Marmi, размер: 1200x1200 мм, толщину уточнить при закупе.
-  Керамогранит №02. Керамогранит. Изготовитель: Nutmeg, кол-я: Woodslate Life, размер: 1200x200 мм, толщину уточнить при закупе.
-  Керамогранит №03. Керамогранит, размер и толщину уточнить при закупе.
-  Покраска №2. Выполнить по подготовленной поверхности (стеклохолст*). Цвет при выборе образца (белый*).
-  Направление и начало укладки
-  Вывод коммуникаций (ХВС, ГВС, канал-ция)
-  Вывод электрокабеля для светодиодной ленты
-  Розетка 220 V, влагозащищенная IP44 и выше
-  Выключатель двухклавишный
-  Вывод 220 V

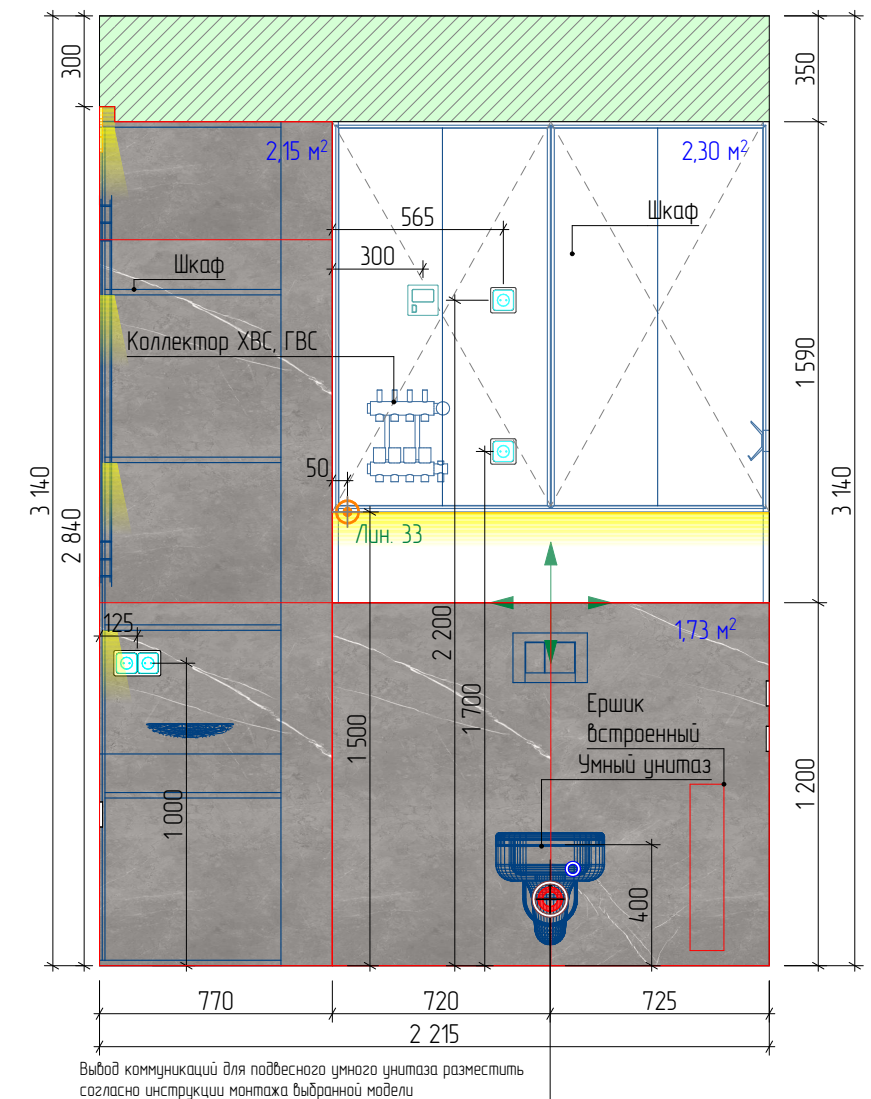

МСК 392.12.25-ЭП ПРЕМИУМ			
Эскизный дизайн-проект интерьера квартиры в г. Москва ЖК "Остров", ул. Нижние Мневники д. 7			
Мастер баннаяРазвертки стен К-03, К-04, К-05.			
Дизайнер интерьера  №1 Александр Батеньков	Студия	Лист	Листов
	ЭП	103	120
		Подп.	Дата
ГАП	Батеньков А.С.		
Гл. дизайнер	Власова В.А.		
Гл. проектиров.	Луныкова В.Н.		
Разработал	Ильина Е.Е.		

Ведомость отделочных материалов.				
№	Обозначение	Наименование	Кол-во	Примечание
Пол:				
1		Покрытие №03. Керамогранит. Изготовитель: Nutmeg, кол-я: Woodslate Life, размер: 1200х200 мм, толщину уточнить при закупе.	4,50 22	м² укладки шт.
2		Покрытие №02. Керамогранит. Изготовитель: Elegant Grey, кол-я: Forte Dei Marmi, размер: 1200х1200 мм, толщину уточнить при закупе.	2,22 2	м² укладки шт.
Стены:				
3		Покраска №3. Влагостойкая. Выполнить по оштукатуренной поверхности. Цвет при выборе образца (белый*).	2,30	м²
4		Керамогранит №02. Керамогранит. Изготовитель: Nutmeg, кол-я: Woodslate Life, размер: 1200х200 мм, толщину уточнить при закупе.	3,65 19	м² укладки шт.
5		Керамогранит №01. Керамогранит. Изготовитель: Elegant Grey, кол-я: Forte Dei Marmi, размер: 1200х1200 мм, толщину уточнить при закупе.	16,49 18*	м² укладки шт.
6		Керамогранит №03. Керамогранит, размер и толщину уточнить при закупе.	4,55	м² укладки
Подоконник:				
7		Подоконник №1. Искусственный камень. Цвет при выборе образца.	0,35	м²

МСК 392.12.25–ЭП ПРЕМИУМ			
Эскизный дизайн–проект интерьера квартиры в г. Москва ЖК “Остров”, ул. Нижние Мневники д. 7			
Мастер ваннаяВедомость отделочных материалов.			
Дизайнер интерьера  №1 Александр Батеньков	Стадия	Лист	Листов
	ЭП	104	120
		Подп.	Дата
ГАП	Батеньков А.С.		
Гл. дизайнер	Власова В.А.		
Гл. проектиров.	Луцькова В.Н.		
Разработал	Ильина Е.Е.		

Примечания.

[illegible]

МСК 392.12.25-ЭП ПРЕМИУМ			
Эскизный дизайн-проект интерьера квартиры в г. Москва ЖК "Остров", ул. Нижние Мневники д. 7			
Примечания.			
Дизайнер интерьера №1  Александр Батеньков	Стадия	Лист	Листов
	ЭП	105	120
		Подп.	Дата
ГАП	Батеньков А.С.		
Гл. дизайнер	Власова В.А.		
Гл. проектиров.	Луныкова В.Н.		