



МСК 392.12.25-ЭП ПРЕМИУМ			
Эскизный дизайн-проект интерьера квартиры в г. Москва ЖК "Остров", ул. Нижние Мневники д. 7			
Мастер спальни. Видовые точки.			
Дизайнер интерьера  Александр Батеньков	Стадия	Лист	Листов
	ЭП	82	120
		Подп.	Дата
ГАП	Батеньков А.С.		
Гл. дизайнер	Власова В.А.		
Гл. проектиров.	Луныкова В.Н.		
Разработал	Ильина Е.Е.		



МСК 392.12.25-ЭП ПРЕМИУМ			
Эскизный дизайн-проект интерьера квартиры в г. Москва ЖК "Остров", ул. Нижние Мневники д. 7			
Мастер спальни. Видовые точки.			
Дизайнер интерьера  Александр Батеньков	Стадия	Лист	Листов
	ЭП	83	120
		Подп.	Дата
ГАП	Батеньков А.С.		
Гл. дизайнер	Власова В.А.		
Гл. проектиров.	Луныкова В.Н.		
Разработал	Ильина Е.Е.		




МСК 392.12.25-ЭП ПРЕМИУМ			
Эскизный дизайн-проект интерьера квартиры в г. Москва ЖК "Остров", ул. Нижние Мневники д. 7			
Мастер спальня. Видовые точки.			
Дизайнер интерьера  Александр Батеньков	Стадия	Лист	Листов
	ЭП	84	120
		Подп.	Дата
Г.АП	Батеньков А.С.		
Гл. дизайнер	Власова В.А.		
Гл. проектиров.	Луныкова В.Н.		
Разработал	Ильина Е.Е.		



МСК 392.12.25-ЭП ПРЕМИУМ			
Эскизный дизайн-проект интерьера квартиры в г. Москва ЖК "Остров", ул. Нижние Мневники д. 7			
Мастер спальня. Видовые точки.			
Дизайнер интерьера №1 Александр Батеньков	Стадия	Лист	Листов
	ЭП	85	120
		Подп.	Дата
ГАП	Батеньков А.С.		
Гл. дизайнер	Власова В.А.		
Гл. проектиров.	Луныкова В.Н.		
Разработал	Ильина Е.Е.		




МСК 392.12.25-ЭП ПРЕМИУМ			
Эскизный дизайн-проект интерьера квартиры в г. Москва ЖК "Остров", ул. Нижние Мневники д. 7			
Мастер спальни. Видовые точки.			
Дизайнер интерьера  Александр Батеньков	Стадия	Лист	Листов
	ЭП	86	120
		Подп.	Дата
ГАП	Батеньков А.С.		
Гл. дизайнер	Власова В.А.		
Гл. проектиров.	Луныкова В.Н.		
Разработал	Ильина Е.Е.		

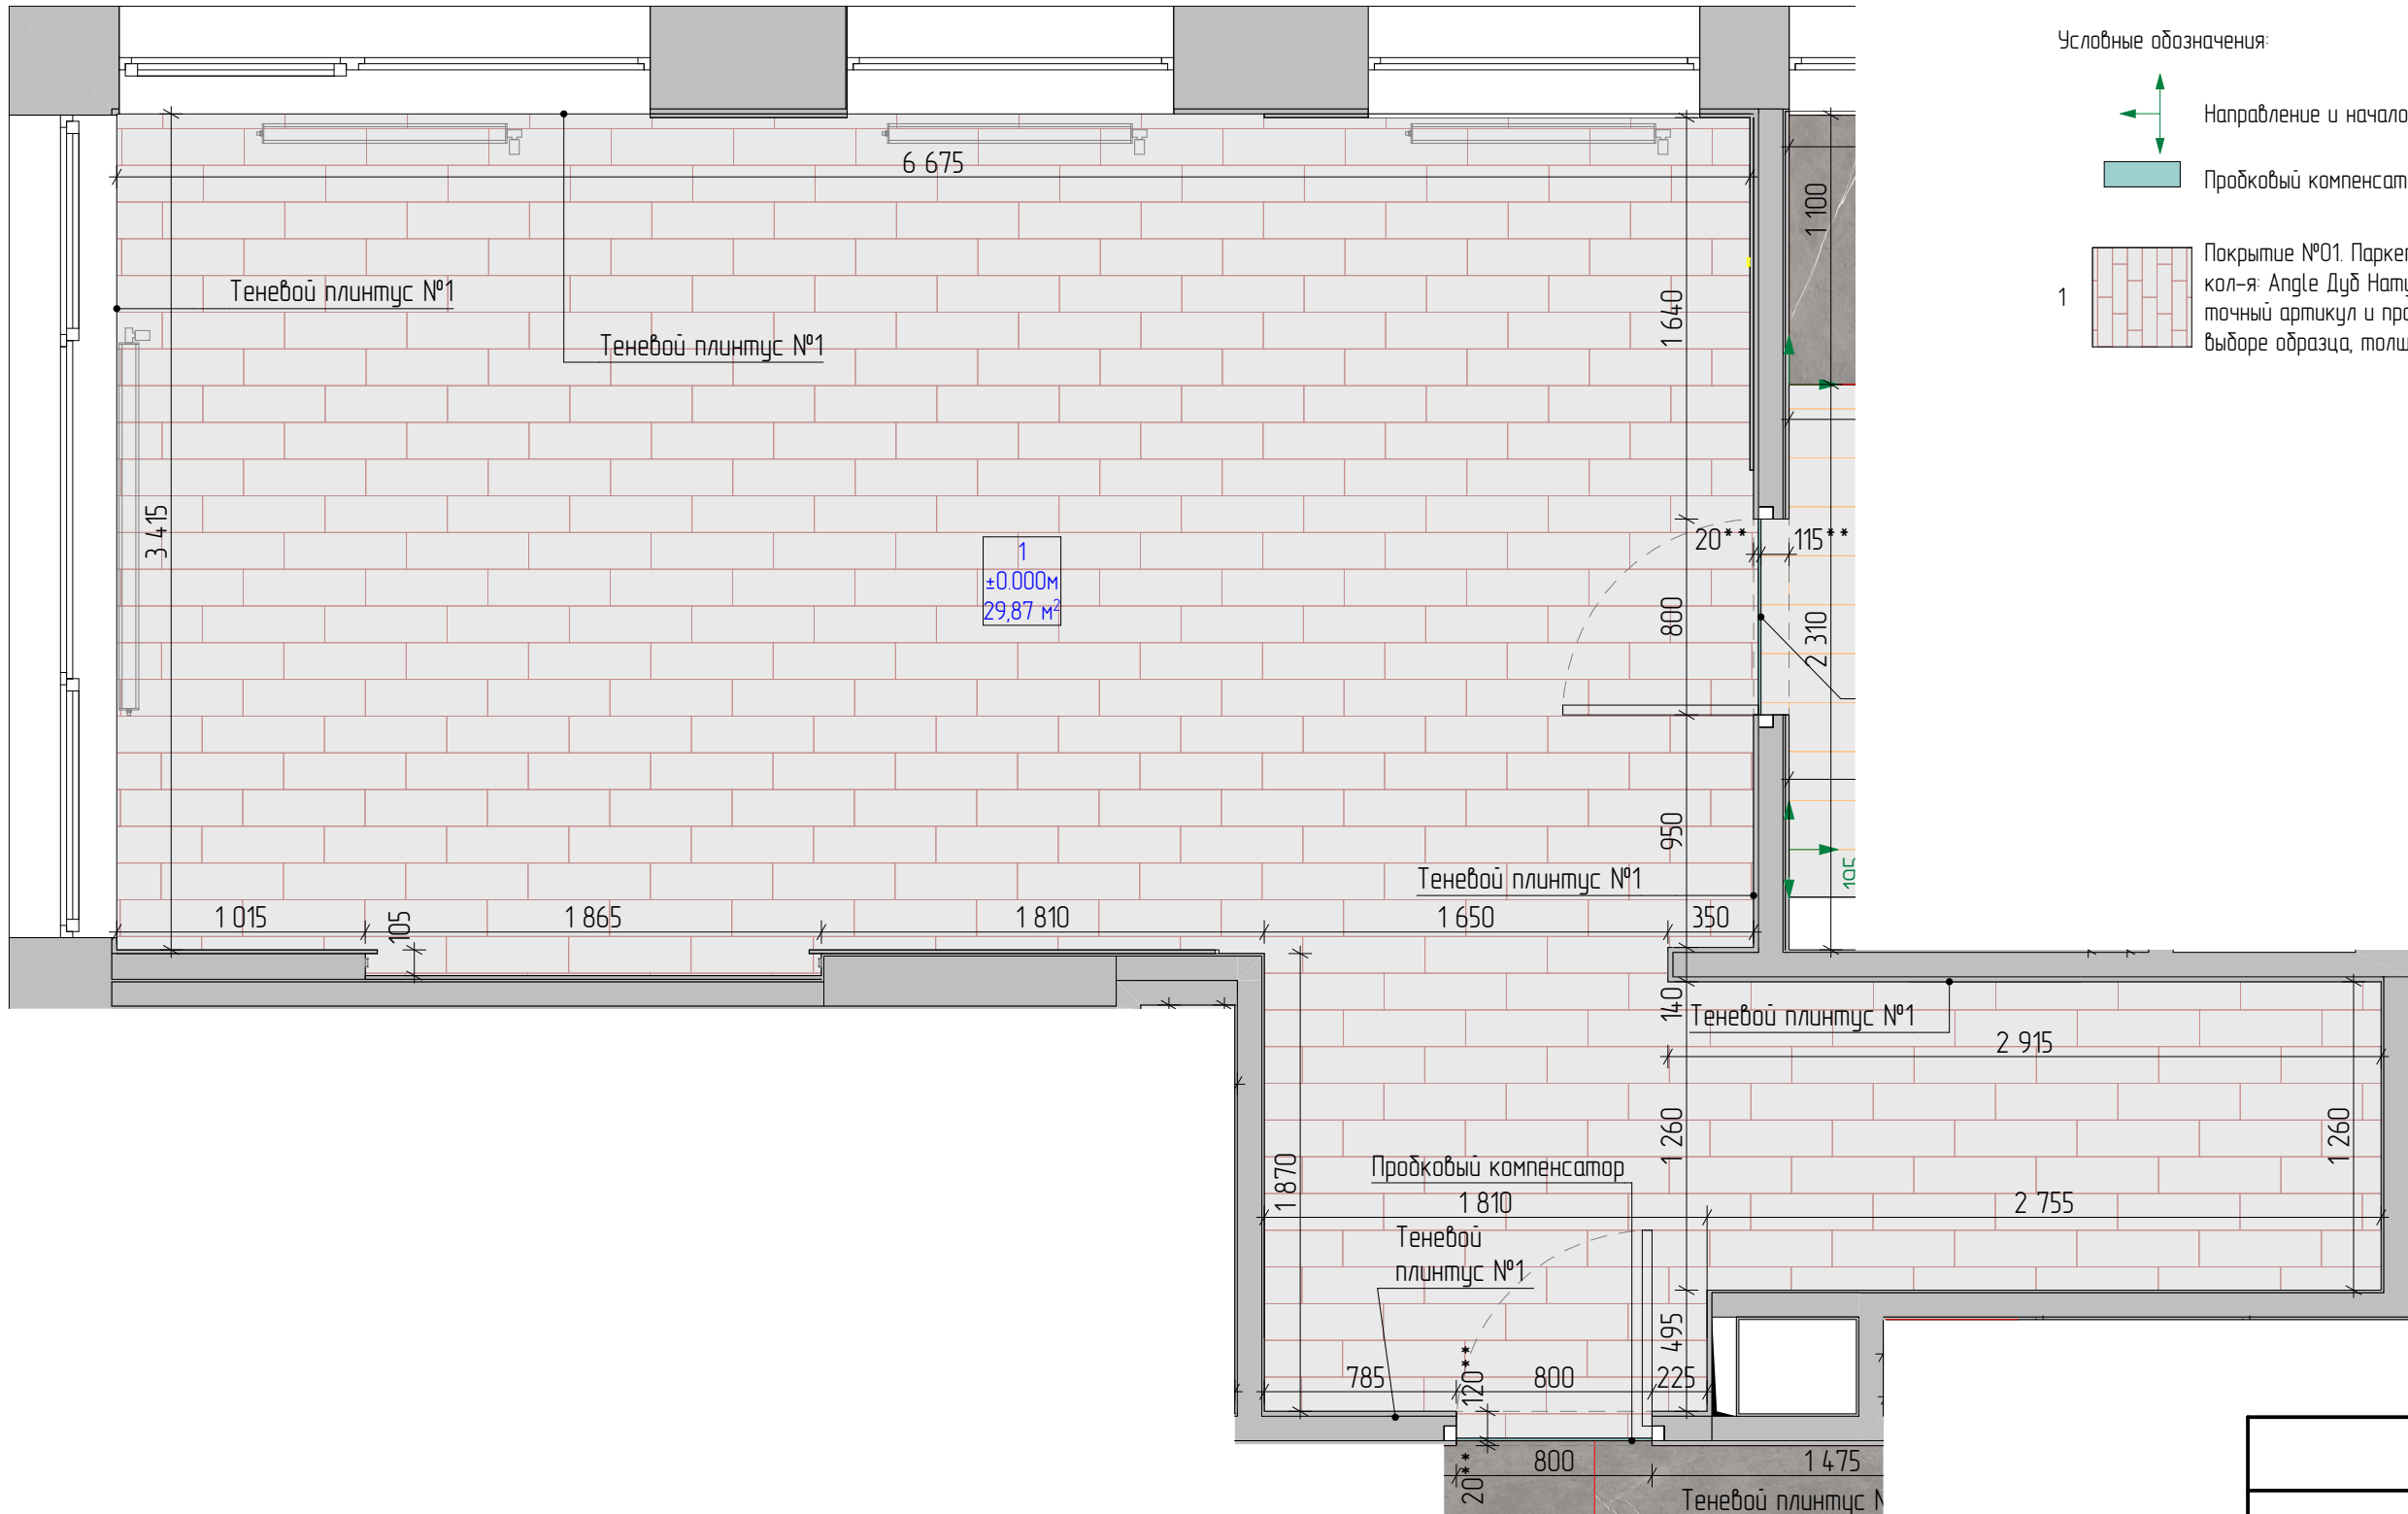

Примечания:

- * – размеры уточнить по месту после выполнения черновых отделочных работ.
- За отметку ±0,000 принят уровень чистого пола.
- При монтаже напольных покрытий уточнить необходимость устройства дверных проемов с порогом.
- * – размеры уточнить по месту после выполнения черновых отделочных работ и установки дверей со скрытой коробкой.
- ** – размер уточнить по месту в зависимости от точного расположения полотна двери, стыковка двух разных напольных покрытий должна проходить точно по центру вдоль дверного полотна.

МСК 392.12.25–ЭП ПРЕМИУМ			
Эскизный дизайн–проект интерьера квартиры в г. Москва ЖК "Остров", ул. Нижние Мневники д. 7			
Мастер спальня.План отделки пола.			
Дизайнер интерьера  №1 Александр Батеньков	Стадия	Лист	Листов
	ЭП	87	120
		Подп.	Дата
ГАП	Батеньков А.С.		
Гл. дизайнер	Власова В.А.		
Гл. проектиров.	Луцкова В.Н.		
Разработал	Ильина Е.Е.		

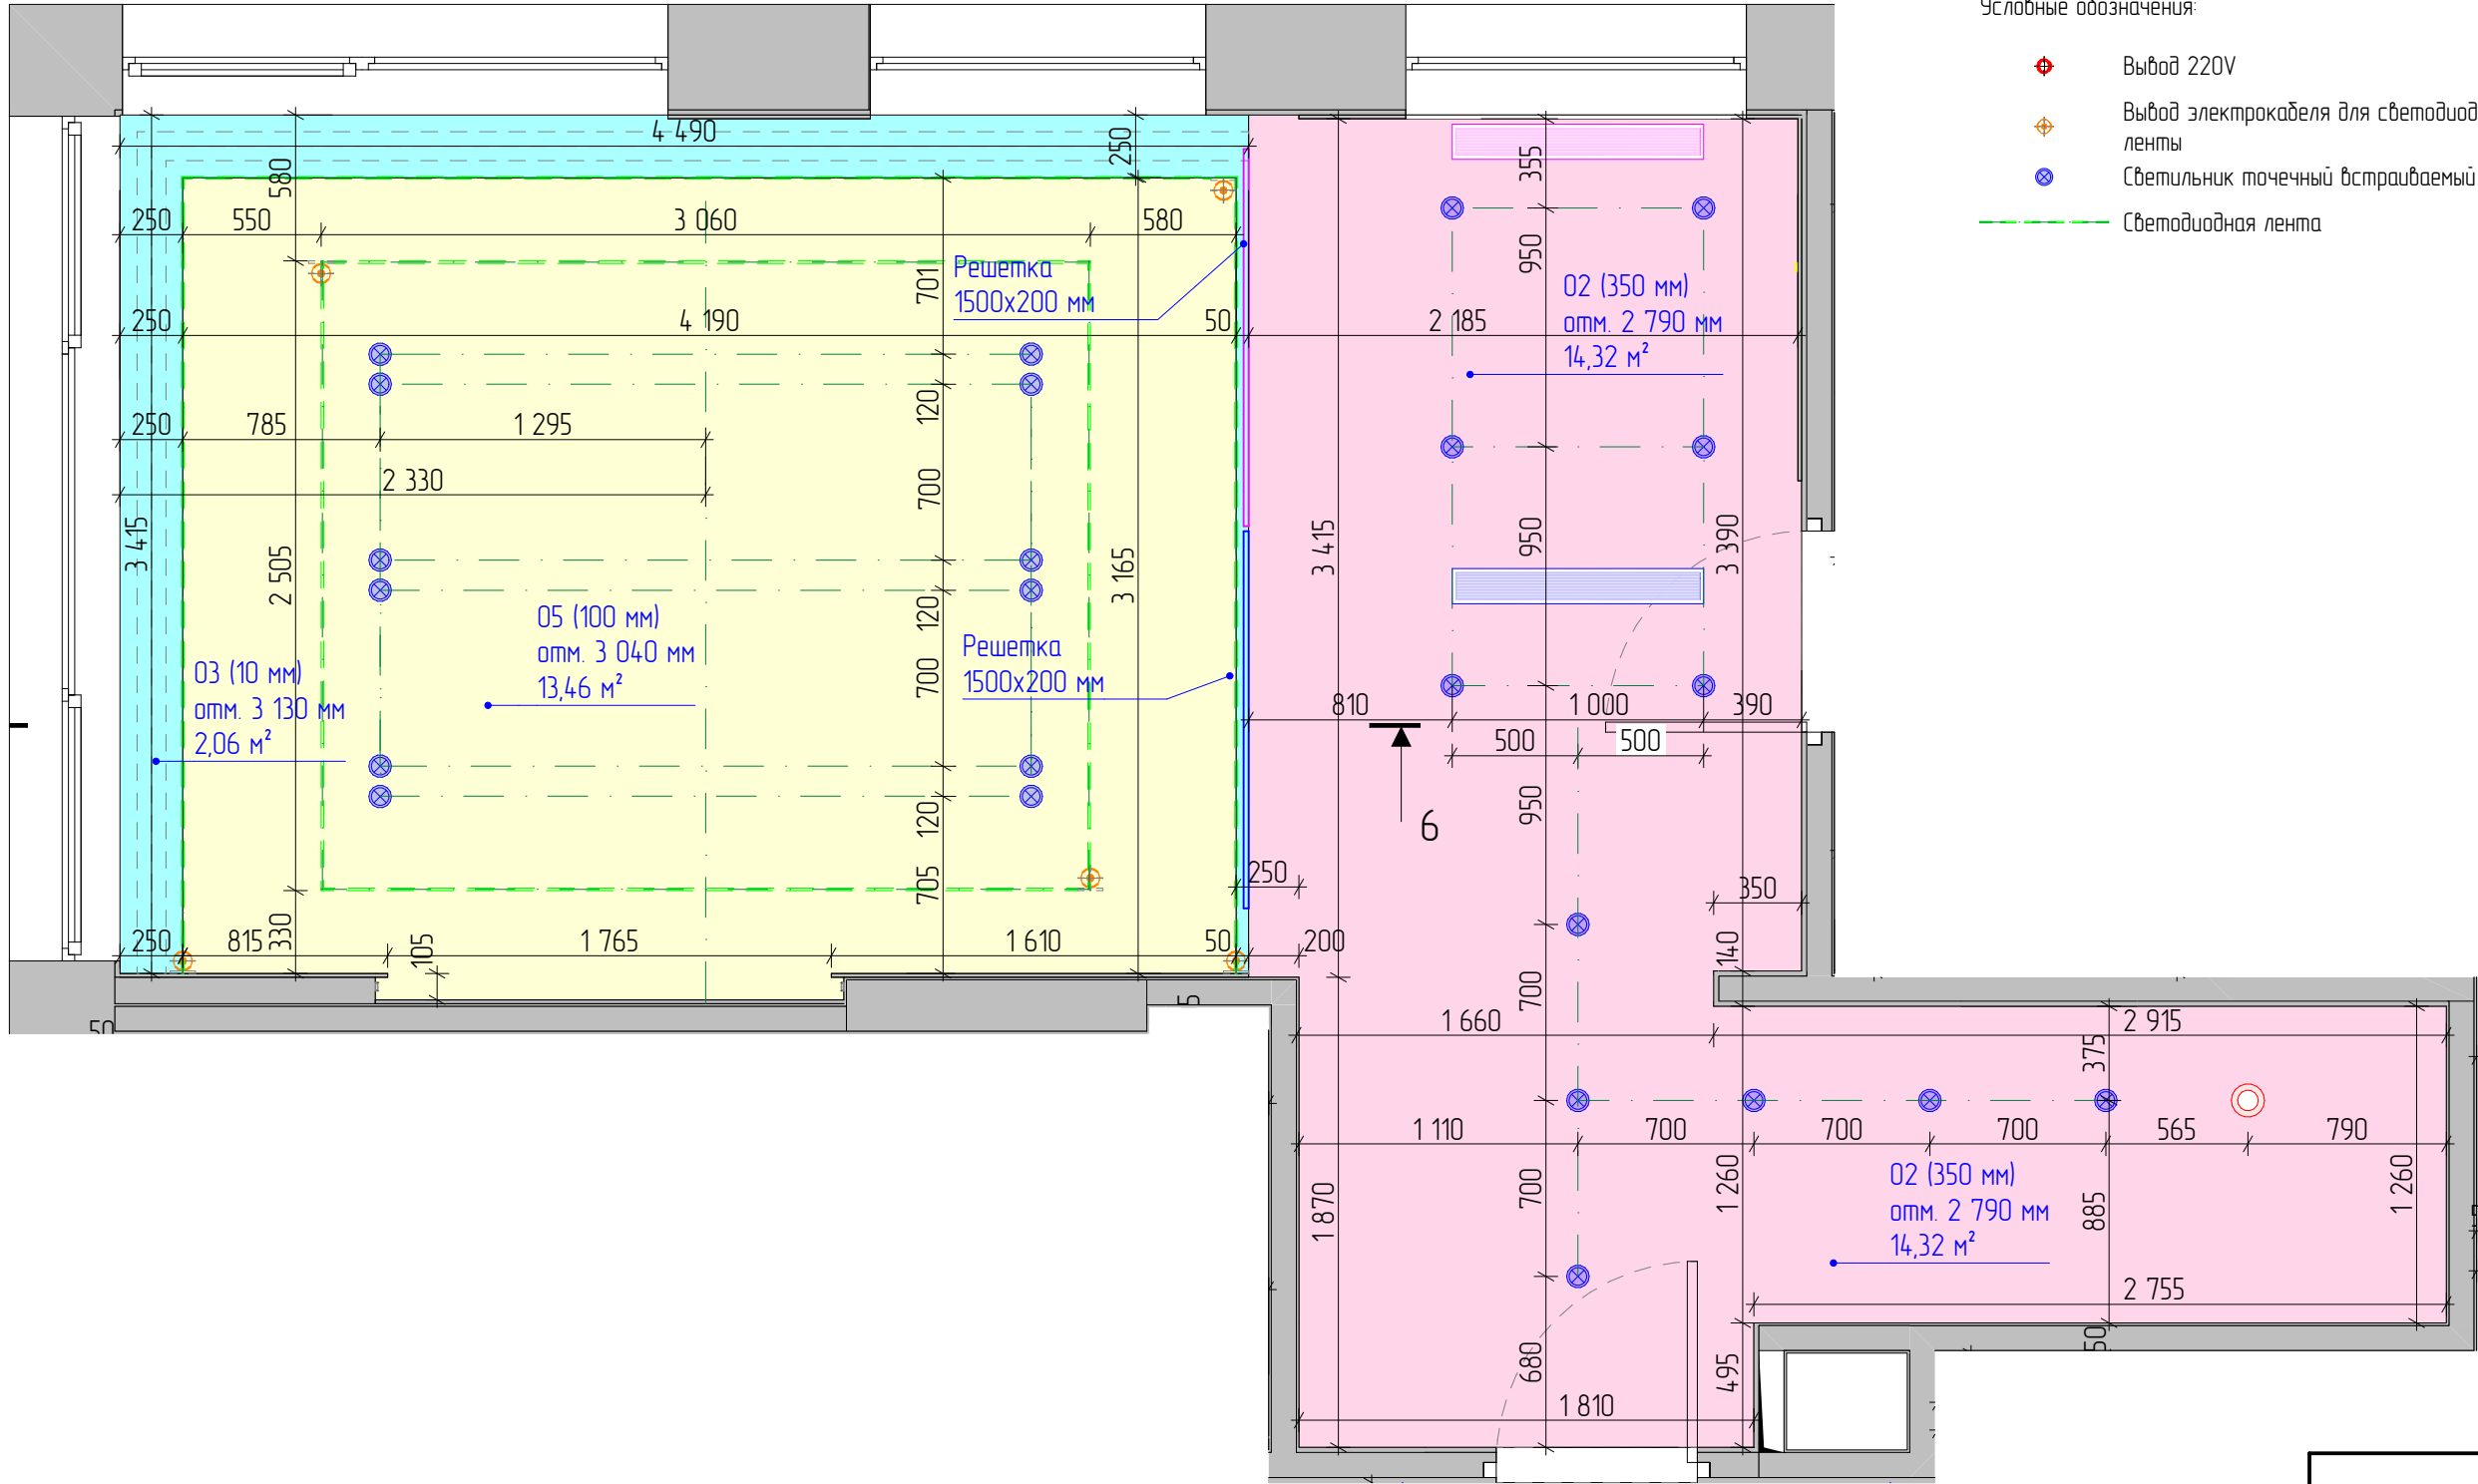

- Условные обозначения:
- Выход 220V
 - Выход электрокабеля для светодиодной ленты
 - Светильник точечный встраиваемый
 - Светодиодная лента

Примечания:

- * – размеры уточнить по месту после выполнения черновых работ.
- Выполнить уровни потолка из влагостойкого ГКЛ для предотвращения деформации потолка при затоплении.
- Высоту уровней потолка отсчитывать от существующей ж/б плиты перекрытия помещения.
- Предусмотреть усиление потолка фанерой в местах крепления потолочных карнизов для штор.
- От вытяжки провести вентиляционный короб до общедомового канала в конструкции потолка, уточнить по месту со специалистами и заказчиком.
- Шумоизоляцию разработать со специалистами, уточнить состав и толщину слоев шумоизоляционных материалов. Уточнить необходимость устройства с заказчиком.

Условные потолки				
№	Обозначение	Опуск	Примечания	Площадь м2
02		350	Потолок ГК/В. Окрасить в цвет выбранного образца (белый) по армирующему материалу (стеклохолст "паутинка").	14,32
03		10	Выворачивать и оштукатурить существующий потолок. Окрасить в цвет выбранного образца (белый) по армирующему материалу (стеклохолст "паутинка"). Размер ниши уточнить.	2,06
05		100	Потолок ГК/В. Окрасить в цвет выбранного образца (белый) по армирующему материалу (стеклохолст "паутинка").	13,46

МСК 392.12.25-ЭП ПРЕМИУМ

Эскизный дизайн-проект интерьера квартиры в г. Москва ЖК "Остров", ул. Нижние Мневники д. 7

Мастер спальни.План отделки потолка.

Дизайнер
интерьера




№1

Александр
Батеньков

Стадия	Лист	Листов
ЭП	88	120
	Подп.	Дата

ГАП	Батеньков А.С.		
Гл. дизайнер	Власова В.А.		
Гл. проектиров.	Луныкова В.Н.		
Разработал	Ильина Е.Е.		

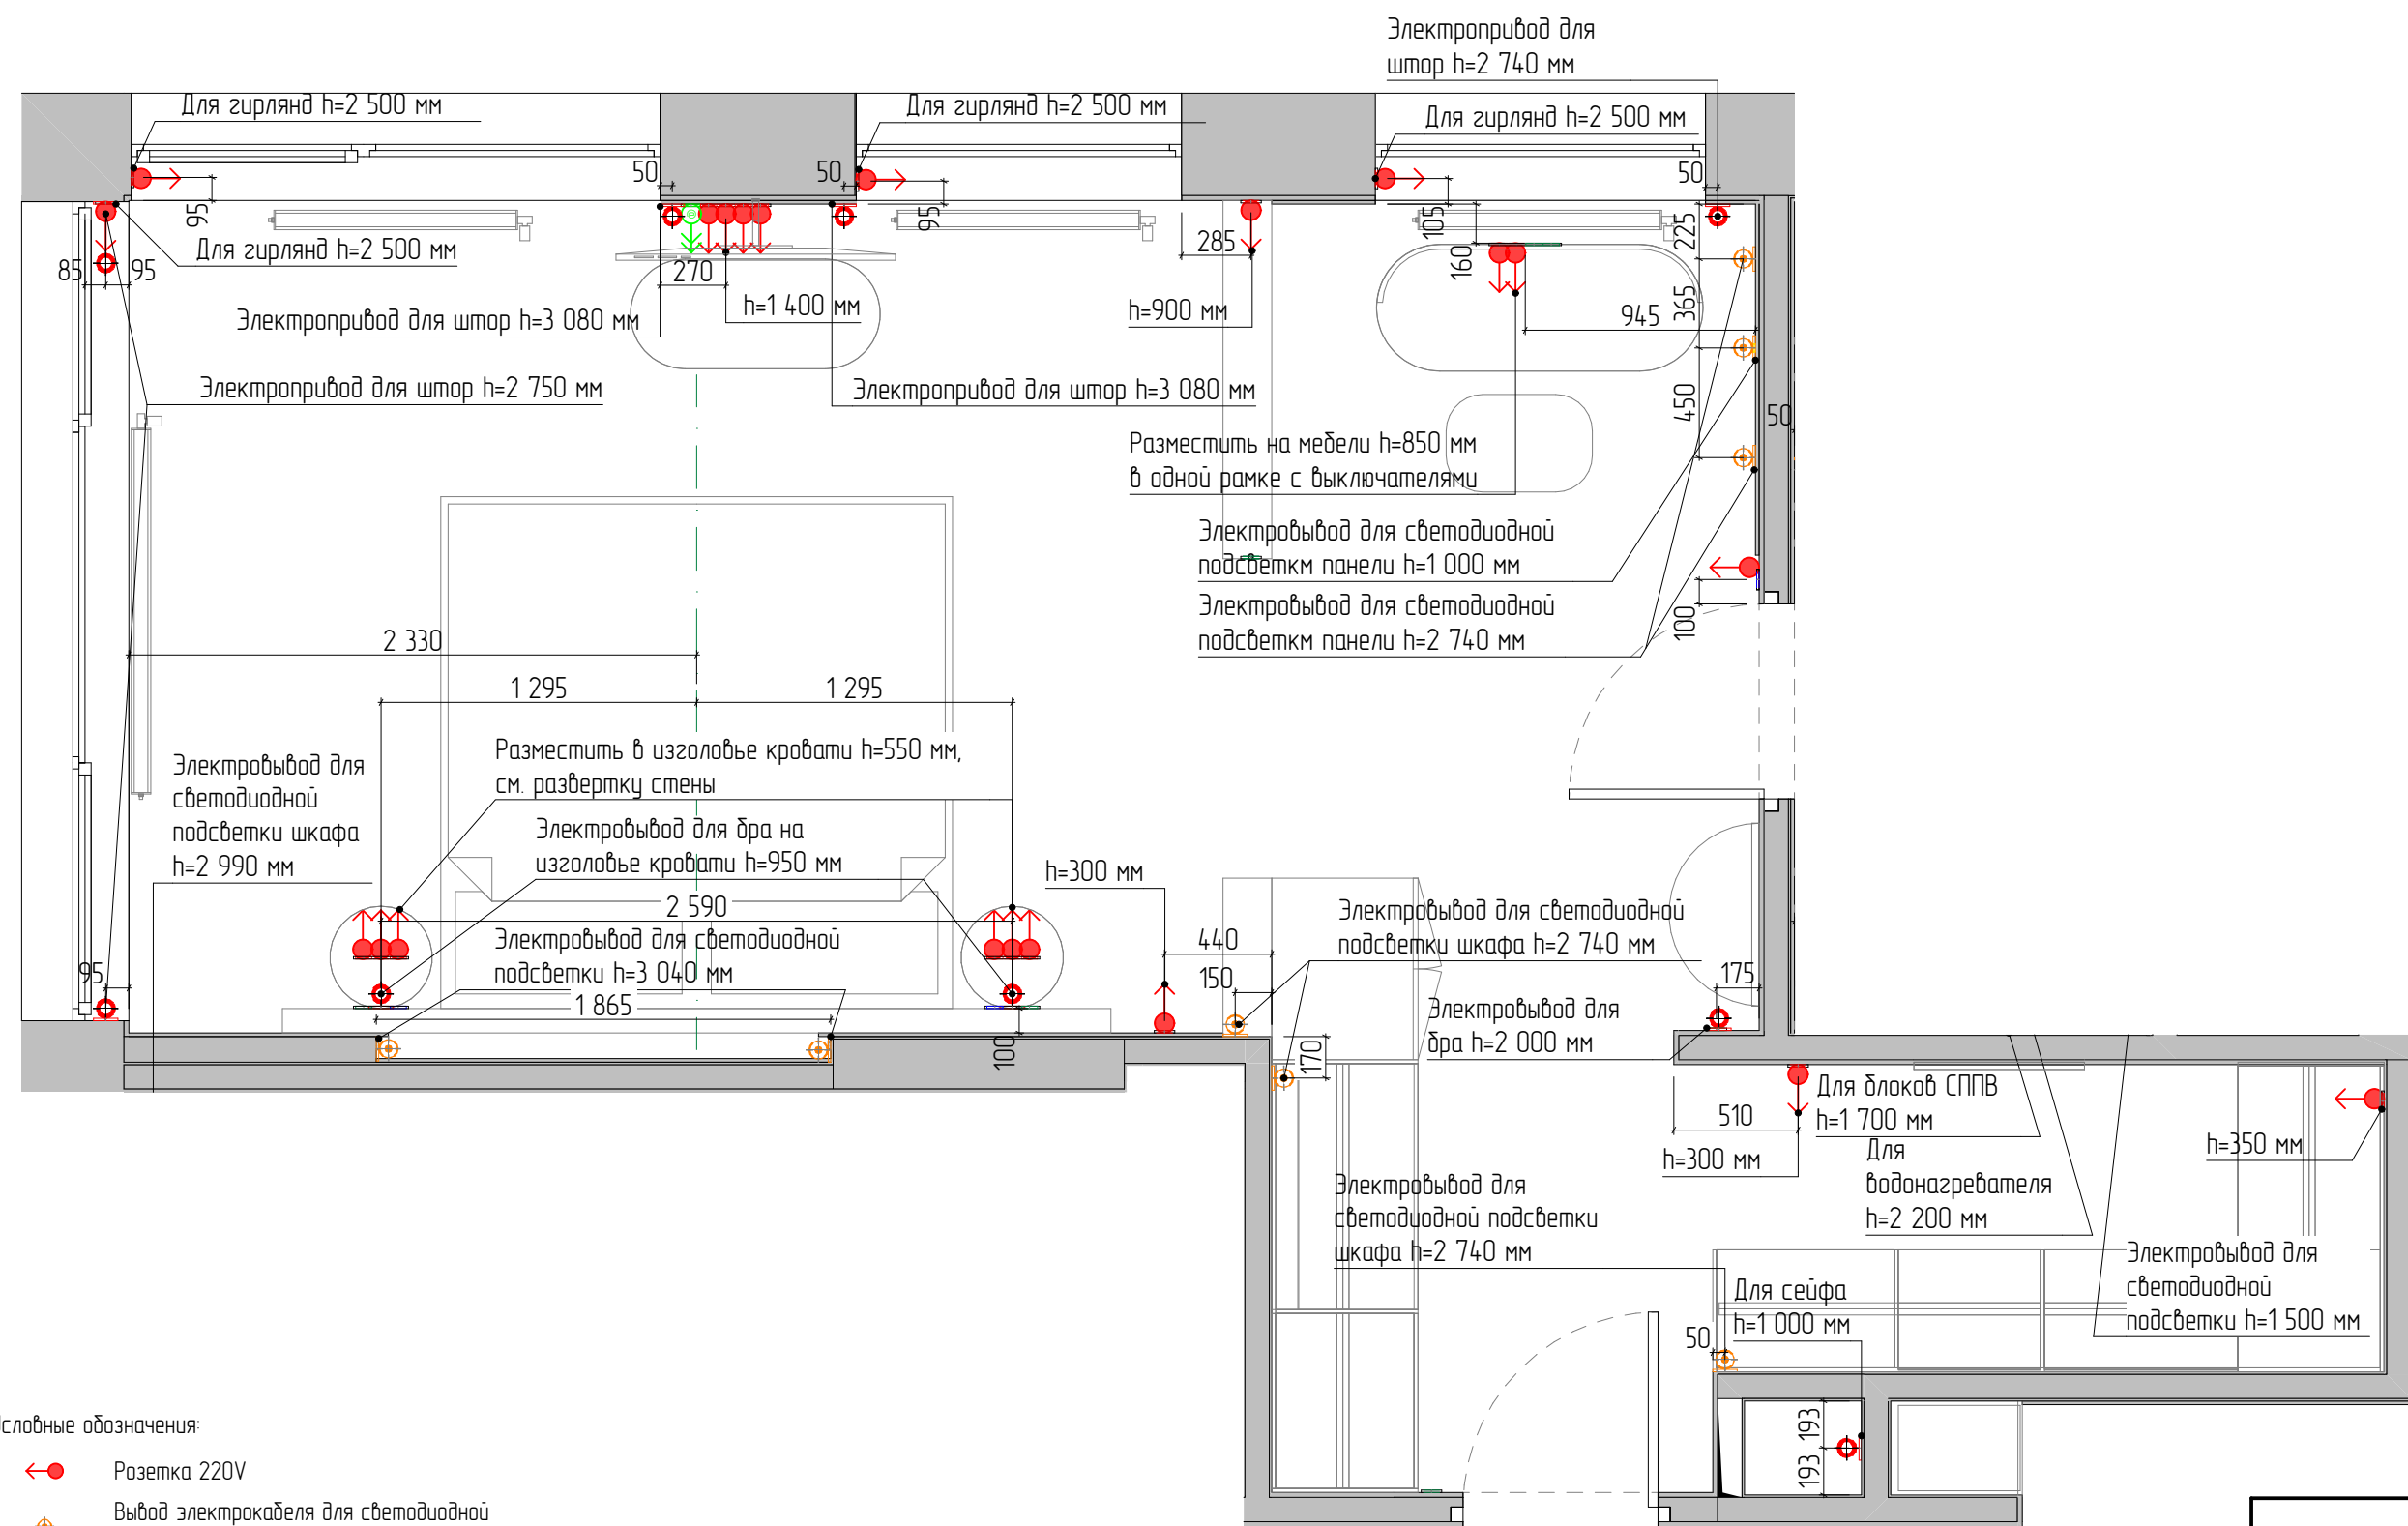

Условные обозначения:

- ←● Розетка 220V
- ◆ Вывод электрокабеля для светодиодной ленты
- ⊗ Вывод электрокабеля для варочной поверхности
- ⊕ Вывод 220V

Примечания:

- * – размеры уточнить по месту.
- Розетки располагать от уровня чистого пола на высоте 0,300 м. Исключения указаны на чертеже.
- Размещение всех выводов и розеток согласовать со специалистами «Умный дом».
- Размеры и характеристики радиаторов отопления согласовать со специалистами, предусмотреть терморегуляторы.
- Датчики пожарной и охранной сигнализации и электровыводы для них разместить совместно со специалистами, предварительно вызвав их на объект.
- Размещение розеток и электровыводов по высоте см. на развертках стен.

МСК 392.12.25–ЭП ПРЕМИУМ			
Эскизный дизайн–проект интерьера квартиры в г. Москва ЖК "Остров", ул. Нижние Мневники д. 7			
Мастер спальни. План размещения электрооборудования.			
Дизайнер интерьера  №1 Александр Батеньков	Стадия	Лист	Листов
	ЭП	89	120
		Подп.	Дата
ГАП	Батеньков А.С.		
Гл. дизайнер	Власова В.А.		
Гл. проектиров.	Луныкова В.Н.		
Разработал	Ильина Е.Е.		




- Условные обозначения:
- Выход 220V
 - Выход электрокабеля для светодиодной ленты
 - Выключатель одноклавишный
 - Выключатель двухклавишный
 - Переключатель двухклавишный
 - Переключатель одноклавишный переходной
 - Светильник точечный встраиваемый
 - Светодиодная лента

Примечания:


- * – размеры уточнить по месту.
- Выключатели располагать от уровня чистого пола на высоте 0,900 м. Исключения указаны на чертеже.
- Светильники, встроенные в мебель, согласовать с изготовителями мебели.

МСК 392.12.25–ЭП ПРЕМИУМ			
Эскизный дизайн–проект интерьера квартиры в г. Москва ЖК "Остров", ул. Нижние Мневники д. 7			
Мастер спальниПлан размещения освещения и выключателей.			
Дизайнер интерьера №1 Александр Батеньков	Стадия	Лист	Листов
	ЭП	90	120
		Подп.	Дата
ГАП	Батеньков А.С.		
Гл. дизайнер	Власова В.А.		
Гл. проектиров.	Луцькова В.Н.		
Разработал	Ильина Е.Е.		

И-01 Развертка стены 1:25

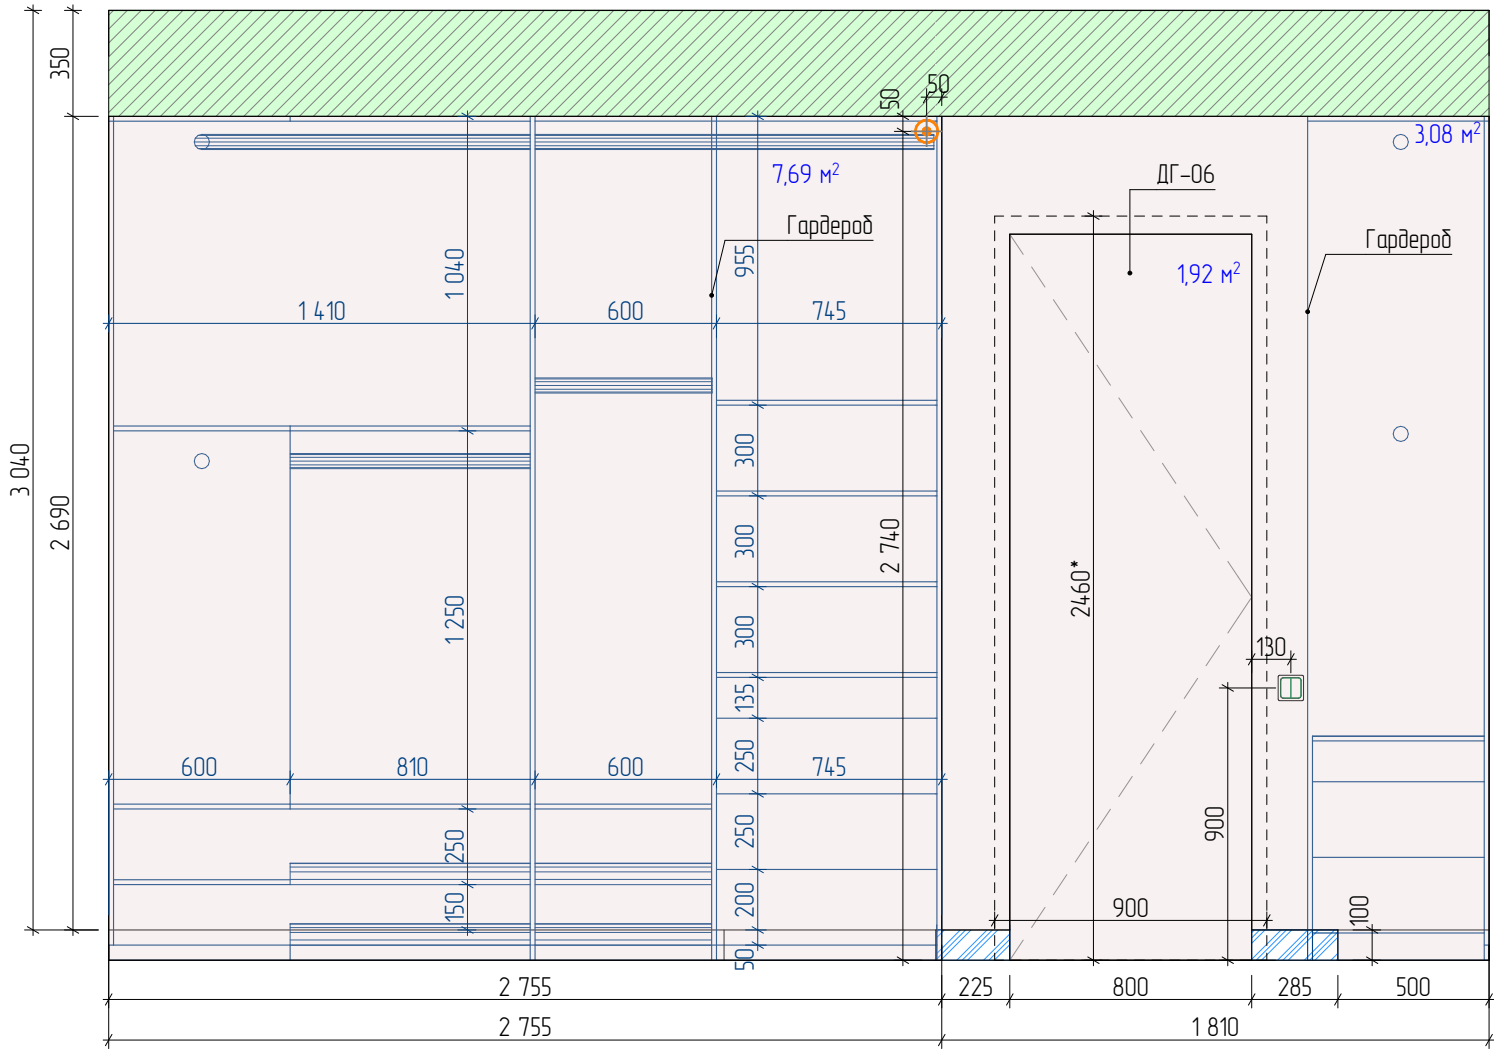

И-02 Развертка стены 1:25

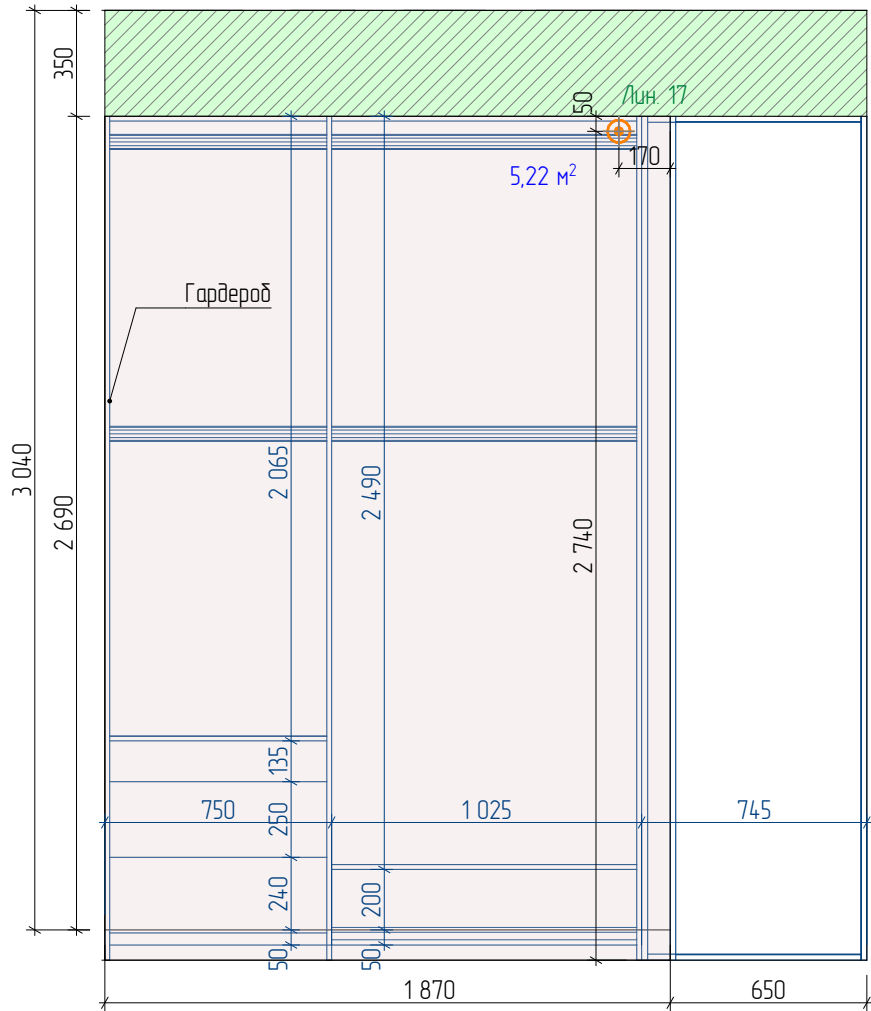

Условные обозначения:

-  Плинтус №1. Теневой плинтус скрытого монтажа с МДФ вставкой. Теневой зазор от пола 100 мм. Цвет при выборе образца (в цвет стен).
-  Монтаж конструкций из ГКВЛ
-  Покраска №1. Выполнить по подготовленной поверхности (стеклохолст*). Цвет при выборе образца (бежевый*).
-  Вывод электрокабеля для светодиодной ленты
-  Переключатель двухклавишный

Примечания:



- * – размеры уточнить по месту после выполнения черновых отделочных работ.
- Выключатели располагать от уровня чистого пола на высоте 900 мм. Исключения указаны на чертеже.
- Розетки располагать от уровня чистого пола на высоте 300 мм. Исключения указаны на чертеже.
- Цвет окрашивания плинтуса уточнить после согласования образца.
- Высоту проемов выполнять 2460 мм от уровня чистого пола. Уточнить после подбора и согласования модели дверей.
- Плинтус подрезать по месту в местах стыковки с дверями и мебелью.
- Внутреннее наполнение мебели разработать со специалистами.
- Серым/синим цветом показаны размеры мебели. Мебель разработать со специалистами, размеры уточнить после выполнения чистовой отделки.

МСК 392.12.25-ЭП ПРЕМИУМ

Эскизный дизайн-проект интерьера квартиры в г. Москва ЖК "Остров", ул. Нижние Мневники д. 7

Мастер спальни.Развертки стен И-01, И-02.

Дизайнер интерьера  №1 Александр Батеньков	Стадия	Лист	Листов
	ЭП	91	120
		Подп.	Дата
ГАП	Батеньков А.С.		
Гл. дизайнер	Власова В.А.		
Гл. проектиров.	Луцкова В.Н.		
Разработал	Ильина Е.Е.		

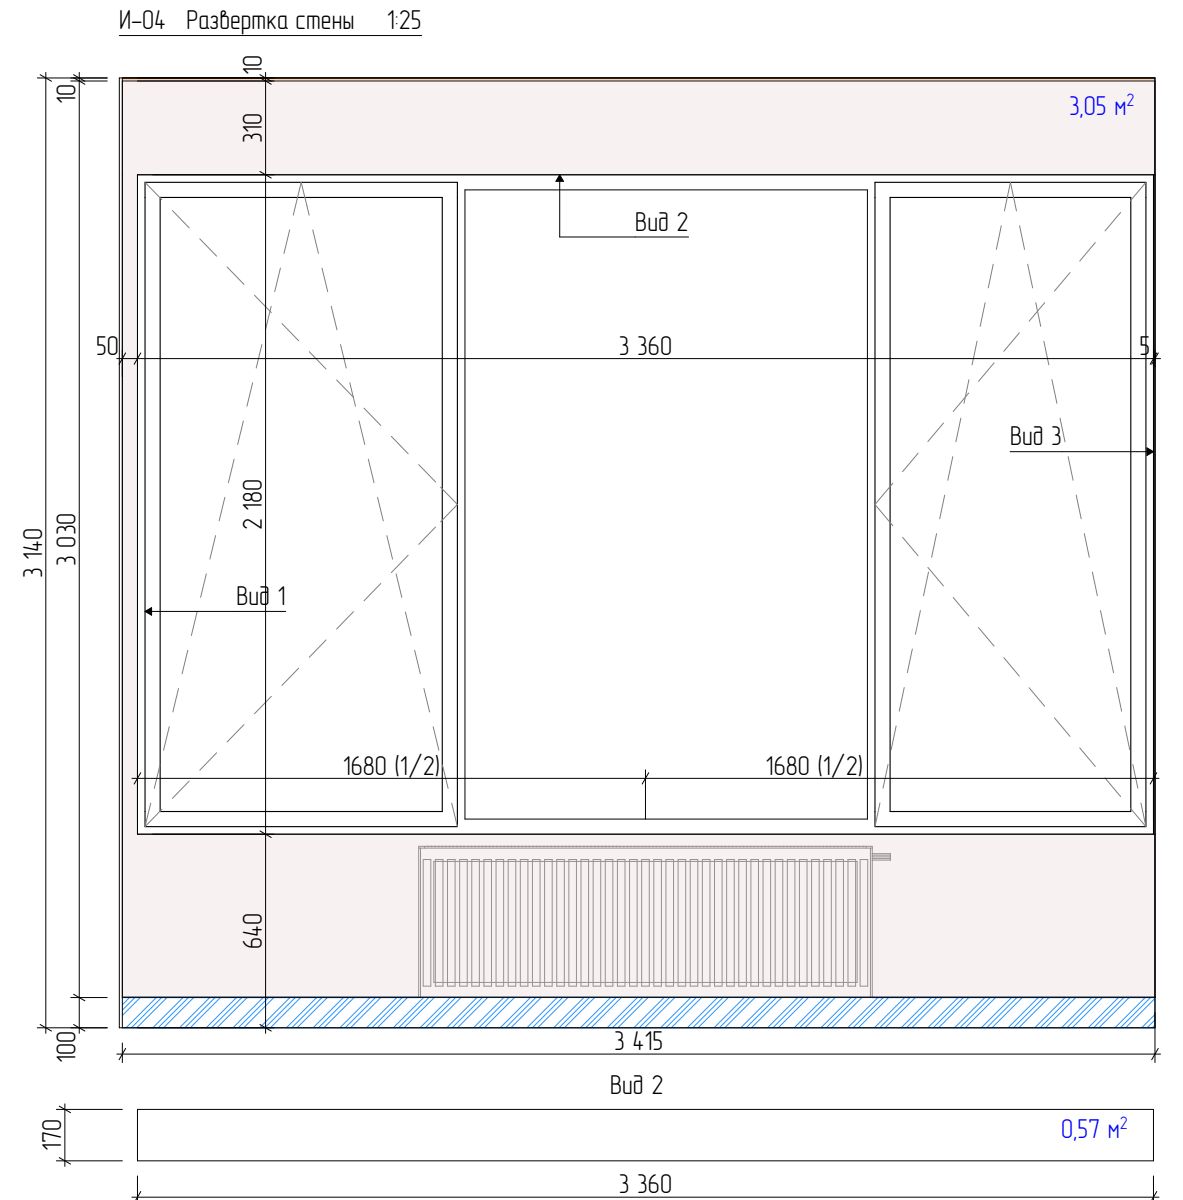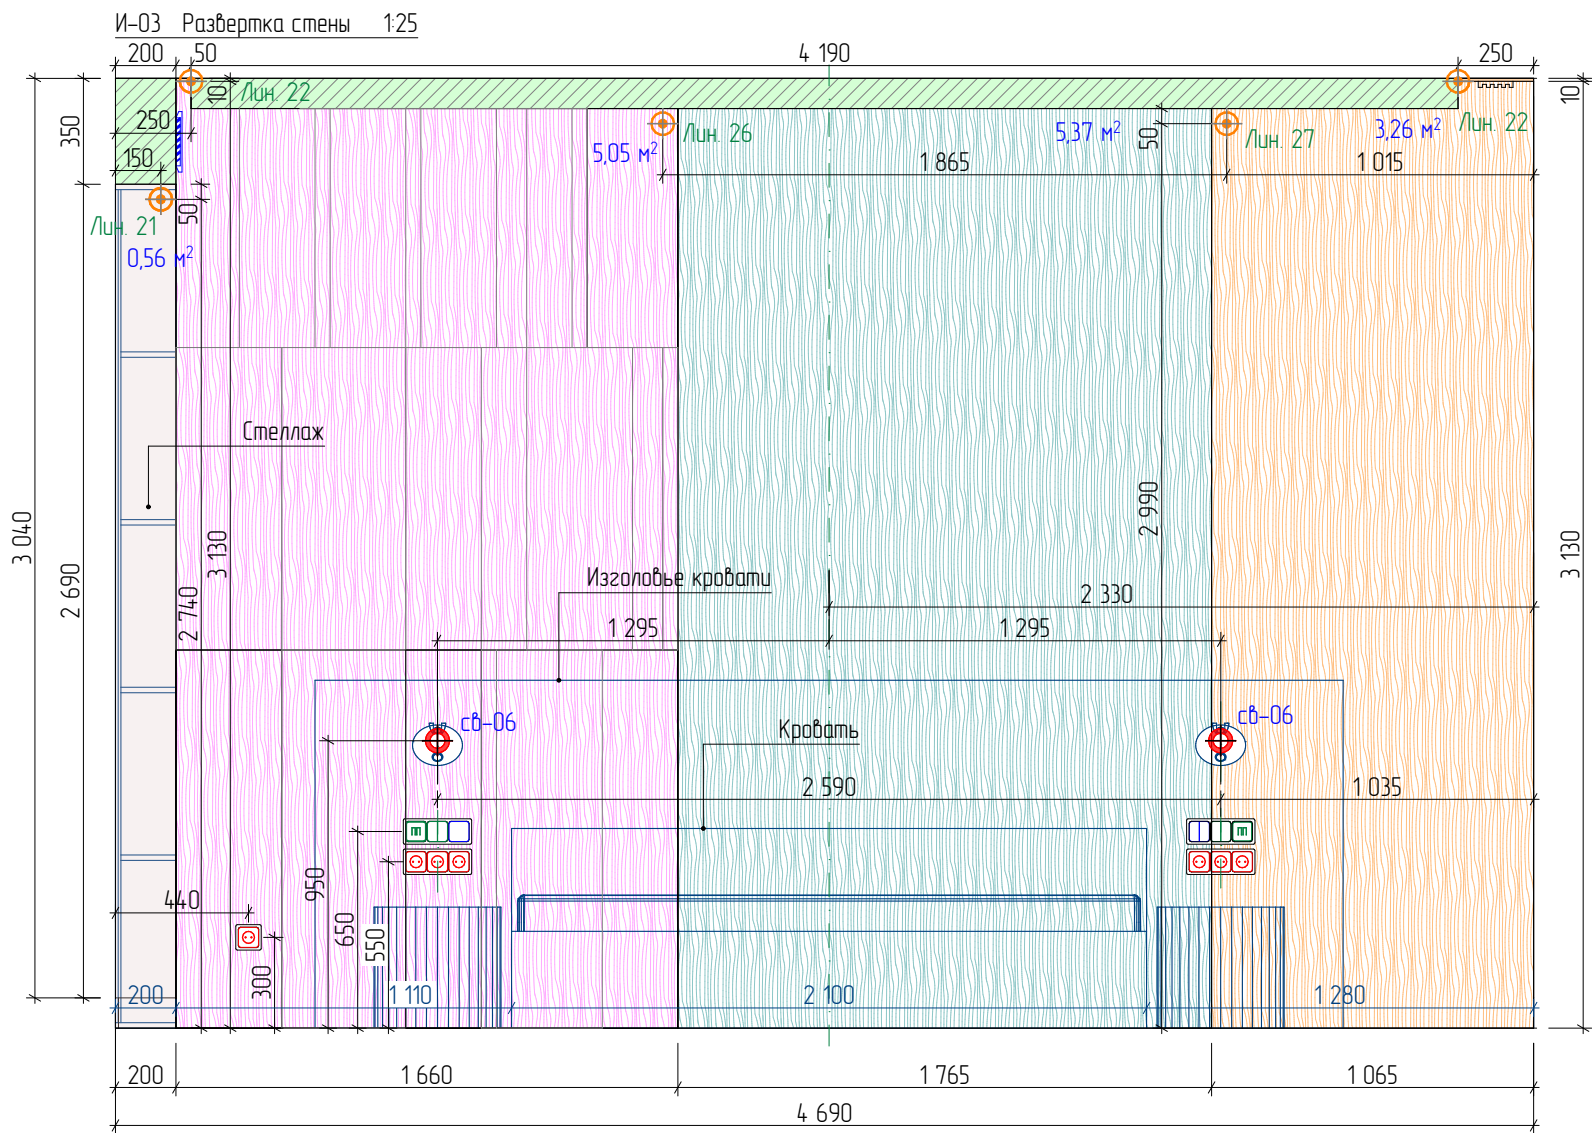


Примечания:

- * – размеры уточнить по месту после выполнения черновых отделочных работ.
- Выключатели располагать от уровня чистого пола на высоте 900 мм. Исключения указаны на чертеже.
- Розетки располагать от уровня чистого пола на высоте 300 мм. Исключения указаны на чертеже.
- Оконные откосы оклеить строительным флизелином и окрасить в белый цвет. Уточнить по месту.
- Размещение выводов для отопления согласовать со специалистами.
- Цвет окрашивания плинтуса уточнить после согласования образца.
- Внутреннее наполнение мебели разработать со специалистами.
- Серым/синим цветом показаны размеры мебели. Мебель разработать со специалистами, размеры уточнить после выполнения чистовой отделки.



Условные обозначения:

- Плинтус №1. Теневой плинтус скрытого монтажа с МДФ вставкой. Теневой зазор от пола 100 мм. Цвет при выборе образца (в цвет стен).
- Монтаж конструкций из ГКВЛ
- Покраска №1. Выполнить по подготовленной поверхности (стеклохолст*). Цвет при выборе образца (бежевый*).
- Покраска №2. Выполнить по подготовленной поверхности (стеклохолст*). Цвет при выборе образца (белый*).
- МДФ панель №4. Цвет и фактура при выборе образца (ржавый металл*).
- МДФ панель №5. Цвет и фактура при выборе образца (ржавый металл*).
- МДФ панель №6. 3д панель. Цвет и фактура при выборе образца (ржавый металл*).

- Выход 220 В
- Выход электрокабеля для светодиодной ленты
- Розетка 220 В
- Выключатель одноклавишный
- Выключатель двухклавишный
- Переключатель одноклавишный переходной
- Переключатель двухклавишный

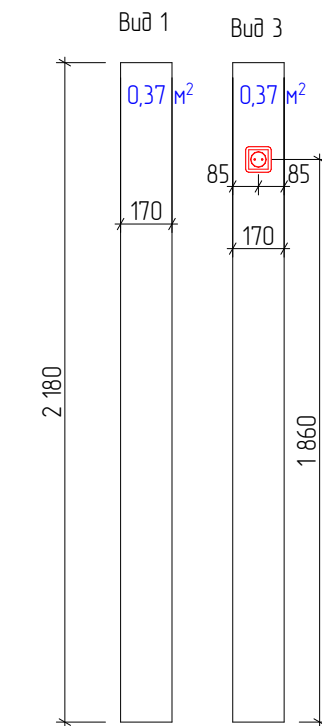

МСК 392.12.25-ЭП ПРЕМИУМ			
Эскизный дизайн-проект интерьера квартиры в г. Москва ЖК "Остров", ул. Нижние Мневники д. 7			
Мастер спальни.Развертки стен И-03, И-04.			
Дизайнер интерьера №1 Александр Батеньков	Стадия	Лист	Листов
	ЭП	92	120
		Подп.	Дата
ГАП	Батеньков А.С.		
Гл. дизайнер	Власова В.А.		
Гл. проектиров.	Луныкова В.Н.		
Разработал	Ильина Е.Е.		

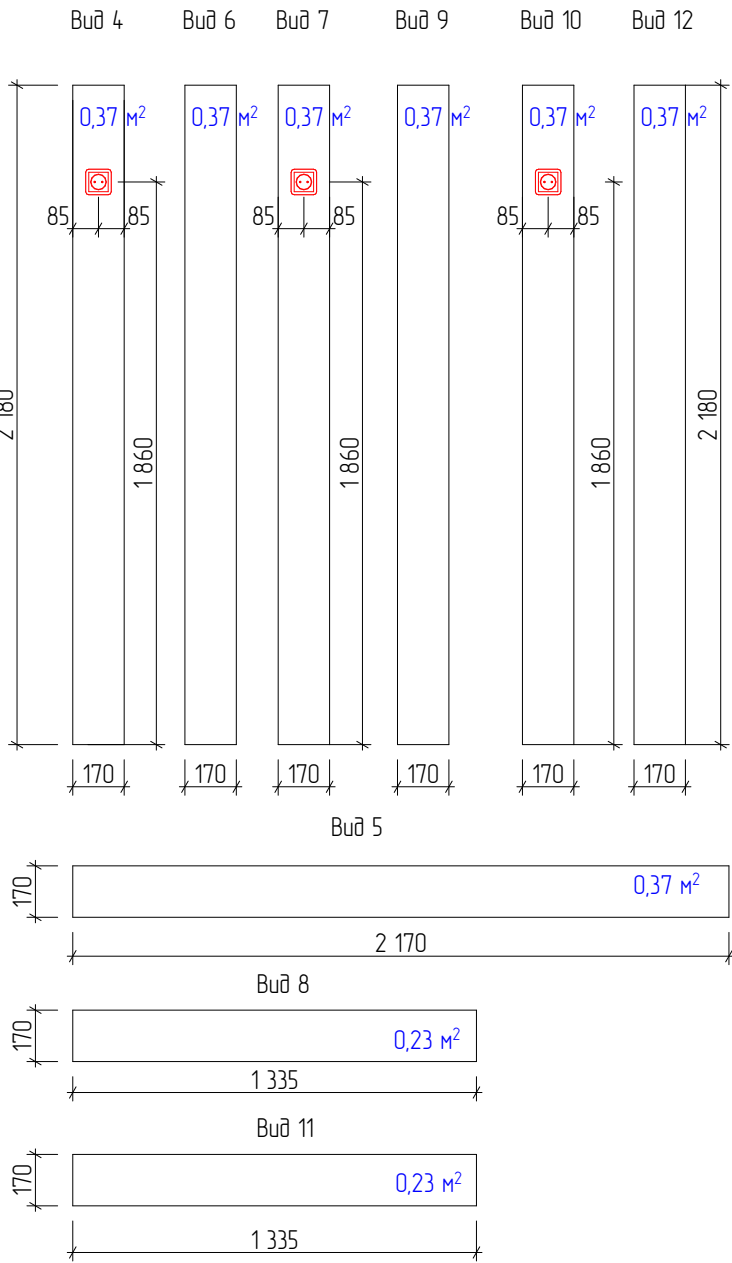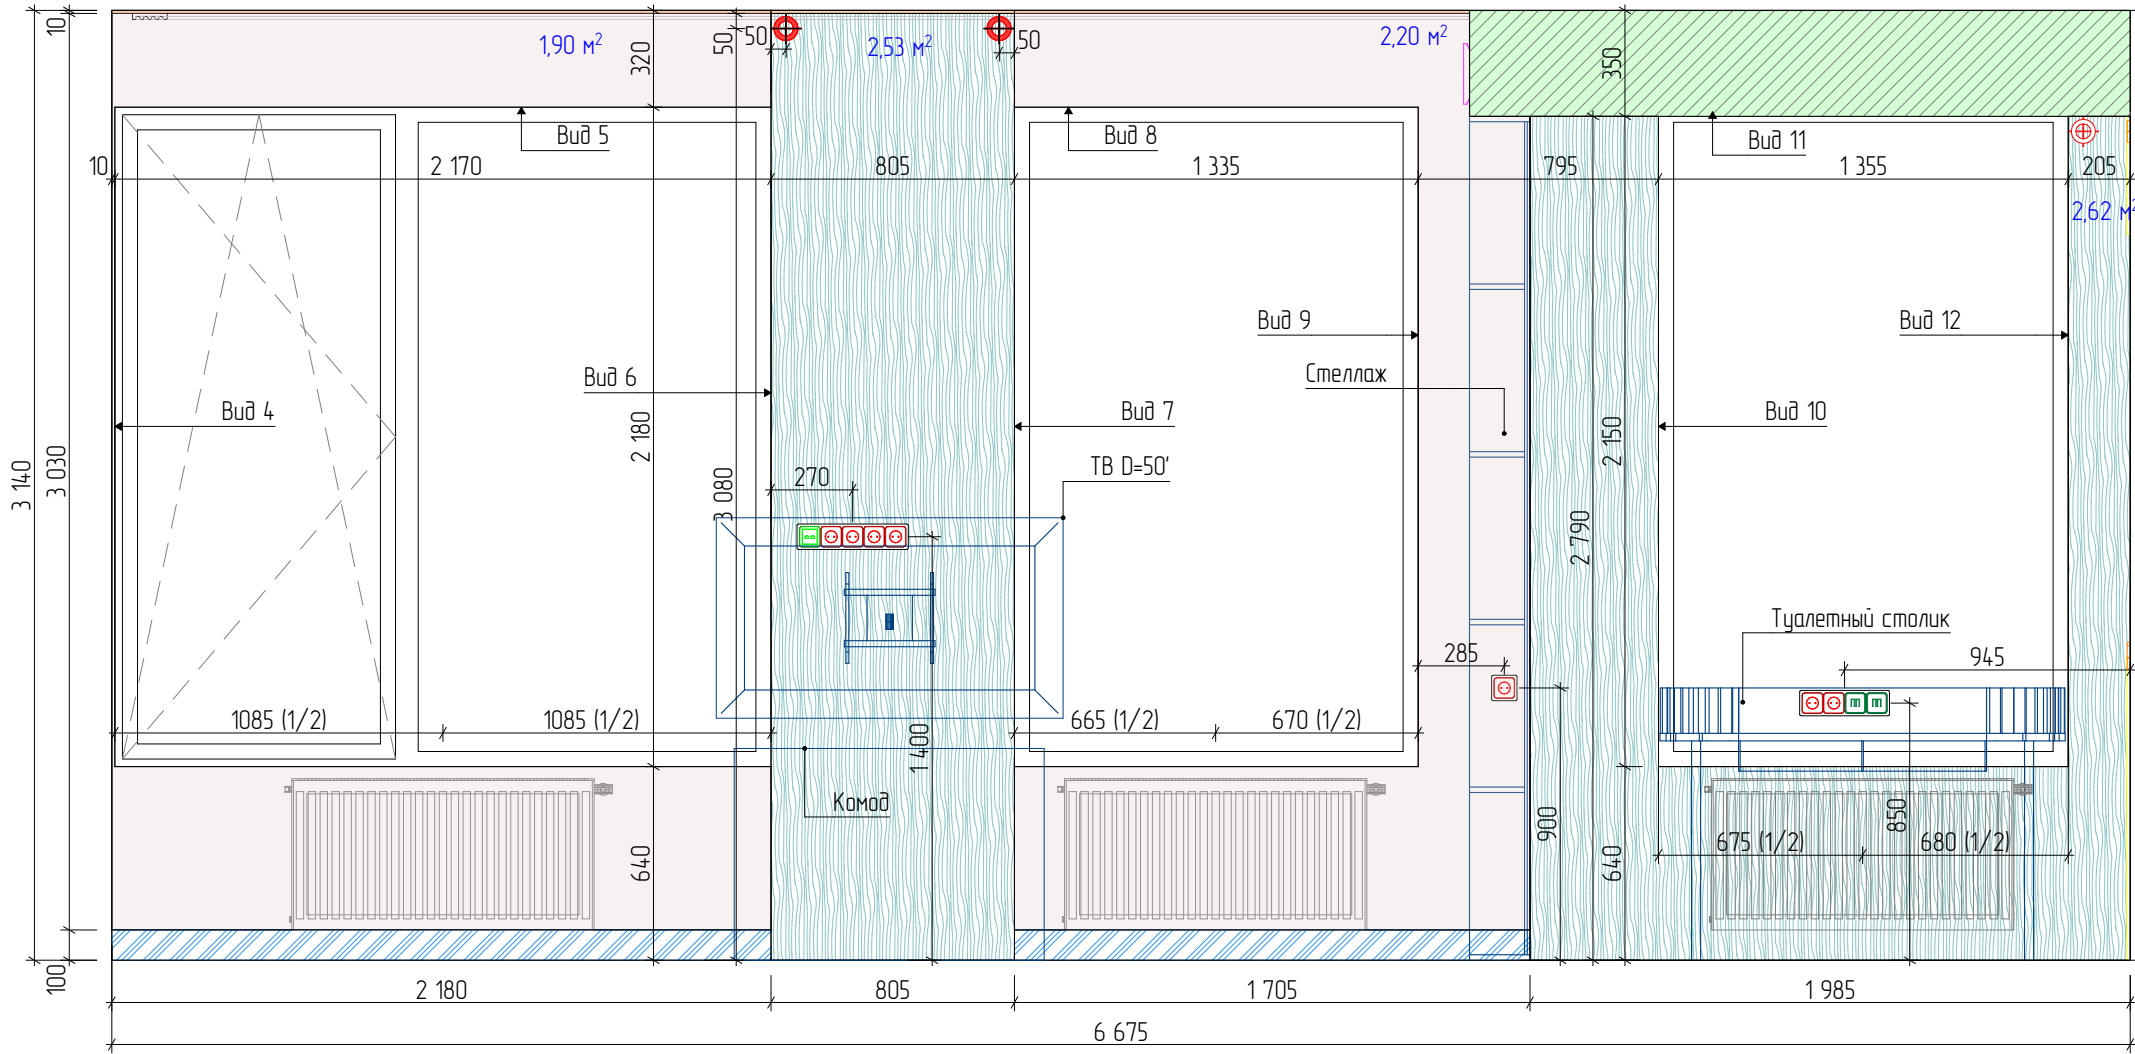


Условные обозначения:

- Плинтус №1. Теневой плинтус скрытого монтажа с МДФ вставкой. Теневой зазор от пола 100 мм. Цвет при выборе образца (в цвет стен).
- Монтаж конструкций из ГКВЛ
- Покраска №1. Выполнить по подготовленной поверхности (стеклохолст*). Цвет при выборе образца (бежевый*).
- Покраска №2. Выполнить по подготовленной поверхности (стеклохолст*). Цвет при выборе образца (белый*).
- МДФ панель №4. Цвет и фактура при выборе образца (ржавый металл*).
- Выход 220 V
- Разетка 220 V
- Переключатель одноклавишный переходной
- Переключатель двухклавишный
- Интернет-розетка двойная


Примечания:
1. *- размеры уточнить по месту после выполнения черновых отделочных работ.
2. Выключатели располагать от уровня чистого пола на высоте 900 мм. Исключения указаны на чертеже.
3. Розетки располагать от уровня чистого пола на высоте 300 мм. Исключения указаны на чертеже.
4. Оконные откосы оклеить строительным флизелином и окрасить в белый цвет. Уточнить по месту.
5. Размещение выводов для отопления согласовать со специалистами.
6. Цвет окрашивания плинтуса уточнить после согласования образца.
7. Плинтус подрезать по месту в местах стыковки с дверями и мебелью.
8. Внутреннее наполнение мебели разработать со специалистами.
9. Серым/синим цветом показаны размеры мебели. Мебель разработать со специалистами, размеры уточнить после выполнения чистовой отделки.

МСК 392.12.25-ЭП ПРЕМИУМ			
Эскизный дизайн-проект интерьера квартиры в г. Москва ЖК "Остров", ул. Нижние Мневники д. 7			
Мастер спальни.Развертка стен И-05.			
Дизайнер интерьера №1 Александр Батеньков	Стадия	Лист	Листов
	ЭП	93	120
		Подп.	Дата
ГАП	Батеньков А.С.		
Гл. дизайнер	Власова В.А.		
Гл. проектиров.	Луцькова В.Н.		
Разработал	Ильина Е.Е.		


И-06 Развертка стены 1:25

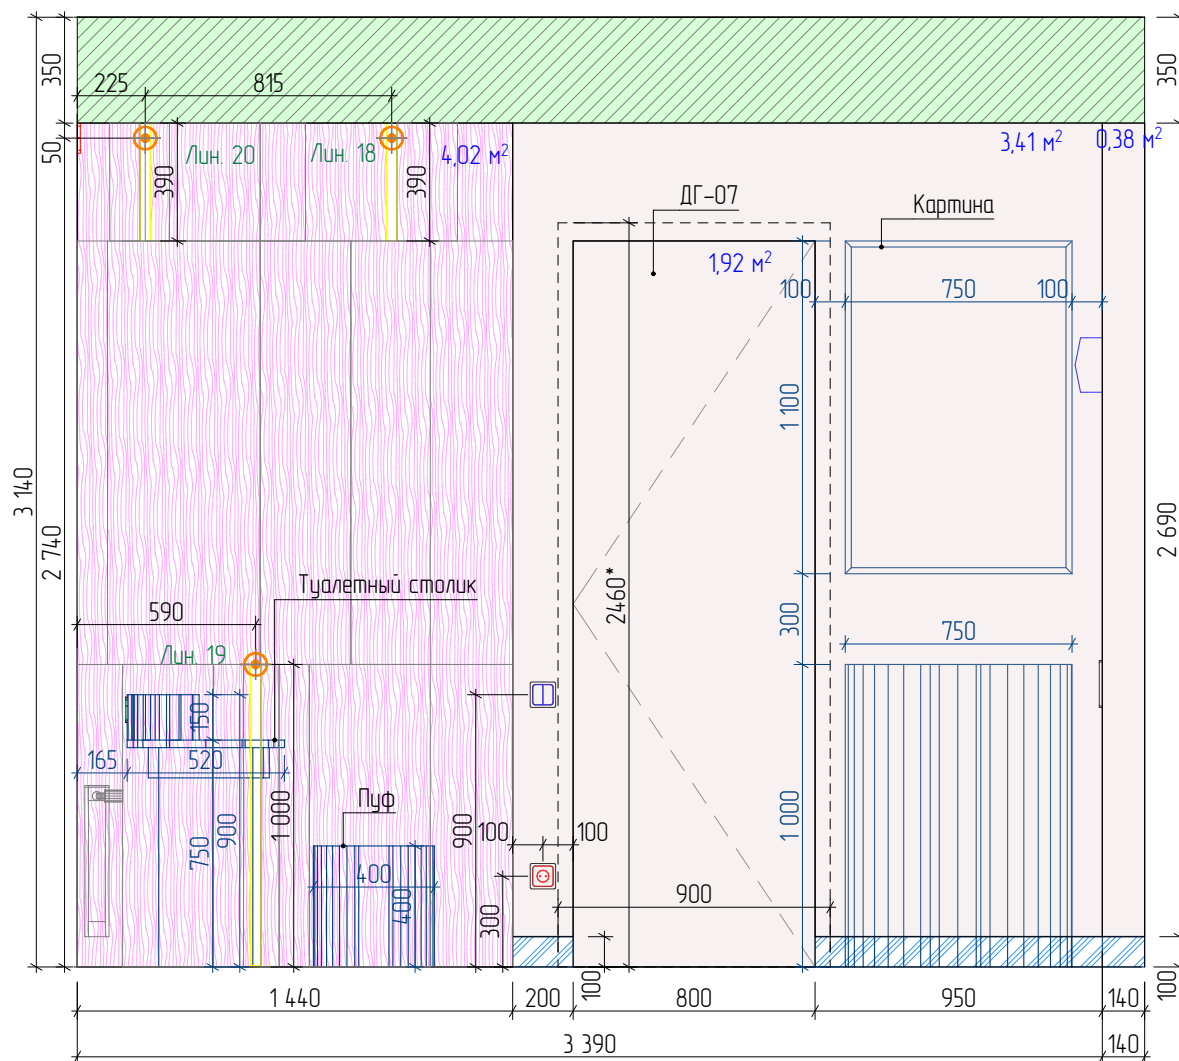


И-07 Развертка стены 1:25

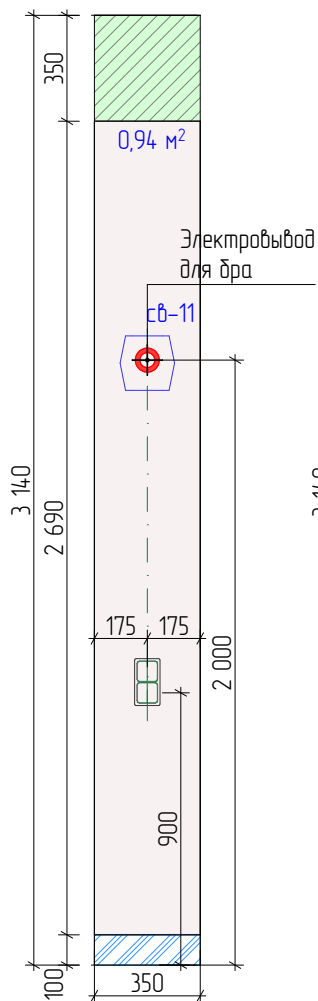


И-08 Развертка стены 1:25

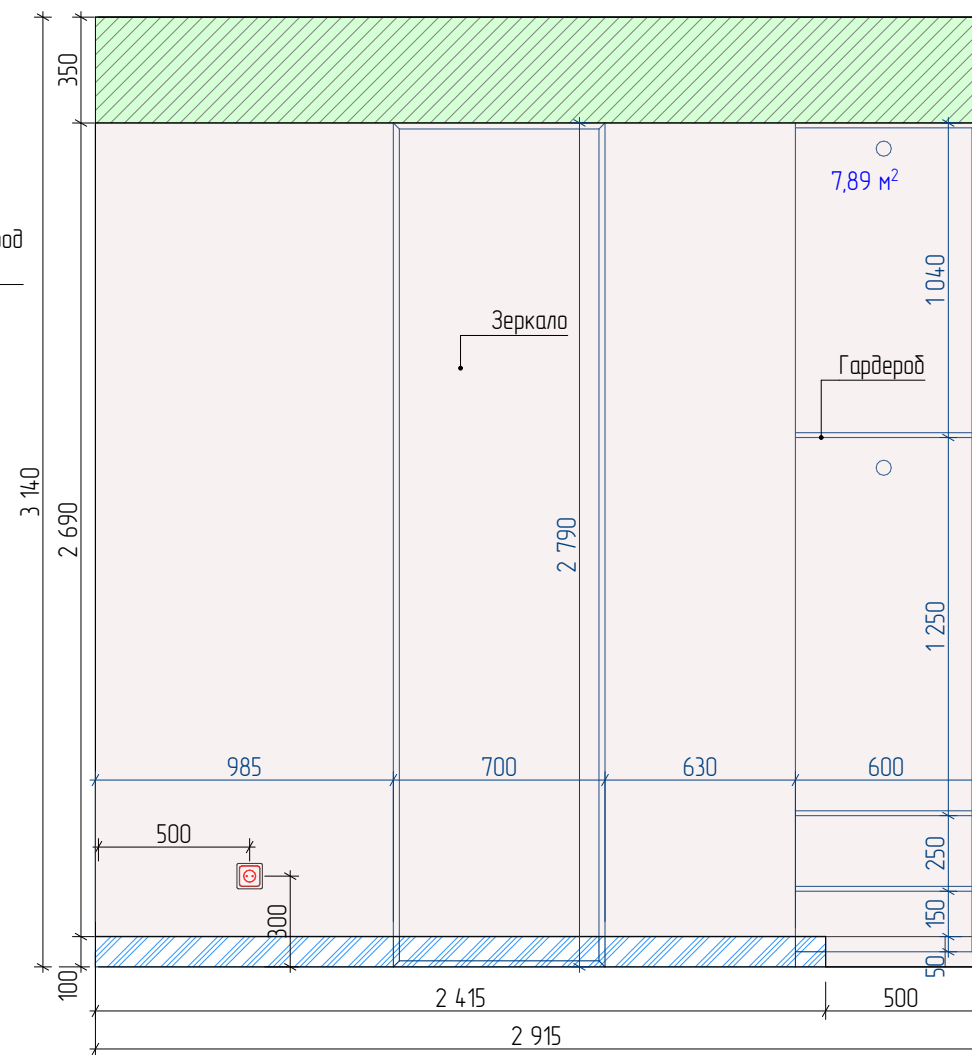

И-09 Развертка стены 1:25

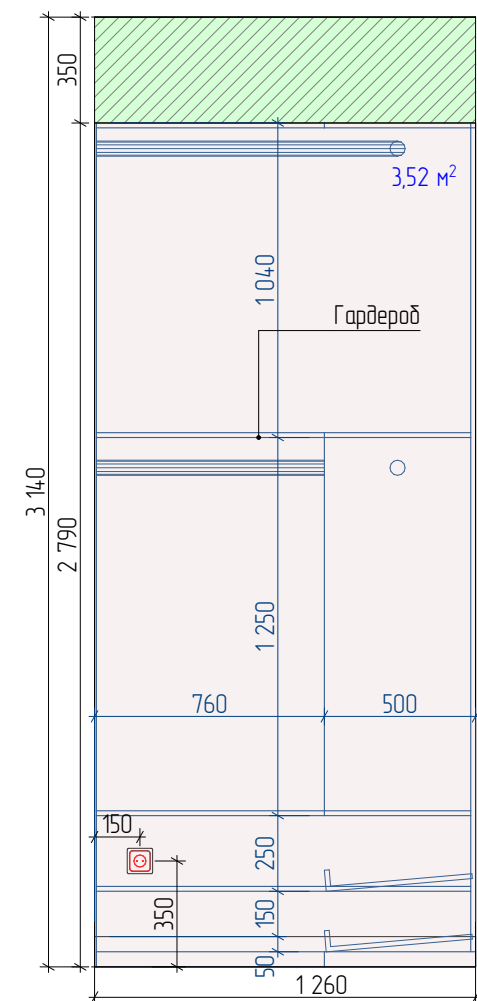

И-10 Развертка стены 1:25

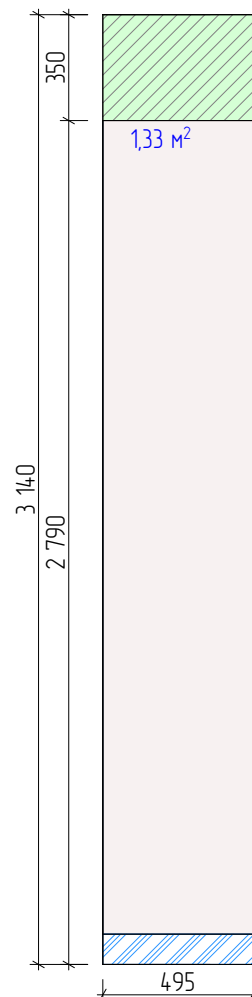

Условные обозначения:

- | | |
|---|---|
|  | Плнтус №1. Теневой плнтус скрытого монтажа с МДФ вставкой. Теневой зазор от пола 100 мм. Цвет при выборе образца (в цвет стен). |
|  | Монтаж конструкций из ГКВЛ |
|  | Покраска №1. Выполнить по подготовленной поверхности (стеклохолст*). Цвет при выборе образца (бежевый*). |
|  | МДФ панель №5. Цвет и фактура при выборе образца (ржавый металл*). |
|  | Розетка 220 В |
|  | Переключатель двухклавишный |
|  | Выключатель двухклавишный |
|  | Вывод 220 В |
|  | Вывод электрокабеля для светодиодной ленты |

Примечания:

1. * – размеры уточнить по месту после выполнения черновых отделочных работ.
2. Выключатели располагать от уровня чистого пола на высоте 900 мм. Исключения указаны на чертеже.
3. Розетки располагать от уровня чистого пола на высоте 300 мм. Исключения указаны на чертеже.
4. Цвет окрашивания плинтуса уточнить после согласования образца.
5. Высоту проемов выполнить 2460 мм от уровня чистого пола. Уточнить после подбора и согласования модели дверей.
6. Плинтус подрезать по месту в местах стыковки с дверями и мебелью.
7. Внутреннее наполнение мебели разработать со специалистами.
8. Серым/синим цветом показаны размеры мебели. Мебель разработать со специалистами, размеры уточнить после выполнения чистовой отделки.

МСК 392.12.25-ЭП ПРЕМИУМ			
Эскизный дизайн-проект интерьера квартиры в г. Москва ЖК "Остров", ул. Нижние Мневники д. 7			
Мастер спальни Развертки стен И-06, И-07, И-08, И-09, И-10.			
Дизайнер интерьера №1  Александр Батеньков	Стандия	Лист	Листов
	ЭП	94	120
		Подп.	Дата
ГАП	Батеньков А.С.		
Гл. дизайнер	Власова В.А.		
Гл. проектиров.	Луныкова В.Н.		
Разработал	Ильина Е.Е.		

Ведомость отделочных материалов.

№	Обозначение	Наименование	Кол-во	Примечание
Пол:				
1		Пробковый компенсатор	0,8	м.п.
2		Покрытие №01. Паркет. Изготовитель: Lab Arte, кол-я: Angle Дуб Натур, размер: 500x150 мм, точный артикул и производителя уточнить при выборе образца, толщину уточнить при закупе.	29,87	м²
Стены:				
3		Плинтус №1. Теневой плинтус скрытого монтажа с МДФ вставкой. Теневой зазор от пола 100 мм. Цвет при выборе образца (в цвет стен).	11,86	м.п.
4		Покраска №1. Выполнить по подготовленной поверхности (стеклохолст*). Цвет при выборе образца (бежевый*).	45,01	м²
5		МДФ панель №4. Цвет и фактура при выборе образца (ржавый металл*).	10,52	м²
6		МДФ панель №5. Цвет и фактура при выборе образца (ржавый металл*).	9,07	м²
7		МДФ панель №6. 3д панель. Цвет и фактура при выборе образца (ржавый металл*).	3,26	м²
Откосы:				
8		Покраска №2. Выполнить по подготовленной поверхности (стеклохолст*). Цвет при выборе образца (белый*).	3,56	м²
Подоконник:				
9		Подоконник №1. Искусственный камень. Цвет при выборе образца.	1,42	м²

МСК 392.12.25–ЭП ПРЕМИУМ			
Эскизный дизайн–проект интерьера квартиры в г. Москва ЖК “Остров”, ул. Нижние Мневники д. 7			
Мастер спальниВедомость отделочных материалов.			
Дизайнер интерьера №1 Александр Батеньков	Стадия	Лист	Листов
	ЭП	95	120
		Подп.	Дата
ГАП	Батеньков А.С.		
Гл. дизайнер	Власова В.А.		
Гл. проектиров.	Луныкова В.Н.		
Разработал	Ильина Е.Е.		