


План отделки пола:

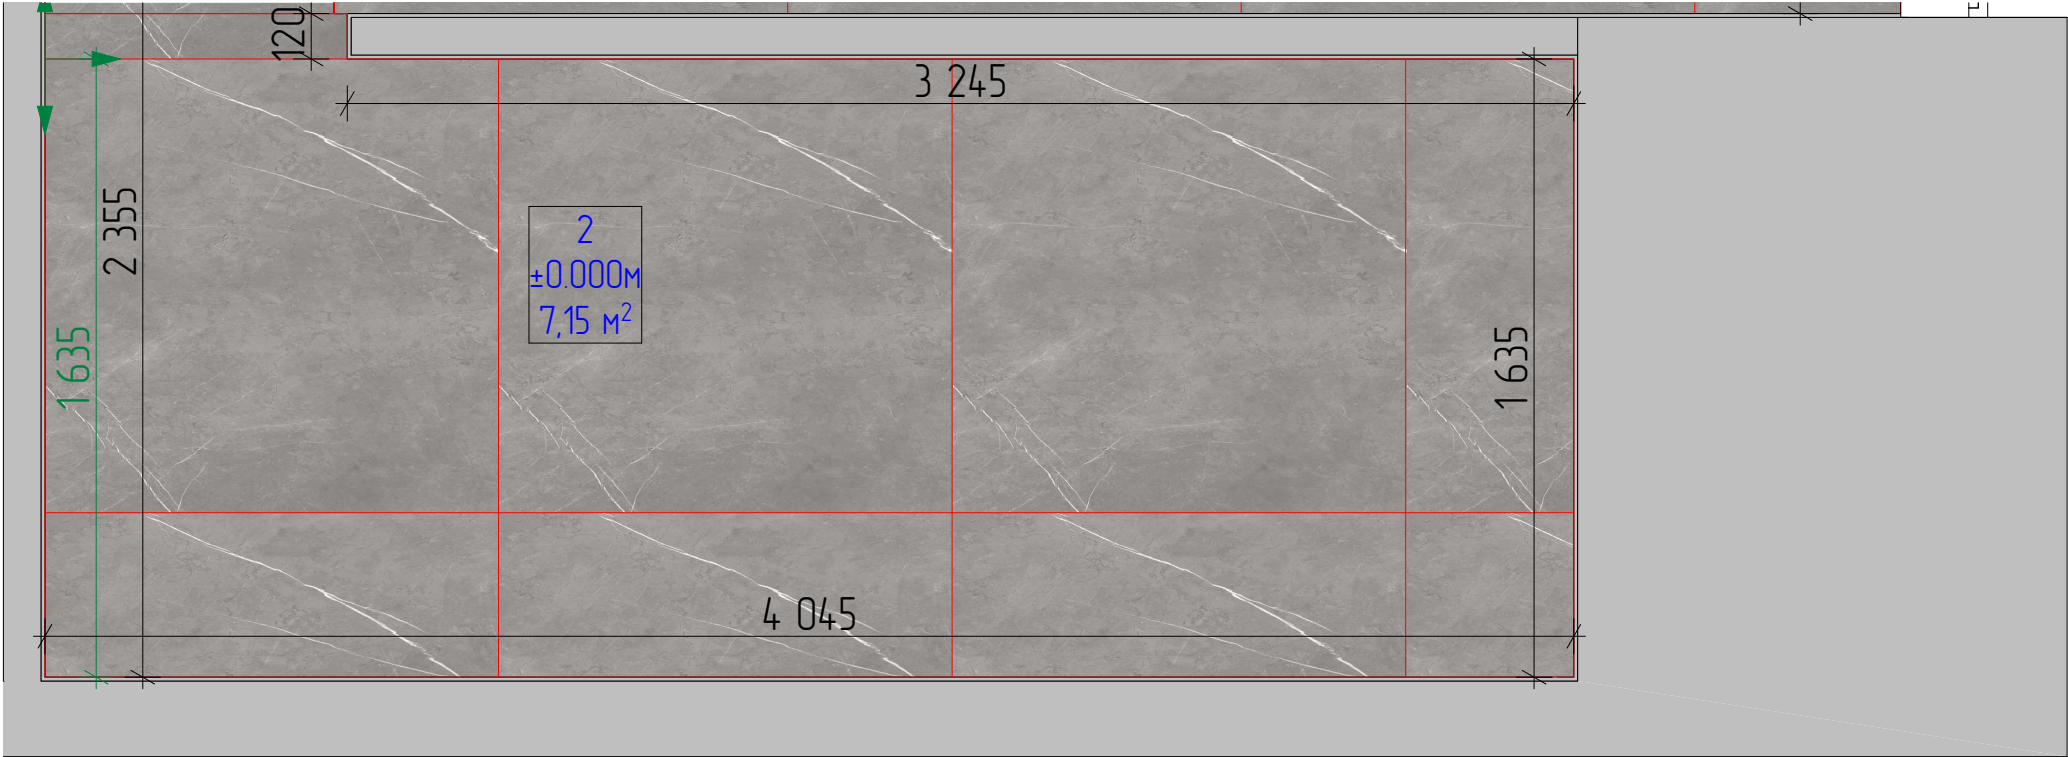


Условные обозначения:

- Направление и начало укладки
- Покрытие №02. Керамогранит. Изготовитель: Elegant Grey, кол-я: Forte Dei Marini, размер: 1200x1200 мм, толщину уточнить при заказе.
- Светильник точечный встраиваемый
- Диффузор, вытяжка

Примечания:

- * – размеры уточнить по месту после выполнения черновых отделочных работ.
- За отметку ±0,000 принят уровень чистого пола.
- Во влажных помещениях предусмотреть гидроизоляцию пола с заведением на стены на 150 мм.
- При монтаже напольных покрытий уточнить необходимость устройства дверных проемов с порогом.
- * – размеры уточнить по месту после выполнения черновых отделочных работ и установки дверей со скрытой коробкой.
- ** – размер уточнить по месту в зависимости от точного расположения полотна двери, стыковка двух разных напольных покрытий должна проходить точно по центру вдоль дверного полотна.
- Выполнить уровень потолка из влагостойкого ГКЛ для предотвращения деформации потолка при затоплении.
- Высоту уровней потолка отсчитывать от существующей ж/б плиты перекрытия помещения.
- От вытяжки провести вентиляционный короб до общедомового канала в конструкции потолка, уточнить по месту со специалистами и заказчиком.
- Шумоизоляцию разработать со специалистами, уточнить состав и толщину слоев шумоизоляционных материалов. Уточнить необходимость устройства с заказчиком.


План отделки потолка:

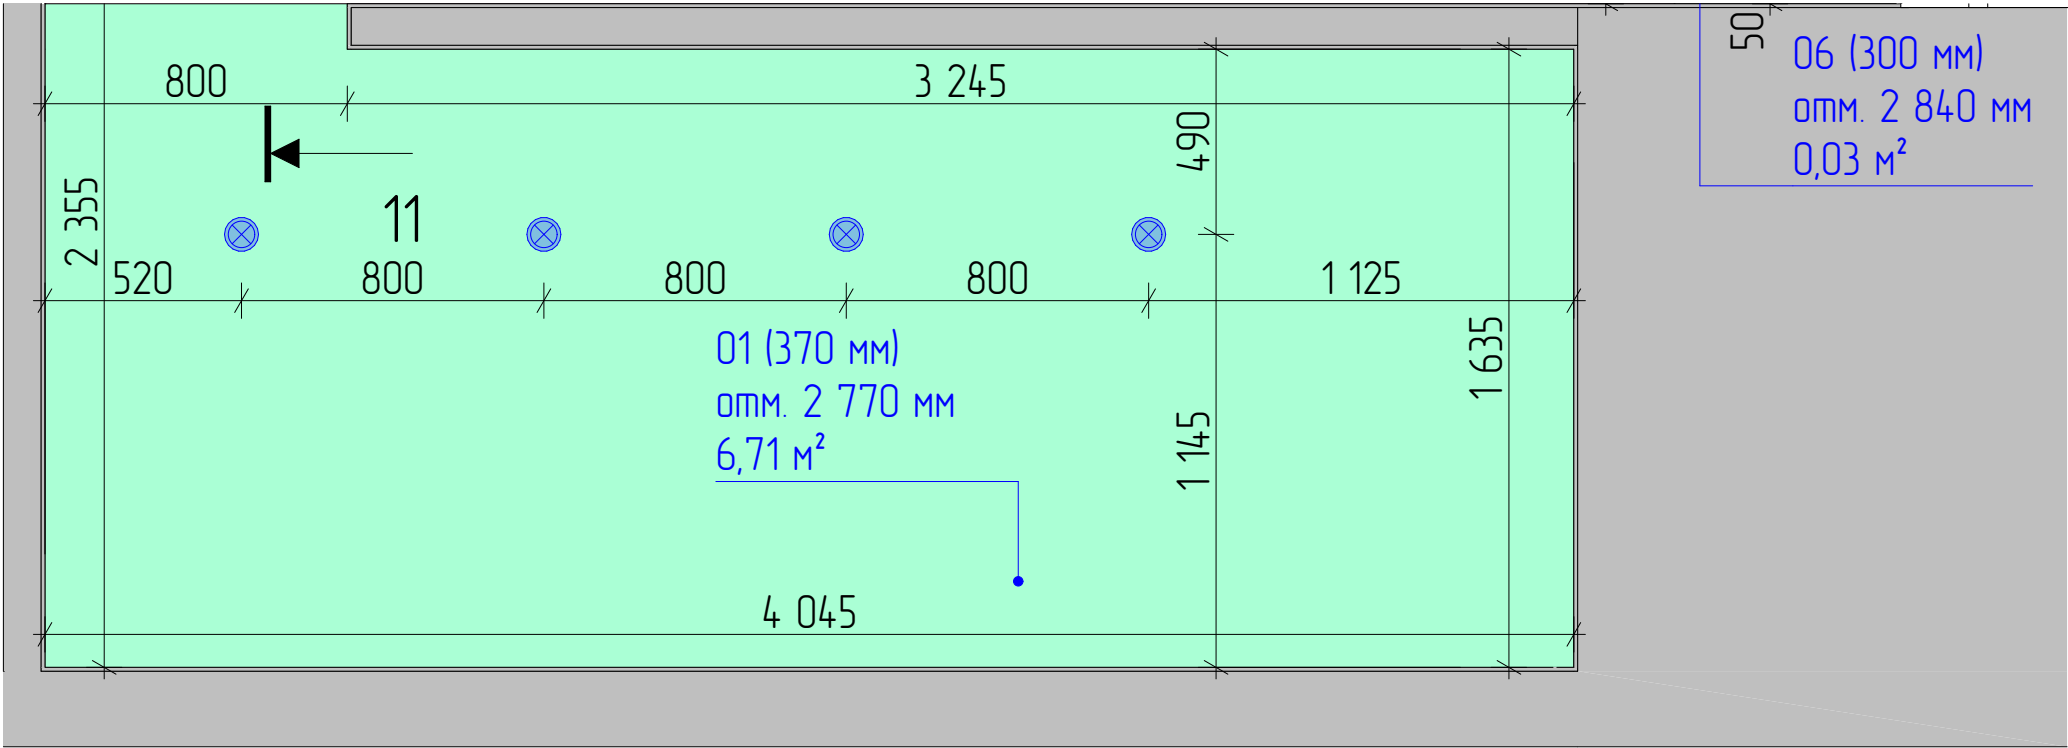


Условные потолки				
№	Обозначение	Опуск	Примечания	Площадь м2
01		370	Потолок ГКЛ/В. Окрасить в цвет выбранного образца (белый) по армирующему материалу (стеклохолст "паутинка").	6,71

МСК 392.12.25-ЭП ПРЕМИУМ			
Эскизный дизайн-проект интерьера квартиры в г. Москва ЖК "Остров", ул. Нижние Мневники д. 7			
Кладовая.План отделки пола. План отделки потолка.			
Дизайнер интерьера №1 Александр Батеньков	Стадия	Лист	Листов
	ЭП	52	120
		Подп.	Дата
ГАП	Батеньков А.С.		
Гл. дизайнер	Власова В.А.		
Гл. проектиров.	Луцькова В.Н.		
Разработал	Ильина Е.Е.		

План электрооборудования:

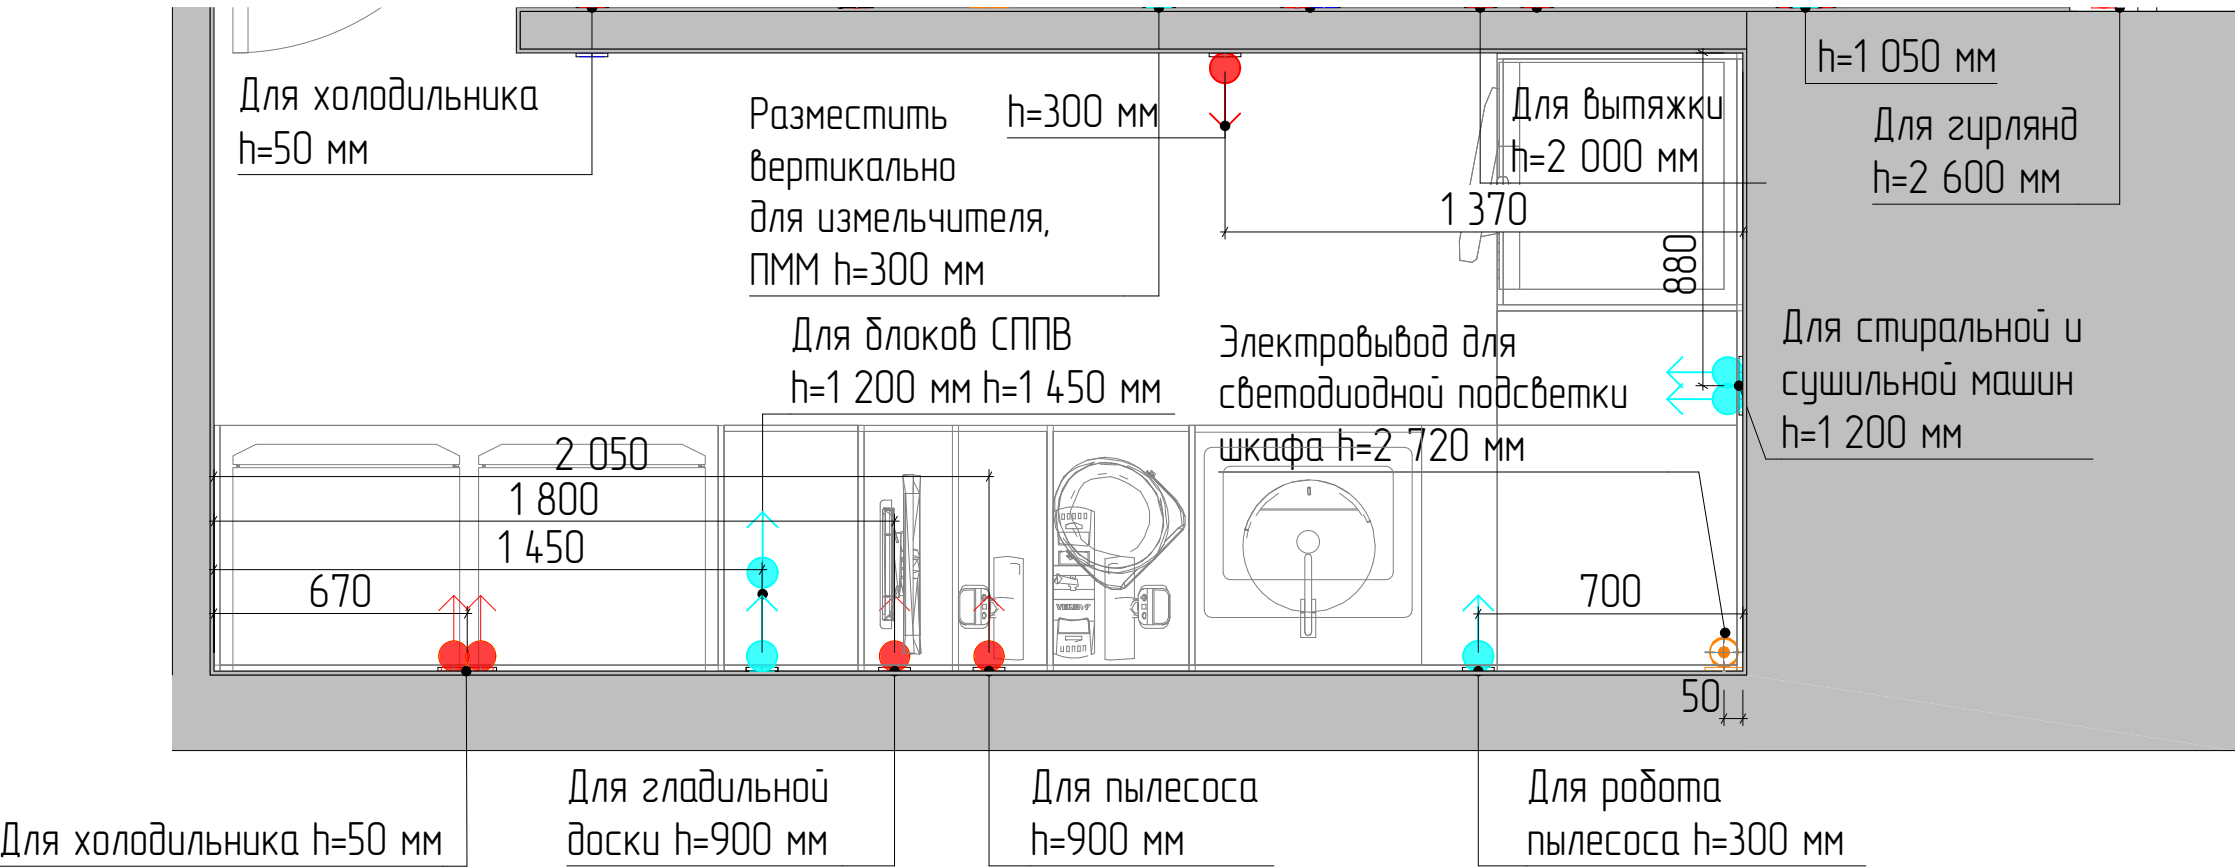

План размещения освещения и выключателей:

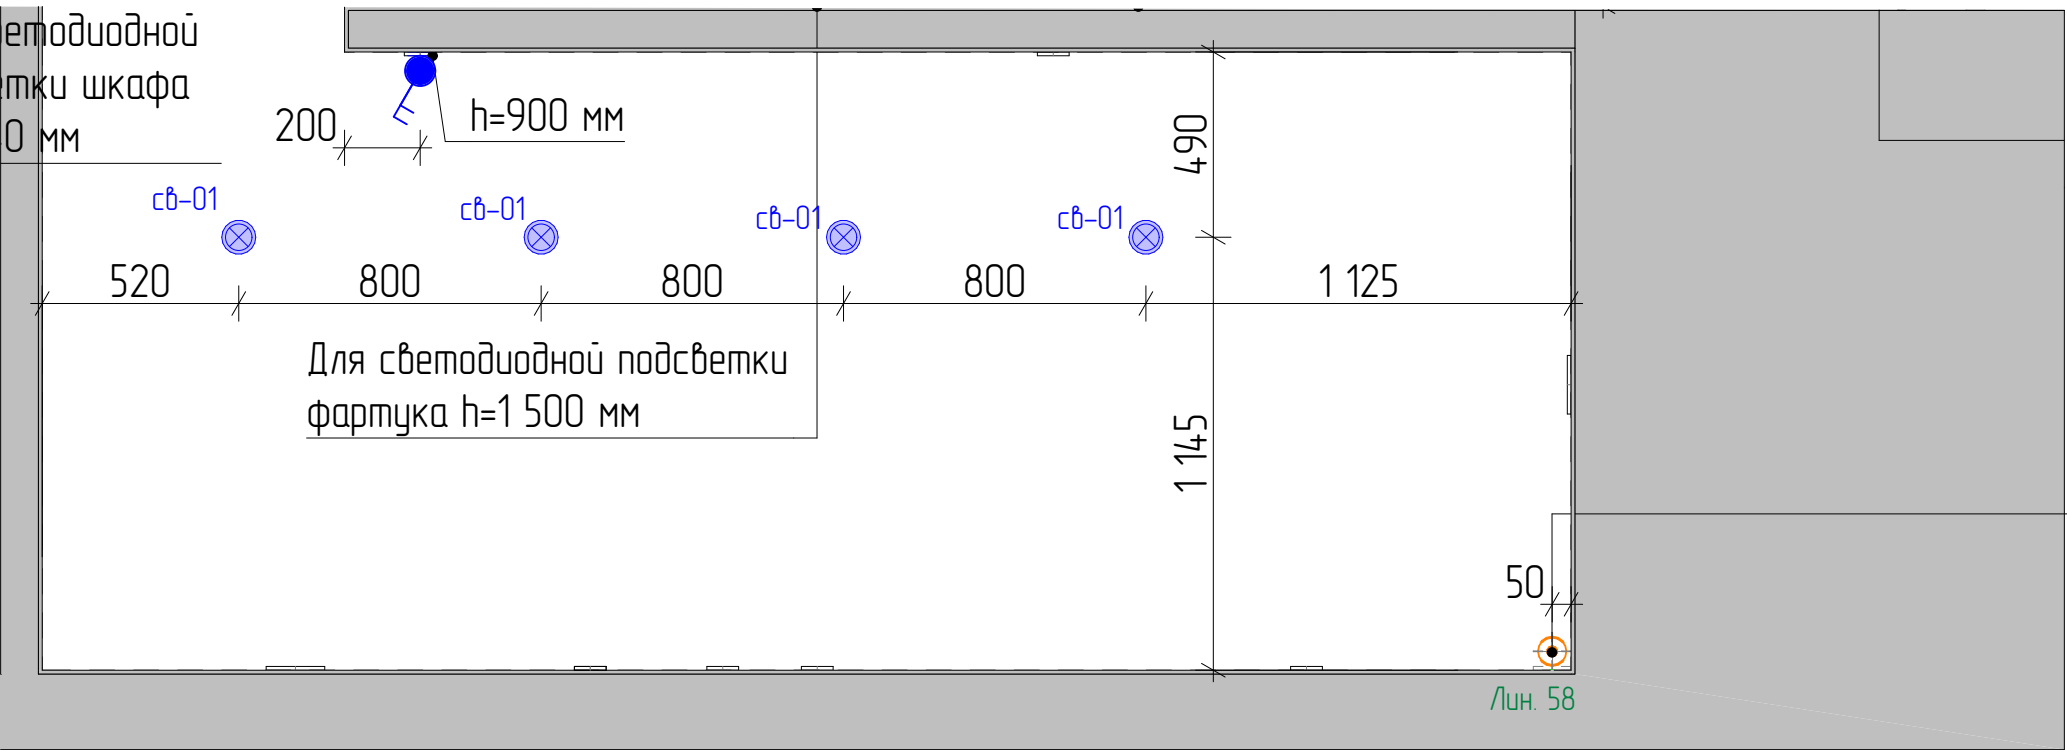

Примечания:

- * – размеры уточнить по месту.
- Розетки располагать от уровня чистого пола на высоте 0,300 м. Исключения указаны на чертеже.
- Размещение всех выводов и розеток согласовать со специалистами «Умный дом».
- Датчики пожарной и охранной сигнализации и электропроводы для них разместить совместно со специалистами, предварительно вызвав их на объект.
- Размещение розеток и электропроводов по высоте см. на развертках стен.


- Выключатели располагать от уровня чистого пола на высоте 0,900 м. Исключения указаны на чертеже.
- Светильники, встроенные в мебель, согласовать с изготовителями мебели.

- Условные обозначения:
- Розетка 220V влагозащищенная
 - Розетка 220V
 - Вывод электрокабеля для варочной поверхности
 - Диффузор, вытяжка
 - Светильник точечный встраиваемый
 - Выключатель двухклавишный


Для светодиодной подсветки шкафа h=2 720 мм

МСК 392.12.25-ЭП ПРЕМИУМ			
Эскизный дизайн-проект интерьера квартиры в г. Москва ЖК "Остров", ул. Нижние Мневники д. 7			
Кладовая.План размещения электрооборудования. План размещения освещения и выключателей.			
Дизайнер интерьера №1 Александр Батеньков	Стадия	Лист	Листов
	ЭП	53	120
		Подп.	Дата
ГАП	Батеньков А.С.		
Гл. дизайнер	Власова В.А.		
Гл. проектиров.	Луныкова В.Н.		
Разработал	Ильина Е.Е.		

Б-01 Развертка стены 1:25

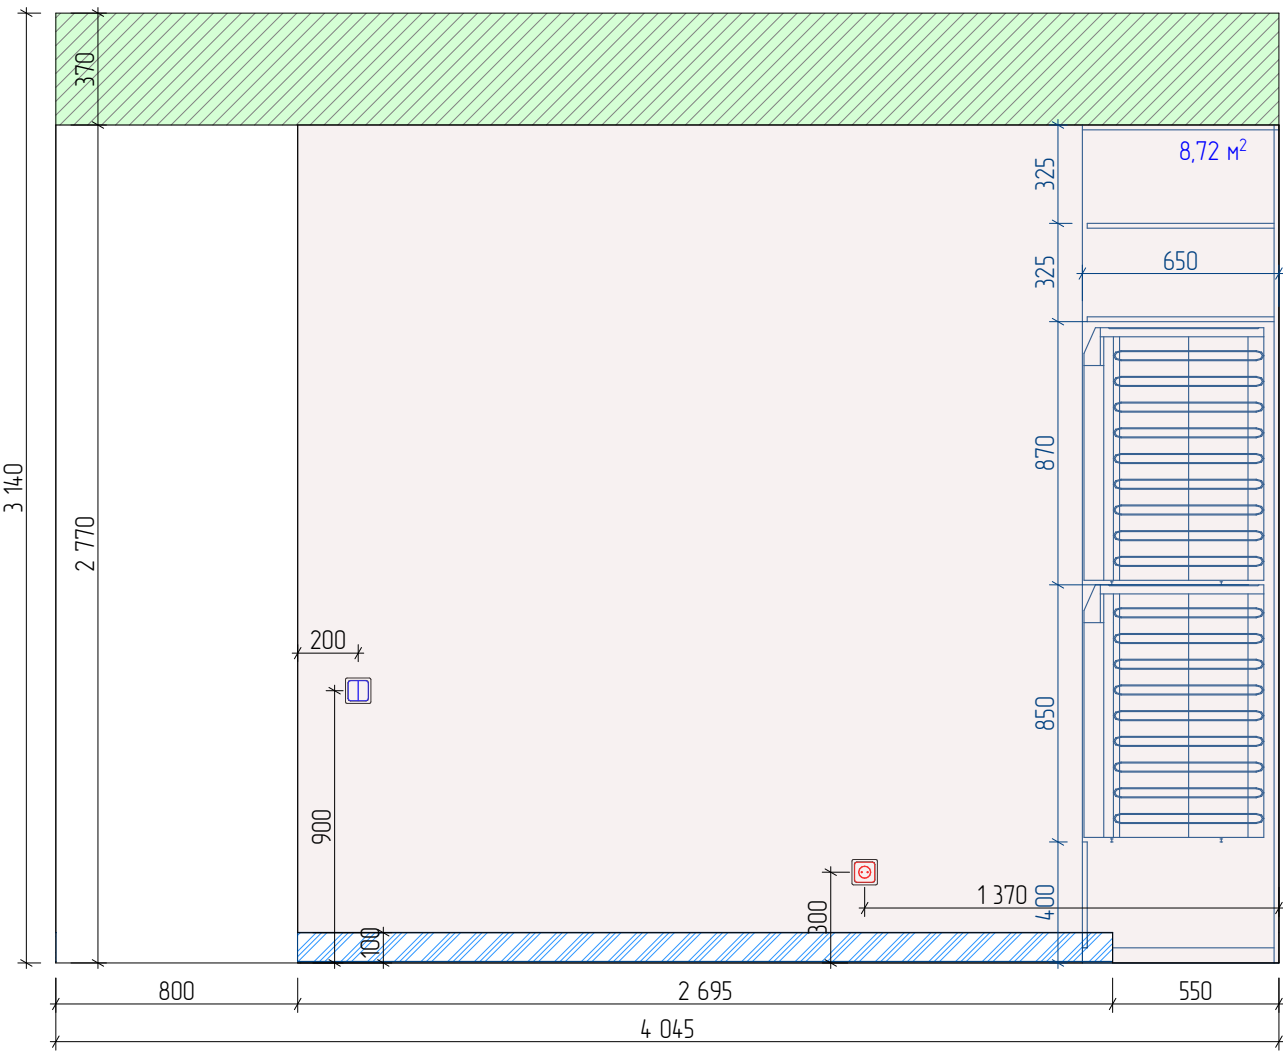

Б-02 Развертка стены 1:25

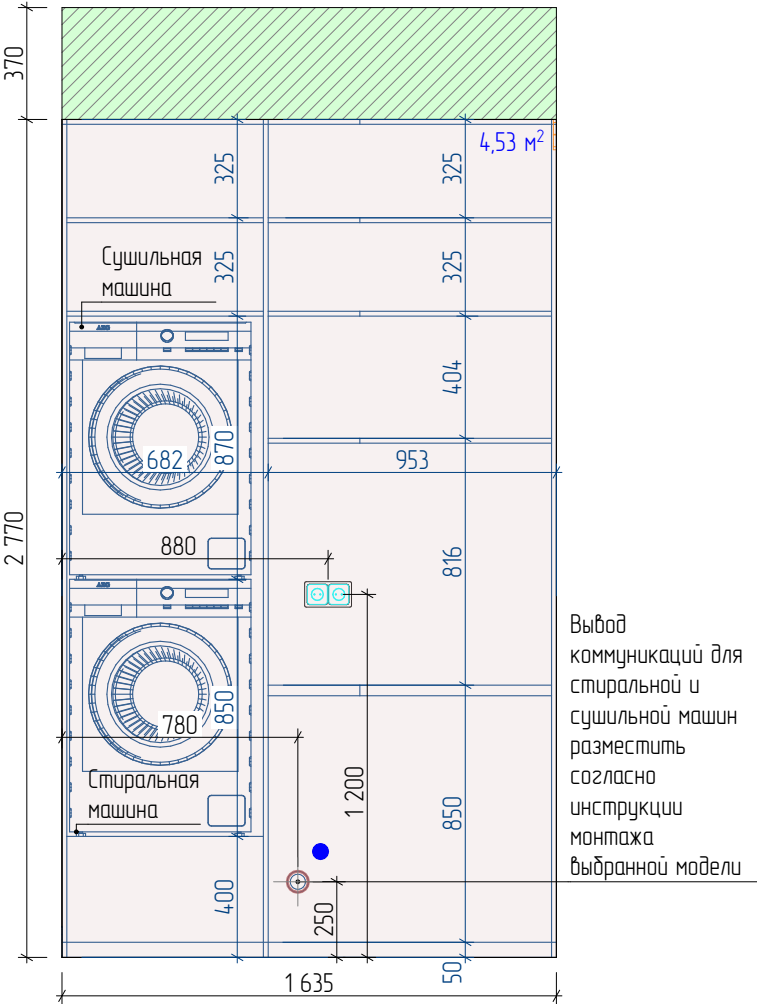

Вывод коммуникаций для стиральной и сушильной машин разместить согласно инструкции монтажа выбранной модели



Условные обозначения:

- Плинтус №1. Теневой плинтус скрытого монтажа с МДФ вставкой. Теневой зазор от пола 100 мм. Цвет при выборе образца (в цвет стен).
- Монтаж конструкций из ГКВ/Л
- Покраска №1. Выполнить по подготовленной поверхности (стеклохолст*). Цвет при выборе образца (бежевый*).
- Розетка 220 V, влагозащитенная IP44 и выше
- Розетка 220 V
- Выключатель двухклавишный
- Вывод коммуникаций (ХВС, ГВС, канал-ция)

Примечания:

- * – размеры уточнить по месту после выполнения черновых отделочных работ.
- Выключатели располагать от уровня чистого пола на высоте 900 мм. Исключения указаны на чертеже.
- Розетки располагать от уровня чистого пола на высоте 300 мм. Исключения указаны на чертеже.
- Цвет окрашивания плинтуса уточнить после согласования образца.
- Точную привязку выводов коммуникаций решить после выбора оборудования по инструкции монтажа.
- Предусмотреть гидроизоляцию пола с заведением на стену (150 мм).
- ** – размер уточнить по инструкции монтажа оборудования.
- Внутреннее наполнение мебели разработать со специалистами.
- Серым/синим цветом показаны размеры мебели. Мебель разработать со специалистами, размеры уточнить после выполнения чистовой отделки.

МСК 392.12.25-ЭП ПРЕМИУМ			
Эскизный дизайн-проект интерьера квартиры в г. Москва ЖК "Остров", ул. Нижние Мневники д. 7			
Кладовая.Развертки стен Б-01, Б-02.			
Дизайнер интерьера №1 Александр Батеньков	Стадия	Лист	Листов
	ЭП	54	120
		Подп.	Дата
ГАП	Батеньков А.С.		
Гл. дизайнер	Власова В.А.		
Гл. проектиров.	Луныкова В.Н.		
Разработал	Ильина Е.Е.		

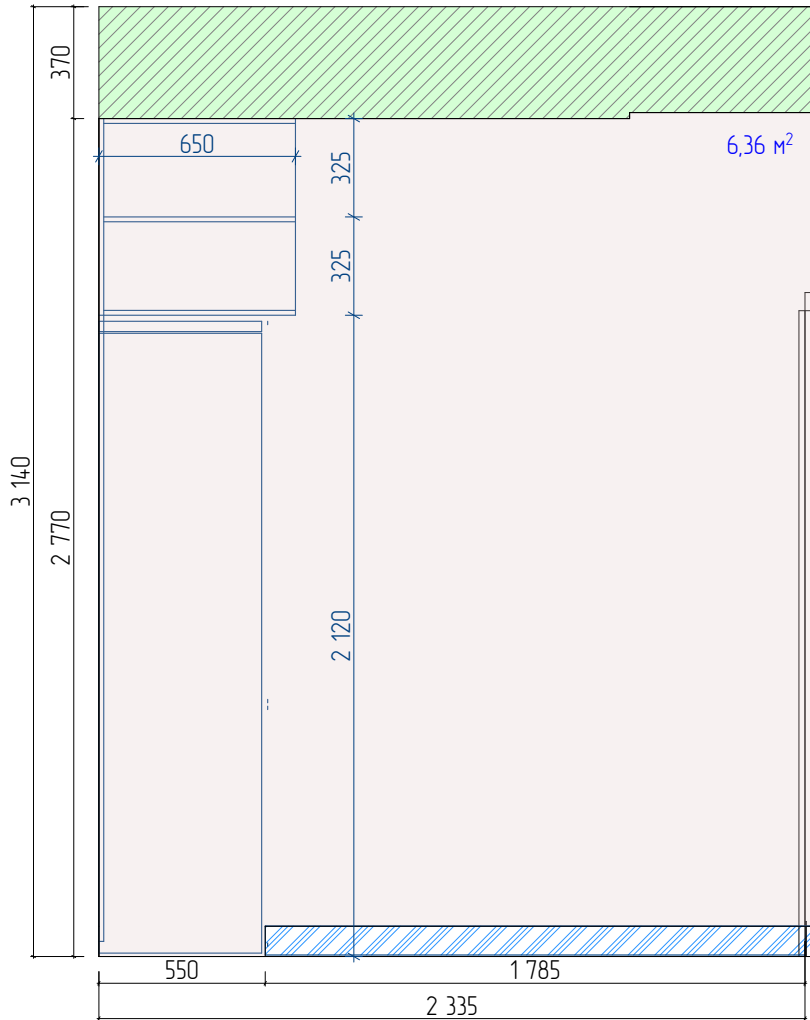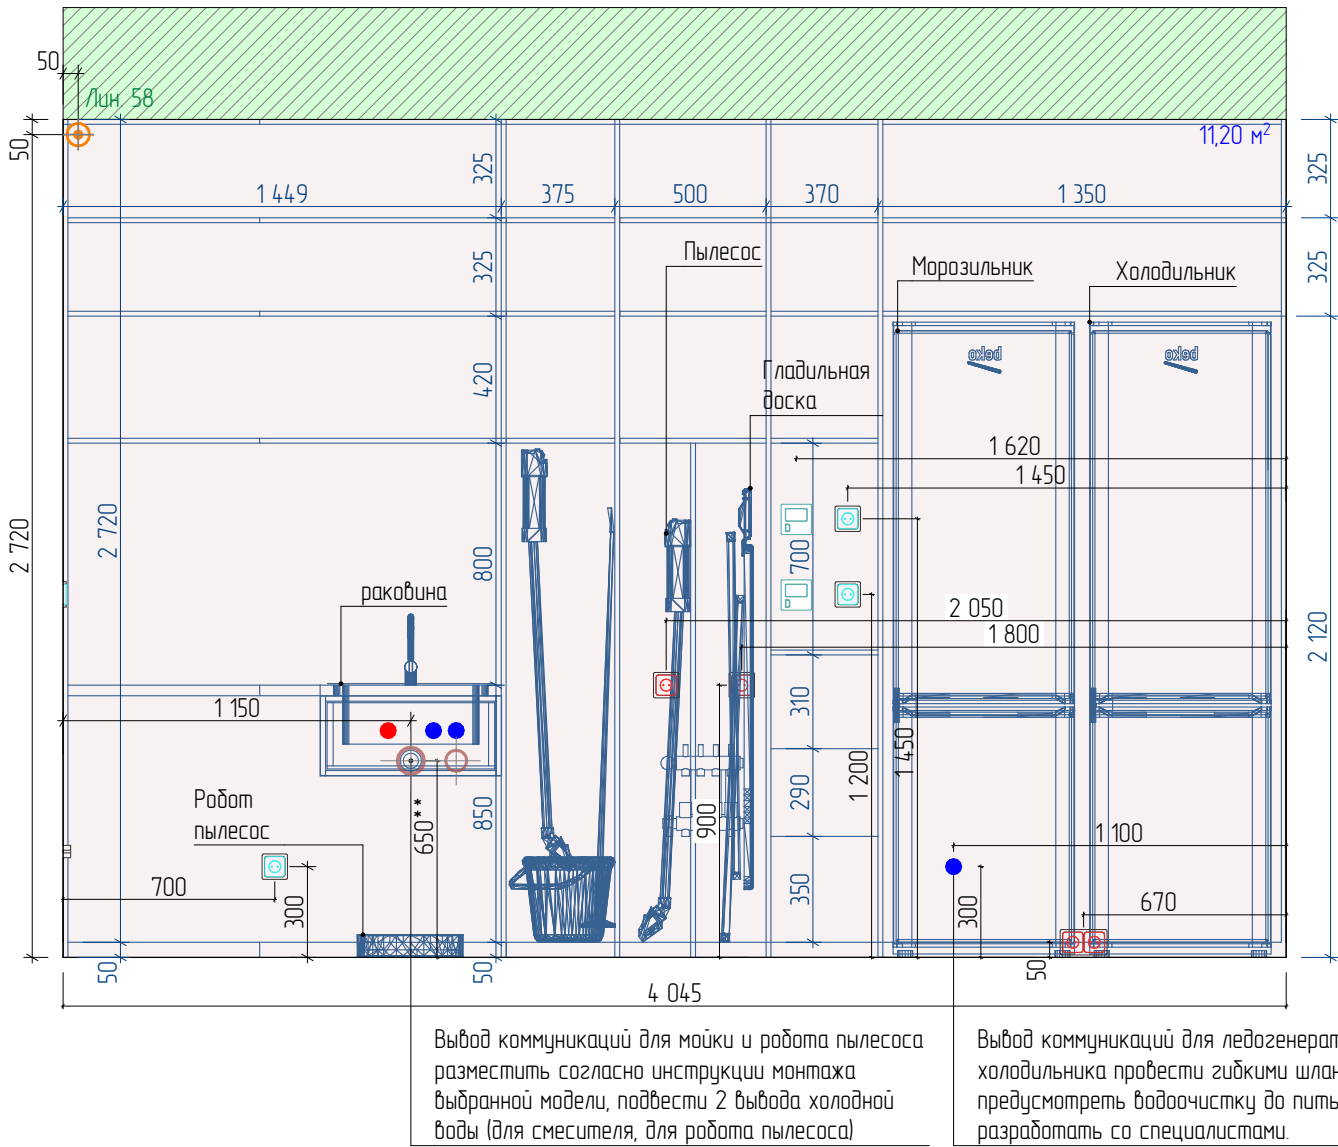

Ведомость отделочных материалов.

№	Обозначение	Наименование	Кол-во	Примечание
Пол:				
1		Покрытие №02. Керамогранит. Изготовитель: Elegant Grey, кол-я: Forte Dei Mariti, размер: 1200x1200 мм, толщину уточнить при заказе.	7,15 6	м² укладки шт.
Стены:				
2		Плинтус №1. Теневой плинтус скрытого монтажа с МДФ вставкой. Теневой зазор от пола 100 мм. Цвет при выборе образца (в цвет стен).	4,48	м.п.
3		Покраска №1. Выполнить по подготовленной поверхности (стеклохолст*). Цвет при выборе образца (бежевый*).	30,81	м²

Условные обозначения:

- Плинтус №1. Теневой плинтус скрытого монтажа с МДФ вставкой. Теневой зазор от пола 100 мм. Цвет при выборе образца (в цвет стен).
- Монтаж конструкций из ГКВЛ
- Покраска №1. Выполнить по подготовленной поверхности (стеклохолст*). Цвет при выборе образца (бежевый*).
- Вывод электрокабеля для светодиодной ленты
- Розетка 220 V, влагозащищенная IP44 и выше
- Розетка 220 V
- Вывод коммуникаций (ХВС, ГВС, канал-ция)

Примечания:

- * – размеры уточнить по месту после выполнения черновых отделочных работ.
- Выключатели располагать от уровня чистого пола на высоте 900 мм. Исключения указаны на чертеже.
- Розетки располагать от уровня чистого пола на высоте 300 мм. Исключения указаны на чертеже.
- Цвет окрашивания плинтуса уточнить после согласования образца.
- Точную привязку выводов коммуникаций решить после выбора оборудования по инструкции монтажа.
- Предусмотреть гидроизоляцию пола с заведением на стену (150 мм).
- ** – размер уточнить по инструкции монтажа оборудования.
- Внутреннее наполнение мебели разработать со специалистами.
- Серым/синим цветом показаны размеры мебели. Мебель разработать со специалистами, размеры уточнить после выполнения чистовой отделки.

МСК 392.12.25–ЭП ПРЕМИУМ			
Эскизный дизайн-проект интерьера квартиры в г. Москва ЖК "Остров", ул. Нижние Мневники д. 7			
Кладовая.Развертки стен Б-03, Б-04. Ведомость отделочных материалов.			
Дизайнер интерьера №1 Александр Батеньков	Стадия	Лист	Листов
	ЭП	55	120
		Подп.	Дата
ГАП	Батеньков А.С.		
Гл. дизайнер	Власова В.А.		
Гл. проектиров.	Луныкова В.Н.		
Разработал	Ильина Е.Е.		