


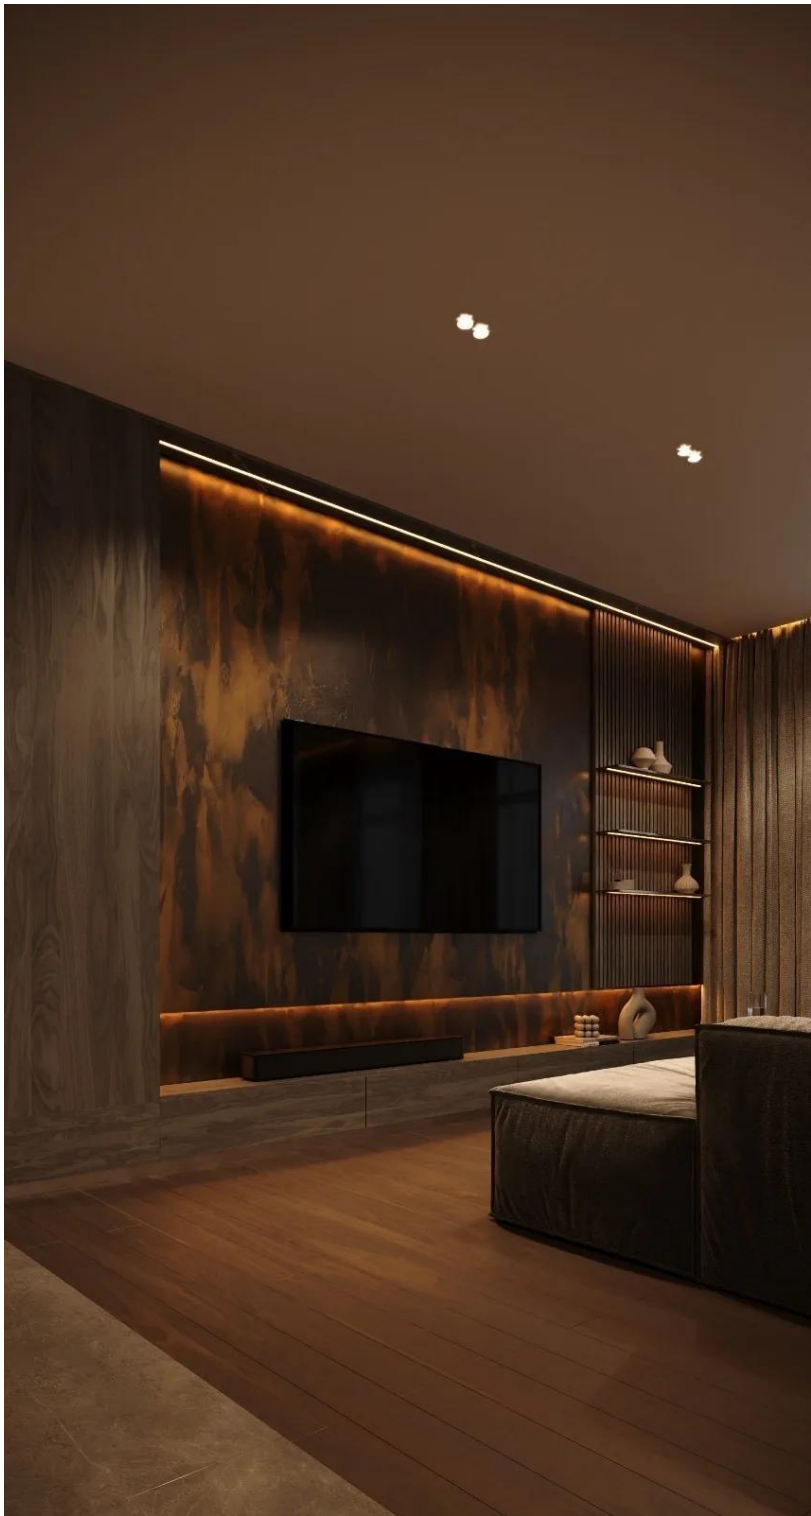


МСК 392.12.25-ЭП ПРЕМИУМ			
Эскизный дизайн-проект интерьера квартиры в г. Москва ЖК "Остров", ул. Нижние Мневники д. 7			
Прихожая Кухня Гостиная.Видовые точки.			
Дизайнер интерьера  Александр Батеньков	Стадия	Лист	Листов
	ЭП	35	120
		Подп.	Дата
ГАП	Батеньков А.С.		
Гл. дизайнер	Власова В.А.		
Гл. проектиров.	Луныкова В.Н.		
Разработал	Ильина Е.Е.		



МСК 392.12.25-ЭП ПРЕМИУМ			
Эскизный дизайн-проект интерьера квартиры в г. Москва ЖК "Остров", ул. Нижние Мневники д. 7			
Прихожая Кухня Гостиная. Видовые точки.			
Дизайнер интерьера  Александр Батеньков	Стадия	Лист	Листов
	ЭП	36	120
		Подп.	Дата
ГАП	Батеньков А.С.		
Гл. дизайнер	Власова В.А.		
Гл. проектиров.	Луныкова В.Н.		
Разработал	Ильина Е.Е.		



МСК 392.12.25-ЭП ПРЕМИУМ			
Эскизный дизайн-проект интерьера квартиры в г. Москва ЖК "Остров", ул. Нижние Мневники д. 7			
Прихожая Кухня ГостинаяВидовые точки.			
Дизайнер интерьера  Александр Батеньков	Стадия	Лист	Листов
	ЭП	37	120
		Подп.	Дата
ГАП	Батеньков А.С.		
Гл. дизайнер	Власова В.А.		
Гл. проектиров.	Луныкова В.Н.		
Разработал	Ильина Е.Е.		

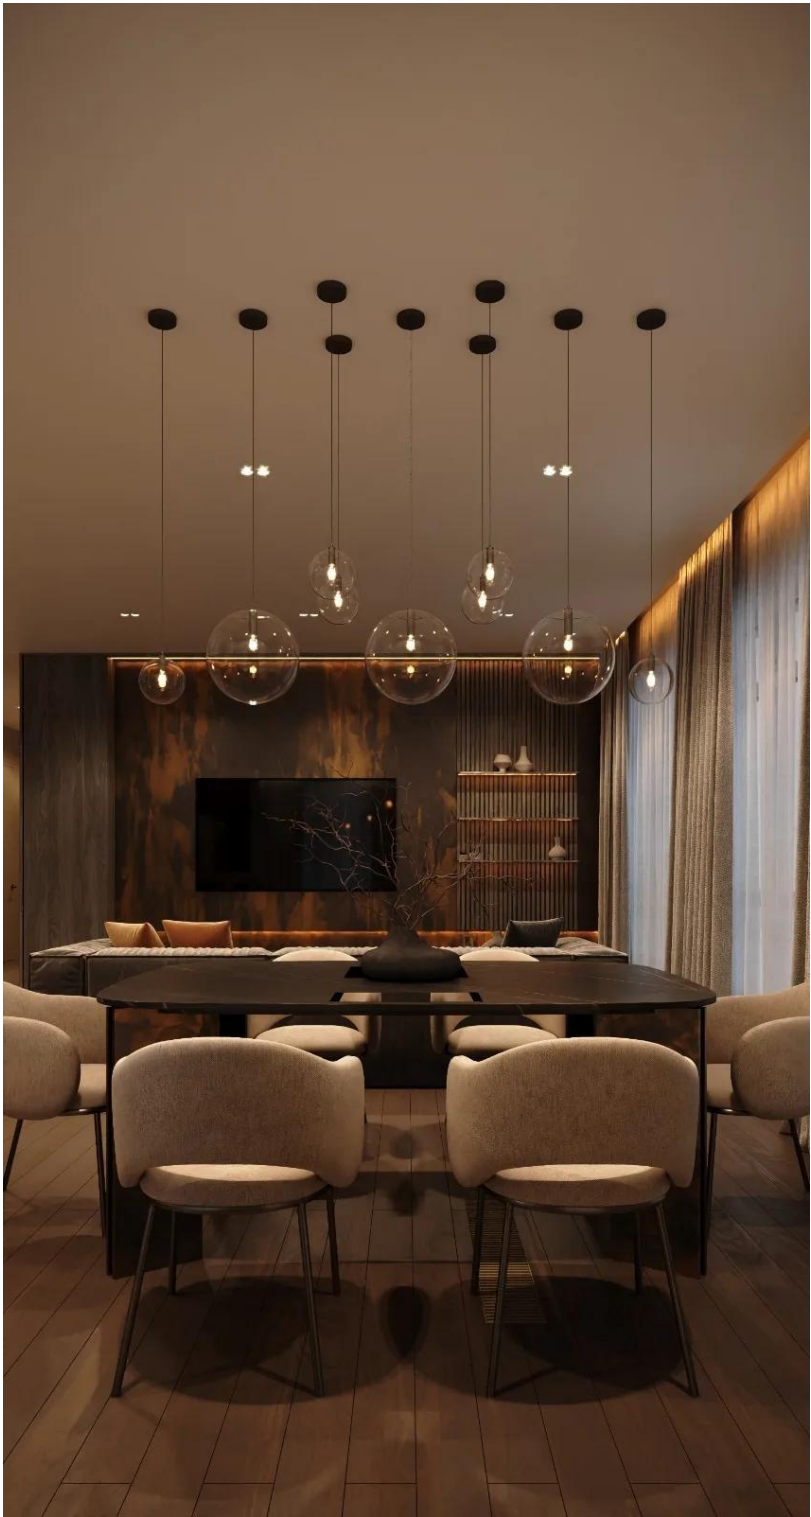

МСК 392.12.25-ЭП ПРЕМИУМ			
Эскизный дизайн-проект интерьера квартиры в г. Москва ЖК "Остров", ул. Нижние Мневники д. 7			
Прихожая Кухня Гостиная. Видовые точки.			
Дизайнер интерьера  Александр Батеньков	Стадия	Лист	Листов
	ЭП	38	120
		Подп.	Дата
ГАП	Батеньков А.С.		
Гл. дизайнер	Власова В.А.		
Гл. проектиров.	Луныкова В.Н.		
Разработал	Ильина Е.Е.		




МСК 392.12.25-ЭП ПРЕМИУМ			
Эскизный дизайн-проект интерьера квартиры в г. Москва ЖК "Остров", ул. Нижние Мневники д. 7			
Прихожая Кухня Гостиная. Видовые точки.			
Дизайнер интерьера  Александр Батеньков	Стадия	Лист	Листов
	ЭП	39	120
		Подп.	Дата
ГАП	Батеньков А.С.		
Гл. дизайнер	Власова В.А.		
Гл. проектиров.	Луныкова В.Н.		
Разработал	Ильина Е.Е.		



МСК 392.12.25-ЭП ПРЕМИУМ			
Эскизный дизайн-проект интерьера квартиры в г. Москва ЖК "Остров", ул. Нижние Мневники д. 7			
Прихожая Кухня Гостиная.Видовые точки.			
Дизайнер интерьера  Александр Батеньков	Стадия	Лист	Листов
	ЭП	40	120
		Подп.	Дата
ГАП	Батеньков А.С.		
Гл. дизайнер	Власова В.А.		
Гл. проектиров.	Луныкова В.Н.		
Разработал	Ильина Е.Е.		



МСК 392.12.25-ЭП ПРЕМИУМ			
Эскизный дизайн-проект интерьера квартиры в г. Москва ЖК "Остров", ул. Нижние Мневники д. 7			
Прихожая Кухня Гостиная. Видовые точки.			
Дизайнер интерьера  №1 Александр Батеньков	Стадия	Лист	Листов
	ЭП	41	120
		Подп.	Дата
ГАП	Батеньков А.С.		
Гл. дизайнер	Власова В.А.		
Гл. проектиров.	Луныкова В.Н.		
Разработал	Ильина Е.Е.		

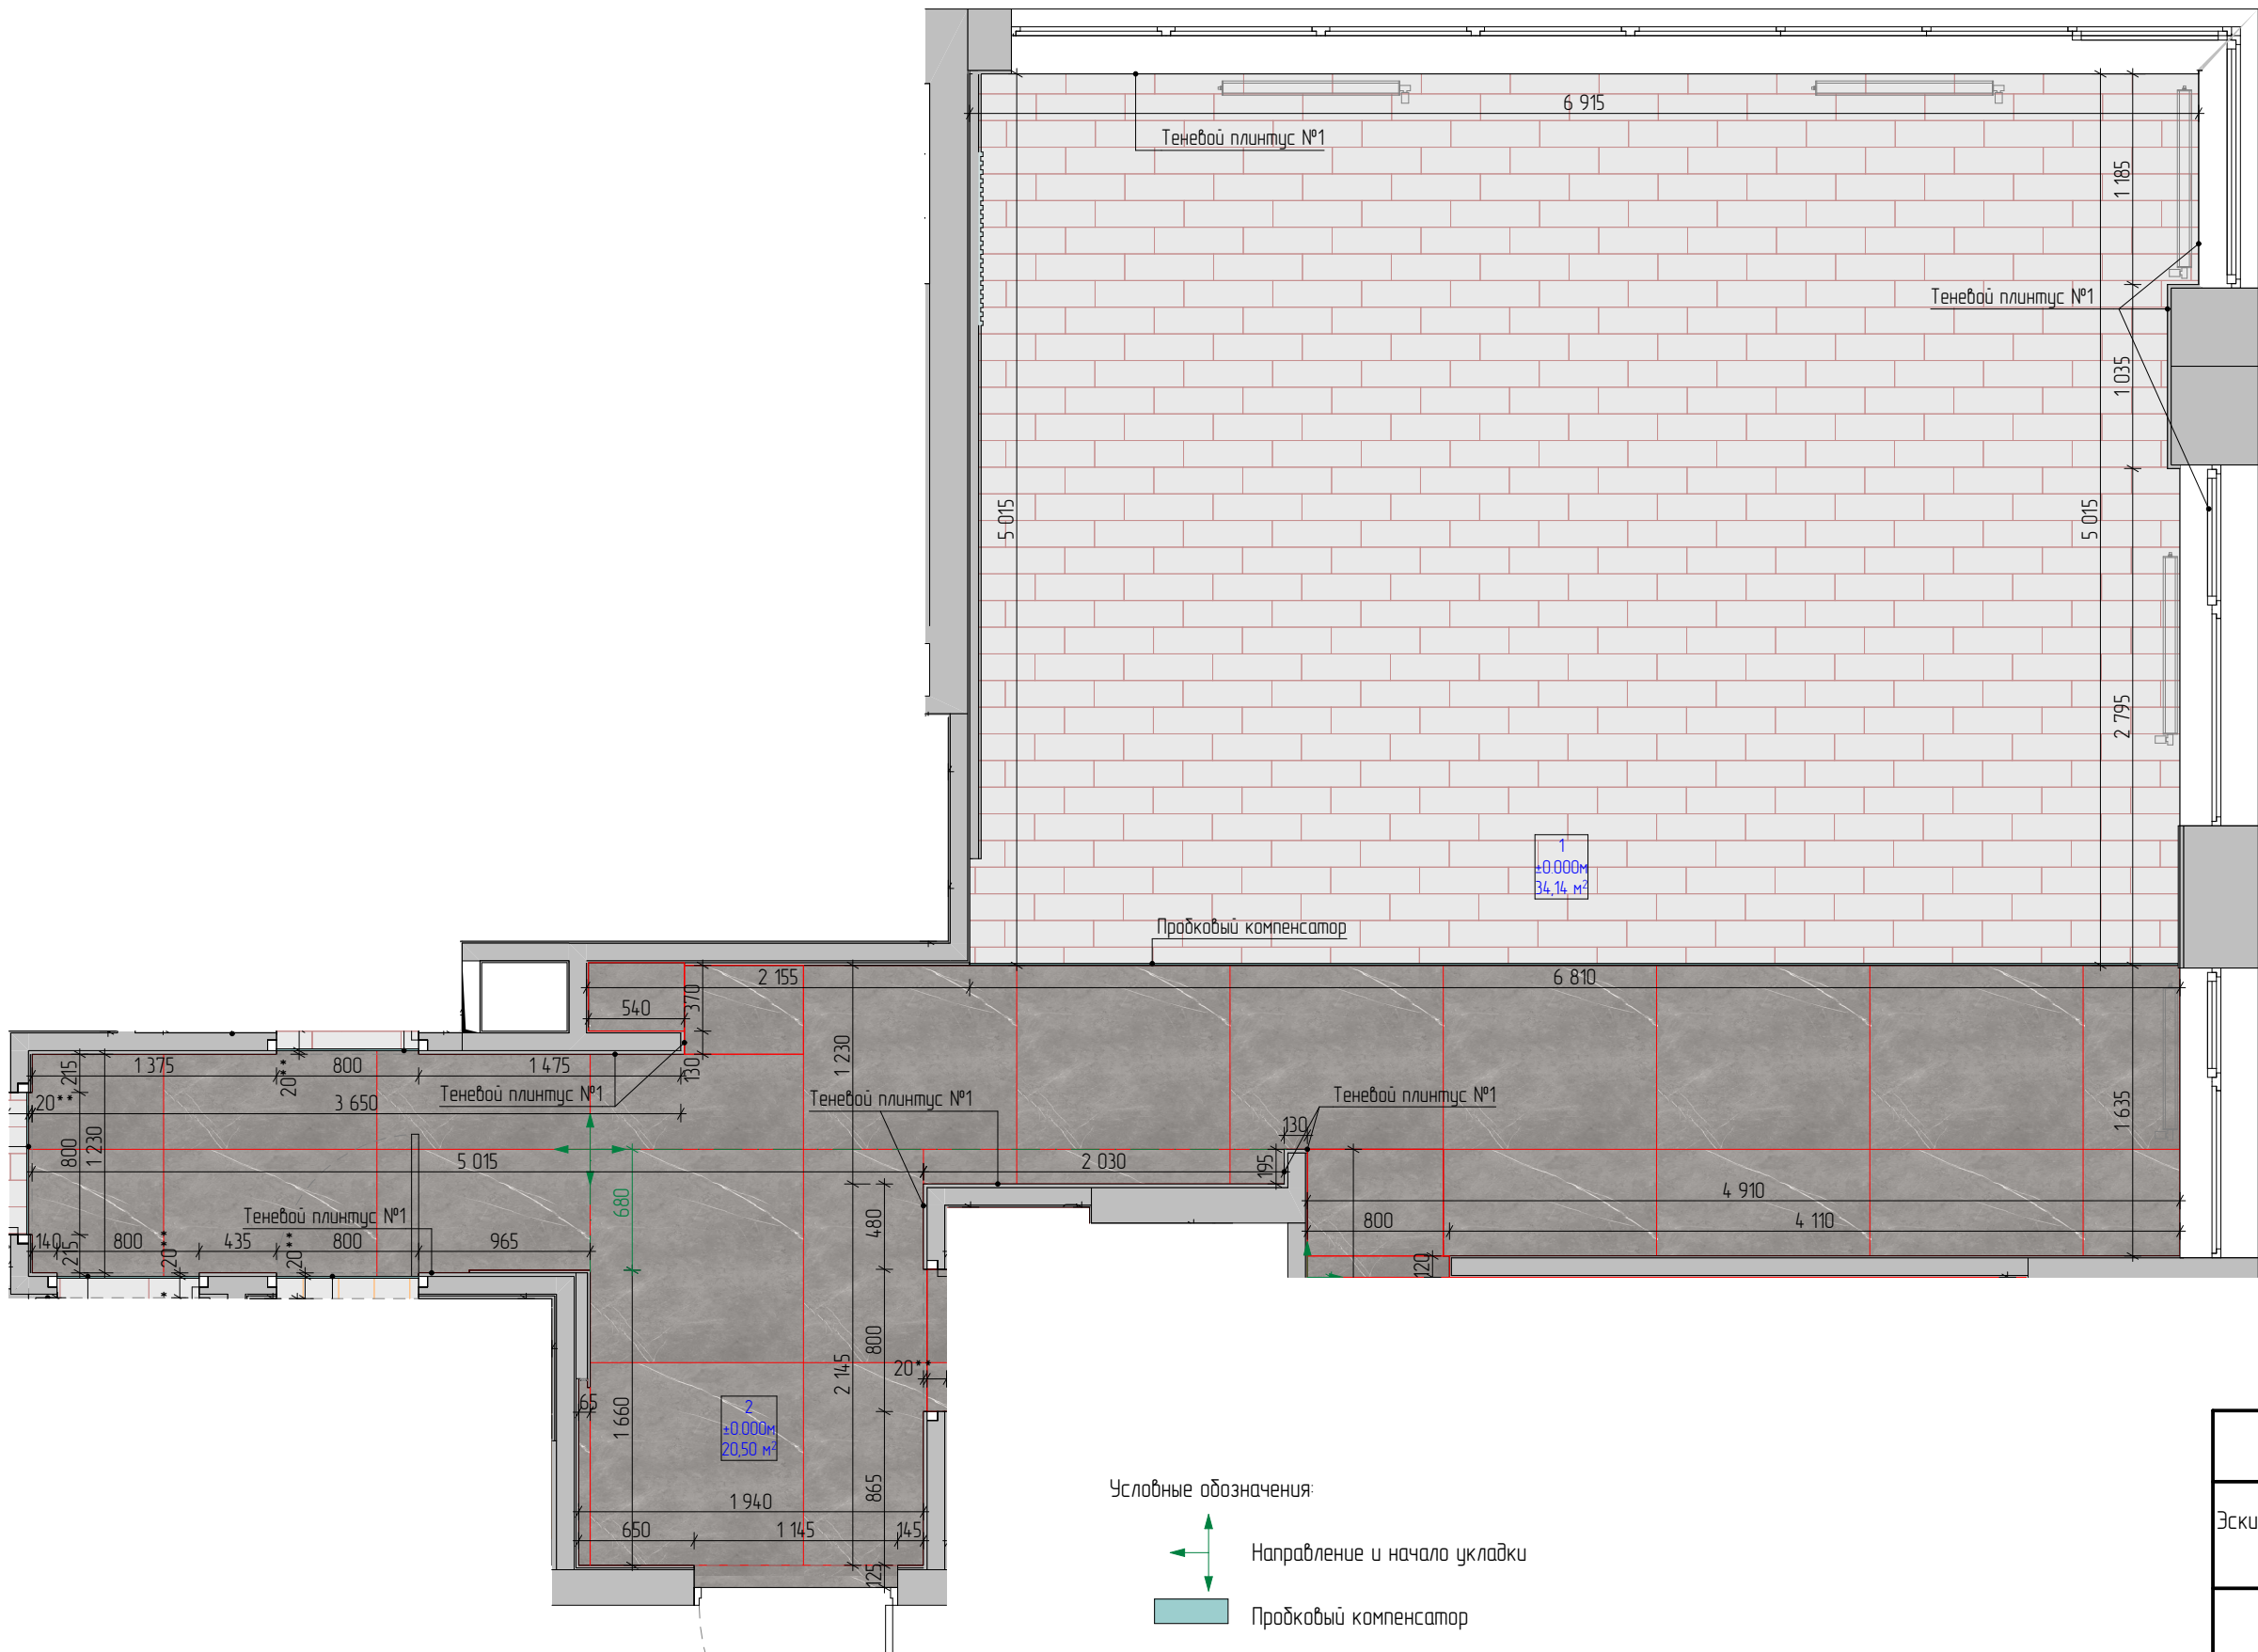

Примечания:

- *- размеры уточнить по месту после выполнения черновых отделочных работ.
- За отметку ±0,000 принят уровень чистого пола.
- При монтаже напольных покрытий уточнить необходимость устройства дверных проемов с порогом.
- *- размеры уточнить по месту после выполнения черновых отделочных работ и установки дверей со скрытой коробкой.
- **-размер уточнить по месту в зависимости от точного расположения полотна двери, стыковка двух разных напольных покрытий должна проходить точно по центру вдоль дверного полотна.


Условные обозначения:

Направление и начало укладки

Пороговый компенсатор

- Покрытие №01. Паркет. Изготовитель: Lab Arte, кол-я: Angle Дуб Натур, размер: 500x150 мм, точный артикул и производителя уточнить при выборе образца, толщину уточнить при покупке..
- Покрытие №02. Керамогранит. Изготовитель: Elegant Grey, кол-я: Forte Dei Marmi, размер: 1200x1200 мм, толщину уточнить при покупке.

МСК 392.12.25-ЭП ПРЕМИУМ			
Эскизный дизайн-проект интерьера квартиры в г. Москва ЖК "Остров", ул. Нижние Мневники д. 7			
Прихожая Кухня ГостинаяПлан отделки пола			
Дизайнер интерьера №1 Александр Батеньков	Стадия	Лист	Листов
	ЭП	42	120
		Подп.	Дата
ГАП	Батеньков А.С.		
Гл. дизайнер	Власова В.А.		
Гл. проектиров.	Луцькова В.Н.		
Разработал	Ильина Е.Е.		

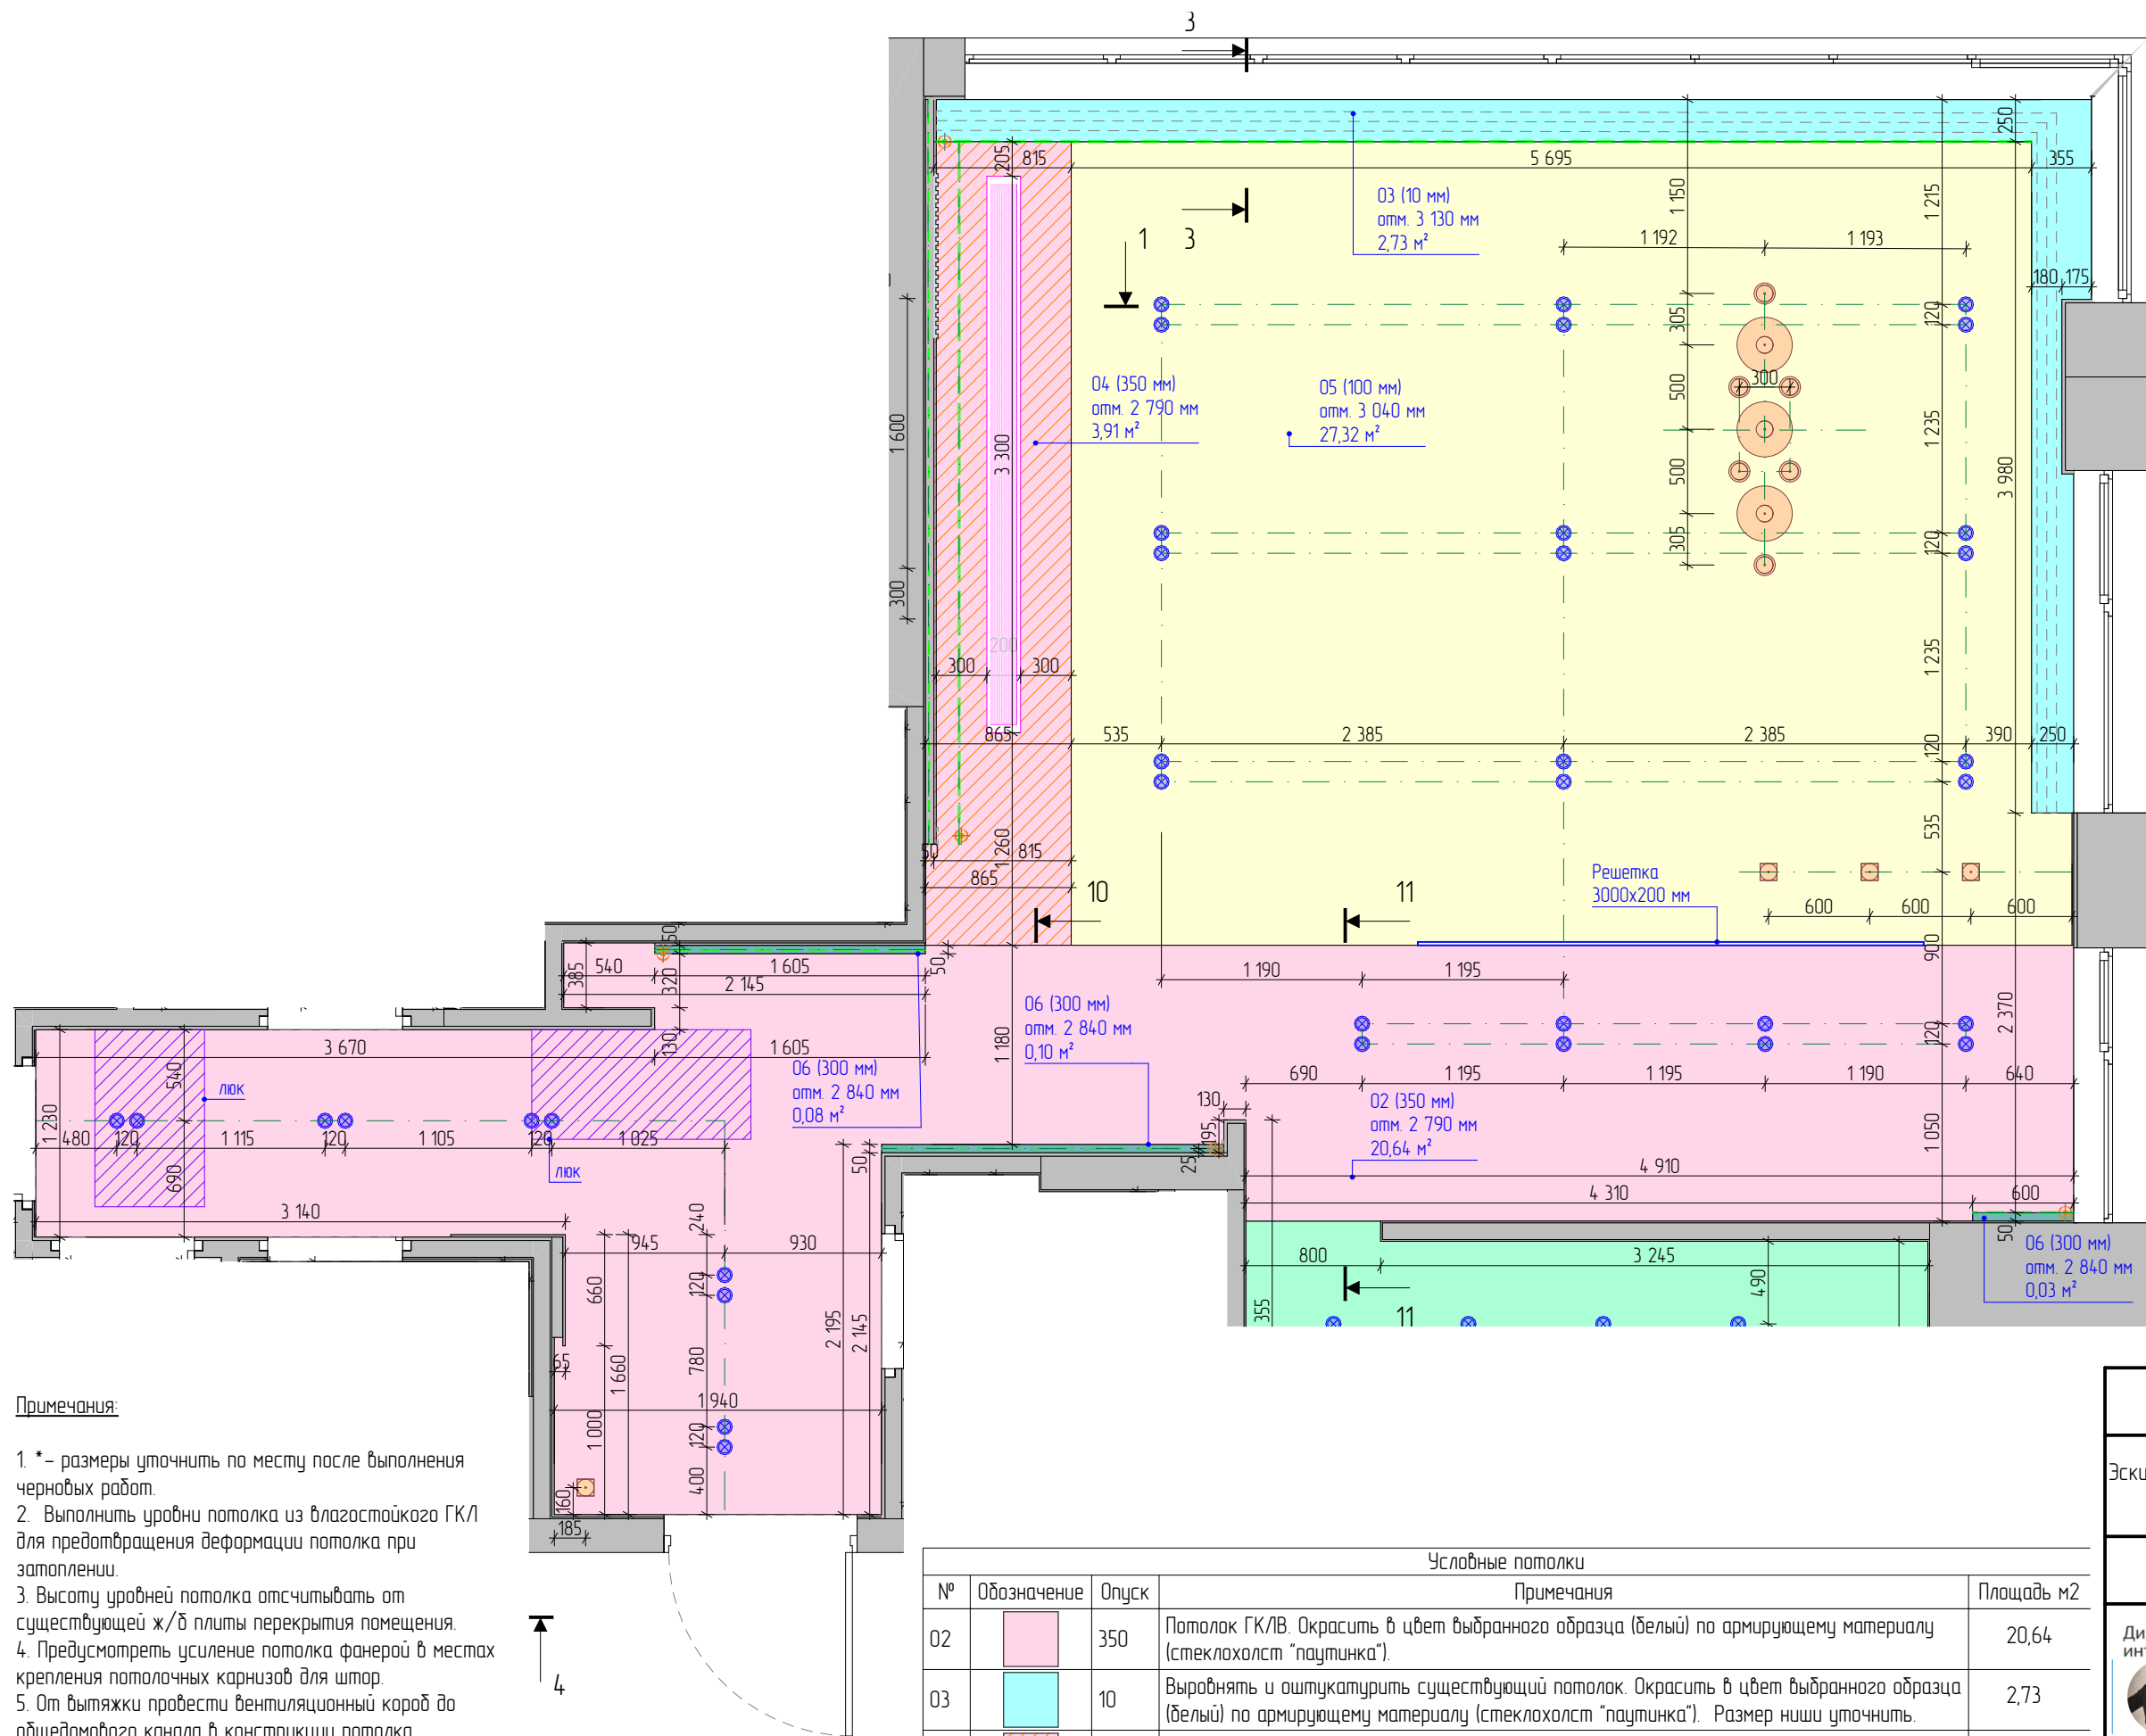


- Условные обозначения:
- Выход электрокабеля для светодиодной ленты
 - Люстра подвесная потолочная
 - Светильник точечный встраиваемый
 - Светодиодная лента
 - Люк доступа

Примечания:

- * – размеры уточнить по месту после выполнения черновых работ.
- Выполнить уровни потолка из влагостойкого ГКЛ для предотвращения деформации потолка при затоплении.
- Высоту уровней потолка отсчитывать от существующей ж/б плиты перекрытия помещения.
- Предусмотреть усиление потолка фанерой в местах крепления потолочных карнизов для штор.
- От вытяжки провести вентиляционный короб до общедомового канала в конструкции потолка, уточнить по месту со специалистами и заказчиком.
- Шумоизоляцию разработать со специалистами, уточнить состав и толщину слоев шумоизоляционных материалов. Уточнить необходимость устройства с заказчиком.

Условные потолки				
№	Обозначение	Опуск	Примечания	Площадь м2
02		350	Потолок ГК/ЛВ. Окрасить в цвет выбранного образца (белый) по армирующему материалу (стеклохолст "паутинка").	20,64
03		10	Выровнять и оштукатурить существующий потолок. Окрасить в цвет выбранного образца (белый) по армирующему материалу (стеклохолст "паутинка"). Размер ниши уточнить.	2,73
04		350	Потолок ГК/ЛВ с МДФ панелью. Цвет выбранного образца (*коричневый) уточнить при закупе.	3,91
05		100	Потолок ГК/ЛВ. Окрасить в цвет выбранного образца (белый) по армирующему материалу (стеклохолст "паутинка").	27,32
06		300	Потолок ГК/ЛВ. Окрасить в цвет выбранного образца (белый) по армирующему материалу (стеклохолст "паутинка").	0,21


МСК 392.12.25-ЭП ПРЕМИУМ				
Эскизный дизайн-проект интерьера квартиры в г. Москва ЖК "Остров", ул. Нижние Мневники д. 7				
Прихожая Кухня Гостиная.План отделки потолка.				
Дизайнер интерьера №1 Александр Батеньков	Стадия	Лист	Листов	
	ЭП	43	120	
		Подп.	Дата	
ГАП	Батеньков А.С.			
Гл. дизайнер	Власова В.А.			
Гл. проектиров.	Луныкова В.Н.			
Разработал	Ильина Е.Е.			

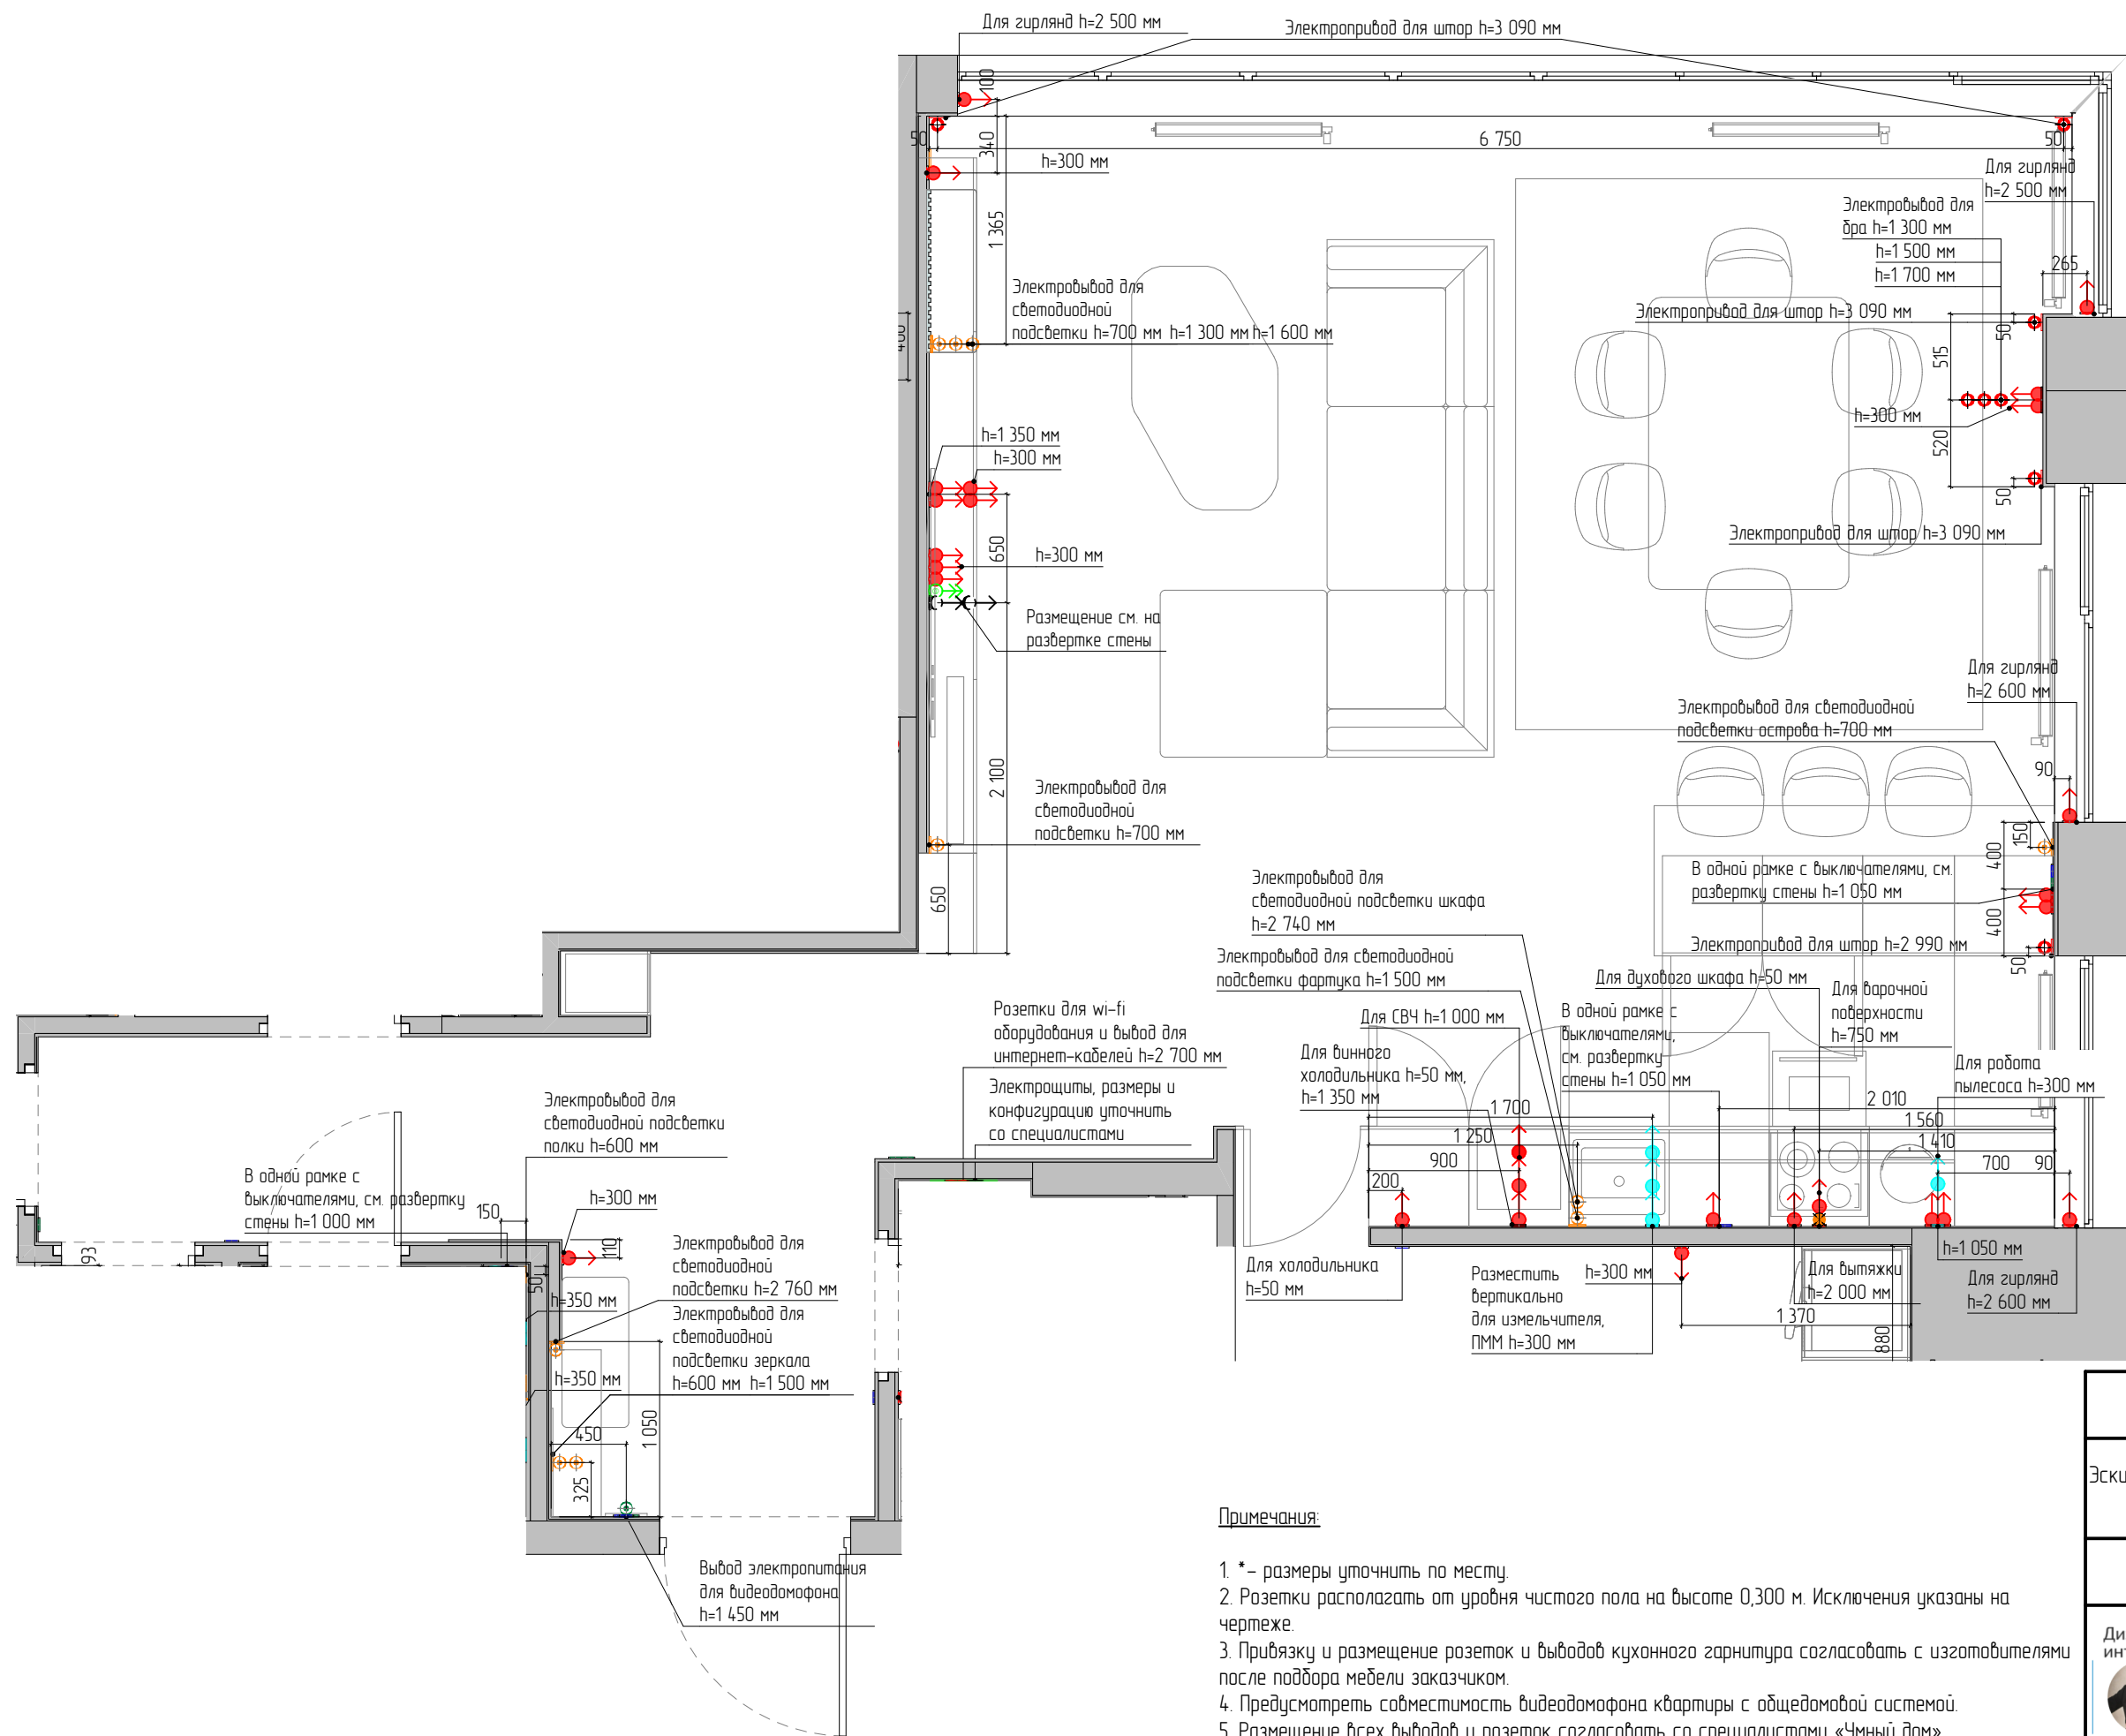

- Условные обозначения:
- Розетка 220V влагозащищенная
 - Розетка 220V
 - Вывод электрокабеля для светодиодной ленты
 - Вывод электрокабеля для варочной поверхности
 - Вывод спец. кабеля
 - Вывод интернет кабеля
 - wi-fi оборудование

- Примечания:
- * – размеры уточнить по месту.
 - Розетки располагать от уровня чистого пола на высоте 0,300 м. Исключения указаны на чертеже.
 - Приязку и размещение розеток и выводов кухонного гарнитура согласовать с изготовителями после подбора мебели заказчиком.
 - Предусмотреть совместимость видеодомофона квартиры с общедомовой системой.
 - Размещение всех выводов и розеток согласовать со специалистами «Умный дом».
 - Размеры и характеристики радиаторов отопления согласовать со специалистами, предусмотреть терморегуляторы.
 - Датчики пожарной и охранной сигнализации и электровыводы для них разместить совместно со специалистами, предварительно вызвав их на объект.
 - Размещение розеток и электровыводов по высоте см. на развертках стен.

МСК 392.12.25–ЭП ПРЕМИУМ			
Эскизный дизайн–проект интерьера квартиры в г. Москва ЖК "Остров", ул. Нижние Мневники д. 7			
Прихожая Кухня Гостиная.План размещения электрооборудования.			
Дизайнер интерьера №1 Александр Батеньков	Стадия	Лист	Листов
	ЭП	44	120
		Подп.	Дата
ГАП	Батеньков А.С.		
Гл. дизайнер	Власова В.А.		
Гл. проектиров.	Луныкова В.Н.		
Разработал	Ильина Е.Е.		






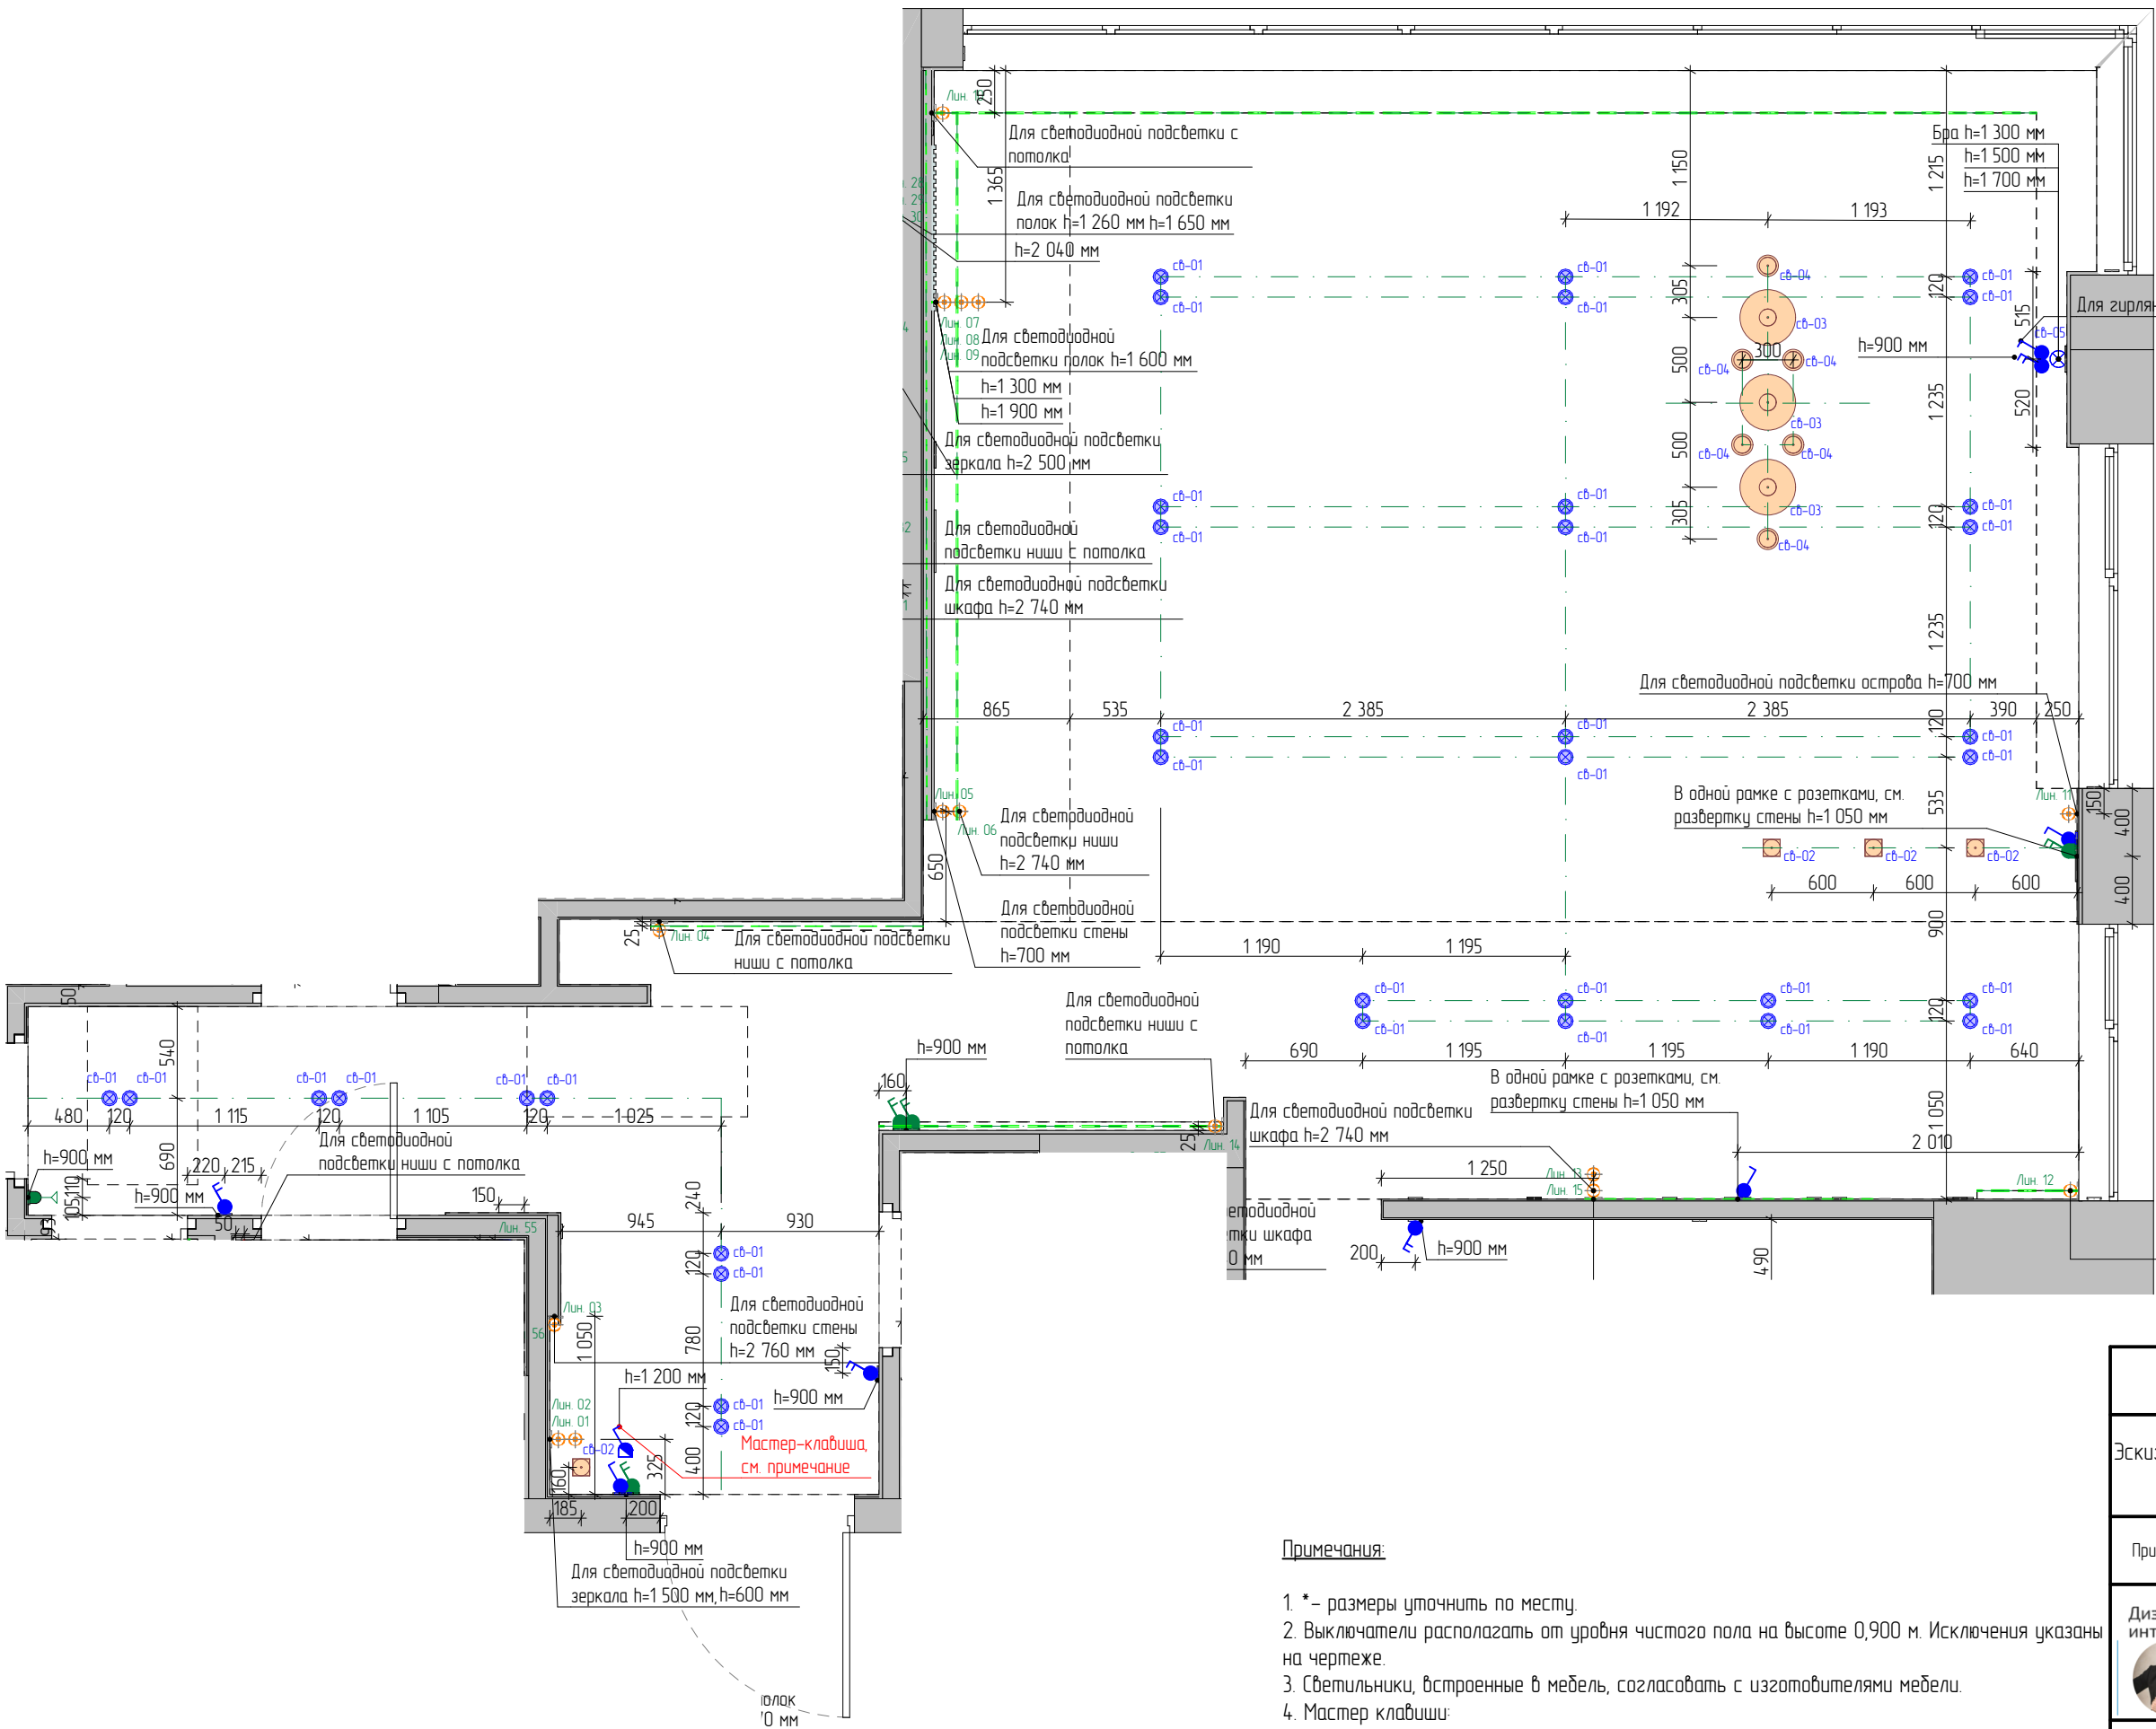


- Условные обозначения:
- Выход 220V
 - Выход электрокабеля для светодиодной ленты
 - Выключатель одноклавишный
 - Выключатель двухклавишный
 - Люстра подвесная потолочная
 - Переключатель двухклавишный
 - Переключатель одноклавишный переходной
 - Светильник точечный встраиваемый
 - Светодиодная лента

Примечания:

- * – размеры уточнить по месту.
- Выключатели располагать от уровня чистого пола на высоте 0,900 м. Исключения указаны на чертеже.
- Светильники, встроенные в мебель, согласовать с изготовителями мебели.
- Мастер клавиш:
№1 – выключение всего освещения квартиры, размещение согласовать с заказчиком при начале строительных работ;
№2 – выключение электропитания (розетки) кроме холодильника, морозильных камер, охранной сигнализации, датчиков протечки и др. по согласованию с заказчиком непосредственно на объекте.

МСК 392.12.25–ЭП ПРЕМИУМ			
Эскизный дизайн–проект интерьера квартиры в г. Москва ЖК "Остров", ул. Нижние Мневники д. 7			
Прихожая Кухня ГостинаяПлан размещения освещения и выключателей.			
Дизайнер интерьера №1 Александр Батеньков	Стадия	Лист	Листов
	ЭП	45	120
		Подп.	Дата
ГАП	Батеньков А.С.		
Гл. дизайнер	Власова В.А.		
Гл. проектиров.	Луныкова В.Н.		
Разработал	Ильина Е.Е.		

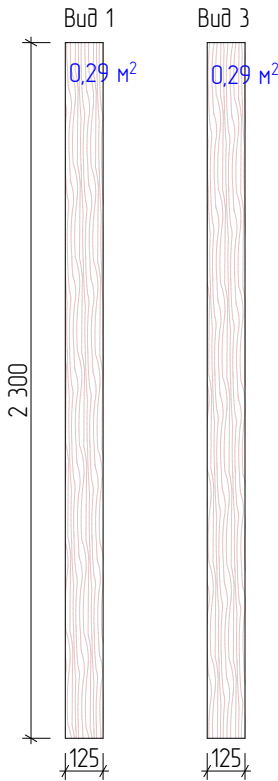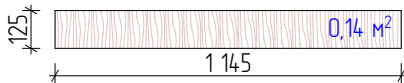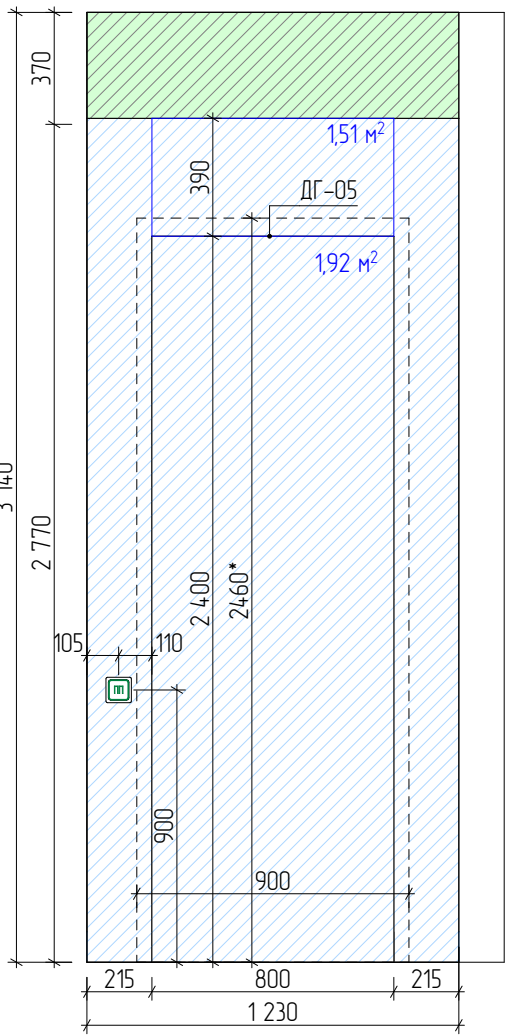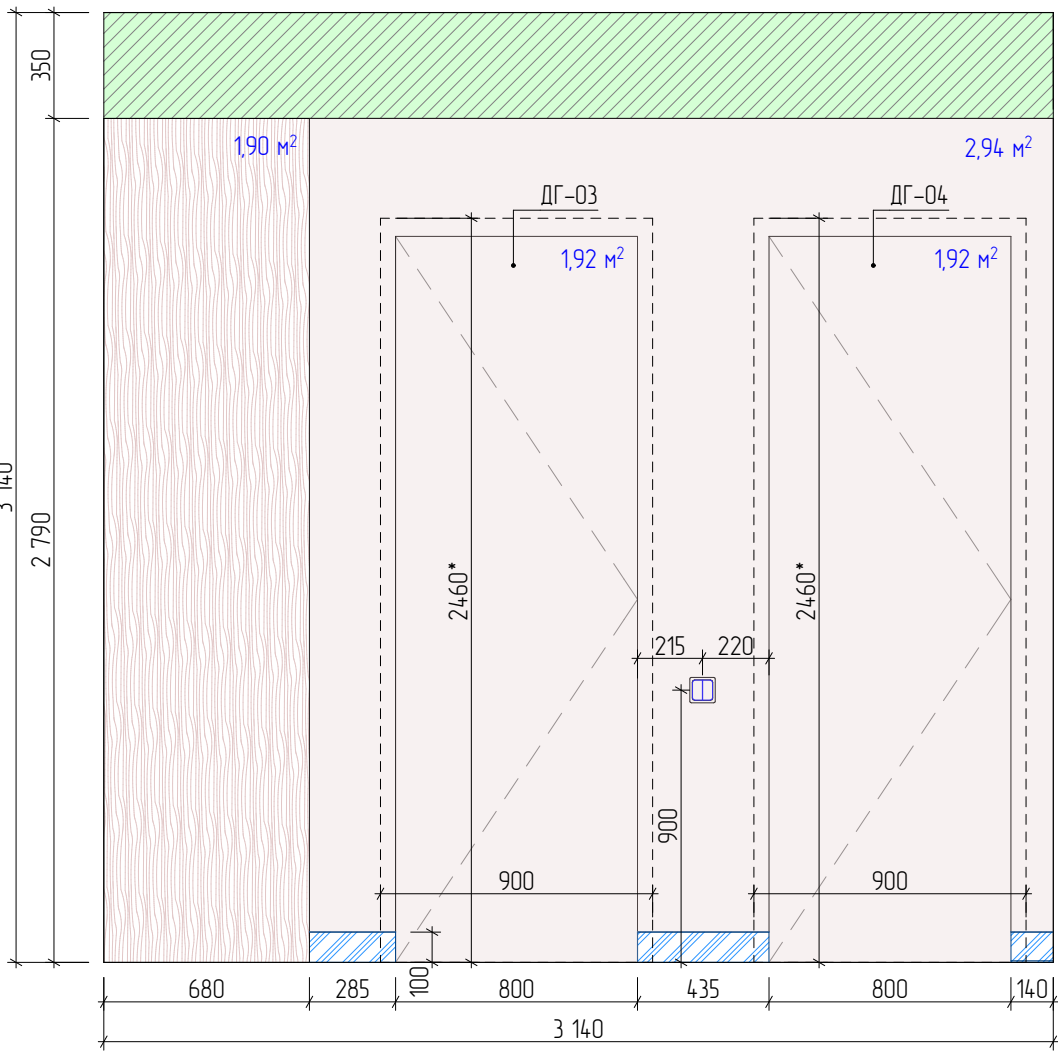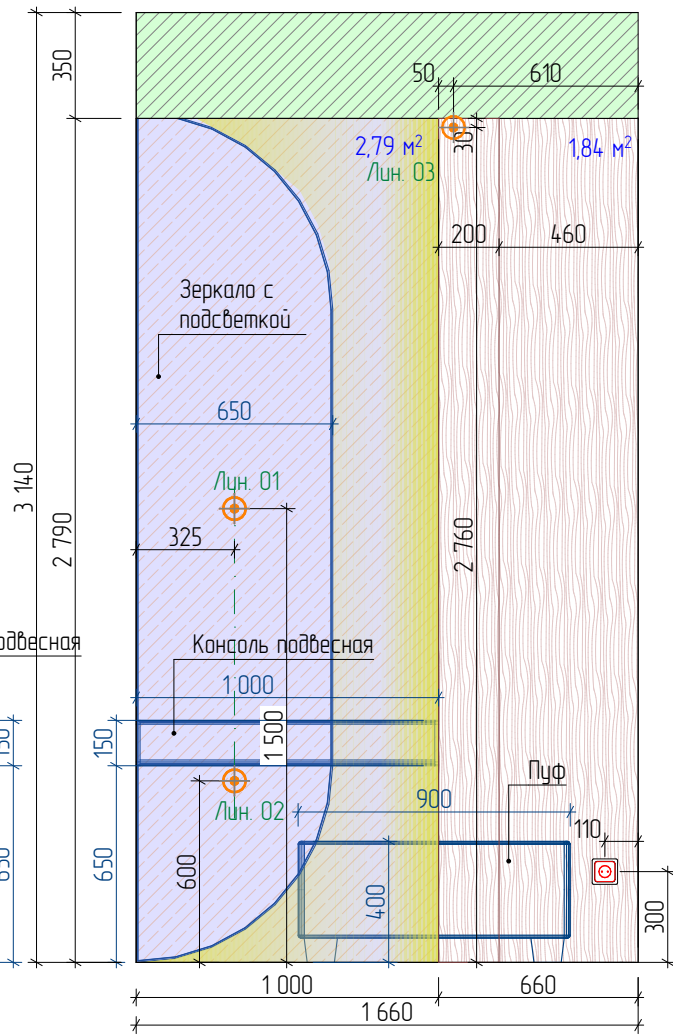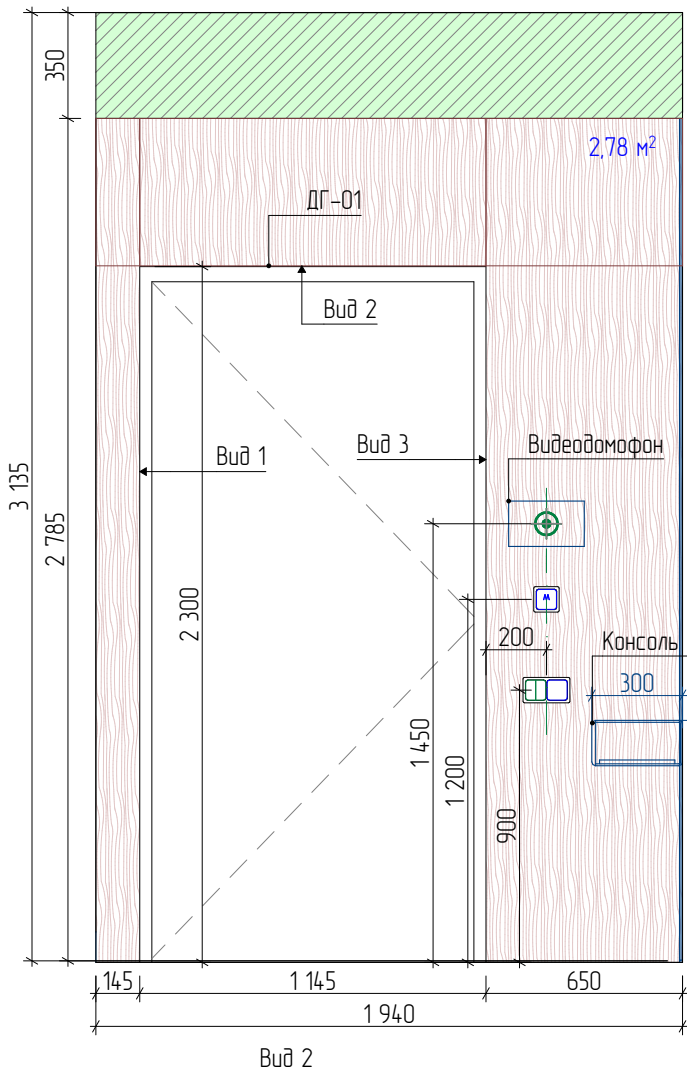





Условные обозначения:

- Плинтус №1. Теневой плинтус скрытого монтажа с МДФ вставкой. Теневой зазор от пола 100 мм. Цвет при выборе образца (в цвет стен).
- Монтаж конструкций из ГКВЛ
- Покраска №1. Выполнить по подготовленной поверхности (стеклохолст*). Цвет при выборе образца (бежевый*).
- МДФ панель №1. Шпонированная. Цвет и фактура при выборе образца (орех*).
- МДФ панель №2. Цвет и фактура при выборе образца (темный мрамор*).
- Зеркало №1. Разработать со специалистами (тонированное*) размеры и резка по чертежу.
- Выход электрокабеля для светодиодной ленты
- Выход спец кабелей
- Розетка 220 V
- Выключатель одноклавишный
- Выключатель двухклавишный
- Переключатель одноклавишный переходной
- Переключатель двухклавишный
- Мастер-клавиша

Примечания:

- * - размеры уточнить по месту после выполнения черновых отделочных работ.
- Выключатели располагать от уровня чистого пола на высоте 900 мм. Исключения указаны на чертеже.
- Розетки располагать от уровня чистого пола на высоте 300 мм. Исключения указаны на чертеже.
- Цвет окрашивания плинтуса уточнить после согласования образца.
- Высоту проемов выполнить 2460 мм от уровня чистого пола. Уточнить после подбора и согласования модели дверей.
- Резку зеркала решить по месту авторским надзором.
- Плинтус подрезать по месту в местах стыковки с дверями и мебелью.
- Внутреннее наполнение мебели разработать со специалистами.
- Серым/синим цветом показаны размеры мебели. Мебель разработать со специалистами, размеры уточнить после выполнения чистовой отделки.

МСК 392.12.25-ЭП ПРЕМИУМ			
Эскизный дизайн-проект интерьера квартиры в г. Москва ЖК "Остров", ул. Нижние Мневники д. 7			
Прихожая Кухня Гостиная.Развертки стен А-01, А-02, А-03, А-04.			
Дизайнер интерьера №1 Александр Батеньков	Стадия	Лист	Листов
	ЭП	46	120
		Подп.	Дата
ГАП	Батеньков А.С.		
Гл. дизайнер	Власова В.А.		
Гл. проектиров.	Луцькова В.Н.		
Разработал	Ильина Е.Е.		

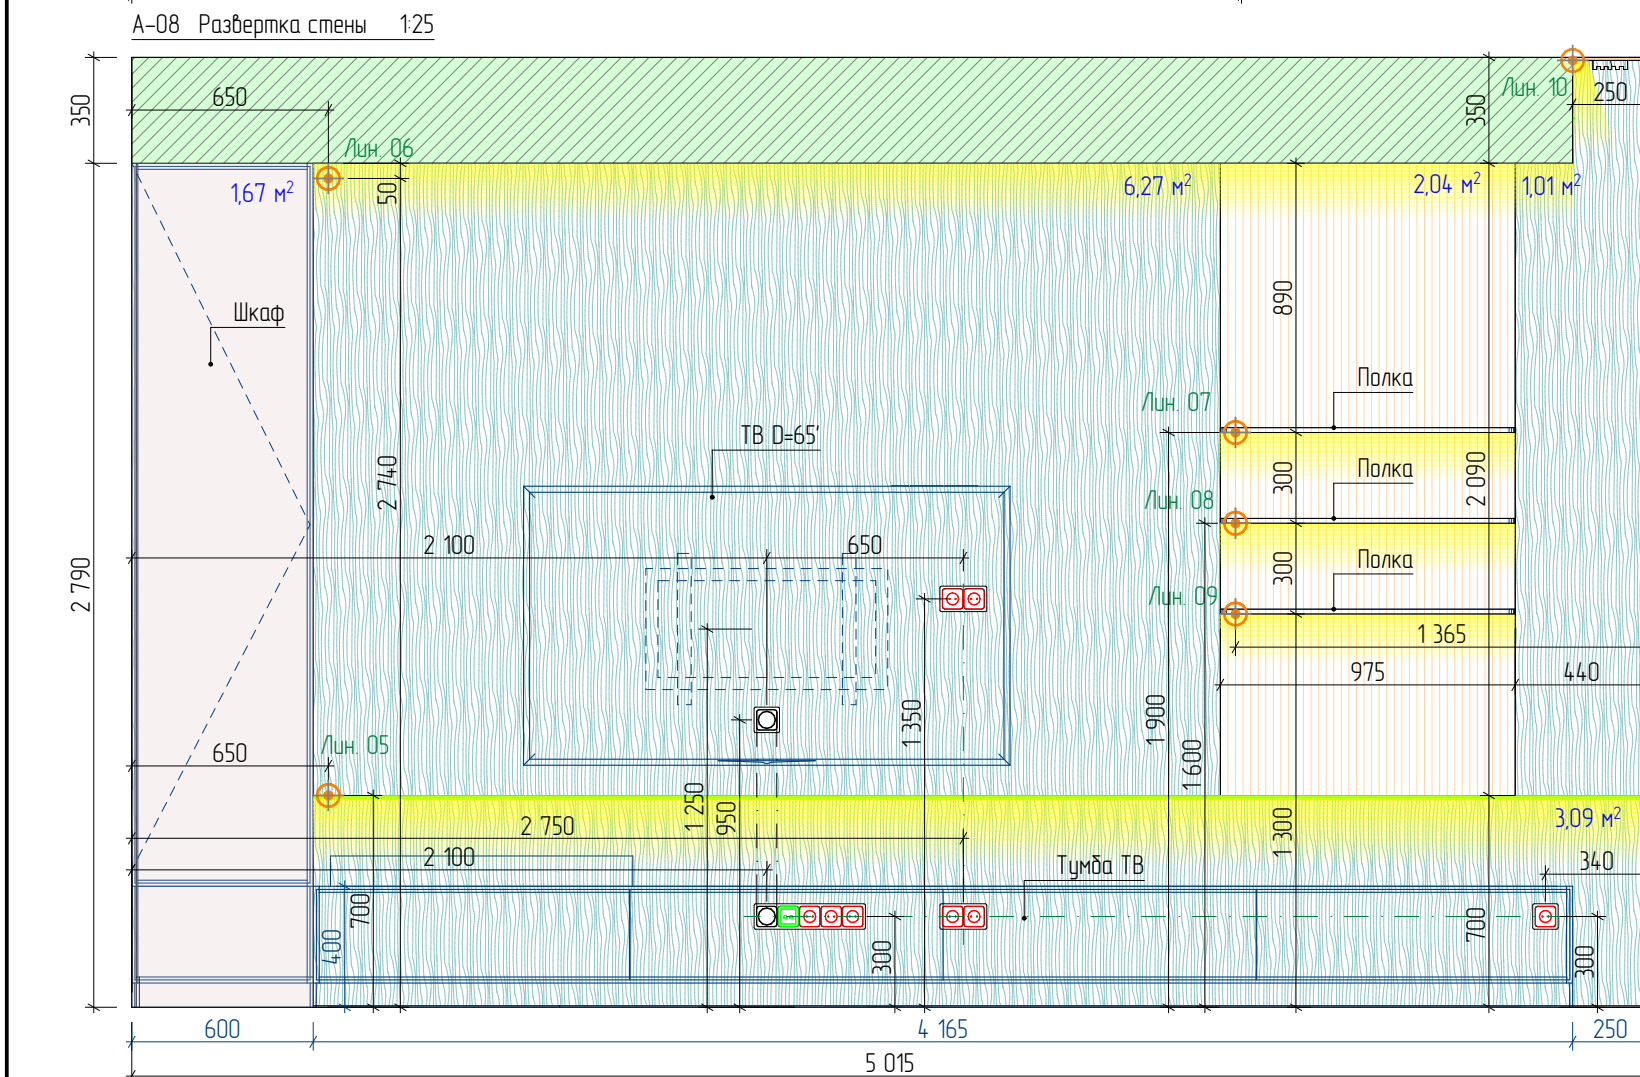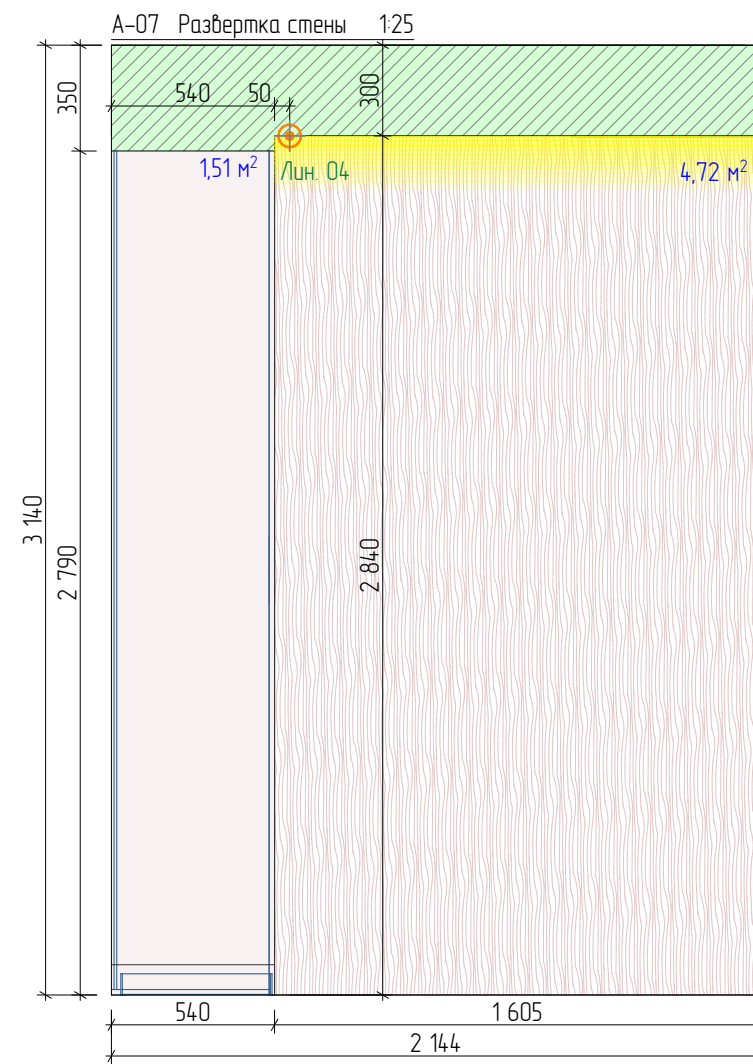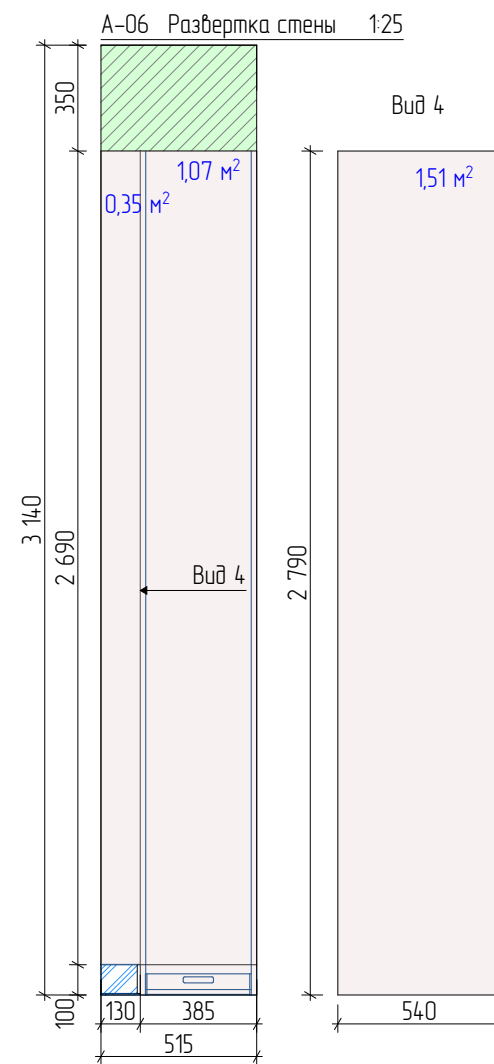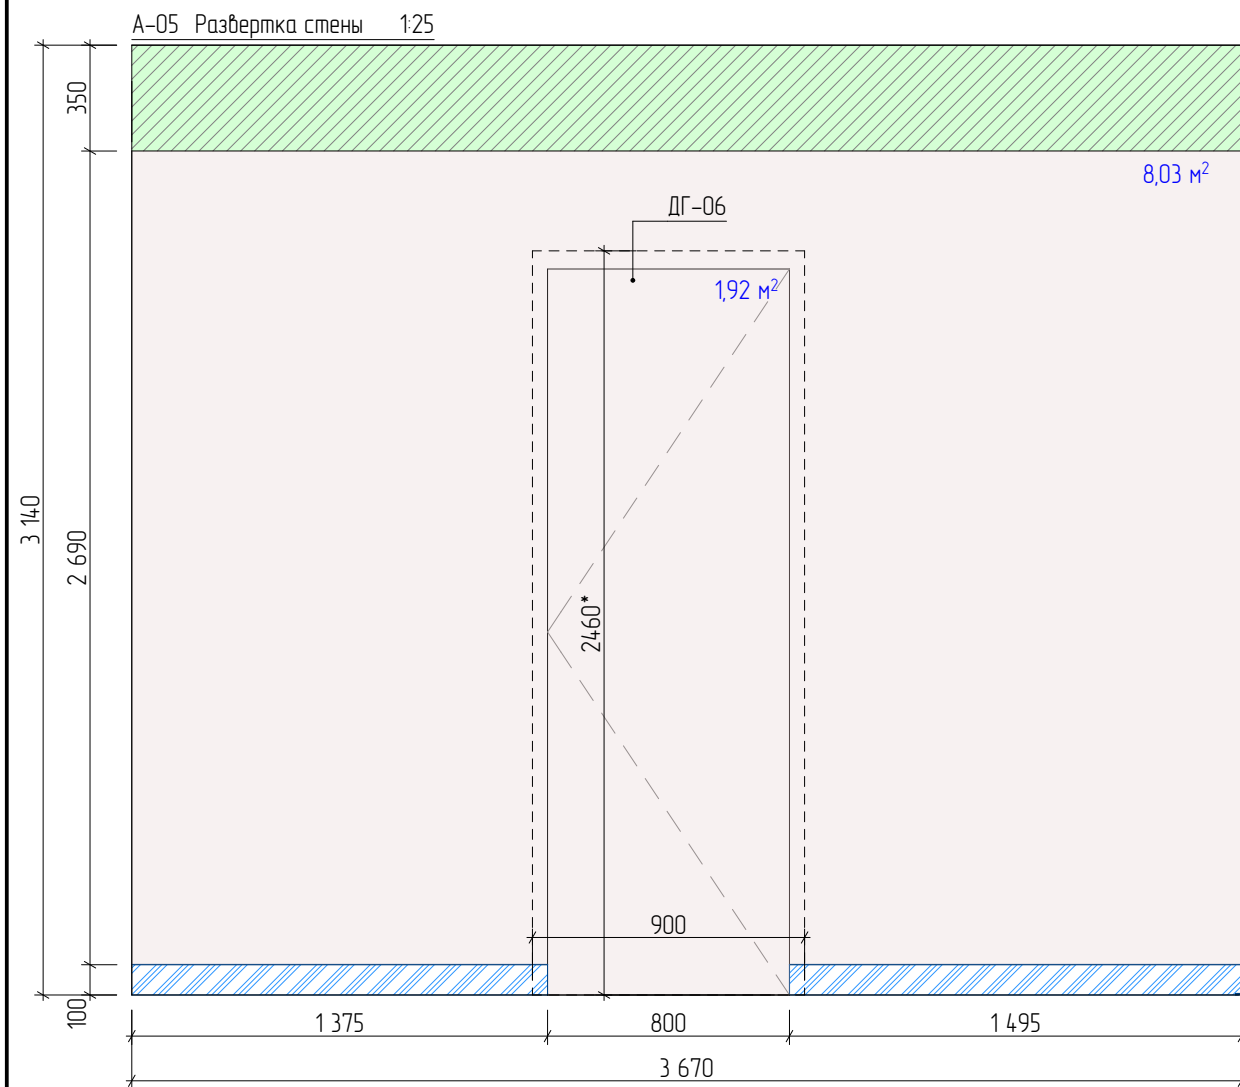

Условные обозначения:



- Плинтус №1. Теневой плинтус скрытого монтажа с МДФ вставкой. Теневой зазор от пола 100 мм. Цвет при выборе образца (в цвет стен).
- Монтаж конструкций из ГКВЛ
- Покраска №1. Выполнить по подготовленной поверхности (стеклохолст*). Цвет при выборе образца (бежевый*).
- МДФ панель №1. Шпонированная. Цвет и фактура при выборе образца (орех*).
- МДФ панель №3. ЗД панель. Цвет и фактура при выборе образца (в цвет мебели*).

- МДФ панель №4. Цвет и фактура при выборе образца (ржавый металл*).
- Розетка 220 V
- Интернет-розетка двойная
- Кабель-канал
- Вывод электрокабеля для светодиодной ленты

Примечания:

- * - размеры уточнить по месту после выполнения черновых отделочных работ.
- Выключатели располагать от уровня чистого пола на высоте 900 мм. Исключения указаны на чертеже.
- Розетки располагать от уровня чистого пола на высоте 300 мм. Исключения указаны на чертеже.
- Цвет окрашивания плинтуса уточнить после согласования образца.
- Высоту проемов выполнить 2460 мм от уровня чистого пола. Уточнить после подбора и согласования модели дверей.
- Плинтус подрезать по месту в местах стыковки с дверями и мебелью.
- Внутреннее наполнение мебели разработать со специалистами.
- Серым/синим цветом показаны размеры мебели. Мебель разработать со специалистами, размеры уточнить после выполнения чистовой отделки.

МСК 392.12.25-ЭП ПРЕМИУМ			
Эскизный дизайн-проект интерьера квартиры в г. Москва ЖК "Остров", ул. Нижние Мневники д. 7			
Прихожая Кухня Гостиная.Развертки стен А-05, А-06, А-07, А-08.			
Дизайнер интерьера  №1 Александр Батеньков	Стадия	Лист	Листов
	ЭП	47	120
		Подп.	Дата
ГАП	Батеньков А.С.		
Гл. дизайнер	Власова В.А.		
Гл. проектиров.	Луныкова В.Н.		
Разработал	Ильина Е.Е.		

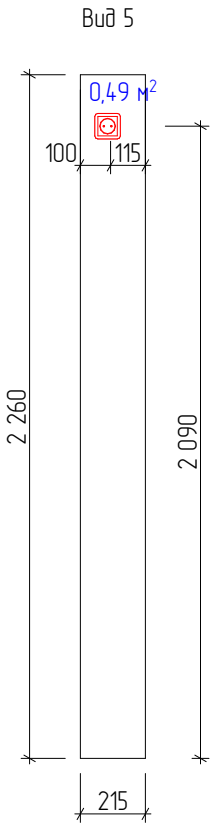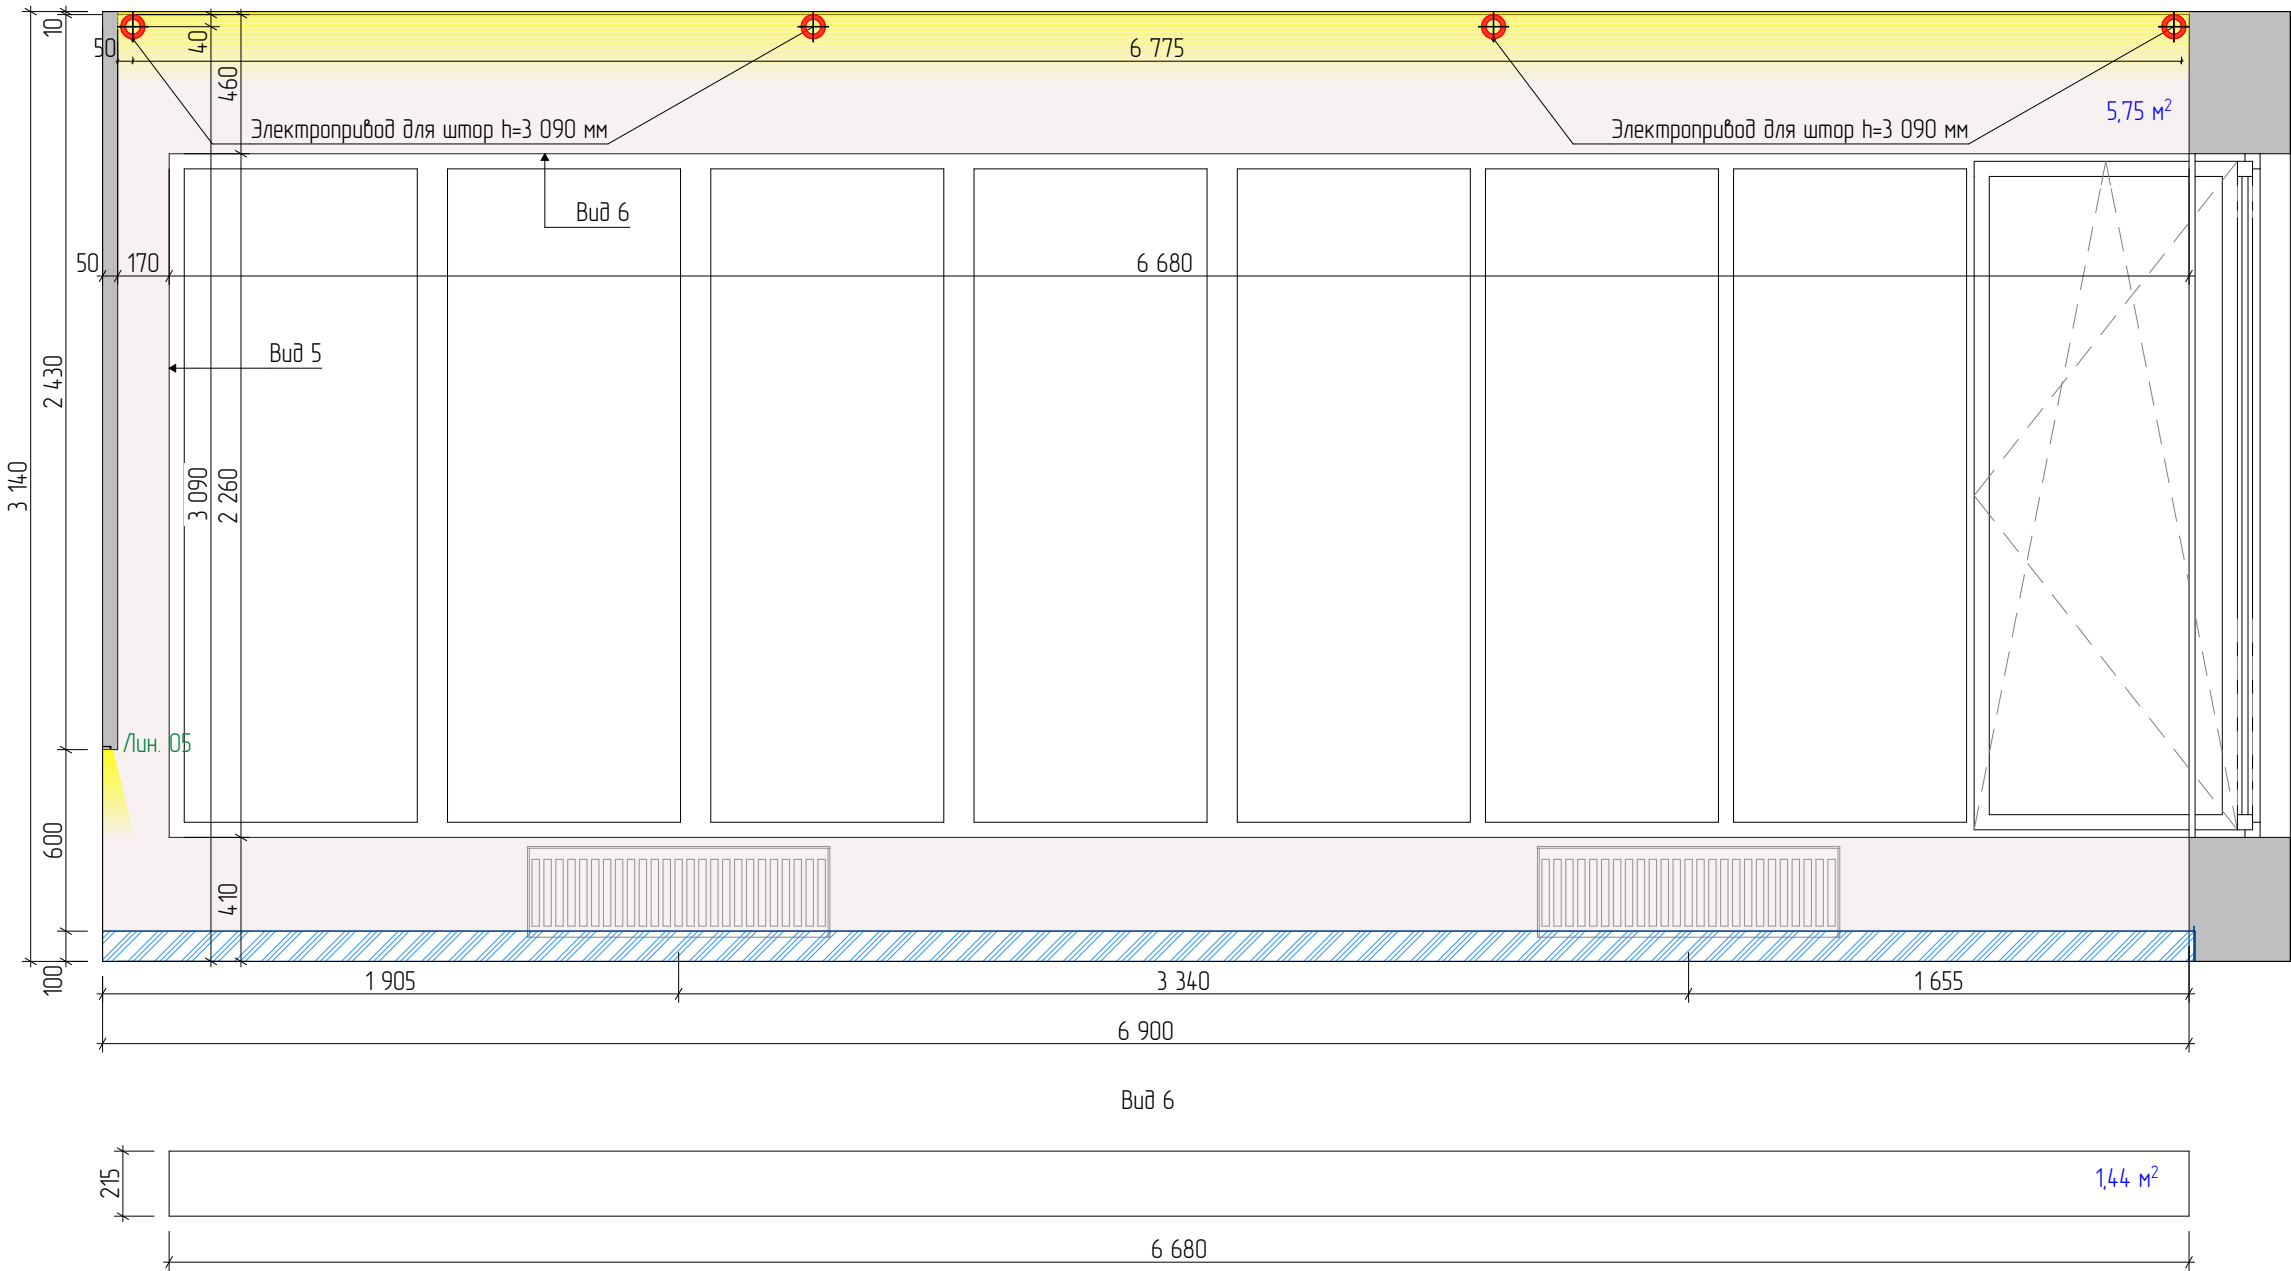


Условные обозначения:

- Плинтус №1. Теневой плинтус скрытого монтажа с МДФ вставкой. Теневой зазор от пола 100 мм. Цвет при выборе образца (в цвет стен).
- Монтаж конструкций из ГКВЛ
- Покраска №1. Выполнить по подготовленной поверхности (стеклохолст*). Цвет при выборе образца (бежевый*).
- Покраска №2. Выполнить по подготовленной поверхности (стеклохолст*). Цвет при выборе образца (белый*).
- Вывод 220 V
- Розетка 220 V


Примечания:

- * – размеры уточнить по месту после выполнения черновых отделочных работ.
- Выключатели располагать от уровня чистого пола на высоте 900 мм. Исключения указаны на чертеже.
- Розетки располагать от уровня чистого пола на высоте 300 мм. Исключения указаны на чертеже.
- Оконные откосы оклеить строительным флизелином и окрасить в белый цвет. Уточнить по месту.
- Размещение выводов для отопления согласовать со специалистами.
- Цвет окрашивания плинтуса уточнить после согласования образца.

МСК 392.12.25–ЭП ПРЕМИУМ			
Эскизный дизайн–проект интерьера квартиры в г. Москва ЖК “Остров”, ул. Нижние Мневники д. 7			
Прихожая Кухня Гостиная.Развертки стен А-09.			
Дизайнер интерьера Александр Батеньков	Стадия	Лист	Листов
	ЭП	48	120
		Подп.	Дата
ГАП	Батеньков А.С.		
Гл. дизайнер	Власова В.А.		
Гл. проектиров.	Луцькова В.Н.		
Разработал	Ильина Е.Е.		

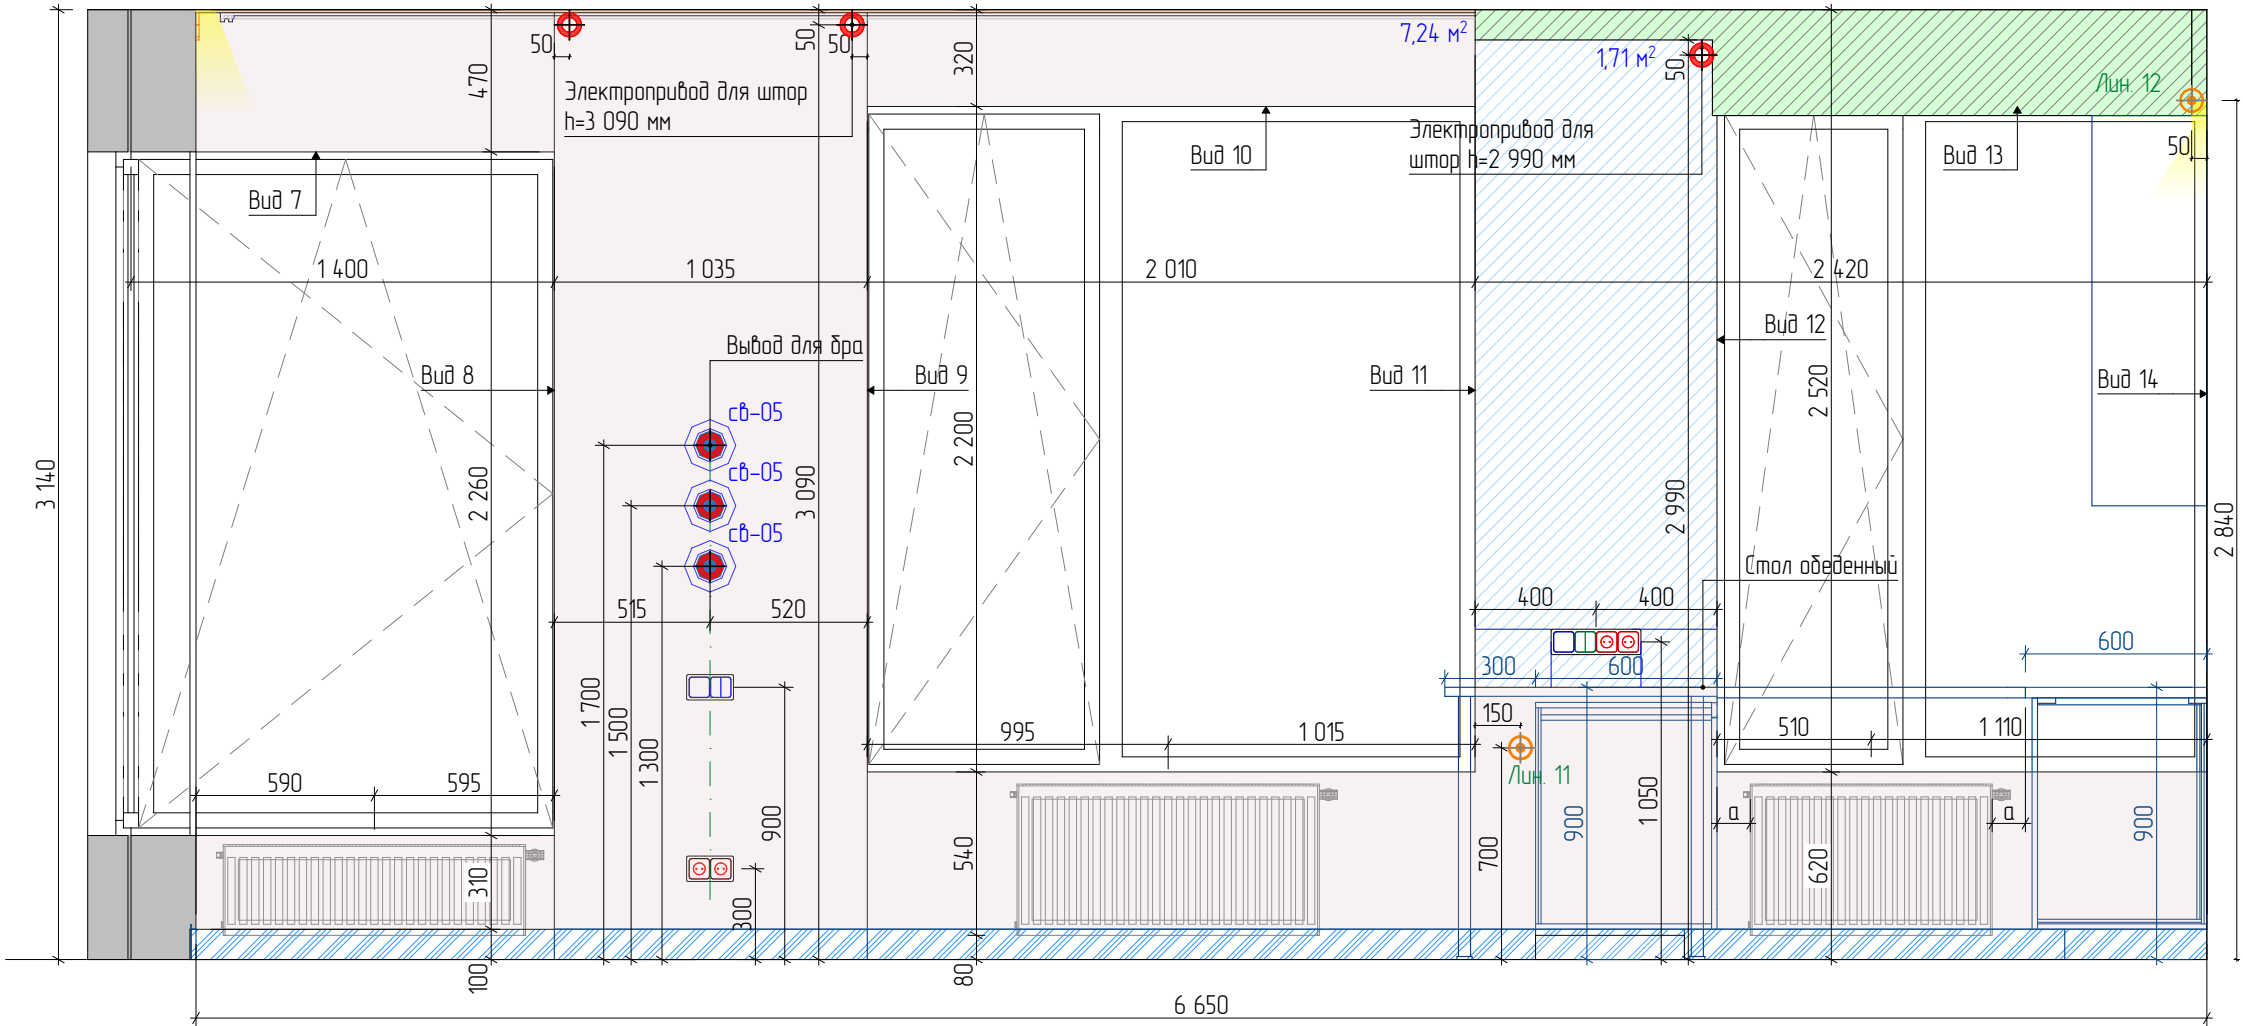


- Условные обозначения:
- Плинтус №1. Теневой плинтус скрытого монтажа с МДФ вставкой. Теневой зазор от пола 100 мм. Цвет при выборе образца (в цвет стен).
 - Монтаж конструкций из ГКВЛ
 - Покраска №1. Выполнить по подготовленной поверхности (стеклохолст*). Цвет при выборе образца (бежевый*).
 - Покраска №2. Выполнить по подготовленной поверхности (стеклохолст*). Цвет при выборе образца (белый*).
 - Зеркало №1. Разработать со специалистами (тонированное*) размеры и резка по чертежу.
 - Вывод 220 V
 - Вывод электрокабеля для светодиодной ленты
 - Розетка 220 V
 - Выключатель одноклавишный
 - Выключатель двухклавишный
 - Переключатель двухклавишный

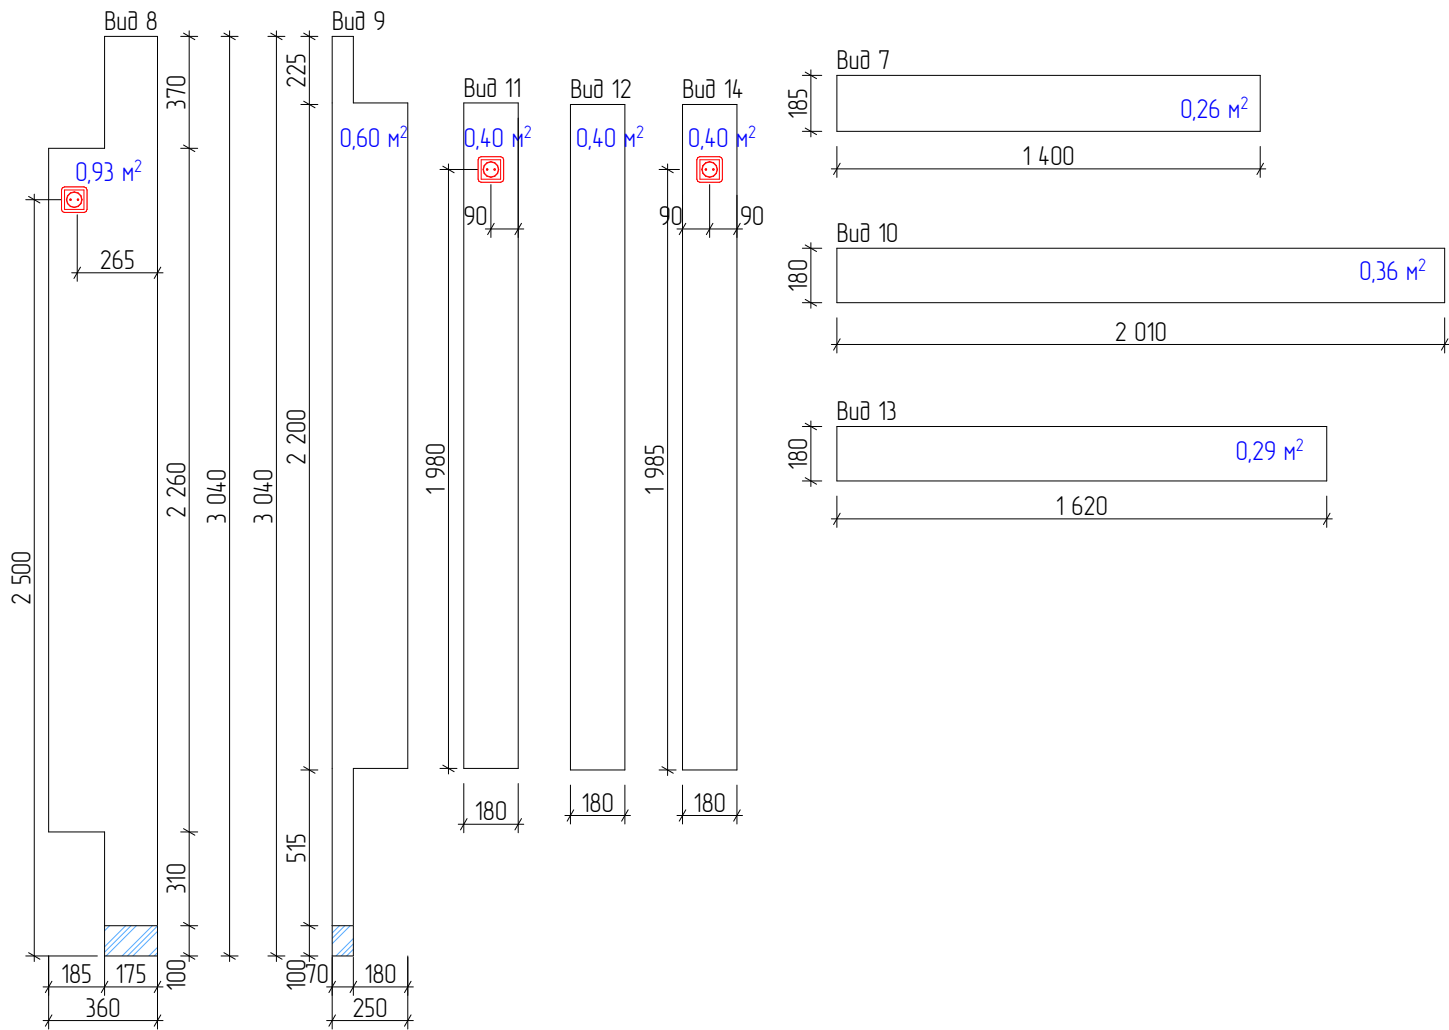

- Примечания:
- * – размеры уточнить по месту после выполнения черновых отделочных работ.
 - Выключатели располагать от уровня чистого пола на высоте 900 мм. Исключения указаны на чертеже.
 - Розетки располагать от уровня чистого пола на высоте 300 мм. Исключения указаны на чертеже.
 - Оконные откосы оклеить строительным флизелином и окрасить в белый цвет. Уточнить по месту.
 - Размещение выводов для отопления согласовать со специалистами.
 - Цвет окрашивания плинтуса уточнить после согласования образца.
 - Резку зеркала решить по месту авторским надзором.
 - Плинтус подрезать по месту в местах стыковки с дверями и мебелью.
 - Внутреннее наполнение мебели разработать со специалистами.
 - Серым/синим цветом показаны размеры мебели. Мебель разработать со специалистами, размеры уточнить после выполнения чистовой отделки.

МСК 392.12.25-ЭП ПРЕМИУМ			
Эскизный дизайн-проект интерьера квартиры в г. Москва ЖК "Остров", ул. Нижние Мневники д. 7			
Прихожая Кухня Гостиная.Развертки стен А-10.			
Дизайнер интерьера №1 Александр Батеньков	Стадия	Лист	Листов
	ЭП	49	120
		Подп.	Дата
ГАП	Батеньков А.С.		
Гл. дизайнер	Власова В.А.		
Гл. проектиров.	Луныкова В.Н.		
Разработал	Ильина Е.Е.		

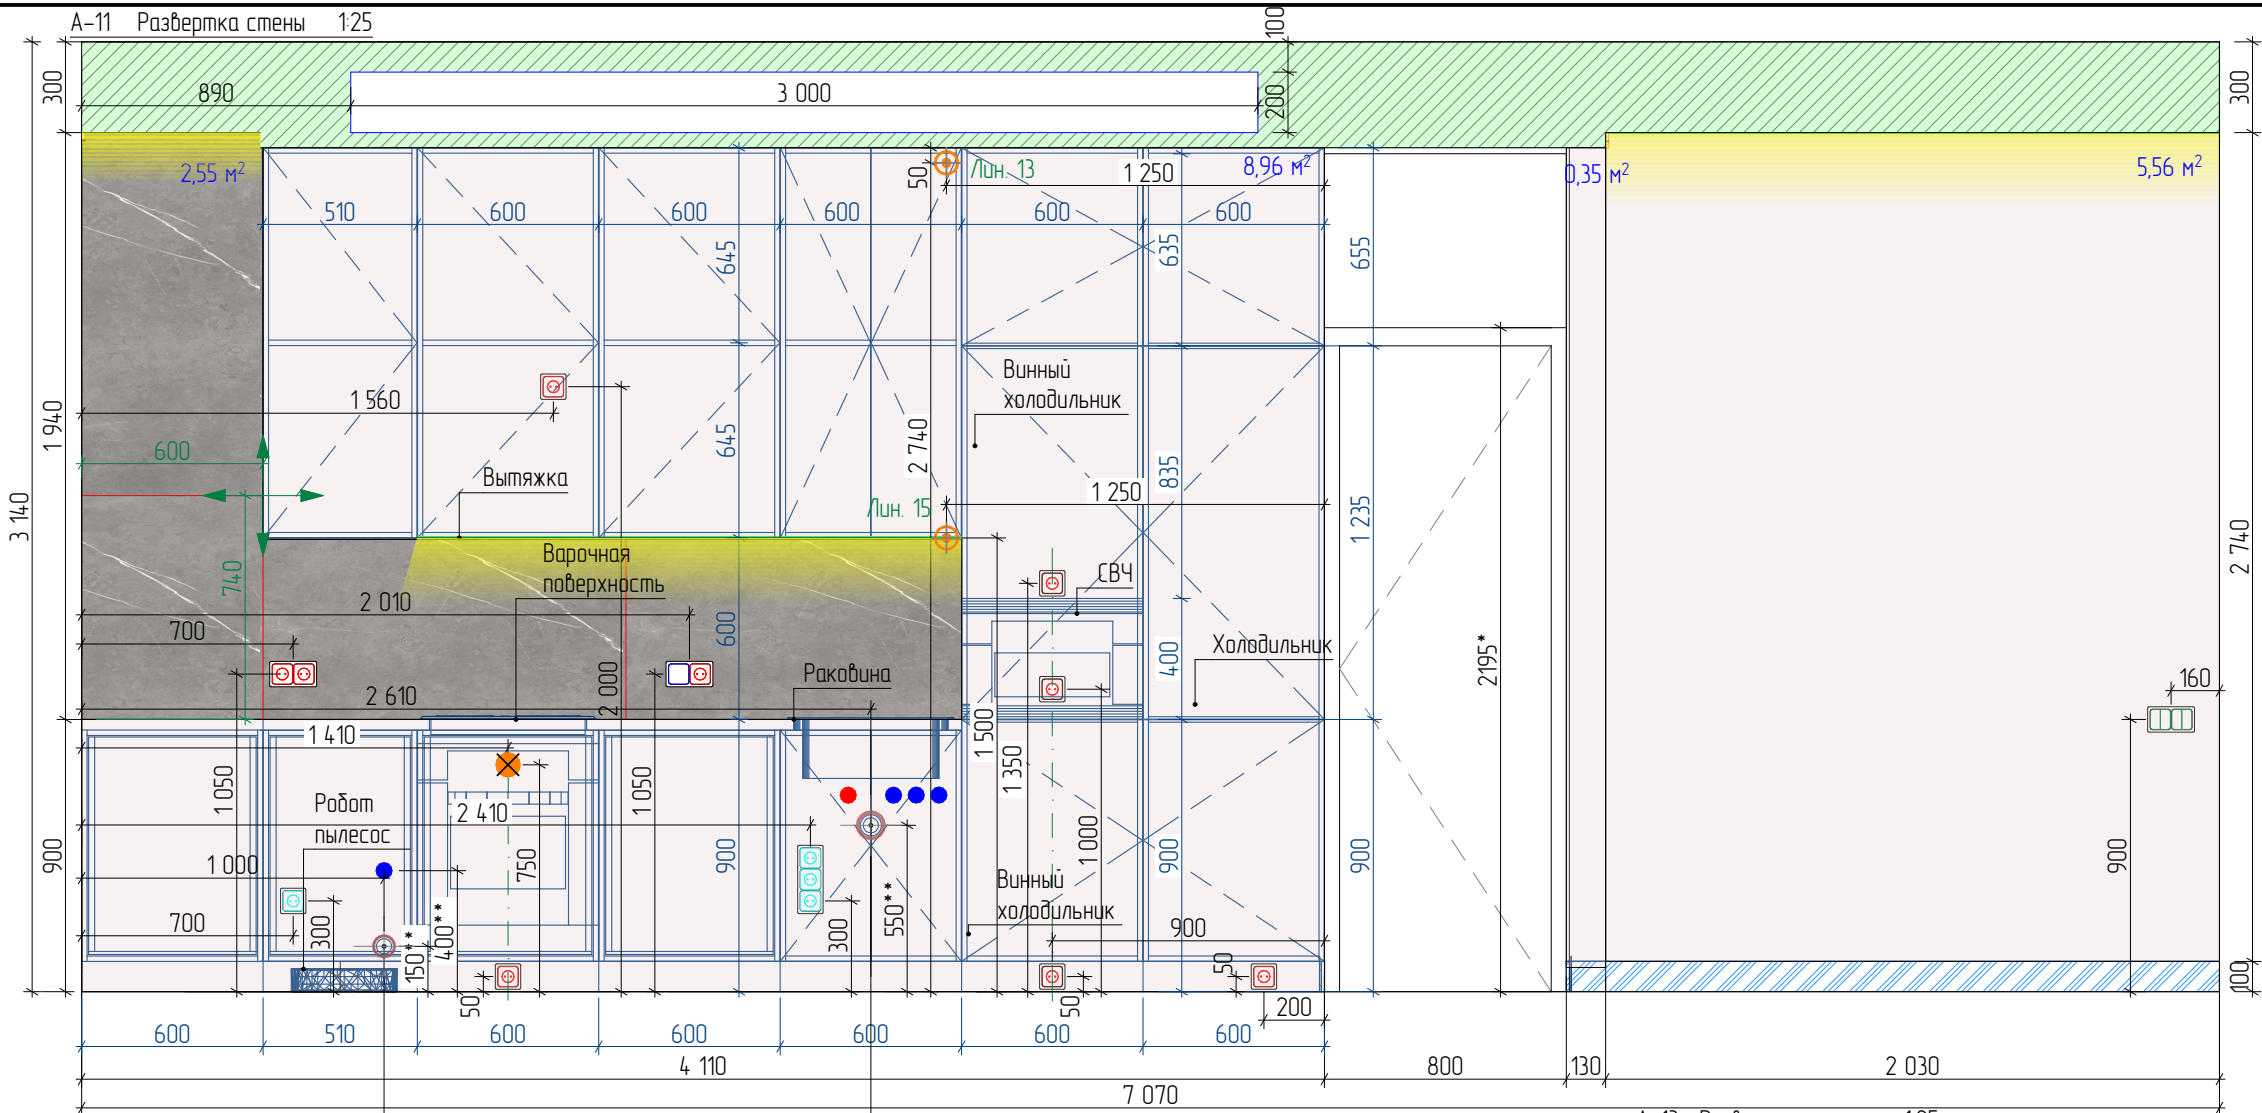

Выход коммуникаций для робота пылесоса разместить согласно инструкции монтажа выбранной модели, подвести 1 выход холодной воды и выход канализации



Выход коммуникаций для мойки и смесителя разместить согласно инструкции монтажа выбранной модели, подвести 3 выхода холодной воды, при необходимости установить фильтры доочистки воды до питьевой.

Условные обозначения:

- Плинтус №1. Теневой плинтус скрытого монтажа с МДФ вставкой. Теневой зазор от пола 100 мм. Цвет при выборе образца (в цвет стен).
- Монтаж конструкций из ГКВЛ
- Покраска №1. Выполнить по подготовленной поверхности (стеклохолст*). Цвет при выборе образца (бежевый*).
- Керамогранит №01. Керамогранит. Изготовитель: Elegant Grey, кол-я: Forte Dei Marmi, размер: 1200x1200 мм, толщину уточнить при заказе.
- Выход коммуникаций (ХВС, ГВС, канал-ция)
- Выход электрокабеля или розетка для варочной поверхности
- Выход электрокабеля для светодиодной ленты
- Розетка 220 В, влагозащищенная IP44 и выше
- Розетка 220 В
- Регулятор теплого пола
- Выключатель одноклавишный

Примечания:

- * – размеры уточнить по месту после выполнения черновых отделочных работ.
- Выключатели располагать от уровня чистого пола на высоте 900 мм. Исключения указаны на чертеже.
- Регуляторы теплого пола располагать от уровня чистого пола на высоте 750 мм. Исключения указаны на чертеже.
- Розетки располагать от уровня чистого пола на высоте 300 мм. Исключения указаны на чертеже.
- Размещение выводов для отопления согласовать со специалистами.
- Размещение вывода 220 В для кондиционеров согласовать со специалистами.
- Расположение розеток согласовать с изготовителями кухонного гарнитура. Внести изменения по технологической карте от специалистов.
- Цвет окрашивания плинтуса уточнить после согласования образца.
- Размеры и конструкцию фартука для кухонного гарнитура уточнить после выбора и детальной проработке кухонного гарнитура, согласовать со специалистами.
- Точную привязку выводов коммуникаций решить после выбора оборудования по инструкции монтажа.
- Расположение розеток и выключателей согласовать с изготовителями кухонного гарнитура.
- ** – размер уточнить по инструкции монтажа оборудования.
- Розетки, выключатели, регуляторы теплого пола размещать по центру керамической плитки.
- Высоту проемов выполнить 2460 мм от уровня чистого пола. Уточнить после подбора и согласования модели дверей.
- Плинтус подрезать по месту в местах стыковки с дверями и мебелью.
- Внутреннее наполнение мебели разработать со специалистами.
- Серым/синим цветом показаны размеры мебели. Мебель разработать со специалистами, размеры уточнить после выполнения чистовой отделки.

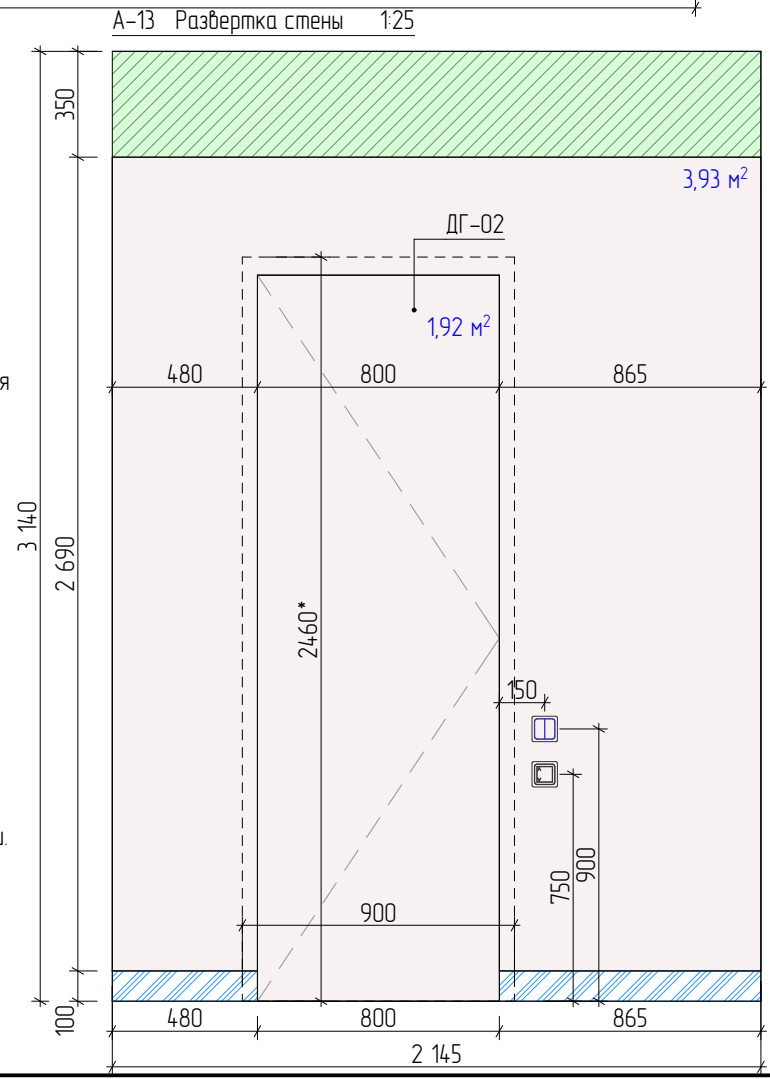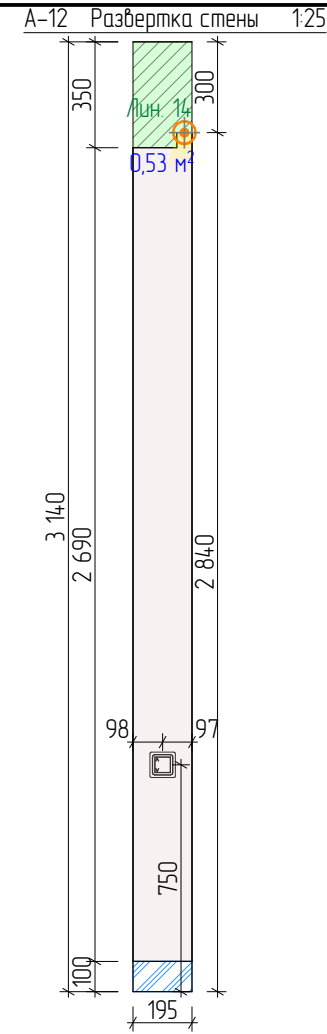

- Выключатель двухклавишный
- Переключатель двухклавишный
- Направление и начало укладки

МСК 392.12.25-ЭП ПРЕМИУМ			
Эскизный дизайн-проект интерьера квартиры в г. Москва ЖК "Остров", ул. Нижние Мневники д. 7			
Прихожая Кухня Гостиная.Развертки стен А-11, А-12, А-13.			
Дизайнер интерьера №1 Александр Батеньков	Стадия	Лист	Листов
	ЭП	50	120
		Подп.	Дата
ГАП	Батеньков А.С.		
Гл. дизайнер	Власова В.А.		
Гл. проектиров.	Луныкова В.Н.		
Разработал	Ильина Е.Е.		

Ведомость отделочных материалов.

№	Обозначение	Наименование	Кол-во	Примечание
Пол:				
1		Пробковый компенсатор	10,01	м.п.
2		Покрытие №01. Паркет. Изготовитель: Lab Arte, кол-я: Angle Дуб Натур, размер: 500x150 мм, точный артикул и производителя уточнить при выборе образца, толщину уточнить при закупке.	34,14	м²
3		Покрытие №02. Керамогранит. Изготовитель: Elegant Grey, кол-я: Forte Dei Marini, размер: 1200x1200 мм, толщину уточнить при закупке.	20,50 19	м² укладки шт.
Стены:				
4		Плинтус №1. Теневой плинтус скрытого монтажа с МДФ вставкой. Теневой зазор от пола 100 мм. Цвет при выборе образца (в цвет стен).	21,36	м.п.
5		Покраска №1. Выполнить по подготовленной поверхности (стеклохолст*). Цвет при выборе образца (бежевый*).	57,08	м²
6		МДФ панель №1. Шпонированная. Цвет и фактура при выборе образца (орех*).	11,96	м²
7		МДФ панель №2. Цвет и фактура при выборе образца (темный мрамор*).	2,79	м²
8		МДФ панель №3. 3Д панель. Цвет и фактура при выборе образца (в цвет мебели*).	2,04	м²
9		МДФ панель №4. Цвет и фактура при выборе образца (ржавый металл*).	7,28	м²
10		Керамогранит №01. Керамогранит. Изготовитель: Elegant Grey, кол-я: Forte Dei Marini, размер: 1200x1200 мм, толщину уточнить при закупке.	2,55 2	м² укладки шт.
11		Зеркало №1. Разработать со специалистами (тонированное*) размеры и резка по чертежу.	4,14	м²
Откосы:				
12		Покраска №2. Выполнить по подготовленной поверхности. Цвет при выборе образца (белый*).	4,54	м²
Подоконник:				
13		Подоконник №1. Искусственный камень. Цвет при выборе образца.	2,35	м²

МСК 392.12.25–ЭП ПРЕМИУМ			
Эскизный дизайн–проект интерьера квартиры в г. Москва ЖК “Остров”, ул. Нижние Мневники д. 7			
Прихожая Кухня Гостиная.Ведомость отделочных материалов			
Дизайнер интерьера  №1 Александр Батеньков	Стадия	Лист	Листов
	ЭП	51	120
		Подп.	Дата
ГАП	Батеньков А.С.		
Гл. дизайнер	Власова В.А.		
Гл. проектиров.	Луцькова В.Н.		
Разработал	Ильина Е.Е.		