


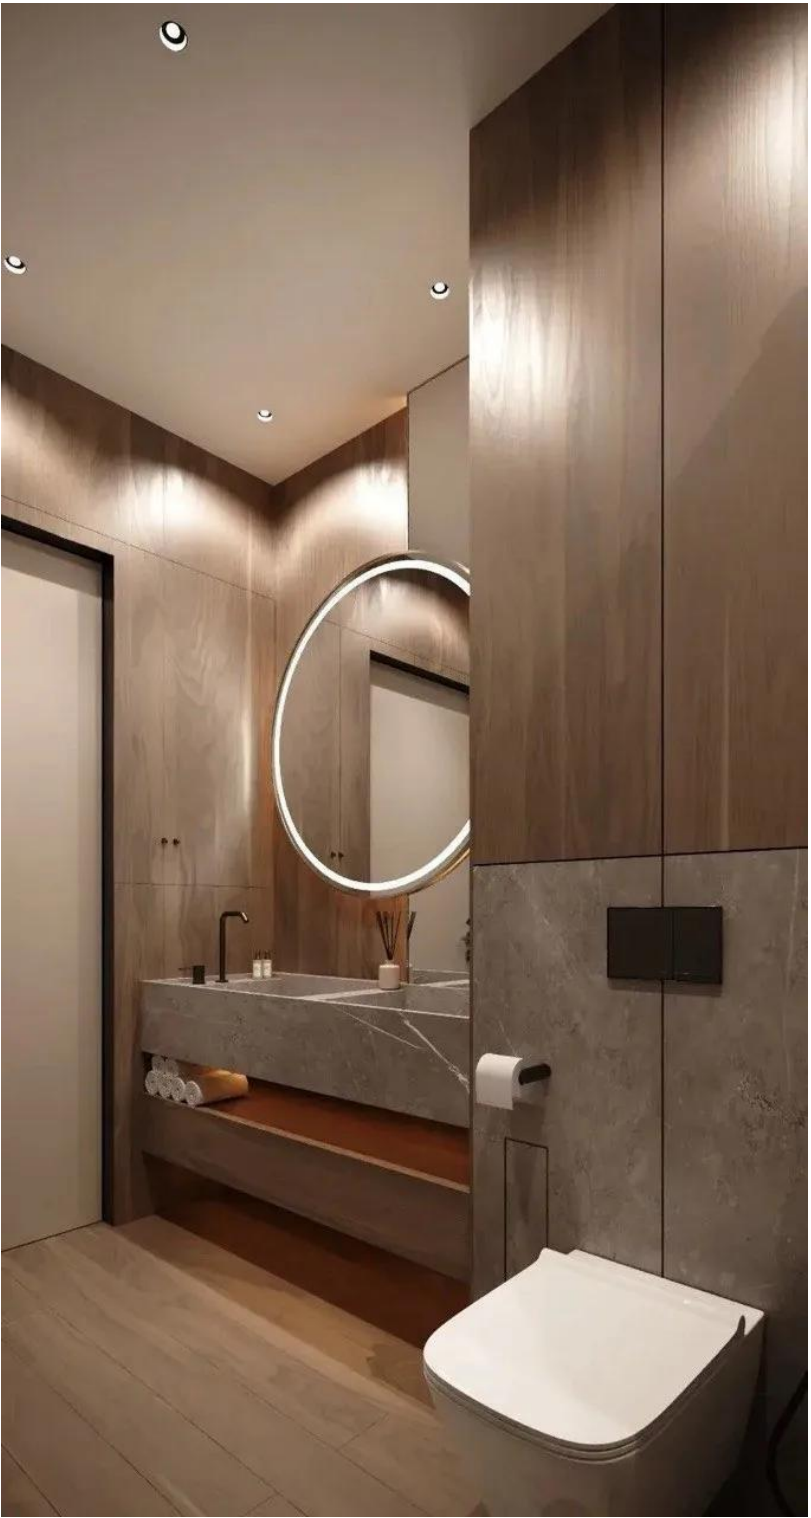


МСК 392.12.25-ЭП ПРЕМИУМ			
Эскизный дизайн-проект интерьера квартиры в г. Москва ЖК "Остров", ул. Нижние Мневники д. 7			
Душевая. Видовые точки.			
Дизайнер интерьера №1 Александр Батеньков	Стадия	Лист	Листов
	ЭП	58	120
		Подп.	Дата
ГАП	Батеньков А.С.		
Гл. дизайнер	Власова В.А.		
Гл. проектиров.	Луныкова В.Н.		
Разработал	Ильина Е.Е.		




МСК 392.12.25-ЭП ПРЕМИУМ			
Эскизный дизайн-проект интерьера квартиры в г. Москва ЖК "Остров", ул. Нижние Мневники д. 7			
Душевая. Видовые точки.			
Дизайнер интерьера №1 Александр Батеньков	Стадия	Лист	Листов
	ЭП	59	120
		Подп.	Дата
ГАП	Батеньков А.С.		
Гл. дизайнер	Власова В.А.		
Гл. проектиров.	Луныкова В.Н.		
Разработал	Ильина Е.Е.		

План отделки пола:

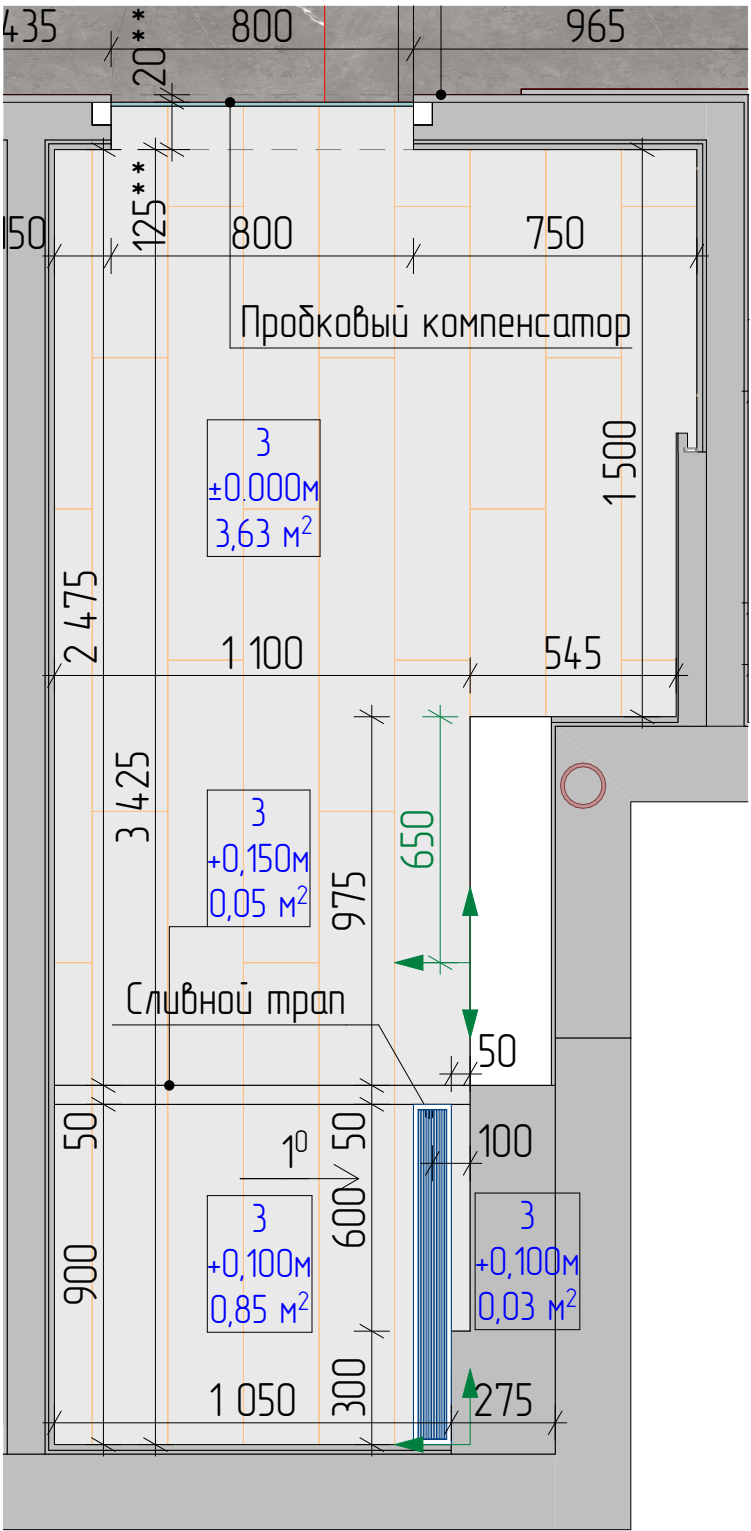

План отделки потолка:

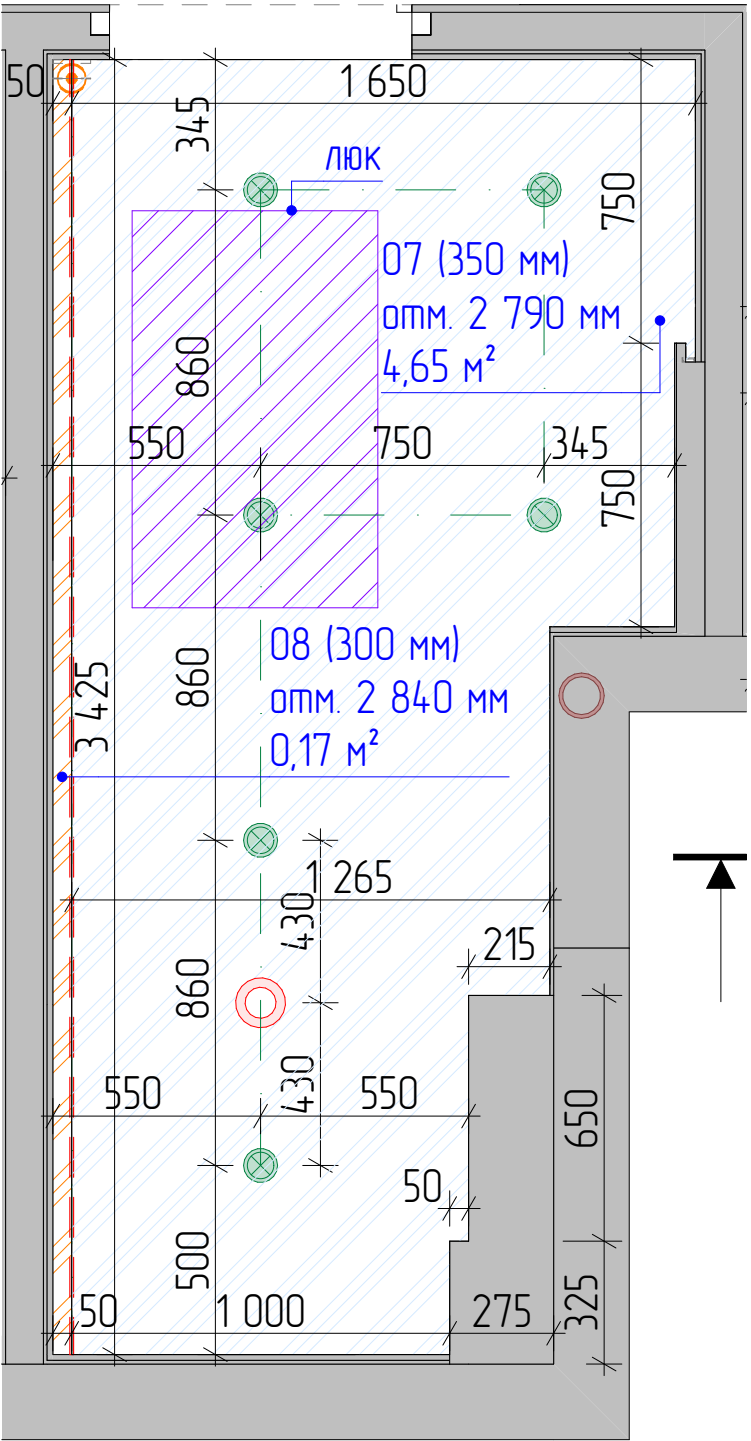

Условные обозначения:


- Направление и начало укладки
- Пробоковый компенсатор
- Покрывтие №03. Керамогранит. Изготовитель: Nutmeg, кол-я: Woodslate Life, размер: 1200x200 мм, толщину уточнить при закупке.
- Вывод 220V
- Вывод электрокабеля для светодиодной ленты
- Диффузор, вытяжка
- Светильник точечный встраиваемый влагозащищенный
- Светодиодная лента, влагозащищенная
- Люк доступа

- Примечания:
- *- размеры уточнить по месту после выполнения черновых отделочных работ.
 - За отметку ±0,000 принят уровень чистого пола.
 - Во влажных помещениях предусмотреть гидроизоляцию пола с заведением на стены на 150 мм, в зоне душевой до потолка.
 - Совместить швы плитки на подиумах и основном полу.
 - При монтаже напольных покрытий уточнить необходимость устройства дверных проемов с порогом.
 - *- размеры уточнить по месту после выполнения черновых отделочных работ и установки дверей со скрытой коробкой.
 - **-размер уточнить по месту в зависимости от точного расположения полотна двери, стыковка двух разных напольных покрытий должна проходить точно по центру вдоль дверного полотна.
 - Выполнить уровни потолка из влагостойкого ГКЛ для предотвращения деформации потолка при затоплении.
 - Высоту уровней потолка отсчитывать от существующей ж/б плиты перекрытия помещения.
 - Во влажных помещениях обои под покраску на потолок не клеить, заменить на оштукатуривание по армирующей сетке, согласовать со специалистами.
 - От вытяжки провести вентиляционный короб до общедомового канала в конструкции потолка, уточнить по месту со специалистами и заказчиком.
 - Шумоизоляцию разработать со специалистами, уточнить состав и толщину слоев шумоизоляционных материалов. Уточнить необходимость устройства с заказчиком.


Условные потолки				
№	Обозначение	Опуск	Примечания	Площадь м2
07		350	Потолок ГКЛ/В, Окрасить в цвет выбранного образца (белый) по оштукатуренной поверхности.	4,65
08		300	Потолок ГКЛ/В, Окрасить в цвет выбранного образца (белый) по оштукатуренной поверхности.	0,17

МСК 392.12.25-ЭП ПРЕМИУМ			
Эскизный дизайн-проект интерьера квартиры в г. Москва ЖК "Остров", ул. Нижние Мневники д. 7			
Душевая.План отделки пола. План отделки потолка.			
Дизайнер интерьера  Александр Батеньков	Стадия	Лист	Листов
	ЭП	60	120
		Подп.	Дата
ГАП	Батеньков А.С.		
Гл. дизайнер	Власова В.А.		
Гл. проектиров.	Лунькова В.Н.		
Разработал	Ильина Е.Е.		

План электрооборудования:

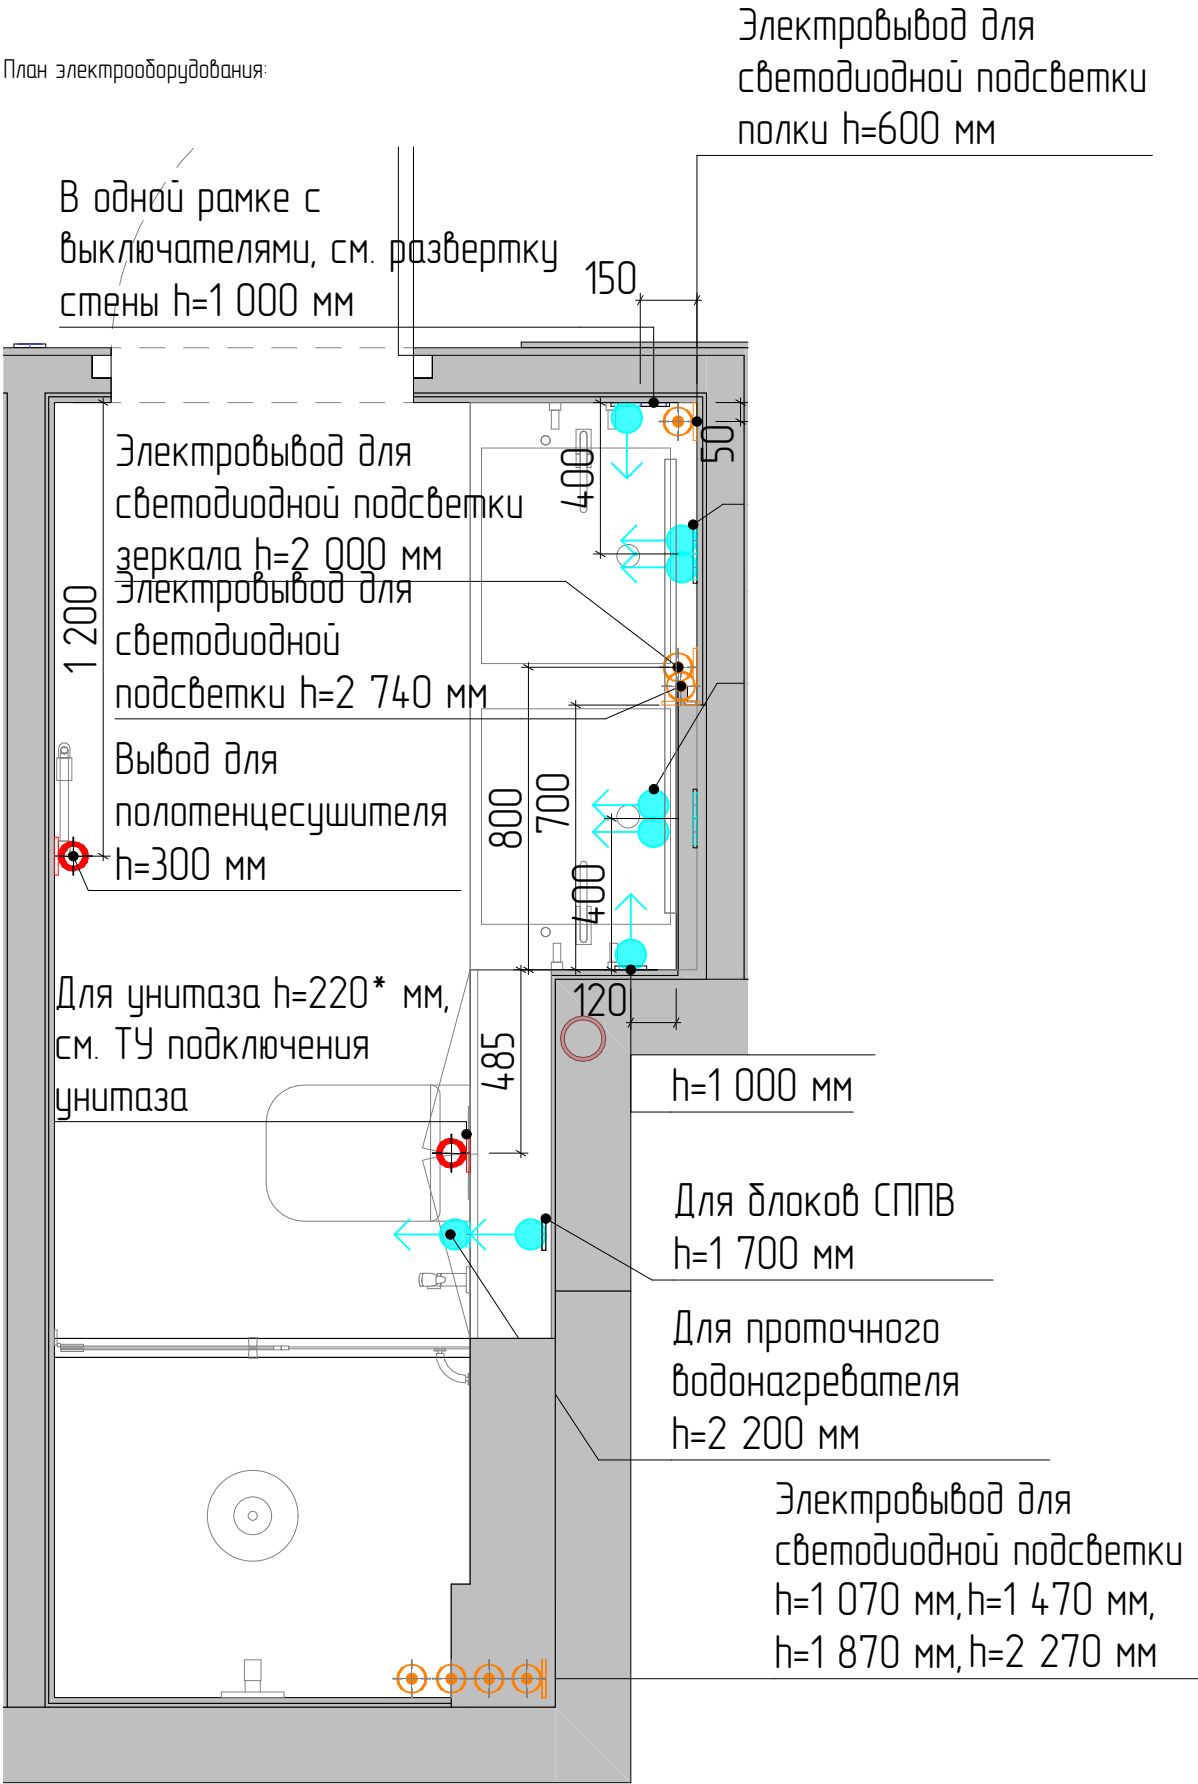

План размещения освещения и выключателей:

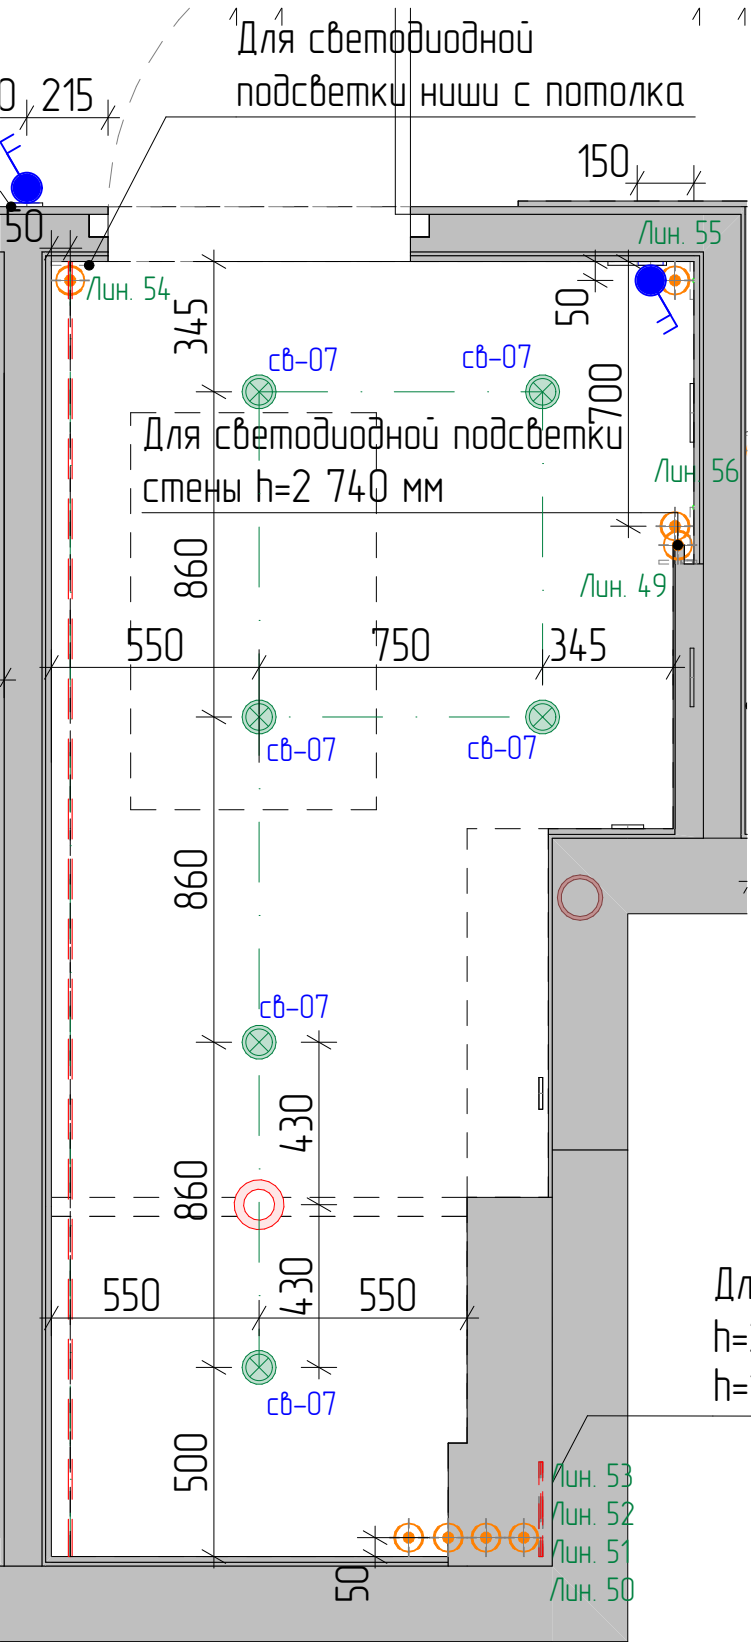

Условные обозначения:


- Розетка 220V влагозащищенная
- Вывод электрокабеля для варочной поверхности
- wi-fi оборудование
- Светильник точечный встраиваемый влагозащищенный
- Светодиодная лента, влагозащищенная
- Выключатель двухклавишный

Примечания:






- * – размеры уточнить по месту.
- ** – размещение вывода 220V для полотенцесушителя уточнить после подбора модели.
- Розетки располагать от уровня чистого пола на высоте 0,300 м. Исключения указаны на чертеже.
- Размещение всех выводов и розеток согласовать со специалистами «Умный дом».
- Размеры и характеристики радиаторов отопления согласовать со специалистами, предусмотреть терморегуляторы.
- Размещение розеток и электровыводов по высоте см. на развертках стен.

- Выключатели располагать от уровня чистого пола на высоте 0,900 м. Исключения указаны на чертеже.
- Светильники, встроенные в мебель, согласовать с изготовителями мебели.

МСК 392.12.25–ЭП ПРЕМИУМ			
Эскизный дизайн–проект интерьера квартиры в г. Москва ЖК "Остров", ул. Нижние Мневники д. 7			
Душевая.План размещения электрооборудования. План размещения освещения и выключателей.			
Дизайнер интерьера №1 Александр Батыков	Стадия	Лист	Листов
	ЭП	61	120
		Подп.	Дата
ГАП	Батыков А.С.		
Гл. дизайнер	Власова В.А.		
Гл. проектиров.	Луцькова В.Н.		
Разработал	Ильина Е.Е.		

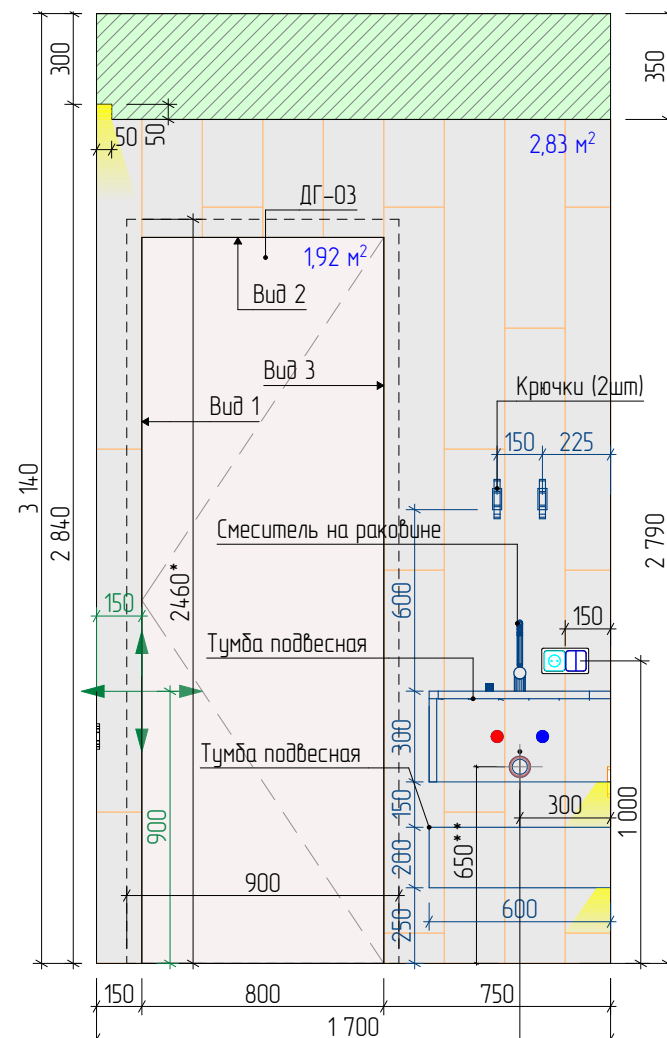

Вывод коммуникаций для раковины и смесителя на столешнице разместить согласно инструкции монтажа выбранной модели

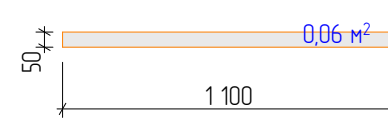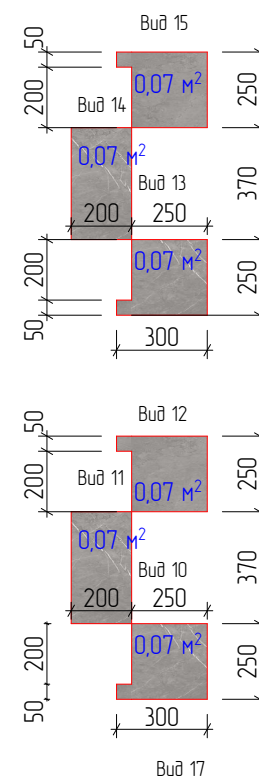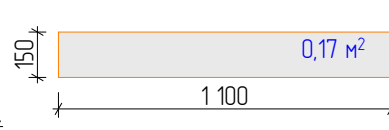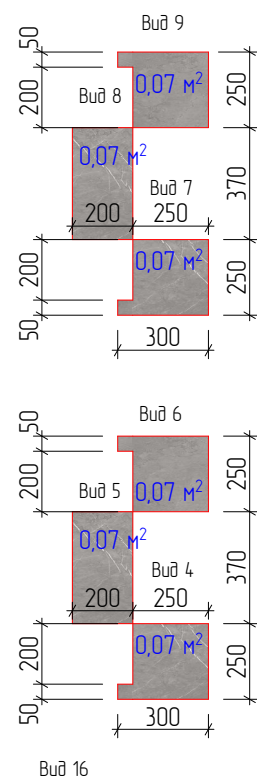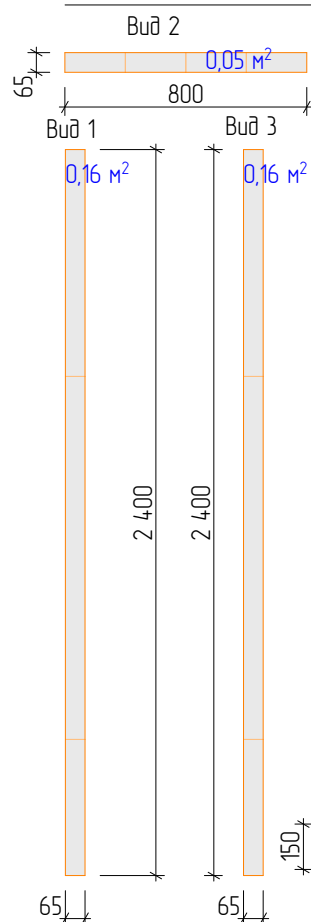


Условное обозначение:

- | | | | |
|---|---|---|--|
|  | Керамогранит №01. Керамогранит.
Изготовитель: Elegant Grey, кол-я: Forte Dei
Marmi, размер: 1200x1200 мм, толщину
уточнить при закупе. |  | Зеркало №2. Разработать со специалистами
(стандарт*) размеры и резка по чертежу. |
|  | |  | Покраска №3. Влагостойкая. Выполнить по
штукатуренной поверхности. Цвет при
выборе образца (белый*). |
|  | Керамогранит №02. Керамогранит.
Изготовитель: Nutmeg, кол-я: Woodslate Life,
размер: 1200x200 мм, толщину уточнить при
закупе. |  | Направление и начало укладки |


Примечания:

1. * – размеры уточнить по месту после выполнения черновых отделочных работ.
2. Выключатели располагать от уровня чистого пола на высоте 900 мм. Исключения указаны на чертеже.
3. Розетки располагать от уровня чистого пола на высоте 300 мм. Исключения указаны на чертеже.
4. Предусмотреть люк скрытого монтажа для доступа к коммуникациям, размещение уточнить по месту.
5. Совместить швы плитки на смежных стенах и полу.
6. Точную привязку выводов коммуникаций решить после выбора оборудования по инструкции монтажа.
7. Расположение розеток и выключателей согласовать с изготовителями кухонного гарнитура.
8. Предусмотреть гидроизоляцию пола с заведением на стену до потолка.
9. ** – размещение вывода 220V для электрического полотенцесушителя уточнить после подбора модели по технической документации.
10. ** – размер уточнить по инструкции монтажа оборудования.
11. Розетки, выключатели, регуляторы теплого пола размещать по центру керамической плитки.
12. Высоту проемов выполнить 2460 мм от уровня чистого пола. Уточнить после подбора и согласования модели дверей.
13. Резку зеркала решить по месту авторским надзором.
14. Внутреннее наполнение мебели разработать со специалистами.
15. Серым/синим цветом показаны размеры мебели. Мебель разработать со специалистами, размеры уточнить после выполнения чистовой отделки.

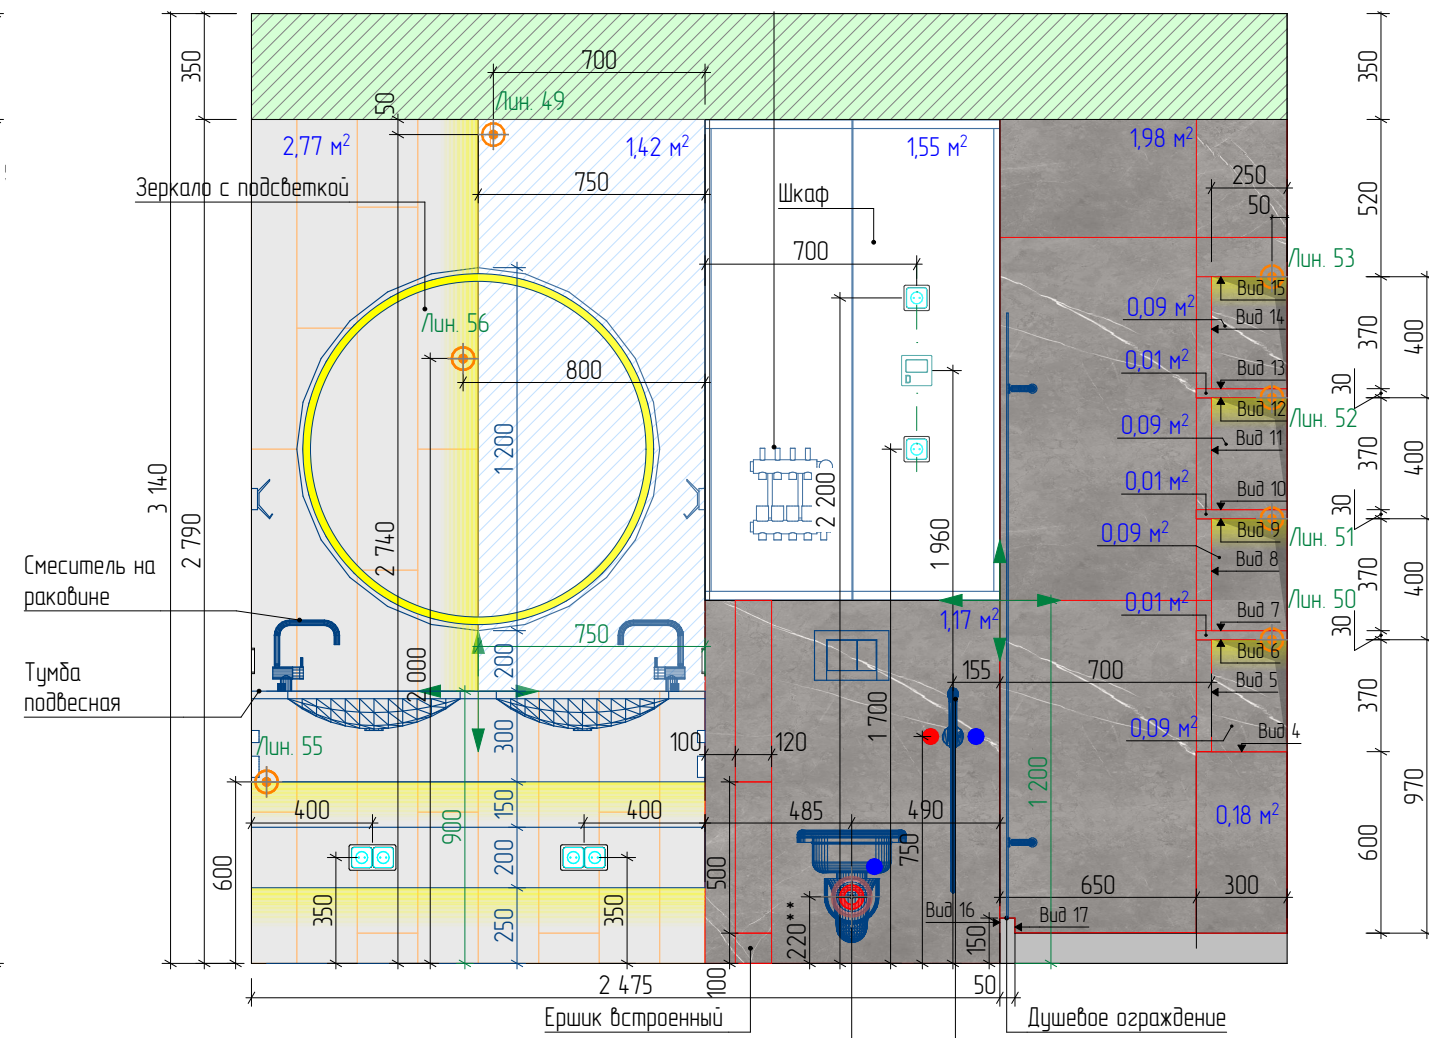

Умный унитаз подвесной
Вывод коммуникаций для подвесного умного унитаза разместить
согласно инструкции монтажа выбранной модели

Гигиенический душ
Вывод коммуникаций для гигиенического душа разместить
согласно инструкции монтажа выбранной модели

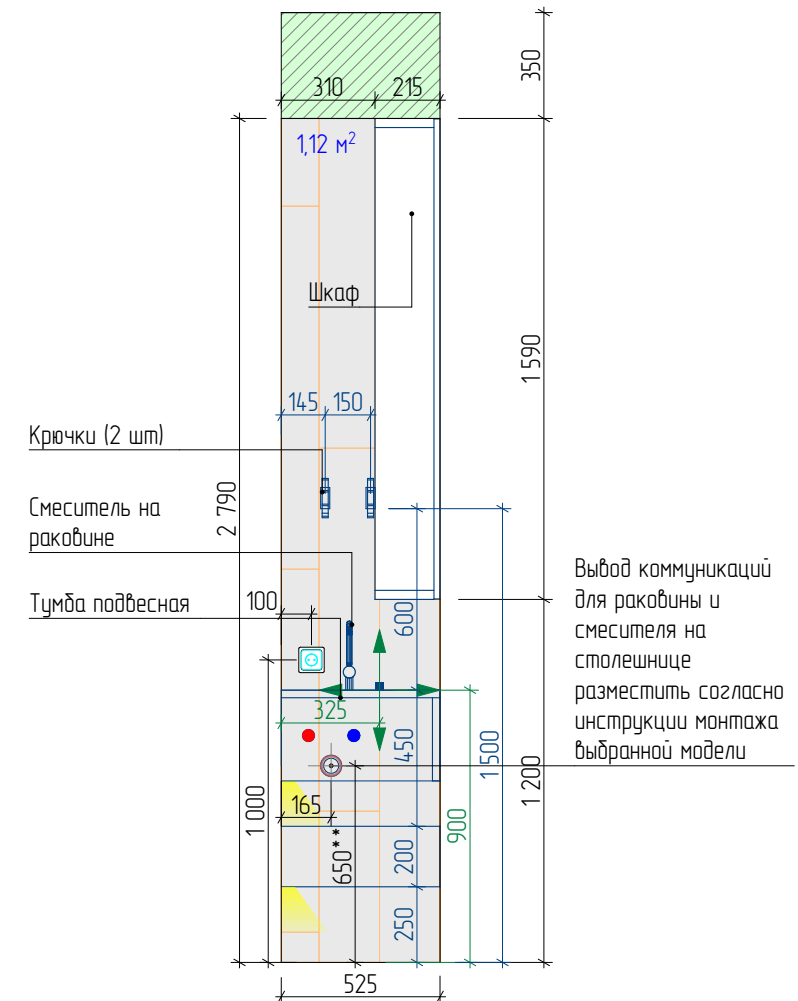

Вывод коммуникаций
для раковины и
смесителя на
столешнице
разместить согласно
инструкции монтажа
выбранной модели

-  Вывод коммуникаций (ХВС, ГВС, канализация)
-  Вывод электрокабеля для светодиодной ленты
-  Розетка 220 V, влагозащищенная IP44 и выше
-  Выключатель двухклавишный
-  Вывод 220 V


МСК 392.12.25-ЭП ПРЕМИУМ

Эскизный дизайн-проект интерьера квартиры в г. Москва ЖК
"Остров", ул. Нижние Мневники д. 7


Душевая.Развертки стен Г-01, Г-02, Г-03.

Дизайнер интерьера  №1 Александр Батеньков	Стадия	Лист	Листов
	ЭП	62	120
		Подп.	Дата
ГАП	Батеньков А.С.		
Гл. дизайнер	Власова В.А.		
Гл. проектиров.	Луцькова В.Н.		
Разработал	Ильина Е.Е.		

Г-04 Развертка стены 1:25

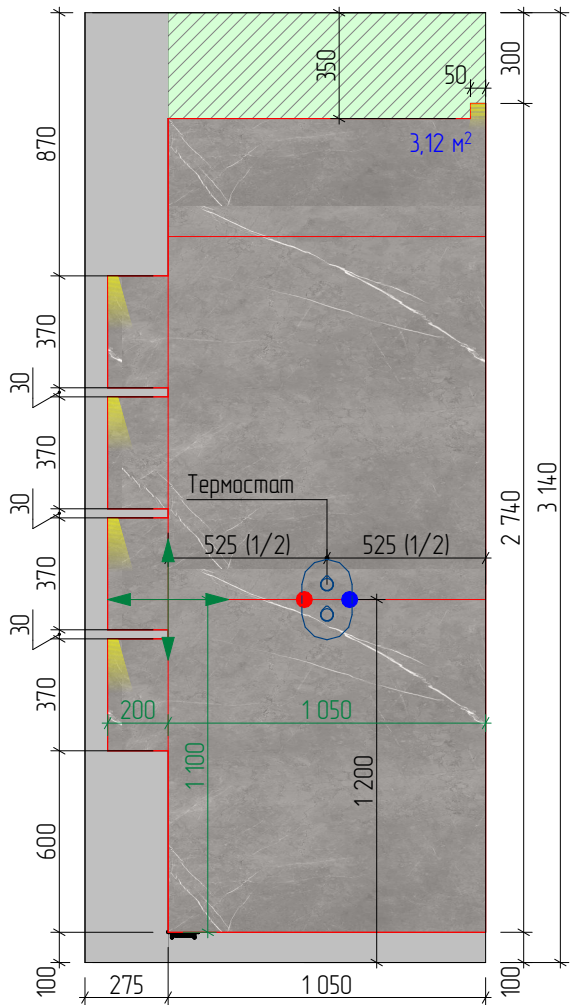

Г-05 Развертка стены 1:25

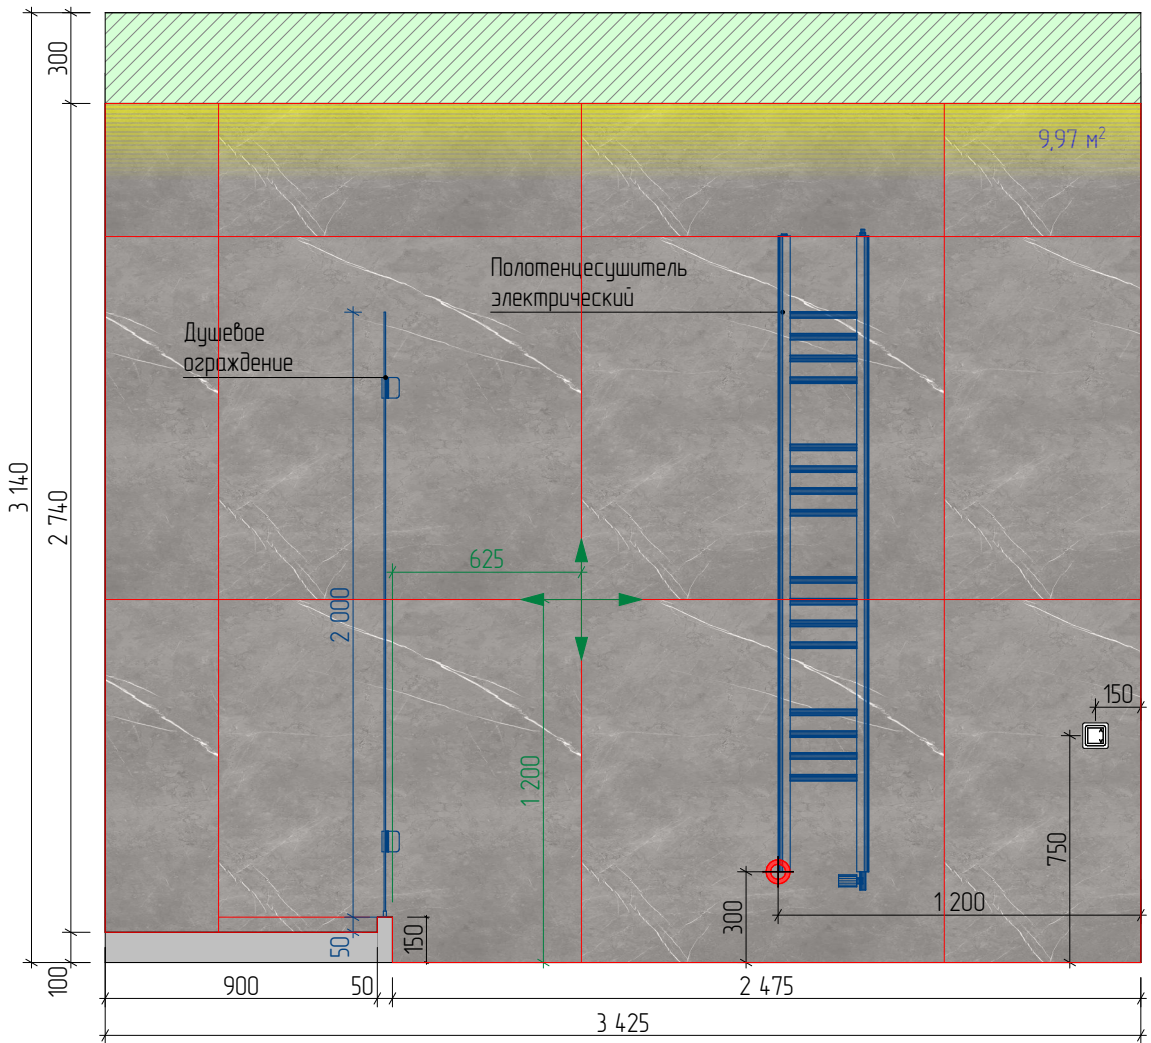

Ведомость отделочных материалов.

№	Обозначение	Наименование	Кол-во	Примечание
Пол:				
1		Покрытие №03. Керамогранит. Изготовитель: Nutmeg, кол-я: Woodslate Life, размер: 1200x200 мм, толщину уточнить при закупе.	4,56 26	м² укладки шт.
Стены:				
2		Покраска №3. Влагостойкая. Выполнить по оштукатуренной поверхности. Цвет при выборе образца (белый*).	3,47	м²
3		Керамогранит №02. Керамогранит. Изготовитель: Nutmeg, кол-я: Woodslate Life, размер: 1200x200 мм, толщину уточнить при закупе.	7,32 37	м² укладки шт.
4		Керамогранит №01. Керамогранит. Изготовитель: Elegant Grey, кол-я: Forte Dei Marini, размер: 1200x1200 мм, толщину уточнить при закупе.	17,65 16	м² укладки шт.
5		Зеркало №2. Разработать со специалистами (стандарт*) размеры и резка по чертежу.	1,42	м²

Условное обозначение:

- Керамогранит №01. Керамогранит. Изготовитель: Elegant Grey, кол-я: Forte Dei Marini, размер: 1200x1200 мм, толщину уточнить при закупе.
- Вывод коммуникаций (ХВС, ГВС, канал-ция)
- Вывод 220 V
- Регулятор теплого пола
- Направление и начало укладки

Примечания:

- * – размеры уточнить по месту после выполнения черновых отделочных работ.
3. Регуляторы теплого пола располагать от уровня чистого пола на высоте 750 мм. Исключения указаны на чертеже.
4. Розетки располагать от уровня чистого пола на высоте 300 мм. Исключения указаны на чертеже.
5. Совместить швы плитки на смежных стенах и полу.
6. Точную привязку выводов коммуникаций решить после выбора оборудования по инструкции монтажа.
7. Предусмотреть гидроизоляцию пола с заведением на стену до потолка.
8. ** – размещение вывода 220V для электрического полотенцесушителя уточнить после подбора модели по технической документации.
9. ** – размер уточнить по инструкции монтажа оборудования.
10. Розетки, выключатели, регуляторы теплого пола размещать по центру керамической плитки.
11. Внутреннее наполнение мебели разработать со специалистами.
12. Серым/синим цветом показаны размеры мебели. Мебель разработать со специалистами, размеры уточнить после выполнения чистовой отделки.

МСК 392.12.25–ЭП ПРЕМИУМ

Эскизный дизайн–проект интерьера квартиры в г. Москва ЖК "Остров", ул. Нижние Мневники д. 7

Душевая.Развертки стен Г-04, Г-05.

 Дизайнер интерьера №1 Александр Батеньков	Стадия	Лист	Листов
	ЭП	63	120
		Подп.	Дата
ГАП	Батеньков А.С.		
Гл. дизайнер	Власова В.А.		
Гл. проектиров.	Луныкова В.Н.		
Разработал	Ильина Е.Е.		