




План отделки пола:

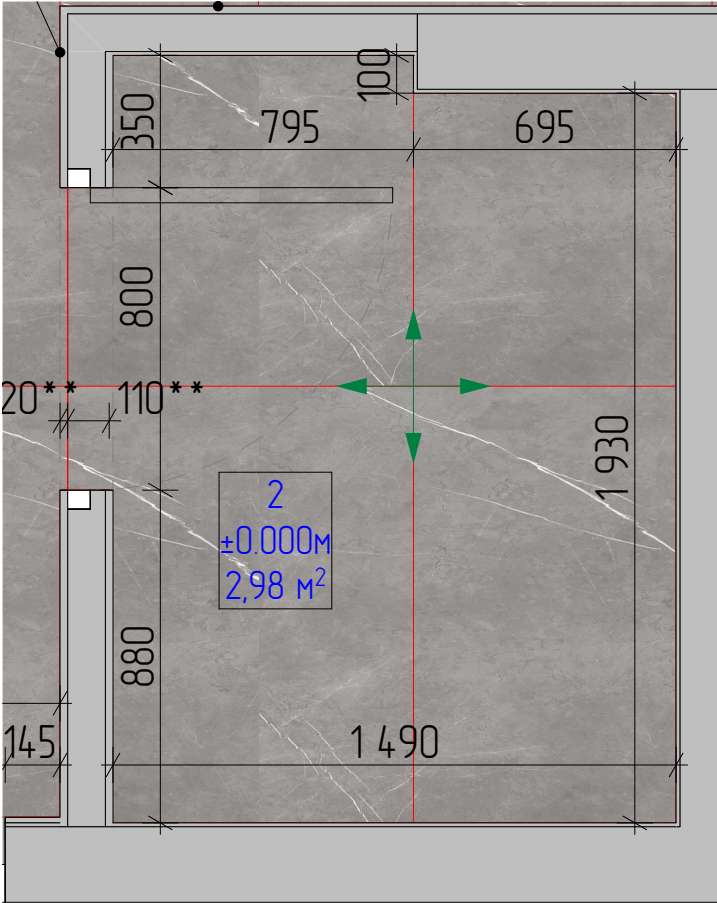

План отделки потолка:

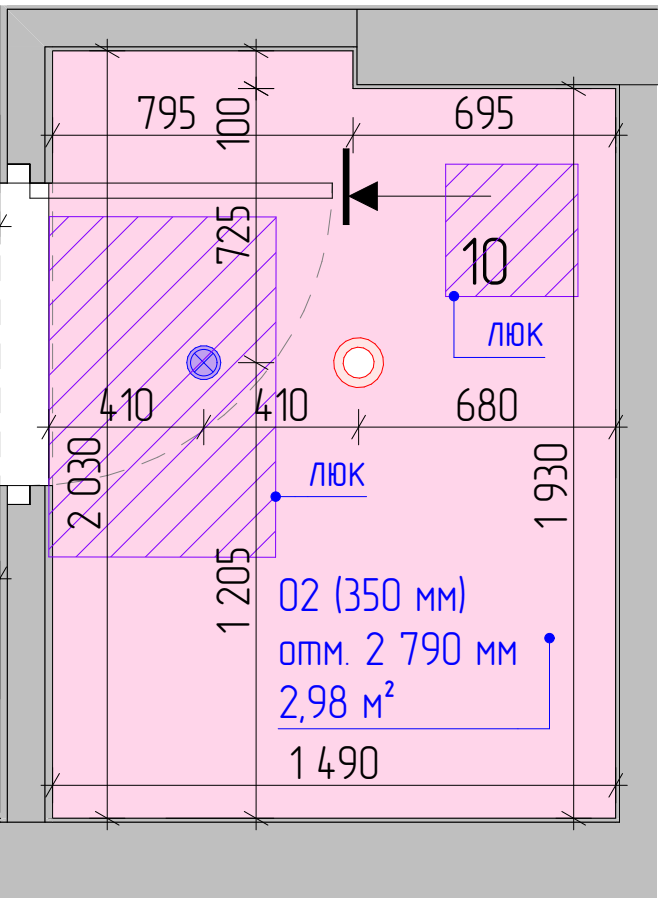


План электрооборудования:

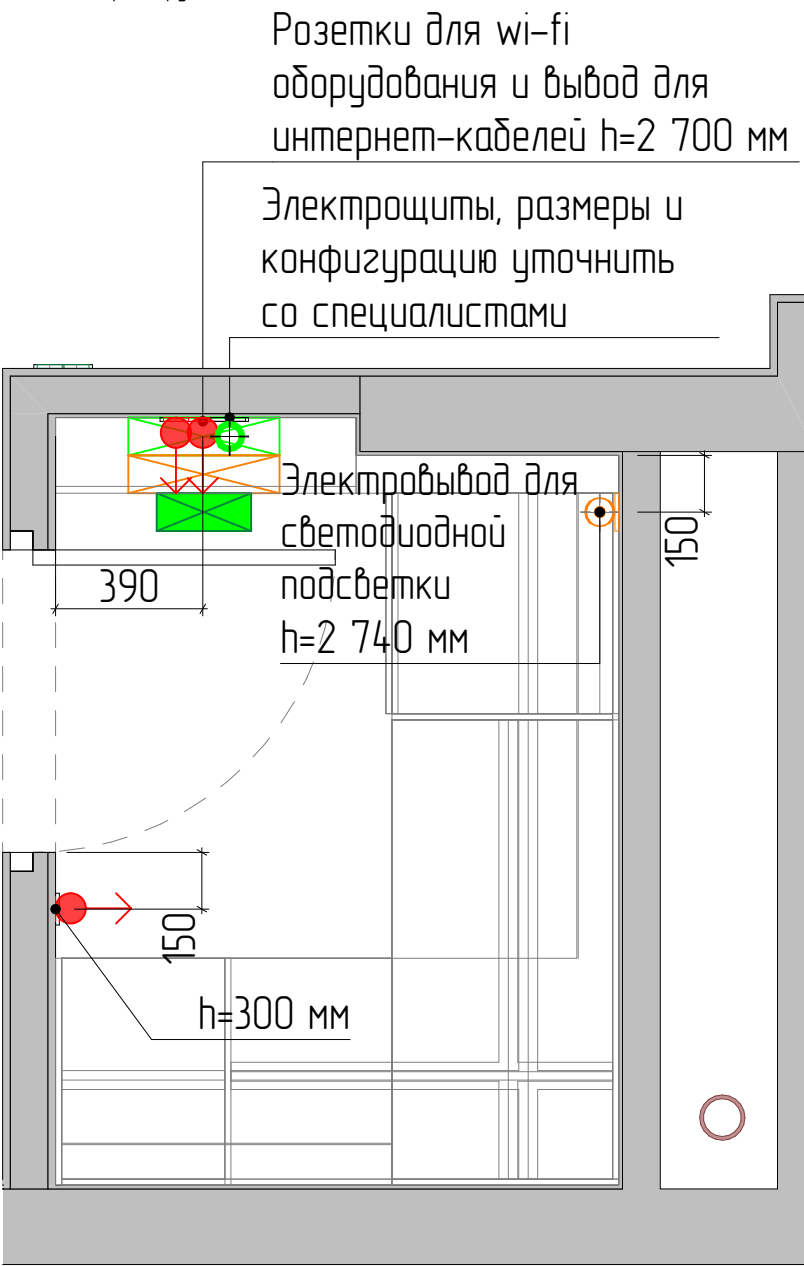

Примечания:

- *- размеры уточнить по месту после выполнения черновых отделочных работ.
- За отметку ±0,000 принят уровень чистого пола.
- При монтаже напольных покрытий уточнить необходимость устройства дверных проемов с порогом.
- *- размеры уточнить по месту после выполнения черновых отделочных работ и установки дверей со скрытой коробкой.
- **-размер уточнить по месту в зависимости от точного расположения полотна двери, стыковка двух разных напольных покрытий должна проходить точно по центру вдоль дверного полотна.
- Выполнить уровни потолка из влагостойкого ГКЛ для предотвращения деформации потолка при затоплении.
- Высоту уровней потолка отсчитывать от существующей ж/б плиты перекрытия помещения.
- От вытяжки провести вентиляционный короб до общедомового канала в конструкции потолка, уточнить по месту со специалистами и заказчиком.
- Шумоизоляцию разработать со специалистами, уточнить состав и толщину слоев шумоизоляционных материалов. Уточнить необходимость устройства с заказчиком.
- Розетки располагать от уровня чистого пола на высоте 0,300 м. Исключения указаны на чертеже.
- Размещение и габаритные размеры электрощита согласовать со специалистами.
- К WI-FI оборудованию подвести 5 выводов интернет-кабеля из расчета: общее количество интернет выводов + розеток + один (вывод в квартиру из подъезда). Размещение wi-fi оборудования и усилителей для него определить по месту, вызвав предварительно на объект специалистов.
- Размещение всех выводов и розеток согласовать со специалистами «Умный дом».
- Датчики пожарной и охранной сигнализации и электровыводы для них разместить совместно со специалистами, предварительно вызвав их на объект.
- Размещение розеток и электровыводов по высоте см. на развертках стен.
- Светильники, встроенные в мебель, согласовать с изготовителями мебели.

План размещения освещения и выключателей:




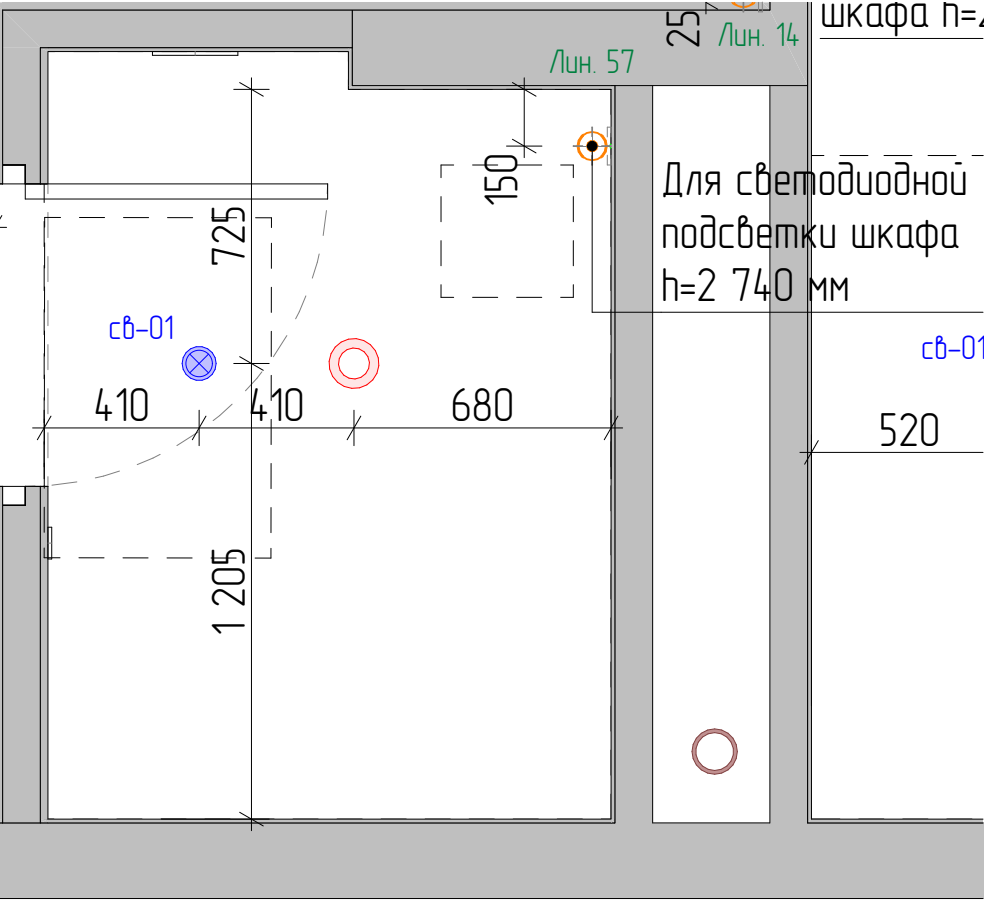


Условные обозначения:

- Условные обозначения:
- Направление и начало укладки
 - Покрывтие №02. Керамогранит. Изготовитель: Elegant Grey, кол-я: Forte Dei Marmi, размер: 1200x1200 мм, толщину уточнить при заказе.
 - Светильник точечный встраиваемый
 - Вывод электрокабеля для светодиодной ленты
 - Люк доступа
 - Розетка 220V
 - Вывод 220V
 - Wifi- оборудование
 - Электрощит
 - Слаботочный щит
 - Диффузор, вытяжка

Условные потолки				
№	Обозначение	Опуск	Примечания	Площадь м2
02		350	Потолок ГК/В. Окрасить в цвет выбранного образца (белый) по армирующему материалу (стеклохолст "паутинка").	2,98

МСК 392.12.25-ЭП ПРЕМИУМ			
Эскизный дизайн-проект интерьера квартиры в г. Москва ЖК "Остров", ул. Нижние Мневники д. 7			
Гардеробная №1.План отделки пола. План отделки потолка. План размещения электрооборудования. План размещения освещения и выключателей.			
Дизайнер интерьера №1 Александр Батеньков	Стадия	Лист	Листов
	ЭП	56	120
		Подп.	Дата
ГАП	Батеньков А.С.		
Гл. дизайнер	Власова В.А.		
Гл. проектиров.	Луныкова В.Н.		
Разработал	Ильина Е.Е.		

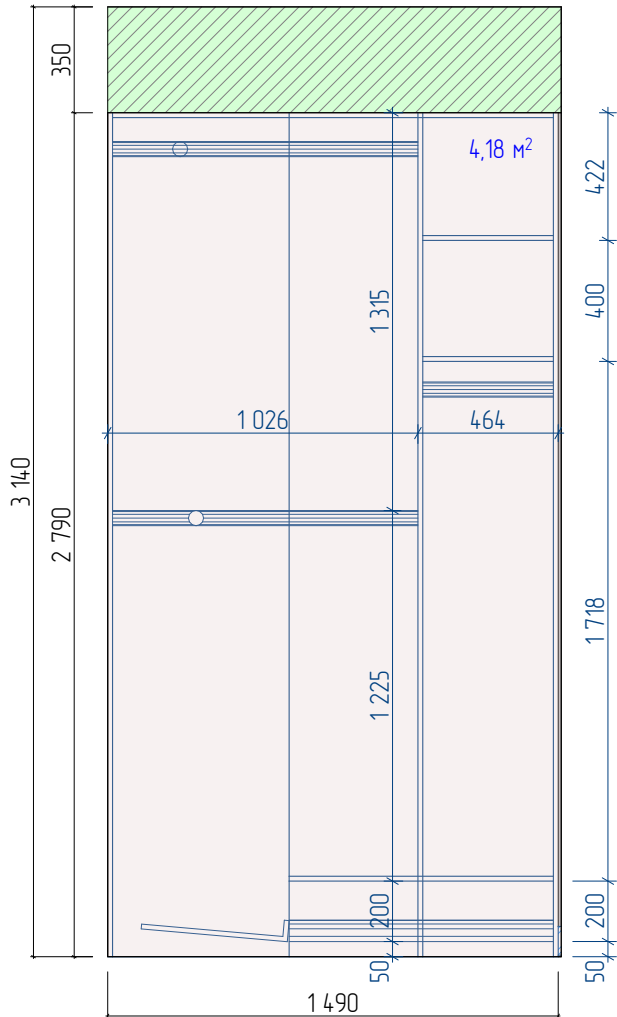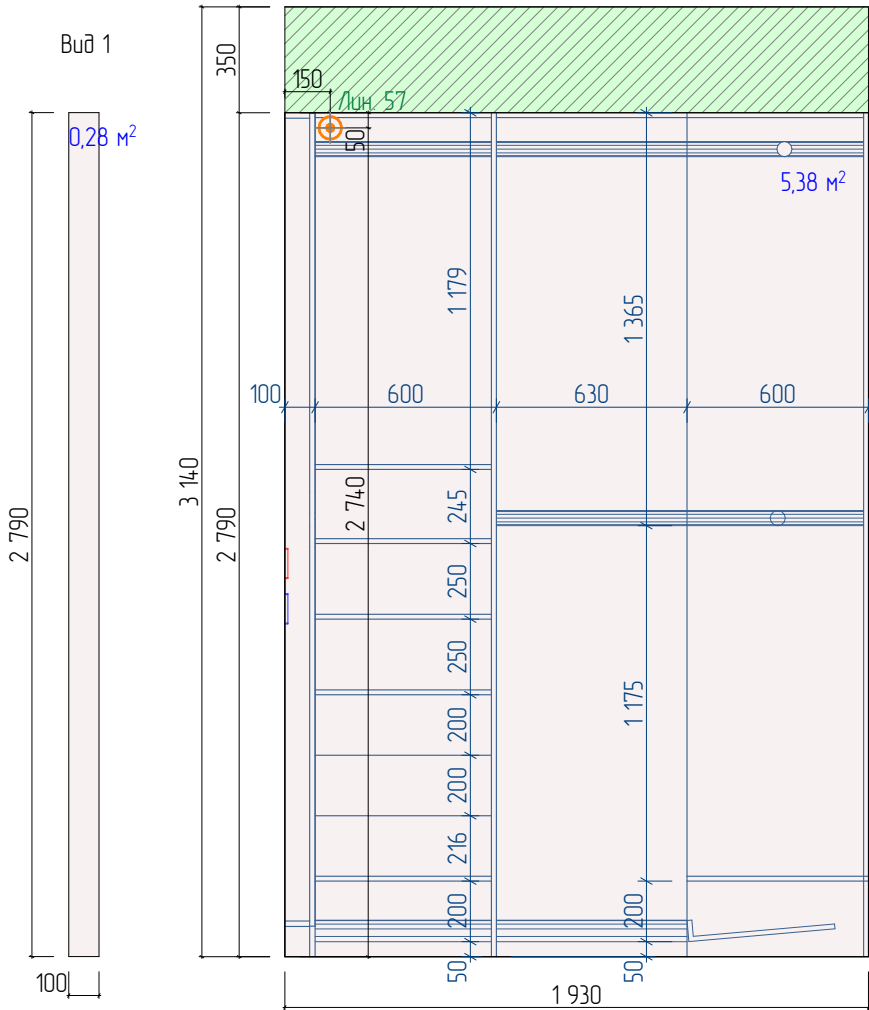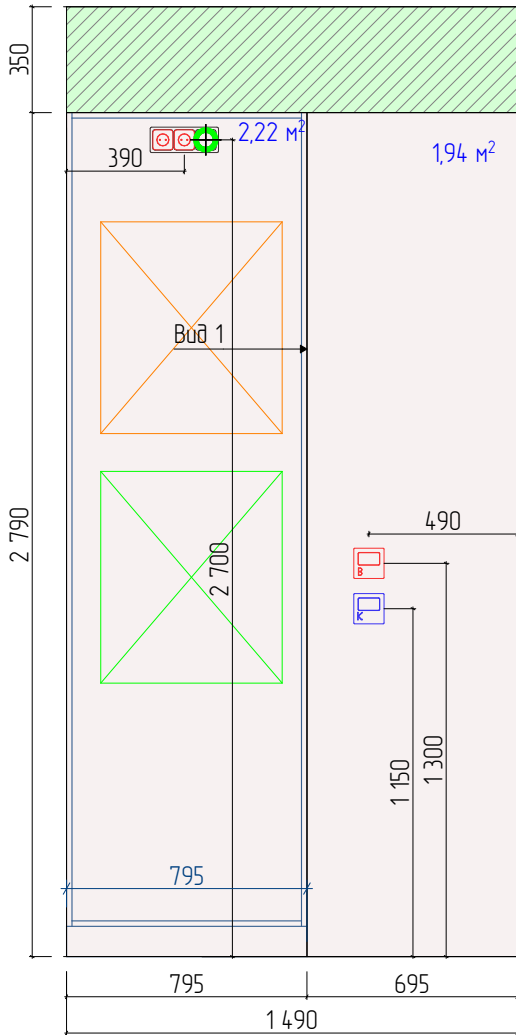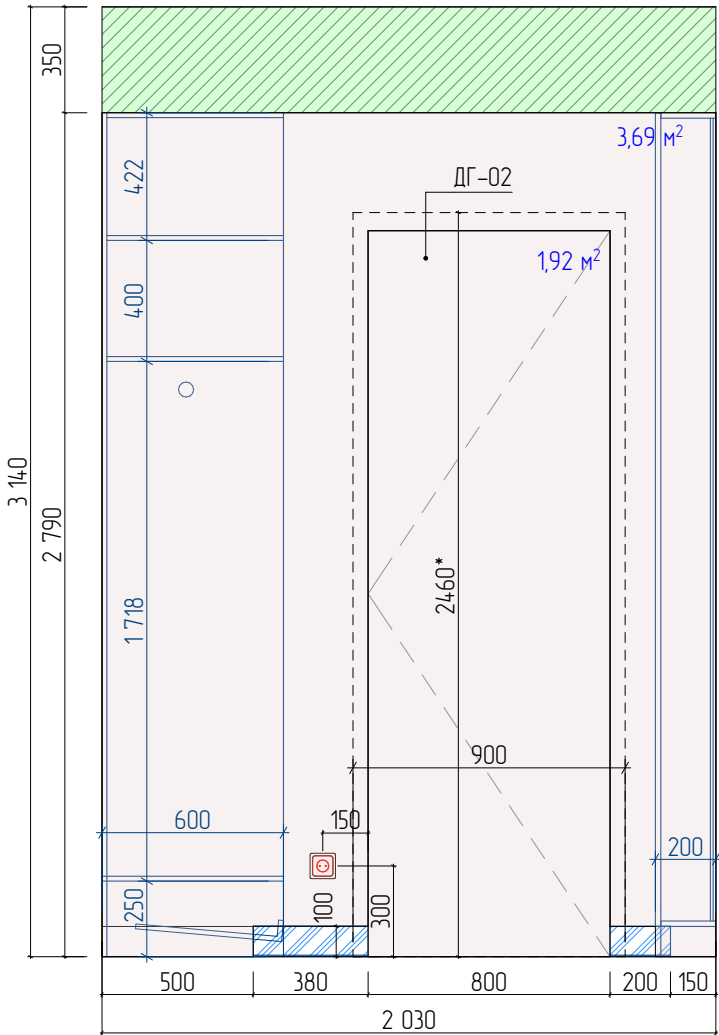

Условные обозначения:

- Монтаж конструкций из ГКВЛ
- Покраска №1. Выполнить по подготовленной поверхности (стеклохолст*). Цвет при выборе образца (бежевый*).
- Плинтус №1. Теневой плинтус скрытого монтажа с МДФ вставкой. Теневой зазор от пола 100 мм. Цвет при выборе образца (в цвет стен).
- Вывод internet-кабеля
- Вывод электрокабеля для светодиодной ленты
- Розетка 220 V
- Электрощит
- Слаботочный щит
- Блок управления каналным кондиционером
- Блок управления вентиляционной системой

Примечания:

- *- размеры уточнить по месту после выполнения черновых отделочных работ.
- Розетки располагать от уровня чистого пола на высоте 300 мм. Исключения указаны на чертеже.
- Цвет окрашивания плинтуса уточнить после согласования образца.
- Высоту проемов выполнить 2460 мм от уровня чистого пола. Уточнить после подбора и согласования модели дверей.
- Плинтус подрезать по месту в местах стыковки с дверями и мебелью.
- Внутреннее наполнение мебели разработать со специалистами.
- Серым/синим цветом показаны размеры мебели. Мебель разработать со специалистами, размеры уточнить после выполнения чистовой отделки.

Ведомость отделочных материалов.

№	Обозначение	Наименование	Кол-во	Примечание
Пол:				
1		Покрывие №02. Керамогранит. Изготовитель: Elegant Grey, кол-я: Forte Dei Marini, размер: 1200x1200 мм, толщину уточнить при покупке.	2,98 3	м² укладки шт.
Стены:				
2		Плинтус №1. Теневой плинтус скрытого монтажа с МДФ вставкой. Теневой зазор от пола 100 мм. Цвет при выборе образца (в цвет стен).	0,50	м.п.
3		Покраска №1. Выполнить по подготовленной поверхности (стеклохолст*). Цвет при выборе образца (бежевый*).	19,61	м²

МСК 392.12.25-ЭП ПРЕМИУМ			
Эскизный дизайн-проект интерьера квартиры в г. Москва ЖК "Остров", ул. Нижние Мневники д. 7			
Гардеробная №1Развертки стен В-01, В-02, В-03, В-04.			
Дизайнер интерьера Александр Батеньков	Стадия	Лист	Листов
	ЭП	57	120
		Подп.	Дата
ГАП	Батеньков А.С.		
Гл. дизайнер	Власова В.А.		
Гл. проектиров.	Луныкова В.Н.		
Разработал	Ильина Е.Е.		